
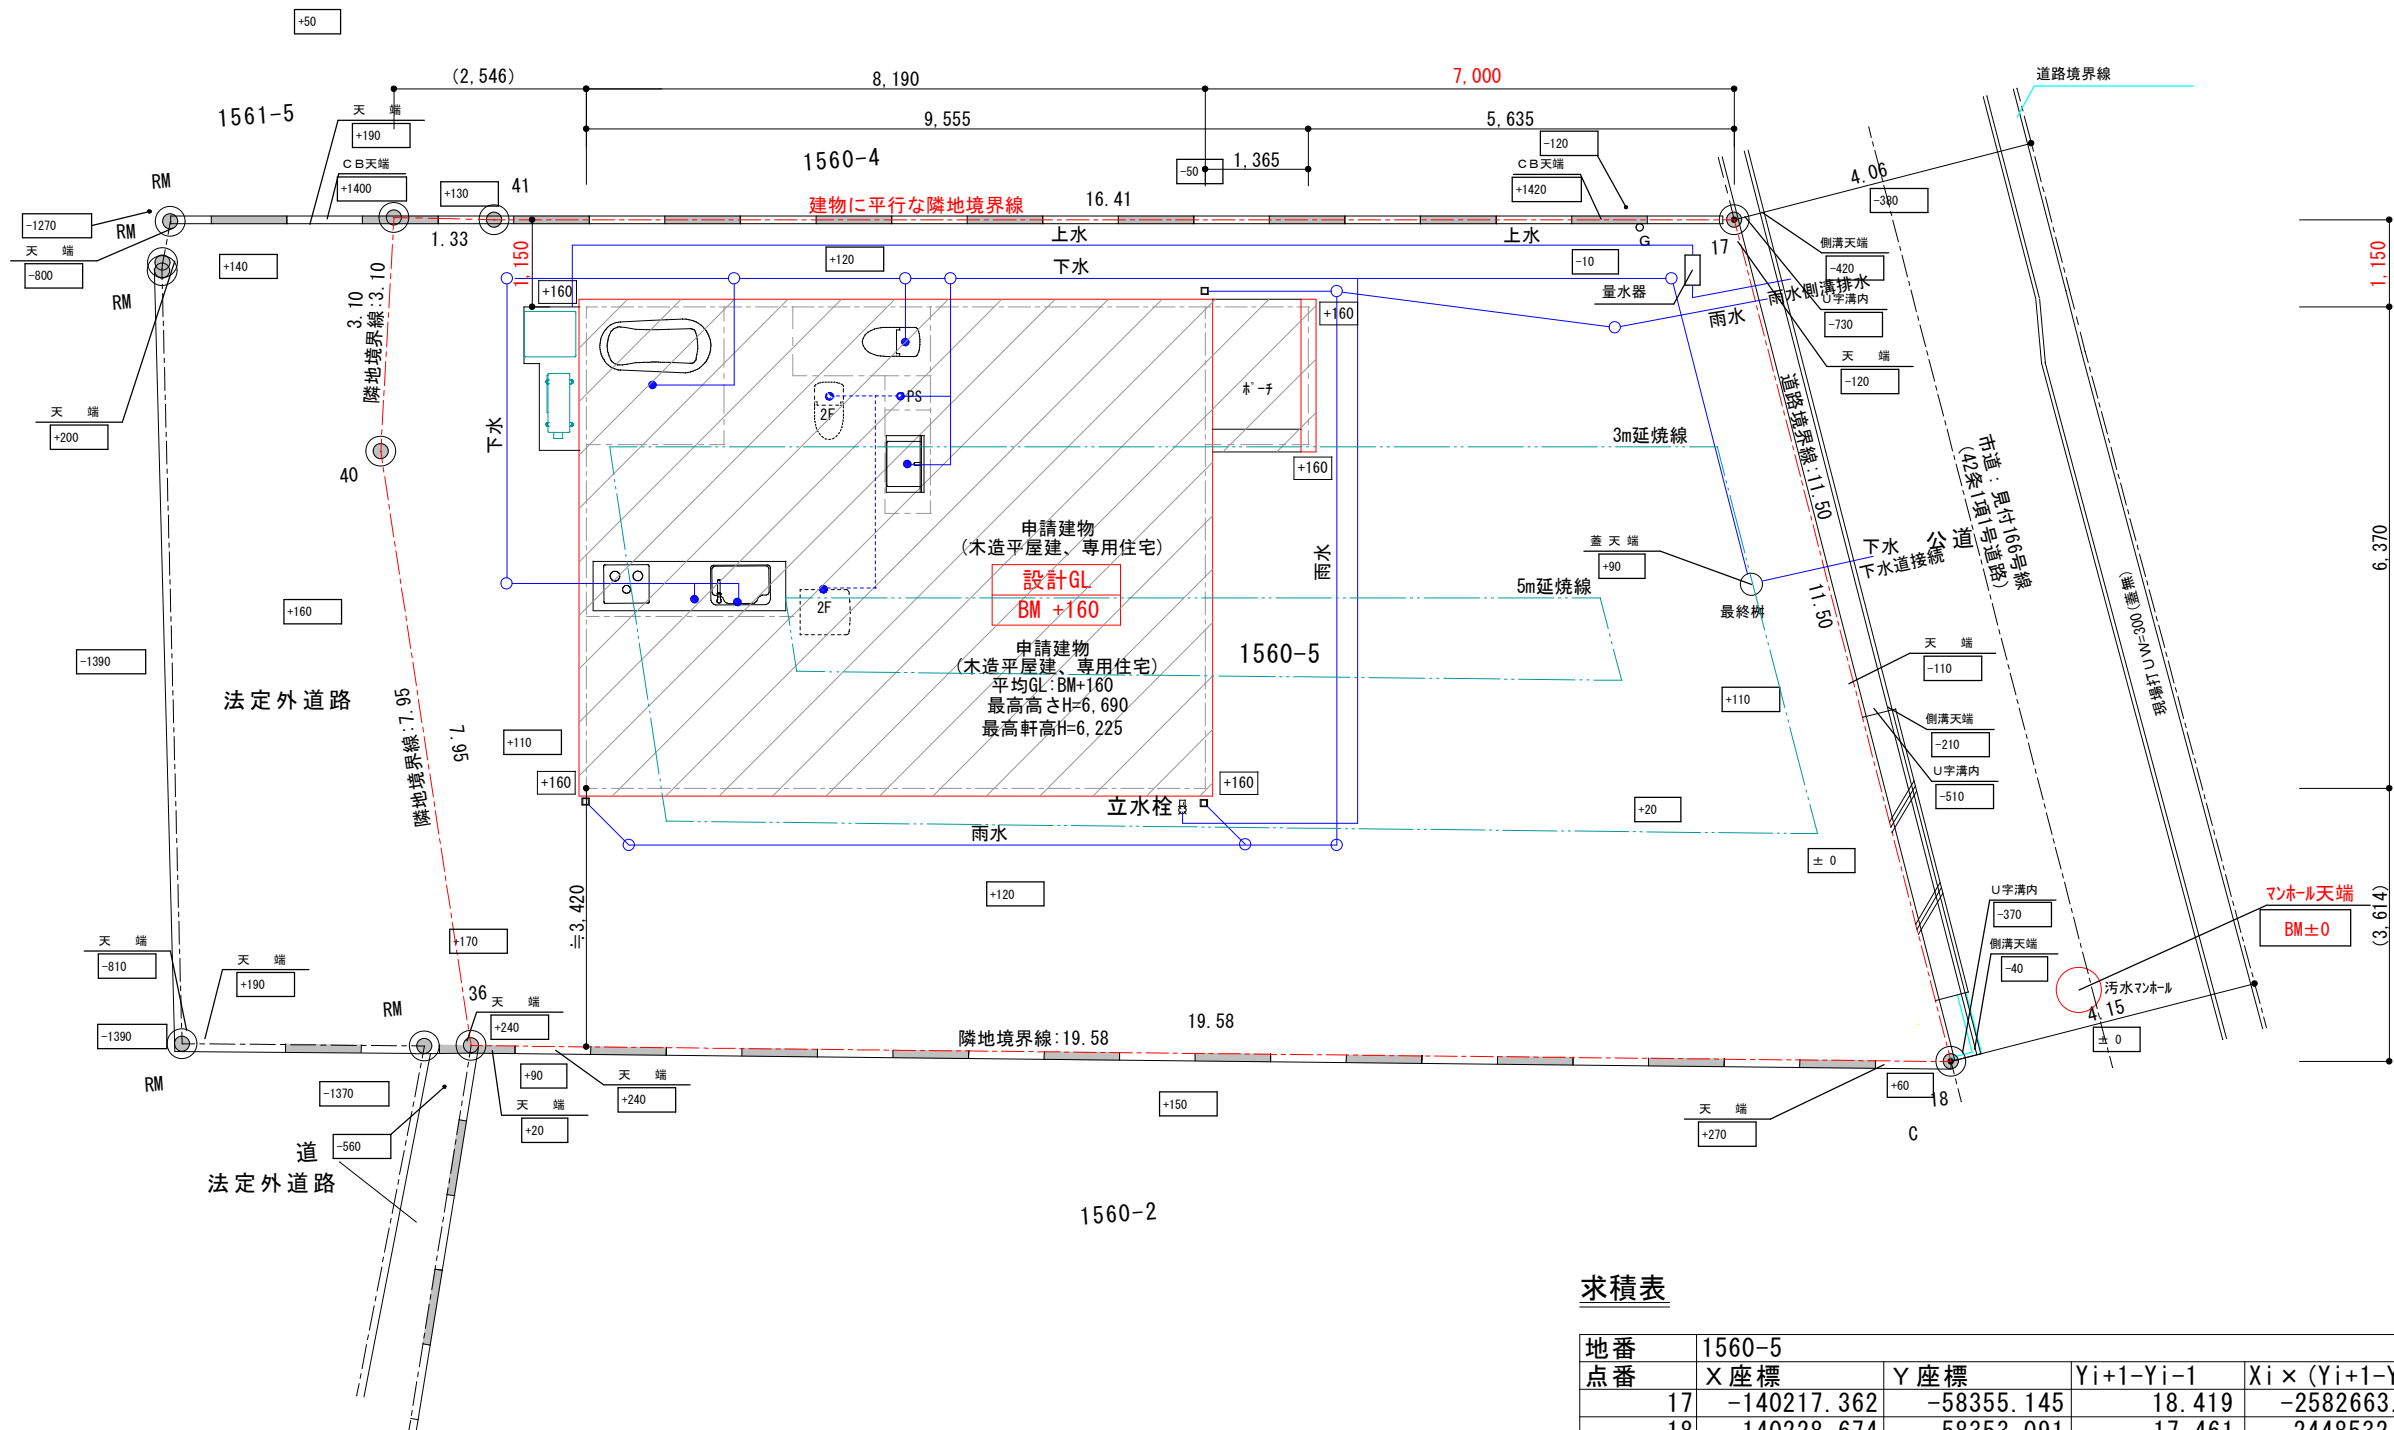


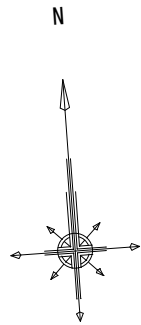

- 凡例
- C : コンクリート杭
 - P : プラスチック杭
 - RM : 金属標
 - R : 金属鋸
 - M : 刻み
 - T : 基準点

トータル面積表		(㎡)
敷地面積		208.09
建築面積		54.65
床面積	1階	52.17
	2階	52.17
延床面積		104.34
建蔽率	$(54.65/208.09) \times 100$	26.27%
容積率	$(104.34/208.09) \times 100$	50.15%

道路斜線制限については、明らかに適合する。
北側斜線制限については、明らかに適合する。
平均地盤面について
申請建物の周囲の平均地盤面高さをBM+160とする。

求積表

地番	1560-5			
点番	X座標	Y座標	Yi+1-Yi-1	Xi x (Yi+1-Yi-1)
17	-140217.362	-58355.145	18.419	-2582663.590678
18	-140228.674	-58353.091	-17.461	2448532.876714
36	-140227.050	-58372.606	-20.135	2823471.651750
40	-140219.124	-58373.226	-0.227	31829.741148
39	-140216.052	-58372.833	1.716	-240610.745232
41	-140216.177	-58371.510	17.688	-2480143.738776
合計				416.194926
合計面積				208.097463
地積				208.09㎡

測地系	世界測地系
座標系	Ⅷ系
測量年月日	令和6年 12月 21日

決定図

訂正	浜岡一級総合設計事務所 一級建築士事務所 静岡県知事登録第 (10)2441号 一級建築士 大臣登録第 365879号 西原利昌	LIFEFUND PG HOUSE	株式会社 LIFEFUND InDesign office 一級建築士事務所 事務所登録 (2)第7595号 一級建築士登録 第179770号 鈴木 達男 〒432-8023 静岡県浜松市中央区鴨江3丁目70番23号	年月日 2025.3.8	件名 西野敬一郎様・さやか様 邸新築工事	設計 倉田	IC	工事 青島	図番 2-1
				縮尺 1/100	図名 配置図				