


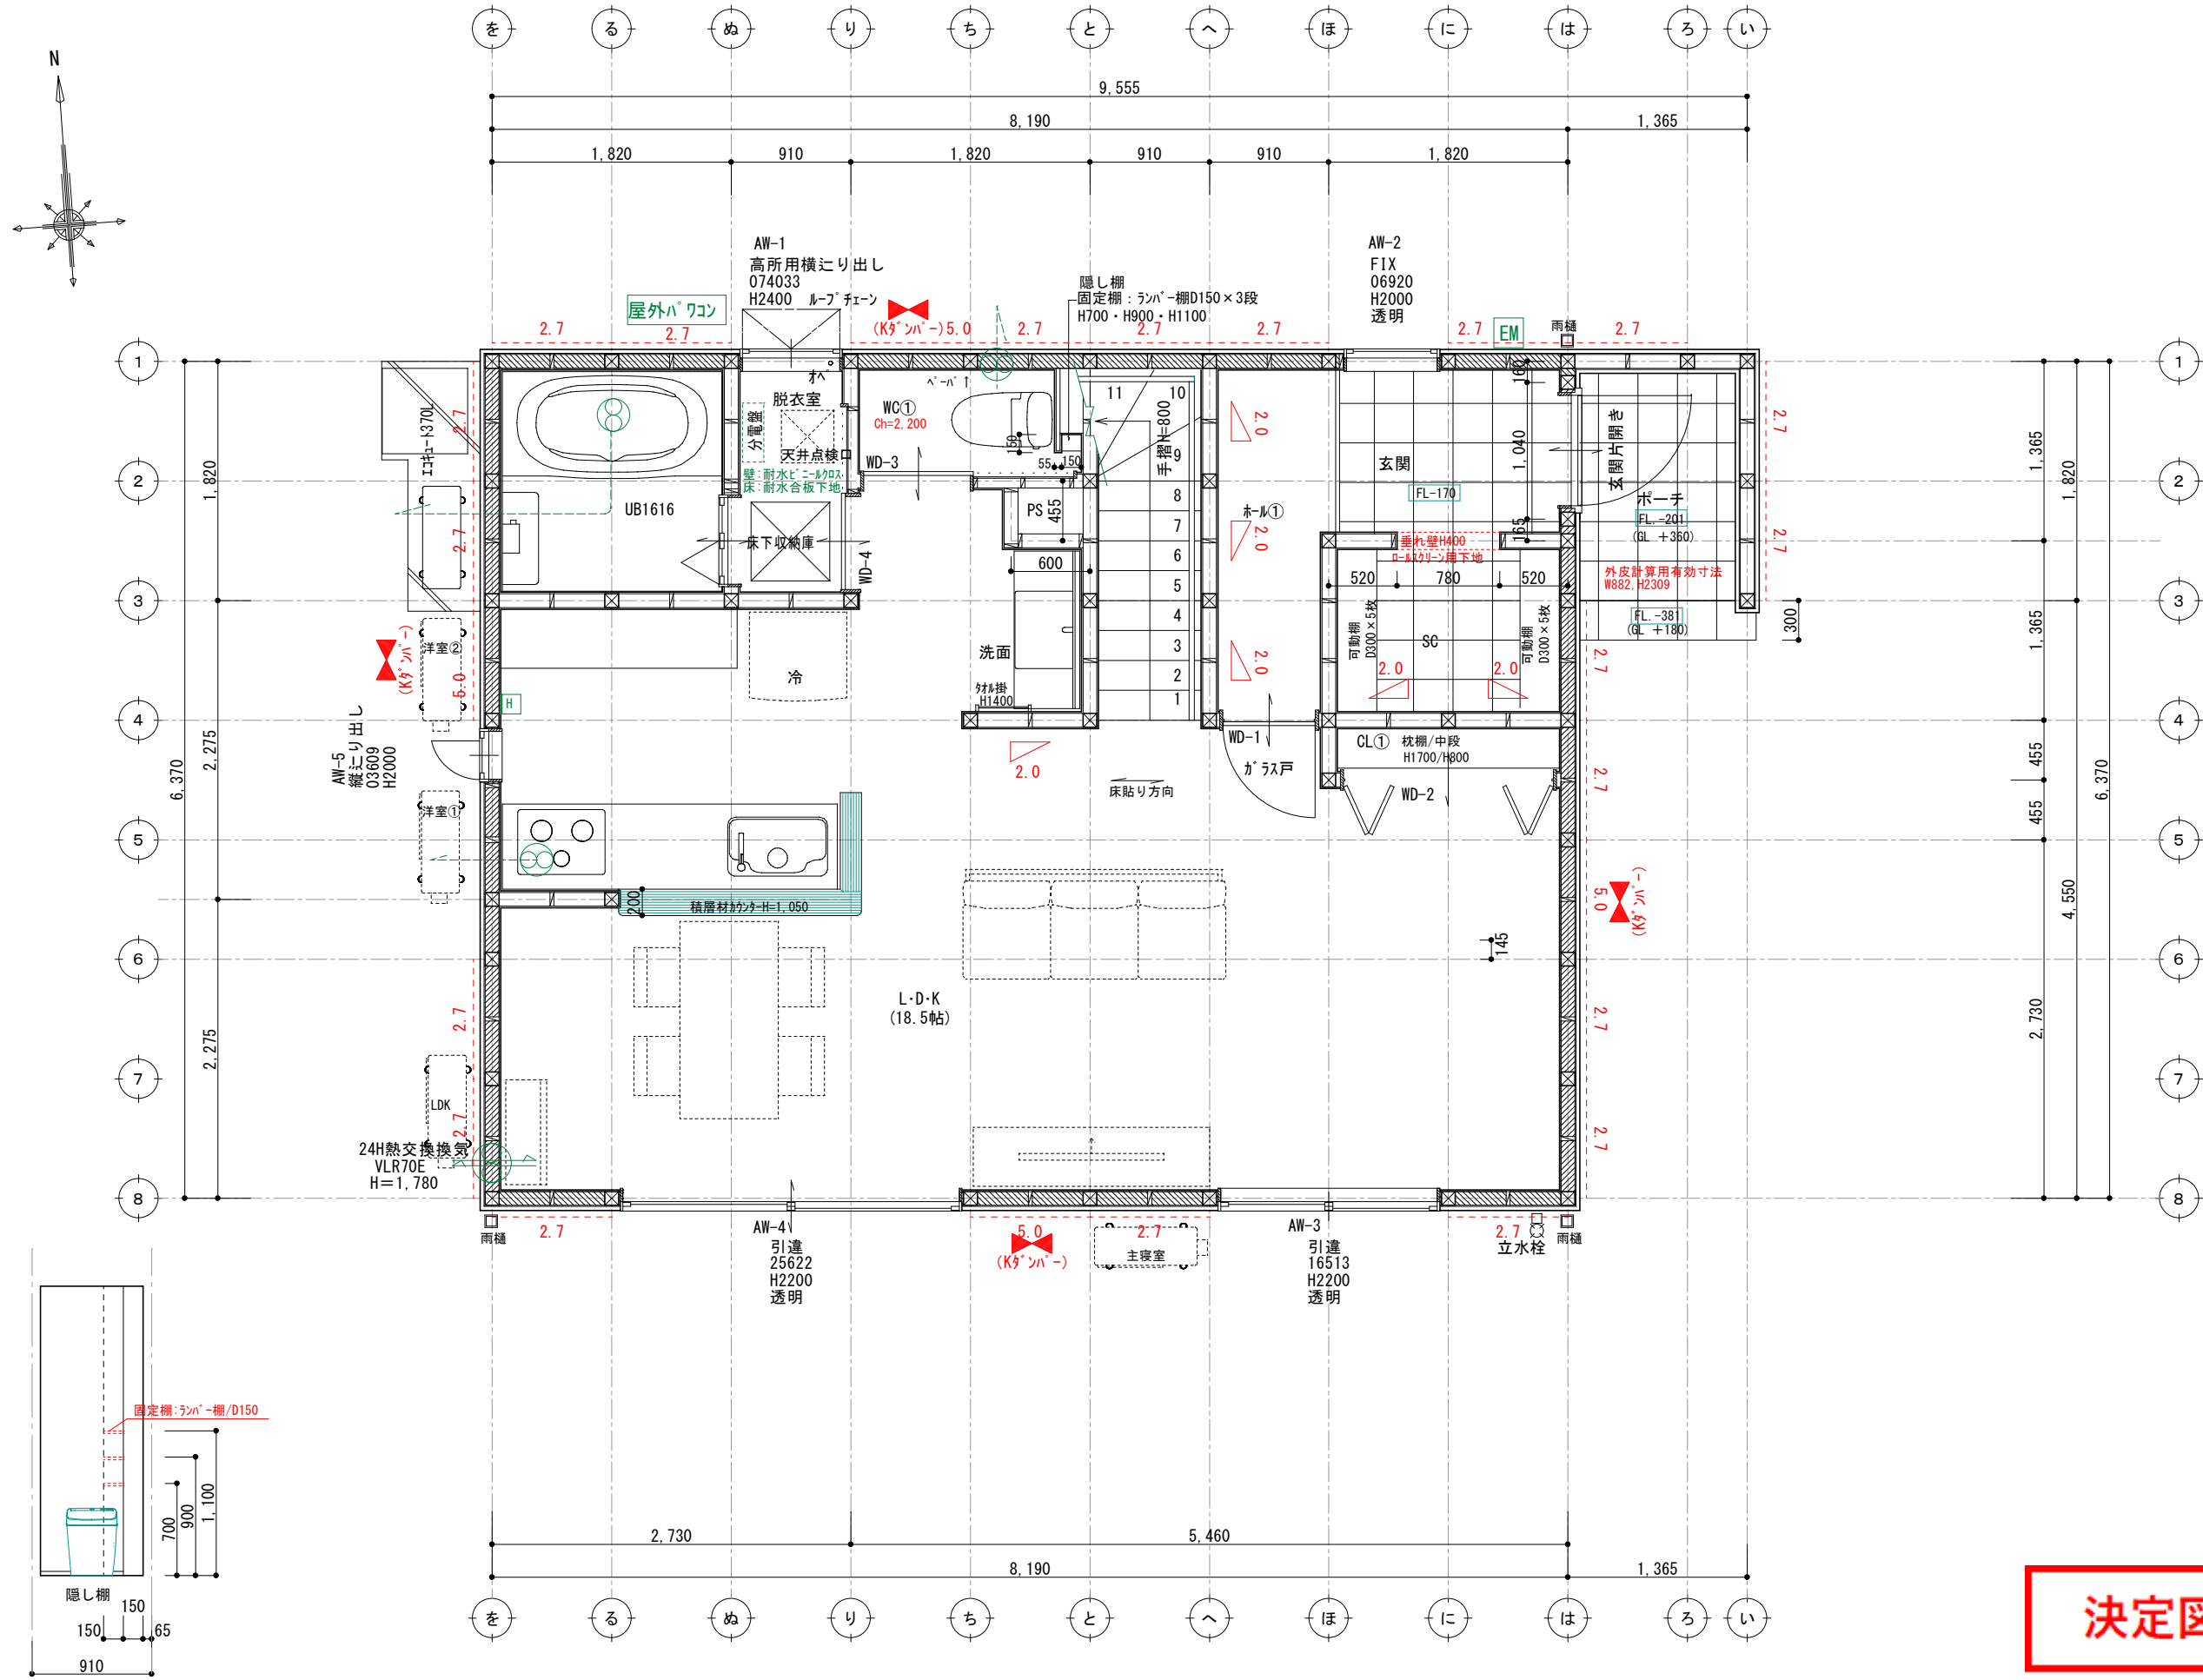

壁付け 住宅用火災報知器			数量
H	熱感知器	電池式(単独型)	1
	露出型		
壁付け 住宅用火災報知器			数量
S	煙感知器	電池式(単独型)	
	露出型		

※ 煙感知器は壁・梁より600mm以上離す
壁に取付ける場合、
天井から150mm以上500mm以内離す
換気扇・エアコン吹出口から1500mm以上離す
※ 全室LED照明とする。
※ 標準天井高さ2,400
※ 特記無きガラスは型ガラス

* 凡例

管柱 (105×105)

Kダクト (3.30倍 FRM-0641)

片筋違い (2.00倍 45×90)
(例 左:柱脚 右:柱頭)

たすき掛筋違い (4.00倍 45×90)

構造用合板 (2.70倍)
(t=9 材質:EXハイパー)

床点検口

天井点検口

換気扇

熱交換換気扇VLR-70

アドバンスシリーズ	
スマートデザイン (外部)	
凡例	
1	コンセント 1ヶ所
2	コンセント 2ヶ所
3	コンセント 3ヶ所
1ET	コンセント1ヶ所接地ターミナル付
2ET	コンセント2ヶ所接地ターミナル付
WP	コンセント 防水型
	エアコン用コンセント
	200V用コンセント
WP	防雨入線プレート
	スイッチ
●	3路スイッチ
●	4路スイッチ
⊗	直結電源
TV	テレビ取出口
TEL	電話取出口 (テレホンガイド)
LAN	LAN取出口 (テレホンガイド)
	壁照明
	リモコン (給湯関係・ルフロ)
	メーター
	分電盤
○	チャイム

※ACコンセント天井付け
※TVアンテナ工事
※スイッチはFL+1100、コンセントはFL+200

決定図