


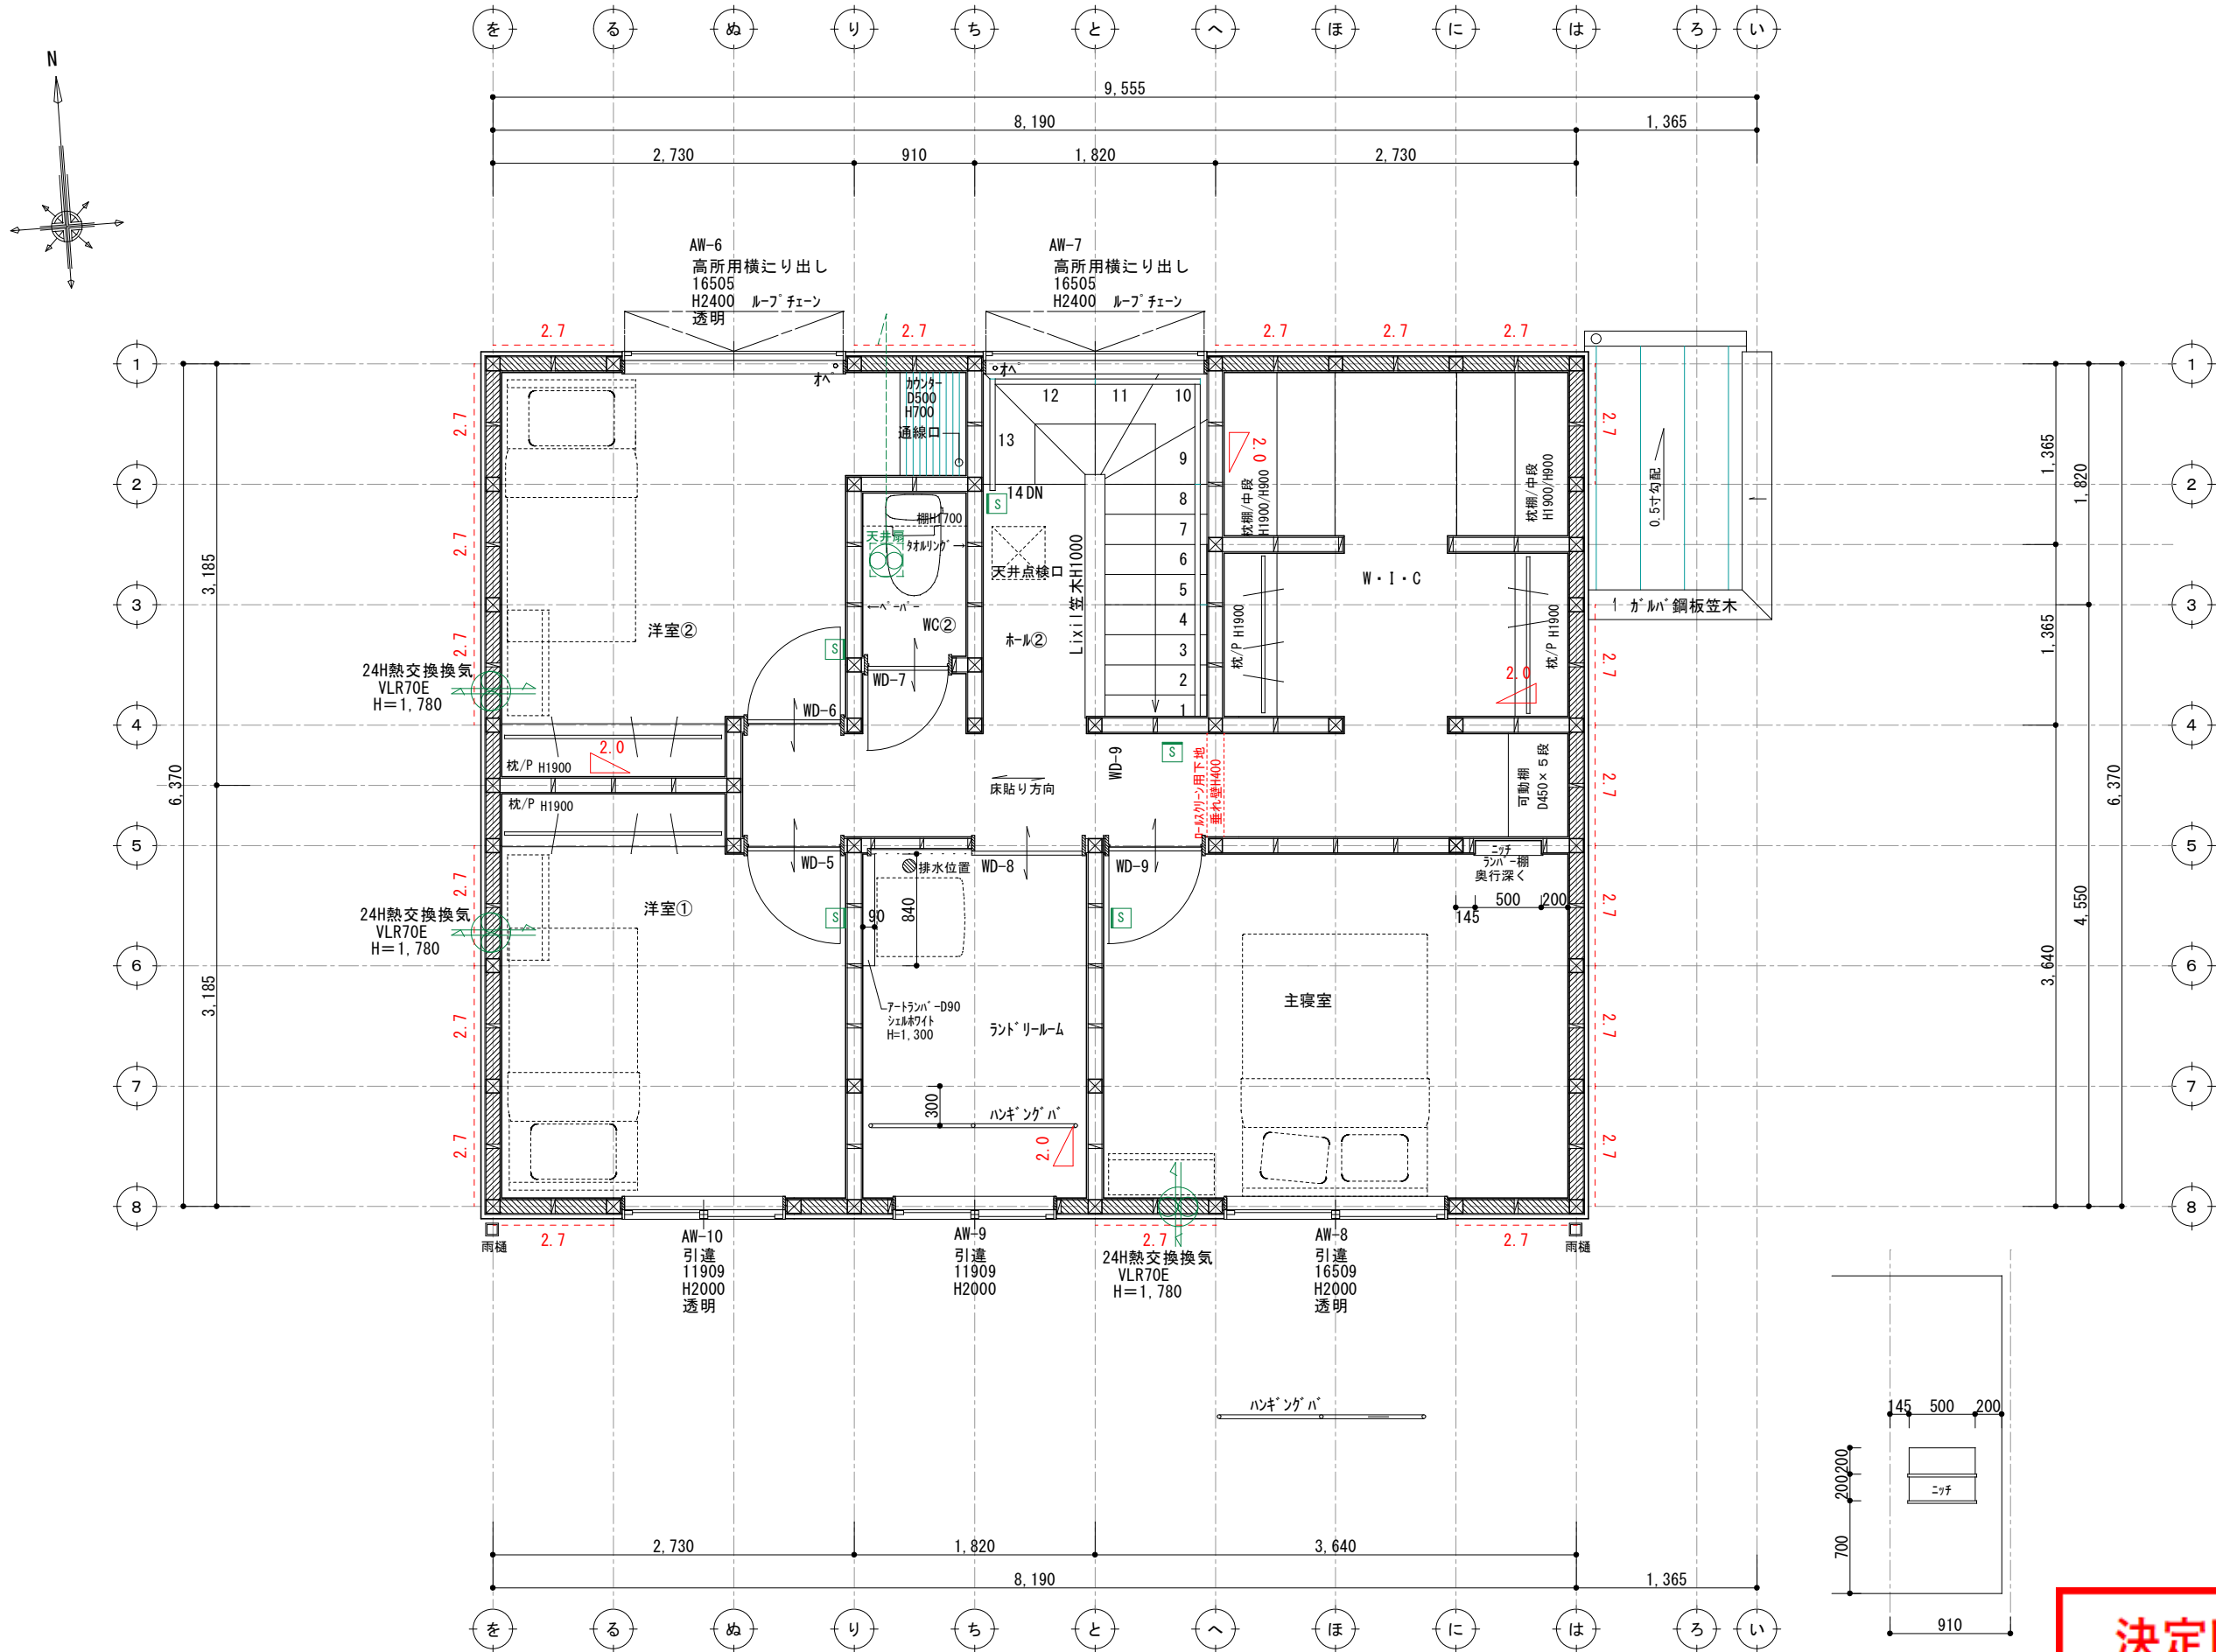

壁付け 住宅用火災報知器			数量
H 熱感知	電池式(単独型)		
	露出型		
壁付け 住宅用火災報知器			数量
S 煙感知	電池式(単独型)		4
	露出型		

※ 煙感知器は壁・梁より600mm以上離す
壁に取付ける場合、
天井から150mm以上500mm以内離す
換気扇・エアコン吹出口から1500mm以上離す
※ 全室LED照明とする。
※ 標準天井高さ2,400
※ 特記無きガラスは型ガラス

* 凡例

管柱 (105×105)

Kダクト (3.30倍 FRM-0641)

片筋違い (2.00倍 45×90)
(例 左:柱脚 右:柱頭)

たすき掛筋違い (4.00倍 45×90)

構造用合板 (2.70倍)
(t=9 9材 EXハイバ)

床点検口

天井点検口

換気扇

熱交換換気扇VLR-70

アドバンスシリーズ		
スマートデザイン (外部)		
凡例	1	コンセント 1ヶ所
2	コンセント 2ヶ所	
3	コンセント 3ヶ所	
1ET	コンセント1ヶ所接地ターミナル付	
2ET	コンセント2ヶ所接地ターミナル付	
WP	コンセント 防水型	
WP	エアコン用コンセント	
WP	200V用コンセント	
WP	防雨入線プレート	
スイッチ	スイッチ	
3	3路スイッチ	
4	4路スイッチ	
直結電源	直結電源	
TV	テレビ取出口	
TEL	電話取出口 (テレホンガイド)	
LAN	LAN取出口 (テレホンガイド)	
壁照明	壁照明	
リモコン	リモコン (給湯関係・ルフロ)	
メーター	メーター	
分電盤	分電盤	
チャイム	チャイム	

※ACコンセント天井付け
※TVアンテナ工事
※スイッチはFL+1100、コンセントはFL+200

決定図