


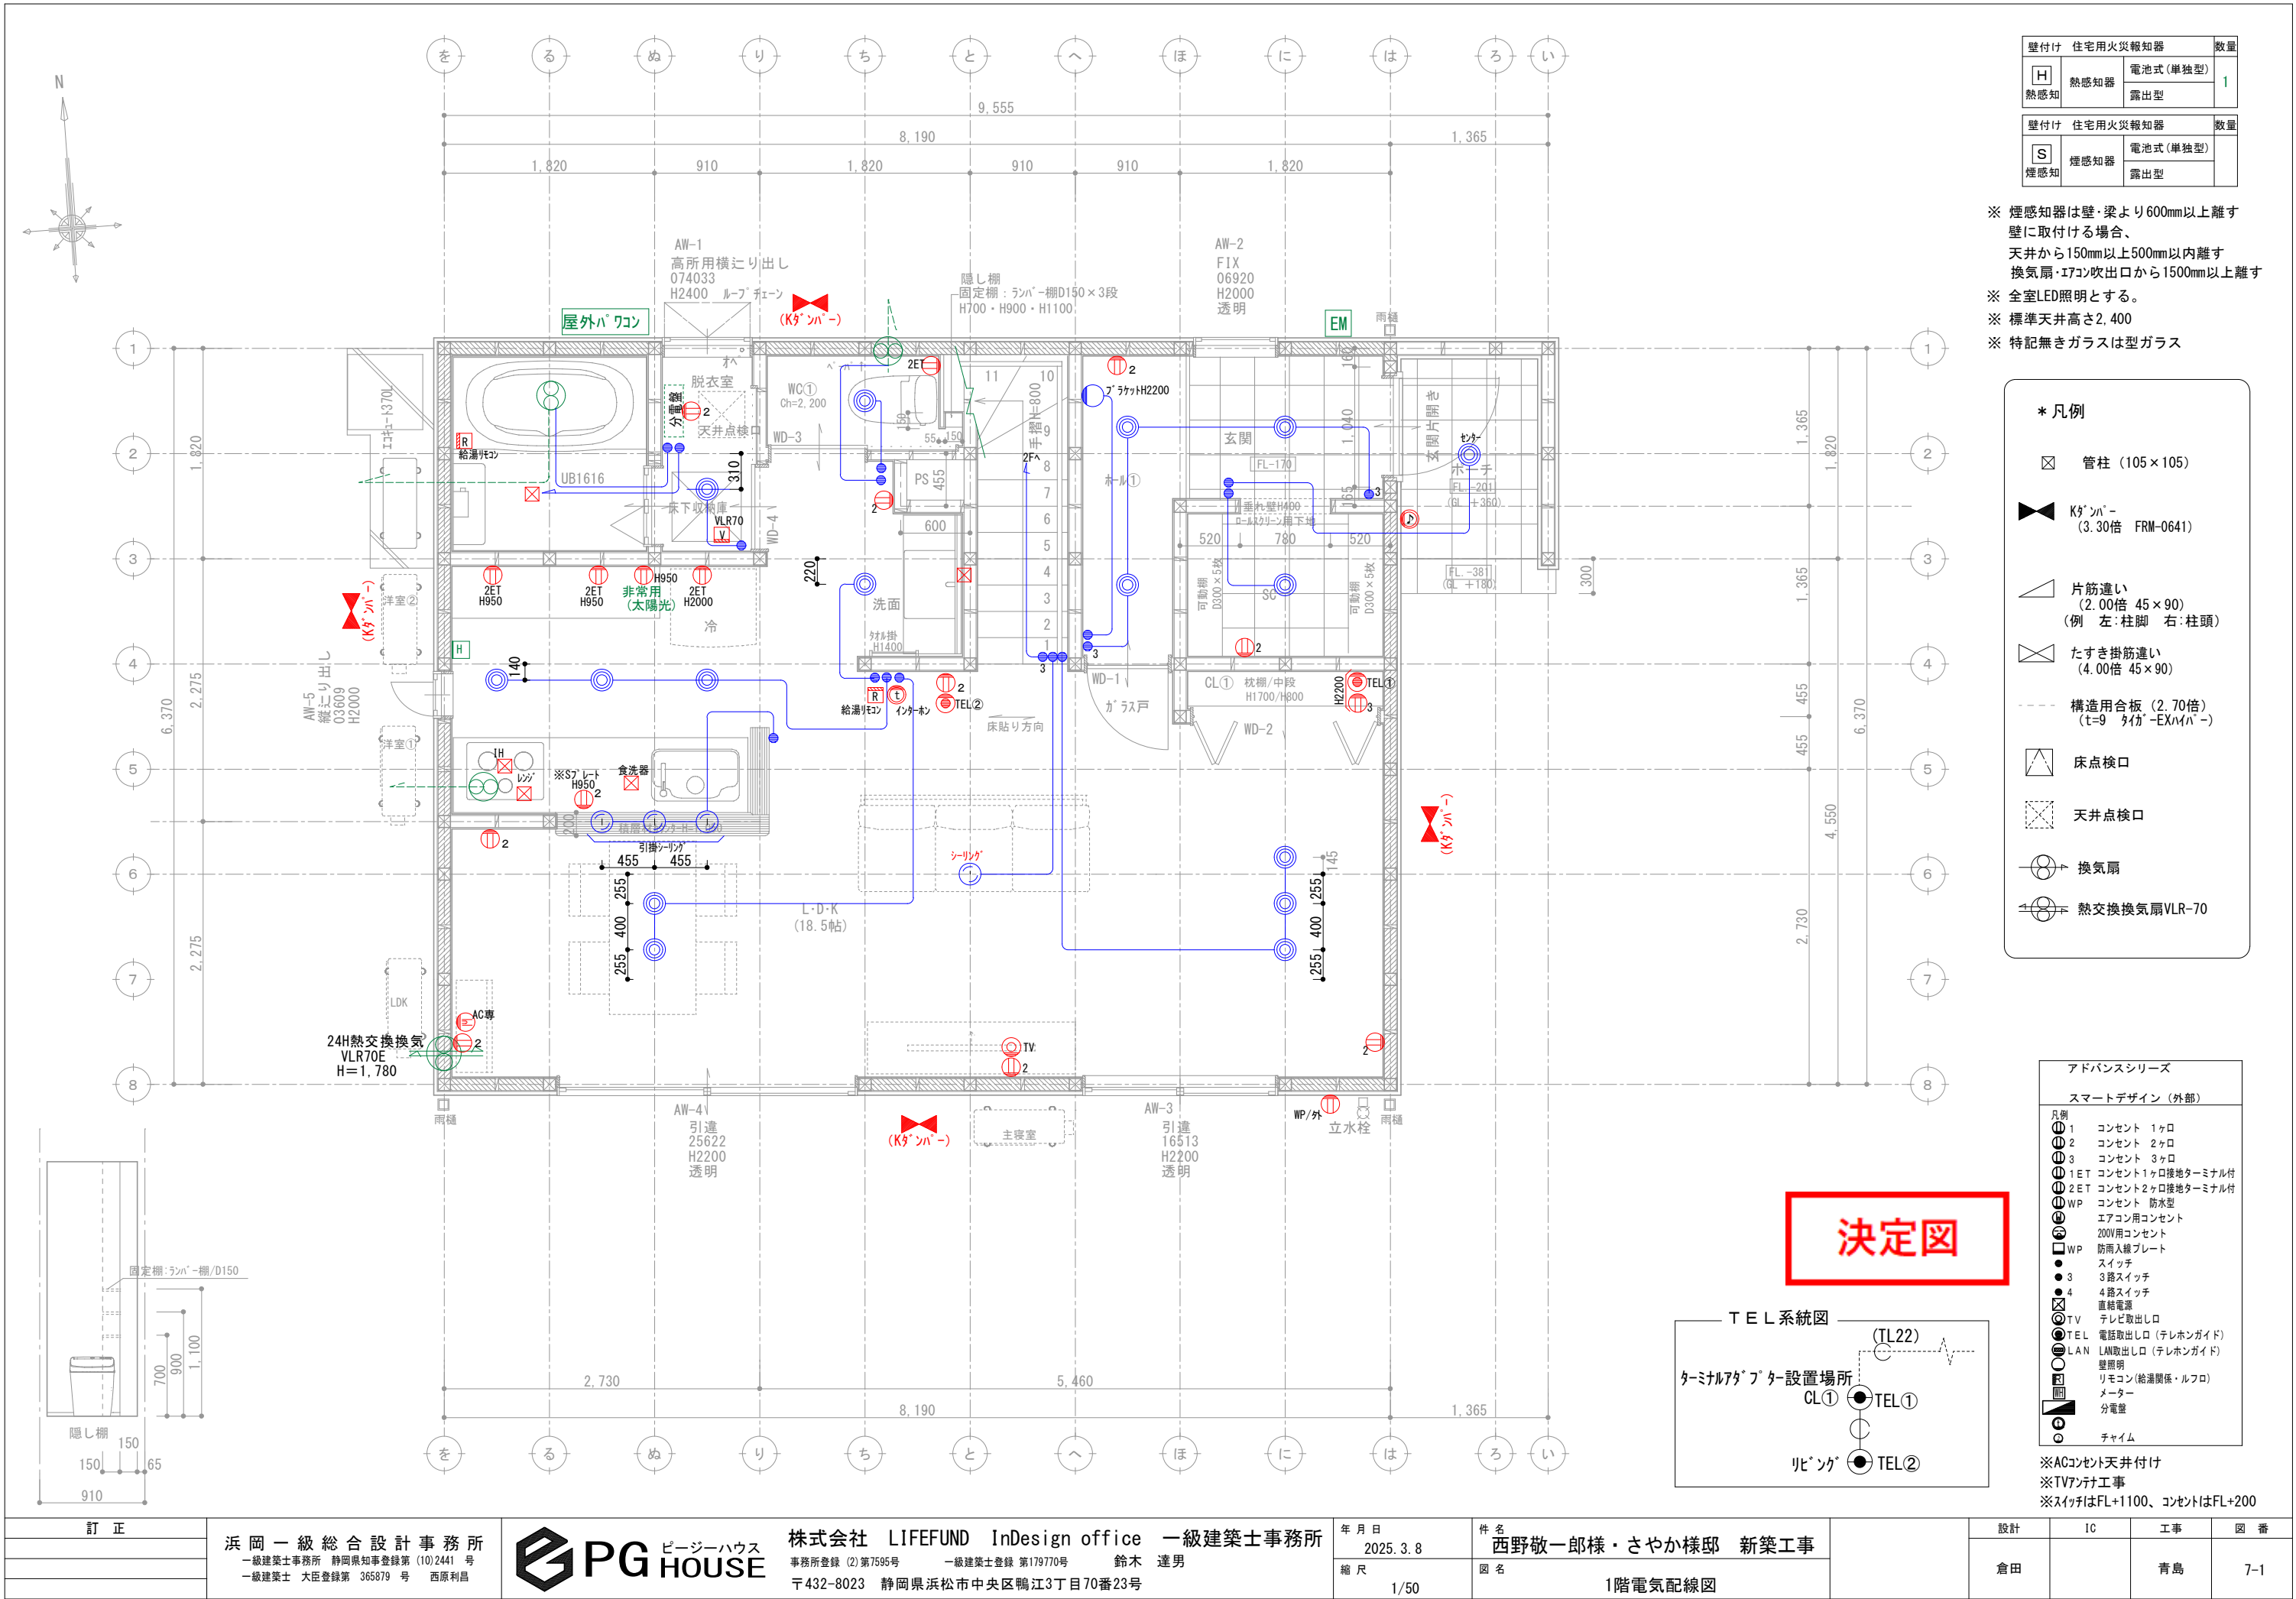

壁付け 住宅用火災報知器			数量
H	熱感知器	電池式(単独型)	1
	熱感知器	露出型	
壁付け 住宅用火災報知器			数量
S	煙感知器	電池式(単独型)	
	煙感知器	露出型	

※ 煙感知器は壁・梁より600mm以上離す
壁に取付ける場合、
天井から150mm以上500mm以内離す
換気扇・エアコン吹出口から1500mm以上離す

※ 全室LED照明とする。

※ 標準天井高さ2,400

※ 特記無きガラスは型ガラス

* 凡例	
☒	管柱 (105×105)
◀▶	Kダクト (3.30倍 FRM-0641)
△	片筋違い (2.00倍 45×90) (例 左:柱脚 右:柱頭)
⊠	たすき掛筋違い (4.00倍 45×90)
---	構造用合板 (2.70倍) (t=9 材種-EXハイバ-)
◻	床点検口
⊠	天井点検口
⊙→	換気扇
⊙⇄	熱交換換気扇VLR-70

アドバンスシリーズ	
スマートデザイン (外部)	
凡例	
①	コンセント 1ヶ所
②	コンセント 2ヶ所
③	コンセント 3ヶ所
①ET	コンセント1ヶ所接地ターミナル付
②ET	コンセント2ヶ所接地ターミナル付
WP	コンセント 防水型
⊙	エアコン用コンセント
⊙	200V用コンセント
WP	防雨入線プレート
●	スイッチ
●	3路スイッチ
●	4路スイッチ
⊙	直結電源
⊙	テレビ取出口
⊙TEL	電話取出口 (テレホンガイド)
⊙LAN	LAN取出口 (テレホンガイド)
⊙	壁照明
⊙	リモコン(給湯関係・ルフロ)
⊙	メーター
⊙	分電盤
⊙	チャイム

※ACコンセント天井付け
※TVアンテナ工事
※スイッチはFL+1100、コンセントはFL+200