


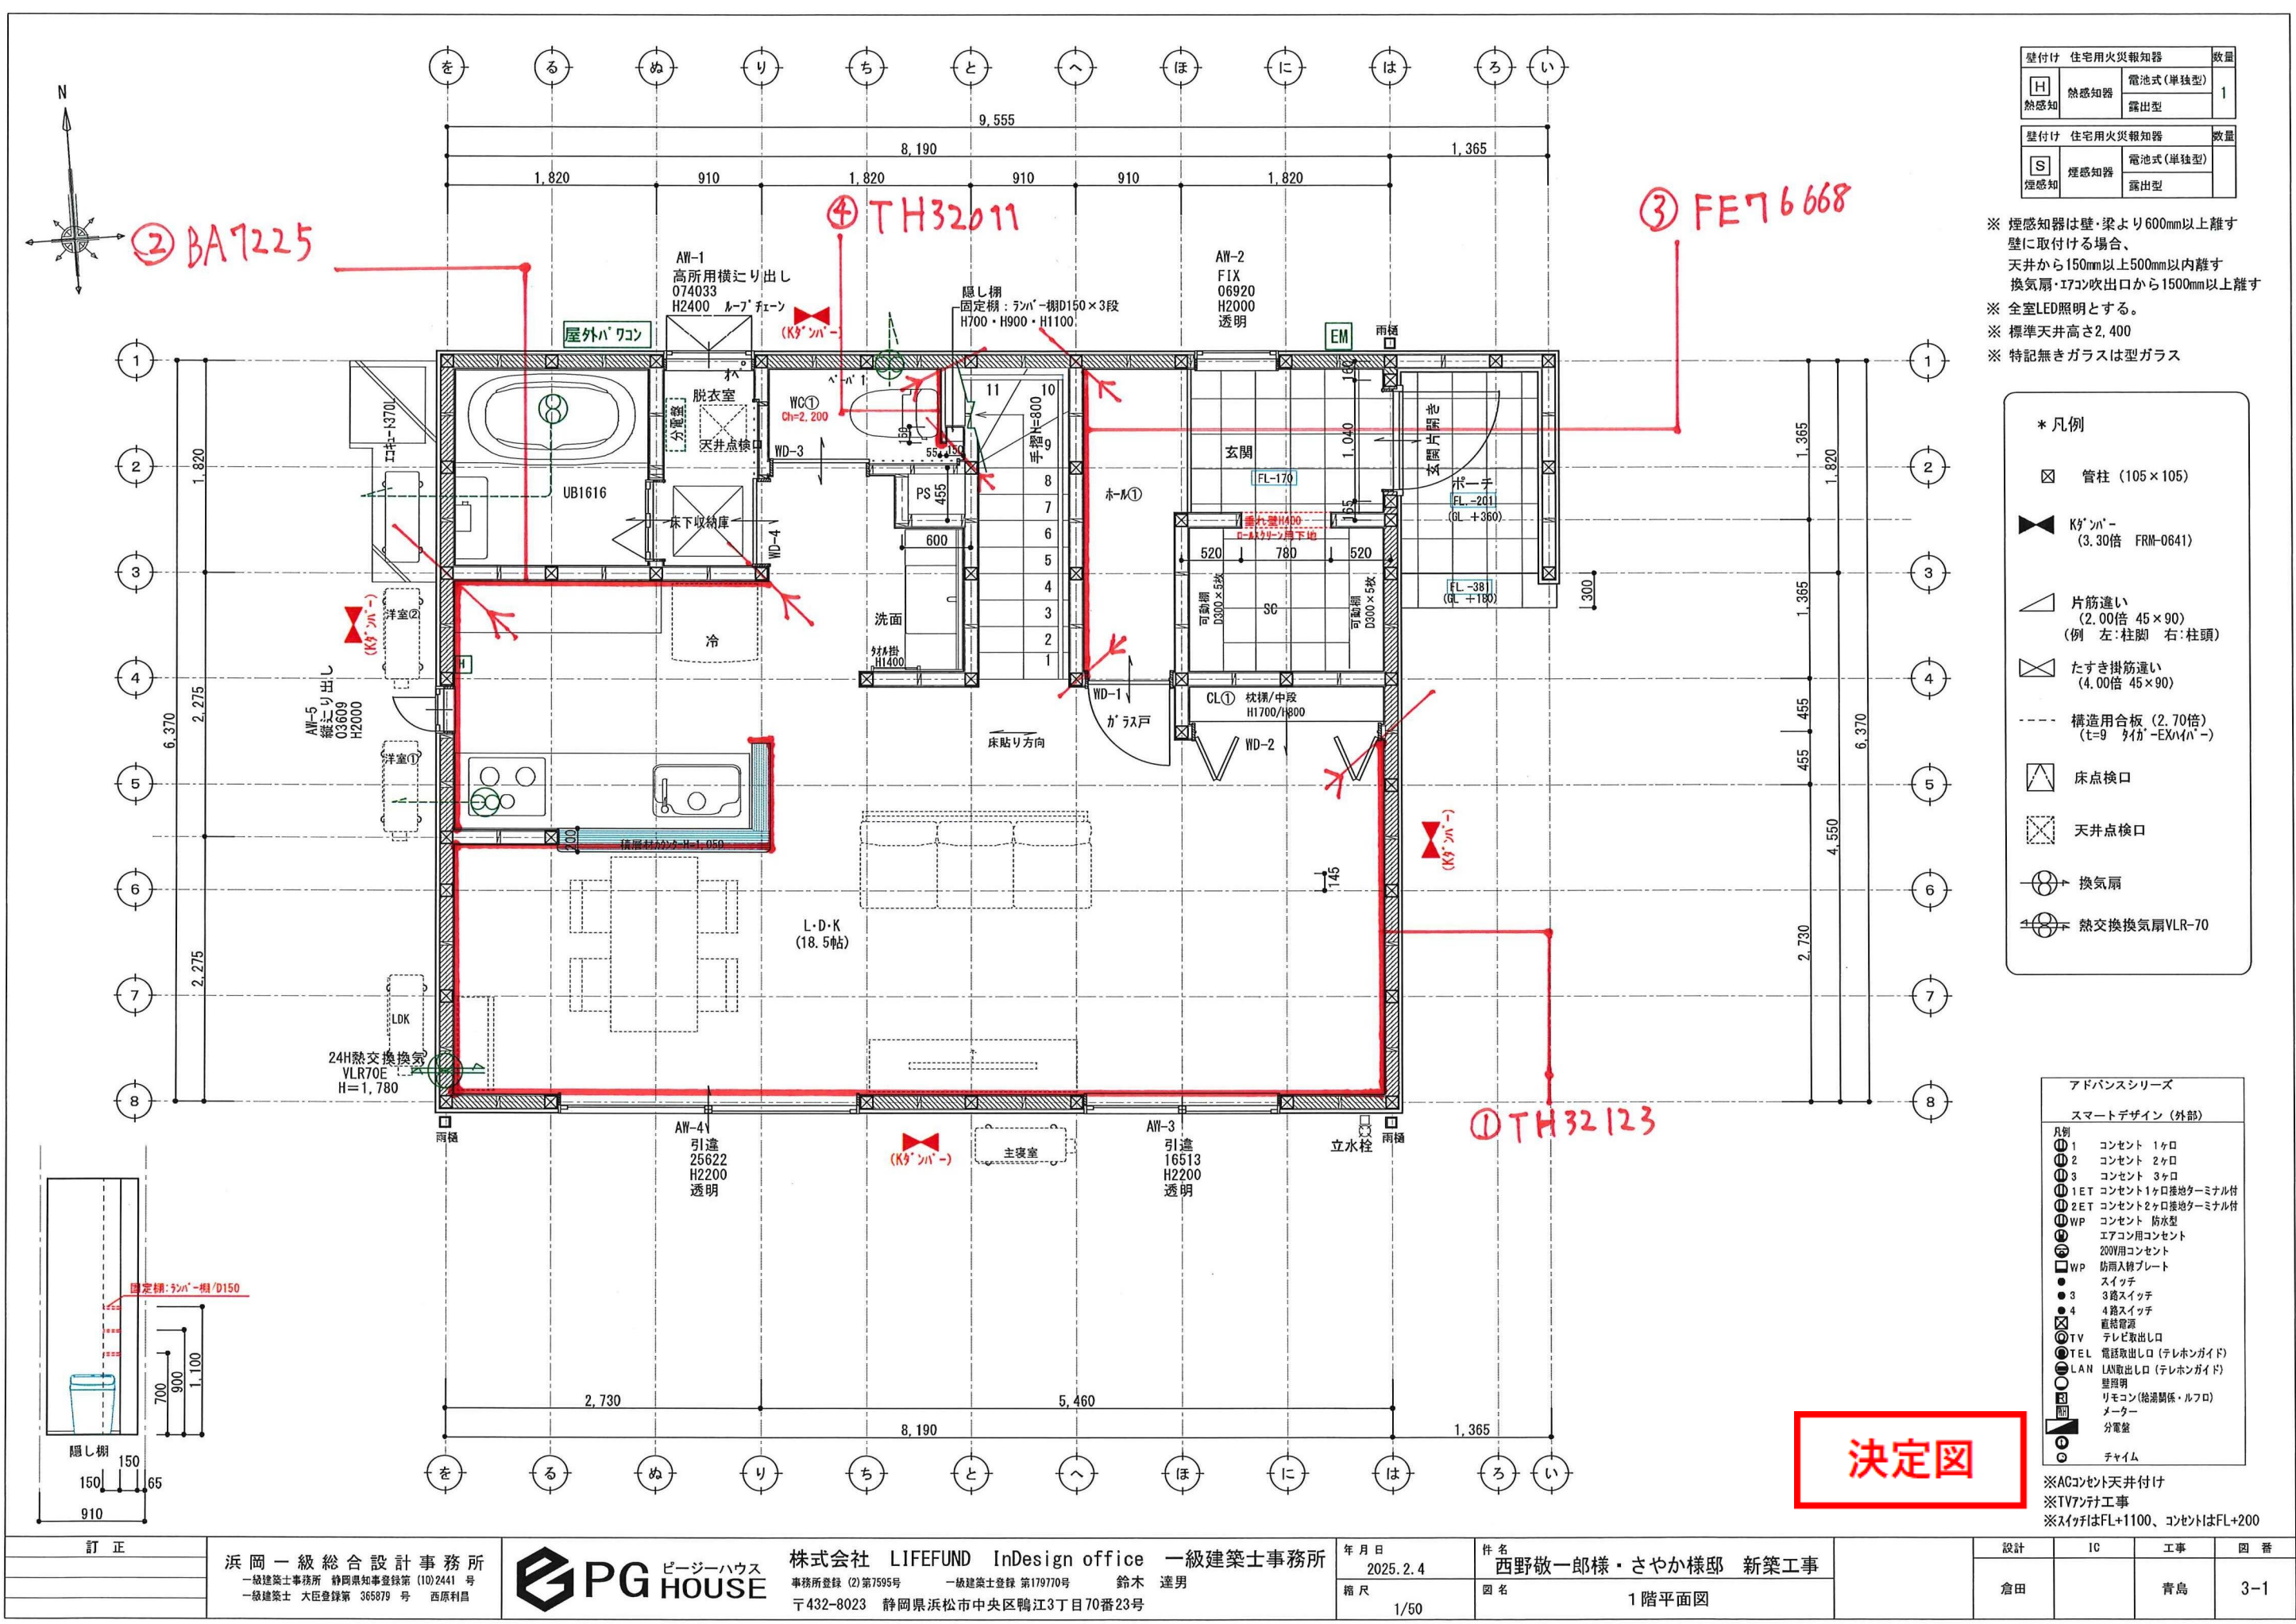

壁付け 住宅用火災報知器			数量
H	熱感知器	電池式(単独型)	1
	熱感知器	露出型	
壁付け 住宅用火災報知器			数量
S	煙感知器	電池式(単独型)	1
	煙感知器	露出型	


※ 煙感知器は壁・梁より600mm以上離す
壁に取付ける場合、
天井から150mm以上500mm以内離す
換気扇・エアコン出口から1500mm以上離す
※ 全室LED照明とする。
※ 標準天井高さ2,400
※ 特記無きガラスは型ガラス

- * 凡例
- 管柱 (105×105)
 - Ky'ンバー (3.30倍 FRM-0641)
 - 片筋違い (2.00倍 45×90)
(例 左:柱脚 右:柱頭)
 - たすき掛筋違い (4.00倍 45×90)
 - 構造用合板 (2.70倍)
(t=9 タイガ-EXVIA-)
 - 床点検口
 - 天井点検口
 - 換気扇
 - 熱交換換気扇VLR-70

アドバンスシリーズ	
スマートデザイン (外部)	
凡例	
①	コンセント 1ヶ所
②	コンセント 2ヶ所
③	コンセント 3ヶ所
1ET	コンセント1ヶ所接地ターミナル付
2ET	コンセント2ヶ所接地ターミナル付
WP	コンセント 防水型
④	エアコン用コンセント
⑤	200V用コンセント
WP	防雨入替プレート
⑥	スイッチ
⑦	3路スイッチ
⑧	4路スイッチ
⑨	直結電源
TV	テレビ取出口
TEL	電話取出口 (テレホンガイド)
LAN	LAN取出口 (テレホンガイド)
⑩	壁照明
⑪	リモコン (給湯関係・ルフロ)
⑫	メーカー
⑬	分電盤
⑭	チャイム

※ACコンセント天井付け
※TVアンテナ工事
※スイッチはFL+1100、コンセントはFL+200

決定図

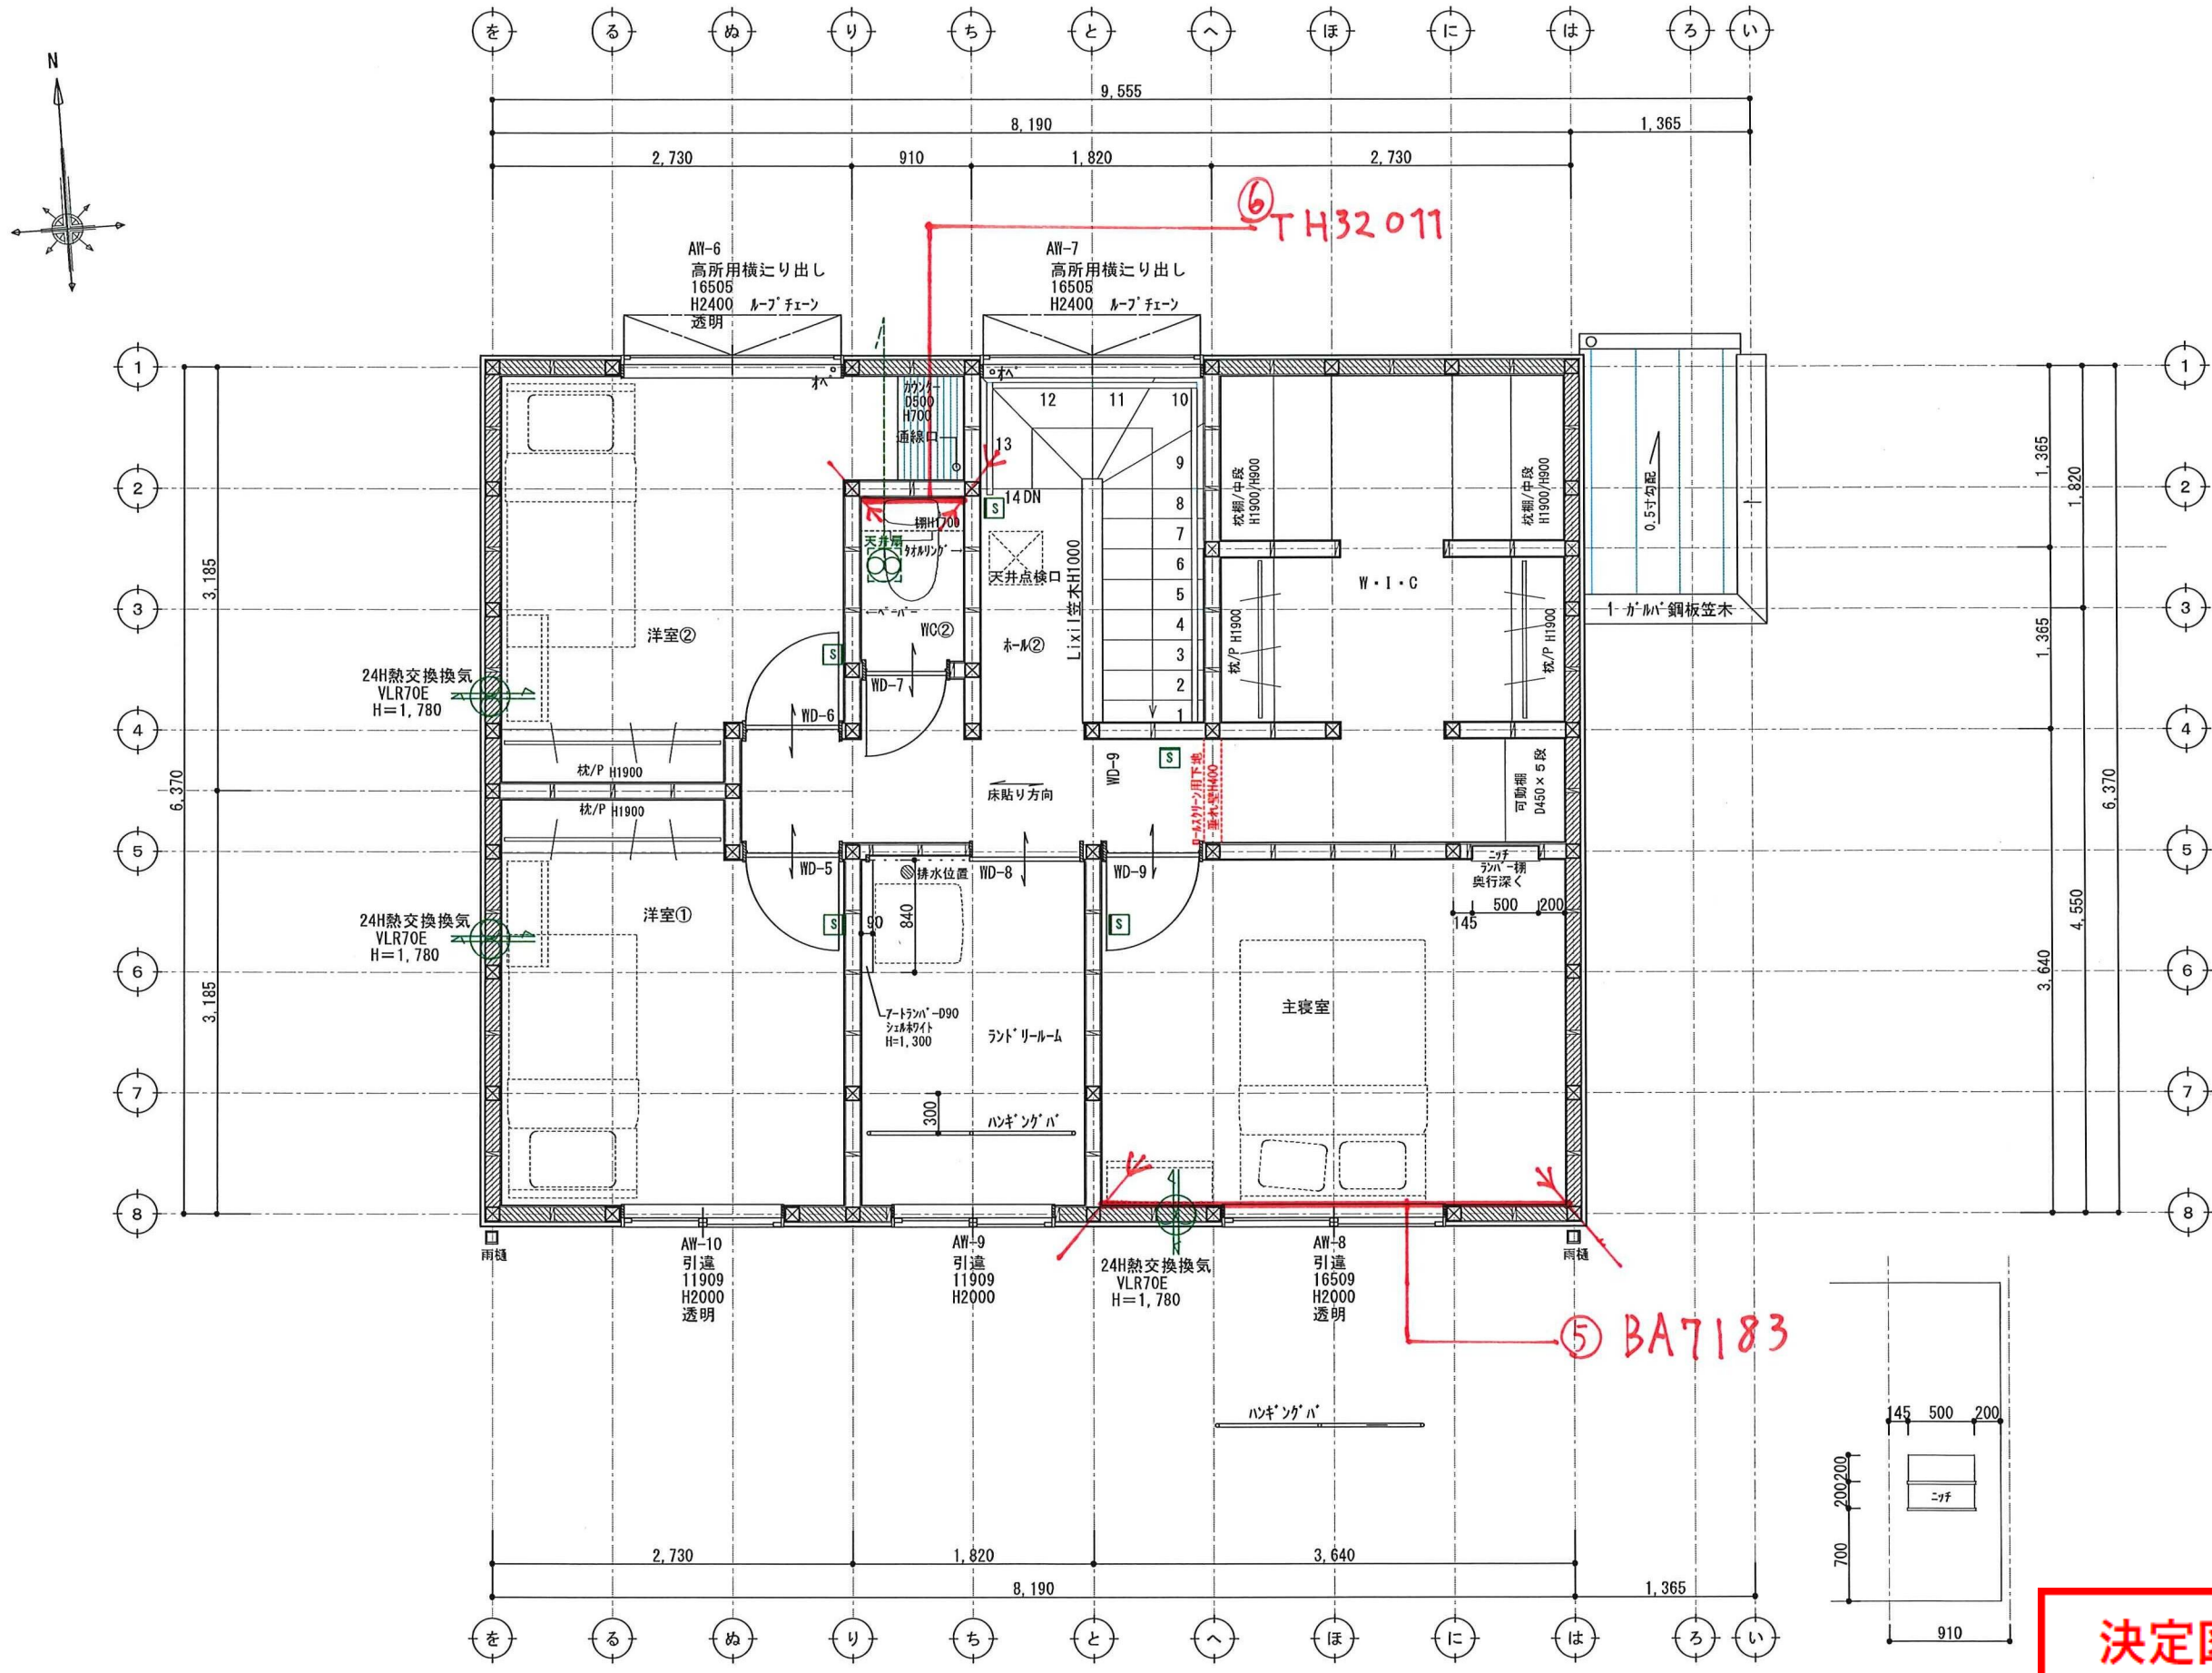

壁付け 住宅用火災報知器			数量
H 熱感知	電池式(単独型)		4
	露出型		
壁付け 住宅用火災報知器			数量
S 煙感知	電池式(単独型)		4
	露出型		

※ 煙感知器は壁・梁より600mm以上離す
壁に取付ける場合、
天井から150mm以上500mm以内離す
換気扇・エアコン吹出口から1500mm以上離す

※ 全室LED照明とする。

※ 標準天井高さ2,400

※ 特記無きガラスは型ガラス

- * 凡例
- ☒ 管柱 (105×105)
 - ▲ Kダクト (3.30倍 FRW-0641)
 - △ 片筋違い (2.00倍 45×90)
(例 左:柱脚 右:柱頭)
 - ⊠ たすき掛筋違い (4.00倍 45×90)
 - 構造用合板 (2.70倍)
(t=9 タイガ EXHAIR)
 - ⬆ 床点検口
 - ⬆ 天井点検口
 - ⊕ 換気扇
 - ⊕ 熱交換換気扇VLR-70

アドバンスシリーズ	
スマートデザイン (外部)	
凡例	
①	コンセント 1ヶ所
②	コンセント 2ヶ所
③	コンセント 3ヶ所
①ET	コンセント1ヶ所接地ターミナル付
②ET	コンセント2ヶ所接地ターミナル付
WP	コンセント 防水型
⊕	エアコン用コンセント
⊕	200V用コンセント
WP	防雨入線プレート
スイッチ	スイッチ
3	3路スイッチ
4	4路スイッチ
直結電線	直結電線
TEL	テレビ取出口
TEL	電話取出口 (テレホンガイド)
LAN	LAN取出口 (テレホンガイド)
照明	照明
リモコン	リモコン (給湯関係・ルーフ)
メーター	メーター
分電盤	分電盤
チャイム	チャイム

※ACコンセント天井付け
※TVアンテナ工事
※スイッチはFL+1100、コンセントはFL+200

決定図