



面

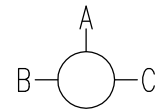

A面




C面

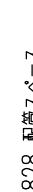[illegible]

【ご注意】

- 壁面仕上材（キッチンパネル・タイルなど）の貼付下端位置が変わります。〔機能図参照〕
- 記載のキャビネット寸法は扉前面までの呼び寸法です。キャビネット本体の寸法・扉厚等は商品ガイドの巻末資料をご確認ください。
- 記載のワークトップ、カウンター、エンドパネル、サイドパネルの寸法は呼び寸法です。詳細寸法は商品ガイドの巻末資料をご確認ください。
- レンジフード電源プラグ仕様：2芯電源プラグ（アース工が必要です。）

特記事項 扉色 VK5:グレンジュスタック 取手 「M」スリム取手（ブラック） ワークトップカラー 【DW】ソルティホワイト	物件名	西野敬一 様邸	案件No.	図面名	担当	図面	図番
			A2501DD0EBVMG	レイアウト図	栗野 友仁		
	仕様	ES21	見積No.	縮尺	日付		株式会社 LIXIL
			M25016242201-006-2	1/30	2025.02.17		

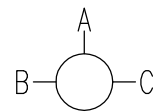

Technical drawing of the 'Eco' model kitchen unit, showing a top-down view with dimensions and numbered callouts (1-14) for various components.

Overall Dimensions:

- Width: 2550 (トップ寸法)
- Height: 850

Internal Dimensions and Callouts:

- Callout 1: 電源・注意 (Power/Note)
- Callout 2: 600 (水栓用) ※注3 (600mm Water Tap Use) ※注3
- Callout 3: 420 (食洗用) (420mm Dishwasher Use)
- Callout 4: 70 (60 (食洗用)) (70mm (60mm Dishwasher Use))
- Callout 5: 60 (食洗用) (60mm Dishwasher Use)
- Callout 6: 160 (160mm)
- Callout 7: 1550 (水栓用) 倒板取付 ※注3 (1550mm Water Tap Use) 倒板取付 ※注3
- Callout 8: 1465 (食洗用) ※注2 (1465mm Dishwasher Use) ※注2
- Callout 9: 1670 給湯・給水位置 (水栓金具) (1670mm Hot Water/Supply Water Position (Water Tap Fitting))
- Callout 10: 1950 排水位置 (シンク) (1950mm Drain Position (Sink))
- Callout 11: 270 (270mm)
- Callout 12: 350 (IH用) (350mm IH Use)
- Callout 13: 1130 排水・給湯 (水) 位置 (食洗) (1130mm Drain/Hot Water (Water) Position (Dishwasher))
- Callout 14: 2250 (IH用) ※注4 (2250mm IH Use) ※注4

Other Dimensions:

- 900 製品寸法 (900mm Product Dimension)
- 900 (900mm)
- 615 排気ダクト径150 (615mm Exhaust Duct Diameter 150)
- 100 (フード用) 2芯 ※注1 (100mm (Hood Use) 2-core) ※注1
- 850 (850mm)
- 1650 (1650mm)
- 800 (800mm)
- 700 (700mm)
- 665 (665mm)
- 35 (35mm)
- 50 (50mm)
- 2350 (2350mm)
- CH= 2400 (CH= 2400mm)

注1) 125V・15A 2極接地極付アースターミナル付コンセント【専用】(フード用)

注2) 125V・15A 2極接地極付アースターミナル付コンセント 側板取付【専用】

注3) 125V・15A 2極接地極付コンセント(側板取付)


注4) 250V・30A 2極接地極付コンセント【専用】

【ご注意】


- 壁面仕上材(キッチンパネル・タイルなど)の貼付下端位置が変わります。[機能図参照]
- 記載のキャビネット寸法は扉前面での呼び寸法です。キャビネット本体の寸法・扉厚等は商品ガイドの巻末資料をご確認ください。
- 記載のワークトップ、カウンター、エンドパネル、サイドパネルの寸法は呼び寸法です。詳細寸法は商品ガイドの巻末資料をご確認ください。
- 電気・ガス・給排水・換気等は法令・規定に従って有資格者が行ってください。
- 水道工事は排水配管工事となります。
- 取付・設置に際し、各製品の取付・設置説明書や図面の機能図を必ずお読み下さい。
- 内線規程上、各機器のプラグ仕様に問わず建築側には接地極付コンセントを推奨しています。
- レンジフードにはアース線は同梱されておりません。別途 御用意願います。
- レンジフード電源プラグ仕様: 2芯電源プラグ(アース工事が必要です。)
- 壁付けでレンジフード上に天井フィラーを設置する場合は、横壁に下地が必要となります。下地位置は、機能図を参照願います。
- 食洗機内配管の詳細については必ず別添の機能図をご確認ください。
- 食器洗い乾燥機配管は、給水接続か給湯接続かお客様に確認したうえで施工願います。

特記事項 扉色 VK5:グレージュスタック 取手 [M]スリム取手 (ブラック) ワークトップカラー 【DW】ソルティホワイト	物件名 西野敬一 様邸	案件No.	図面名	担当	図面	図番 : 株式会社 LIXIL
		A2501DDDD0EBVMG	納まり図	栗野 友仁		
	仕様 ES21	見積No.	縮尺	日付		
		M25016242201-006-2	1/30	2025.02.17		

B面

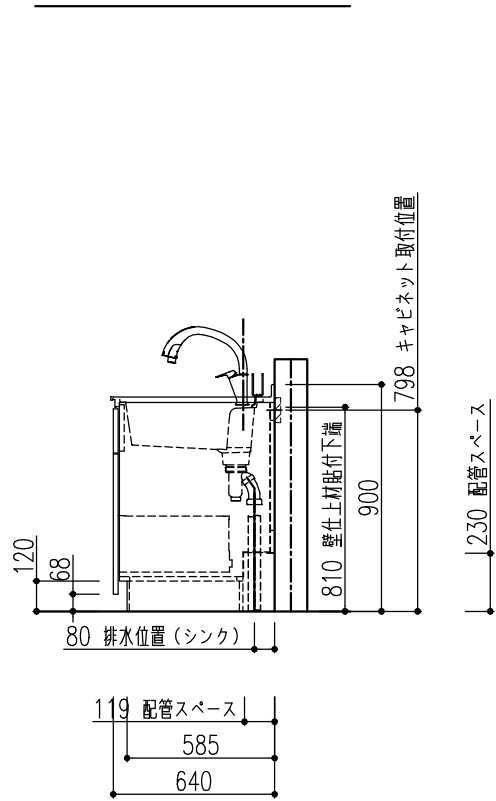

C面

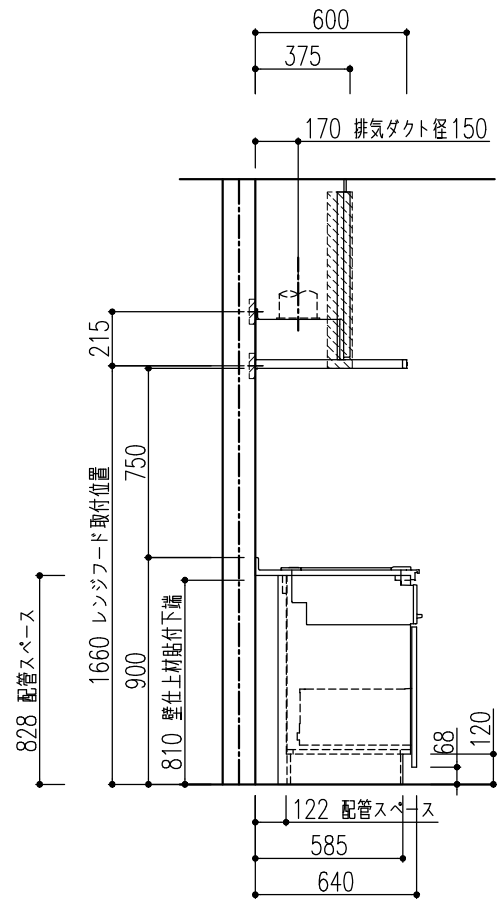


特記事項 扉色 VK5:グレージュスタック 取手 [M]スリム取手 (ブラック) ワークトップカラー 【DW】 ソルティホワイト	物件名	西野 敬一 様邸	案件No.	図面名	担当	図面	図番
	仕様	ES21	A2501DDD0EBVMG	納まり図	栗野 友仁		株式会社 LIXIL
			見積No.	縮尺	日付		
			M25016242201-006-2	1/30	2025.02.17		

■壁面仕上材（キッチンパネル）取付注意事項〔貼付向き〕

●キッチンパネルの貼付向き


キッチンパネルの貼付向きにご注意ください。

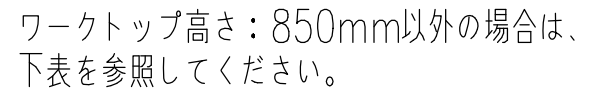

ワークトップ高さ	キッチンパネル 貼付下端位置
900	860
875	835
825	785
800	760

●上表はキッチンパネルの場合です。ステンレスパネルの場合は、キッチンパネルの「取付・設置説明書」を参照してください。

《ワークトップ高さ：850mmの場合》

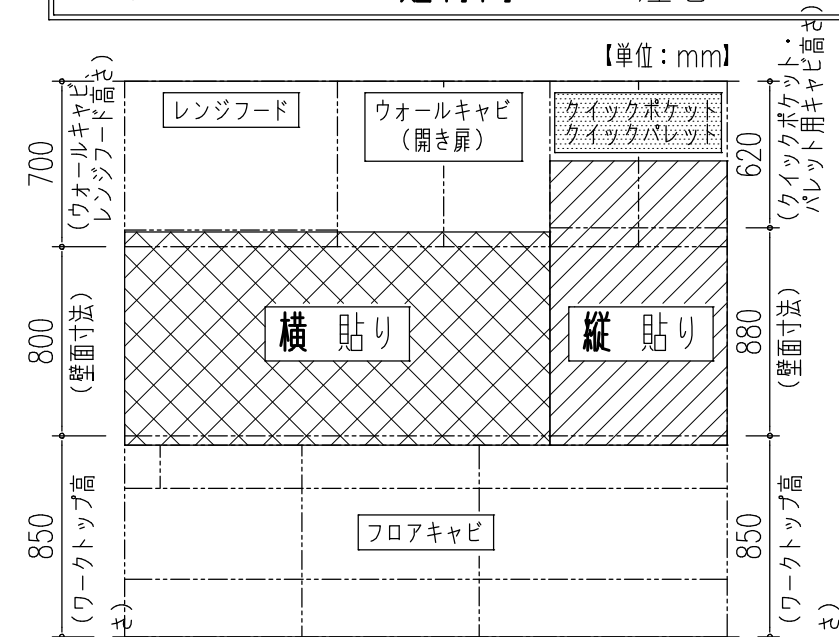


《キッチンパネル 貼付方向》
総高さ：2350mmの場合

	ウォールキャビ		
	開き扉		クイックボケット クイックバレット
	H700	H600 H500	H700 (620) H600 (520)
キッチンパネル 貼付方向	横	縦	

【ご注意】
リシエル以外のクイックパレットは、
キャビネットの背板高さがショート
（-80mm）してありませんので、
『開き扉』のキッチンパネル貼付方向
に合せてください。

《バックガード：なし、ワークトップ高さ：850mm、ウォールキャビ高さ：700mmの場合》

■レンジフード取付注意事項（壁面取付時）

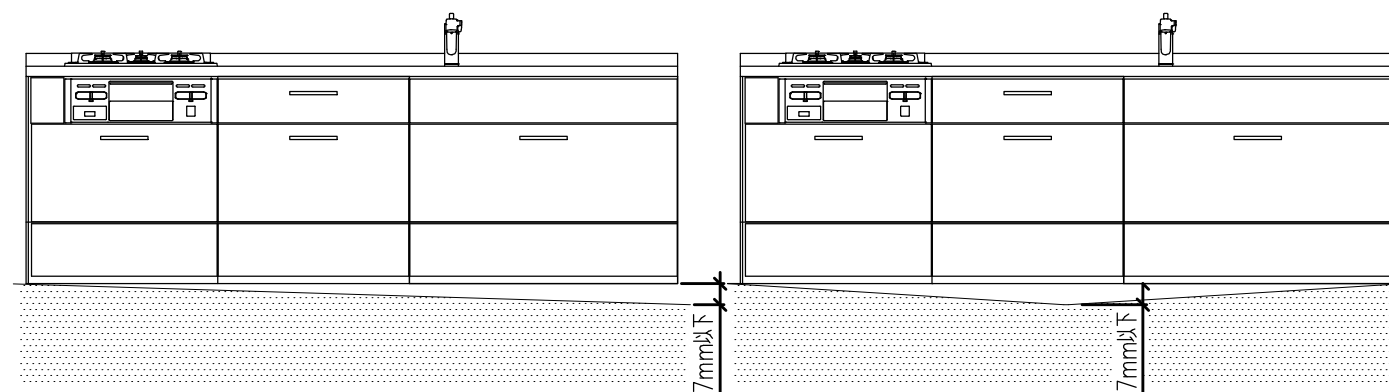


床の不陸は、7mm以下に抑えるようにしてください。不陸が大きい場合は、現場責任者に床の修正を依頼してください。
※キャビネット取付時には不陸調整スペーサー等で水平になるように設置してください。


レンジフードを取付ける場合は下地の桱が厚み30 mm以上、幅100 mm以上、
ビス固定位置が桱の端部から25 mm以上であることを確認してください。
また、壁強度などの詳細は「レンジフード設置説明書」を必ず事前に確認してください。

取付位置については、取付設置図を確認してください。


参考図_CLS、SER、NST、ASR、ADR、RVJ、GSR、BFRS、TARシリーズ
(※RVJ、GSRシリーズの場合はレンジフードパネルの取付下地は不要です。)

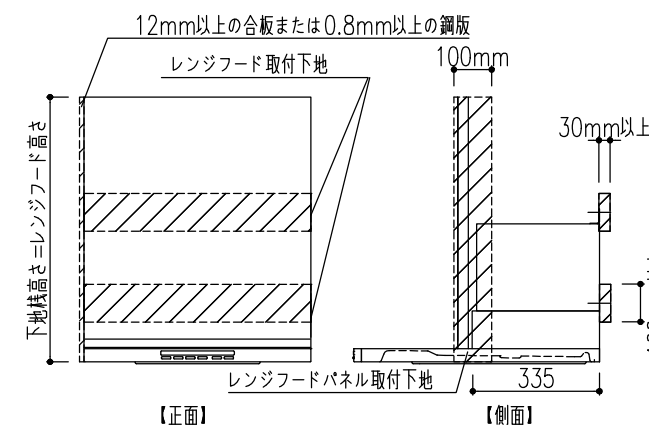

参考図 FED、HVR、NSDシリーズ（サイドマントルタイプ）

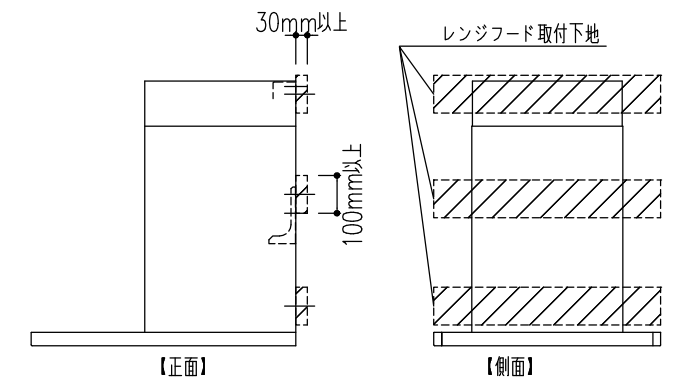


参考図 NBHシリーズ

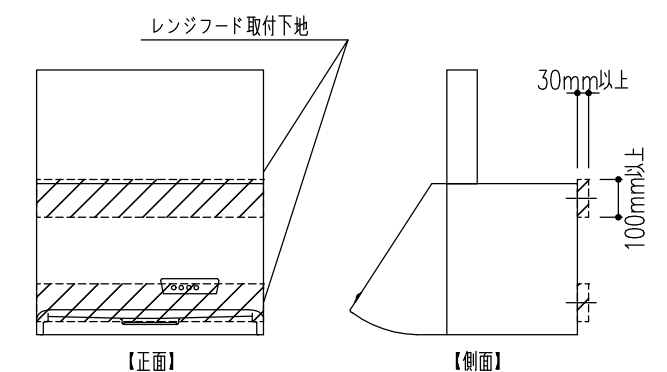


特記事項 扉色 VK5:グレンジュスタック 取手 [M]スリム取手（ブラック） ワークトップカラー 【DW】ソルティホワイト	物件名	西野敬一 様邸	案件No.	図面名	担当	図面	図番
			A2501DD00EBVMG	機能図	栗野 友仁		株式会社 LIXIL
	仕様	ES21	見積No.	縮尺	日付		
			M25016242201-006-2		2025.02.17		

■天井フィラーの取付（レンジフード上部）

レンジフード横に壁がくるレイアウト時は、横壁にも取付桎が必要になります。

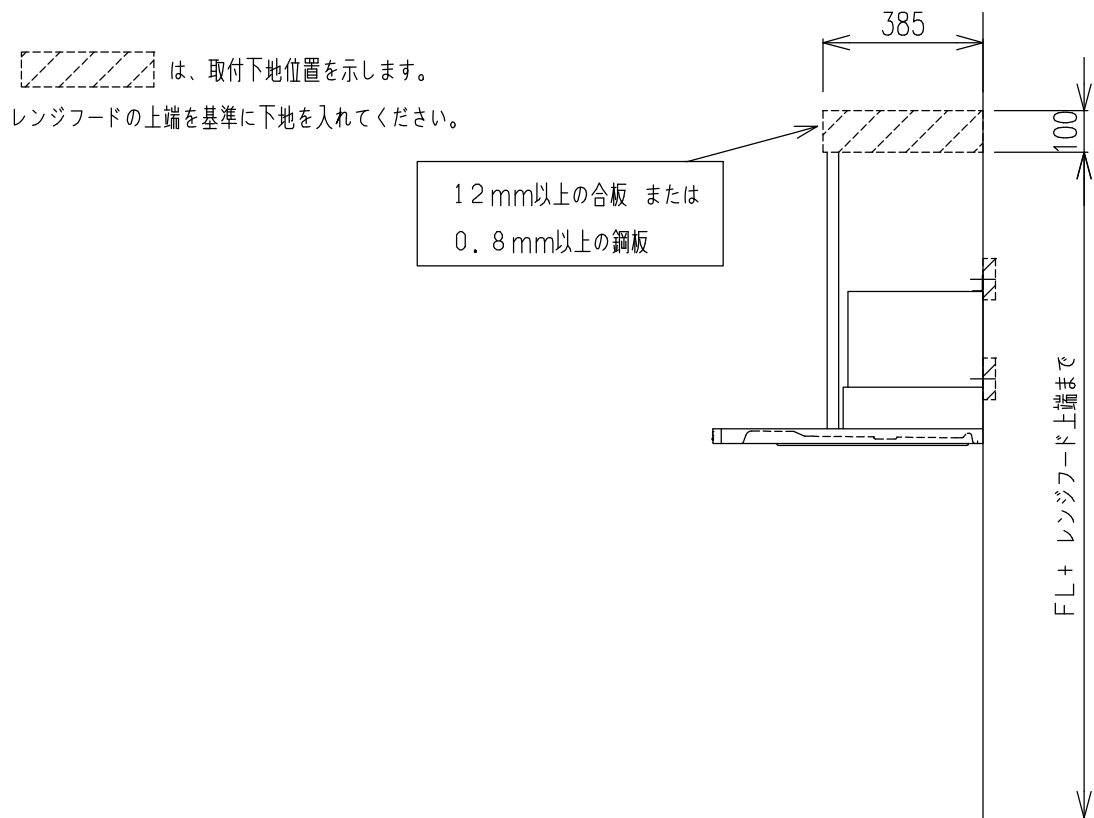

■ ASRフード

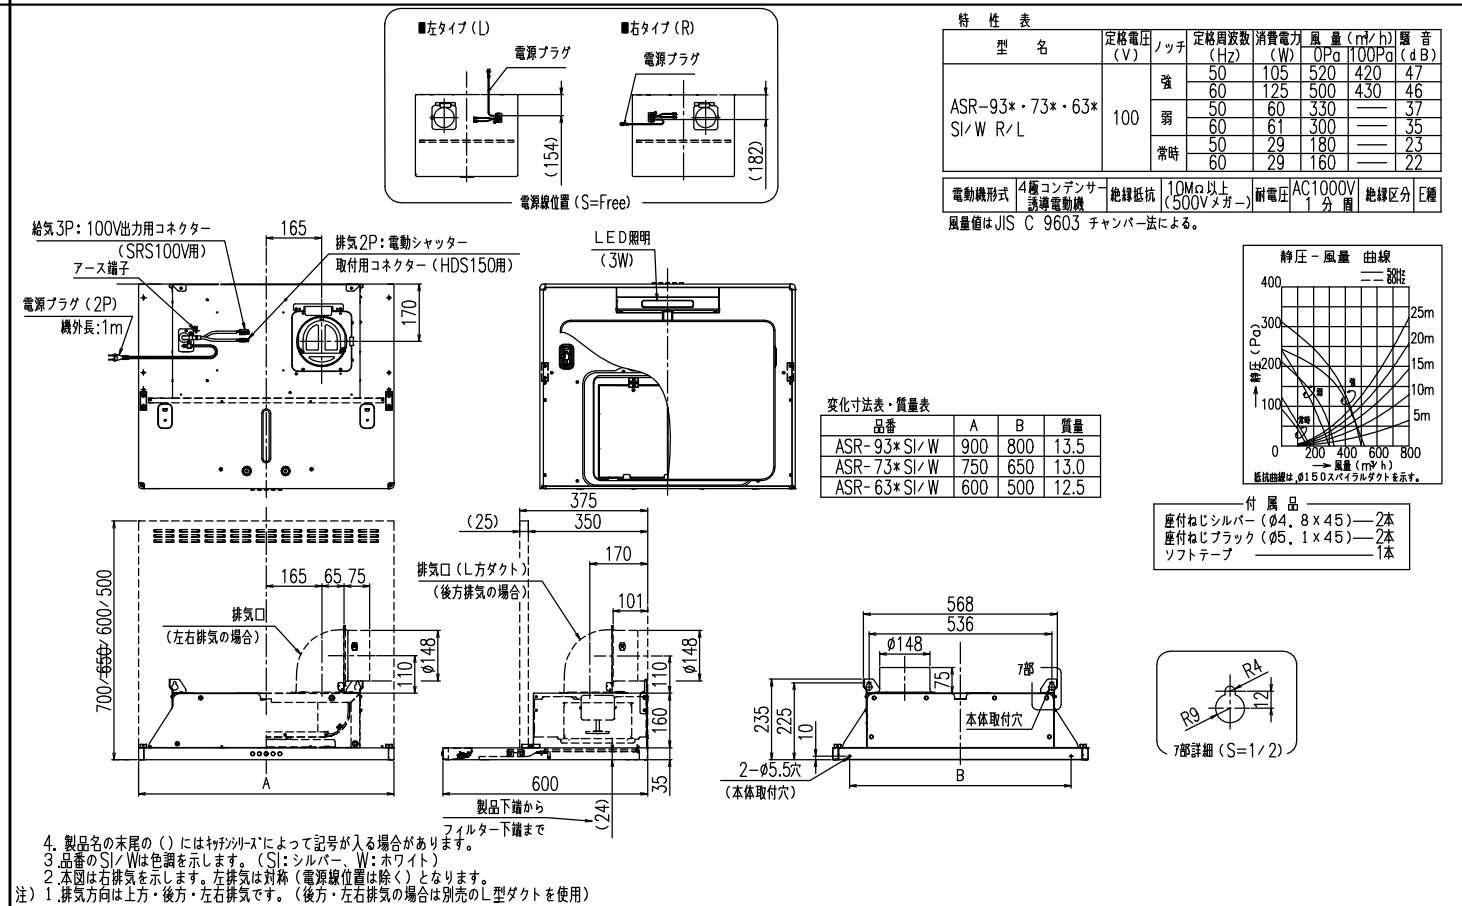


■ IHヒーター用コンセント推奨位置図 / 壁付設置の場合

※コンセントや電源プラグが、引き出しおよびIHヒーター用仕切板（オプション）に接触しないように注意してください。


※木製キャビネットの配管スペース付キャビネットを使用する場合は点検口裏の配管スペース内にコンセントを設置してください。

キッチン高さ	電源線高さ
800	400
850	450
900	500

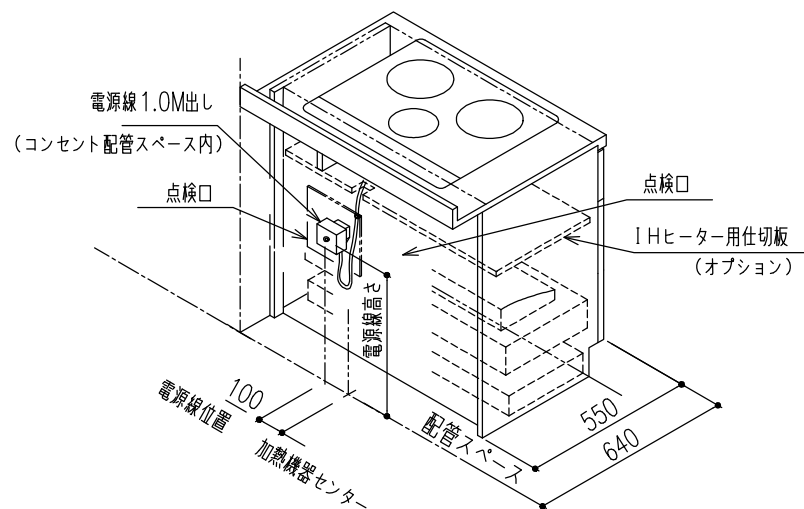

注意：引き出しおよびIHヒーター用仕切板（オプション）に接触しないように上記寸法を参照してください。

■食器洗い乾燥機内配管図 床立上げ配管例

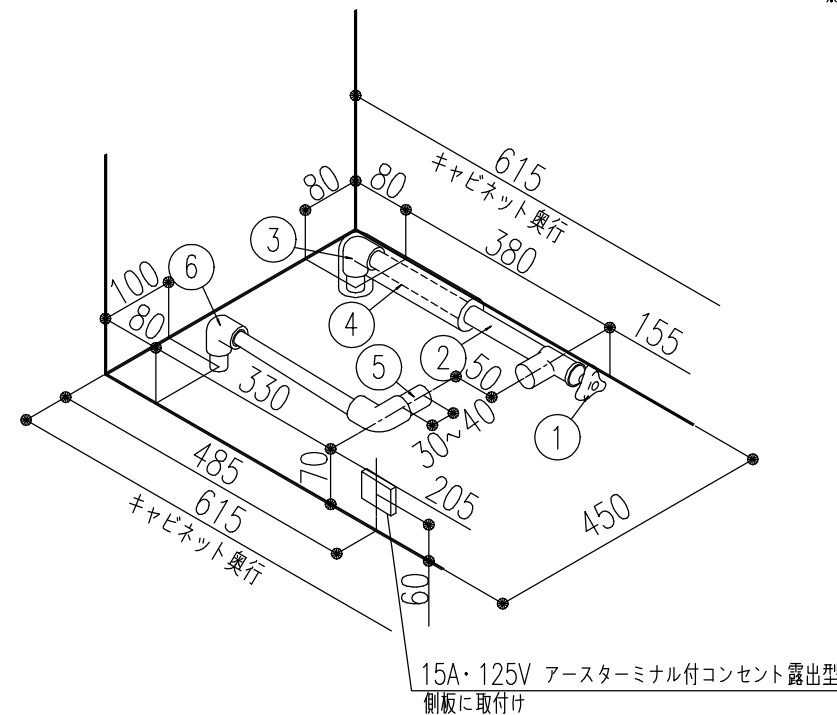

注意：配管立ち上げ位置は必ず本図の位置に立ち上げて下さい。

※給水接続か給湯接続かお客様に確認したうえで施工願います。

給水（給湯の場合は耐熱配管）

①アンゲル型止水栓（ハンドル式・固定ゴマタイプ）

※必ず固定ゴマタイプをご使用ください。

落としゴマタイプを使用すると、水栓内でコマが移動し、

ゴトゴト音を生じる恐れがあります。

②硬質塩化ビニルライニング鋼管（相当品）

③RC1/2ソケット

④断熱材 (Φ48)

排水（耐熱塩ビ使用のこと）

⑤排水パイプHT20


⑥HTエルボ

※配水管先端のエルボを上向きにしないでください。


キャビネットに当たるため、排水ホース折れの原因になります。

特記事項 屋色 VK5:グレージュスタッコ 取手 [M]スリム取手(ブラック) ワークトップカラー 【DW】 ソルティホワイト	物件名	西野敬一 様邸	案件No.	図面名	担当	図面	図番 : 株式会社 LIXIL
			A2501DDD0EBVMG	機能図	葉野 友仁		
	仕様	ES21	見積No.	縮尺	日付		
			M25016242201-006-2		2025.02.17		

■ 止水栓図（床立上げ）

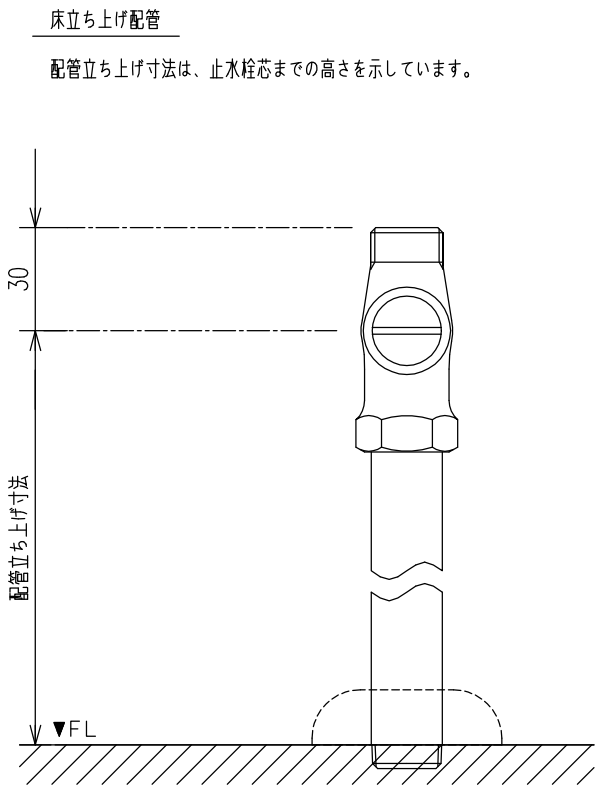

■ タッチレス水栓ナビッシュ 推奨電源位置図



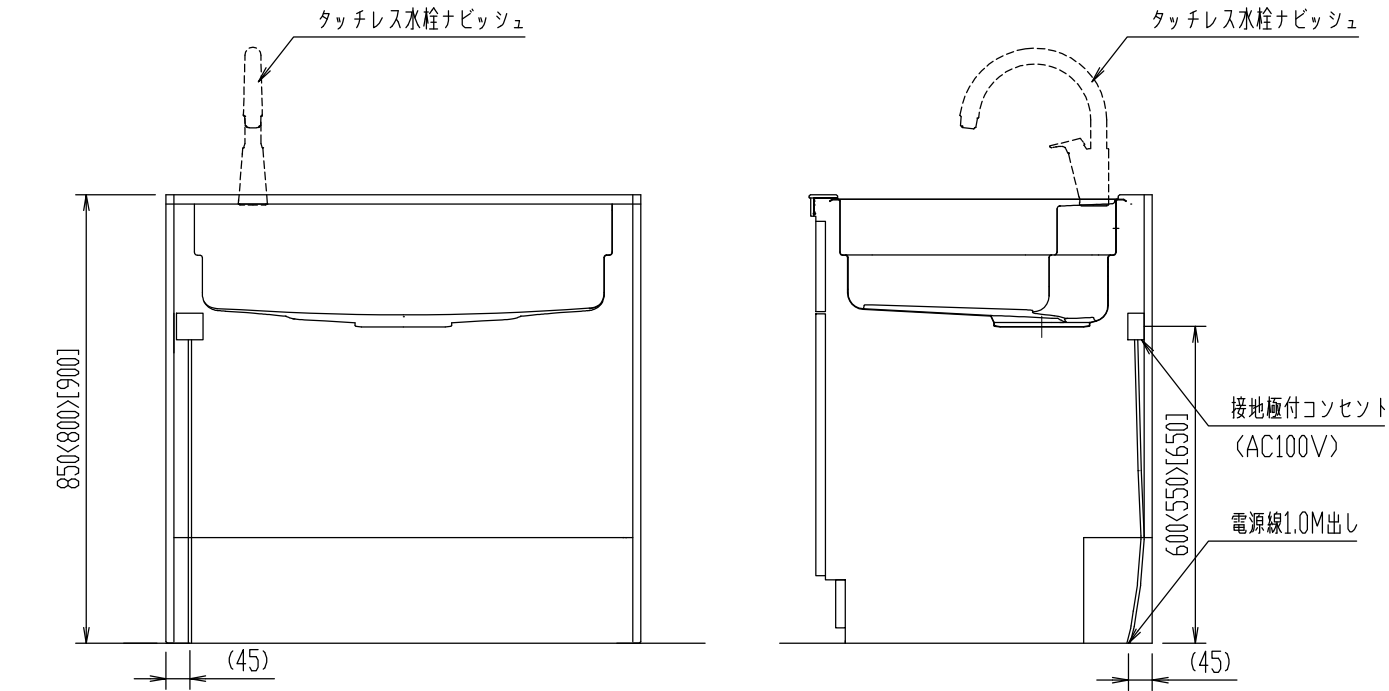


○水栓がシンク右側の場合、電源位置は左右対象の位置にしてください。
○＜＞内寸法はワークトップ高さ80cmの場合、[]内寸法はワークトップ高さ90cmの場合。

■ キッチン取付者さま向け 動画コンテンツ ■
商品取付けの注意点を2次元コードでご視聴いただけます。
取付日より前に、是非ご確認ください。




1 ページ目

1 $\wedge^0$ — ジ

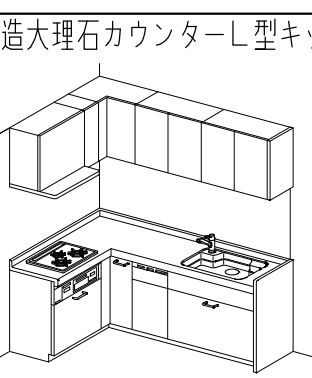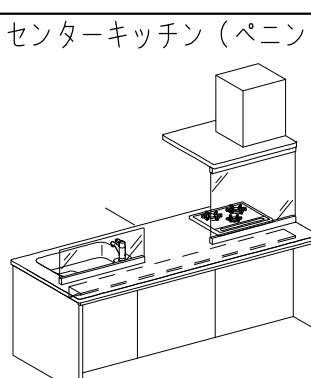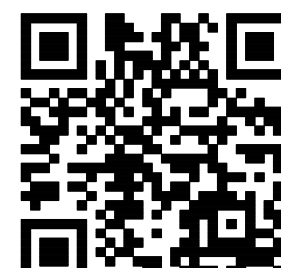人造大理石カウンターL型キッチン   作成日：2024年02月07日	センターキッチン（ペニンシュラ型）   作成日：2024年02月07日		
---	---	--	--

特記事項 扉色 VK5:グレージュスタック 取手 M スリム取手 (ブラック) ワークトップカラー 【DW】ソルティホワイト		物件名	西野敬一 様邸		案件No.	図面名	担当	図面	図番 :
		A2501DDD0EBVMG			機能図	栗野 友仁			
		仕様	ES21	見積No.	縮尺	日付		株式会社 LIXIL	
				M25016242201-006-2		2025.02.17			

■ キッチン取付者さま向け 動画コンテンツ ■
商品取付けの注意点を2次元コードでご視聴いただけます。
取付日より前に、是非ご確認ください。

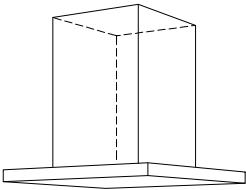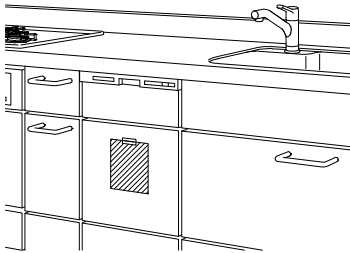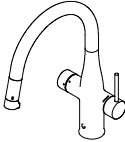センターフード型レンジフード (天吊りフード)  作成日：2024年06月03日 	I H加熱機器関連 I H加熱機器 仕切り板 作成日：2024年02月07日 	食器洗い乾燥機  作成日：2024年02月07日 	ミネラル浄水栓 Greentap  作成日：2024年06月03日 
---	--	--	---

--	--	--	--

--	--	--	--

特記事項 扉色 VK5:グレージュスタック 取手 [M]スリム取手 (ブラック) ワークトップカラー 【DW】 ソルティホワイト	物件名	西野 敬一 様邸	案件No.	図面名	担当	図面	図番 : 株式会社 LIXIL
			A2501DDD0EBVMG	機能図	栗野 友仁		
	仕様	ES21	見積No.	縮尺	日付		
			M25016242201-006-2		2025.02.17		