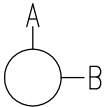
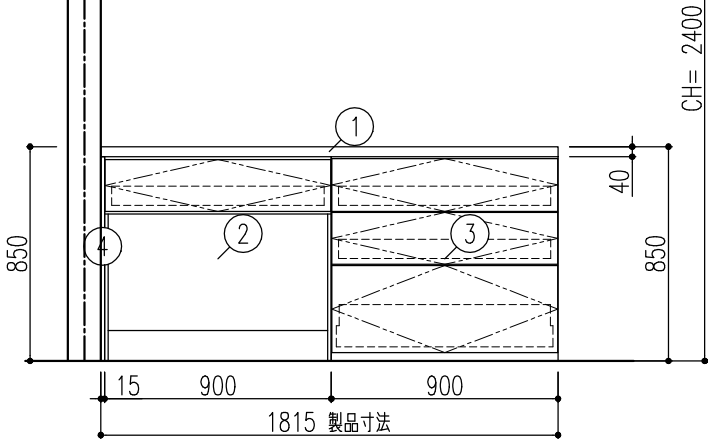




面



A面



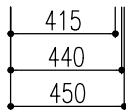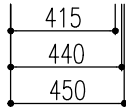
面

[illegible]

【 ご注意 】

- 記載のキャビネット寸法は扉前面までの呼び寸法です。キャビネット本体の寸法・扉厚み等は商品ガイドの巻末資料をご確認ください。
- 記載のワークトップ、カウンター、エンドパネル、サイドパネルの寸法は呼び寸法です。詳細寸法は商品ガイドの巻末資料をご確認ください。



特記事項 扉色 VK5:グレイジュスタック 取手 [M]スリム取手(ブラック)	物件名	西野敬一 様邸	案件No.	図面名	担当	図面	図番 : 株式会社 LIXIL
			A2501DDD0EBVMG	レイアウト図	栗野 友仁		
	仕様	ES21	見積No.	縮尺	日付		
			M25016242201-006-3	1/30	2025.02.17		

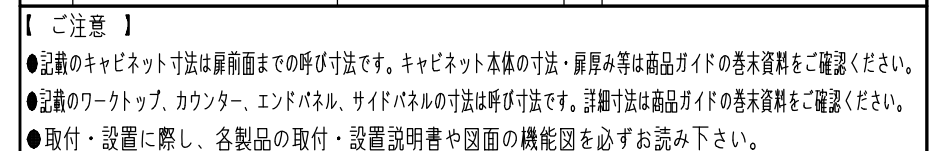

特記事項 扉色 VK5:グレンジュスタッコ 取手 [M]スリム取手（ブラック）	物件名	西野敬一 様邸	案件No.	図面名	担当	図面	図番
			A2501DDDD0EBVMG	納まり図	栗野 友仁		株式会社 LIXIL
	仕様	ES21	見積No.	縮尺	日付		
			M25016242201-006-3	1/30	2025.02.17		


B面

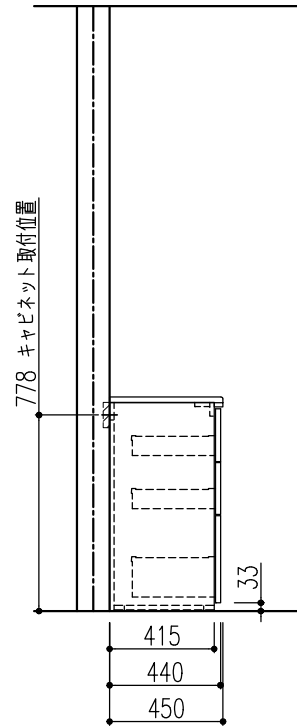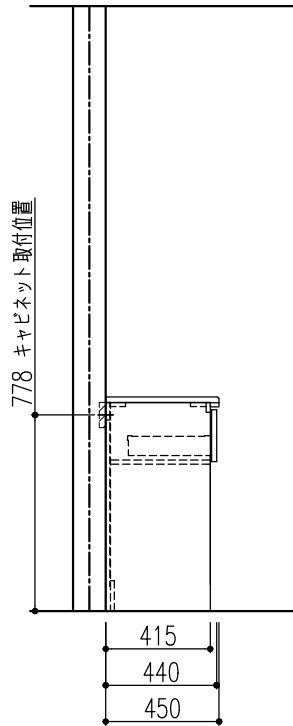B面



特記事項 扉色 VK5:グレージュスタック 取手 [M]スリム取手（ブラック）	物件名	西野敬一 様邸	案件No.	図面名	担当	図面	図番
			A2501DDD0EBVMG	納まり図	栗野 友仁		株式会社 LIXIL
	仕様	ES 2 1	見積No.	縮尺	日付		
			M25016242201-006-3	1/30	2025.02.17		

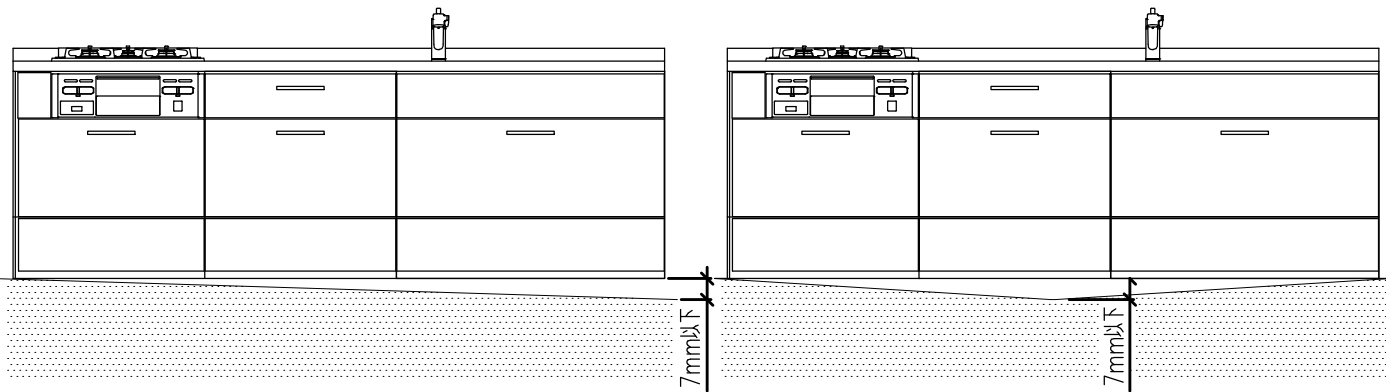■ 床の不陸に関して








床の不陸は、7 m m 以下に抑えるようにしてください。不陸が大きい場合は、現場責任者に床の修正を依頼してください。
※キャビネット取付時には不陸調整スペーサー等で水平になるように設置してください。

	特記事項 扉色 VK5:グレージュスタック 取手 [M]スリム取手（ブラック）	物件名	西野 敬一 様邸	案件No.	図面名	担当	図面	図番
				A2501DDD0EBVMG	機能図	栗野 友仁		株式会社 LIXIL
				見積No.	縮尺	日付		
				M25016242201-006-3		2025.02.17		
		仕様	ES 2 1					

■ キッチン取付者さま向け 動画コンテンツ ■

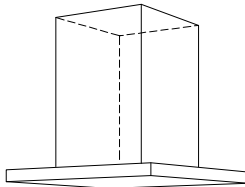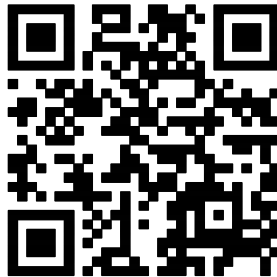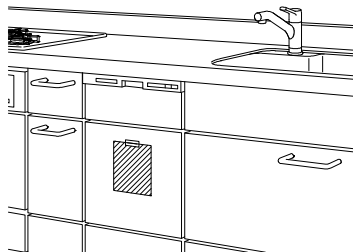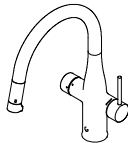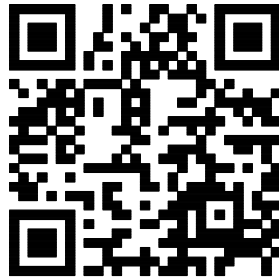商品取付けの注意点を2次元コードでご視聴いただけます。
取付日より前に、是非ご確認ください。

センターフード型レンジフード (天吊りフード)  作成日：2024年06月03日 		I H加熱機器関連 I H加熱機器 仕切り板 作成日：2024年02月07日 		食器洗い乾燥機  作成日：2024年02月07日 		ミネラル浄水栓 Greentap  作成日：2024年06月03日 			
特記事項 扉色 VK5:グレージュスタック 取手 [M]スリム取手 (ブラック)		物件名 西野敬一 様邸 仕様 ES21		案件No.		図面名	担当	図面	図番
				A2501DDD0EBVMG		機能図	栗野 友仁		株式会社 LIXIL
				見積No.		縮尺	日付		
				M25016242201-006-3			2025.02.17		