

■ 仕 様			■ HEAT20 G1		
断熱工事		■ 床:カネライトフォーム t65 ■ 土間床等の外周:スタイロフォームAT t25 ■ 壁:アクアフォームLITE吹付 t85 ■ 天井:アクファフォームLITE吹付 t170			
床下換気		■ 基礎パッキン JOTO (玄関・UB周り:気密基礎パッキン)			
防虫防蟻		■ 土壌処理・木部 ガントナーMC			
■ 外 部 仕 上 表			22条地域		
部位		仕上・仕様・メーカー		色番・品番	
屋根		■ ガルバリウム鋼板(t0.35)UK立平 ニスクカラーPro GH 軒先通気金物 日本住環境株式会社【REV-15】		GCA51 Sマットグレー	
パラペット笠木		■ ガルバリウム鋼板		GHK01 Sブラック	
破風・鼻隠		■ なし			
雨樋	(軒樋)	■ Panasonic サーフেসケアFS-I型		ブラック	
	(縦樋)	■ Panasonic S30角樋		ブラック	
軒天	屋根軒	■			
	ポーチ軒	■ ニチハ軒天5 木目調 910×1820×5		ライト	
	バルコニー軒	■			
オーバーハング水切り		■ ガルバリウム鋼板 ※外壁合わせ JOTO:HF-A3550		アンバーグレー	
外壁 ※下地面材:タイガーEXハイパー 防火認定 PC030BE-4028	通気金物(15mm)	■メイン	ニチハ エモンエクセラードV16 Vシリーズ ポルプストーン調V	エアルMGトリュフ	
		■アクセントA	なし		
		■アクセントB	なし		
玄関ポーチ		■ 床 LIXILパセオ300/PSO-BR 1		-	
基礎		■ 立上り巾木: モルタル刷毛引き		-	
基礎水切り金物		■ JOTO鋼板製 防鼠材付き水切り JOTO:WMF-N35		アンバーグレー	
バルコニー	床・内壁	■ なし		-	
	笠木	■ なし			
外部建具		■ LIXIL EW(アルゴンガス高遮熱仕様LowE複層ガラスグリーン) ・SD、TSは、メーカー設定によるが、オペレーターハンドル優先とする ・オペレーター付サッシの場合は固定網戸とする ・グレモンハンドル式サッシの場合は可動網戸とする		外観 ブラック 内観 ショドーオークforDesign ※樹脂パッキン・網戸付	
シャッター		■ なし			
軒天通気金物					
玄関扉		■ LIXIL ジエスタ2 K2仕様 LIXILファミロック タグキー×3 (電池式)		ドア型: M26 型 ドア色: ラスティックオーク ハンドル: S型ハンドル 色 ブラック	
外部物干し金物		■			
換気フード		■ 局所換気扇(トイレ 浴室 キッチンフード) 防火ダンパー無		外気フード: ブラック	
		■ ダクトレス熱交換換気システム (日本スティーベル株式会社) VLR-70E 防火ダンパー無		外気フード: B ブラック 室内パネル ホワイト	

■ 構 造 概 要						
基礎	■ RCベタ基礎コンクリート					
通し柱・管柱	■ 構造用集成材 105×105			間柱	■ 集成材	
土台	■ 桧 105×105	大引き	■ 桧 90*90	筋交い	■ 構造用製材	火打梁 ■ 鋼製火打(当社基準により米松あり)
桁・梁	■ 構造用製材及び集成材			制震装置	■ Kダンパー (株)アイ・エム・エー	
■ 設 備 装 着 品						
住宅設備	部位	メーカー	商品名 ES	※ 詳細は見積り、プレゼン参照	見積りNo.	(日付)
	キッチン	LIXIL	■ ES I型 扉グレージュスタコ 天板ソルティホワイト キッチンパネル:フレッシュホワイト		見積り番号	: M250 1624 2201-007-2
			標準食洗器 標準IH, 壁付レンジフードASR(ブラック) スリム取手ブラック		(日付)	2025.2.18
	バックカウンタ	LIXIL	■ ES L1800(W900スライドストッカー+マルチスペース)		見積り番号	: M250 1624 2201-007-3
					(日付)	2025.2.18
	浴室	LIXIL	■ AX1616 PGハウス標準仕様 アクセント壁:シルバーグレー 浴槽:エコベンチ ホワイト 床:グレー マグネットシェフ検討中		見積り番号	: M250 1624 2201-007-1
					(日付)	2025.2.18
	1Fトイレ	LIXIL	■ ベーシアハーマモJタイプ 白 ● タオル掛け: タンク手洗 無し ● 紙巻き器: なし(支給品取付)		見積り番号	: M250 1624 2201-007-5
					(日付)	2025.2.18
	2Fトイレ	LIXIL	■ ベーシアシャワートイレ 白 ● タオル掛け: KF-AA70D(リング) タンク手洗 有り ● 紙巻き器: CF-AA22H /WA		見積り番号	: M250 1624 2201-007-6
				(日付)	2025.2.18	
洗面台	LIXIL	■ EV W1200(D500タイプ) 扉:クリアダーク [引出しタイプ シングルハンドシャワー スタンダードLED三面鏡 その他 ● タオル掛け: KF-AA71D(バー)		見積り番号	: M250 1624 2201-007-4	
				(日付)	2025.2.18	
給排水設備	給湯器	■ エコキュート370L Panasonic NSシリーズ スタンダードモデル 追い焚きフルオート※在庫限り				
	排水	■ 下水				
	外水栓	■ 1 カ所 (平面図参照)	■ 外部立栓柱: PVC製 水栓柱12型【前澤化成工業】			
	外部ガーデンパン	■ 無し				
	その他	■ 洗濯機用単水栓: 緊急止水弁付		■ 洗濯機用排水: トラップ金物(標準)		
	■ 排水さや管(長期優良住宅仕様)					
ガス配管設備	■ なし (配置図・平面図参照)		■ ガス使用器具			
電気設備	インターホン	■ パナソニック VL-SZ30KL				
	TVアンテナ	■ UHF + BS・110度CS／CSアンテナ [2K・4K・8K対応] ■ブラック ※電波状況によりホワイトになる可能性あり				
	エアコン	■ 設置場所:				
	ソーラー	■ あり(Qセルズ)	12 枚	5.28 KW	Re.RISE-G3 440 (1722×1134×30)	
	※標準搭載	■ 屋外パワコン				
その他		決定図				

	浜 岡 一 級 総 合 設 計 事 務 所 一級建築士事務所 静岡県知事登録第 (10)2441 号 一級建築士 大臣登録第 365879 号 西原利昌	 株式会社 LIFEFUND InDesign office 一級建築士事務所 事務所登録 (2)第7595号 一級建築士登録 第179770号 鈴木 達男 〒432-8023 静岡県浜松市中央区鴨江3丁目70番23号	年 月 日	2025.3.8	件名	西野敬一郎様さやか様 邸新築工事			設計	IC	工務	図 番	
			縮尺		図面	仕上表 1			倉田		青島	1-1	



内 部 仕 上 表 （壁下地:石膏ボード12.5mm/天井下地:9.5mm）※脱衣室:床合板特類 下地									
階		床	巾木	壁	品番	廻 縁	天 井	品番	特記事項
1F	ポーチ	LIXIL/パセオ300/PSO-BR 2							
	玄関	LIXIL/パセオ300/PSO-BR 2	ライン巾木(W)	ビニルクロス	SLP-252	突付	ビニルクロス	SLP-252	
	ホール①	イタ銘木フロアースティックt12 ナラ桎3P	ライン巾木(W)	ビニルクロス	SLP-252	突付	ビニルクロス	SLP-252	
	LDK	イタ銘木フロアースティックt12 ナラ桎3P	ライン巾木(W)	ビニルクロス	SLP-252	突付	ビニルクロス	SLP-252	壁アクセントクロス:2カ所
	洗面	イタ銘木フロアースティックt12 ナラ桎3P	ライン巾木(W)	ビニルクロス	SLP-252	突付	ビニルクロス	SLP-252	
	脱衣室	フロアタイルt2.3 サンゲツIS-2071	H40ソフト巾木 W8	ビニルクロス	SLP-252	突付	ビニルクロス	SLP-252	
	WC①	フロアタイルt2.3 サンゲツIS-2071	H40ソフト巾木 W8	ビニルクロス	SLP-252	突付	ビニルクロス	SLP-252	
2F	ホール②	イタ銘木フロアースティックt12 ナラ桎3P	ライン巾木(W)	ビニルクロス	SLP-252	突付	ビニルクロス	SLP-252	
	主寝室	イタ銘木フロアースティックt12 ナラ桎3P	ライン巾木(W)	ビニルクロス	SLP-252	突付	ビニルクロス	SLP-252	壁1面アクセントクロス
	洋室①	イタ銘木フロアースティックt12 ナラ桎3P	ライン巾木(W)	ビニルクロス	SLP-252	突付	ビニルクロス	SLP-252	
	洋室②	イタ銘木フロアースティックt12 ナラ桎3P	ライン巾木(W)	ビニルクロス	SLP-252	突付	ビニルクロス	SLP-252	
	W・I・C	イタ銘木フロアースティックt12 ナラ桎3P	ライン巾木(W)	ビニルクロス	SLP-252	突付	ビニルクロス	SLP-252	
	WC②	フロアタイルt2.3 サンゲツIS-2071	H40ソフト巾木 W8	ビニルクロス	SLP-252	突付	ビニルクロス	SLP-252	
物入・収納・CL etc		※接続する部屋と同仕様とする							

上 框 ※	■ LIXILラシッサS上框のみ30×150 色: クリエペール
階 段	■ LIXIL KA 階段 ササラ: プレシャスホワイト
KA階段で対応できない場合、オプション	段 板 : クリエペール 蹴込板: プレシャスホワイト
ラウンド手摺: クリエペール	手摺金物 プレシャスホワイト
にてラシッサS階段	上段框: クリエペール 長尺笠木156: LIXIL 段板同色
窓 枠	■ LIXIL スマート10 色 プレシャスホワイト
	※浴室ドア枠 フクビ3方枠 [ホワイト]
キッチン笠木	■ ゴム集成カウンター(オスモカラー) 色 30627ロアーグリアmatt
カウンター	形状 L型(ジョイント加工) t=30
天井点検口	■ 天井アルミ点検口枠 450角 TAN45BW フクビ化学工業
	ミルキーホワイト
床下収納庫	■ 高気密型床下点検口断熱型 SPF-R6060 城東テクノ 収納付
	(脱衣室) ライトグレー(LG)
トイレ棚	■ 1,2階トイレ D250 アートランバー棚(シェルホワイト)
室内物干し金物	■ シーリングハンガーパイプL=1550
洋室①	■ ゴム集成カウンター(オスモカラ 色 30627ロアーグリアmatt
	t=25

支給品	■ 無し
備考	壁ぎわ付框:プレシャスホワイト 可動棚アートランバー色 ダークグレー 棚受金物類は全てブラック

内 部 建 具 表							
LIXIL		建具色： クリエモカ		枠色 ： 扉同色		※その他、下記特記による	
ラシッサS(標準)		把手 ： スクエアL (シャインニッケル) 丁番 固定枠(156) 外付戸当り ガイドピン床色合せ 引戸のみ上吊Wソフトモーション					
階	No	室名	形式	枠外W サイズ	デザイン	枠色	特記事項
				枠外H サイズ	建具色	把手	
1	1	LDK	片開き戸	—	RZA	ブラック	ラフィス
	WD			2400	ブラック		クリアガラス
	2	CL①	折れ戸	—	LAA	—	
	WD			2000	—	—	
	3	WC①	片引き戸	—	LAA	—	明り窓・表示錠
	WD			2000	—	—	
	4	脱衣室	片引き戸	—	LAA	—	明り窓・表示錠
	WD			2000	—	—	
2							
	5	洋室①	片開き戸	—	LAA	—	
	WD			2000	—	—	
	6	洋室②	片開き戸	—	LAA	—	
	WD			2000	—	—	
	7	WC②	片開き戸	—	LAA	—	明り窓・表示錠
	WD			2000	—	—	
	8	ランドリー	片引き戸	—	LAA	—	
	WD			2000	—	—	
	9	主寝室	片開き戸	—	LAA	—	
	WD			2000	—	—	

		浜 岡 一 級 総 合 設 計 事 務 所		株式会社 LIFEFUND InDesign office 一級建築士事務所		年 月 日	件名			設計	IC	工務	図 番
		一級建築士事務所 静岡県知事登録第 (10)2441 号		事務所登録 (2) 第7595号 一級建築士登録 第179770号 鈴木 達男		2025.03.13	西野敬一郎様さやか様 邸新築工事			倉田	0	青島	1-2
		一級建築士 大臣登録第 365879 号 西原利昌		〒432-8023 静岡県浜松市中央区鴨江3丁目70番23号		縮尺	図面	仕上表 2					

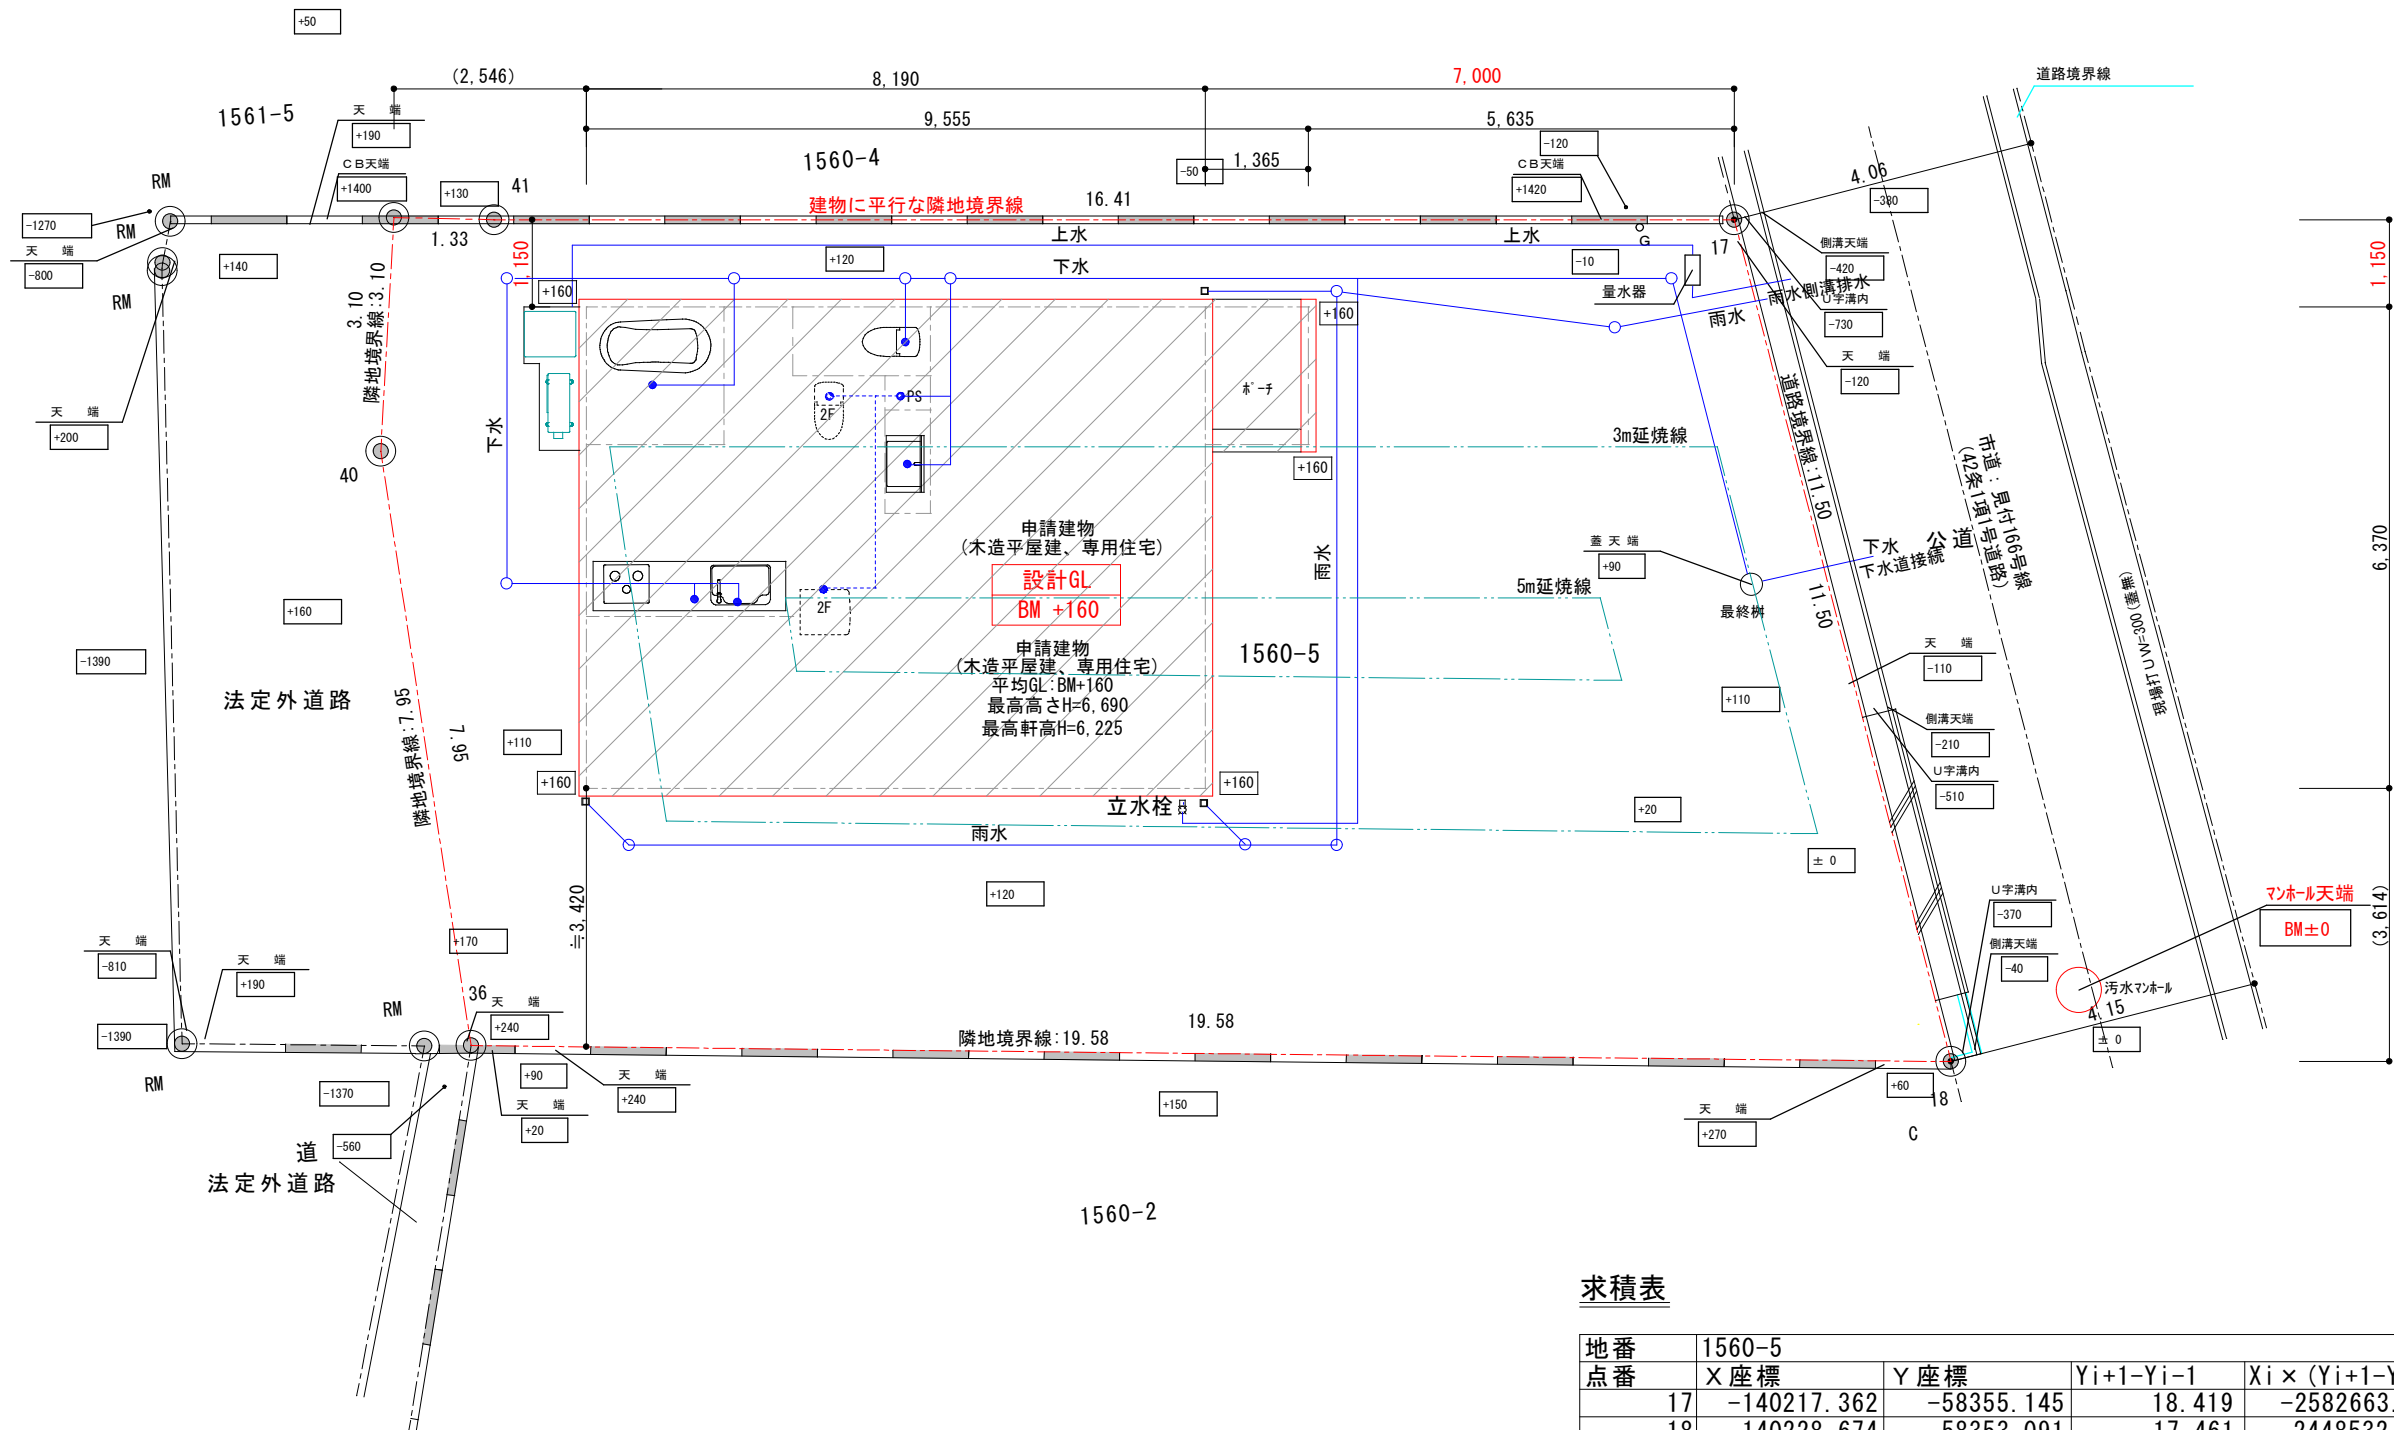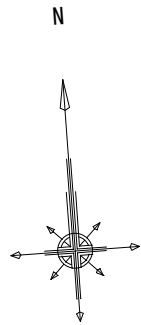

- 凡例
- C : コンクリート杭
 - P : プラスチック杭
 - RM : 金属標
 - R : 金属鋸
 - M : 刻み
 - T : 基準点

トータル面積表		(㎡)
敷地面積		208.09
建築面積		54.65
床面積	1階	52.17
	2階	52.17
延床面積		104.34
建蔽率	(54.65/208.09) × 100	
容積率	(104.34/208.09) × 100	

道路斜線制限については、明らかに適合する。
北側斜線制限については、明らかに適合する。
平均地盤面について
申請建物の周囲の平均地盤面高さをBM+160とする。


求積表

地番	1560-5			
点番	X座標	Y座標	Yi+1-Yi-1	Xi × (Yi+1-Yi-1)
17	-140217.362	-58355.145	18.419	-2582663.590678
18	-140228.674	-58353.091	-17.461	2448532.876714
36	-140227.050	-58372.606	-20.135	2823471.651750
40	-140219.124	-58373.226	-0.227	31829.741148
39	-140216.052	-58372.833	1.716	-240610.745232
41	-140216.177	-58371.510	17.688	-2480143.738776
合計				416.194926
合計面積				208.097463
地積				208.09㎡

測地系	世界測地系
座標系	Ⅷ系
測量年月日	令和6年 12月 21日

決定図

訂正	浜岡一級総合設計事務所 一級建築士事務所 静岡県知事登録第 (10)2441号 一級建築士 大臣登録第 365879号 西原利昌	LIFEFUND PG HOUSE	株式会社 LIFEFUND InDesign office 一級建築士事務所 事務所登録 (2)第7595号 一級建築士登録 第179770号 鈴木 達男 〒432-8023 静岡県浜松市中央区鴨江3丁目70番23号	年月日 2025.3.8 縮尺 1/100	件名 西野敬一郎様・さやか様 邸新築工事 図名 配置図	設計 倉田	IC	工事 青島	図番 2-1
----	--	----------------------	--	--------------------------------	--------------------------------------	----------	----	----------	-----------

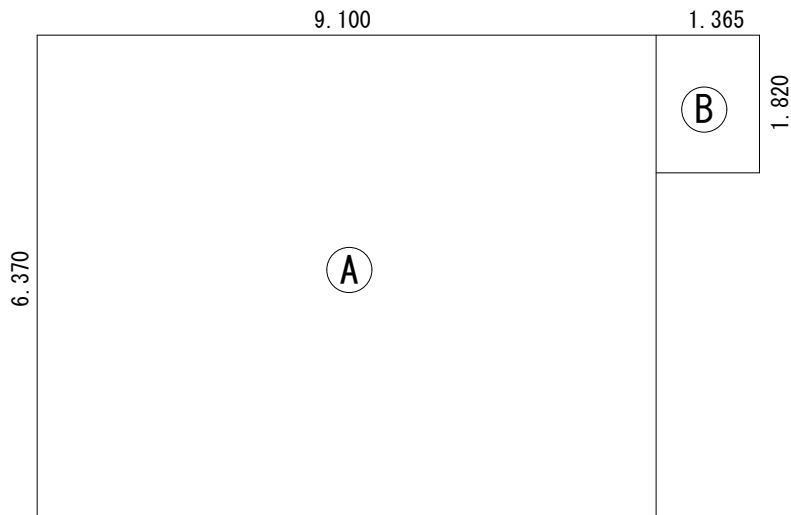


建築面積求積図 S=1/100

建築面積求積表

番号	計算式	(m)	面積 (㎡)
Ⓐ	8.190 × 6.370		52.1703
Ⓑ	1.3650 × 1.820		2.4843
合計			54.6546 54.65

(16.5坪)

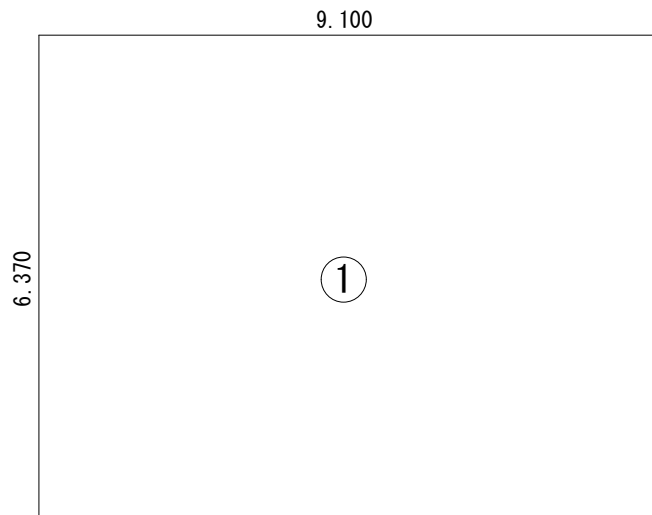


1階床面積図 S=1/100

1階床面積求積表

番号	計算式	(m)	面積 (㎡)
①	8.190 × 6.370		52.1703
合計			52.1703 52.17

(15.7坪)

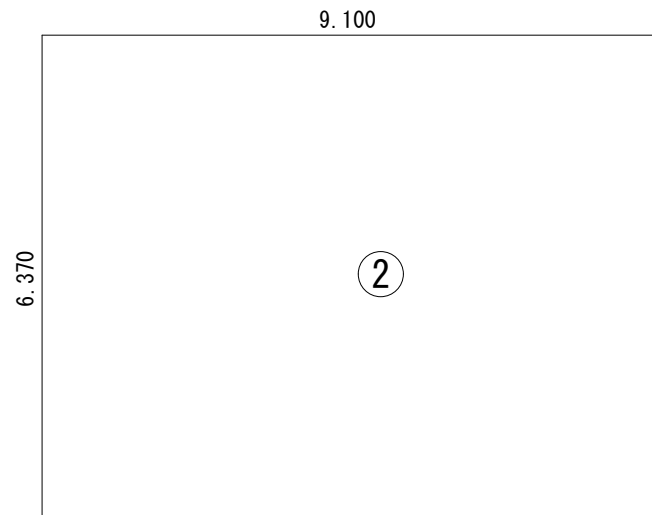

2階床面積図 S=1/100

2階床面積求積表

番号	計算式	(m)	面積 (㎡)
②	8.190 × 6.370		52.1703
合計			52.1703 52.17


(15.7坪)

延べ床面積表

	番号	(m)	面積 (㎡)
1階床面積	①		52.17
2階床面積	②		52.17
合計			104.34

(31.5坪)

決定図

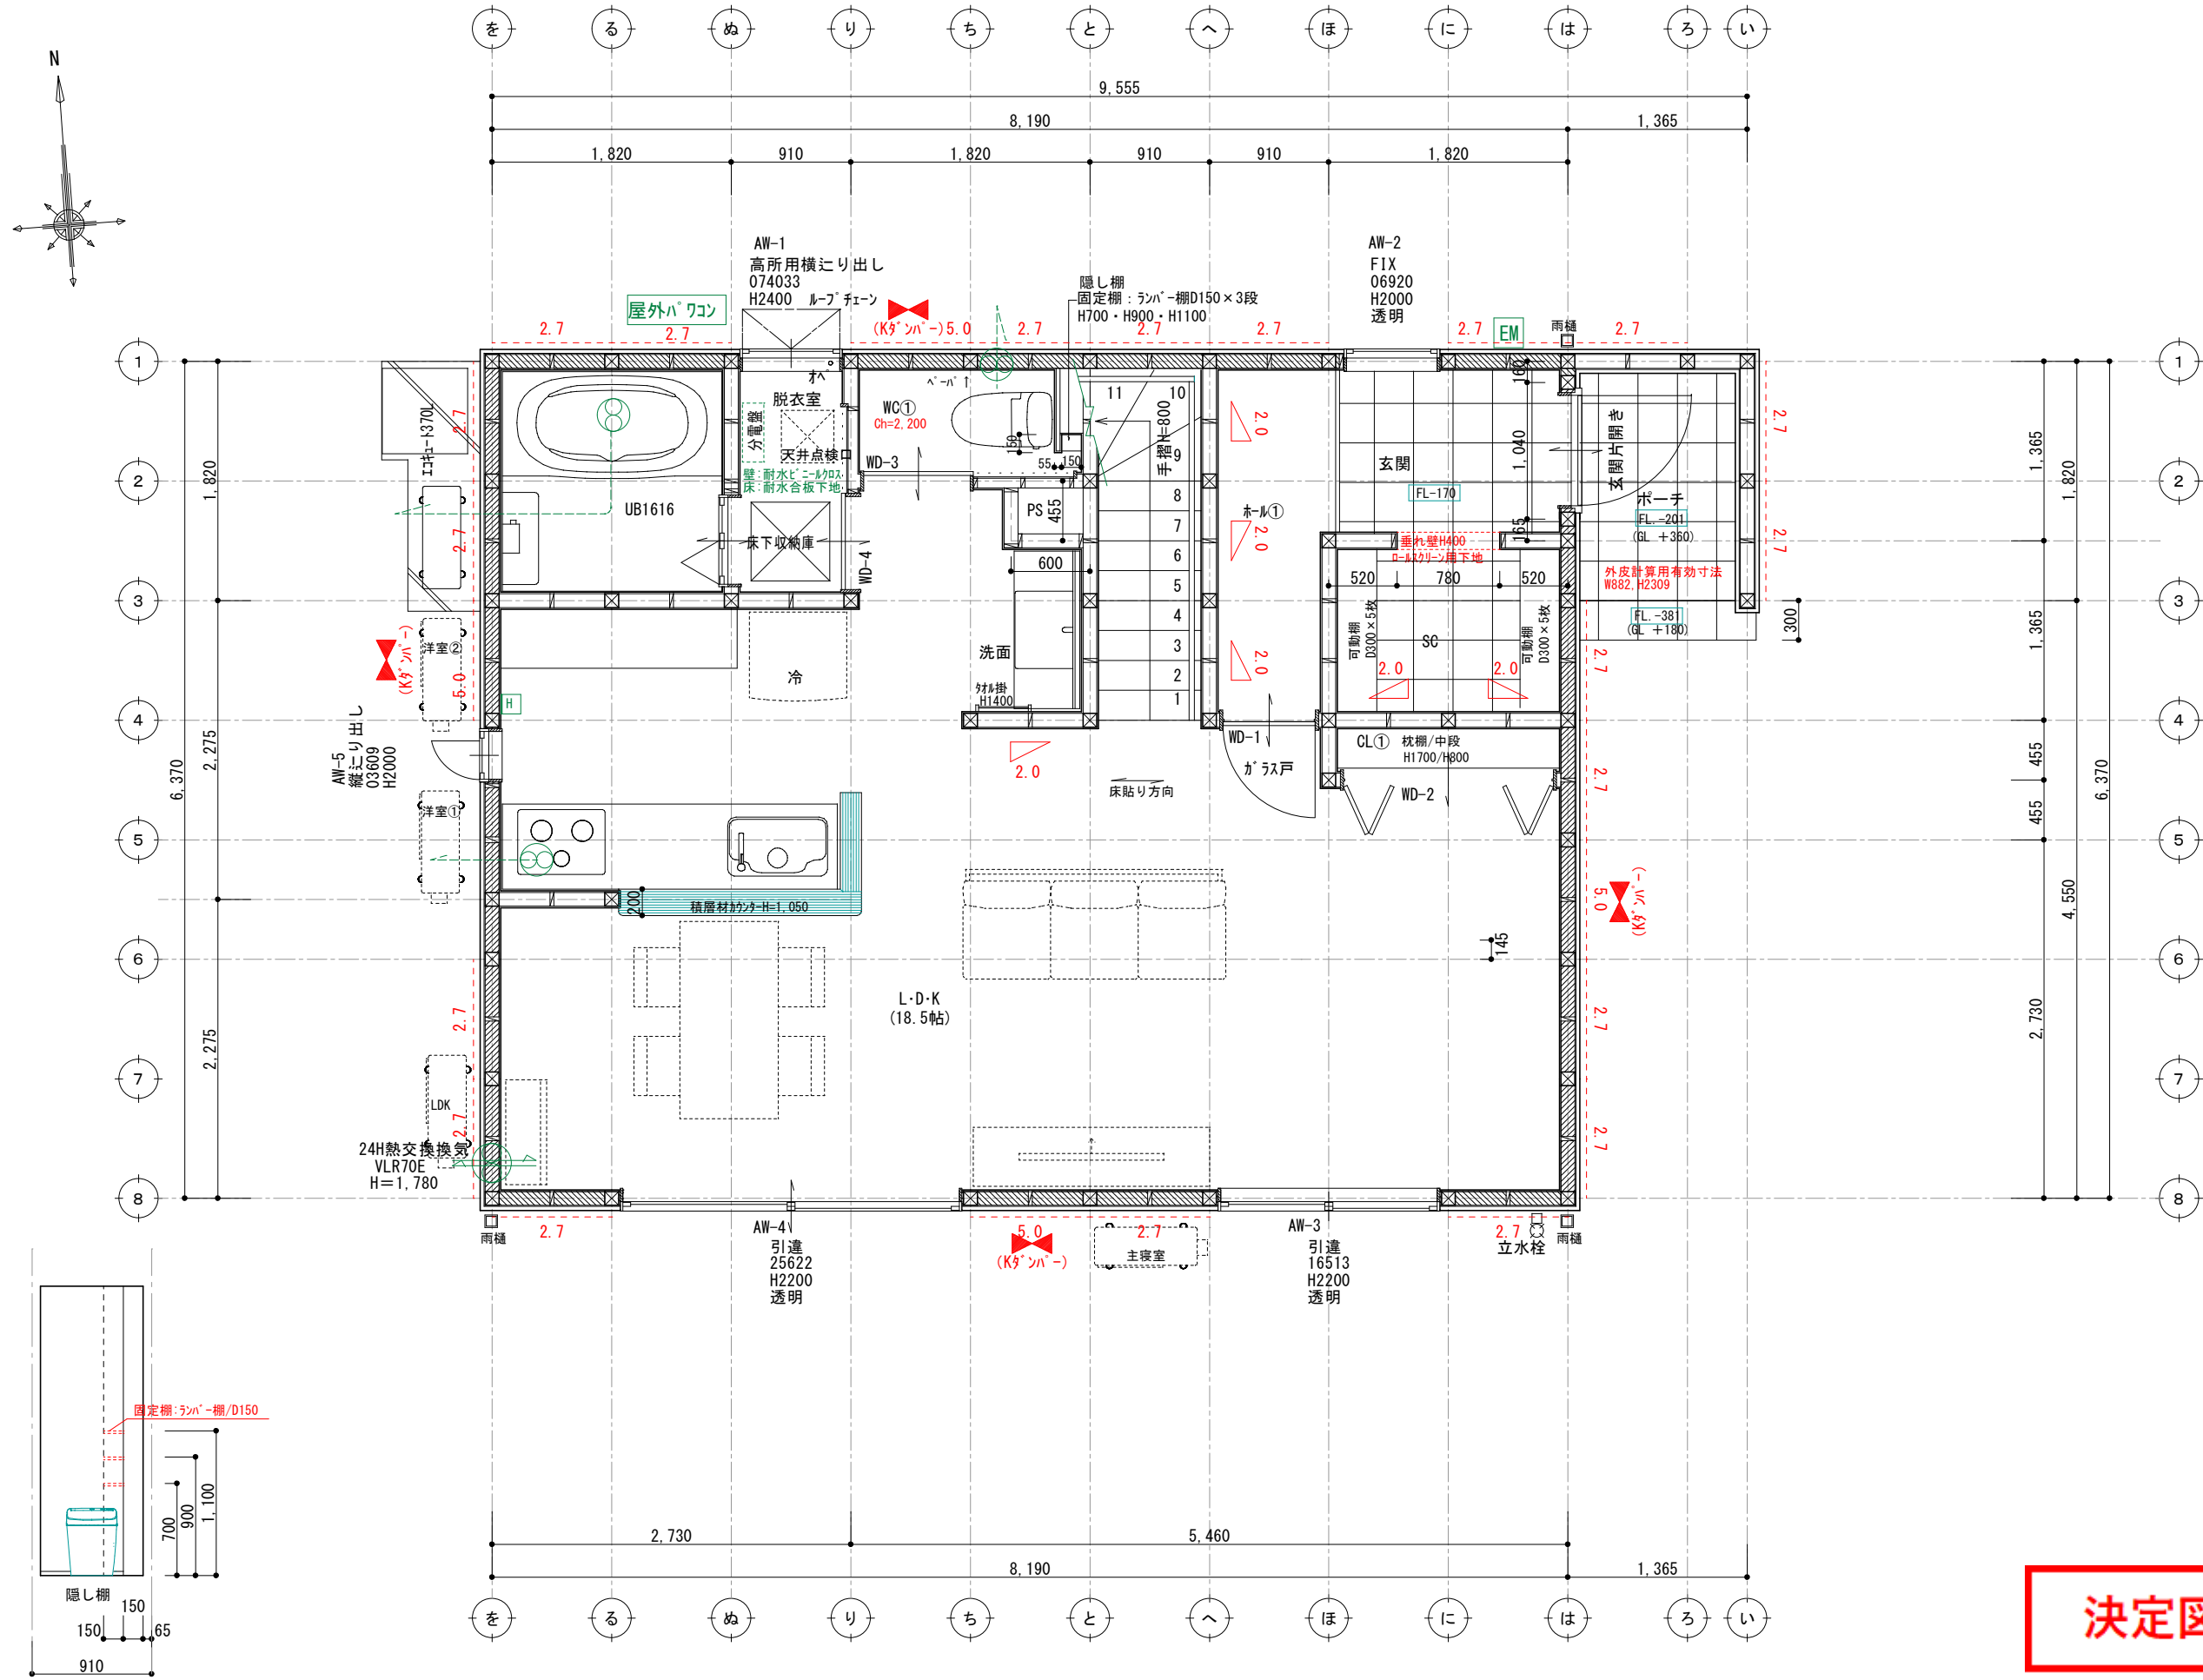

壁付け 住宅用火災報知器			数量
H 熱感知	電池式(単独型)		1
	露出型		
壁付け 住宅用火災報知器			数量
S 煙感知	電池式(単独型)		
	露出型		

※ 煙感知器は壁・梁より600mm以上離す
壁に取付ける場合、
天井から150mm以上500mm以内離す
換気扇・エアコン吹出口から1500mm以上離す
※ 全室LED照明とする。
※ 標準天井高さ2,400
※ 特記無きガラスは型ガラス

* 凡例

管柱 (105×105)

Kダクト (3.30倍 FRM-0641)

片筋違い (2.00倍 45×90)
(例 左:柱脚 右:柱頭)

たすき掛筋違い (4.00倍 45×90)

構造用合板 (2.70倍)
(t=9 材質:EXハイパー)

床点検口

天井点検口


換気扇

熱交換換気扇VLR-70

アドバンスシリーズ	
スマートデザイン (外部)	
凡例	
1	コンセント 1ヶ所
2	コンセント 2ヶ所
3	コンセント 3ヶ所
1ET	コンセント1ヶ所接地ターミナル付
2ET	コンセント2ヶ所接地ターミナル付
WP	コンセント 防水型
	エアコン用コンセント
	200V用コンセント
WP	防雨入線プレート
	スイッチ
●	3路スイッチ
●	4路スイッチ
⊗	直結電源
TV	テレビ取出口
TEL	電話取出口 (テレホンガイド)
LAN	LAN取出口 (テレホンガイド)
	壁照明
	リモコン (給湯関係・ルフロ)
	メーター
	分電盤
○	チャイム

※ACコンセント天井付け
※TVアンテナ工事
※スイッチはFL+1100、コンセントはFL+200

決定図

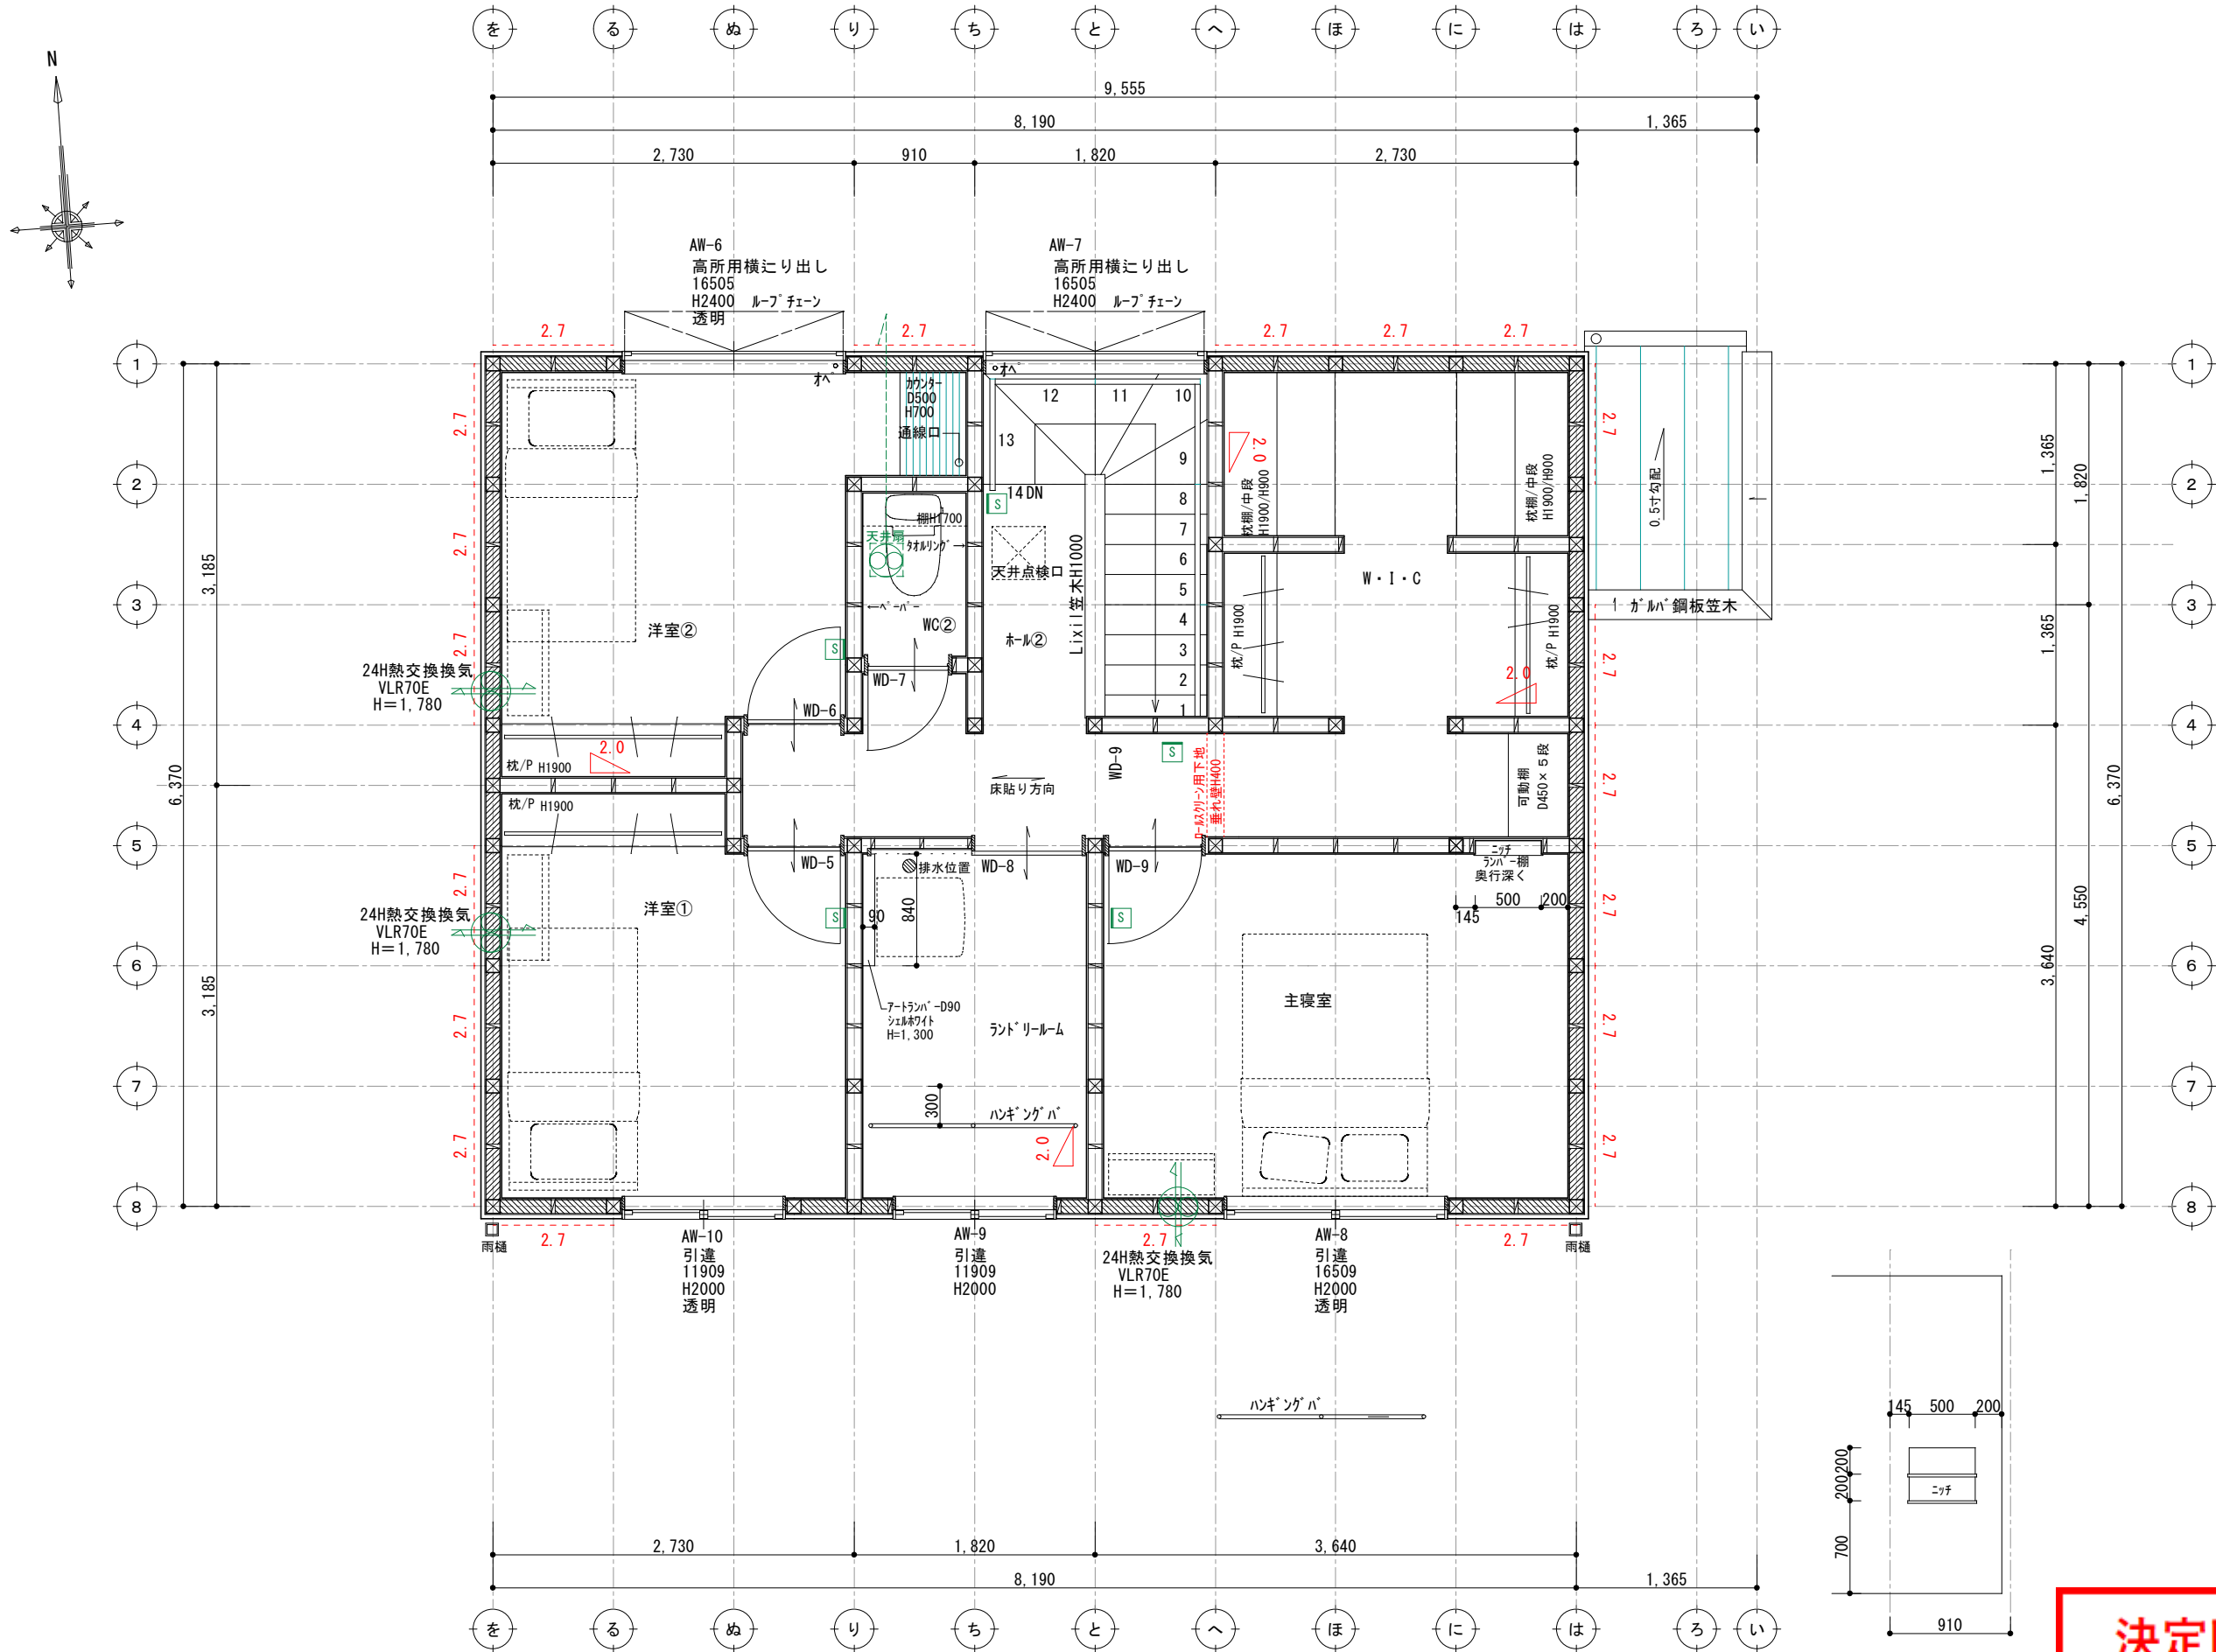

壁付け 住宅用火災報知器			数量
H	熱感知器	電池式(単独型)	
	熱感知器	露出型	
壁付け 住宅用火災報知器			数量
S	煙感知器	電池式(単独型)	4
	煙感知器	露出型	

※ 煙感知器は壁・梁より600mm以上離す
壁に取付ける場合、
天井から150mm以上500mm以内離す
換気扇・エアコン吹出口から1500mm以上離す
※ 全室LED照明とする。
※ 標準天井高さ2,400
※ 特記無きガラスは型ガラス

* 凡例

管柱 (105×105)

Kダクト (3.30倍 FRM-0641)

片筋違い (2.00倍 45×90)
(例 左:柱脚 右:柱頭)

たすき掛筋違い (4.00倍 45×90)

構造用合板 (2.70倍)
(t=9 9材 EX-HV)

床点検口

天井点検口


換気扇

熱交換換気扇VLR-70


アドバンスシリーズ		
スマートデザイン (外部)		
凡例	1	コンセント 1ヶ所
2	コンセント 2ヶ所	
3	コンセント 3ヶ所	
1ET	コンセント1ヶ所接地ターミナル付	
2ET	コンセント2ヶ所接地ターミナル付	
WP	コンセント 防水型	
WP	エアコン用コンセント	
WP	200V用コンセント	
WP	防雨入線プレート	
スイッチ	スイッチ	
3	3路スイッチ	
4	4路スイッチ	
直結電源	直結電源	
TV	テレビ取出口	
TEL	電話取出口 (テレホンガイド)	
LAN	LAN取出口 (テレホンガイド)	
壁照明	壁照明	
リモコン	リモコン (給湯関係・ルフロ)	
メーター	メーター	
分電盤	分電盤	
チャイム	チャイム	

※ACコンセント天井付け
※TVアンテナ工事
※スイッチはFL+1100、コンセントはFL+200


決定図

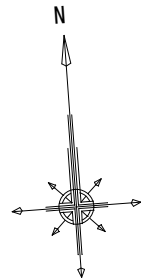

太陽光あり

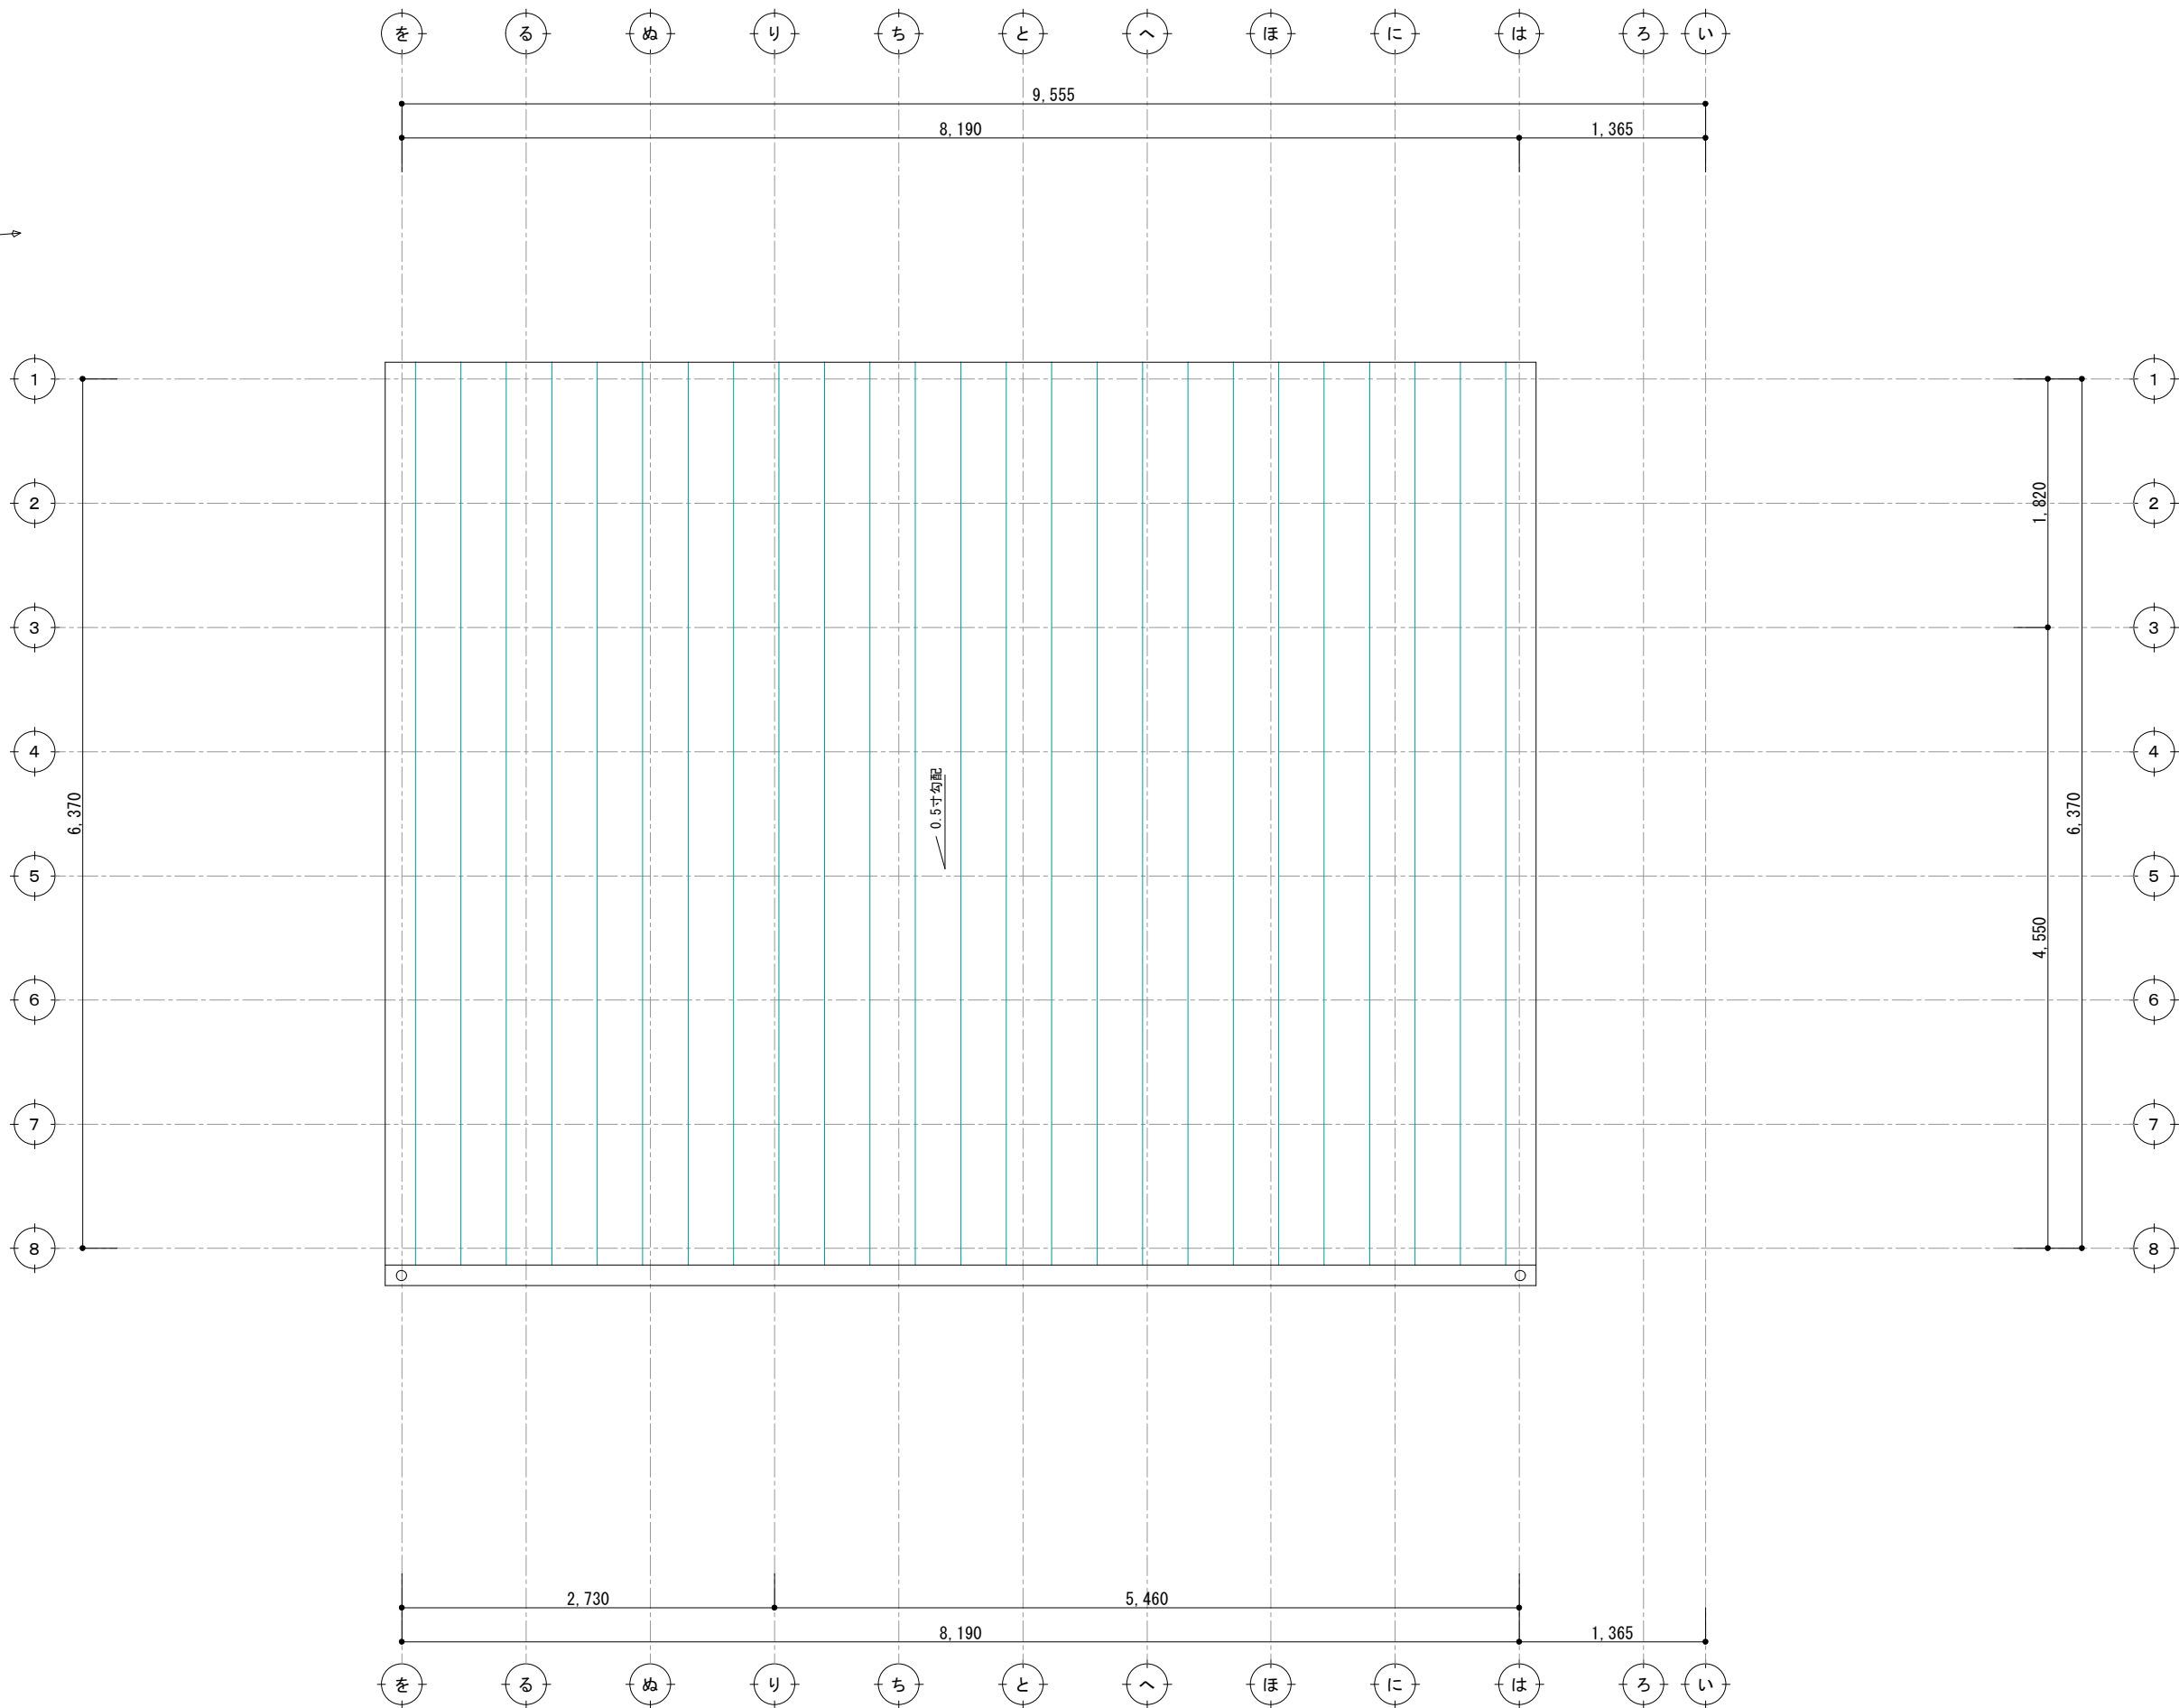


訂正	浜岡一級総合設計事務所		株式会社 LIFEFUND InDesign office 一級建築士事務所	年月日 2025. 2. 4	件名 西野敬一郎様・さやか様邸 新築工事		設計	IC	工事	図番
	一級建築士事務所 静岡県知事登録第 (10)2441 号						倉田		青島	3-3
	一級建築士 大臣登録第 365879 号 西原利昌									
			事務所登録 (2) 第7595号 一級建築士登録 第179770号 鈴木 達男	縮尺 1/100	図名 屋根伏図					
			〒432-8023 静岡県浜松市中央区鴨江3丁目70番23号							

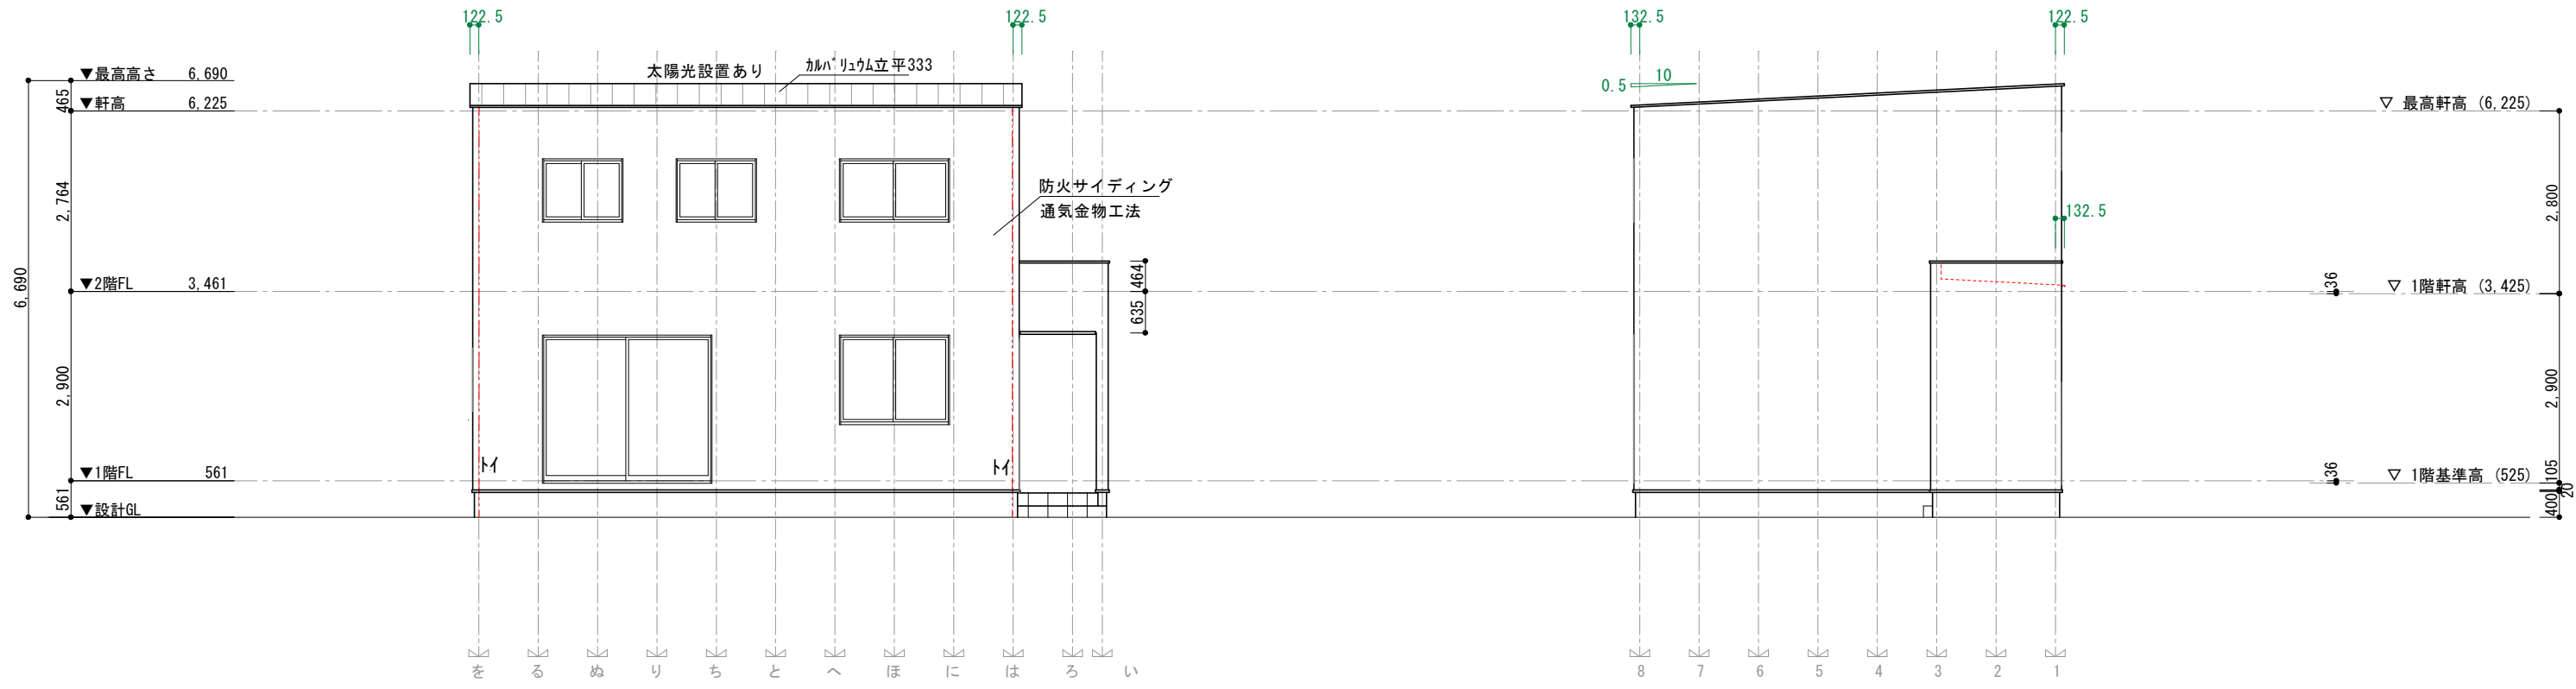

南側立面図 S=1/100

東側立面図 S=1/100

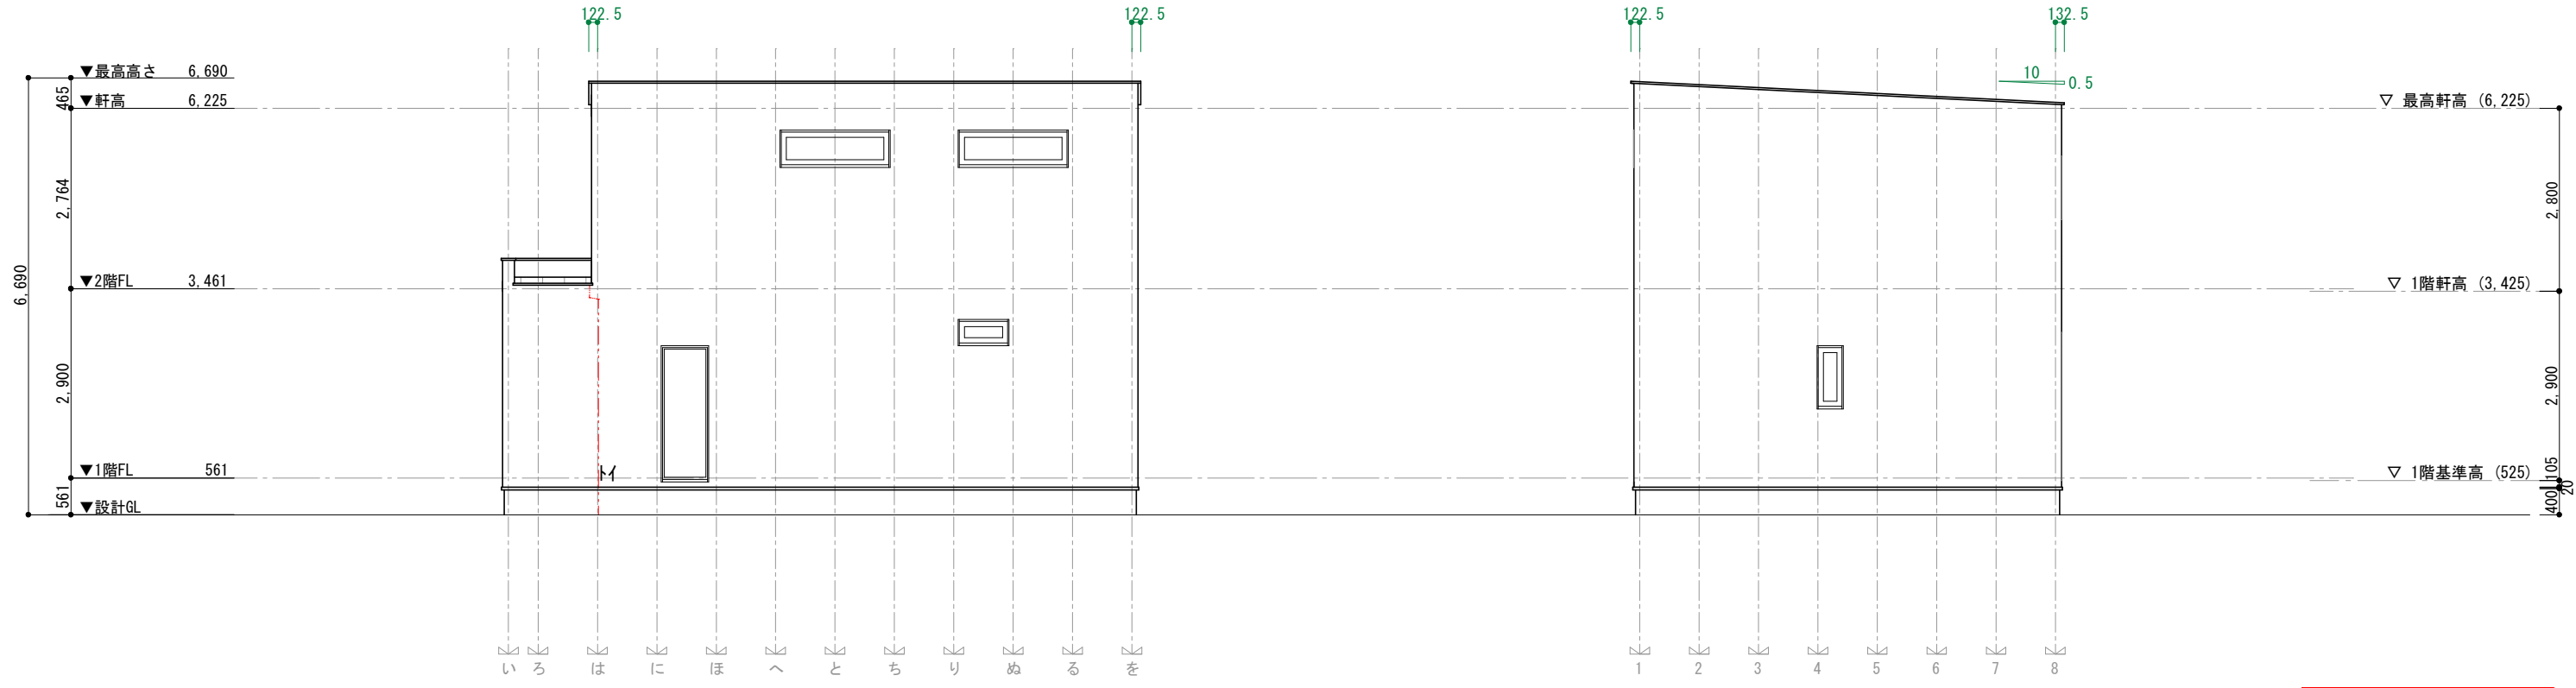

北側立面図 S=1/100


西側立面図 S=1/100

決定図

訂 正	浜 岡 一 級 総 合 設 計 事 務 所 一級建築士事務所 静岡県知事登録第 (10)2441 号 一級建築士 大臣登録第 365879 号 西原利昌		株式会社 LIFEFUND InDesign office 一級建築士事務所 事務所登録 (2) 第7595号 一級建築士登録 第179770号 鈴木 達男 〒432-8023 静岡県浜松市中央区鴨江3丁目70番23号	年 月 日 2025. 3. 8	件 名 西野敬一郎様・さやか様邸 新築工事		設計	IC	工事	図 番
				縮 尺 1/100	図 名 立面図					
				倉田	青島					


太陽光パネル有

G 1

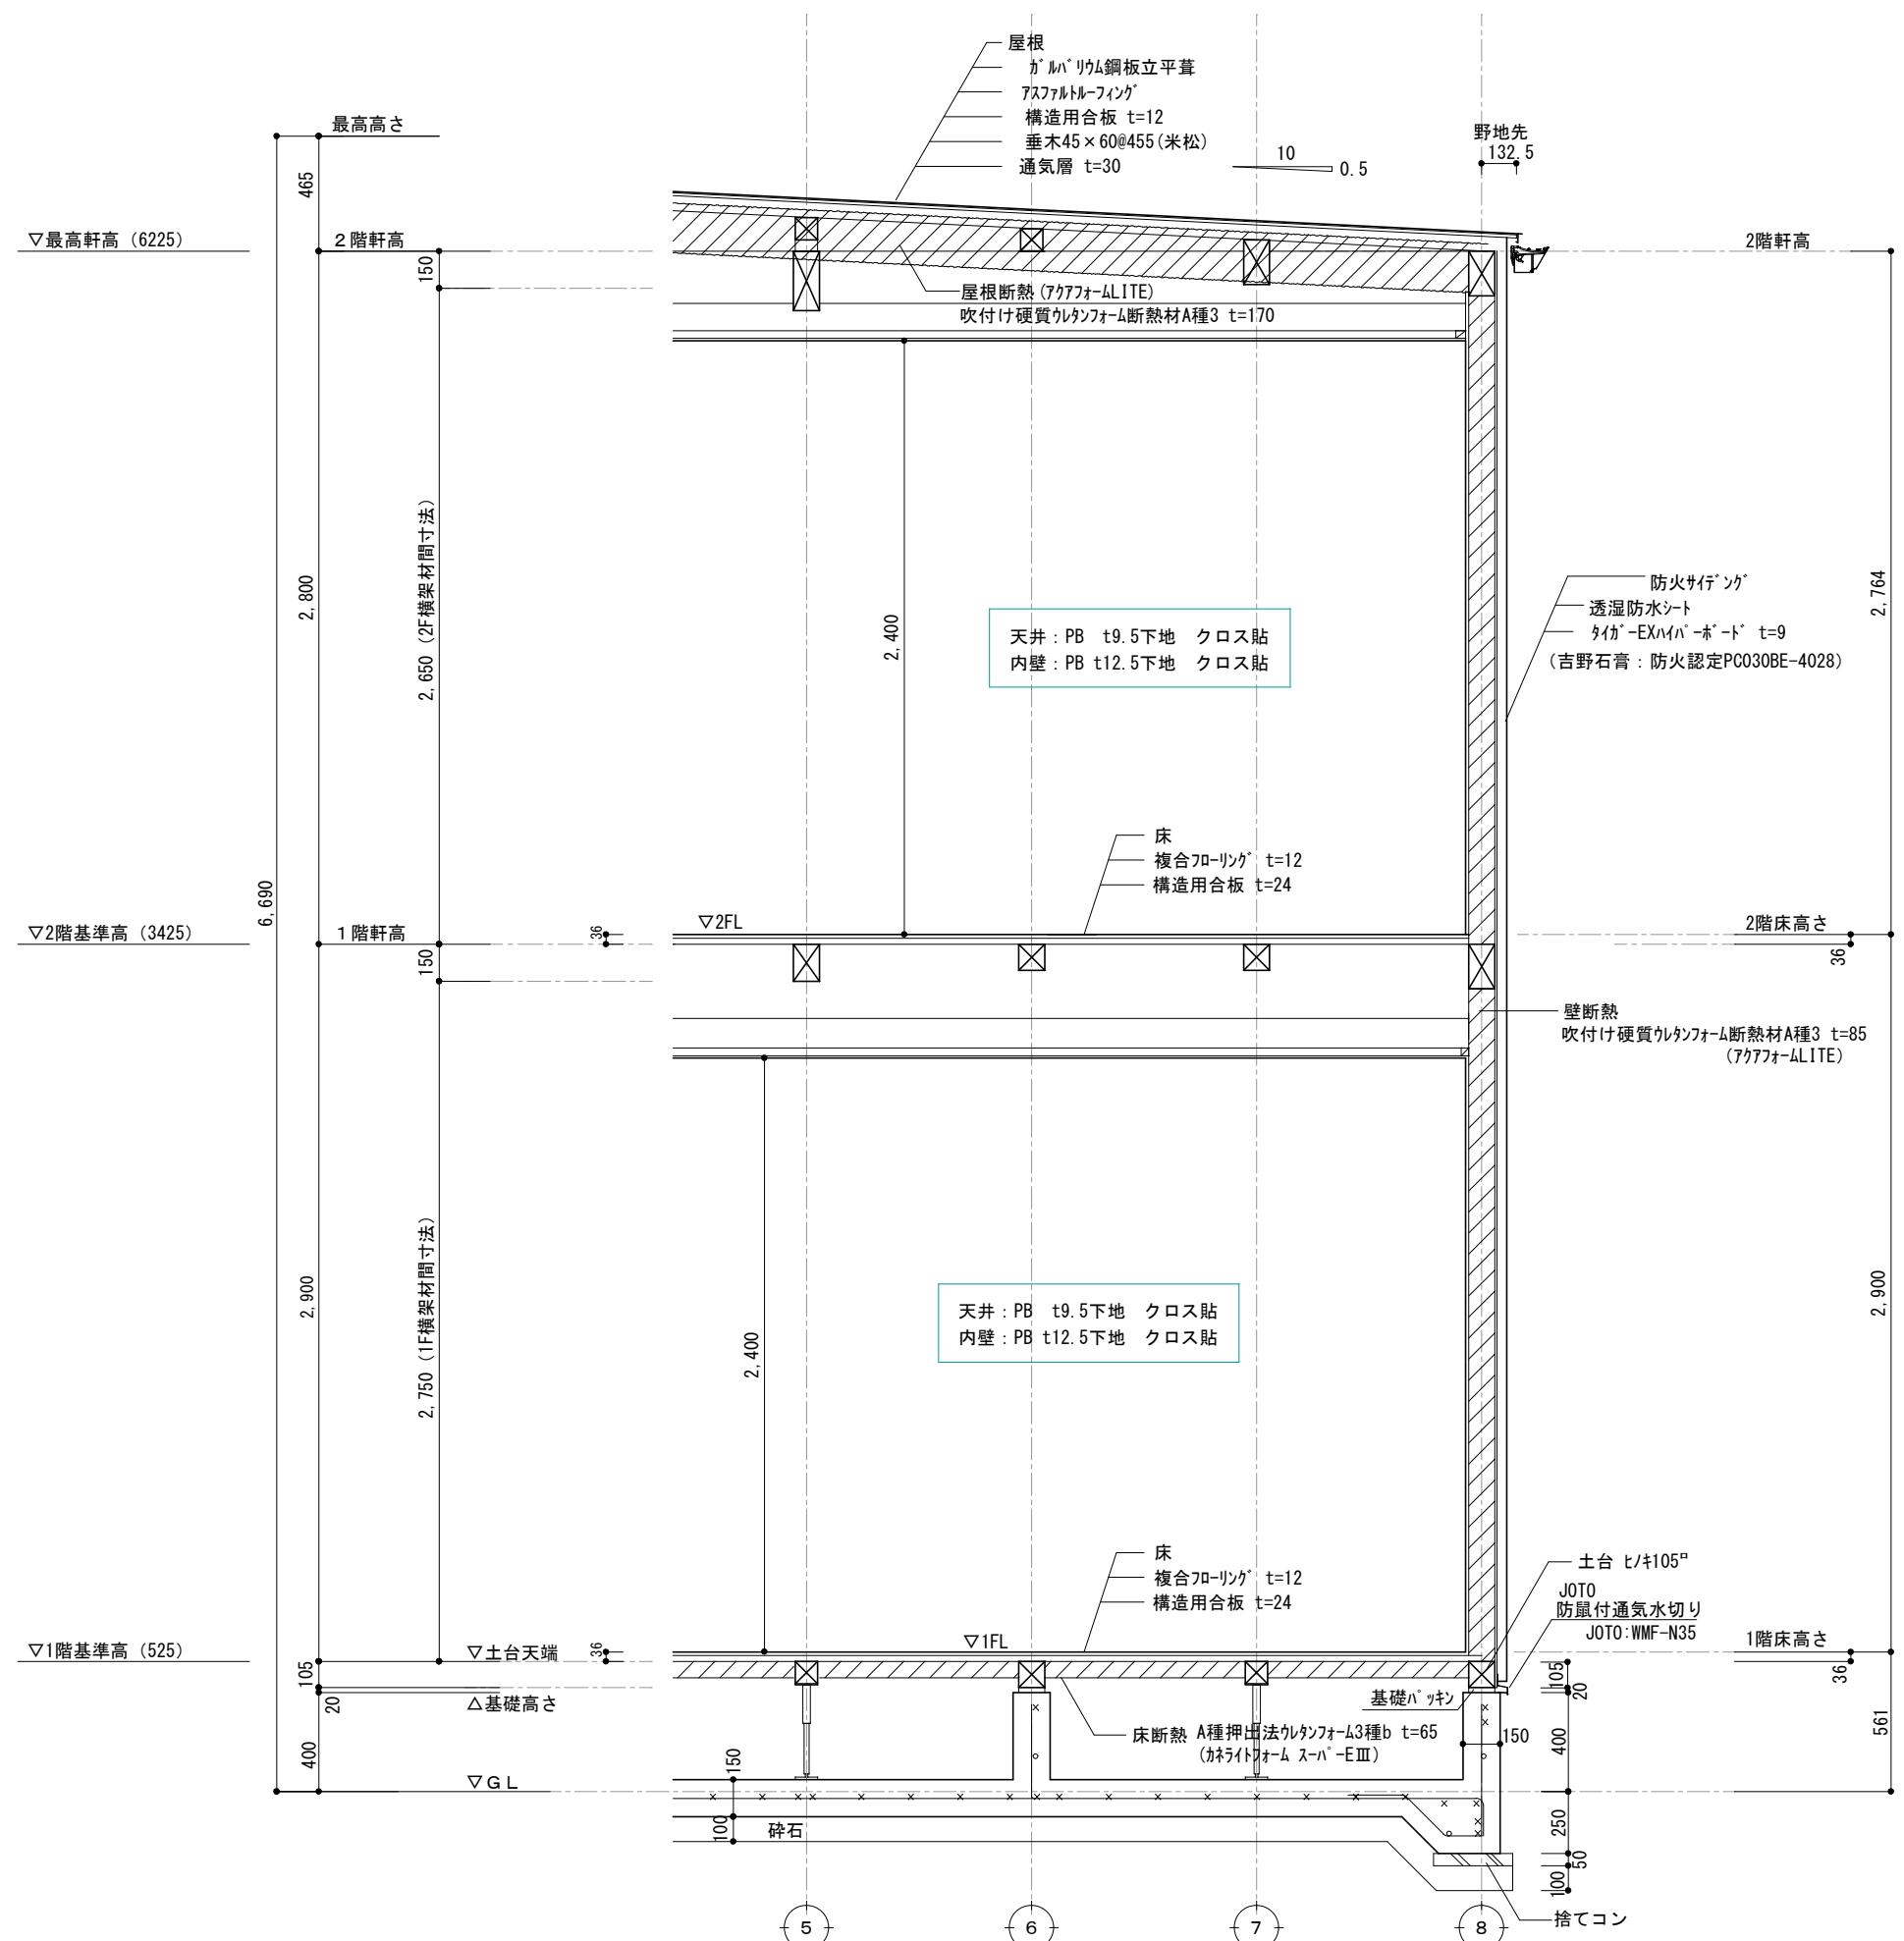

決定図

訂正	浜岡一級総合設計事務所 一級建築士事務所 静岡県知事登録第 (10) 2441 号 一級建築士 大臣登録第 365879 号 西原利昌	PG HOUSE ピージーハウス	株式会社 LIFEFUND InDesign office 一級建築士事務所 事務所登録 (2) 第7595号 一級建築士登録 第179770号 鈴木 達男 〒432-8023 静岡県浜松市中央区鴨江3丁目70番23号	年月日 2025.3.8 縮尺 1/30	件名 西野敬一郎様・さやか様 邸新築工事 図名 矩計図	設計 倉田	IC	工事 青島	図番 A-5
----	---	---------------------	---	-------------------------------	--------------------------------------	----------	----	----------	-----------

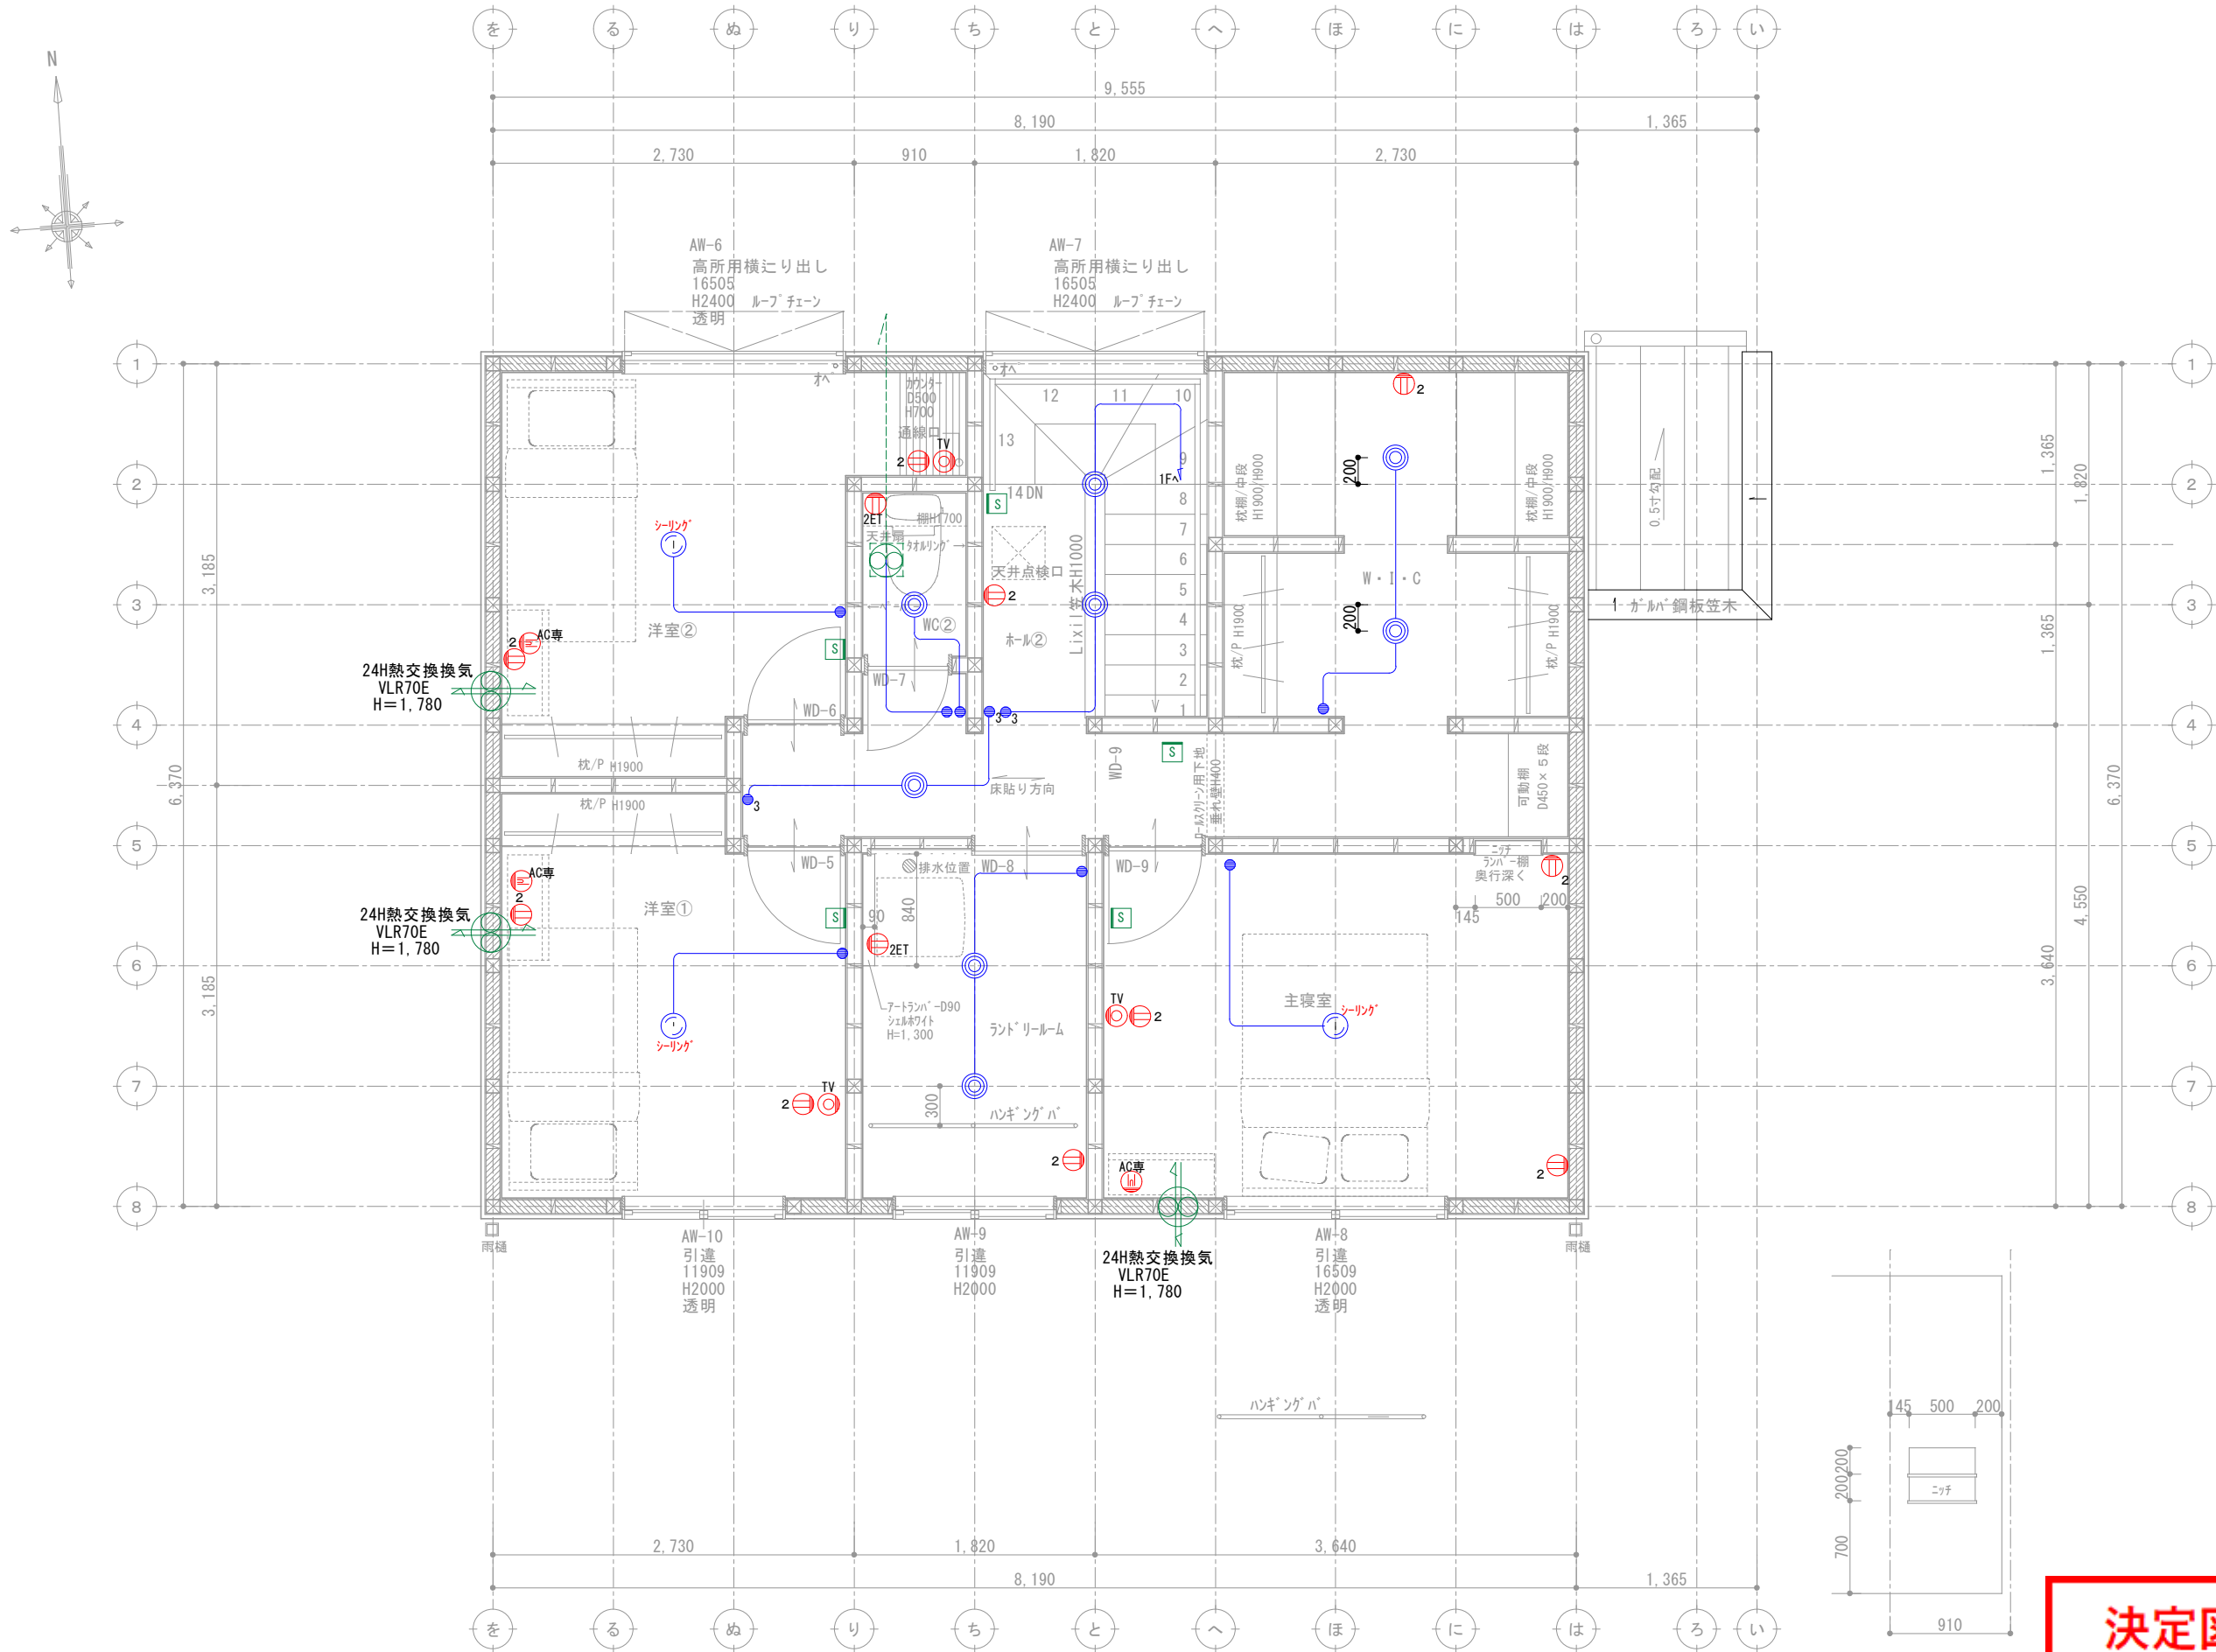

壁付け 住宅用火災報知器			数量
H 熱感知	熱感知器	電池式(単独型)	
		露出型	
壁付け 住宅用火災報知器			数量
S 煙感知	煙感知器	電池式(単独型)	4
		露出型	

※ 煙感知器は壁・梁より600mm以上離す
壁に取付ける場合、
天井から150mm以上500mm以内離す
換気扇・エアコン吹出口から1500mm以上離す

※ 全室LED照明とする。

※ 標準天井高さ2,400

※ 特記無きガラスは型ガラス

*** 凡例**

☒ 管柱 (105×105)

◀▶ Kダクト (3.30倍 FRM-0641)

△ 片筋違い (2.00倍 45×90)
(例 左:柱脚 右:柱頭)

⊠ たすき掛筋違い (4.00倍 45×90)

--- 構造用合板 (2.70倍)
(t=9 3枚付 EXハイバ)

◻ 床点検口

⊠ 天井点検口


⊙→ 換気扇

⊙⇄ 熱交換換気扇VLR-70


アドバンスシリーズ	
スマートデザイン (外部)	
凡例	
①	コンセント 1ヶ所
②	コンセント 2ヶ所
③	コンセント 3ヶ所
①ET	コンセント1ヶ所接地ターミナル付
②ET	コンセント2ヶ所接地ターミナル付
WP	コンセント 防水型
⊙	エアコン用コンセント
⊙	200V用コンセント
WP	防雨入線プレート
□	スイッチ
●	3路スイッチ
●	4路スイッチ
⊙	直結電源
⊙	テレビ取出口
TEL	電話取出口 (テレホンガイド)
LAN	LAN取出口 (テレホンガイド)
⊙	壁照明
⊙	リモコン (給湯関係・ルフロ)
⊙	メーター
⊙	分電盤
⊙	チャイム

※ACコンセント天井付け
※TVアンテナ工事
※スイッチはFL+1100、コンセントはFL+200

決定図

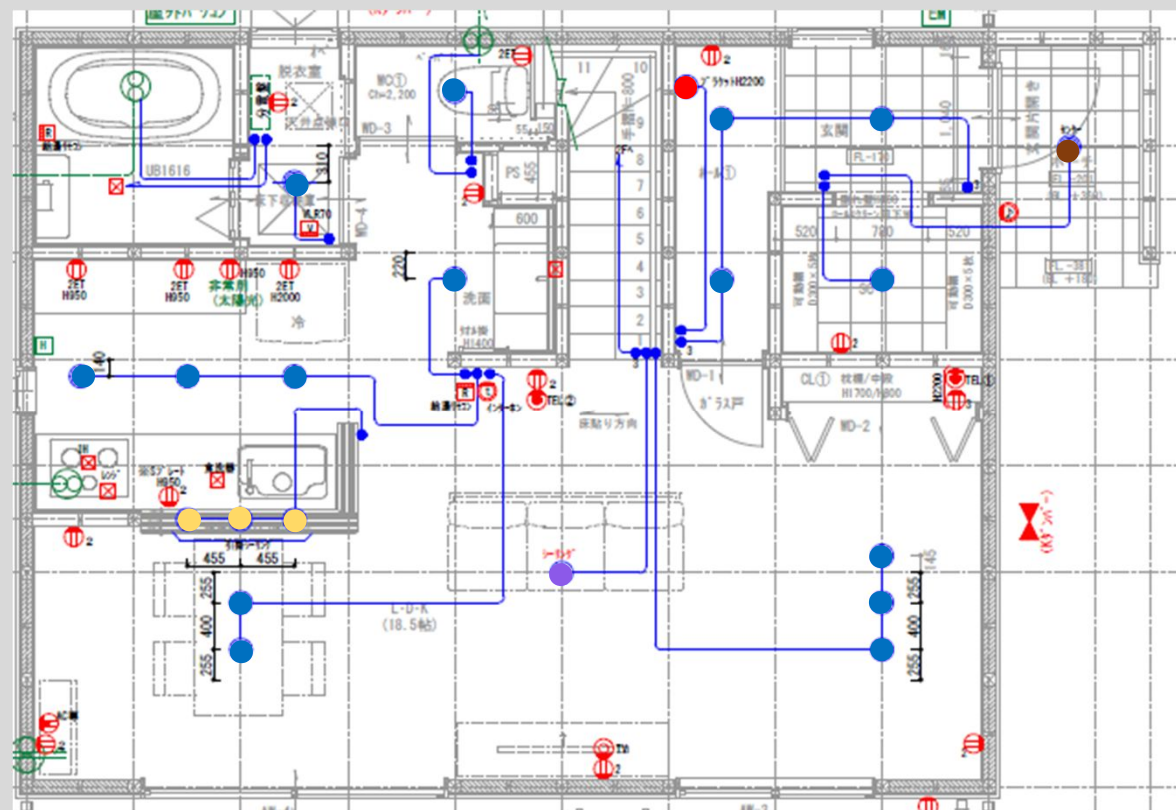

1 階

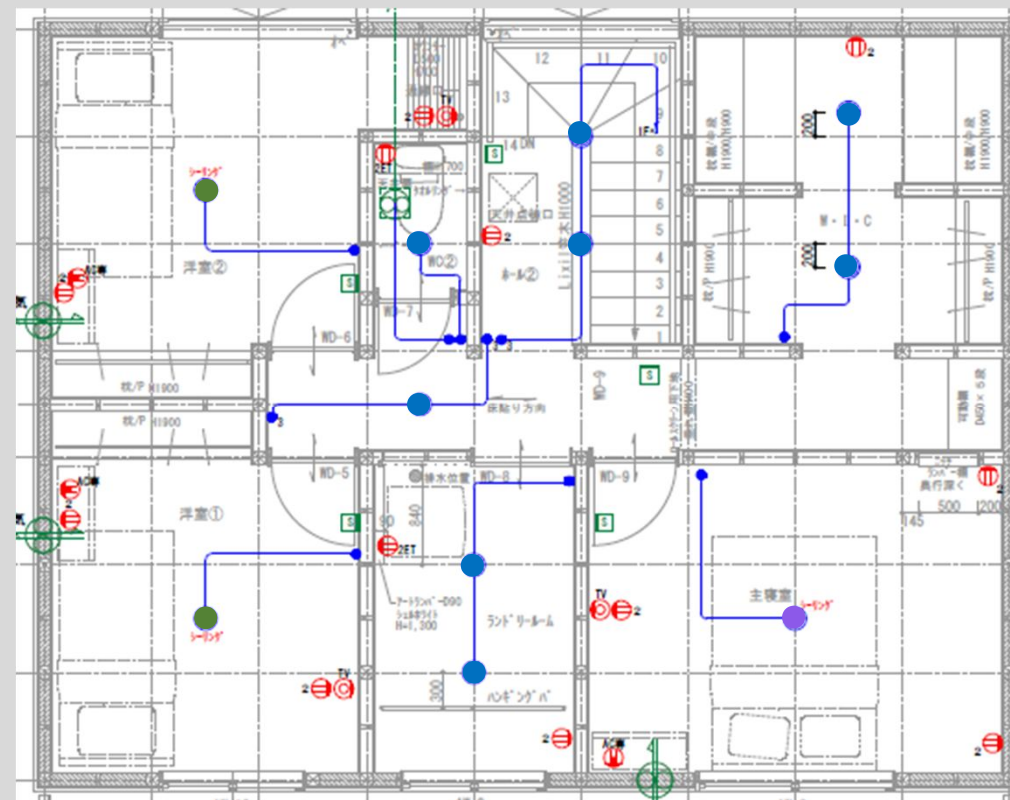

2 階

ドアホン：VL-SZ30KL
(Panasonic)



内部SW：アドバンス
マッドホワイト



引っ掛けシーリング

● × 3



決定図

外部：スマーデザインシリーズ
ブラック



決定図

2025. 3.8

ポーチ灯
● × 1

DDL-4496YW



高気密Se形 | 人感センサー | 連動マルチタイプ

DDL-4496 YW
電球色 / 2700K・Ra83

定格光束	消費電力	固有エネルギー消費効率
520lm	7.7W	67.5lm/W

¥18,800-(税抜) (LED内蔵)

LED LED 7.7W 白熱灯60W相当

- アルミダイカスト 白塗装
- アクリル 乳白(マット)
- 径φ111 埋込穴φ100 埋込深80mm 0.5kg
- 14VA
- 点灯照度調節機能付(暗・明・切)
- 点灯保持時間(1分)
- 拡散バネル付
- AC100V
- 光源寿命50,000時間
- 取付可能天井厚5~25mm
- 調光器併用不可

【連動器具について】
LED調光タイプ60VAまで
LED非調光タイプ不可 蛍光灯不可 白熱灯60Wまで

強制ON
ソフトスタート
フードアウト
増込穴100
埋込穴80
LED交換不可
防雨形
温度保護機能付

基本照明ダウンライト

● × 23 (15+8)

DDL6102AW



COBタイプ | 高気密Se形

DDL-6102 AW
温白色 / 3500K・Ra83

定格光束	消費電力	固有エネルギー消費効率
470lm	4.6W	102.1lm/W

¥3,600-(税抜) (LED内蔵)

LED LED 4.6W 白熱灯60W相当

- 鋼板 白塗装
- アクリル 乳白(マット)
- 径φ116 埋込穴φ100 埋込深70mm 0.3kg
- 8VA
- 拡散バネル付
- AC100V
- 光源寿命60,000時間
- 取付可能天井厚5~25mm
- 調光器併用不可

LED交換不可
防雨形
温度保護機能付
埋込穴100
埋込穴80
LED交換不可
防雨形
温度保護機能付

洋室①②

● × 2

DCL40507



タイマー付リモコン・ブルレス | 調色調光タイプ

DCL-40507
昼光色 / 6500K・Ra83 ~ 電球色 / 2700K・Ra83

LED	LED 29.5W	定格光束	消費電力	固有エネルギー消費効率
● 30VA	3699lm	29.5W	125.3lm/W	

¥22,000-(税抜) (LED内蔵)

- アクリル 乳白(マット)
- 径φ510 高128mm 1.6kg
- ブルレススイッチ付(全灯・※点灯・常夜灯)
- ※消灯前の調色調光状態
- 調色機能付(6500K~2700K)
- 調光機能付(5%~100%)
- 常夜灯6段階調光
- AC100V
- 光源寿命40,000時間
- 消費効率昼白色時
- 調光器併用不可
- シーンコントローラーは使用できません。

クイック取付式
カバー回転式

傾斜天井 55° 取付パーツ DP-40091
平天井 可能 取付パーツ DP-40638

リビング・主寝室シーリング

● × 2

DCL40508



タイマー付リモコン・ブルレス | 調色調光タイプ

DCL-40508
昼光色 / 6500K・Ra83 ~ 電球色 / 2700K・Ra83

LED	LED 34W	定格光束	消費電力	固有エネルギー消費効率
● 35VA	4299lm	34W	126.4lm/W	

¥26,000-(税抜) (LED内蔵)

- アクリル 乳白(マット)
- 径φ510 高128mm 1.6kg
- ブルレススイッチ付(全灯・※点灯・常夜灯)
- ※消灯前の調色調光状態
- 調色機能付(6500K~2700K)
- 調光機能付(5%~100%)
- 常夜灯6段階調光
- AC100V
- 光源寿命40,000時間
- 消費効率昼白色時
- 調光器併用不可
- シーンコントローラーは使用できません。


クイック取付式
カバー回転式

傾斜天井 55° 取付パーツ DP-40091
平天井 可能 取付パーツ DP-40638

玄関ブラケット

● × 1

OB255127LR

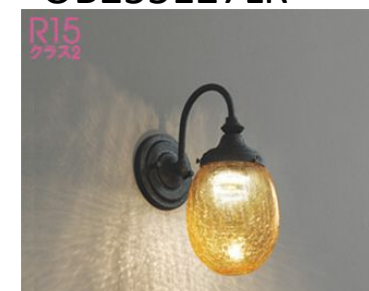

高演色LED 白熱灯器具60W相当


OB 255 127LR
¥22,800 (税抜)






固有エネルギー消費効率	定格光束	定格消費電力	Ra	色温度
74.5 lm/W	440 lm	5.9 W	94	2700K

調光器別売
電球色





- LED
- 鋼(黒色チタミ)
- ガラス(アンバー色・ヒビ模様入)
- 巾124 高259 出198 1.0kg
- 光源寿命40,000時間
- 連続調光100~5%・位相制御
- 別売調光器: LC 211・212P1・214・216・217・702・613・615
- 6VA(100V)

化粧ネジ式


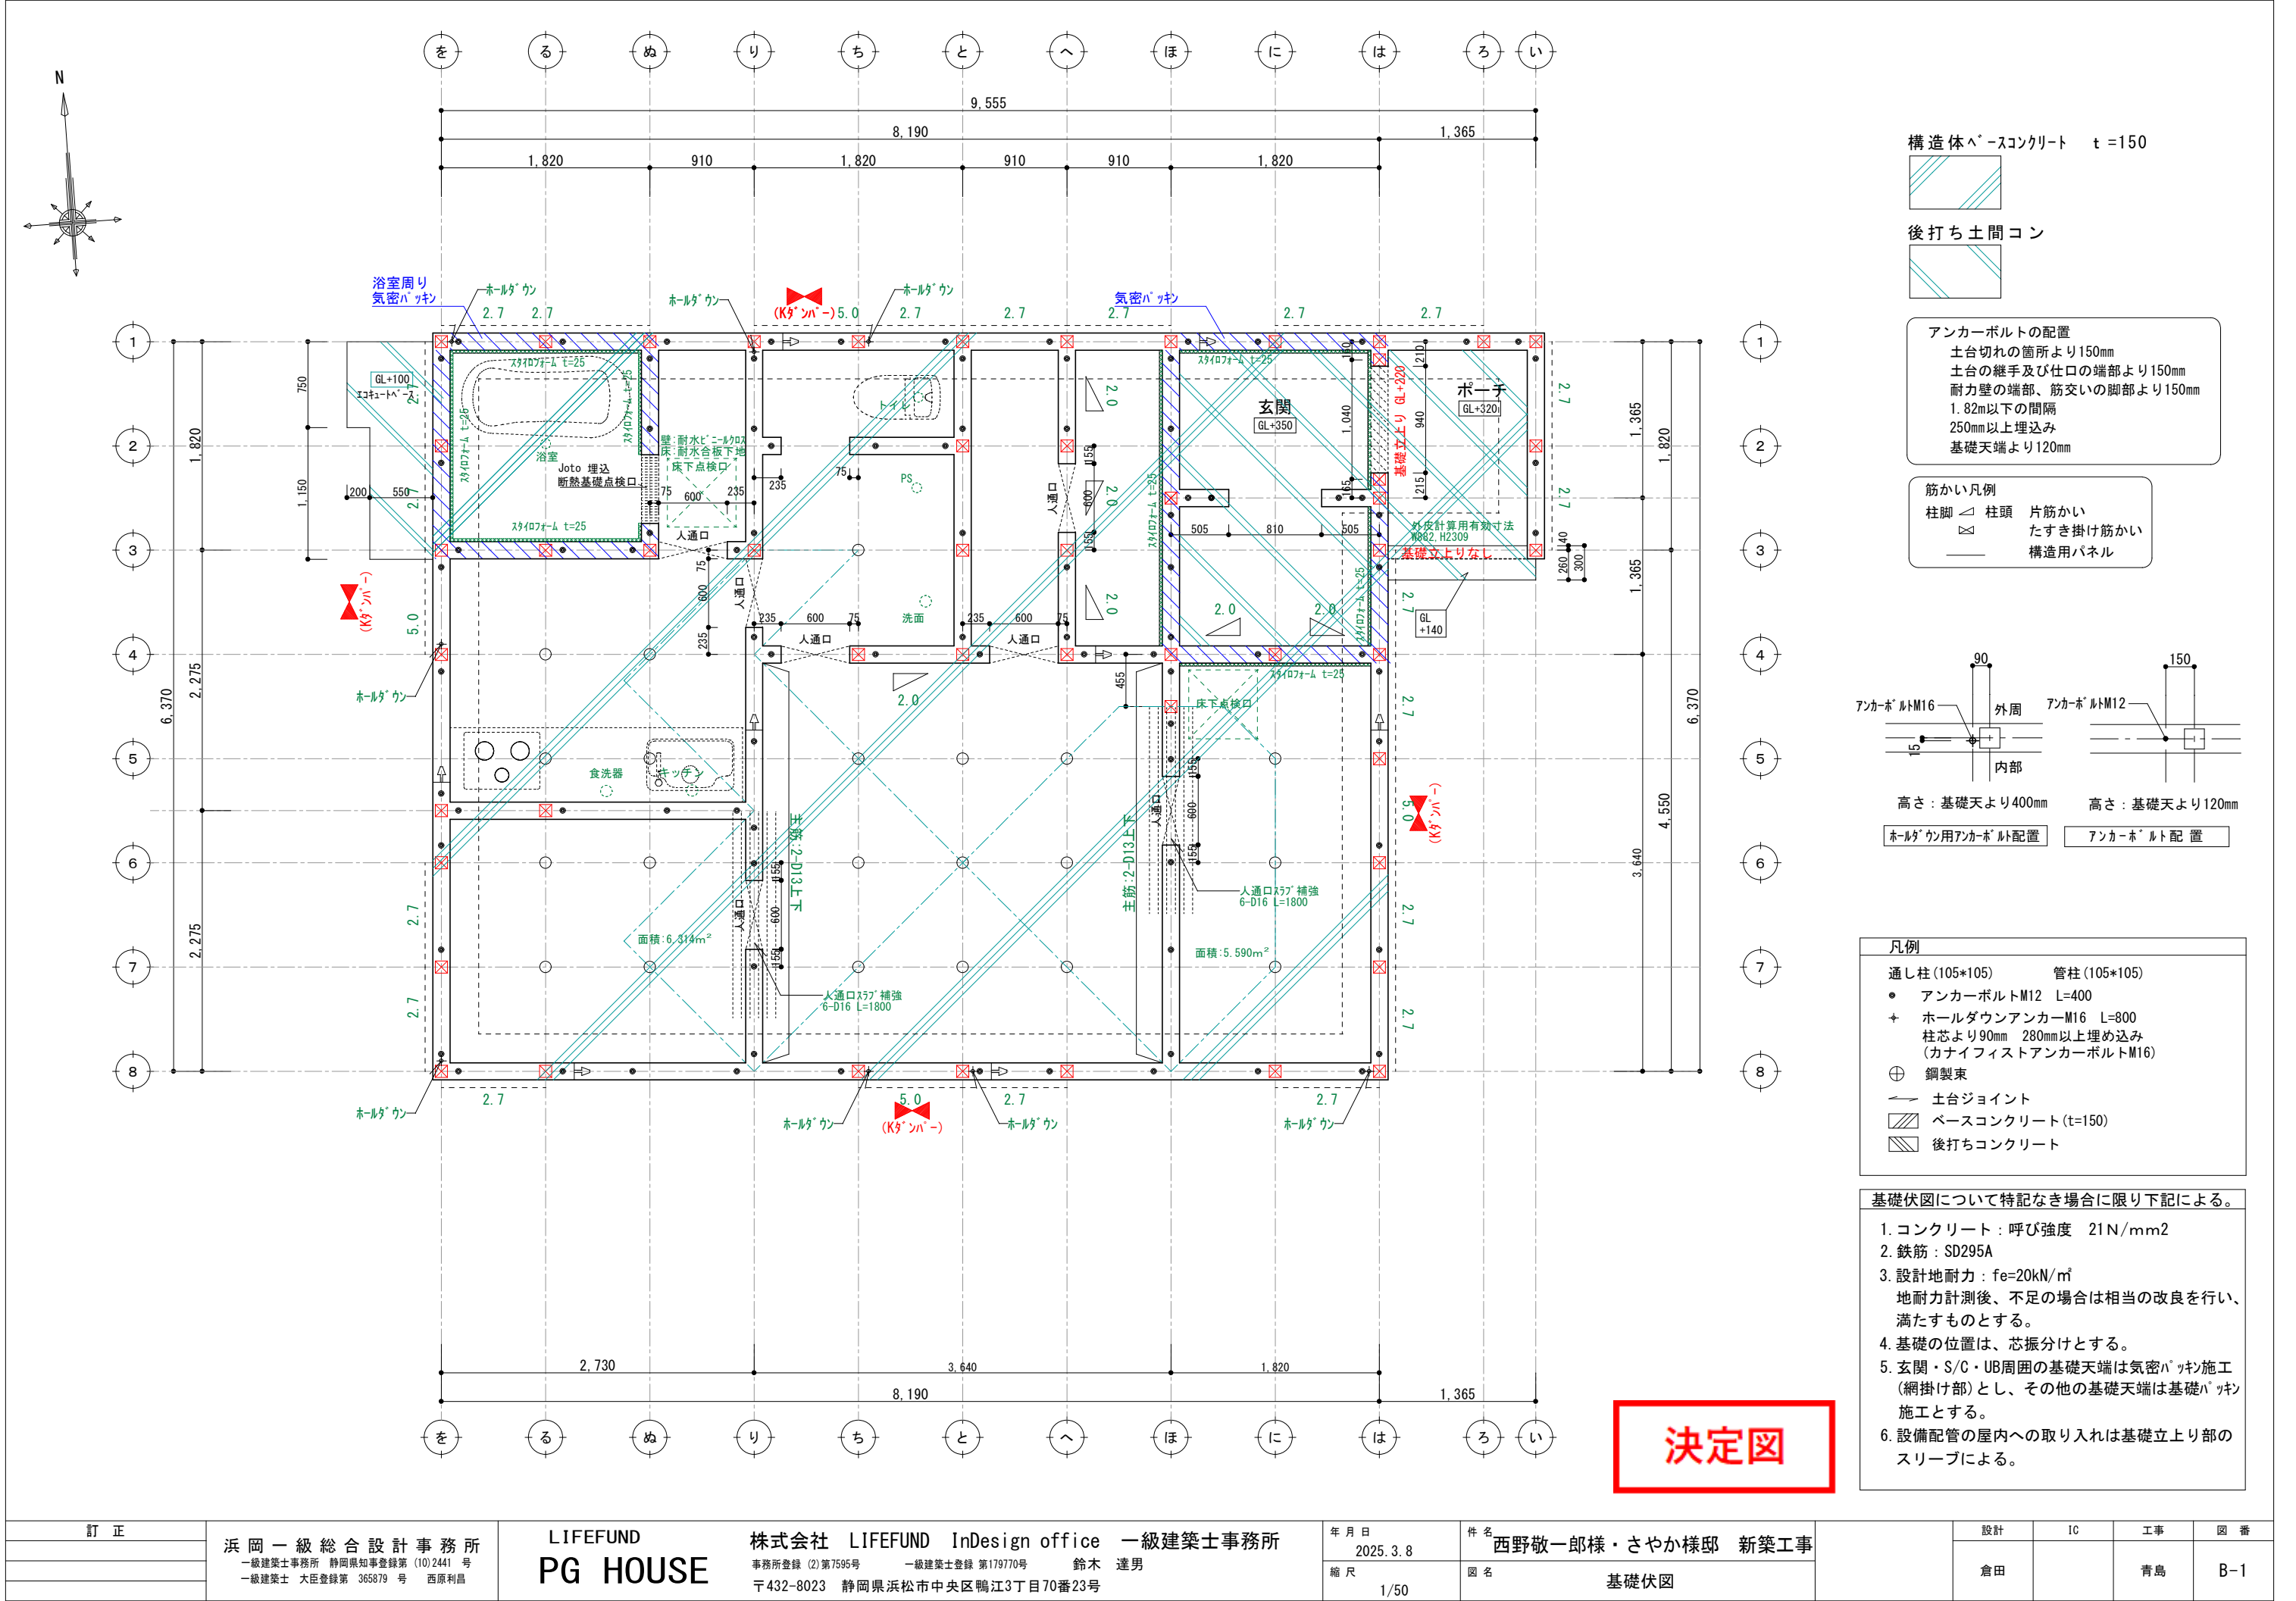


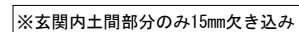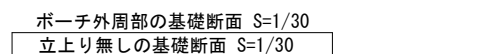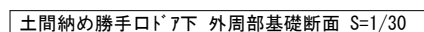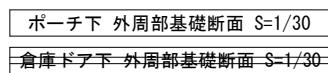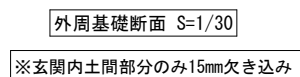

※注意：基礎伏図に特記のない内部基礎の場合

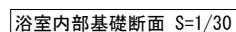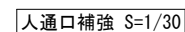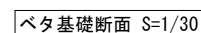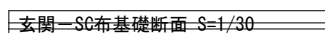


※注意：基礎伏図に特記のない内部基礎の場合

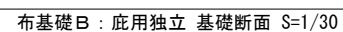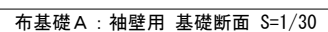


決定図

訂 正	浜岡一級総合設計事務所 一級建築士事務所 静岡県知事登録第 (10)2441 号 一級建築士 大田登録第 365879 号 西原利昌	 ピージーハウス HOUSE	株式会社 LIFEFUND InDesign office 一級建築士事務所 事務所登録 (2) 第7595号 一級建築士登録 第179770号 鈴木 達男 〒432-8023 静岡県浜松市中央区鴨江3丁目70番23号	年月日 2025.3.8 縮尺 1/30	件名 西野敬一郎様・さやか様邸新築工事 図名 基礎断面リスト	倉田	IC 工務 図番 青島 B-2
-----	--	---	---	-------------------------------	---	----	--------------------------

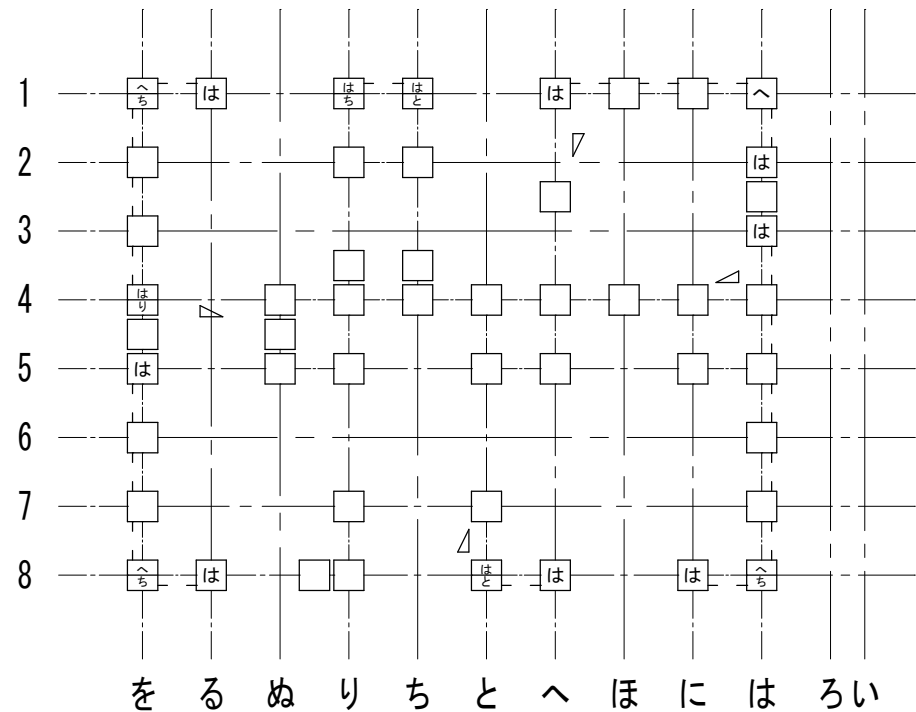

2階柱壁伏図

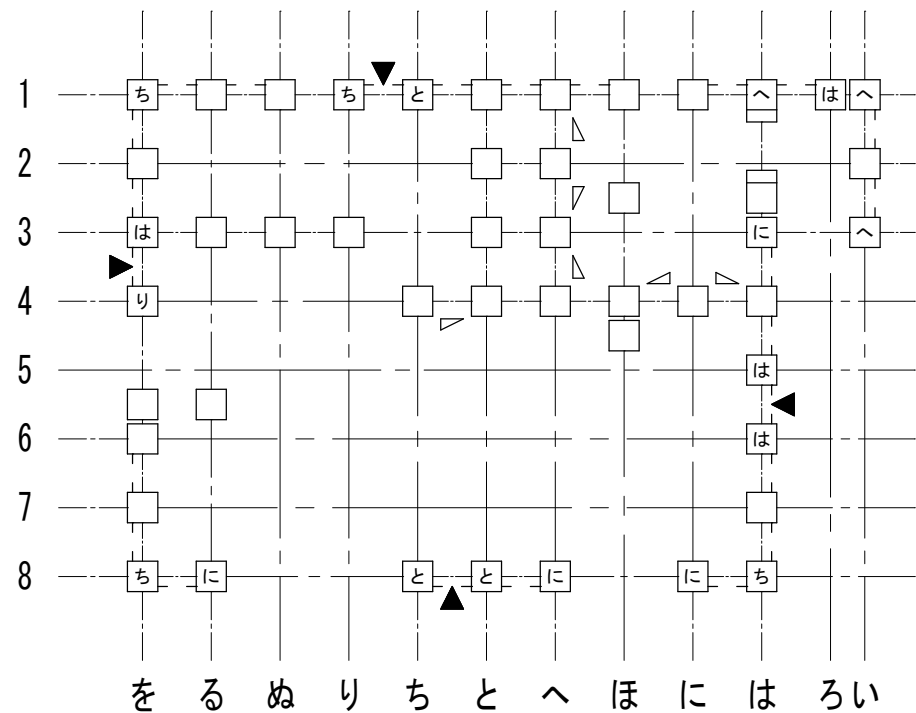

1階柱壁伏図

接合部凡例				*接合部凡例はユーザ設定されたものです。	
記号	仕様（カナイ金物）		N	倍率	
SBCP	スリムビルドコーナー75		0.00	1.00	
SBCP	スリムビルドコーナー75		0.65	1.00	
SBCP	は	スリムビルドコーナー75	1.00	1.00	
ARCG	に	アレントコーナー合板用	1.40	2.20	
ARCG	ほ	アレントコーナー合板用	1.60	2.20	
ARCG	へ	アレントコーナー合板用	1.80	2.20	
HD15	と	ブレイブホールダウン B-HD15	2.80	3.60	
HD20	ち	ブレイブホールダウン B-HD20	3.70	4.70	
HD25	り	ブレイブホールダウン B-HD25	4.70	4.80	
HD30	ぬ	ブレイブホールダウン B-HD30	5.60	7.20	
J1	る	腰掛け蟻若しくは大入れ蟻掛け+羽子板ボルト、短冊金物		1.90	
J2	を	腰掛け蟻若しくは大入れ蟻掛け+羽子板ボルト、短冊金物×2		3.00	

※表示なき金物は「は」とする。

梁継手・仕口用

梁継手・仕口用

接合部凡例				*接合部凡例はユーザ設定されたものです。	
記号	仕様（タナカ金物）		N	倍率	
FCP	フックコーナー		0.00	1.00	
FCP	フックコーナー		0.65	1.00	
FCP	は	フックコーナー	1.00	1.00	
GCP	に	シナコーナー	1.40	2.20	
GCP	ほ	シナコーナー	1.60	2.20	
GCP	へ	シナコーナー	1.80	2.20	
HD15	と	ビス止めホールダウンU HD15	2.80	3.60	
HD20	ち	ビス止めホールダウンU HD20	3.70	4.70	
HD25	り	ビス止めホールダウンU HD25	4.70	4.80	
HD30	ぬ	ビス止めホールダウンU HD15×2 (HD35)	5.60	7.20	
J1	る	腰掛け蟻若しくは大入れ蟻掛け+羽子板ボルト、短冊金物		1.90	
J2	を	腰掛け蟻若しくは大入れ蟻掛け+羽子板ボルト、短冊金物×2		3.00	

※表示なき金物は「は」とする。


梁継手・仕口用

梁継手・仕口用

筋かいの種類に応じた筋かいの端部の接合部の仕様		
	筋かいの種類	接合部の仕様（構造方法）
イ	鉄筋φ9	柱又は横架材を貫通し、三角座金を介してナット締め、又は鋼板添え板を用い鋼板を柱及び横架材にCN90, 8本平打ち
ロ	筋かい:15×90	柱・横架材を欠き込み、柱・横架材双方に対してN65, 5本平打ち
ハ	筋かい:30×90	鋼板添え板t=1.6mmを筋かいに対してボルトφ12及びCN65, 3本平打ち、柱に対してCN65, 3本平打ち、横架材に対してCN65, 4本平打ち。筋かいプレートBP同等品
ニ	筋かい:45×90	鋼板添え板t=2.3mmを筋かいに対してボルトφ12及びスクリュー釘φ4.5L50, 7本平打ち、柱及び横架材に対してスクリュー釘φ4.5L50, 5本平打ち。筋かいプレートBP-2同等品
ホ	筋かい:90×90	柱又は横架材にボルトφ12mmを用いて一面剪断接合

胴差と通し柱の接合部の仕様		
	胴差と通し柱の条件	仕口
T1	通し柱の片側に胴差が来る場合	胴差を柱にかたぎ大入れ短ほぞ差しの上、羽子板ボルト、かね折り金物又は同等以上の仕口
T2	通し柱の両側に胴差が来る場合	胴差を柱にかたぎ大入れ短ほぞ差しの上、短冊金物又は、同等以上の仕口で胴差相互を緊結
T3	通し柱と胴差の接合部の近くに90×90以上の筋かいが来る場合(通し柱が建物の出隅にあるか、筋かい壁が外壁と直交して接する場合)	胴差を通し柱に、15KN用引き寄せ金物を水平に用いて緊結

決定図

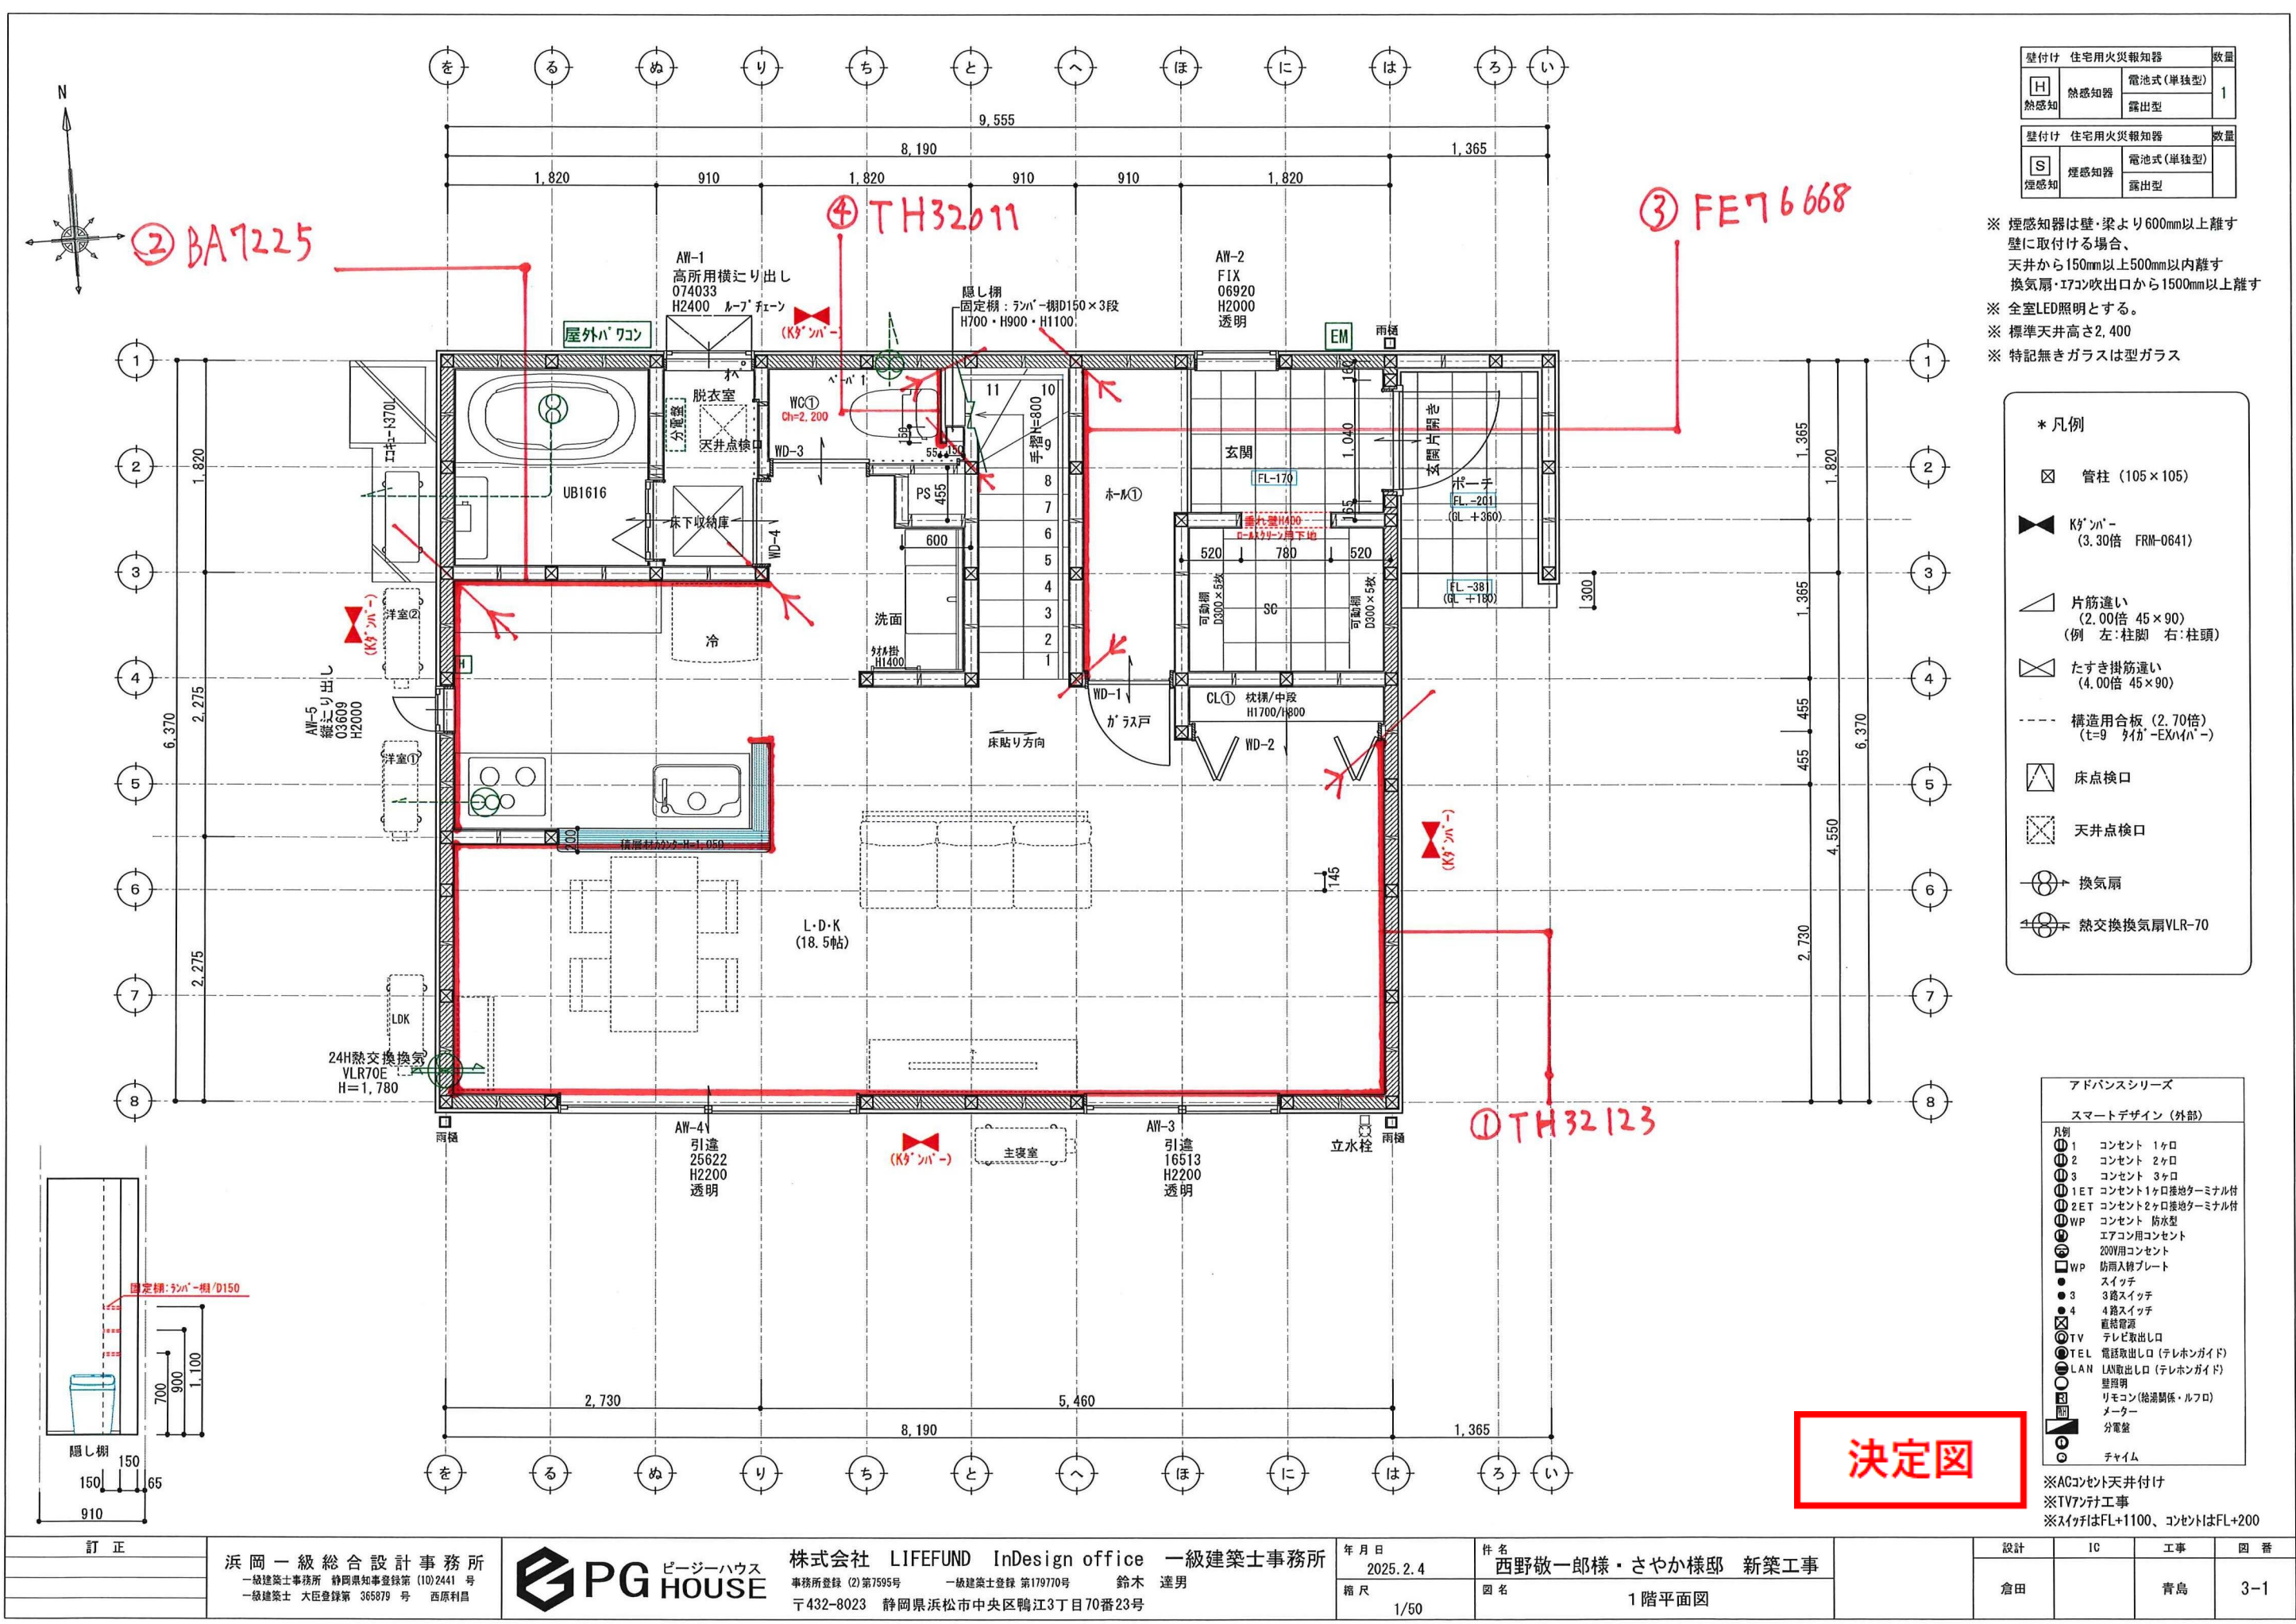

壁付け 住宅用火災報知器			数量
H	熱感知器	電池式(単独型)	1
S	煙感知器	電池式(単独型)	


※ 煙感知器は壁・梁より600mm以上離す
壁に取付ける場合、
天井から150mm以上500mm以内離す
換気扇・エアコン出口から1500mm以上離す
※ 全室LED照明とする。
※ 標準天井高さ2,400
※ 特記無きガラスは型ガラス

- * 凡例
- 管柱 (105×105)
 - Ky'ンパ- (3.30倍 FRM-0641)
 - 片筋違い (2.00倍 45×90)
(例 左:柱脚 右:柱頭)
 - たすき掛筋違い (4.00倍 45×90)
 - 構造用合板 (2.70倍)
(t=9 タイカ-EXV(ハ-))
 - 床点検口
 - 天井点検口
 - 換気扇
 - 熱交換換気扇VLR-70

アドバンスシリーズ	
スマートデザイン (外部)	
凡例	
1	コンセント 1ヶ所
2	コンセント 2ヶ所
3	コンセント 3ヶ所
1ET	コンセント1ヶ所接地ターミナル付
2ET	コンセント2ヶ所接地ターミナル付
WP	コンセント 防水型
WP	エアコン用コンセント
WP	200V用コンセント
WP	防雨入替プレート
スイッチ	スイッチ
3	3路スイッチ
4	4路スイッチ
直結電源	直結電源
TV	テレビ取出口
TEL	電話取出口 (テレホンガイド)
LAN	LAN取出口 (テレホンガイド)
壁照明	壁照明
リモコン	リモコン (給湯関係・ルフロ)
メーカー	メーカー
分電盤	分電盤
チャイム	チャイム

※ACコンセント天井付け
※TVアンテナ工事
※スイッチはFL+1100、コンセントはFL+200

決定図

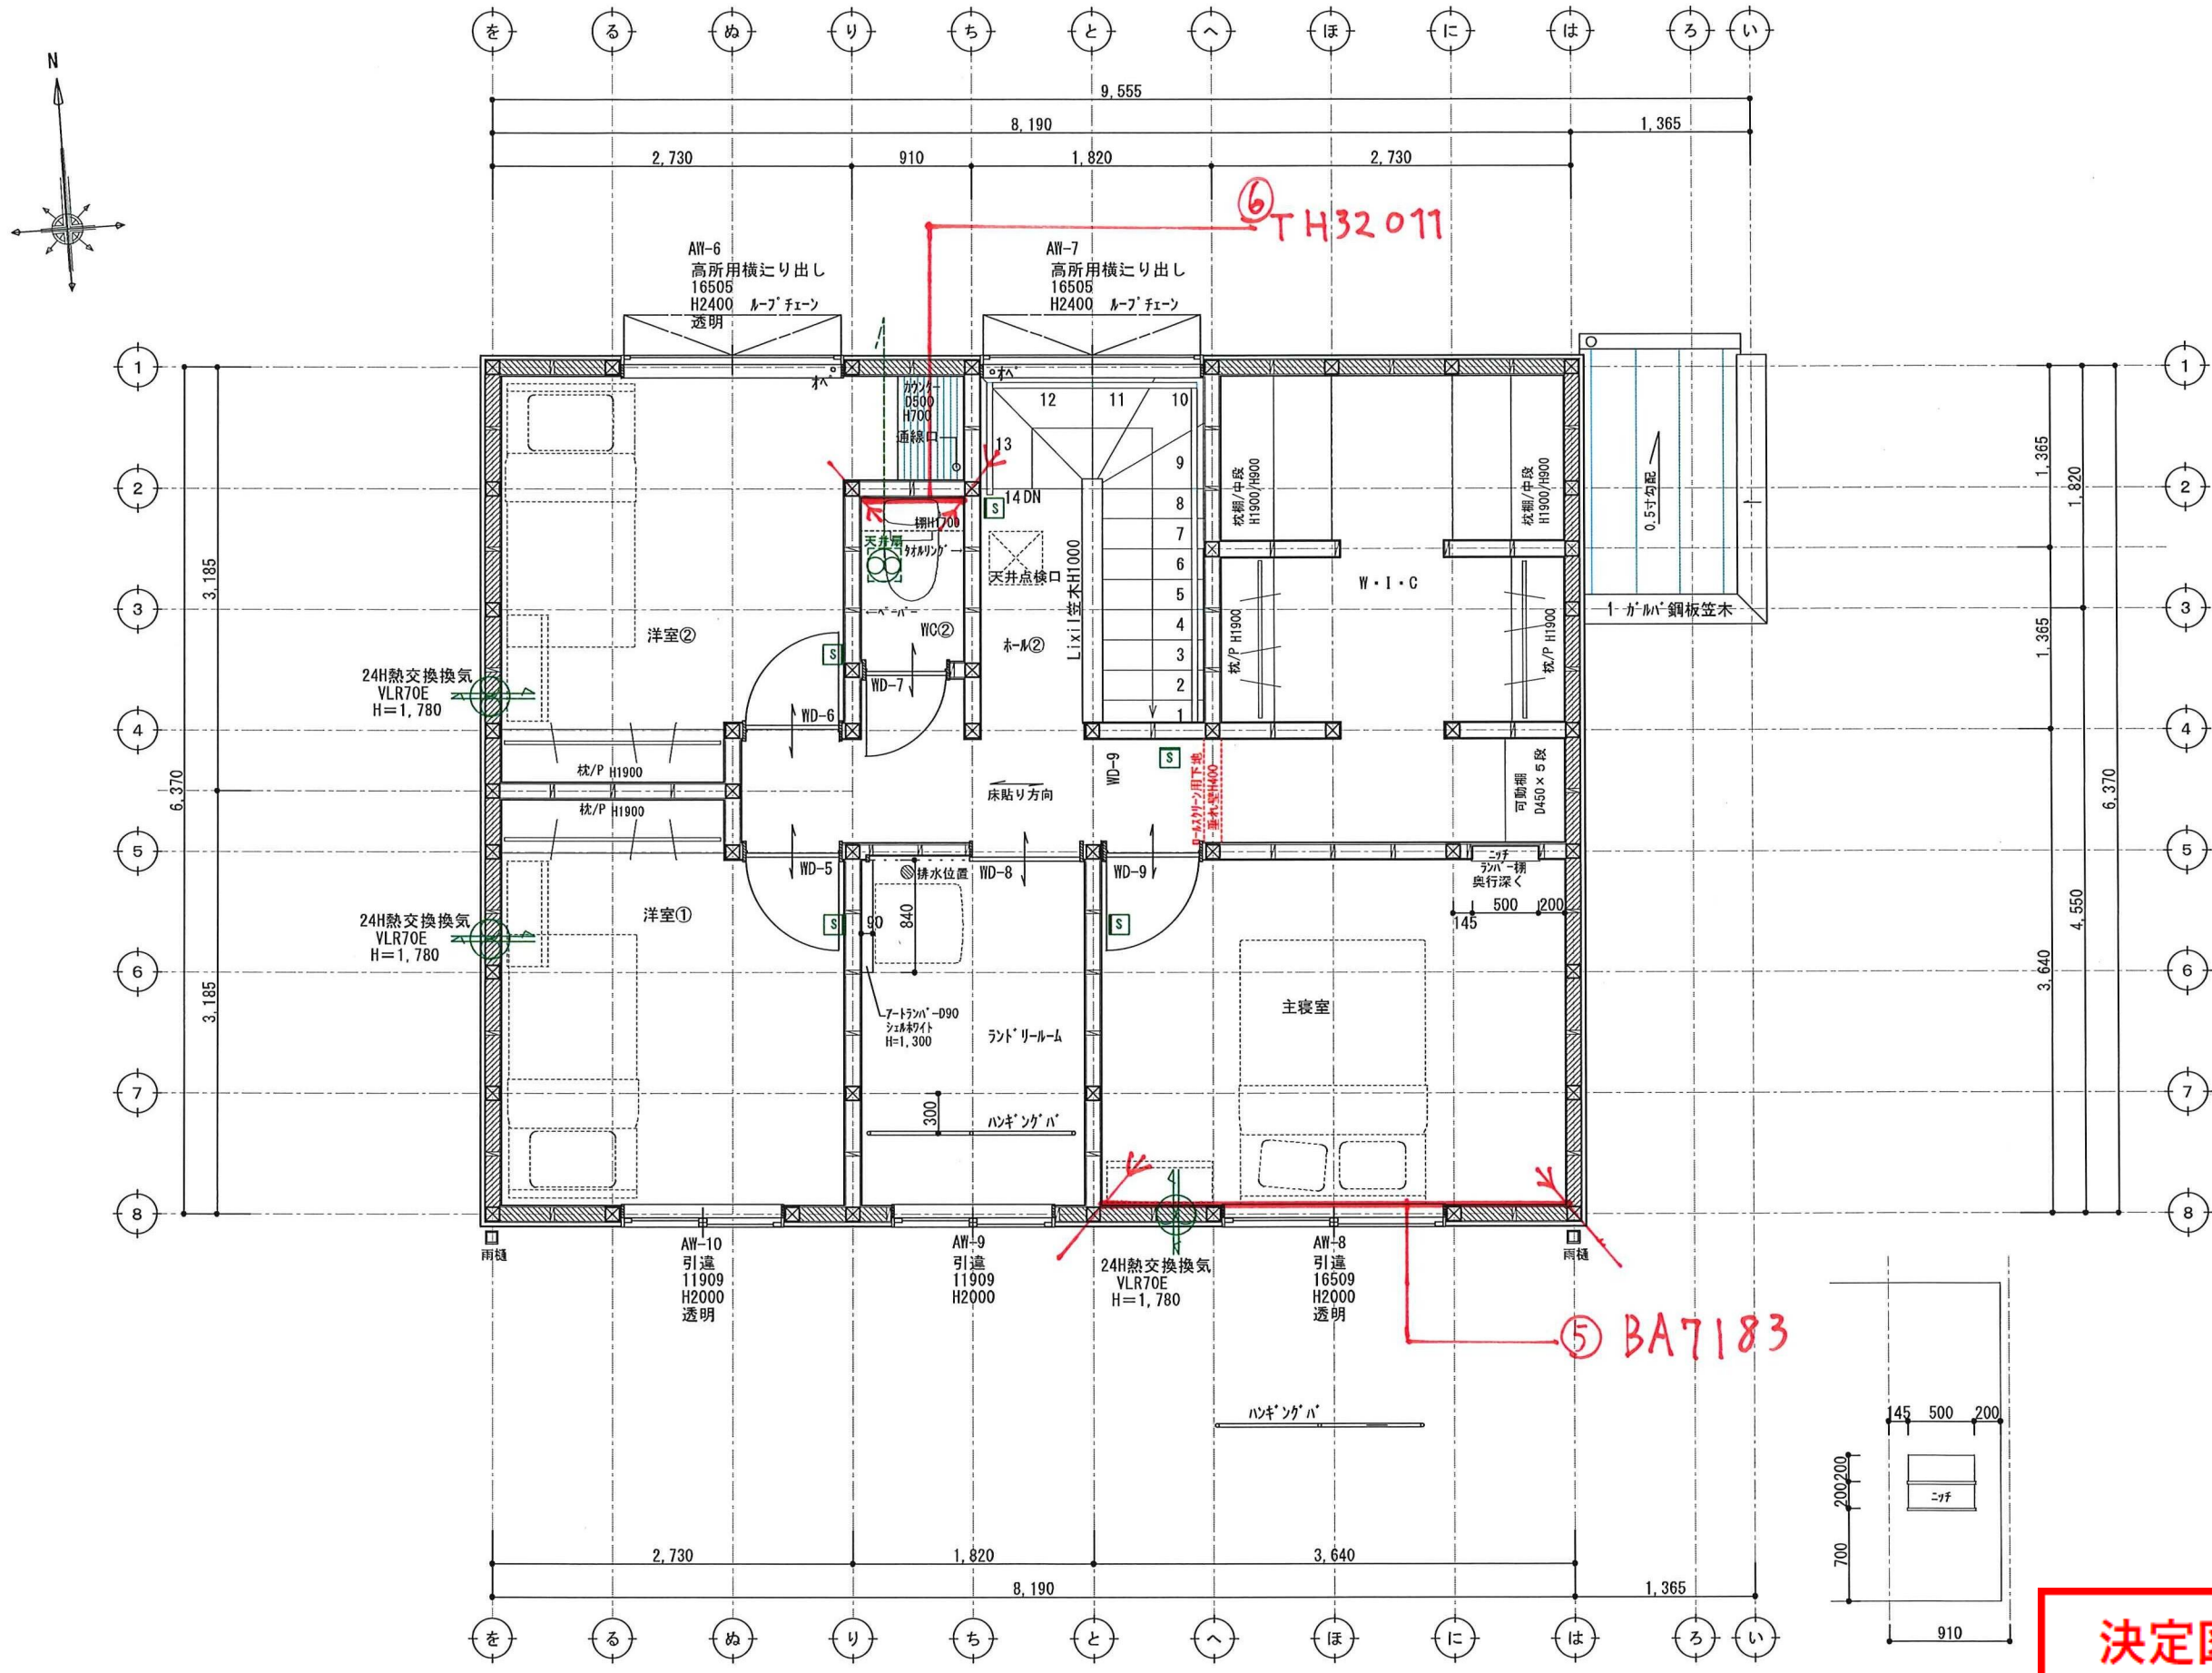

壁付け 住宅用火災報知器			数量
H 熱感知	熱感知器	電池式(単独型)	4
		露出型	
壁付け 住宅用火災報知器			数量
S 煙感知	煙感知器	電池式(単独型)	4
		露出型	

※ 煙感知器は壁・梁より600mm以上離す
壁に取付ける場合、
天井から150mm以上500mm以内離す
換気扇・エアコン吹出口から1500mm以上離す

※ 全室LED照明とする。

※ 標準天井高さ2,400

※ 特記無きガラスは型ガラス

- * 凡例
- ☒ 管柱 (105×105)
 - ▲ Kダクト (3.30倍 FRW-0641)
 - △ 片筋違い (2.00倍 45×90)
(例 左:柱脚 右:柱頭)
 - ⊠ たすき掛筋違い (4.00倍 45×90)
 - 構造用合板 (2.70倍)
(t=9 タイグ EXH41A-)
 - ⬆ 床点検口
 - ⬆ 天井点検口
 - ⊕ 換気扇
 - ⊕ 熱交換換気扇VLR-70

アドバンスシリーズ	
スマートデザイン (外部)	
凡例	
①	コンセント 1ヶ所
②	コンセント 2ヶ所
③	コンセント 3ヶ所
①ET	コンセント1ヶ所接地ターミナル付
②ET	コンセント2ヶ所接地ターミナル付
WP	コンセント 防水型
⊕	エアコン用コンセント
⊕	200V用コンセント
WP	防雨入線プレート
スイッチ	スイッチ
3	3路スイッチ
4	4路スイッチ
直結電線	直結電線
TV	テレビ取出口
TEL	電話取出口 (テレホンガイド)
LAN	LAN取出口 (テレホンガイド)
照明	照明
リモコン	リモコン (給湯関係・ルーフ)
メーター	メーター
分電盤	分電盤
チャイム	チャイム

※ACコンセント天井付け
※TVアンテナ工事
※スイッチはFL+1100、コンセントはFL+200

決定図