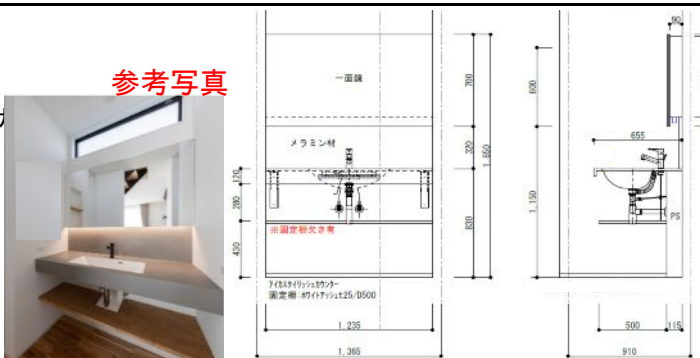


■ 仕 様				■ HEAT20 G1	
断熱工事		■ 床:カネライトフォーム t65 ■ 土間床等の外周:スタイロフォームAT t25 ■ 壁:アクアフォームLITE吹付 t85 ■ 天井:アクファフォームLITE吹付 t170			
床下換気		■ 基礎パッキン JOTO (玄関・UB周り:気密基礎パッキン)			
防虫防蟻		■ 土壌処理・木部 ガントナーMC			
■ 外 部 仕 上 表				■ 22条地域	
部位		仕上・仕様・メーカー		色番・品番	
屋根		■ ガルバリウム鋼板(t0.35)UK立平 ニスクカラーPro GH 軒先通気金物 日本住環境株式会社【REV-15】		GHK01 Sブラック	
パラペット笠木		■ なし			
破風・鼻隠		■ なし			
雨樋	(軒樋)	■ Panasonic サーフেসケアFS-I型		オークグレー	
	(縦樋)	■ Panasonic S30角樋		オークグレー	
軒天	屋根軒	■			
	ポーチ軒	■ ニチハ軒天5 木目調 910×1820×5		ライト	
	バルコニー軒	■			
オーバーハング水切り		■ ガルバリウム鋼板 ※外壁合わせ JOTO:HF-A3550			
外壁 ※下地面材:タイガーEXハイパー 防火認定 PC030BE-4028	通気金物(15mm)	■メイン	Kmewエクセレージ・シマンフラット	ソイルダークグレー EW7304	
		■アクセントA	なし		
		■アクセントB	なし		
玄関ポーチ		■ 床 玄関タイルに同じ		-	
基礎		■ 立上り巾木: モルタル刷毛引き		-	
基礎水切り金物		■ JOTO鋼板製 防鼠材付き水切り JOTO:WMF-N35		ブラック	
バルコニー	床・内壁	■ なし		-	
	笠木	■ なし			
外部建具		■ LIXIL EW(アルゴンガス高遮熱仕様LowE複層ガラス クリーン) ・SD、TSは、メーカー設定によるが、オペレーターハンドル優先とする ・オペレーター付サッシの場合は固定網戸とする ・グレモンハンドル式サッシの場合は可動網戸とする		外観 ブラック 内観 ショドーオークforDesign ※樹脂パッキン・網戸付	
シャッター		■ 窓シャッターは手動			
軒天通気金物				ブラック	
玄関扉		■ LIXIL ジエスタ2 K2仕様 LIXILファミロック タグキー×3 (電池式)		ドア型: M17 型 ドア色: ラスティックオーク ハンドル: S型ハンドル 色 ブラック	
外部物干し金物		■ 川口技研RK型-550 外壁付		ブラック	
換気フード		■ 局所換気扇(トイレ 浴室 キッチンフード) 防火ダンパー無		外気フード: シルバー	
		■ ダクトレス熱交換換気システム (日本スティーベル株式会社) VLR-70E 防火ダンパー無		外気フード: S シルバー 室内パネル ホワイト	

■ 構 造 概 要				
基礎	■ RCベタ基礎コンクリート			
通し柱・管柱	■ 構造用集成材 105×105		間柱	■ 集成材
土台	■ 桧 105×105	大引き ■ 桧 90*90	筋交い	■ 構造用製材 火打梁 ■ 鋼製火打(当社基準により米松あり)
桁・梁	■ 構造用製材及び集成材		制震装置	■ Kダンパー (株)アイ・エム・エー
■ 設 備 装 着 品				
住宅設備	部位	メーカー	商品名 ※ 詳細は見積り、プレゼン参照	見積りNo. (日付)
	キッチン	LIXIL	■ ES I型 扉グレージュスタック 天板ソルティホワイト キッチンパネル:フレッシュホワイト 標準食洗器 標準IH、壁付レンジフードASR(シルバー) スリム取手ブラック キレイシンク	見積り番号 : M25026434852-002 (日付) 2025/2/4
	バックカウンタ ※オプション	LIXIL	■ ES L1800(W900スライドストッカー+マルチスペース)	見積り番号 : M25026434852-002 (日付) 2025/2/4
	浴室	LIXIL	■ AX1616 PGハウス標準仕様 アクセント壁:シルバーグレー 浴槽:ストリートライン ホワイト 床:ホワイト マグネットシェフ:不要 開き戸	見積り番号 : M25026434852-002 (日付) 2025/2/4
	トイレ	LIXIL	■ ベーシアシャワートイレ 白 ● タオル掛け: タンク手洗 無し ● 紙巻き器: CF-AA22H /WA ■ トイレ コーナーウォールキャビネット SUA-CN101 ホワイト	見積り番号 : M25026434852-002 (日付) 2025/2/4
	洗面台	造作	■ 洗面 アイカスタイルッシュカウンター ミラー:一面鏡(下部照明) ボウル:ボウル5 水栓:K4750NV-MDP/アイカ カウンター・立上り部分:TJ-10239K 棚:ゴム集成材(オスモリアMAT) タオル掛けは支給品取付	
給排水設備	給湯器	■ エコキュート370L Panasonic NSシリーズ スタンダードモデル 追い焚きフルオート※在庫限り		
	排水	■ 下水		
	外水栓	■ 1 カ所 (平面図参照)	■ 外部立栓柱: PVC製 水栓柱12型【前澤化成工業】	
	外部ガーデンパン	■ 無し		
	その他	■ 洗濯機用単水栓: 緊急止水弁付 ■ 洗濯機用排水: トラップ金物(標準) ■ 排水さや管(長期優良住宅仕様)		
ガス配管設備		■ なし (配置図・平面図参照) ■ガス使用器具 すべての熱源 専用架台		
電気設備	インターホン	■ パナソニック VL-SZ30KL		
	TVアンテナ	■ UHF + BS・110度CS/CSアンテナ [2K・4K・8K対応] ■ホワイト		
	エアコン	■ 設置場所:		
	ソーラー ※標準搭載	■ あり(Qセルズ) 12 枚 5.28 KW Re.RISE-G3 440 (1722×1134×30) ■ 屋外パワコン		
その他				

決定図

浜 岡 一 級 総 合 設 計 事 務 所			株式会社 LIFEFUND InDesign office 一級建築士事務所		年 月 日	件名		設計	IC	工務	図 番	
一級建築士事務所 静岡県知事登録第 (10)2441 号			事務所登録 (2)第7595号 一級建築士登録 第179770号 鈴木 達男		2025.04.09	尾高麻琴様 恵様 邸新築工事		倉田		青島	1-1	
一級建築士 大臣登録第 365879 号 西原利昌			〒432-8023 静岡県浜松市中央区鴨江3丁目70番23号		縮尺	図面						
						仕上表 1						