太陽光搭載あり

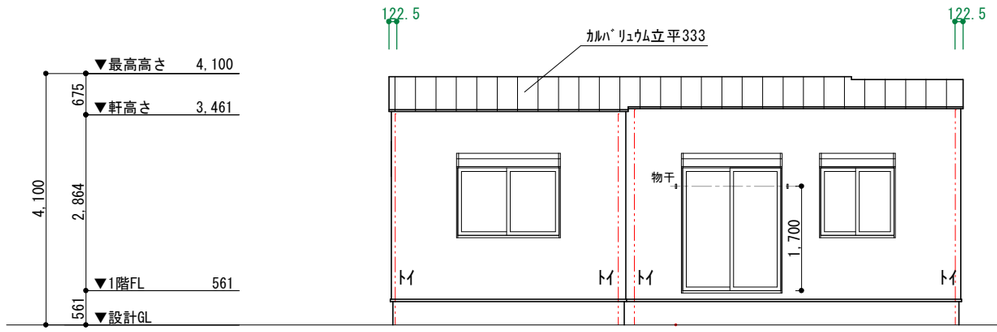

南立面図 S=1/100

南側立面図 S=1/100

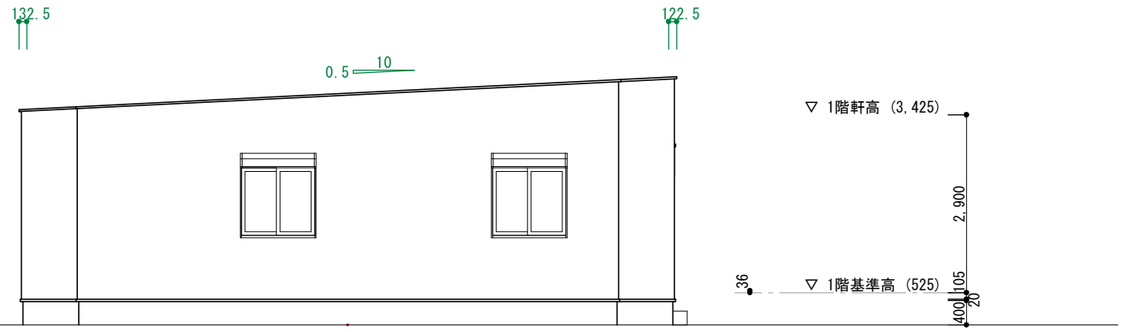

東立面図 S=1/100

東側立面図 S=1/100

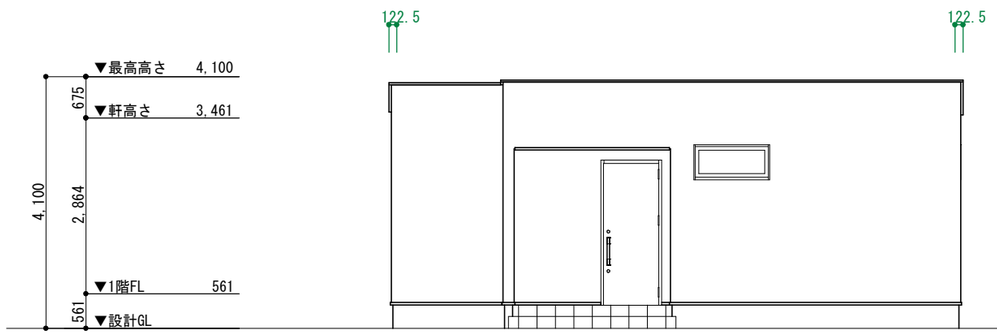

北立面図 S=1/100

北側立面図 S=1/100

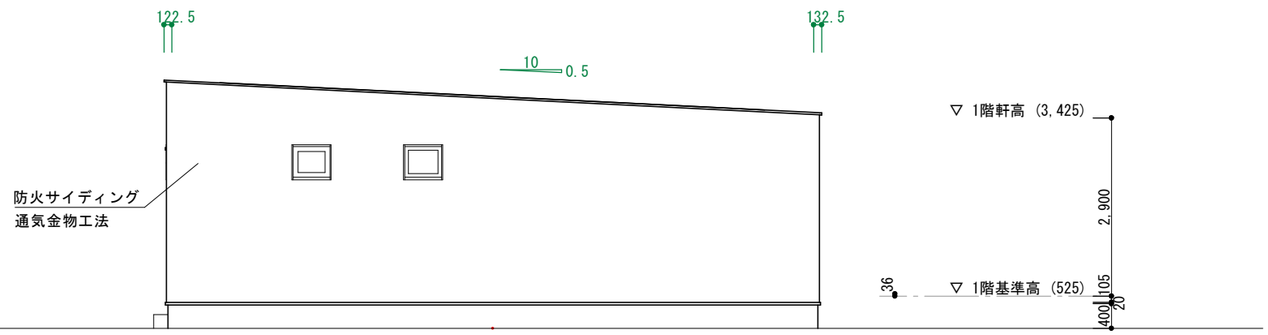

西立面図 S=1/100

西側立面図 S=1/100

決定図

訂正	浜岡一級総合設計事務所 一級建築士事務所 静岡県知事登録第(10)2441号 一級建築士 大臣登録第 365879 号 西原利昌	PG ピージーハウス HOUSE 株式会社 LIFEFUND InDesign office 一級建築士事務所 事務所登録 (2)第7595号 一級建築士登録 第179770号 鈴木 達男 〒432-8023 静岡県浜松市中央区鴨江3丁目70番23号	年月日 2025.4.9 縮尺 1/100	件名 尾高麻琴様 恵様 邸新築工事 図名 立面図		設計 倉田 / IC / 工事 青島 / 図番 4