



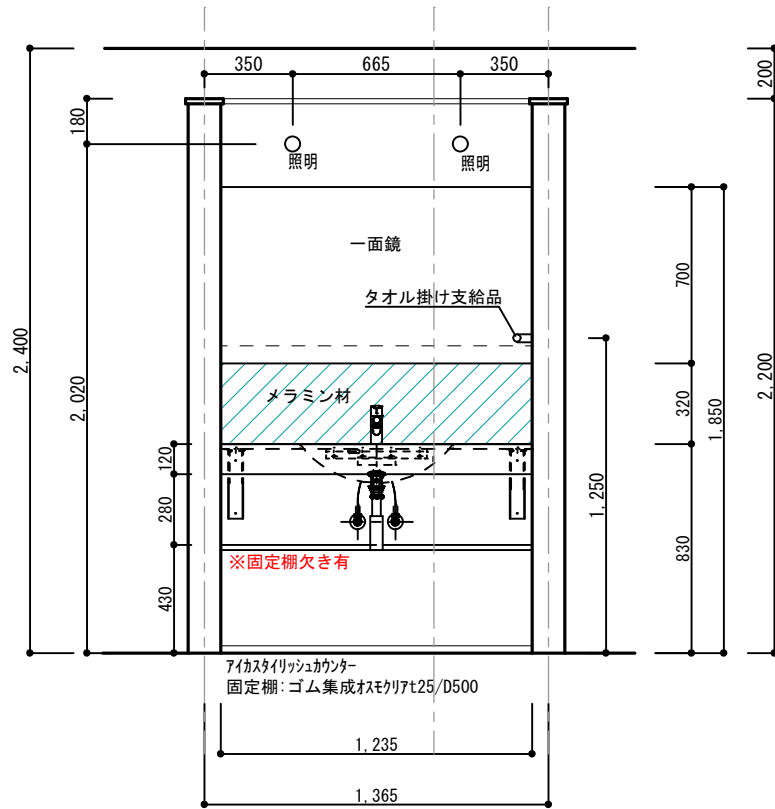


洗面 北

タオル掛け支給品取付

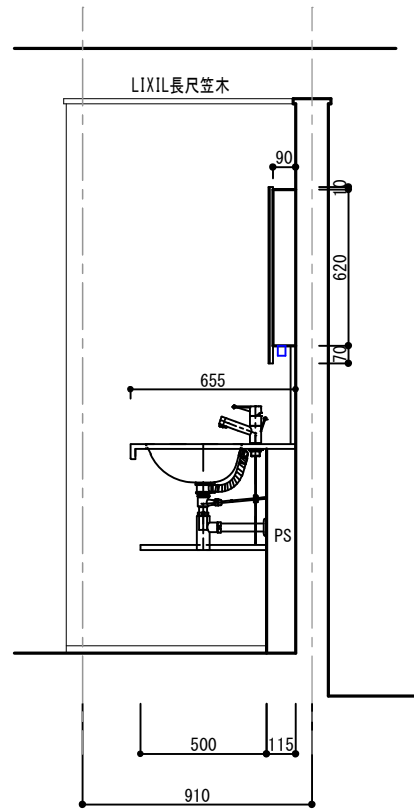

洗面 西

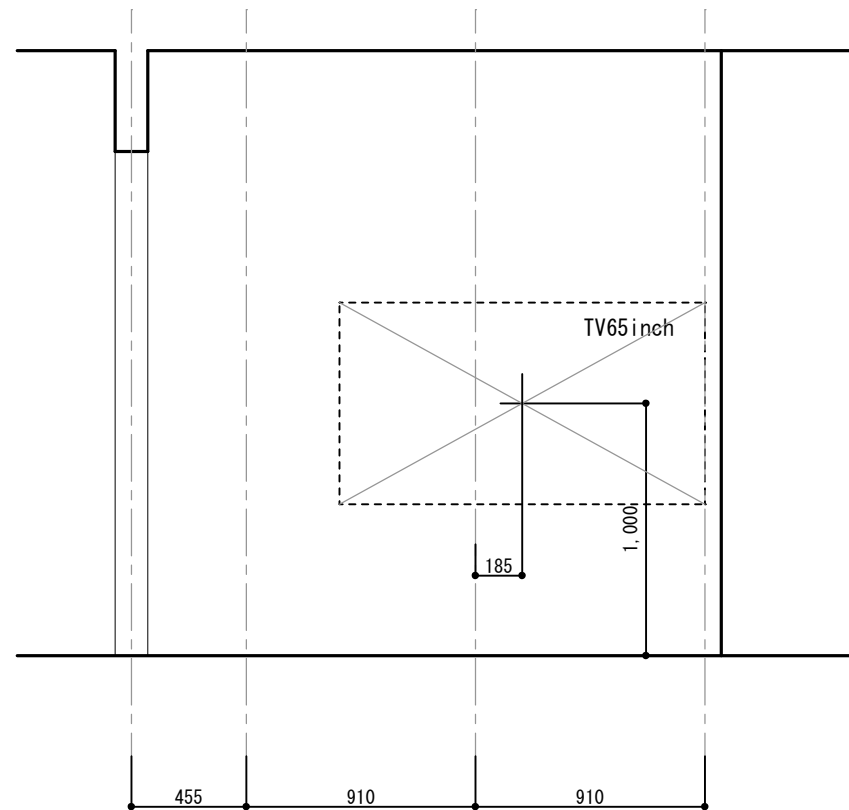

LDK 東

決定図

訂正	浜岡一級総合設計事務所 一級建築士事務所 静岡県知事登録第(10)2441号 一級建築士 大臣登録第 365879号 西原利昌	LIFEFUND PG HOUSE	株式会社 LIFEFUND InDesign office 一級建築士事務所 事務所登録(2)第7595号 一級建築士登録 第179770号 鈴木 達男 〒432-8023 静岡県浜松市中央区鴨江3丁目70番23号	年月日 2025.4.9 縮尺 1/50	件名 尾高 麻琴様 様恵様 邸新築工事 図名 展開図		設計 倉田	IC	工事 青島	図番 6-1
----	---	----------------------	---	-------------------------------	-------------------------------------	--	----------	----	----------	-----------