


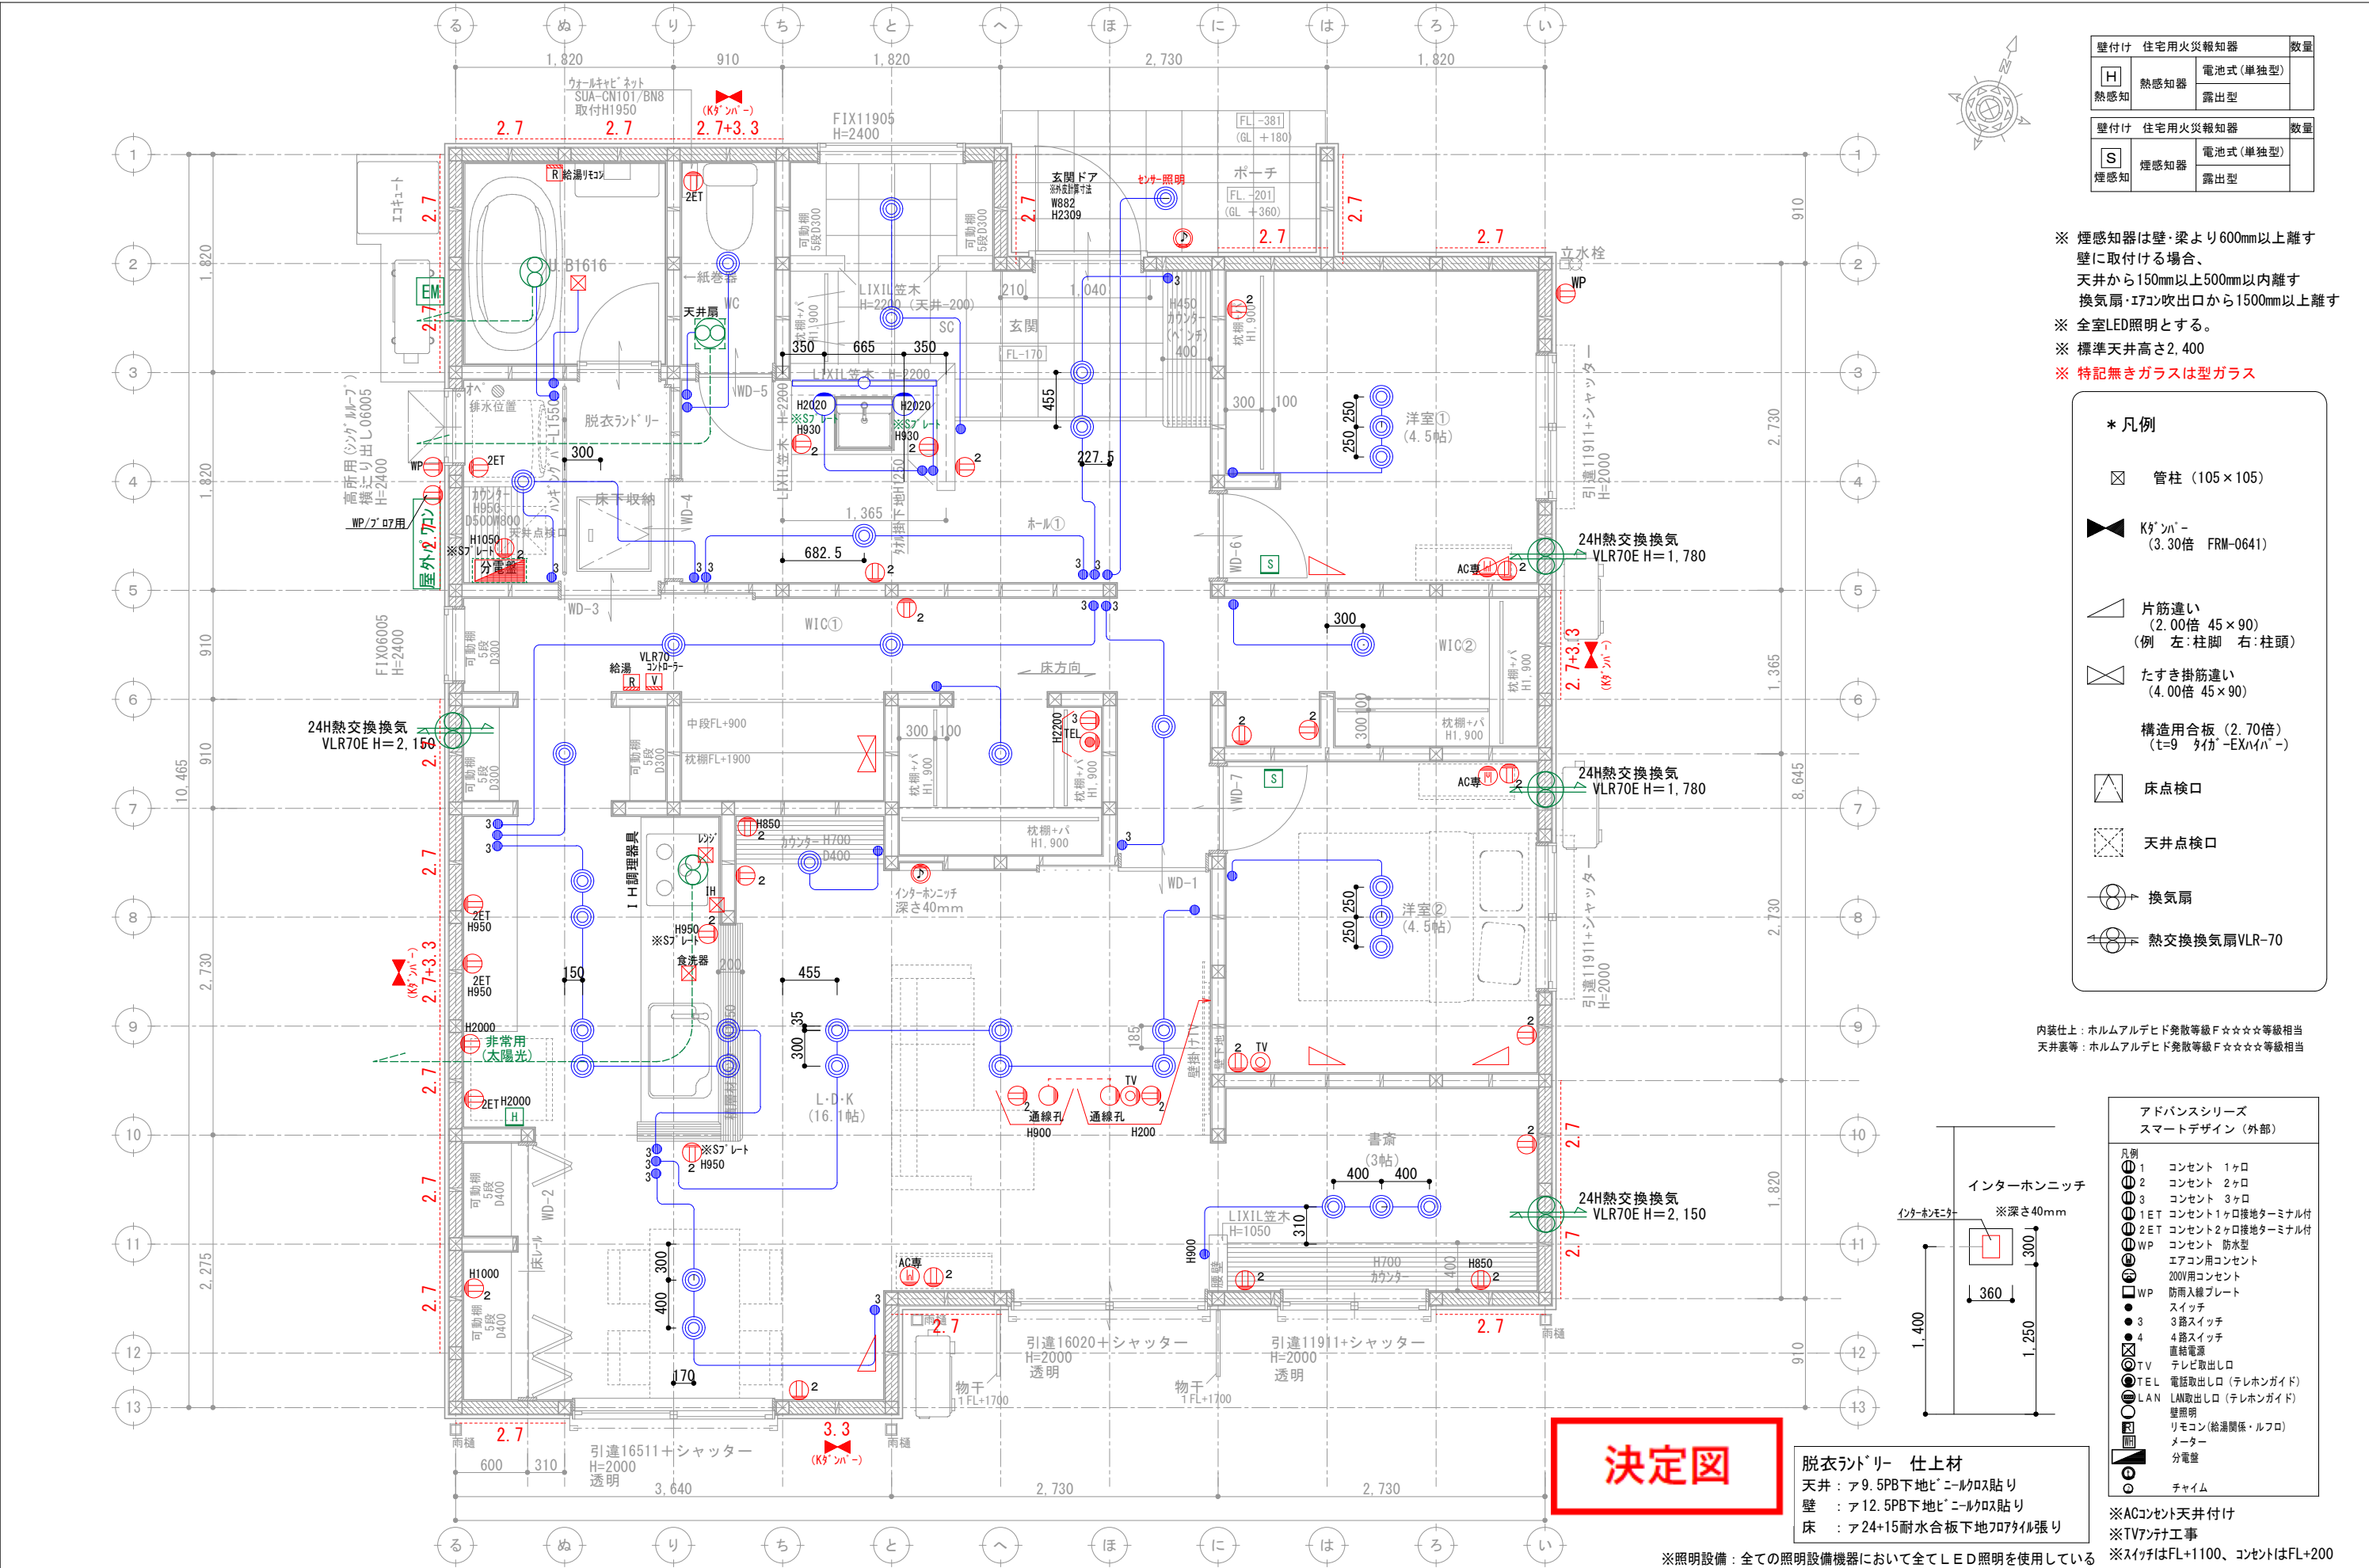

壁付け 住宅用火災報知器			数量
H	熱感知器	電池式(単独型)	
	熱感知器	露出型	
壁付け 住宅用火災報知器			数量
S	煙感知器	電池式(単独型)	
	煙感知器	露出型	

※ 煙感知器は壁・梁より600mm以上離す
壁に取付ける場合、
天井から150mm以上500mm以内離す
換気扇・エアコン吹出口から1500mm以上離す
※ 全室LED照明とする。
※ 標準天井高さ2,400
※ 特記無きガラスは型ガラス

- * 凡例
- 管柱 (105×105)
 - K's'n' (3.30倍 FRM-0641)
 - 片筋違い (2.00倍 45×90)
(例 左:柱脚 右:柱頭)
 - たすき掛筋違い (4.00倍 45×90)
 - 構造用合板 (2.70倍)
(t=9 9'f'-EX'f'n')
 - 床点検口
 - 天井点検口
 - 換気扇
 - 熱交換換気扇VLR-70

内装仕上: ホルムアルデヒド発散等級F☆☆☆☆等級相当
天井裏等: ホルムアルデヒド発散等級F☆☆☆☆等級相当

アドバンスシリーズ スマートデザイン (外部)		
凡例	1	コンセント 1ヶ所
①	2	コンセント 2ヶ所
②	3	コンセント 3ヶ所
③	1ET	コンセント1ヶ所接地ターミナル付
④	2ET	コンセント2ヶ所接地ターミナル付
⑤	WP	コンセント 防水型
⑥	⑦	エアコン用コンセント
⑧	⑨	200V用コンセント
⑩	WP	防雨入線プレート
⑪	⑫	スイッチ
⑬	⑭	3路スイッチ
⑮	⑯	4路スイッチ
⑰	⑱	直結電源
⑲	⑳	テレビ取出口
㉑	TEL	電話取出口 (テレホンガイド)
㉒	LAN	LAN取出口 (テレホンガイド)
㉓	㉔	壁照明
㉕	㉖	リモコン (給湯関係・ルフロ)
㉗	㉘	メーター
㉙	㉚	分電盤
㉛	㉜	チャイム

※ACコンセント天井付け
※TVアンテナ工事
※スイッチはFL+1100、コンセントはFL+200

決定図

脱衣ランドリー 仕上材
天井: ア9.5PB下地ビニルクロス貼り
壁: ア12.5PB下地ビニルクロス貼り
床: ア24+15耐水合板下地フロアタイル張り

※照明設備: 全ての照明設備機器において全てLED照明を使用している