


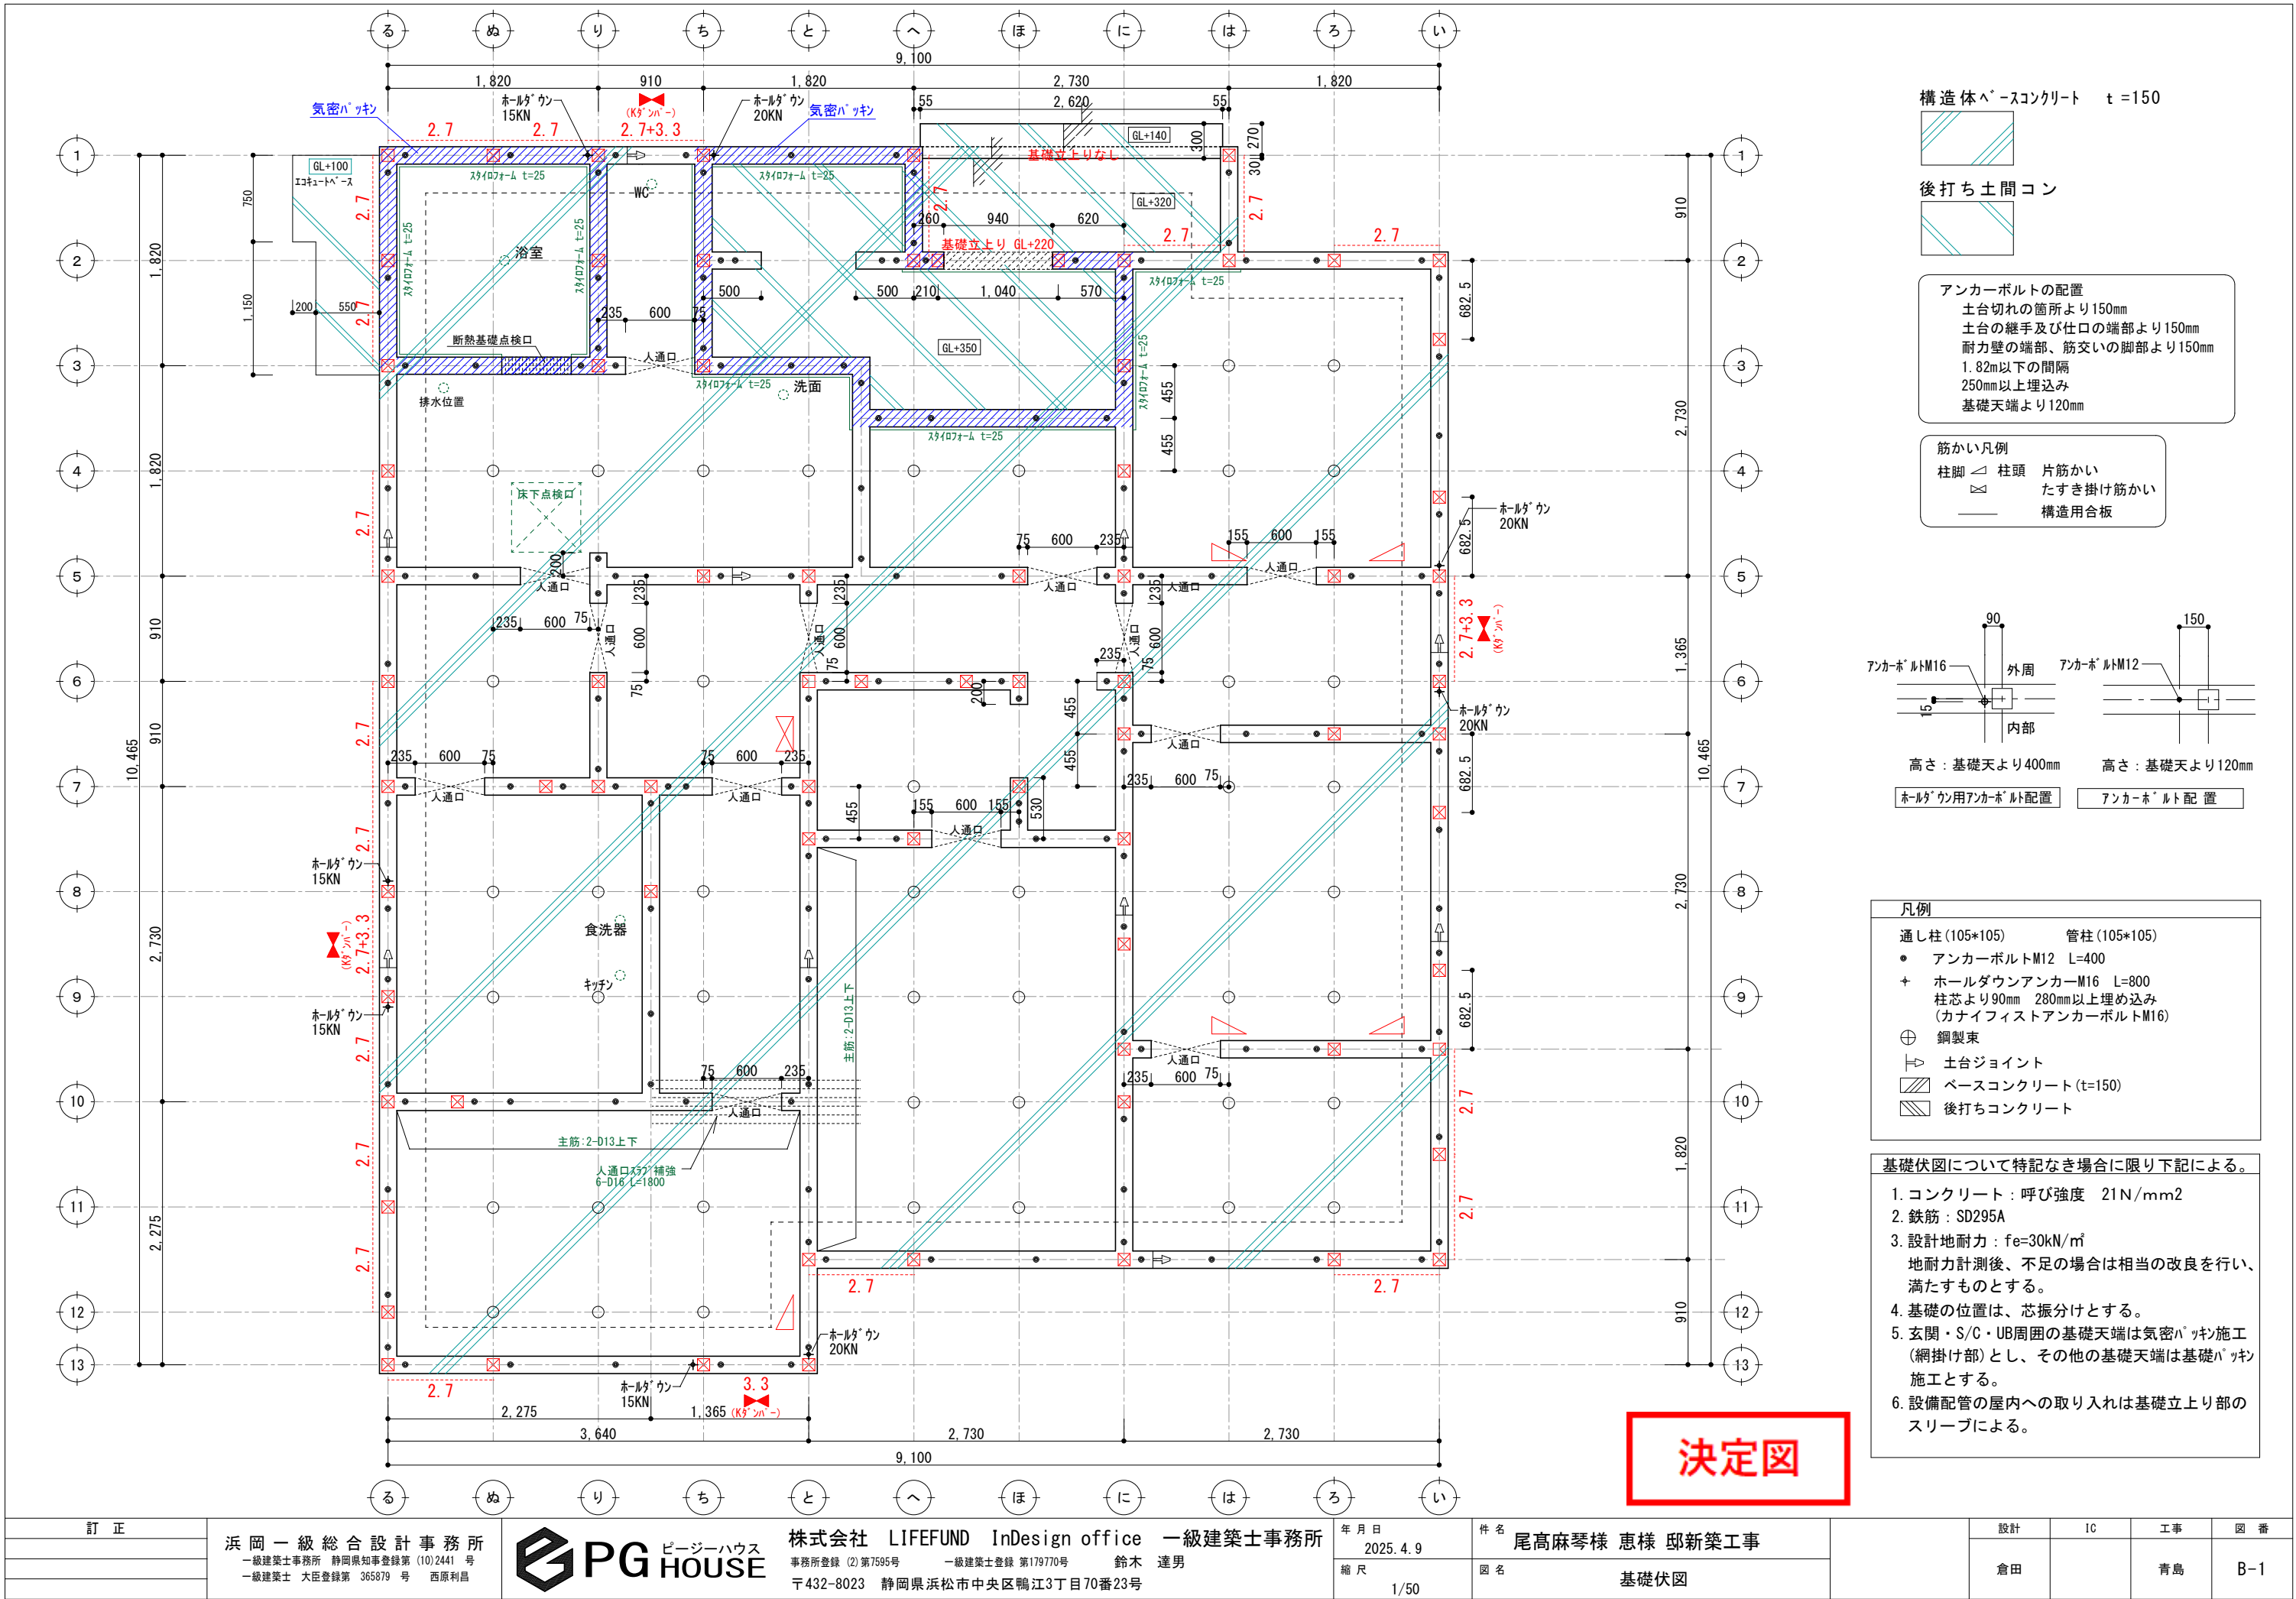

構造体ベースコンクリート t=150


後打ち土間コン

アンカーボルトの配置

- 土台切れの箇所より150mm
- 土台の継手及び仕口の端部より150mm
- 耐力壁の端部、筋交いの脚部より150mm
- 1.82m以下の間隔
- 250mm以上埋込み
- 基礎天端より120mm

筋かい凡例

- 柱脚 柱頭 片筋かい
- たすき掛け筋かい
- 構造用合板

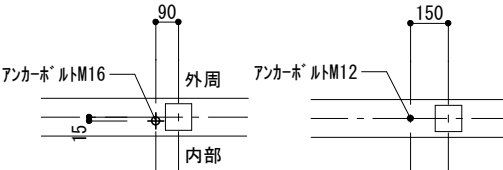

高さ：基礎天より400mm 高さ：基礎天より120mm

ホールダウン用アンカーボルト配置 アンカーボルト配置

凡例

- 通し柱(105*105) 管柱(105*105)
- アンカーボルトM12 L=400
- ✦ ホールダウンアンカーM16 L=800
- 柱芯より90mm 280mm以上埋め込み (カナフィストアンカーボルトM16)
- ⊕ 鋼製束
- ⊢ 土台ジョイント
- ▨ ベースコンクリート(t=150)
- ▨ 後打ちコンクリート

基礎伏図について特記なき場合に限り下記による。

- コンクリート：呼び強度 21N/mm²
- 鉄筋：SD295A
- 設計地耐力：fe=30kN/m²
地耐力計測後、不足の場合は相当の改良を行い、満たすものとする。
- 基礎の位置は、芯振分けとする。
- 玄関・S/C・UB周囲の基礎天端は気密パッキン施工（網掛け部）とし、その他の基礎天端は基礎パッキン施工とする。
- 設備配管の屋内への取り入れは基礎立上り部のスリーブによる。

決定図