


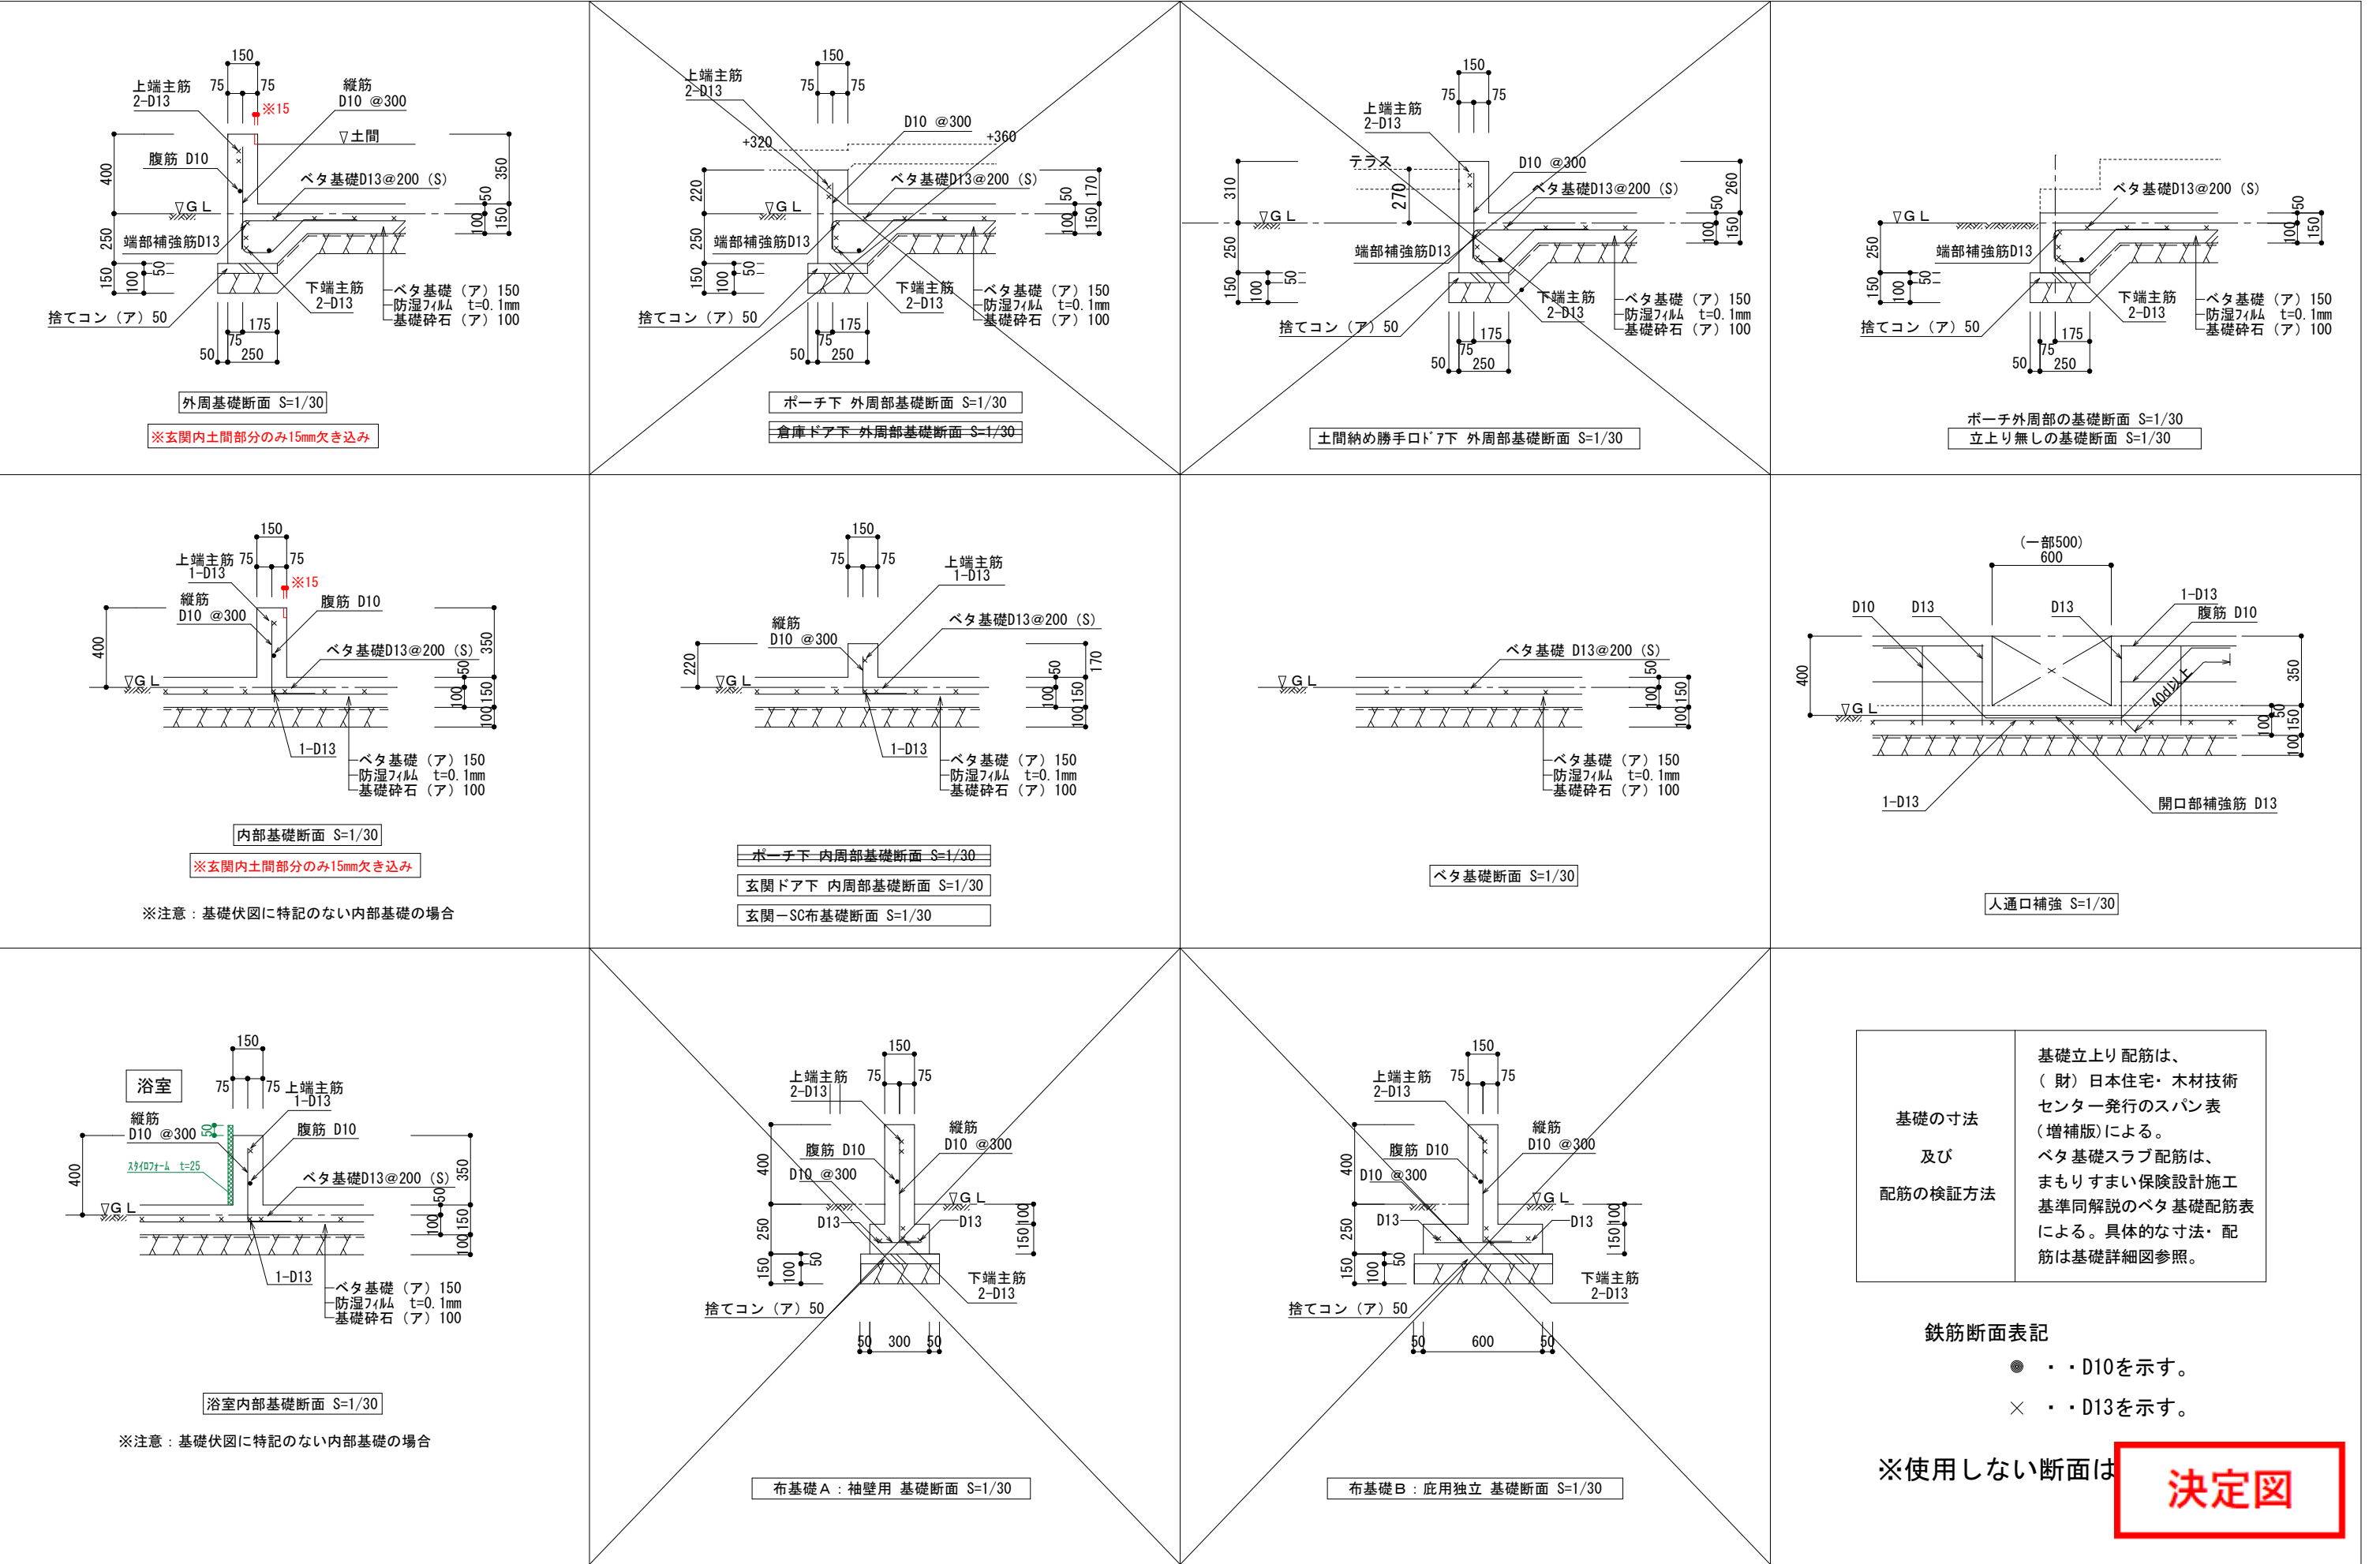

訂 正	浜 岡 一 級 総 合 設 計 事 務 所			株式会社 LIFEFUND InDesign office		一級建築士事務所		年 月 日	件 名			設計	I C	工務	図 番
	一級建築士事務所 静岡県知事登録第 (10)2441 号			事務所登録 (2)第7595号		一級建築士登録 第179770号		2025. 4. 9	尾高麻琴様 恵様 邸新築工事						
	一級建築士 大臣登録第 365879 号 西原利昌			〒432-8023 静岡県浜松市中央区鴨江3丁目70番23号		鈴木 達男		縮 尺	図 名						
								1/30	基礎断面リスト			倉田		青島	B-2



株式会社 LIFEFUND InDesign office 一級建築士事務所
事務所登録 (2) 第7595号 一級建築士登録 第179770号 鈴木 達男
〒432-8023 静岡県浜松市中央区鴨江3丁目70番23号