


※ 37セトクロス 指示書

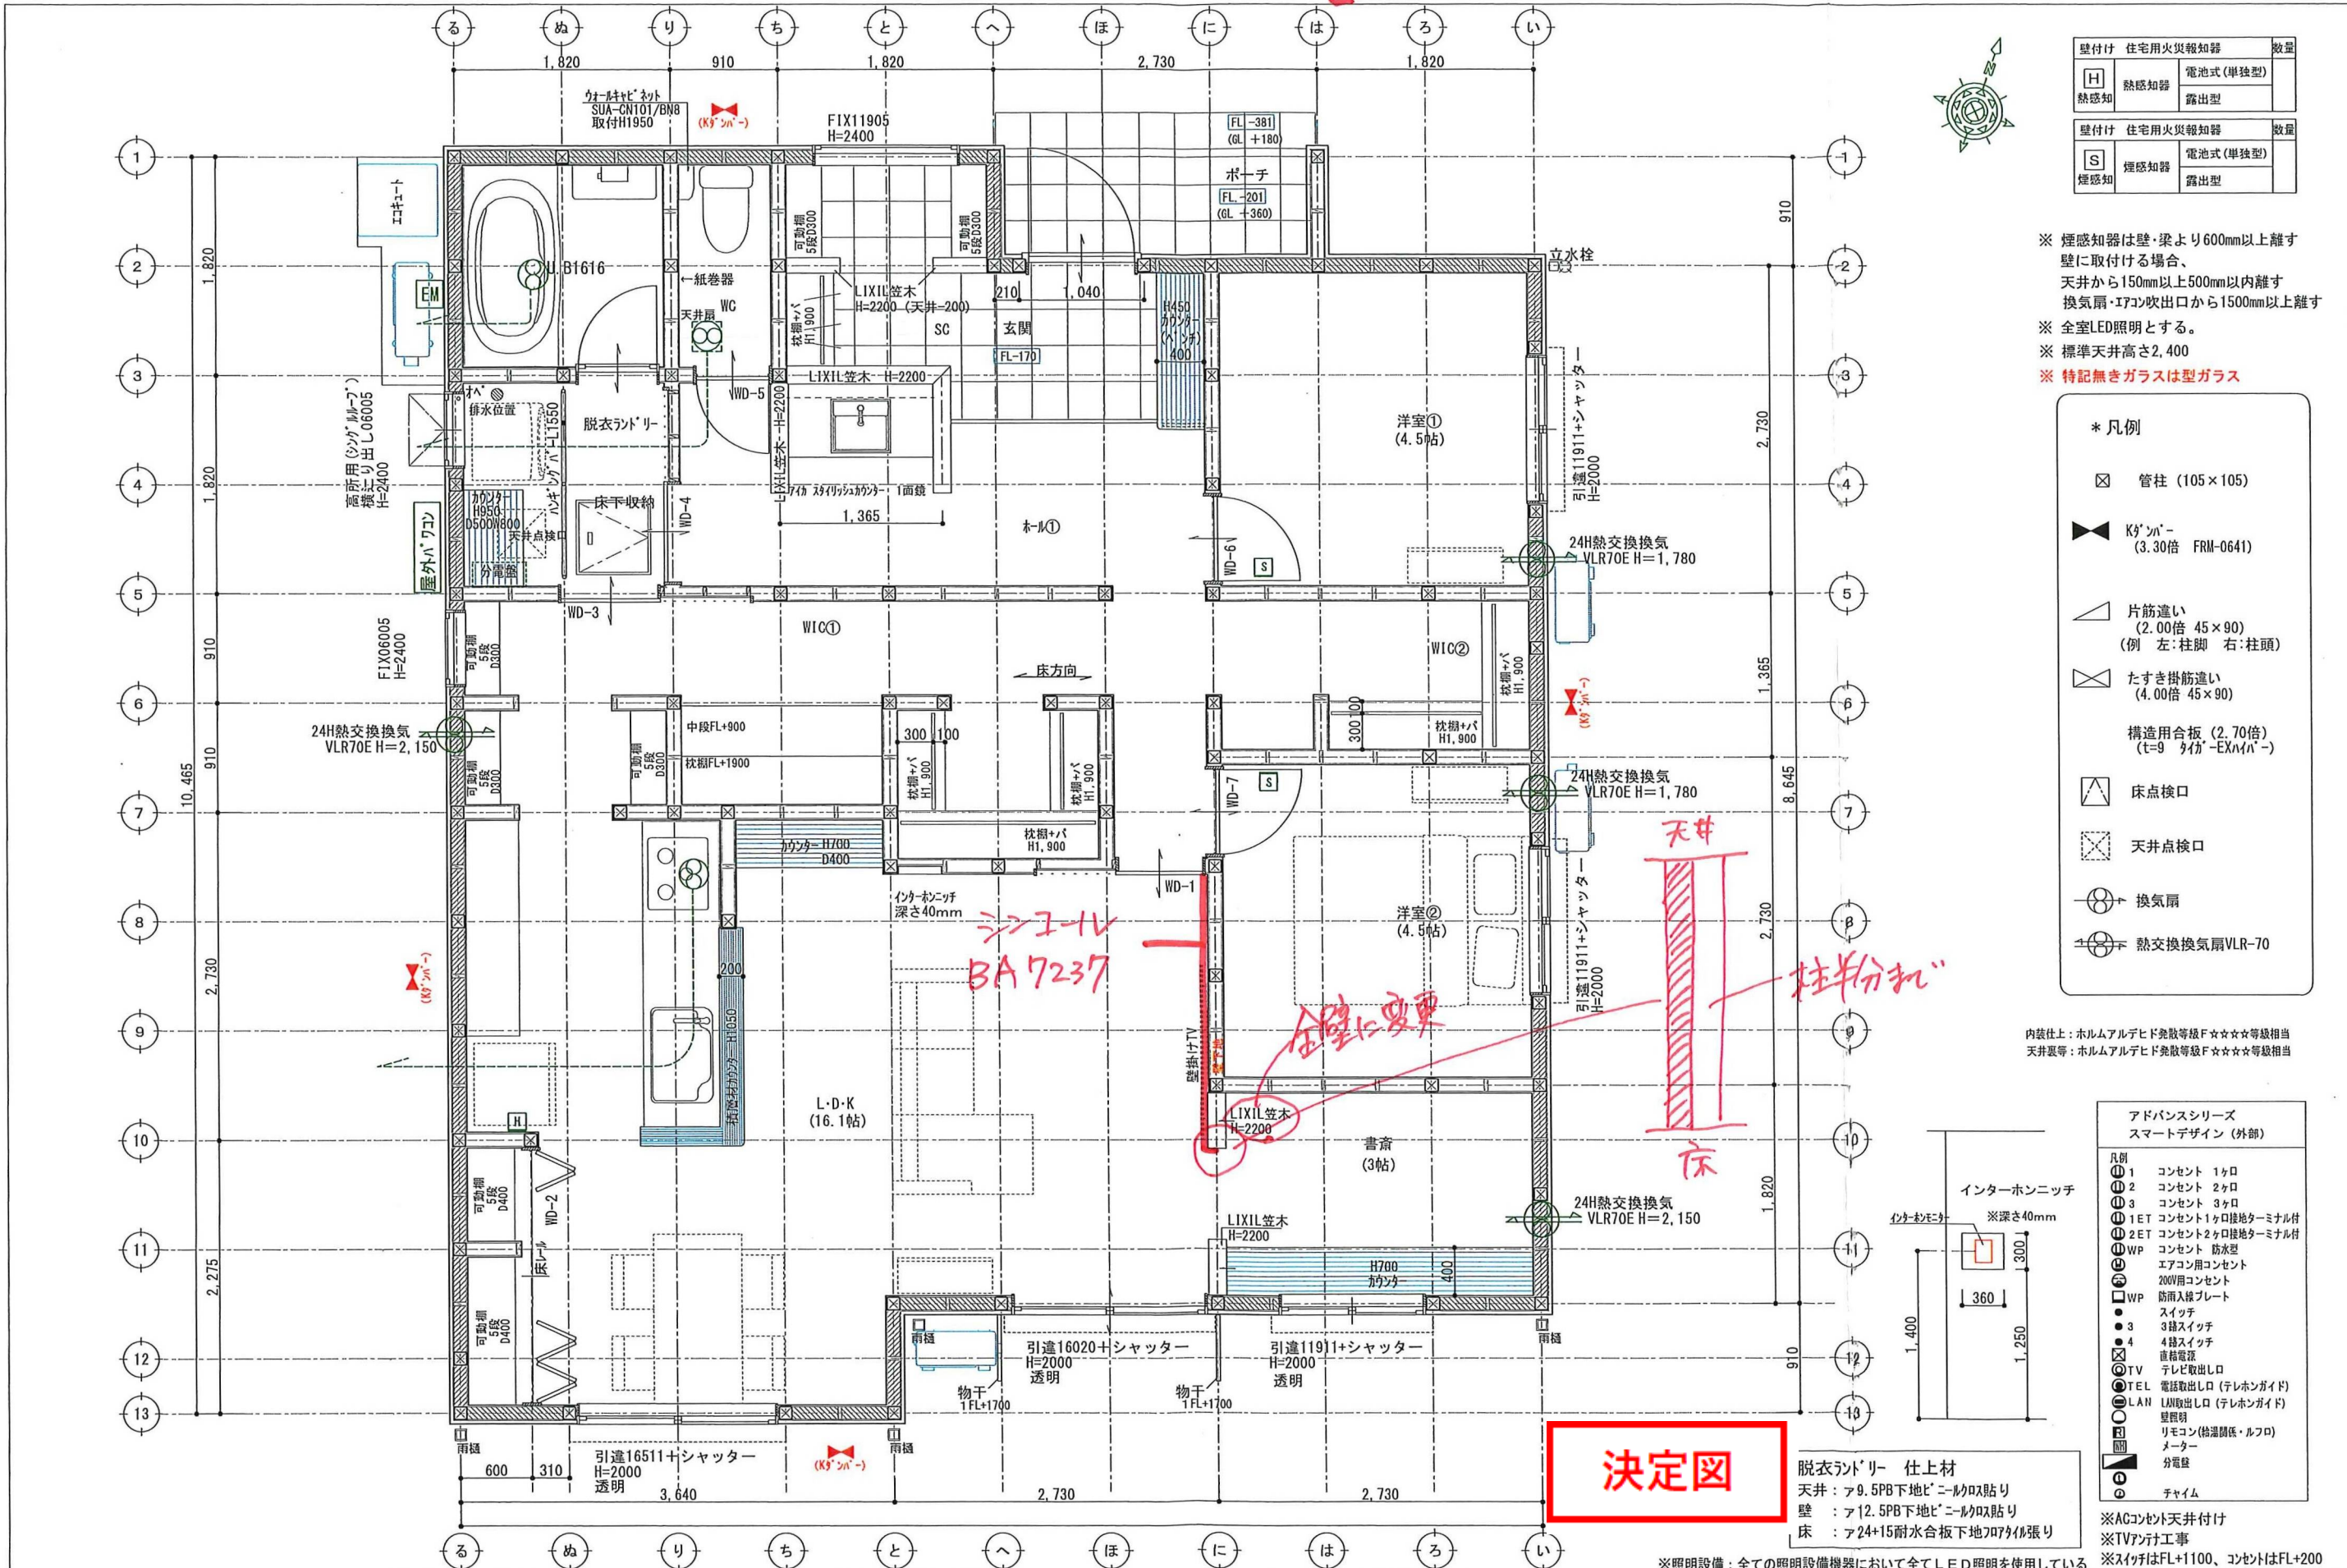

壁付け 住宅用火災報知器			数量
[H] 熱感知	熱感知器	電池式(単独型)	
		露出型	
壁付け 住宅用火災報知器			数量
[S] 煙感知	煙感知器	電池式(単独型)	
		露出型	


※ 煙感知器は壁・梁より600mm以上離す
壁に取付ける場合、
天井から150mm以上500mm以内離す
換気扇・エアコン吹出口から1500mm以上離す
※ 全室LED照明とする。
※ 標準天井高さ2,400
※ 特記無きガラスは型ガラス

* 凡例

- ☒ 管柱 (105×105)
- ☒ K'ンバー (3.30倍 FRM-0641)
- △ 片筋違い (2.00倍 45×90) (例 左:柱脚 右:柱頭)
- ☒ たすき掛筋違い (4.00倍 45×90)
- 構造用合板 (2.70倍) (t=9 タイプ-EXN/A-)
- △ 床点検口
- ☒ 天井点検口
- ☒ 換気扇
- ☒ 熱交換換気扇VLR-70

内装仕上: ホルムアルデヒド発散等級F☆☆☆☆等級相当
天井裏等: ホルムアルデヒド発散等級F☆☆☆☆等級相当

アドバンスシリーズ スマートデザイン (外部)		
凡例	①	コンセント 1ヶ口
	②	コンセント 2ヶ口
	③	コンセント 3ヶ口
	①1ET	コンセント1ヶ口接地ターミナル付
	①2ET	コンセント2ヶ口接地ターミナル付
	WP	コンセント 防水型
	EA	エアコンコンセント
	200V	200V用コンセント
	WP	防雨入線プレート
	●	スイッチ
	●3	3路スイッチ
	●4	4路スイッチ
	☒	直結電源
	☒TV	テレビ取出口
	☒TEL	電話取出口 (テレホンガイド)
	☒LAN	LAN取出口 (テレホンガイド)
	☒	壁照明
	☒	リモコン (給湯関係・ルフロ)
	☒	メーター
	☒	分電盤
	☒	チャイム

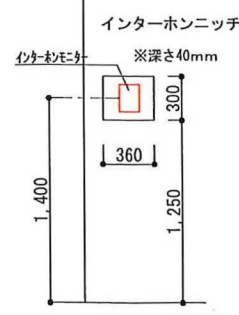

脱衣ランドリー 仕上材
天井: ア9.5PB下地ビニル吹張り
壁: ア12.5PB下地ビニル吹張り
床: ア24+15耐水合板下地70アタリ張り

※照明設備: 全ての照明設備機器において全てLED照明を使用している