
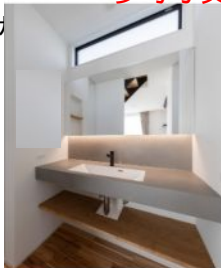


■ 仕 様				■ HEAT20 G1	
断熱工事		■ 床:カネライトフォーム t65 ■ 土間床等の外周:スタイロフォームAT t25 ■ 壁:アクアフォームLITE吹付 t85 ■ 天井:アクファフォームLITE吹付 t170			
床下換気		■ 基礎パッキン JOTO (玄関・UB周り:気密基礎パッキン)			
防虫防蟻		■ 土壌処理・木部 ガントナーMC			
■ 外 部 仕 上 表				■ 22条地域	
部位		仕上・仕様・メーカー		色番・品番	
屋根		■ ガルバリウム鋼板(t0.35)UK立平 ニスクカラーPro GH 軒先通気金物 日本住環境株式会社【REV-15】		GHK01 Sブラック	
パラペット笠木		■ なし			
破風・鼻隠		■ なし			
雨樋	(軒樋)	■ Panasonic サーフেসケアFS-I型		オークグレー	
	(縦樋)	■ Panasonic S30角樋		オークグレー	
軒天	屋根軒	■			
	ポーチ軒	■ ニチハ軒天5 木目調 910×1820×5		ライト	
	バルコニー軒	■			
オーバーハング水切り		■ ガルバリウム鋼板 ※外壁合わせ JOTO:HF-A3550			
外壁 ※下地面材:タイガーEXハイパー 防火認定 PC030BE-4028	通気金物(15mm)	■メイン	Kmewエクセレージ・シマンフラット	ソイルダークグレー EW7304	
		■アクセントA	なし		
		■アクセントB	なし		
玄関ポーチ		■ 床 玄関タイルに同じ		-	
基礎		■ 立上り巾木: モルタル刷毛引き		-	
基礎水切り金物		■ JOTO鋼板製 防鼠材付き水切り JOTO:WMF-N35		ブラック	
バルコニー	床・内壁	■ なし		-	
	笠木	■ なし			
外部建具		■ LIXIL EW(アルゴンガス高遮熱仕様LowE複層ガラス クリーン) ・SD、TSは、メーカー設定によるが、オペレーターハンドル優先とする ・オペレーター付サッシの場合は固定網戸とする ・グレモンハンドル式サッシの場合は可動網戸とする		外観 ブラック 内観 シャドーオークforDesign ※樹脂パッキン・網戸付	
シャッター		■ 窓シャッターは手動			
軒天通気金物				ブラック	
玄関扉		■ LIXIL ジエスタ2 K2仕様 LIXILファミロック タグキー×3 (電池式)		ドア型: M17 型 ドア色: ラステックオーク ハンドル: S型ハンドル 色 ブラック	
外部物干し金物		■ 川口技研RK型-550 外壁付		ブラック	
換気フード		■ 局所換気扇(トイレ 浴室 キッチンフード) 防火ダンパー無		外気フード: シルバー	
		■ ダクトレス熱交換換気システム (日本スティーベル株式会社) VLR-70E 防火ダンパー無		外気フード: S シルバー 室内パネル ホワイト	

■ 構 造 概 要				
基礎	■ RCベタ基礎コンクリート			
通し柱・管柱	■ 構造用集成材 105×105		間柱	■ 集成材
土台	■ 桧 105×105	大引き ■ 桧 90*90	筋交い	■ 構造用製材 火打梁 ■ 鋼製火打(当社基準により米松あり)
桁・梁	■ 構造用製材及び集成材		制震装置	■ Kダンパー (株)アイ・エム・エー
■ 設 備 装 着 品				
住宅設備	部位	メーカー	商品名 ※ 詳細は見積り、プレゼン参照	見積りNo. (日付)
	キッチン	LIXIL	■ ES I型 扉グレージュスタック 天板ソルティホワイト キッチンパネル:フレッシュホワイト 見積り番号 : M25026434852-002 標準食洗器 標準IH、壁付レンジフードASR(シルバー) スリム取手ブラック キレイシンク (日付) 2025/2/4	
	バックカウンタ ※オプション	LIXIL	■ ES L1800(W900スライドストッカー+マルチスペース) 見積り番号 : M25026434852-002 (日付) 2025/2/4	
	浴室	LIXIL	■ AX1616 PGハウス標準仕様 見積り番号 : M25026434852-002 アクセント壁:シルバーグレー 浴槽:ストリートライン ホワイト 床:ホワイト マグネットシェフ:不要 開き戸 (日付) 2025/2/4	
	トイレ	LIXIL	■ ベーシアシャワートイレ 白 ● タオル掛け: タンク手洗 無し ● 紙巻き器: CF-AA22H /WA 見積り番号 : M25026434852-002 ■ トイレ コーナーウォールキャビネット SUA-CN101 ホワイト (日付) 2025/2/4	
	洗面台	造作	■ 洗面 アイカスタイルッシュカウンター ミラー:一面鏡(下部照明) ボウル:ボウル5 水栓:K4750NV-MDP/アイカ カウンター・立上り部分:TJ-10239K 棚:ゴム集成材(オスモリアMAT) タオル掛けは支給品取付  参考写真 	
給排水設備	給湯器	■ エコキュート370L Panasonic NSシリーズ スタンダードモデル 追い焚きフルオート※在庫限り		
	排水	■ 下水		
	外水栓	■ 1 カ所 (平面図参照)	■ 外部立栓柱: PVC製 水栓柱12型【前澤化成工業】	
	外部ガーデンパン	■ 無し		
	その他	■ 洗濯機用単水栓: 緊急止水弁付 ■ 洗濯機用排水:トラップ金物(標準) ■ 排水さや管(長期優良住宅仕様)		
ガス配管設備		■ なし (配置図・平面図参照)	■ガス使用器具 すべての熱源	専用架台
電気設備	インターホン	■ パナソニック VL-SZ30KL		
	TVアンテナ	■ UHF + BS・110度CS/CSアンテナ [2K・4K・8K対応] ■ホワイト		
	エアコン	■ 設置場所:		
	ソーラー	■ あり(Qセルズ) 12 枚 5.28 KW	Re.RISE-G3 440 (1722×1134×30)	
	※標準搭載	■ 屋外パワコン		
その他				


決定図

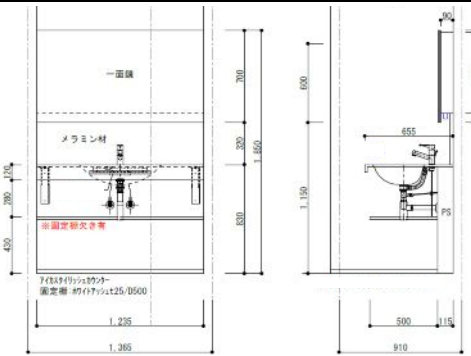

浜 岡 一 級 総 合 設 計 事 務 所		 PG HOUSE	株式会社 LIFEFUND InDesign office 一級建築士事務所		年 月 日	2025.04.09	件名	尾高麻琴様 恵様 邸新築工事		設計	IC	工務	図 番
一級建築士事務所 静岡県知事登録第 (10)2441 号			事務所登録 (2)第7595号 一級建築士登録 第179770号 鈴木 達男		縮尺		図面	仕上表 1		倉田		青島	1-1
一級建築士 大臣登録第 365879 号 西原利昌			〒432-8023 静岡県浜松市中央区鴨江3丁目70番23号										




訂 正	浜 岡 一 級 総 合 設 計 事 務 所 一級建築士事務所 静岡県知事登録第 (10)2441 号 一級建築士 大臣登録第 365879 号 西原利昌	LIFEFUND PG HOUSE 株式会社 LIFEFUND InDesign office 一級建築士事務所 事務所登録 (2)第7595号 一級建築士登録 179770号 鈴木 達男 〒432-8023 静岡県浜松市中央区鴨江3丁目70番23号	年 月 日 2025. 4. 9	件 名 尾高麻琴様 恵様 邸新築工事		設計	IC	工事	図 番
			縮 尺 1/100	図 名 配置図		倉田	青島	2-1	

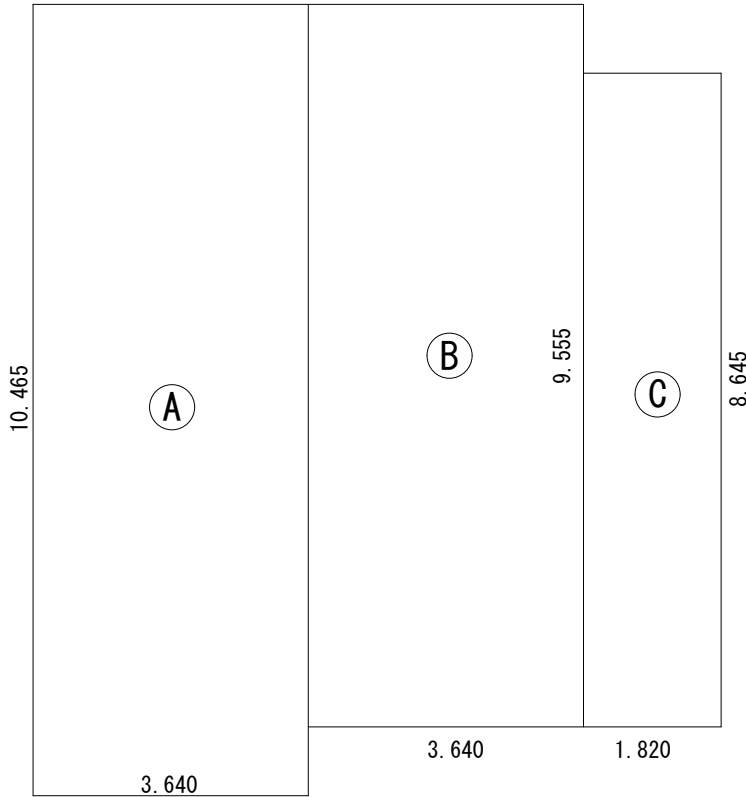

建築面積求積図 S=1/100

建築面積求積表

番号	計算式 (m)	面積 (㎡)
Ⓐ	3.640 × 10.465	38.0926
Ⓑ	3.640 × 9.555	34.7802
Ⓒ	1.820 × 8.645	15.7339
合計 ≡		88.6067 86.60 (26.8坪)

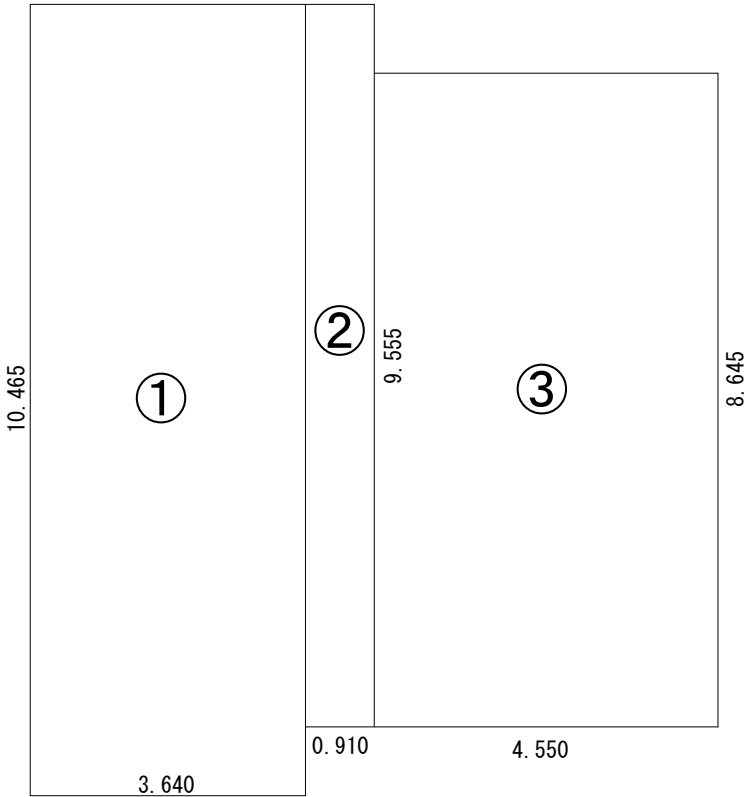



1階床面積図 S=1/100

1階床面積求積表

番号	計算式 (m)	面積 (㎡)
①	3.640 × 10.465	38.0926
②	0.910 × 9.555	8.69505
③	4.550 × 8.645	39.33475
合計 ≡		86.1224 86.12 (26.0坪)

決定図

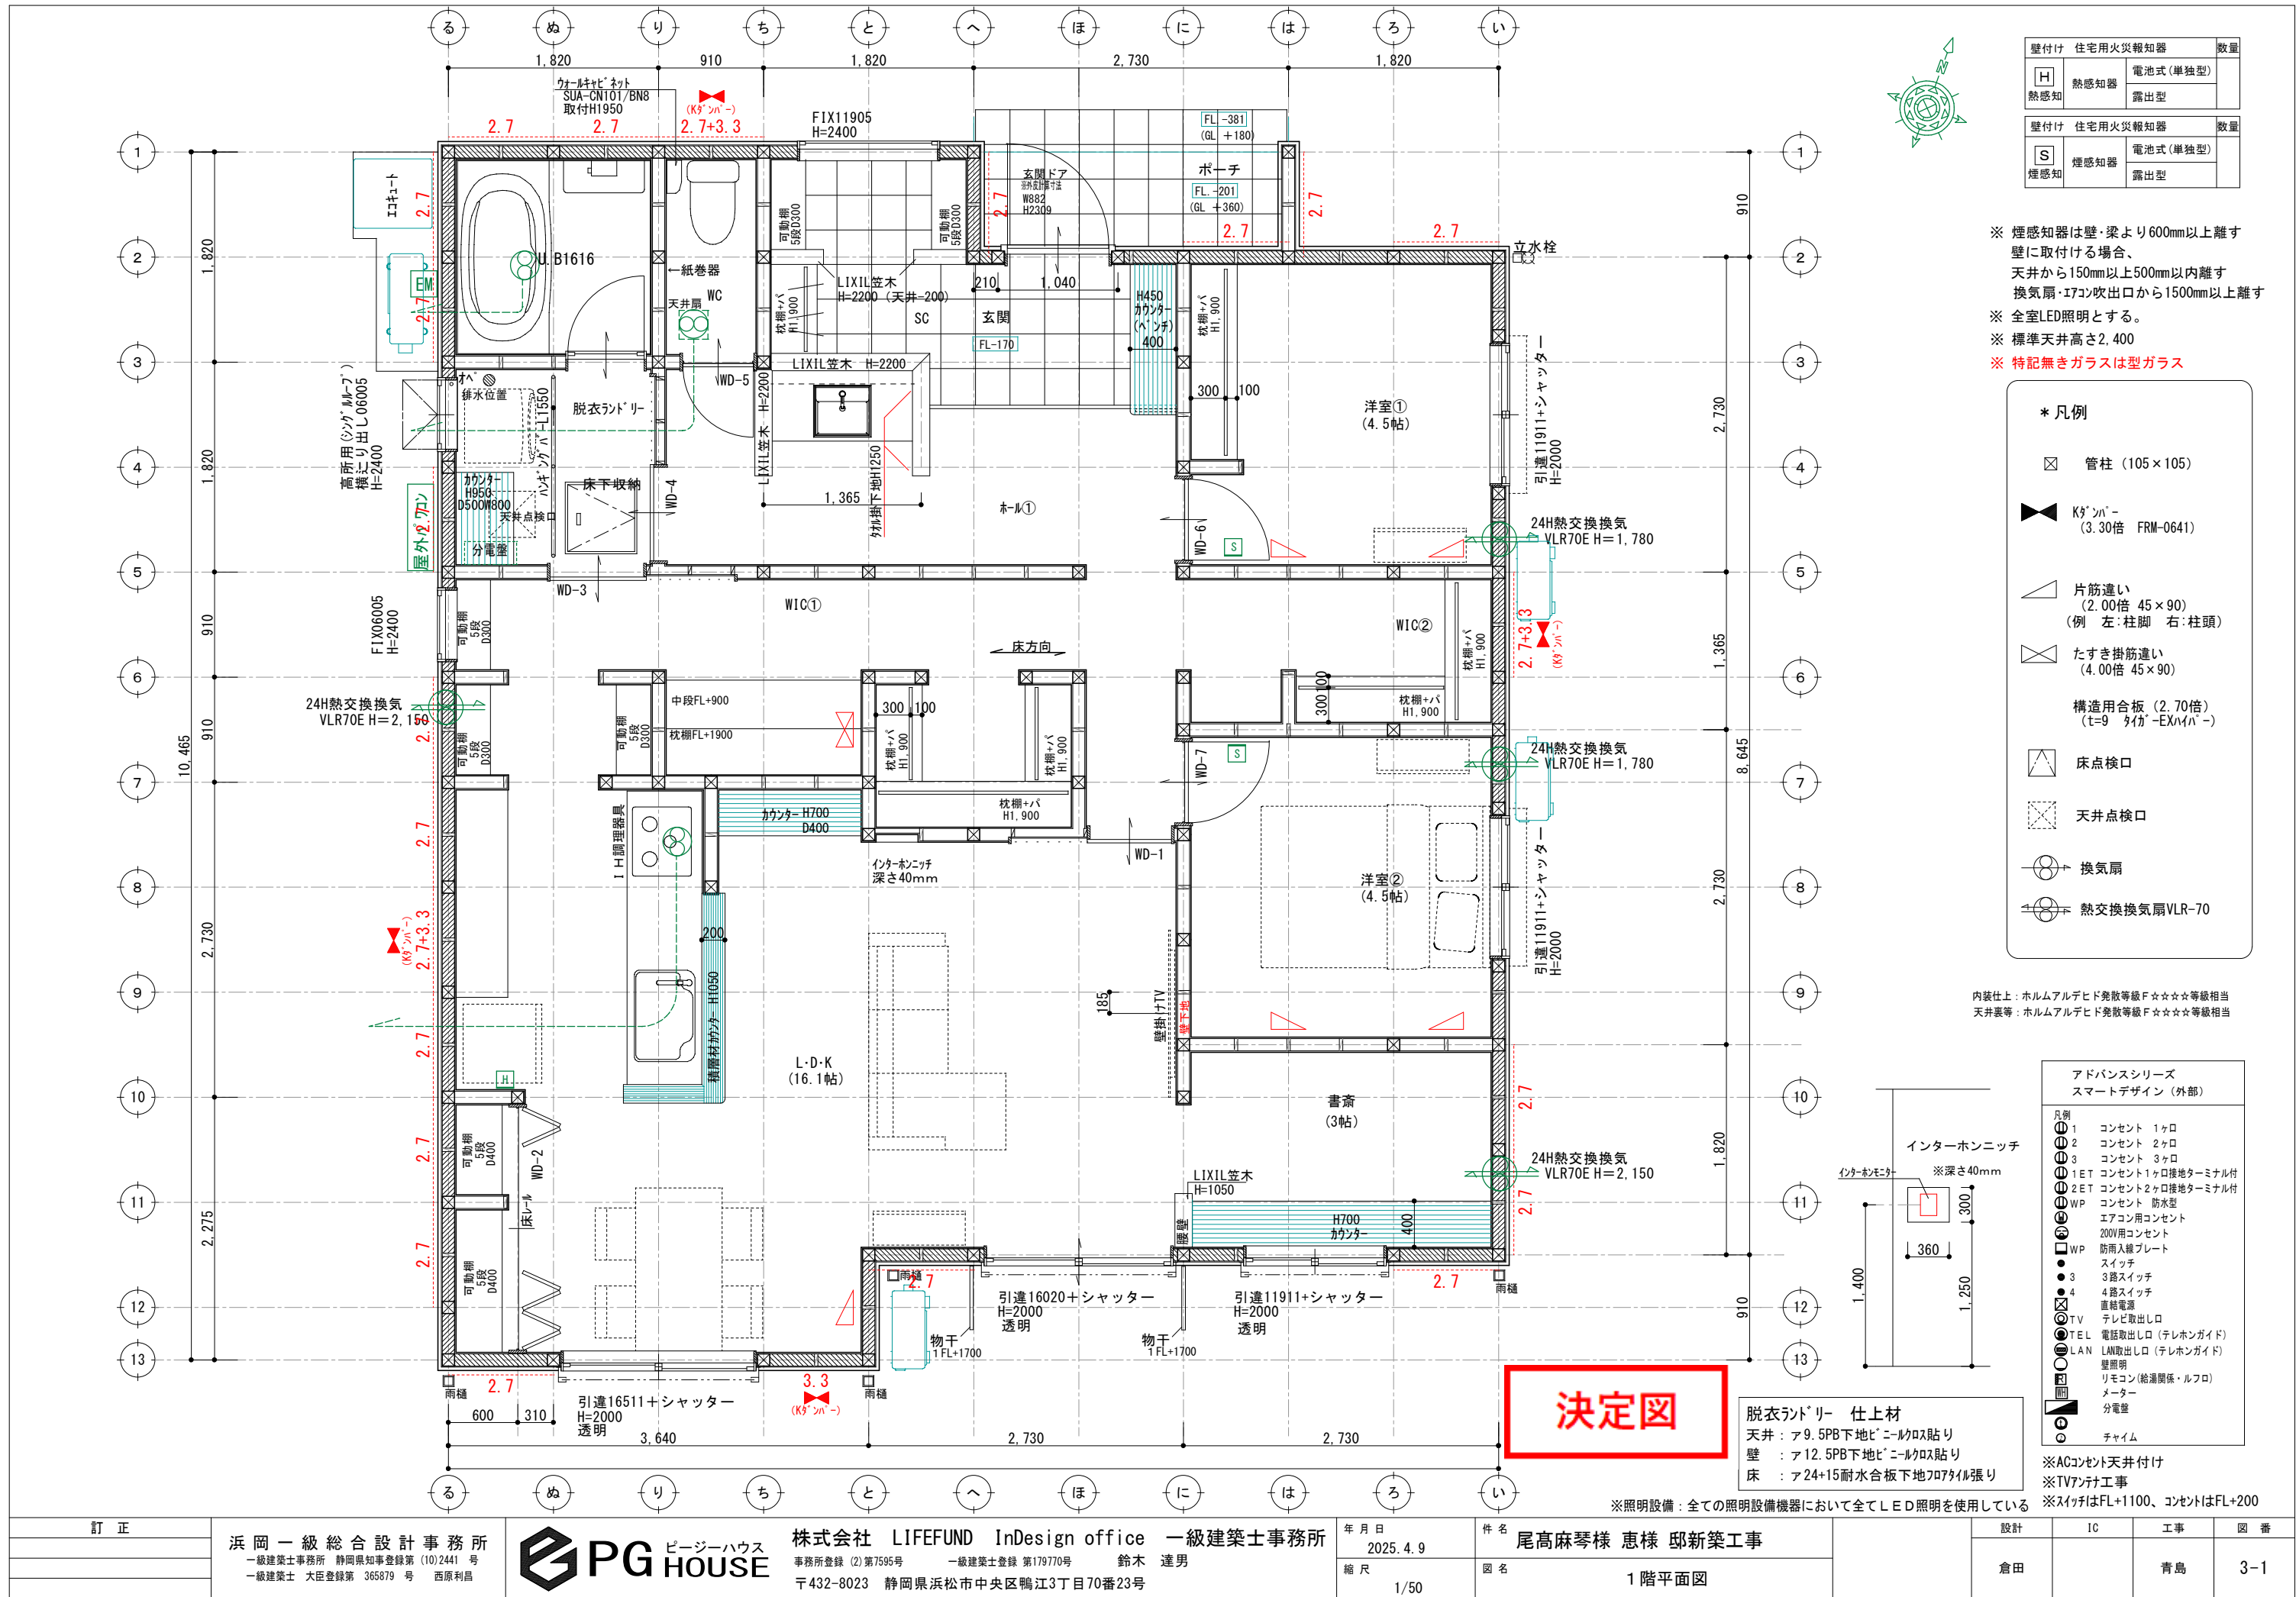


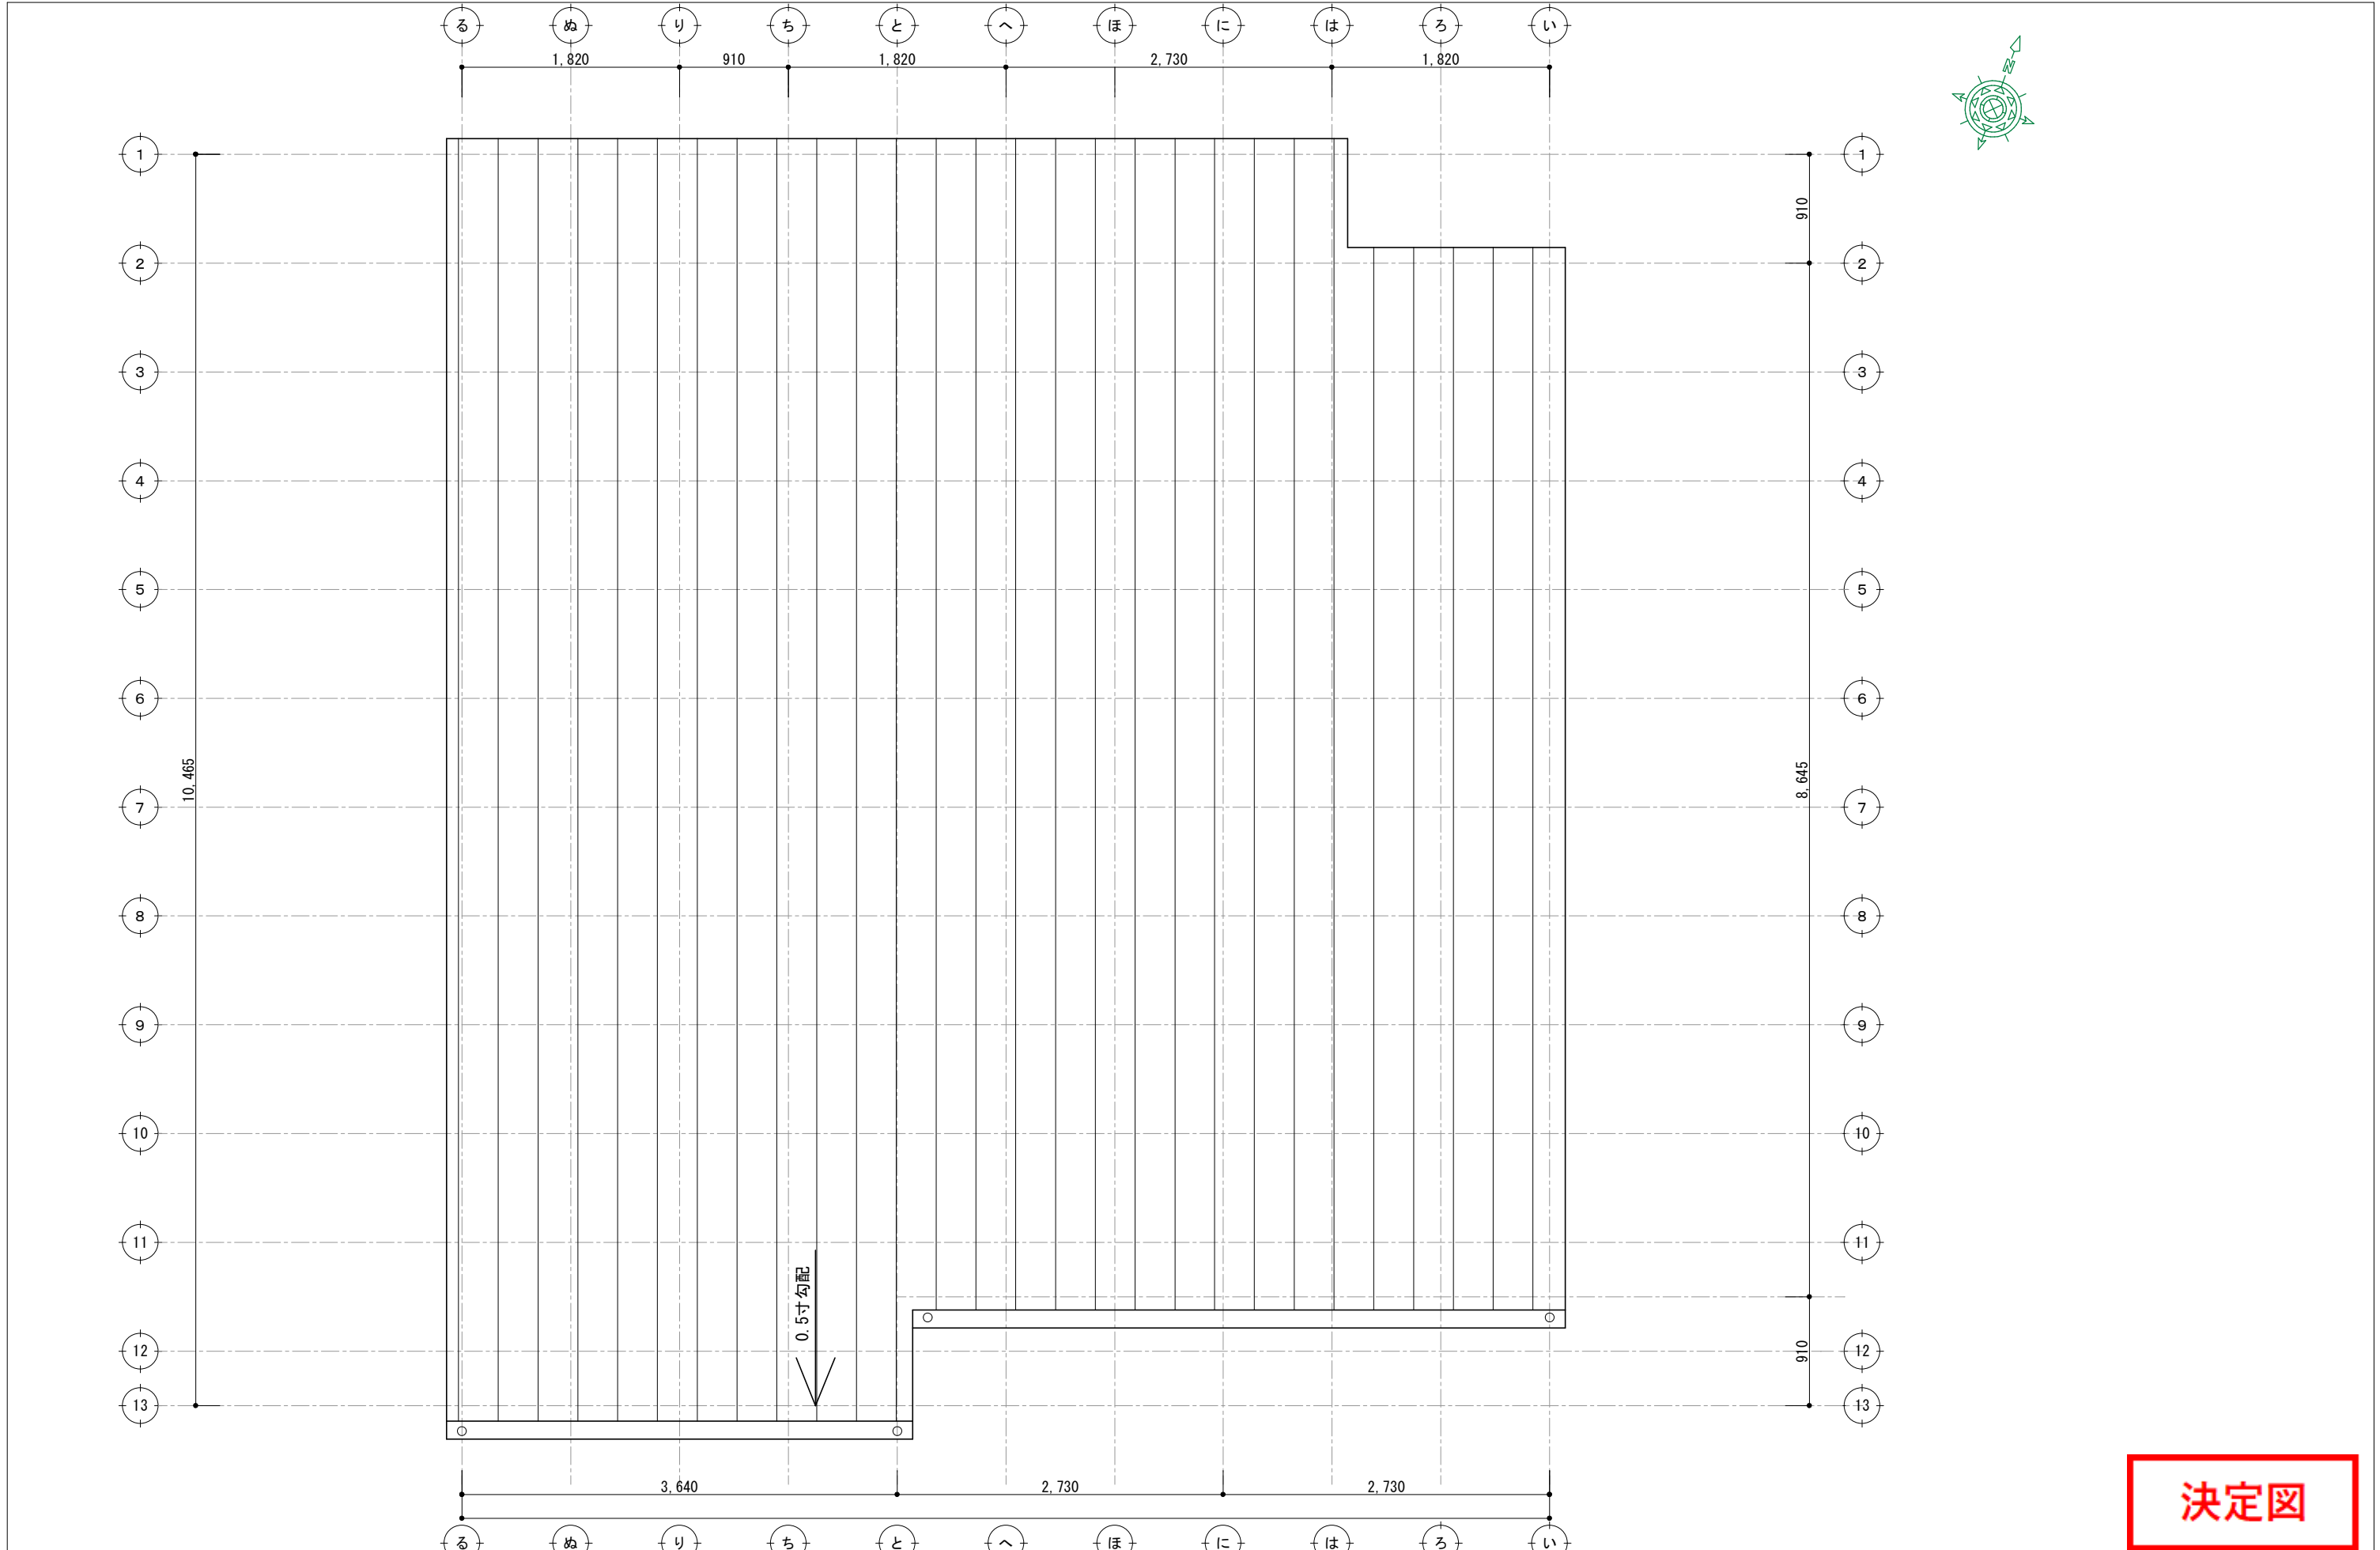

決定図


訂正	浜岡一級総合設計事務所 一級建築士事務所 静岡県知事登録第 (10)2441 号 一級建築士 大臣登録第 365879 号 西原利昌	 ピージーハウス	株式会社 LIFEFUND InDesign office 一級建築士事務所 事務所登録 (2) 第7595号 一級建築士登録 第179770号 鈴木 達男 〒432-8023 静岡県浜松市中央区鴨江3丁目70番23号	年月日 2025. 4. 9 縮尺 1/50	件名 尾高麻琴様 恵様 邸新築工事 図名 屋根伏図		設計	IC	工事	図番
							倉田		青島	3-2

太陽光搭載あり

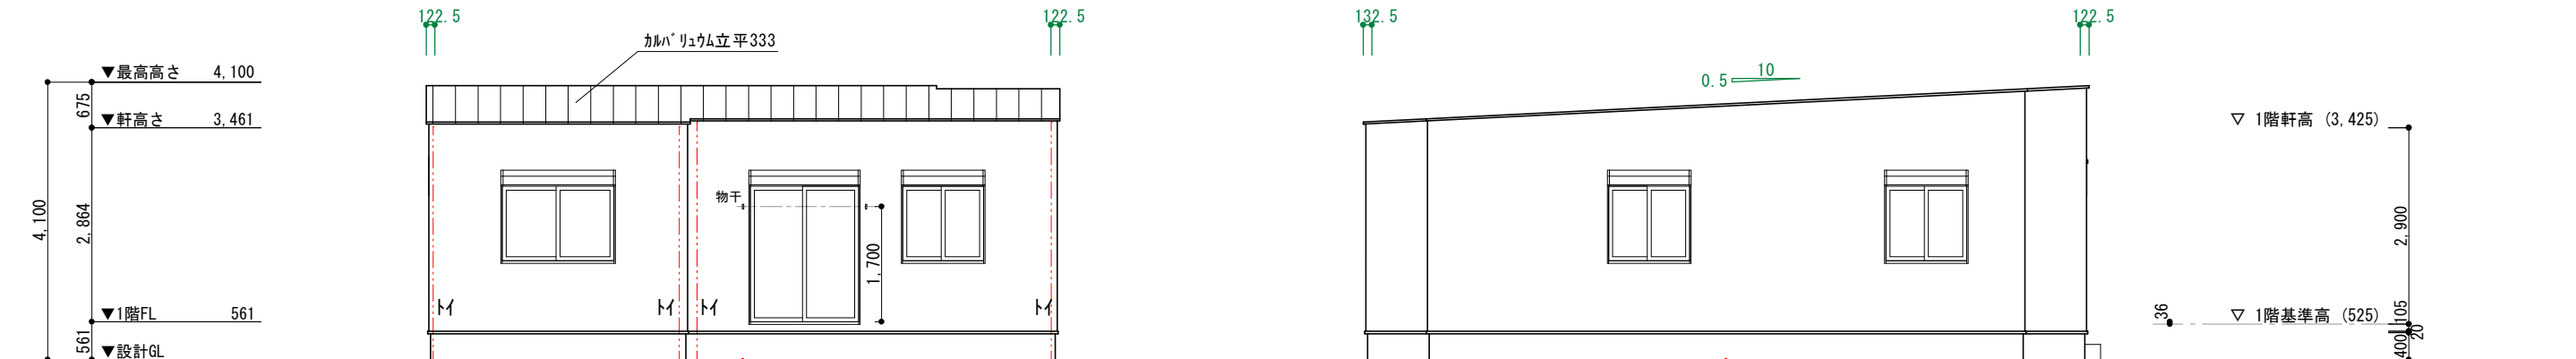

南立面図 S=1/100
南側立面図 S=1/100

東立面図 S=1/100
東側立面図 S=1/100

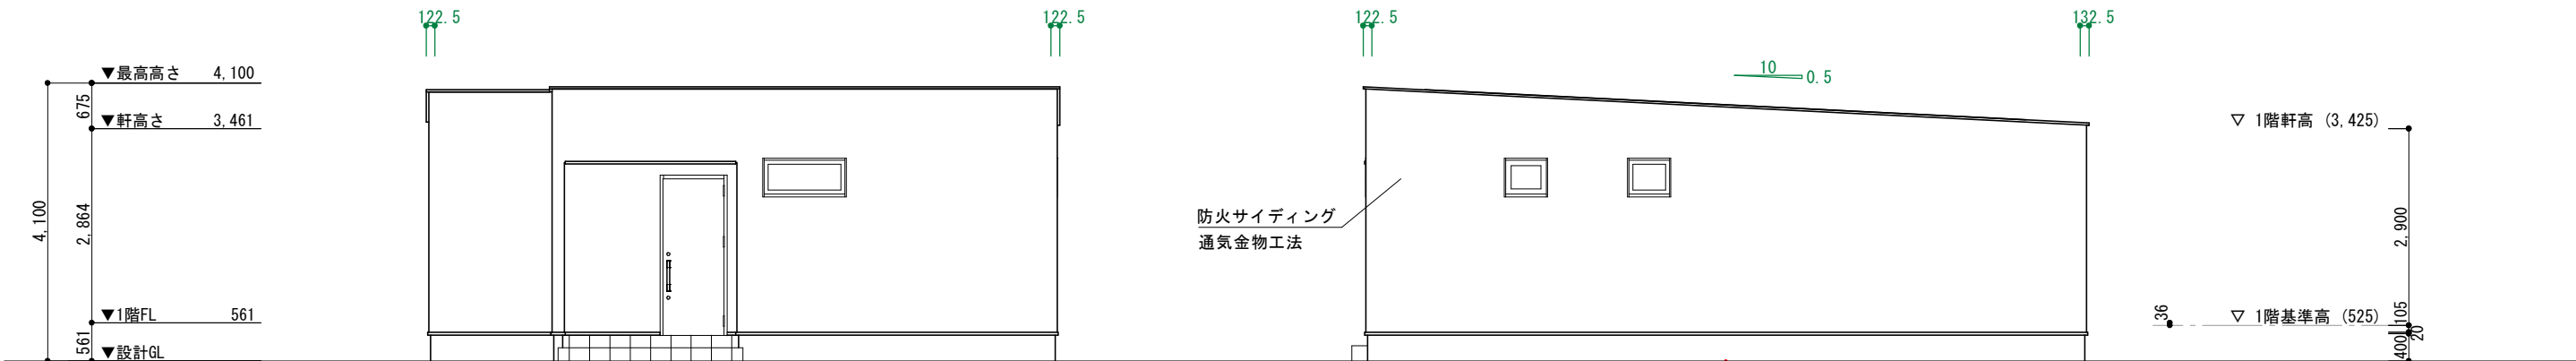


北立面図 S=1/100
北側立面図 S=1/100

西立面図 S=1/100
西側立面図 S=1/100


決定図

訂 正	浜 岡 一 級 総 合 設 計 事 務 所 一級建築士事務所 静岡県知事登録第 (10)2441 号 一級建築士 大臣登録第 365879 号 西原利昌		株式会社 LIFEFUND InDesign office 一級建築士事務所 事務所登録 (2) 第7595号 一級建築士登録 第179770号 鈴木 達男 〒432-8023 静岡県浜松市中央区鴨江3丁目70番23号	年 月 日	件 名		設計	IC	工事	図 番
				2025. 4. 9	尾高麻琴様 恵様 邸新築工事					
				縮 尺	図 名					
				1/100	立面図		倉田		青島	4

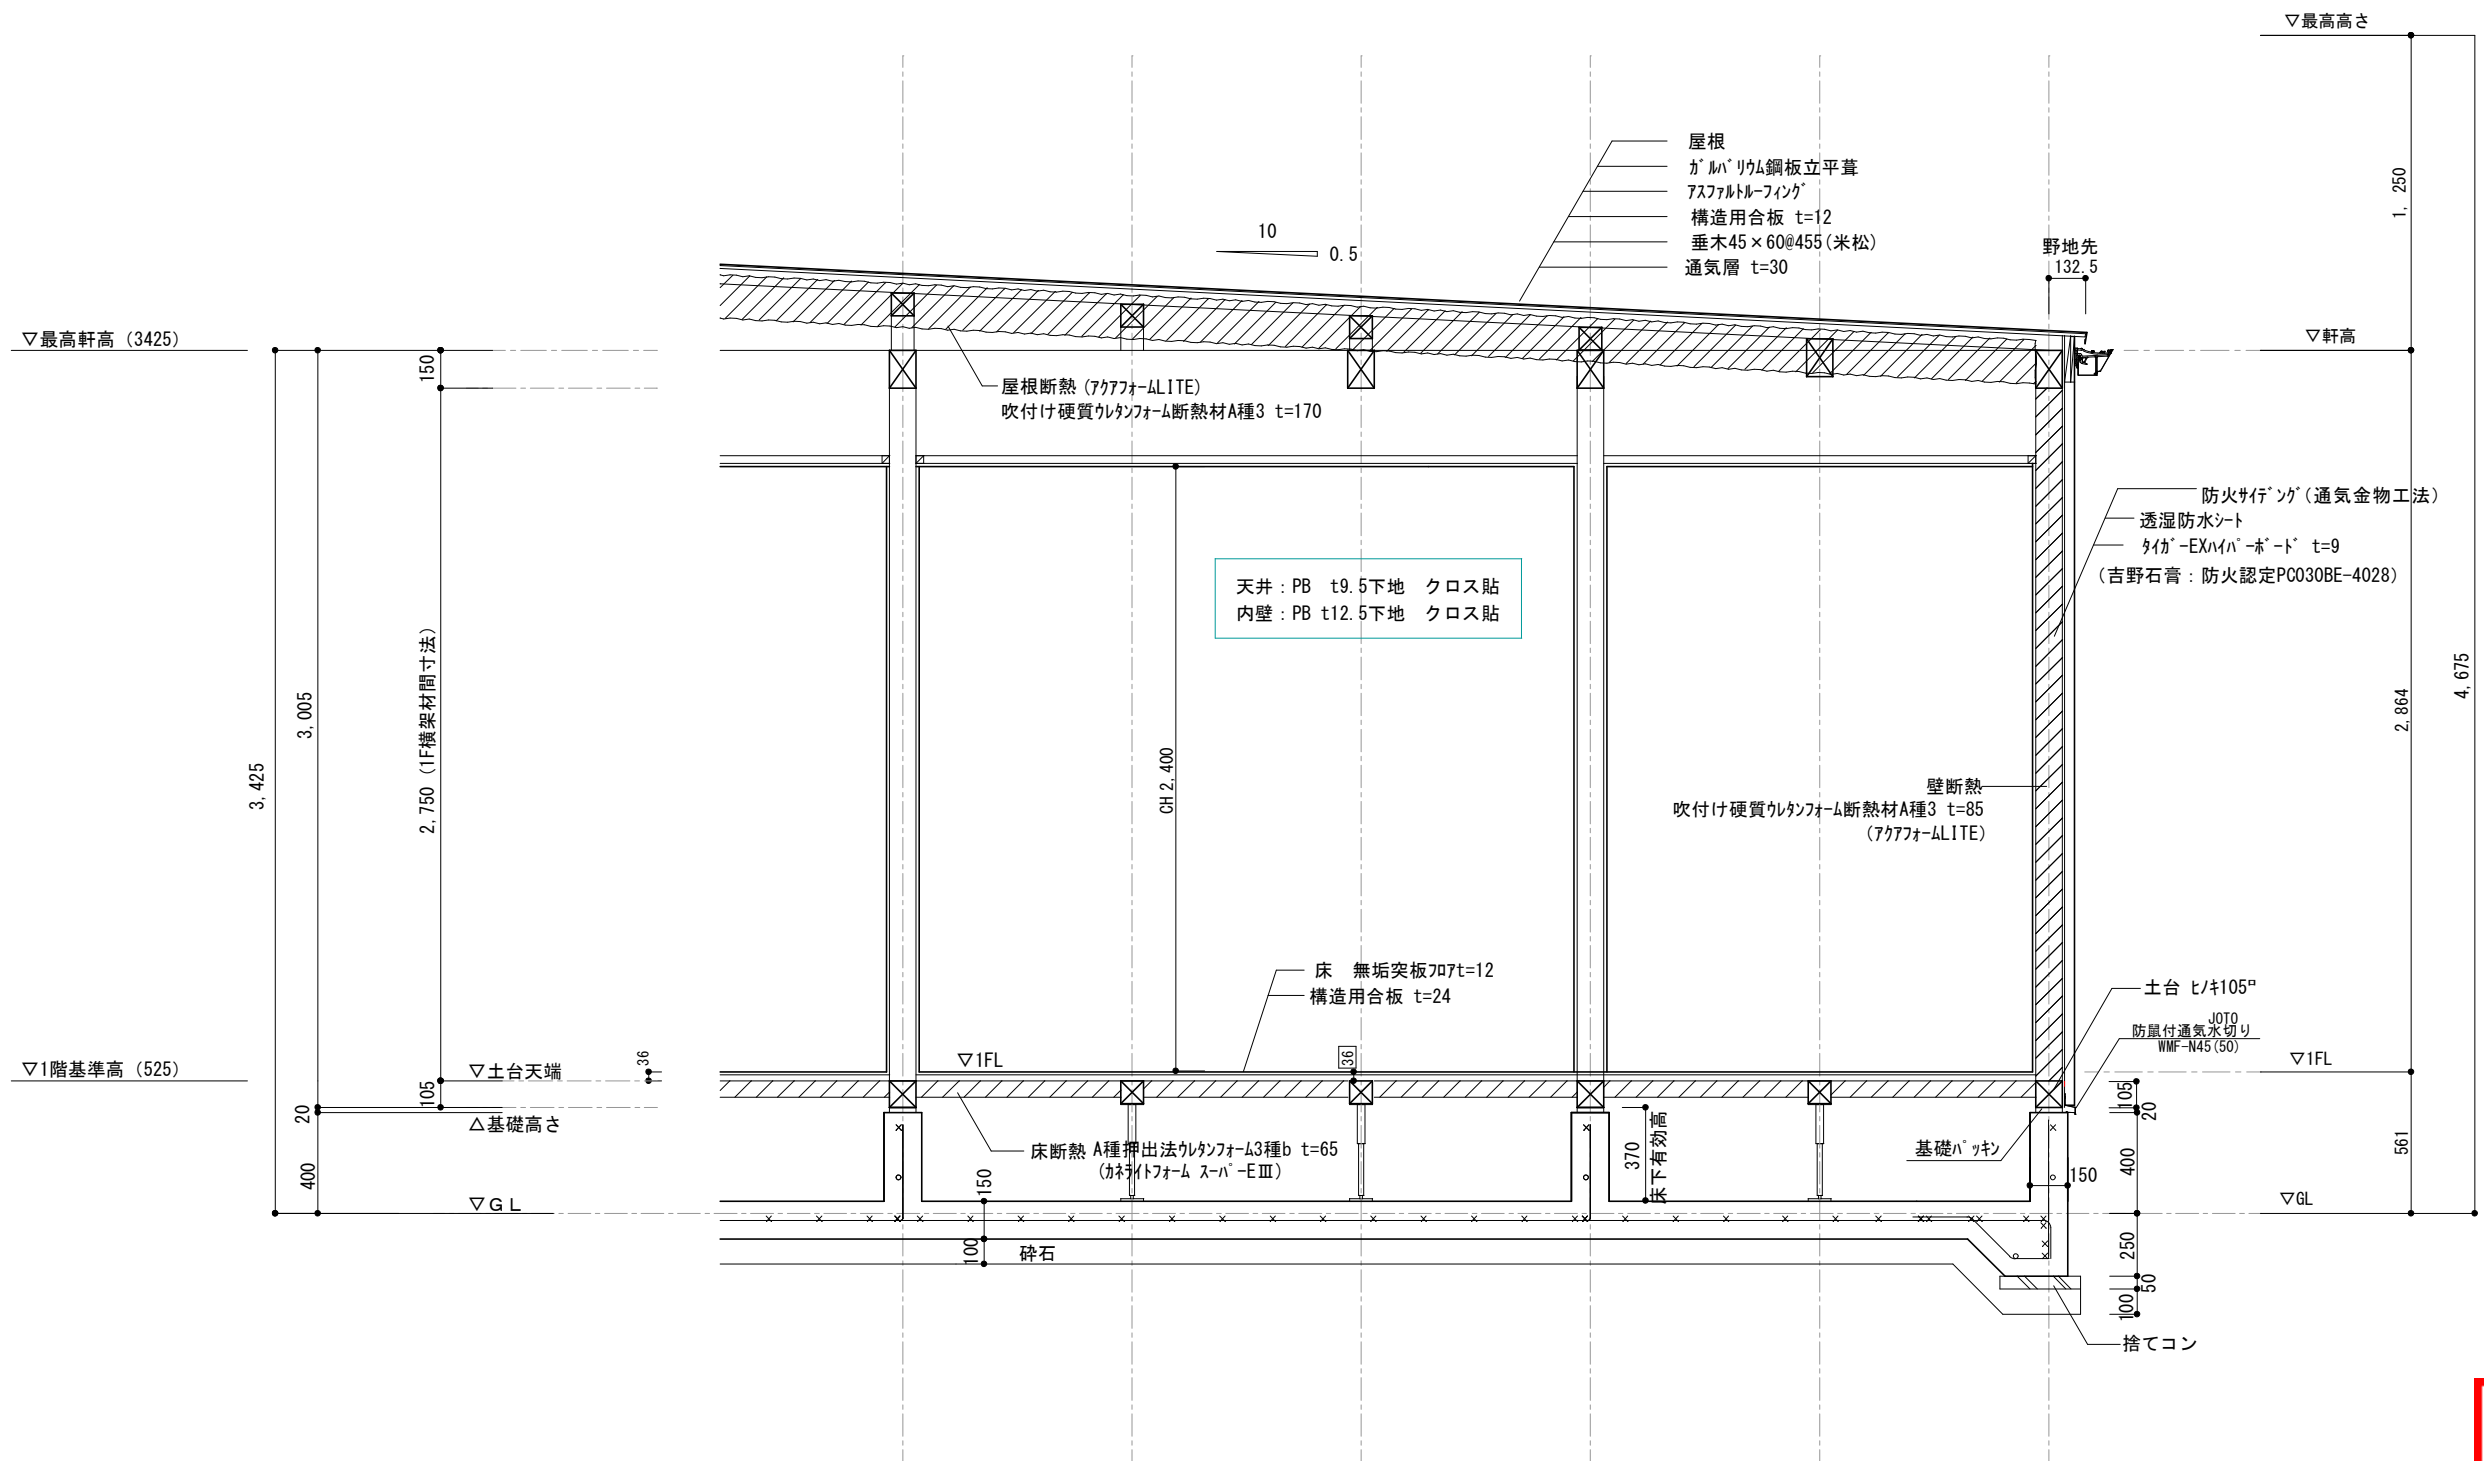


決定図

訂正	浜岡一級総合設計事務所 一級建築士事務所 静岡県知事登録第 (10)2441 号 一級建築士 大臣登録第 365879 号 西原利昌	PG HOUSE ピージーハウス	株式会社 LIFEFUND InDesign office 一級建築士事務所 事務所登録 (2) 第7595号 一級建築士登録 第179770号 鈴木 達男 〒432-8023 静岡県浜松市中央区鴨江3丁目70番23号	年月日 2025. 4. 9 縮尺 1/30	件名 尾高麻琴様 恵様 邸新築工事 図名 矩計図	設計 倉田	IC	工事 青島	図番 5
----	--	---------------------	---	---------------------------------	-----------------------------------	----------	----	----------	---------

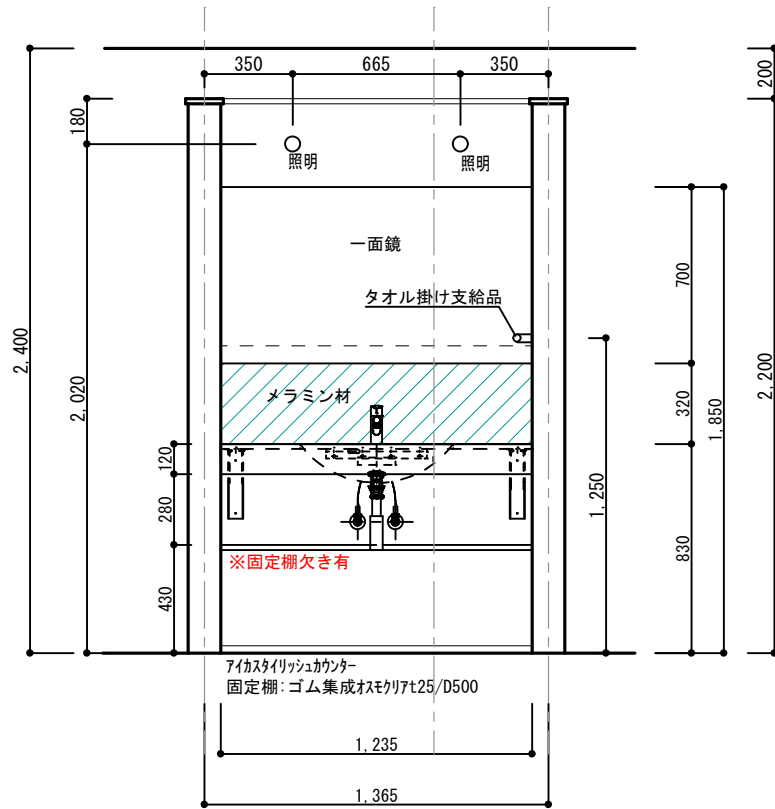


洗面 北

タオル掛け支給品取付

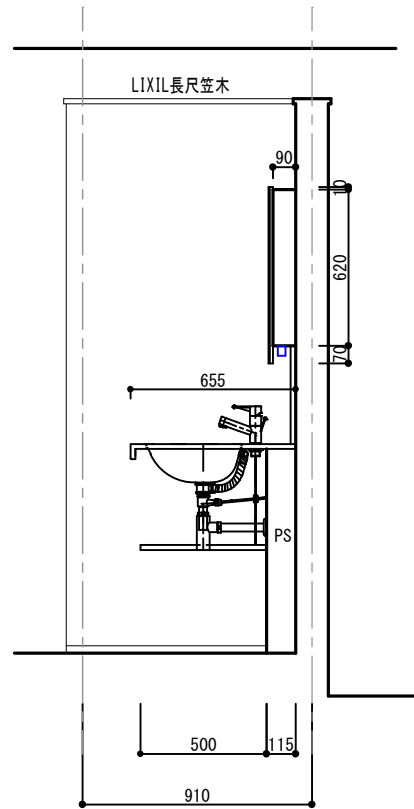

洗面 西


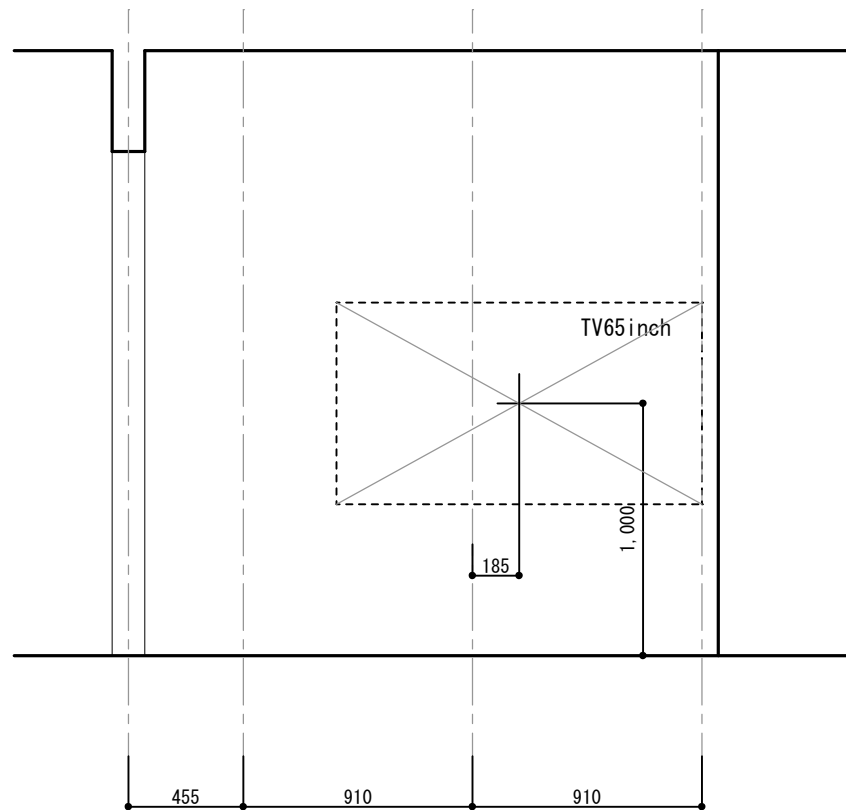


LDK 東


決定図

訂正	浜岡一級総合設計事務所 一級建築士事務所 静岡県知事登録第(10)2441号 一級建築士 大臣登録第 365879号 西原利昌	LIFEFUND PG HOUSE	株式会社 LIFEFUND InDesign office 一級建築士事務所 事務所登録(2)第7595号 一級建築士登録 第179770号 鈴木 達男 〒432-8023 静岡県浜松市中央区鴨江3丁目70番23号	年月日 2025.4.9 縮尺 1/50	件名 尾高 麻琴様 様恵様 邸新築工事 図名 展開図		設計 倉田	IC	工事 青島	図番 6-1
----	---	----------------------	---	-------------------------------	-------------------------------------	--	----------	----	----------	-----------


■洗面 アイカスタイルカウンター
ミラー：一面鏡(照明有)
ボウル：ボウル5
水栓：K4750NV-MDP/アイカ
ンター・立上り部分：TJ-10239K
※タオル掛けは支給品

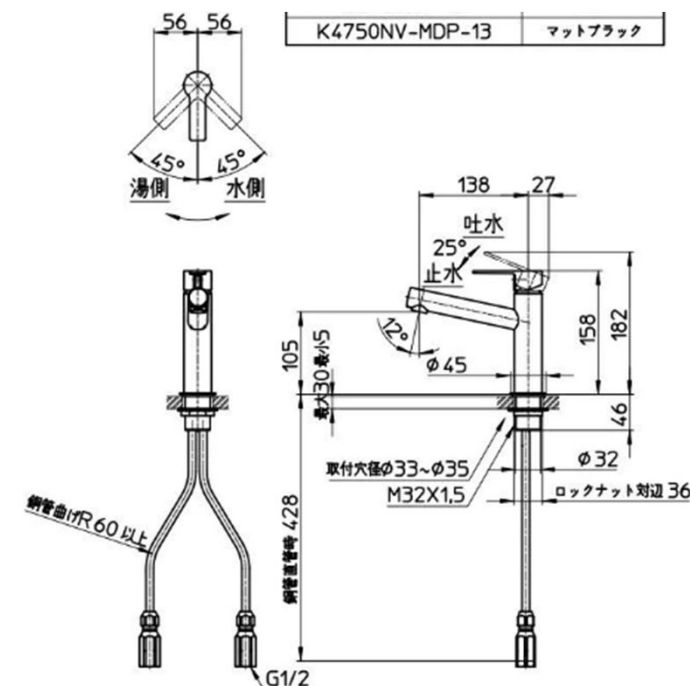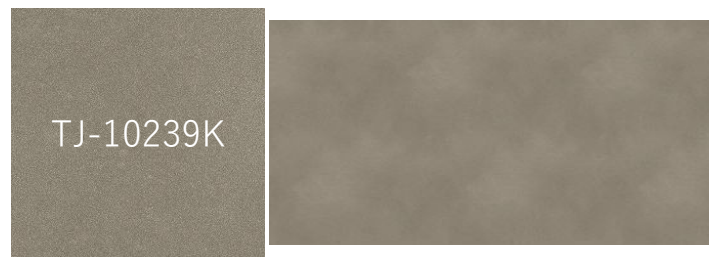


●シングルワンホール洗面混合栓

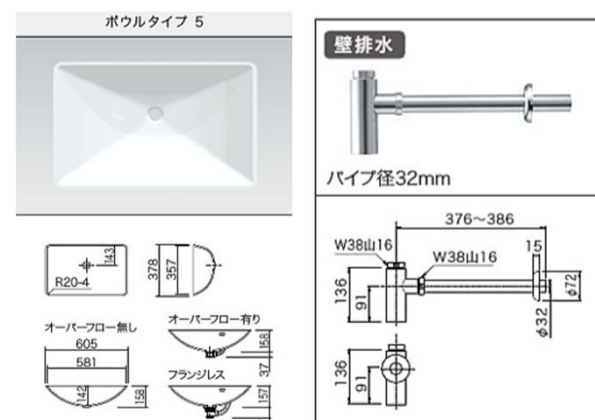






KSA タイプ

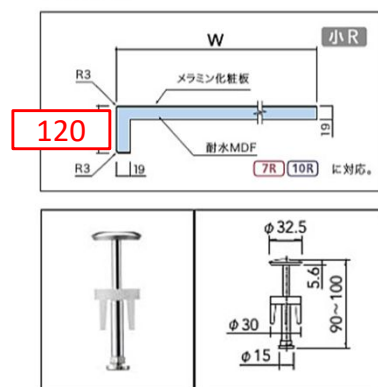

オーバーフロー有り
ポップアップ栓有(水溜め可)

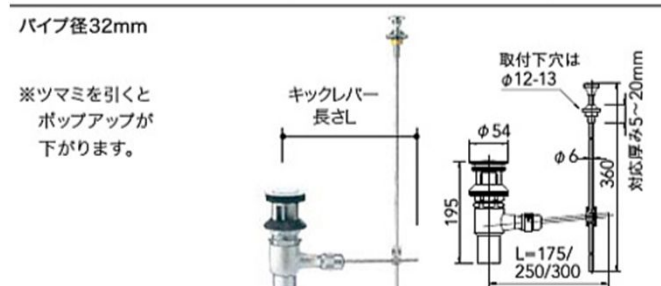



パーツ	色	仕様
①カウンター	TJ-10239K	※ストフォーム 特注
②立ち上がり部材	TJ-10239K	※ストフォーム KAAタイプ
ボウル	KMB5AGW-1	シームレス-取付(フラット)
給水栓	K4750NV-MDP	
排水栓	HMB3002H	ヘアキャッチャー付
排水トラップ	HMB3008	
ブラケット	KH-341WA2	

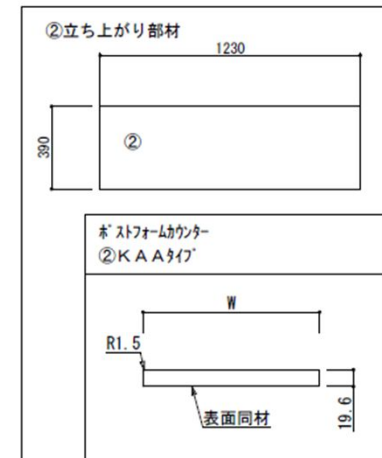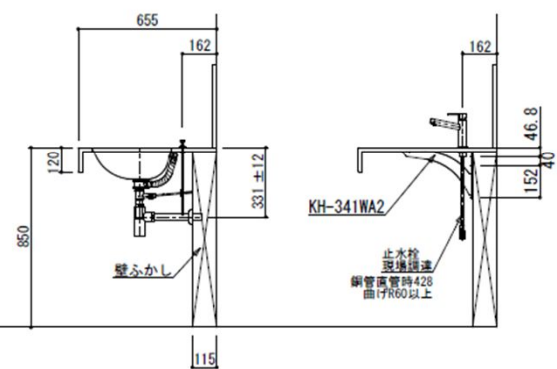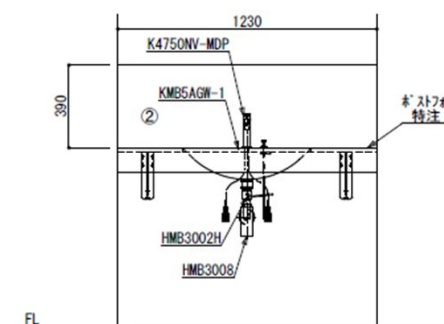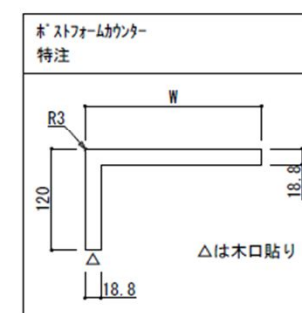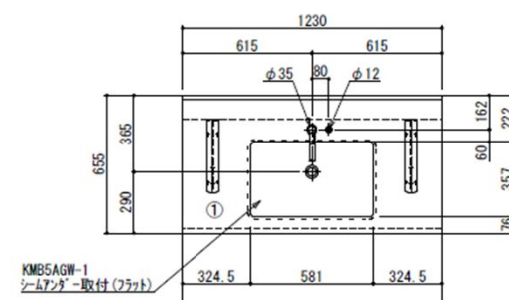

十分に強度のある下地に適切な施工を行ってください。

決定図

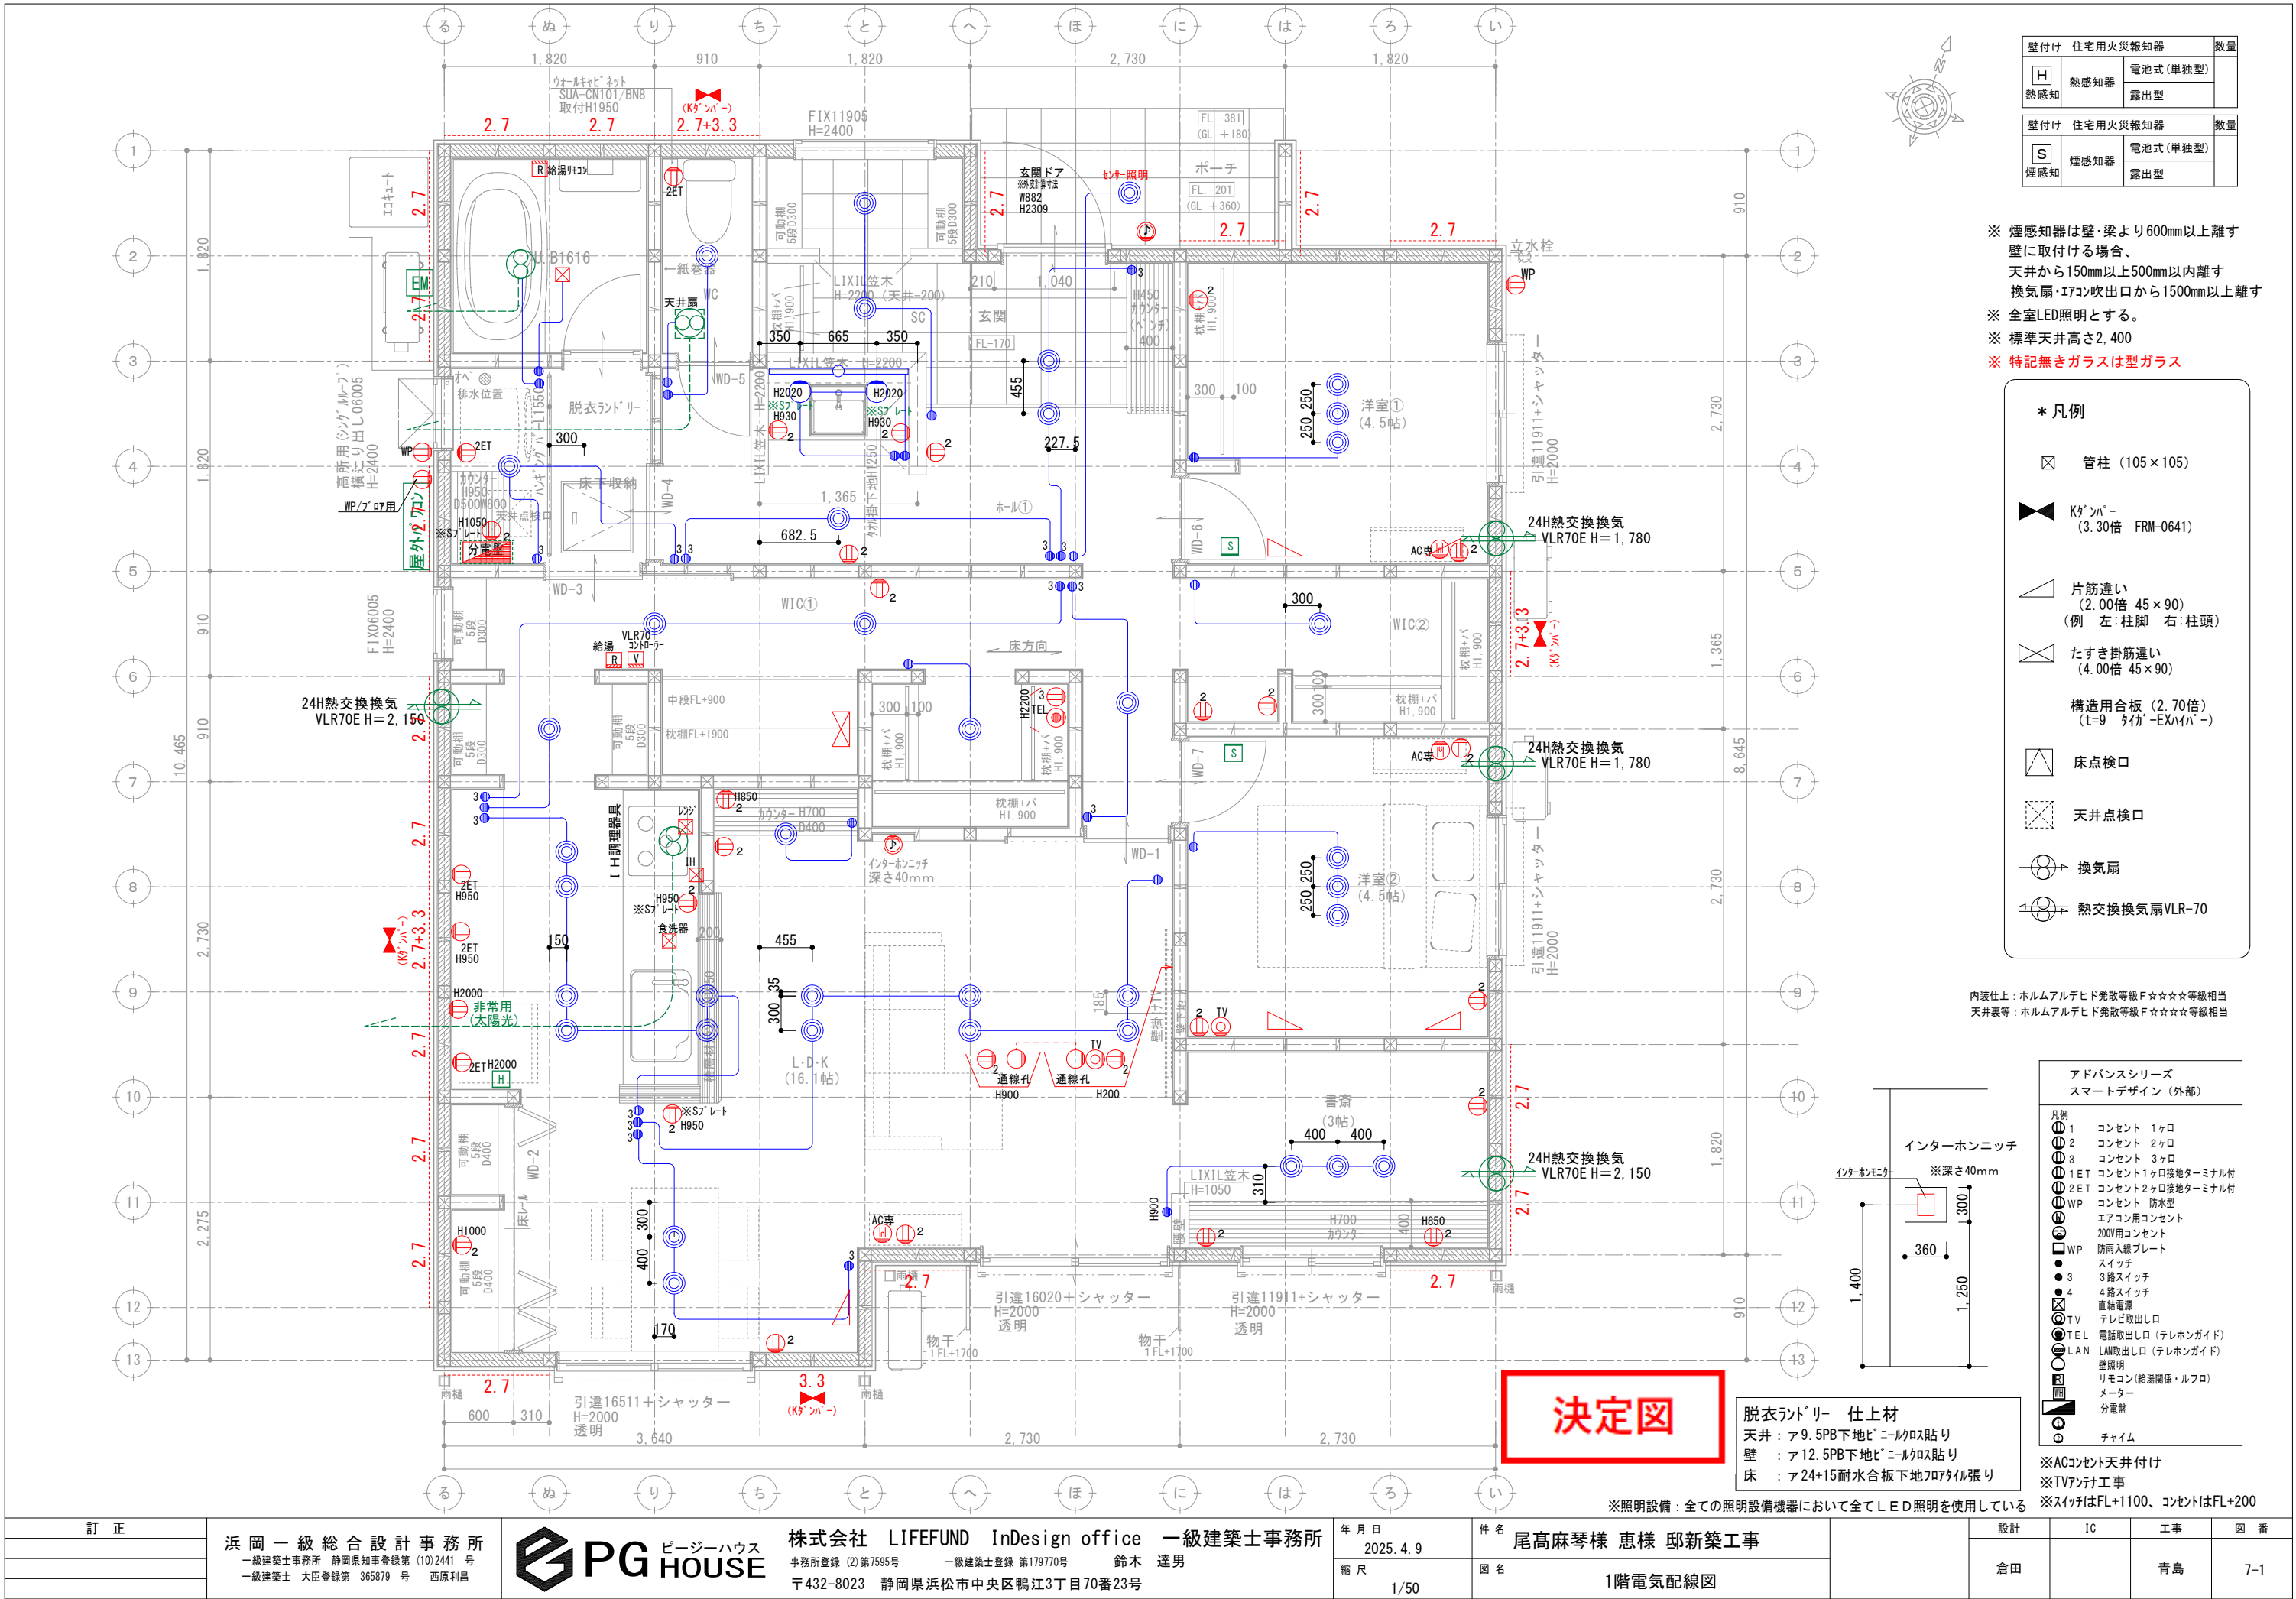

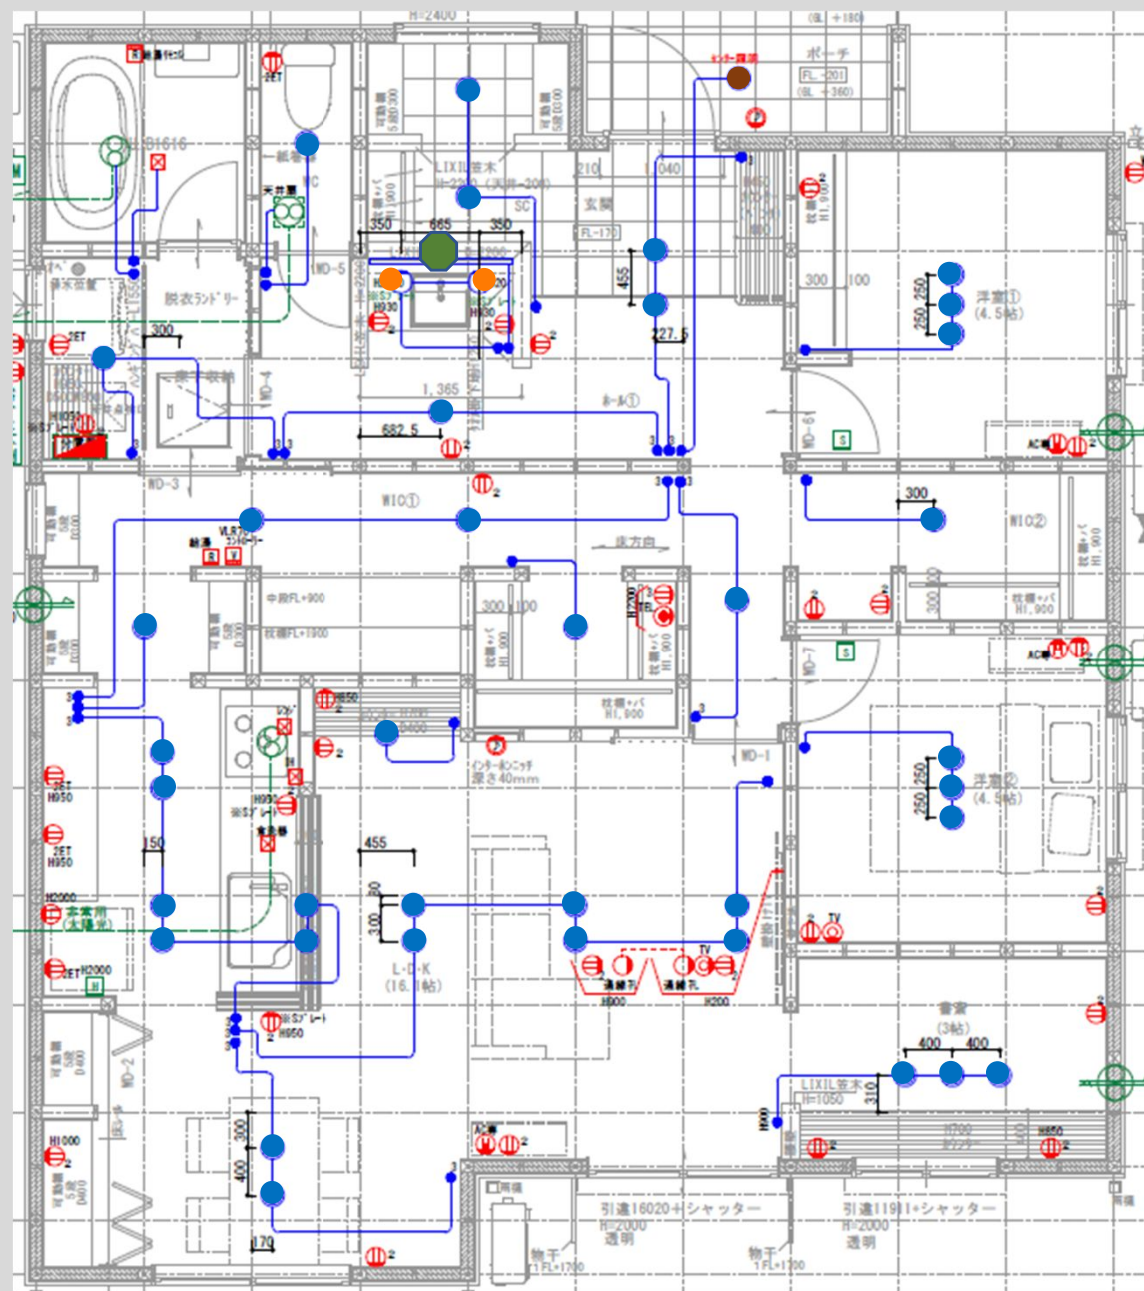

基本照明ダウナイト

● × 36

DDL6102YB



DDL-6102 YB
電球色 / 2700K・Ra83

定格光束 消費電力 固有エネルギー消費効率
370lm 4.6W 80.4lm/W

¥3,600-(税抜) (LED内蔵)

- LED LED 4.6W 白熱灯60W相当
- 鋼板 黒塗装
 - アクリル 乳白(マット)
 - 径φ116 埋込穴φ100 埋込深70mm 0.3kg
 - 8VA
 - 拡散パネル付
 - AC100V
 - 光源寿命60,000時間
 - 取付可能天井厚5~25mm
 - 調光器併用不可

- LED交換不可 非調光
- 防雨形
- 温度保護機能付
- 0.1m 近接限度
- 埋込穴 100
- 埋込必要高 70
- 傾斜天井 55°
- 準耐火

洗面手元灯

● × 1

DDL-4496YB



DSY-3904 ATE
温白色 / 3500K・Ra83

定格光束 消費電力 固有エネルギー消費効率
2170lm 18W 120.5lm/W

¥35,000-(税抜) (ランプ別梱包)

- LED 18W DECO-LINE(ランプ別梱包)
- アルミ型材 シルバーアルマイト
 - 鋼板
 - ポリカーボネート 乳白
 - 巾43 長1200 高52mm 1.3kg
 - 19VA(100V)/20VA(200V)
 - AC100V/200V兼用
 - 連結最大27台(100V時)、54台(200V時)まで
 - 光源寿命40,000時間
 - 調光器併用不可
- 天井・壁(縦・横)・床・浴槽用

- 非調光
- 傾斜天井可能 (縦・横)
- LED交換可能
- 電源内蔵

ポーチ灯

● × 1

DDL-4496YB



DDL-4496 YB
電球色 / 2700K・Ra83

定格光束 消費電力 固有エネルギー消費効率
425lm 7.7W 55.1lm/W

¥18,800-(税抜) (LED内蔵)

- LED LED 7.7W 白熱灯60W相当
- アルミダイカスト 黒塗装
 - アクリル 乳白(マット)
 - 径φ111 埋込穴φ100 埋込深80mm 0.5kg
 - 14VA
 - 点灯照度調節機能付(暗・明・切)
 - 点灯保持時間(1分)
 - 拡散パネル付
 - AC100V
 - 光源寿命50,000時間
 - 取付可能天井厚5~25mm
 - 調光器併用不可
- 【連動器具について】
LED調光タイプ60VAまで
LED非調光タイプ不可 蛍光灯不可
白熱灯60Wまで

- 強制ON 非調光
- ソフトスタート
- フェードアウト
- 60°
- 0.1m 近接限度
- 埋込穴 100
- 埋込必要高 80
- LED交換不可
- 防雨形
- 温度保護機能付

外部：スマートサインシリーズ (Panasonic)



ドアホン：VL-SZ30KL (Panasonic)



洗面灯

● × 2

DBK-42023AG



DBK-42023 AG
温白色 / 3500K・Ra93

定格光束 消費電力 固有エネルギー消費効率
430lm 4W 107.5lm/W

¥17,800-(税抜) (ランプ付)

- LED 4W(E11) 中角形 12Vダイクロロハロゲン35W相当
- アルミ型材 黒塗装
 - アルミダイカスト 黒塗装
 - 巾70 高133 出78mm 0.3kg
 - スイッチ付(入切)
 - 首振り90°・回転360°
 - AC100V
 - 調光可能(5%~100%)
 - 調光にはLED専用(逆位相制御)調光器(別売)をご使用ください。
 - 光源寿命40,000時間

- 調光
- 27°
- 0.1m 近接限度
- 傾斜天井可能
- LED交換可能

内部SW：アドバンス
マッドブラック



2025.4.9


PG House

尾高麻琴様 恵様 邸新築工事

Lighting Plan

(図番 7-2)

決定図

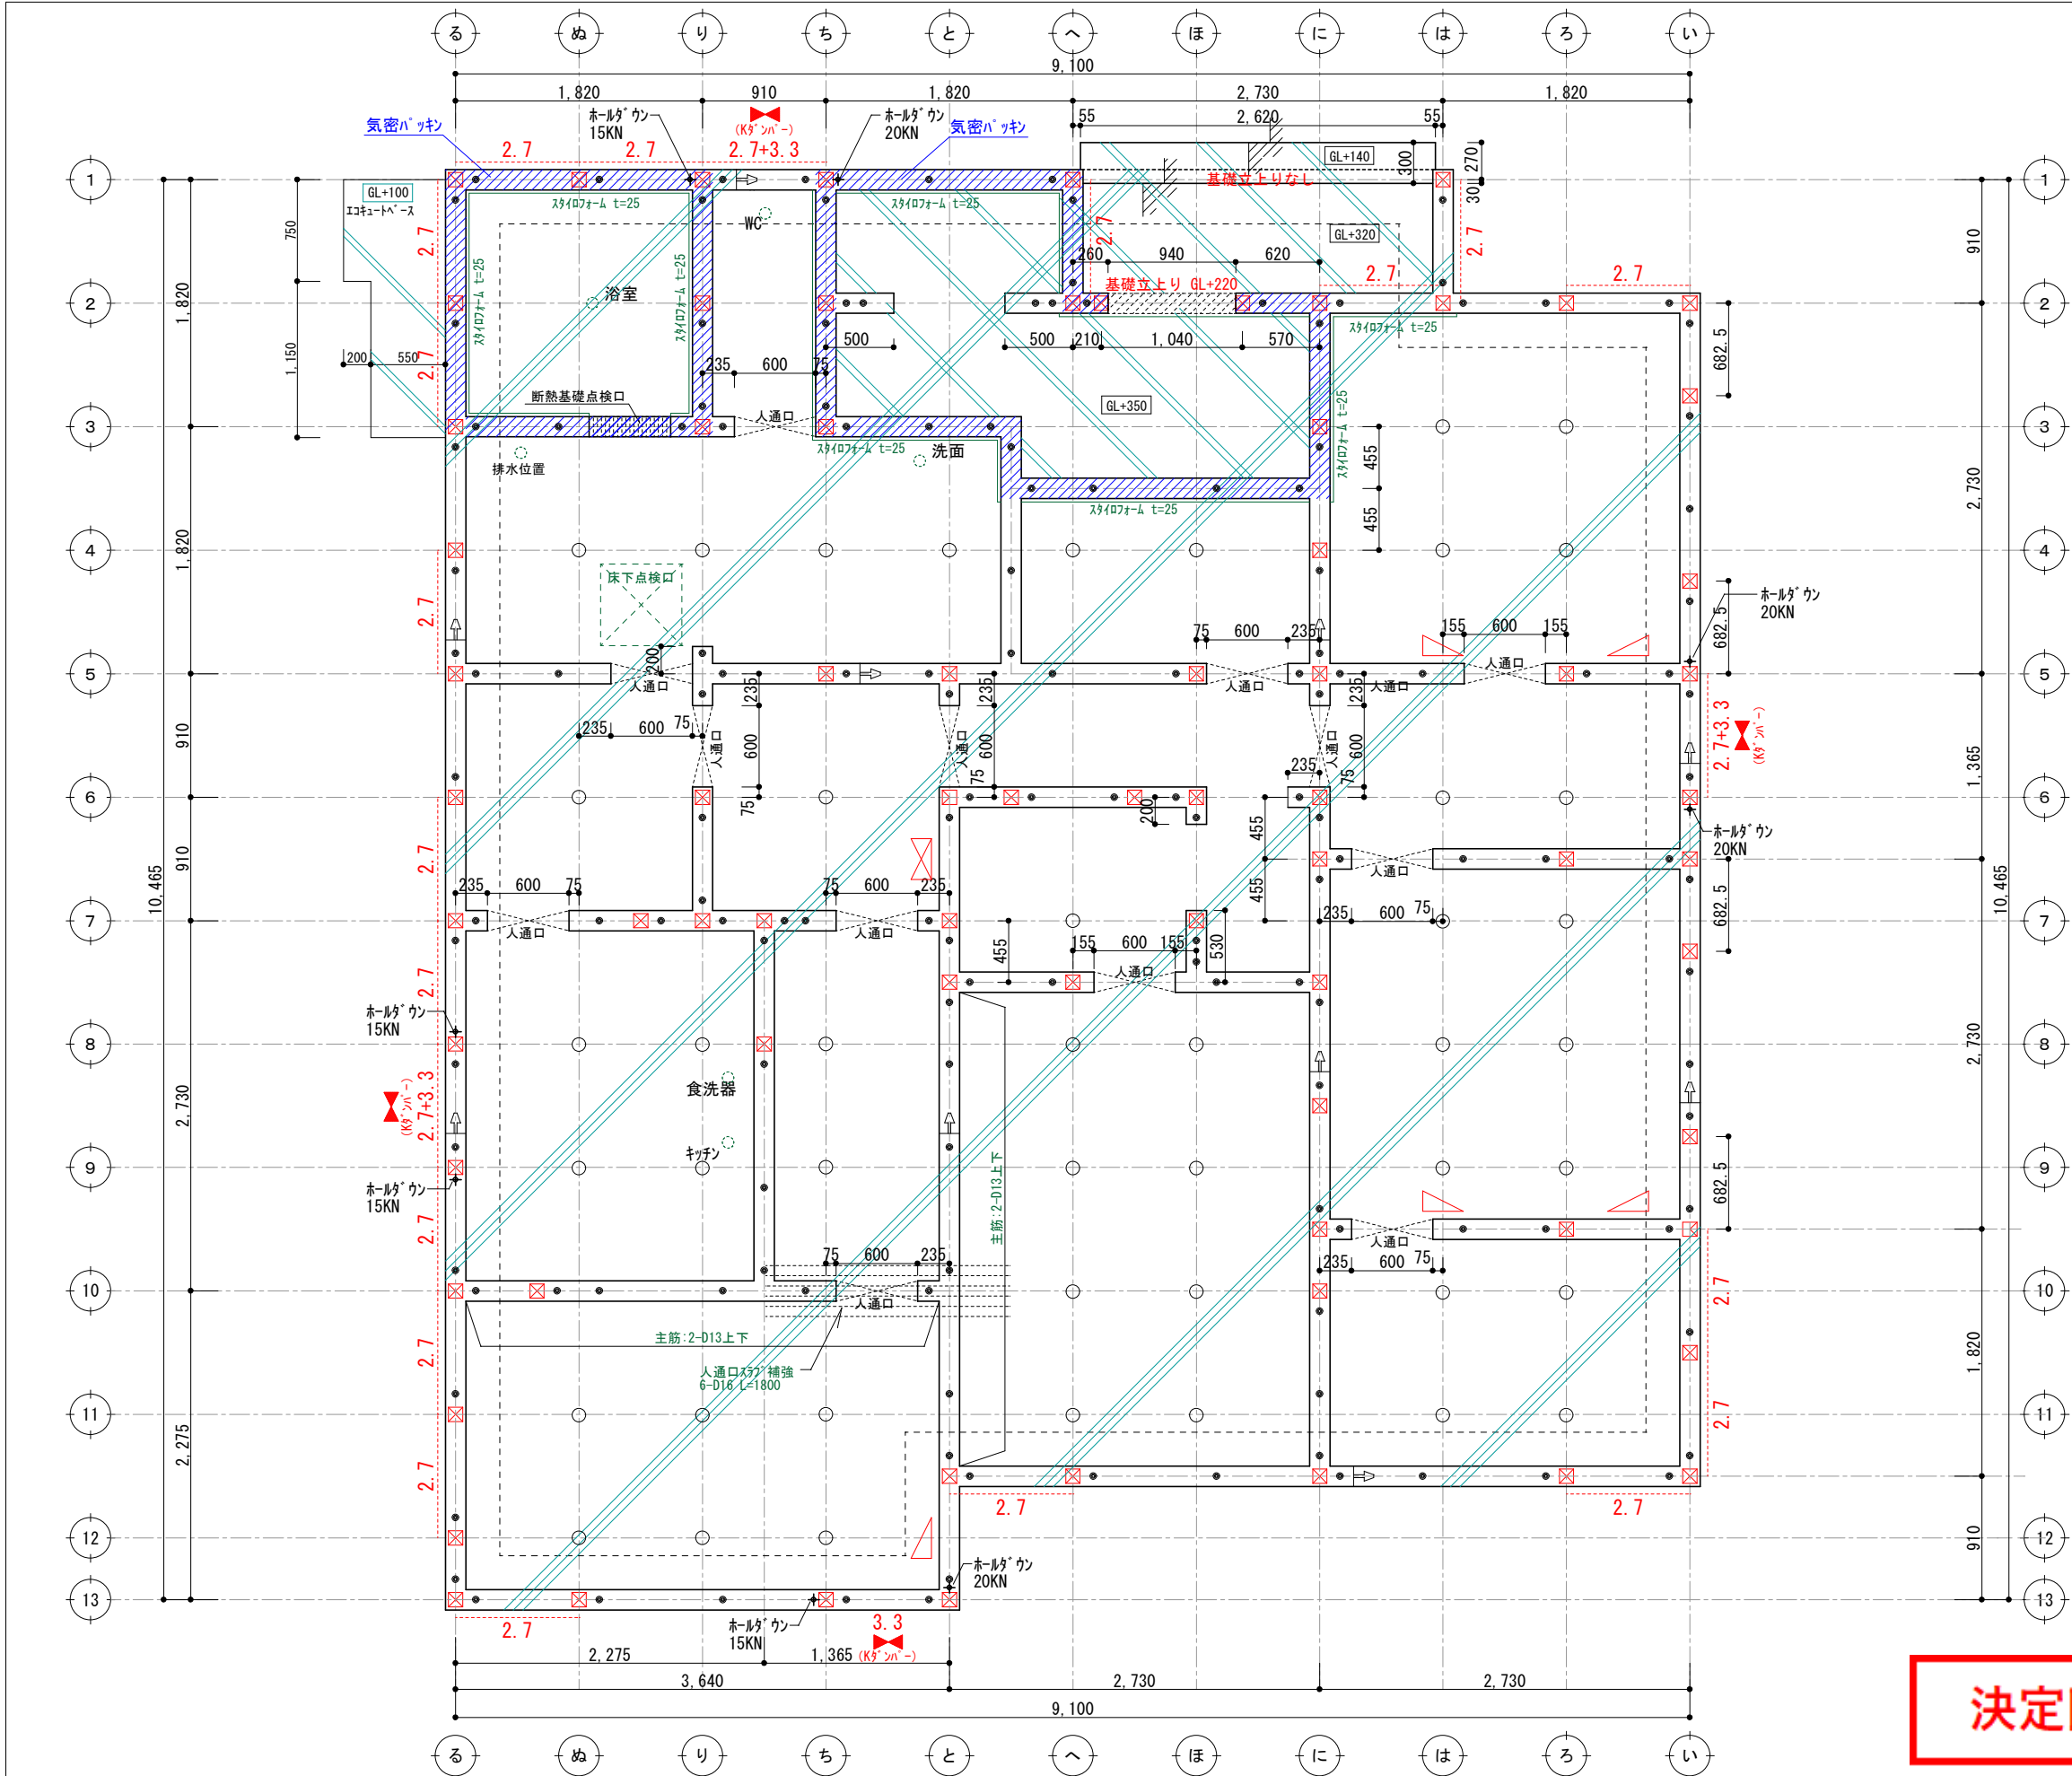

構造体ベースコンクリート t=150


後打ち土間コン

アンカーボルトの配置

- 土台切れの箇所より150mm
- 土台の継手及び仕口の端部より150mm
- 耐力壁の端部、筋交いの脚部より150mm
- 1.82m以下の間隔
- 250mm以上埋込み
- 基礎天端より120mm

筋かい凡例

- 柱脚 柱頭 片筋かい
- たすき掛け筋かい
- 構造用合板

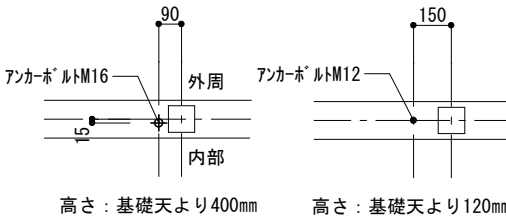

ホールダウン用アンカーボルト配置

アンカーボルト配置

凡例

- 通し柱 (105*105) 管柱 (105*105)
- アンカーボルト M12 L=400
- ✦ ホールダウンアンカー M16 L=800
- 柱芯より90mm 280mm以上埋め込み (カナフィストアンカーボルト M16)
- ⊕ 鋼製束
- ⊢ 土台ジョイント
- ▨ ベースコンクリート (t=150)
- ▨ 後打ちコンクリート

基礎伏図について特記なき場合に限り下記による。

- コンクリート：呼び強度 21N/mm²
- 鉄筋：SD295A
- 設計地耐力：fe=30kN/m²
地耐力計測後、不足の場合は相当の改良を行い、満たすものとする。
- 基礎の位置は、芯振分けとする。
- 玄関・S/C・UB周囲の基礎天端は気密パッキン施工 (網掛け部) とし、その他の基礎天端は基礎パッキン施工とする。
- 設備配管の屋内への取り入れは基礎立上り部のスリーブによる。

決定図

訂正

浜岡一級総合設計事務所
一級建築士事務所 静岡県知事登録第 (10)2441 号
一級建築士 大臣登録第 365879 号 西原利昌




株式会社 LIFE FUND InDesign office 一級建築士事務所
事務所登録 (2) 第7595号 一級建築士登録 第179770号 鈴木 達男
〒432-8023 静岡県浜松市中央区鴨江3丁目70番23号

年月日 2025.4.9
縮尺 1/50

件名 尾高麻琴様 恵様 邸新築工事
図名 基礎伏図

設計	IC	工事	図番
倉田		青島	B-1

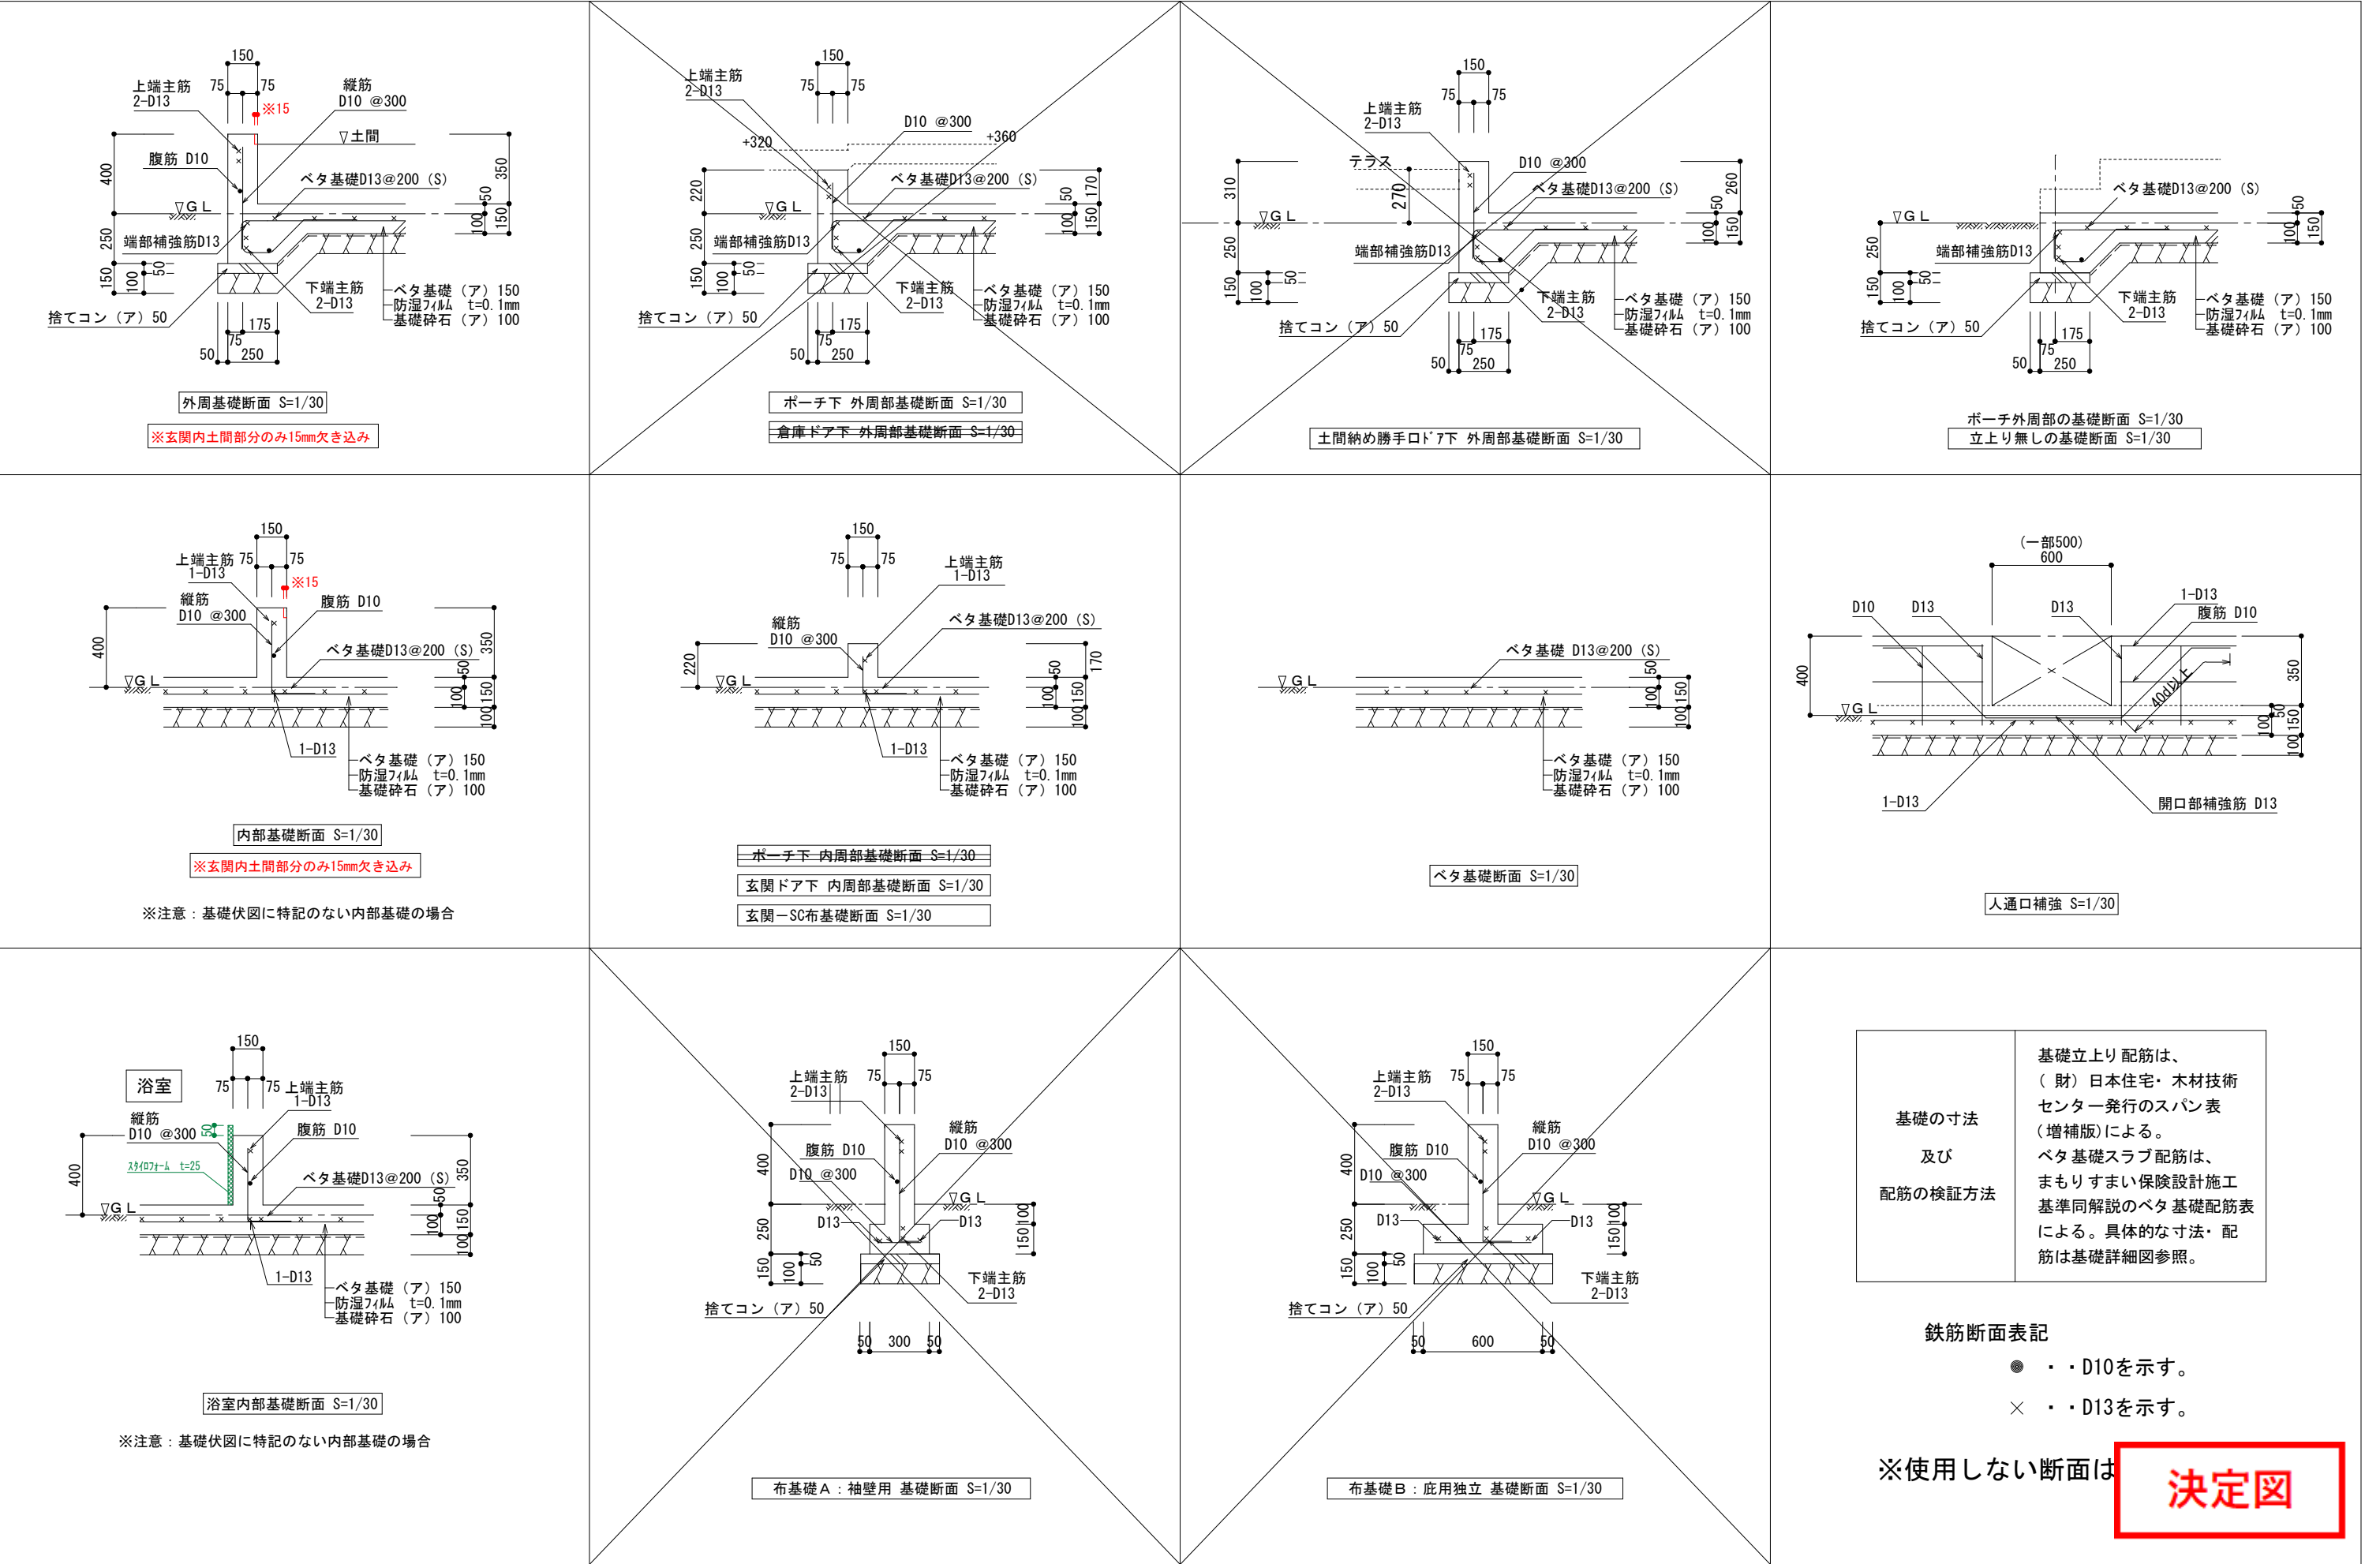

基礎の寸法
及び
配筋の検証方法


基礎立上り配筋は、
(財)日本住宅・木材技術
センター発行のスパン表
(増補版)による。
ベタ基礎スラブ配筋は、
まもりすまい保険設計施工
基準同解説のベタ基礎配筋表
による。具体的な寸法・配
筋は基礎詳細図参照。

鉄筋断面表記

- ・・・D10を示す。
- ×・・・D13を示す。

※使用しない断面は

決定図

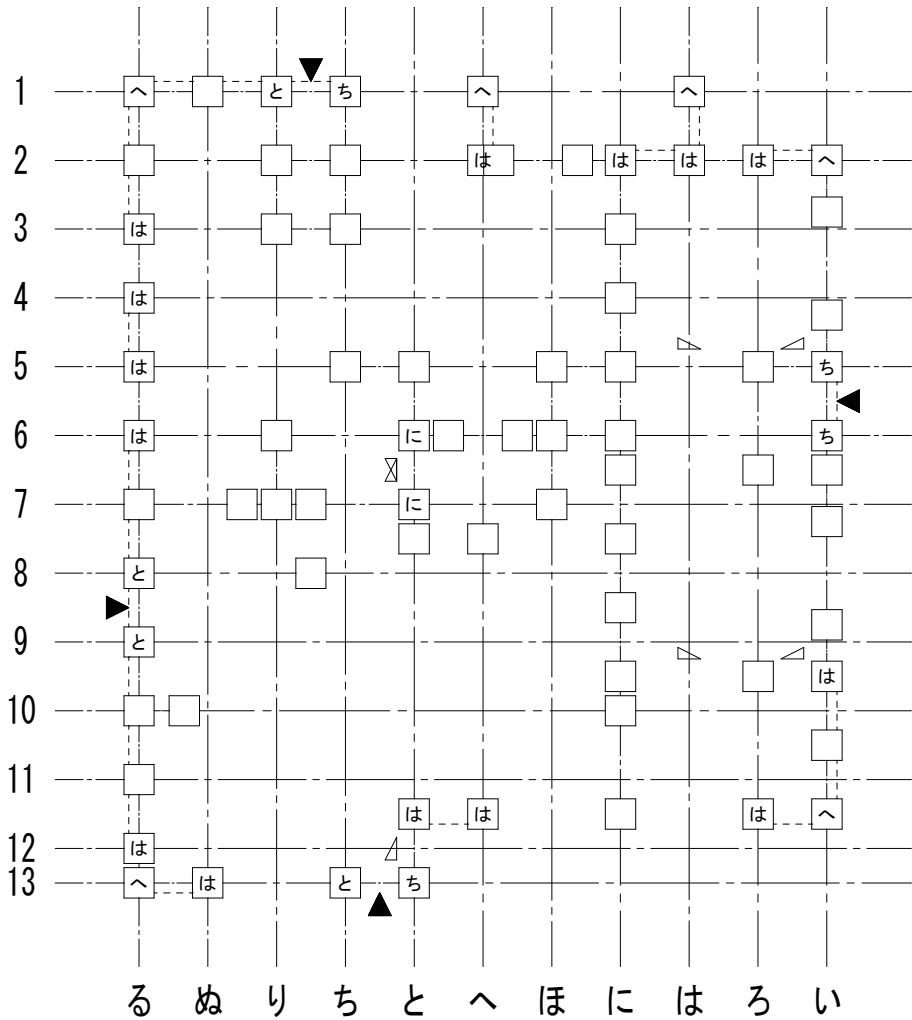

1 階柱壁伏図

接合部凡例				*接合部凡例はユーザ設定されたものです。	
記号	仕様（カナイ金物）		N	倍率	
SBCP	スリムビルドコーナー75, チビクリCK(化粧柱の場合)		0.00	1.00	
SBCP	スリムビルドコーナー75, チビクリCK(化粧柱の場合)		0.65	1.00	
SBCP	は	スリムビルドコーナー75	1.00	1.00	
ARCG	に	アレントコーナー合板用	1.40	2.20	
ARCG	ほ	アレントコーナー合板用	1.60	2.20	
ARCG	へ	アレントコーナー合板用	1.80	2.20	
HD15	と	ブレイブホールダウン B-HD15	2.80	3.60	
HD20	ち	ブレイブホールダウン B-HD20	3.70	4.70	
HD25	り	ブレイブホールダウン B-HD25	4.70	4.80	
HD30	ぬ	ブレイブホールダウン B-HD30	5.60	7.20	
J1	る	腰掛け蟻若しくは大入れ蟻掛け+羽子板ボルト、短冊金物		1.90	梁継手・仕口用
J2	を	腰掛け蟻若しくは大入れ蟻掛け+羽子板ボルト、短冊金物×2		3.00	梁継手・仕口用

※表示なき金物は「は」とする。

接合部凡例				*接合部凡例はユーザ設定されたものです。	
記号	仕様（タナカ金物）		N	倍率	
FCP	フックコーナー, チビクリCK(化粧柱の場合)		0.00	1.00	
FCP	フックコーナー, チビクリCK(化粧柱の場合)		0.65	1.00	
FCP	は	フックコーナー	1.00	1.00	
CCP	に	シナコーナー	1.40	2.20	
CCP	ほ	シナコーナー	1.60	2.20	
CCP	へ	シナコーナー	1.80	2.20	
HD15	と	ビス止めホールダウンU HD15	2.80	3.60	
HD20	ち	ビス止めホールダウンU HD20	3.70	4.70	
HD25	り	ビス止めホールダウンU HD25	4.70	4.80	
HD30	ぬ	ビス止めホールダウンU HD15×2 (HD35)	5.60	7.20	
J1	る	腰掛け蟻若しくは大入れ蟻掛け+羽子板ボルト、短冊金物		1.90	梁継手・仕口用
J2	を	腰掛け蟻若しくは大入れ蟻掛け+羽子板ボルト、短冊金物×2		3.00	梁継手・仕口用


※表示なき金物は「は」とする。

筋かいの種類に応じた筋かいの端部の接合部の仕様		
	筋かいの種類	接合部の仕様（構造方法）
イ	鉄筋φ9	柱又は横架材を貫通し、三角座金を介してナット締め、又は鋼板添え板を用い鋼板を柱及び横架材にCN90, 8本平打ち
ロ	筋かい:15×90	柱・横架材を欠き込み、柱・横架材双方に対してN65, 5本平打ち
ハ	筋かい:30×90	鋼板添え板t=1.6mmを筋かいに対してボルトφ12及びCN65, 3本平打ち、柱に対してCN65, 3本平打ち、横架材に対してCN65, 4本平打ち。筋かいプレートBP同等品
ニ	筋かい:45×90	鋼板添え板t=2.3mmを筋かいに対してボルトφ12及びスクリュー釘φ4.5L50, 7本平打ち、柱及び横架材に対してスクリュー釘φ4.5L50, 5本平打ち。筋かいプレートBP-2同等品
ホ	筋かい:90×90	柱又は横架材にボルトφ12mmを用いて一面剪断接合

胴差と通し柱の接合部の仕様		
	胴差と通し柱の条件	仕口
T1	通し柱の片側に胴差が来る場合	胴差を柱にかたぎ大入れ短ほぞ差しの上、羽子板ボルト、かね折り金物又は同等以上の仕口
T2	通し柱の両側に胴差が来る場合	胴差を柱にかたぎ大入れ短ほぞ差しの上、短冊金物又は、同等以上の仕口で胴差相互を緊結
T3	通し柱と胴差の接合部の近くに90×90以上の筋かいが来る場合(通し柱が建物の出隅にあるか、筋かい壁が外壁と直交して接する場合)	胴差を通し柱に、15KN用引き寄せ金物を水平に用いて緊結

決定図

※ 37セトクロス 指示書

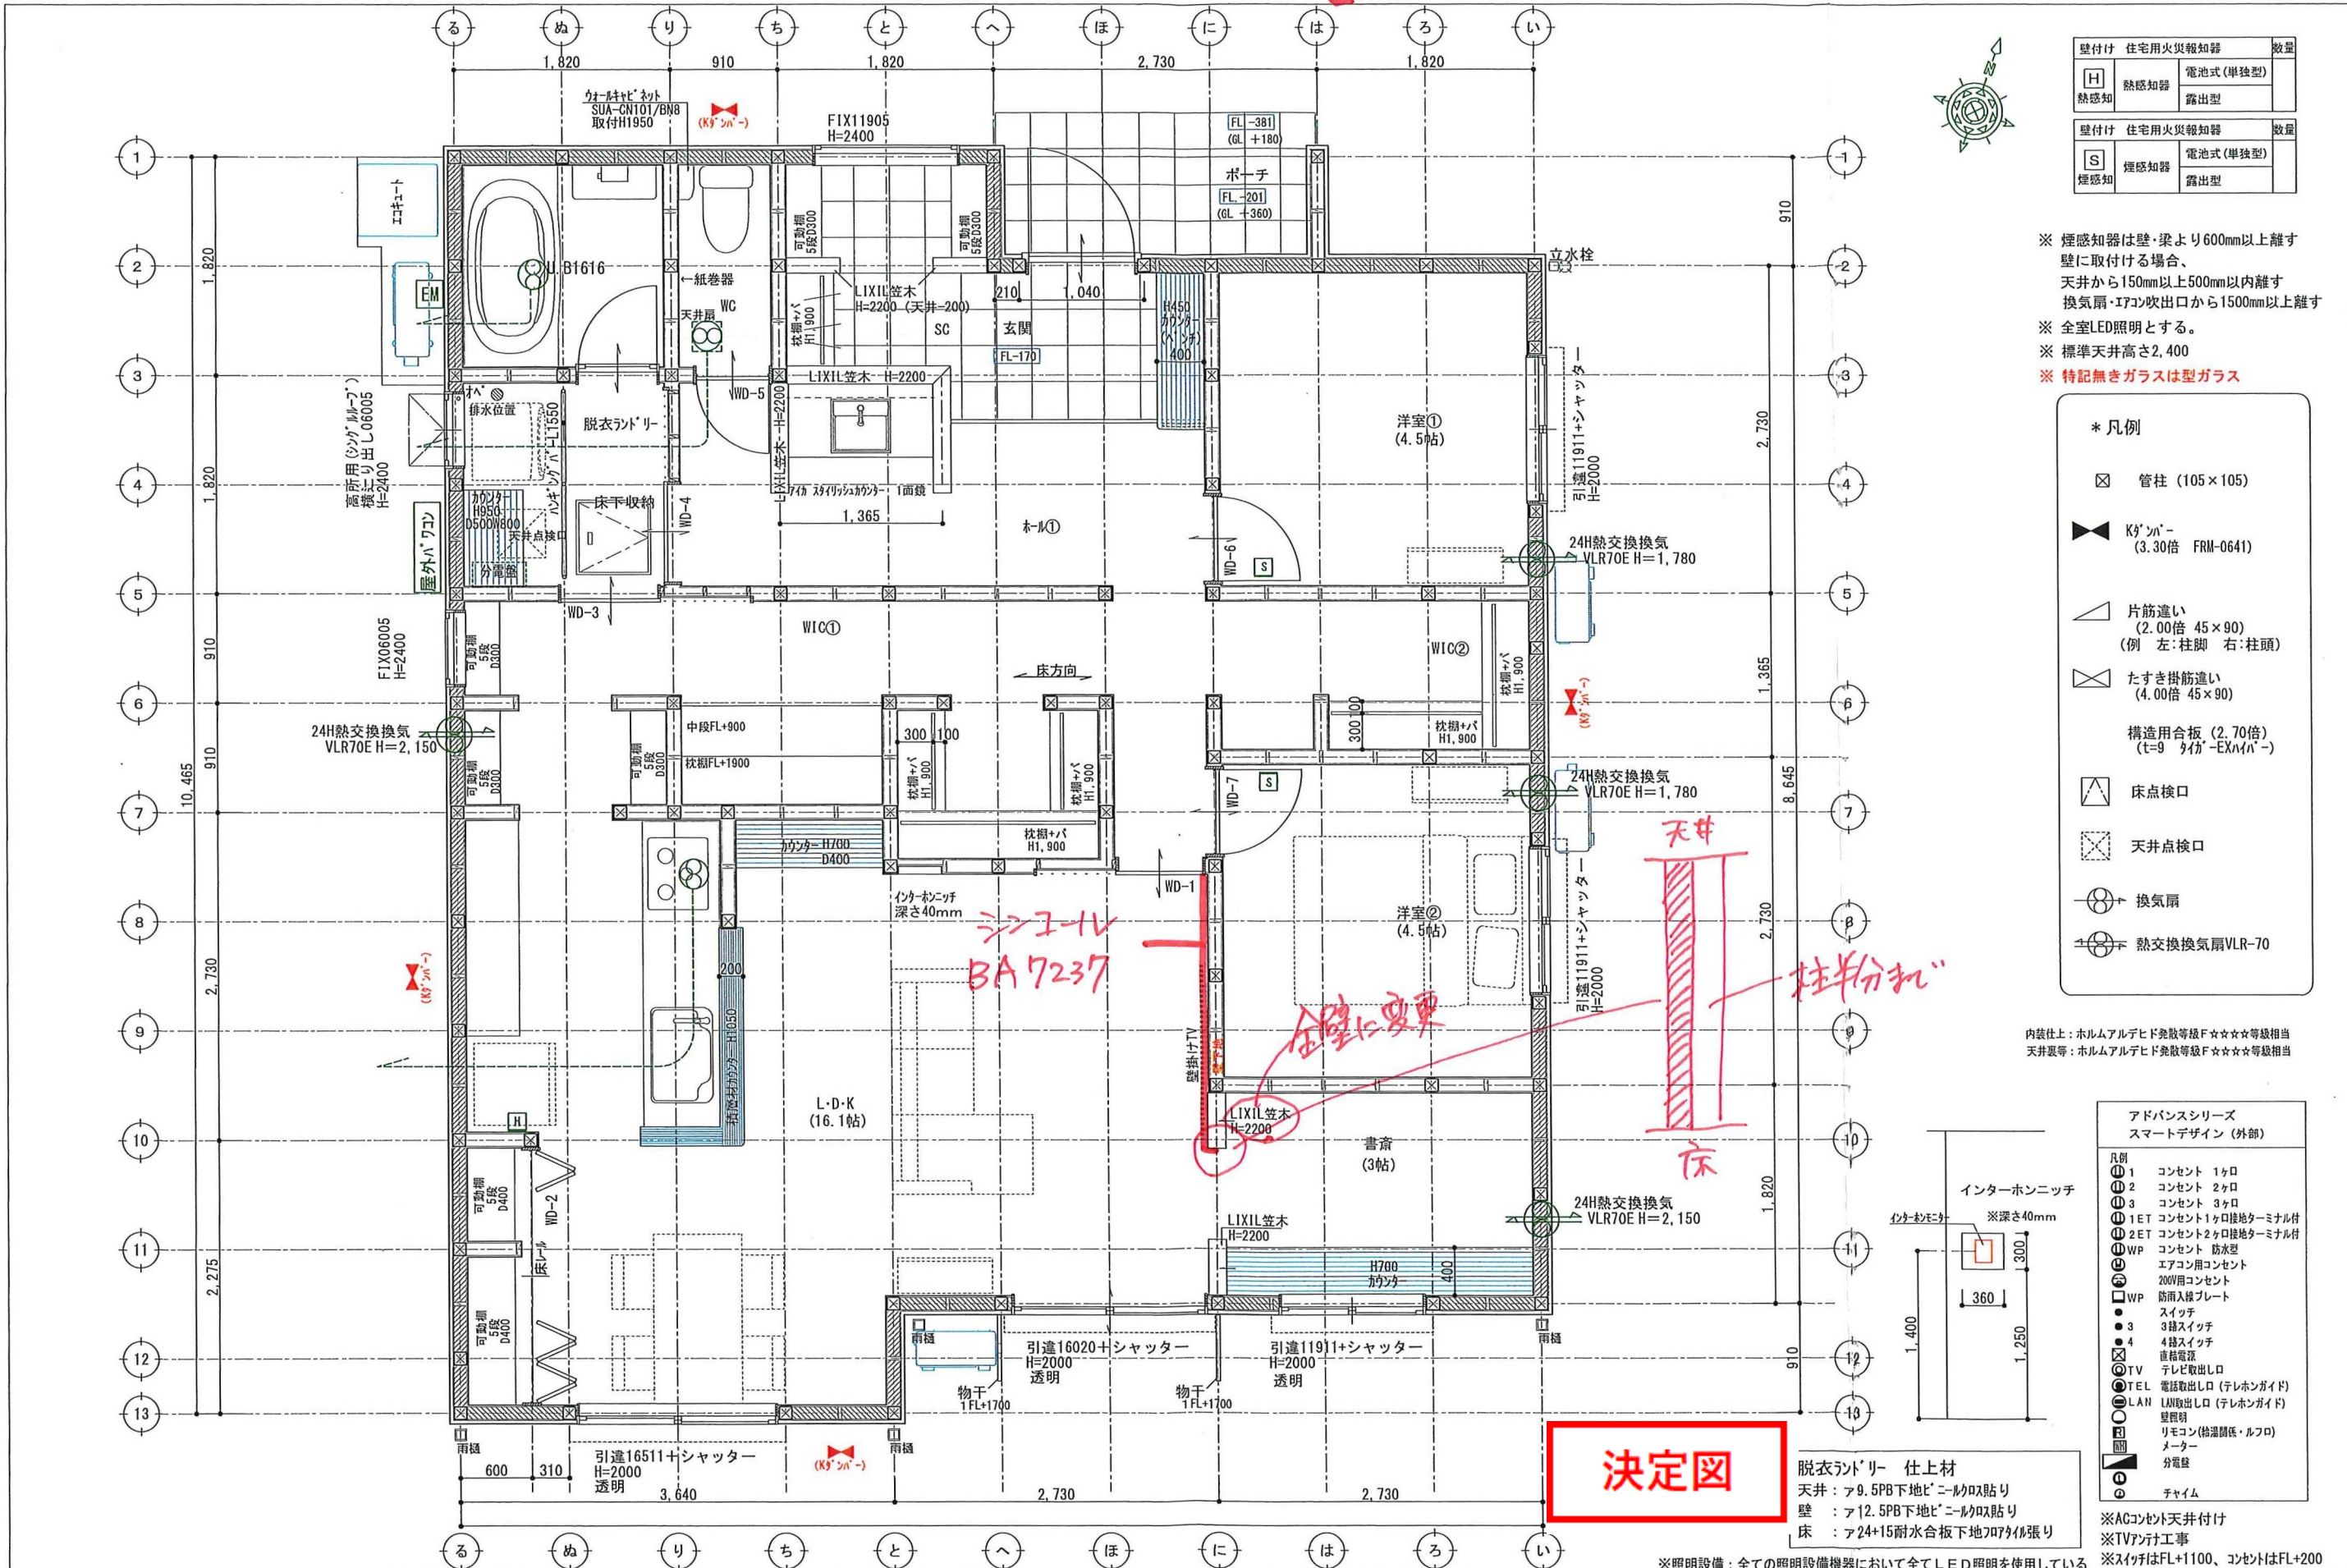

壁付け 住宅用火災報知器			数量
[H] 熱感知	熱感知器	電池式(単独型)	
		露出型	
壁付け 住宅用火災報知器			数量
[S] 煙感知	煙感知器	電池式(単独型)	
		露出型	


※ 煙感知器は壁・梁より600mm以上離す
壁に取付ける場合、
天井から150mm以上500mm以内離す
換気扇・エアコン吹出口から1500mm以上離す
※ 全室LED照明とする。
※ 標準天井高さ2,400
※ 特記無きガラスは型ガラス

* 凡例

- ☒ 管柱 (105×105)
- ☒ K'ンバー (3.30倍 FRM-0641)
- △ 片筋違い (2.00倍 45×90) (例 左:柱脚 右:柱頭)
- ☒ たすき掛筋違い (4.00倍 45×90)
- 構造用合板 (2.70倍) (t=9 タイプ-EXN/A-)
- △ 床点検口
- ☒ 天井点検口
- ⊕ 換気扇
- ⊕ 熱交換換気扇VLR-70

内装仕上: ホルムアルデヒド発散等級F☆☆☆☆等級相当
天井裏等: ホルムアルデヒド発散等級F☆☆☆☆等級相当

アドバンスシリーズ スマートデザイン (外部)		
凡例	①	コンセント 1ヶ口
	②	コンセント 2ヶ口
	③	コンセント 3ヶ口
	①1ET	コンセント1ヶ口接地ターミナル付
	①2ET	コンセント2ヶ口接地ターミナル付
	WP	コンセント 防水型
	Ⓜ	エアコンコンセント
	Ⓜ	200V用コンセント
	WP	防雨入線プレート
	●	スイッチ
	●3	3路スイッチ
	●4	4路スイッチ
	Ⓜ	直結電源
	ⓂTV	テレビ取出口
	ⓂTEL	電話取出口 (テレホンガイド)
	ⓂLAN	LAN取出口 (テレホンガイド)
	Ⓜ	壁照明
	Ⓜ	リモコン (給湯・暖房・ルフロ)
	Ⓜ	メーター
	Ⓜ	分電盤
	Ⓜ	チャイム

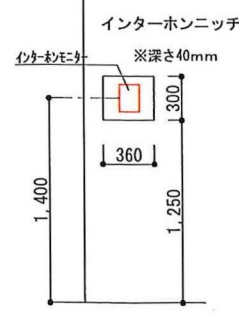

脱衣ランドリー 仕上材
天井: ア9.5PB下地ビニール貼
壁: ア12.5PB下地ビニール貼
床: ア24+15耐水合板下地70アタリ張り

※照明設備: 全ての照明設備機器において全てLED照明を使用している