



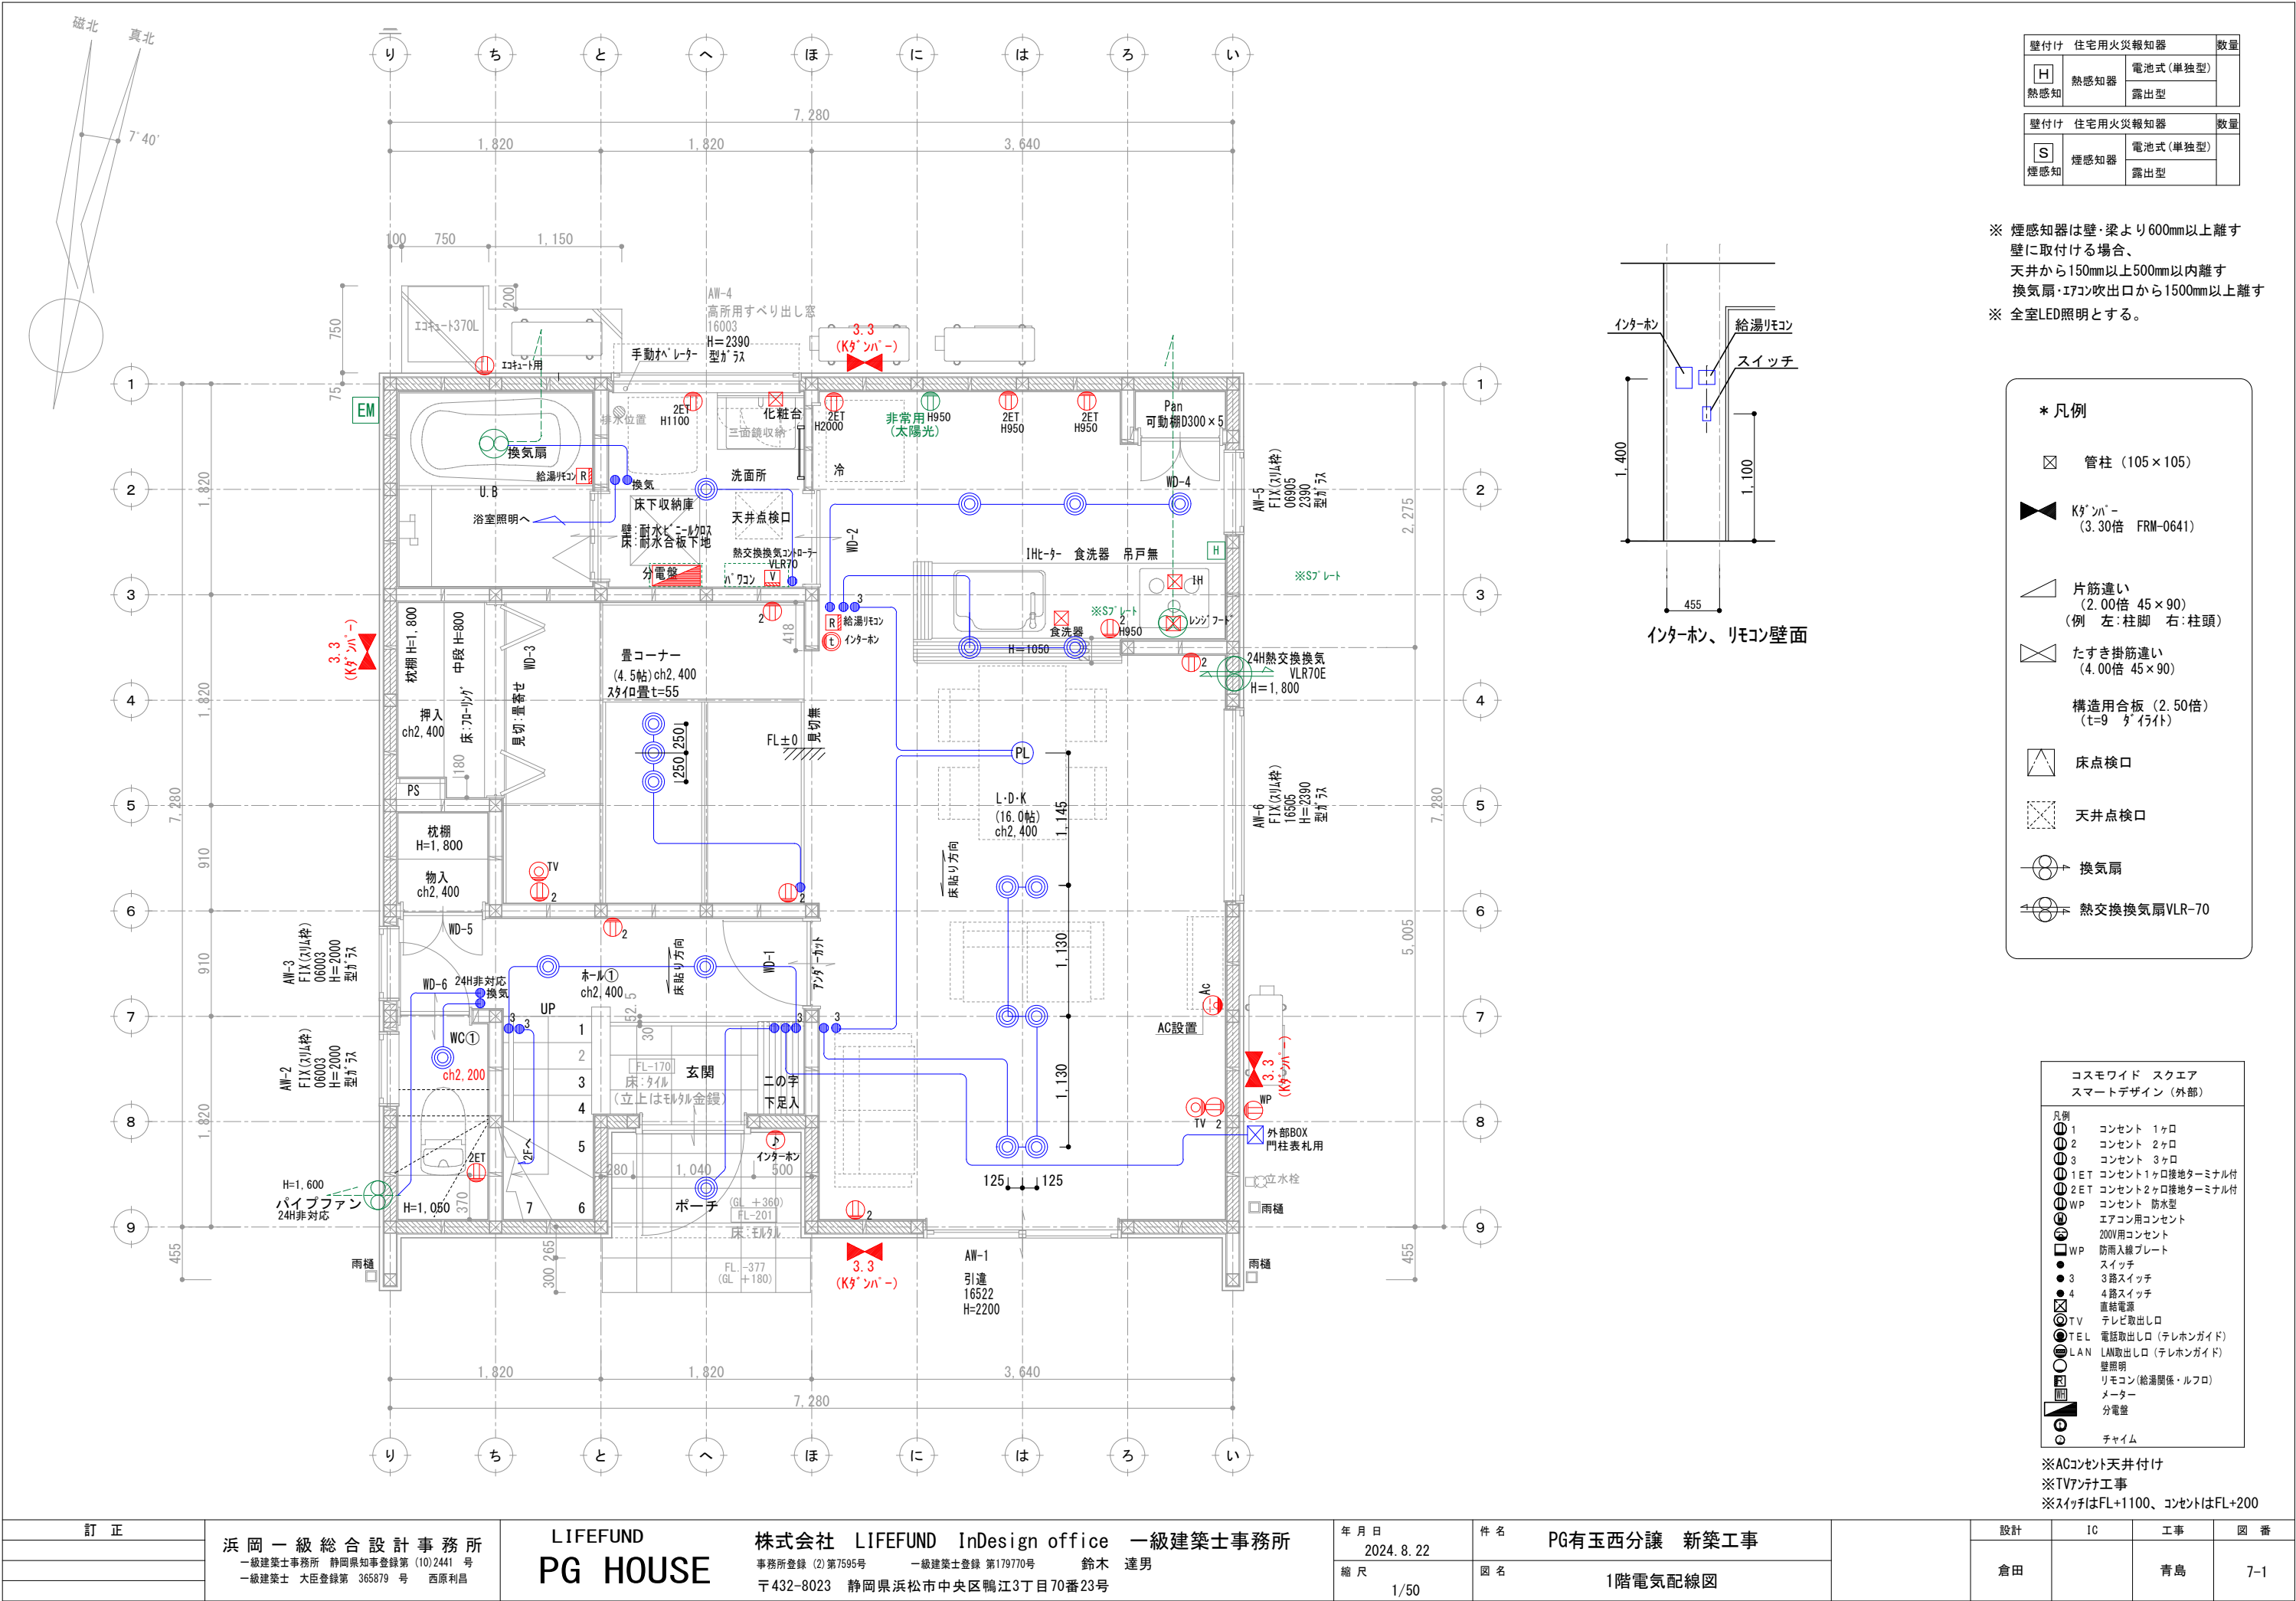

壁付け 住宅用火災報知器			数量
H 熱感知	電池式 (単独型)		
	露出型		

壁付け 住宅用火災報知器			数量
S 煙感知	電池式 (単独型)		
	露出型		

※ 煙感知器は壁・梁より600mm以上離す壁に取付ける場合、天井から150mm以上500mm以内離す換気扇・エアコン吹出口から1500mm以上離す
※ 全室LED照明とする。

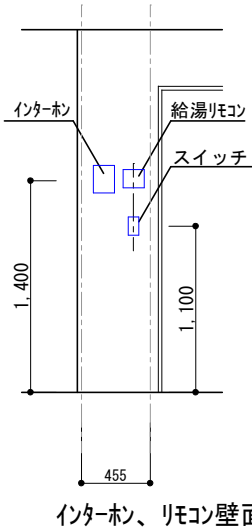

- * 凡例**
- 管柱 (105×105)
 - Kダクト (3.30倍 FRM-0641)
 - 片筋違い (2.00倍 45×90)
(例 左:柱脚 右:柱頭)
 - たすき掛筋違い (4.00倍 45×90)
 - 構造用合板 (2.50倍)
(t=9 タイライト)
 - 床点検口
 - 天井点検口
 - 換気扇
 - 熱交換換気扇 VLR-70

コスモワイド スクエア スマートデザイン (外部)	
凡例	
1	コンセント 1ヶ所
2	コンセント 2ヶ所
3	コンセント 3ヶ所
1ET	コンセント1ヶ所接地ターミナル付
2ET	コンセント2ヶ所接地ターミナル付
WP	コンセント 防水型
Ⓐ	エアコン用コンセント
200V	200V用コンセント
WP	防雨入線プレート
スイッチ	スイッチ
3	3路スイッチ
4	4路スイッチ
直結電源	直結電源
TV	テレビ取出口
TEL	電話取出口 (テレホンガイド)
LAN	LAN取出口 (テレホンガイド)
壁照明	壁照明
リモコン	リモコン (給湯関係・ルフロ)
メーター	メーター
分電盤	分電盤
チャイム	チャイム

※ACコンセント天井付け
※TVアンテナ工事
※スイッチはFL+1100、コンセントはFL+200