


■ 仕 様		■ HEAT20 G1
断熱工事	■ 床:カネライトフォーム t65 ■ 土間床等の外周:スタイロフォームAT t25 ■ 壁:アクアフォームLITE吹付 t85 ■ 天井:アクアフォームLITE吹付 t170	
床下換気	■ 基礎パッキン JOTO (玄関・UB周り:気密基礎パッキン)	
防虫防蟻	■ 土壌処理・木部 ガントナーMC	

■ 外 部 仕 上 表			■ 22条地域
部位		仕上・仕様・メーカー	色番・品番
屋根		■ ガルバリウム鋼板(t0.35)UK立平 ニスクカラーPro GH 軒先 金物 日本住環境REV-1	GHK01 Sブラック
パラペット笠木		■ なし	
破風・鼻隠		■ なし	
雨樋	(軒樋)	■ Panasonic サーフeskエアFS-I型	ミルクホワイト
	(縦樋)	■ Panasonic S30角樋	ミルクホワイト
軒天	屋根軒	■ ニチハ軒天5 木目調 910×1820×5	ライト
	ポーチ軒	■ 神島化学 t= 6mm 軒天ボード エンボス	Wファリーホワイト
	バルコニー軒	■ なし	
オーバーハング水切り		■ ガルバリウム鋼板 ※外壁合わせ JOTO:HF-A3550	ホワイト
外壁	通気金物(15mm)	■メイン ニチハ エモンekセラード16 Vシリーズ しぶきV	MG/パニラホワイトII
	※下地面材:タイガーEXハイパー	■アクセントA なし	
	防火認定 PC030BE-4028	■アクセントB なし	
玄関ポーチ		■ 床 LIXILパセオ300/PSO-FIO 4	-
基礎		■ 立上り巾木: モルタル刷毛引き	-
基礎水切り金物		■ JOTO鋼板製 防鼠材付き水切り JOTO:WMF-N35	ホワイト
バルコニー	床・内壁	■ 床:FRP防水仕上(グレー) 壁:外壁同仕上げ	-
	笠木	■ アルミ笠木	ブラック
外部建具		■ Ykkap APW330 (アルゴンガス日射遮蔽型 断熱タイプLow-E ブルー) ・SD、TSで記載がないものは、オペレーターハンドルとする ・オペレーター付サッシは固定網戸とする ・グレモンハンドル式サッシの選択箇所は可動網戸とする	外観 ブラック 内観 外観色と同じ ※網戸付 樹脂スパーサ
シャッター		■ なし	
壁体通気水切り		FVK-415F JOTO ※軒天換気兼用	ホワイト
玄関扉		■ YKKapヴェナートD30(D2仕様) タグキーx3、非常用キーx2 (電池式) ※ピタットキー	ドア型: N08N ドア色: ガッシュウォールナット ハンドル: ストレート 色 ブラック
外部物干し金物		■ 川口技研LP型-550 バルコニー内側壁	ホワイト
換気フード		■ 局所換気扇(トイレ 浴室 キッチンフード) 防火ダンパー無 ■ ダクトレス熱交換換気システム (日本スティーベル株式会社) VLR-70E 防火ダンパー無	外気フード: ホワイト 外気フード: W ホワイト

	浜 岡 一 級 総 合 設 計 事 務 所	株式会社 LIFEFUND InDesign office 一級建築士事務所	年 月 日	2024.7.15	件名	PG有玉西 分譲		設計	IC	工務	図 番
	一級建築士事務所 静岡県知事登録第 (10)2441 号	事務所登録 (2)第7595号 一級建築士登録 第179770号 鈴木 達男	縮尺		図面	仕上表 1		倉田		青島	1-1
	一級建築士 大臣登録第 365879 号 西原利昌	〒432-8023 静岡県浜松市中央区鴨江3丁目70番23号									


■ 構 造 概 要			
基礎	■ RCベタ基礎コンクリート		
通し柱・管柱	■ 構造用集成材 105×105		間柱 ■ 集成材
土台	■ 桧 105×105	大引き ■ 桧 90*90	筋交い ■ 構造用製材 火打梁 ■ 鋼製火打(当社基準により米松あり)
桁・梁	■ 構造用製材及び集成材		制震装置 ■ Kダンパー (株)アイ・エム・エー

■ 設 備 装 着 品				
住宅設備	部位	メーカー	商品名 ※ 詳細は見積り、プレゼン参照	見積りNo. (日付)
	キッチン	LIXIL	■ ES I型D650 食洗器 IH 壁付レンジフードASR	見積り番号 : (日付)
	バックカウンタ ※オプション	LIXIL	■ なし	見積り番号 : (日付)
	浴室	LIXIL	■ AX1616 ※換気扇	見積り番号 : (日付)
	1Fトイレ	LIXIL	■ ベーシアシャワートイレ 白 ● タオル掛け: KF-AA70D(リンク) タンク手洗 有り ● 紙巻き器: CF-AA22H /WA	見積り番号 : (日付)
	2Fトイレ	LIXIL	■ ベーシアシャワートイレ 白 ● タオル掛け: KF-AA70D(リンク) タンク手洗 有り ● 紙巻き器: CF-AA22H /WA	見積り番号 : (日付)
	洗面台	LIXIL	■ EV W750(D500タイプ) 扉:グロスホワイト [引出しタイプ シングルハンドシャワー スタンダードLED三面鏡 ● タオル掛け: KF-AA71D(バー)	見積り番号 : (日付)
給排水設備	給湯器		■ エコキュート370L Panasonic NSシリーズ スタンダードモデル 追い焚きフルオート	
	排水		■ 下水	
	外水栓		■ 1 カ所 (平面図参照) ■ 外部立栓柱: PVC製 水栓柱12型【前澤化成工業】	
	外部ガーデンパン		■ 無し	
	その他		■ 洗濯機用単水栓: 緊急止水弁付 ■ 洗濯機用排水:トラップ金物(標準)	
ガス配管設備			■ なし (平面図参照)	
電気設備	インターホン		■ パナソニック VL-SZ30KL	
	TVアンテナ		■ UHF + BS・110度CS／CSアンテナ [2K・4K・8K対応] ■ホワイト	
	エアコン		■ 無し 設置場所:	
	ソーラー		■ あり(Qセルズ) 12 枚 5.22 KW Re.RISE-G2 435 (1722×1134×30)	
	※5.16kw標準搭載		■ 蓄電池:無	
その他				

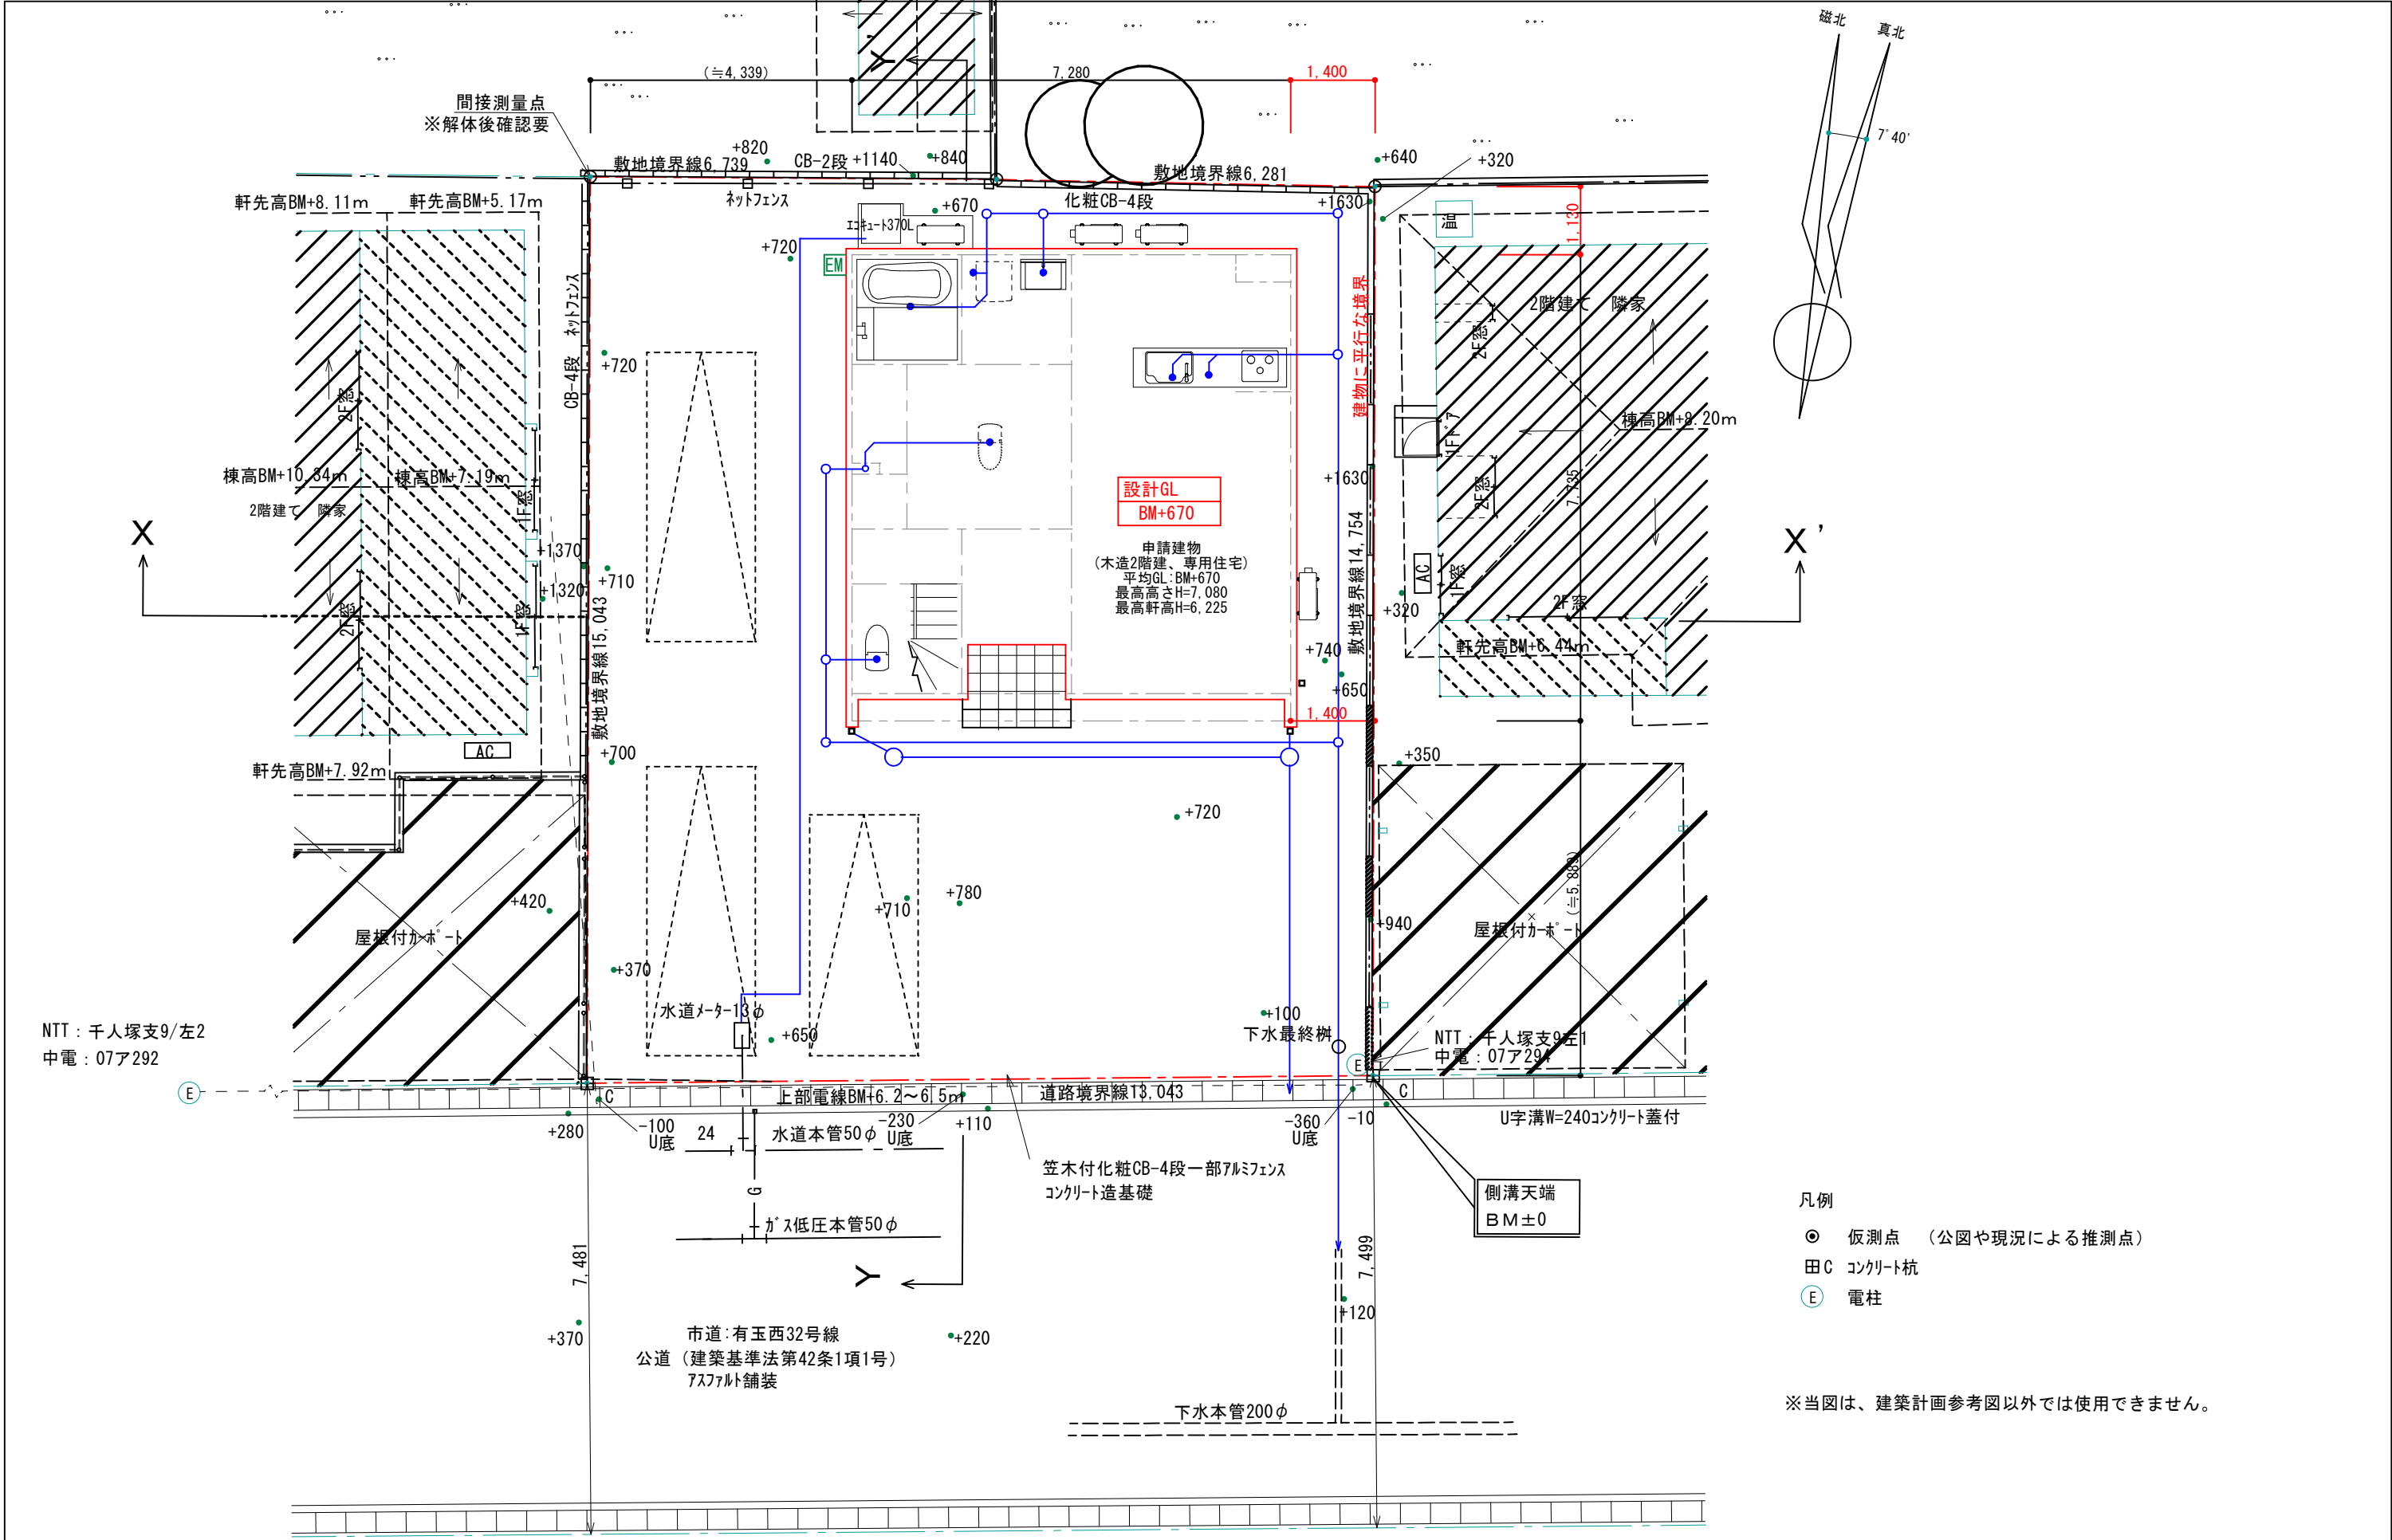

現況平面図 S=1/100

訂正	浜岡一級総合設計事務所 一級建築士事務所 静岡県知事登録第 (10) 2441 号 一級建築士 大臣登録第 365879 号 西原利昌	LIFEFUND PG HOUSE	株式会社 LIFEFUND InDesign office 一級建築士事務所 事務所登録 (2) 第7595号 一級建築士登録 第179770号 鈴木 達男 〒432-8023 静岡県浜松市中央区鴨江3丁目70番23号	年月日 2024. 7. 15	件名 PG有玉西分譲 新築工事		設計	IC	工事	図番
				縮尺 1/50	図名 配置図		倉田		青島	2-1

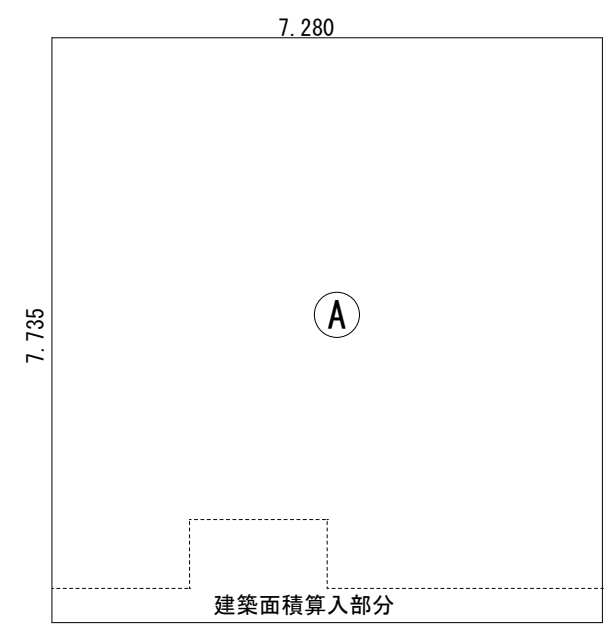


建築面積求積図 S=1/100

建築面積求積表

番号	計算式	(m)	面積 (㎡)
㊦	7.280 × 7.735		56.3108
合計			56.3108 56.31


(17.0坪)

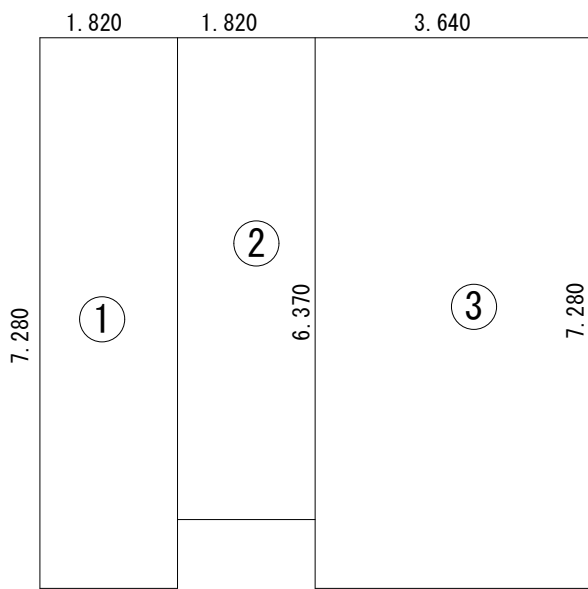

1階床面積図 S=1/100

1階床面積求積表

番号	計算式	(m)	面積 (㎡)
㊦	1.820 × 7.280		13.2496
㊦	1.820 × 6.370		11.5934
㊦	3.640 × 7.280		26.4992
合計			51.3422 51.34

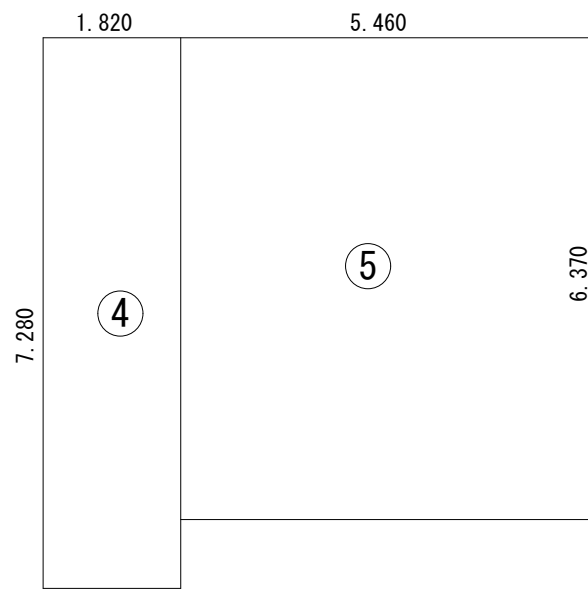


2階床面積図 S=1/100

2階床面積求積表

番号	計算式	(m)	面積 (㎡)
㊦	1.820 × 7.280		13.2496
㊦	5.460 × 6.370		34.7802
合計			48.0298 48.02

延べ床面積表

	番号	(m)	面積 (㎡)
1階床面積	㊦ ㊦ ㊦		51.34
2階床面積	㊦ ㊦		48.02
合計			99.36 (30.0坪)

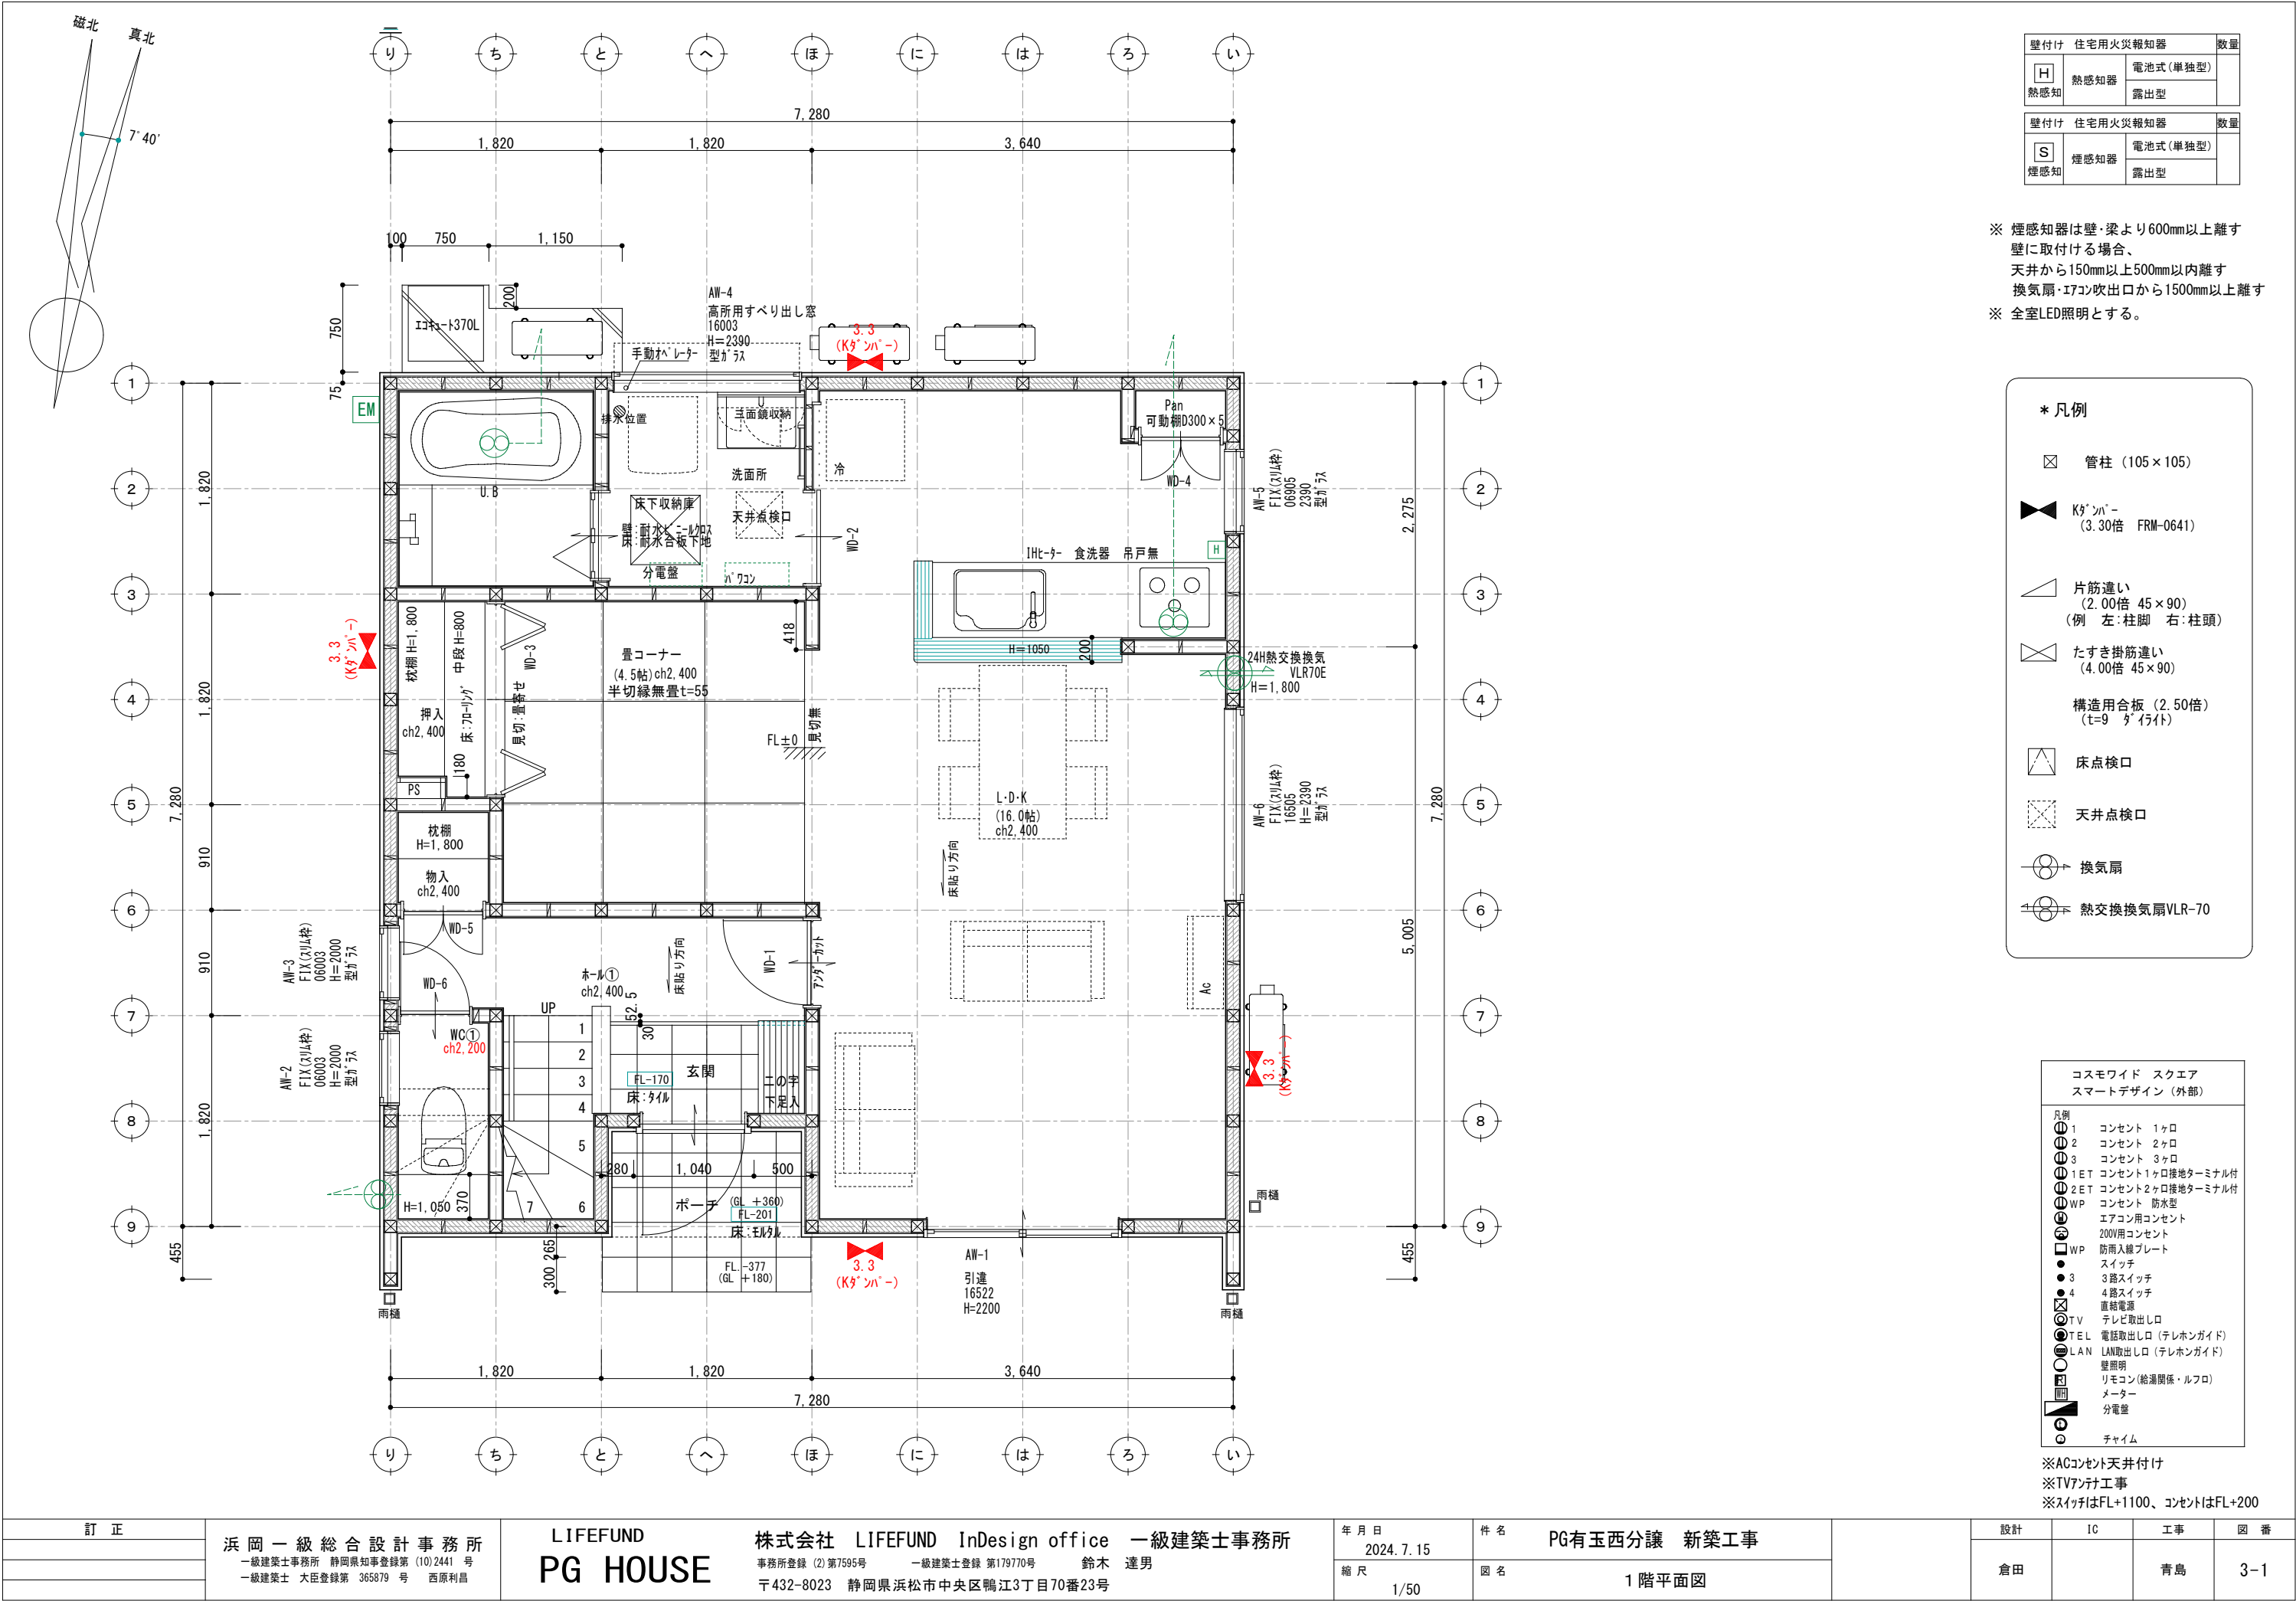

壁付け 住宅用火災報知器			数量
熱感知	H	電池式(単独型)	
		露出型	

壁付け 住宅用火災報知器			数量
煙感知	S	電池式(単独型)	
		露出型	

※ 煙感知器は壁・梁より600mm以上離す壁に取付ける場合、天井から150mm以上500mm以内離す換気扇・エアコン吹出口から1500mm以上離す

※ 全室LED照明とする。

* 凡例


- 管柱 (105×105)
- Kタ'ンパ' (3.30倍 FRM-0641)
- 片筋違い (2.00倍 45×90) (例 左:柱脚 右:柱頭)
- たすき掛筋違い (4.00倍 45×90)
- 構造用合板 (2.50倍) (t=9 タ'イラ'ト)
- 床点検口
- 天井点検口
- 換気扇
- 熱交換換気扇VLR-70

コスモワイド スクエア スマートデザイン (外部)		
凡例	1	コンセント 1ヶロ
2	コンセント 2ヶロ	
3	コンセント 3ヶロ	
1ET	コンセント1ヶロ接地ターミナル付	
2ET	コンセント2ヶロ接地ターミナル付	
WP	コンセント 防水型	
WP	エアコン用コンセント 200V用コンセント	
WP	防雨入線プレート	
●	スイッチ	
●3	3路スイッチ	
●4	4路スイッチ	
⊠	直結電源	
TV	テレビ取出口	
TEL	電話取出口 (テレホンガイド)	
LAN	LAN取出口 (テレホンガイド)	
●	壁照明	
リモ	リモコン (給湯関係・ルフロ)	
メー	メーター	
分電	分電盤	
チャ	チャイム	


※ACコンセント天井付け

※TVアンテナ工事


※スイッチはFL+1100、コンセントはFL+200

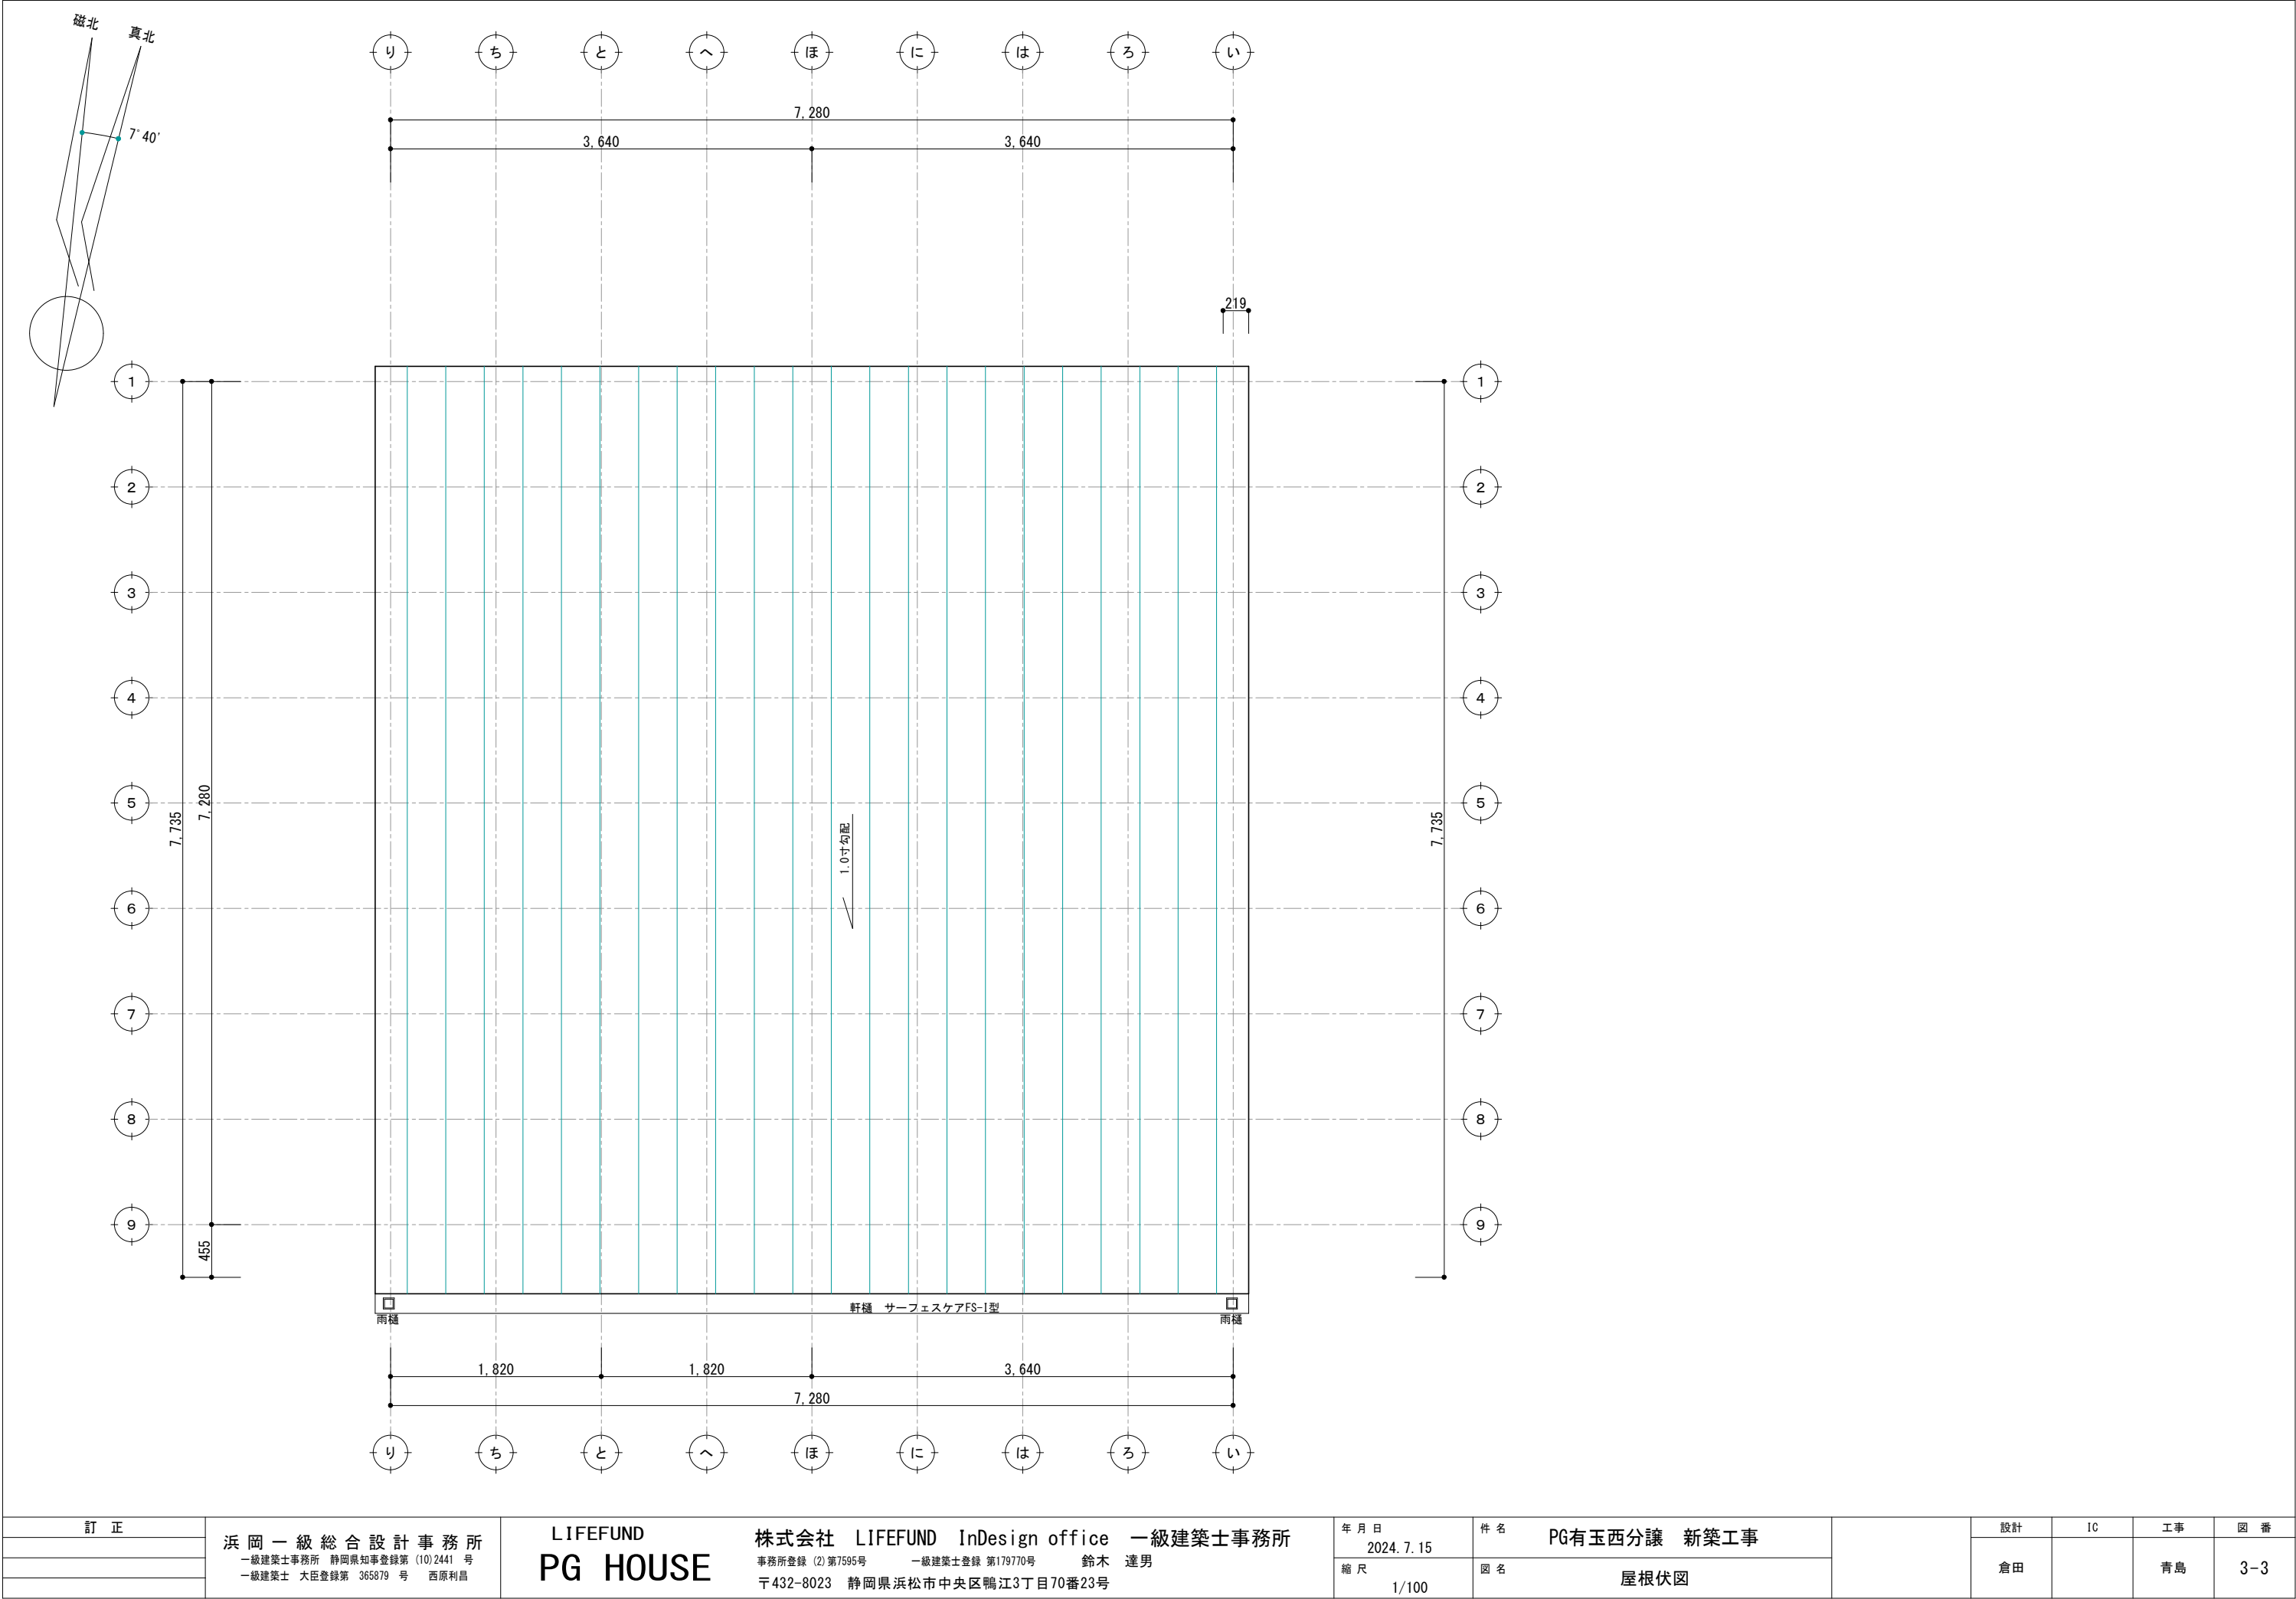


訂正	浜岡一級総合設計事務所 一級建築士事務所 静岡県知事登録第 (10)2441 号 一級建築士 大臣登録第 365879 号 西原利昌	LIFEFUND PG HOUSE	株式会社 LIFEFUND InDesign office 一級建築士事務所 事務所登録 (2) 第7595号 一級建築士登録 第179770号 鈴木 達男 〒432-8023 静岡県浜松市中央区鴨江3丁目70番23号	年月日	件名		設計	IC	工事	図番
				2024. 7. 15	PG有玉西分譲 新築工事		倉田		青島	3-3
				縮尺	図名					
				1/100	屋根伏図					

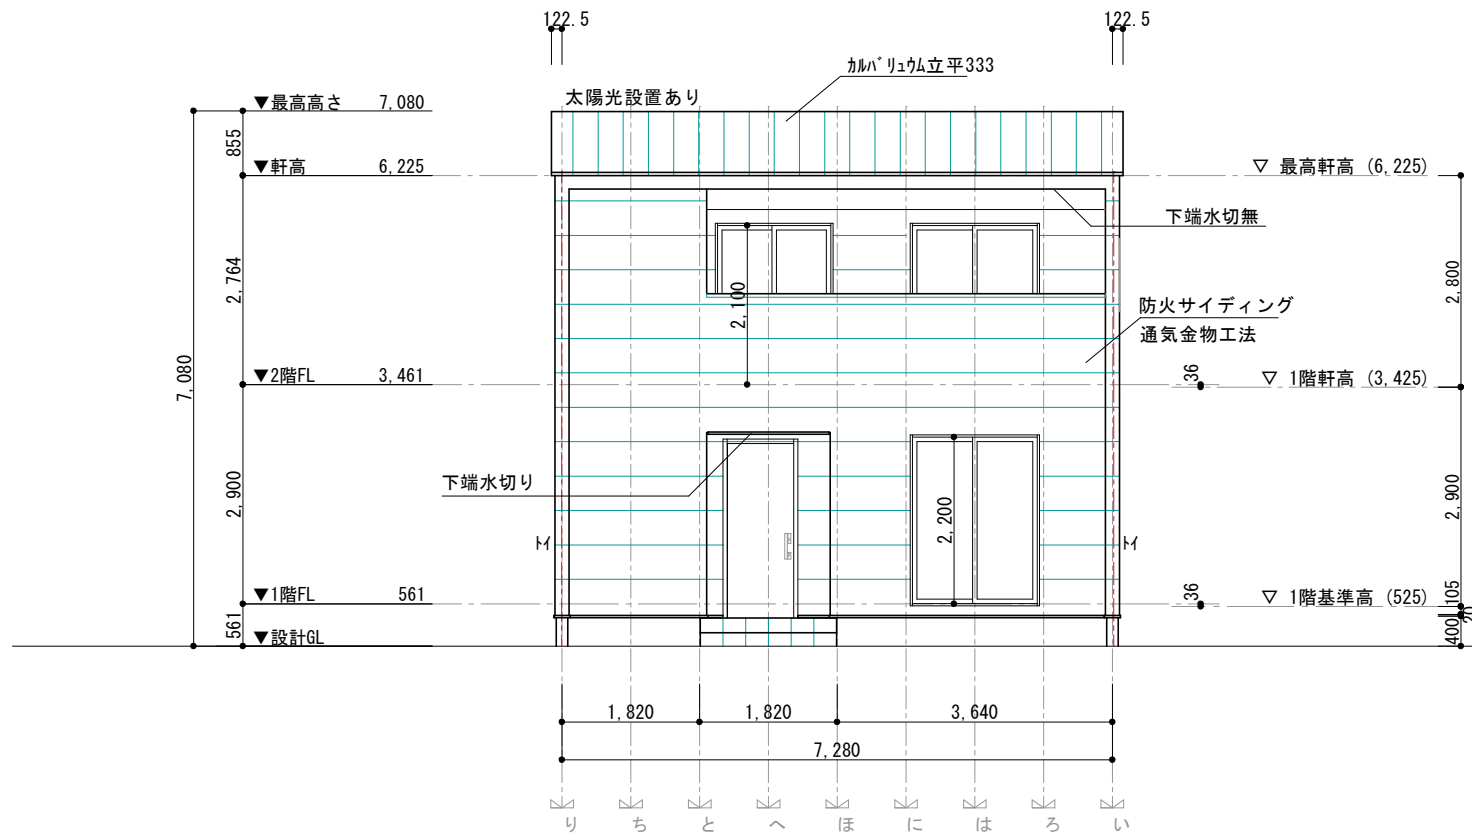


南側立面図 S=1/100

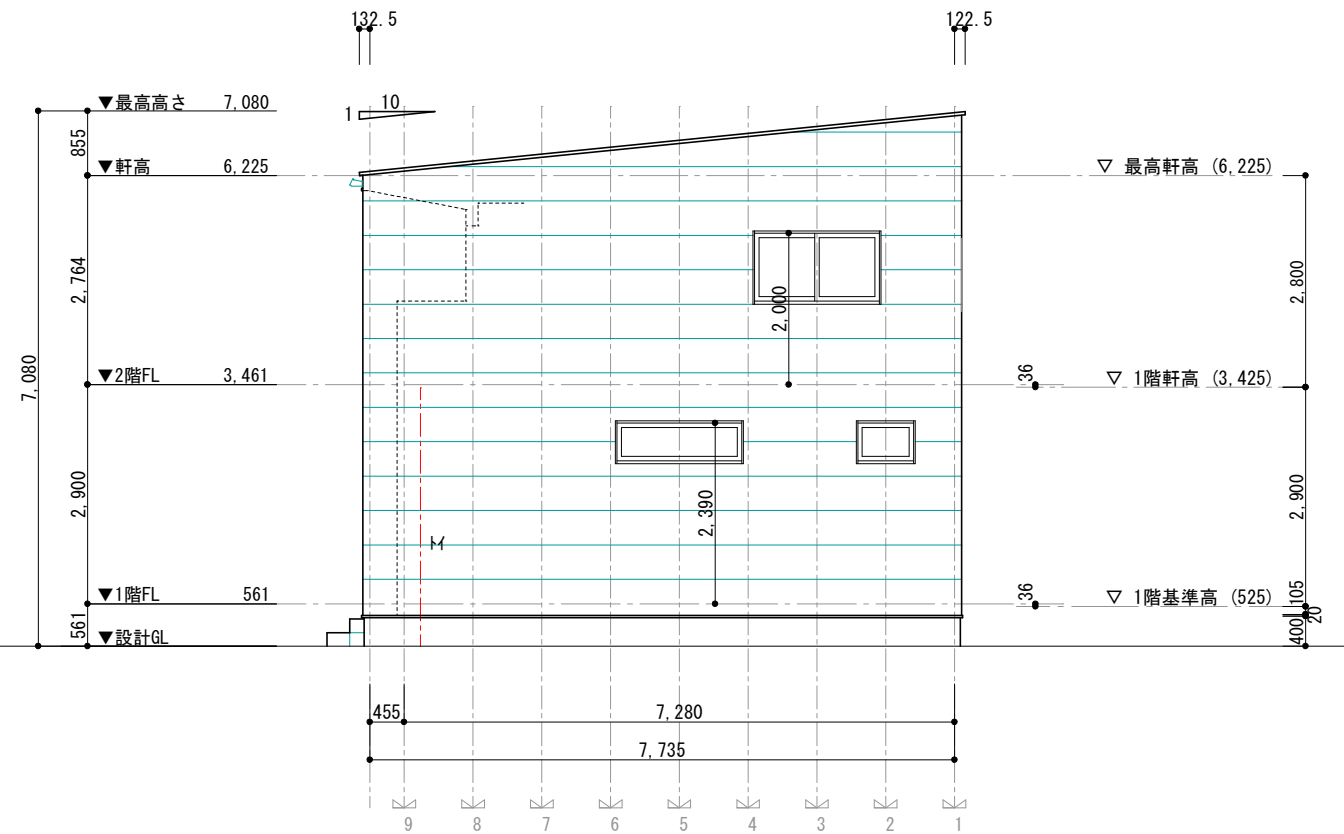

東側立面図 S=1/100

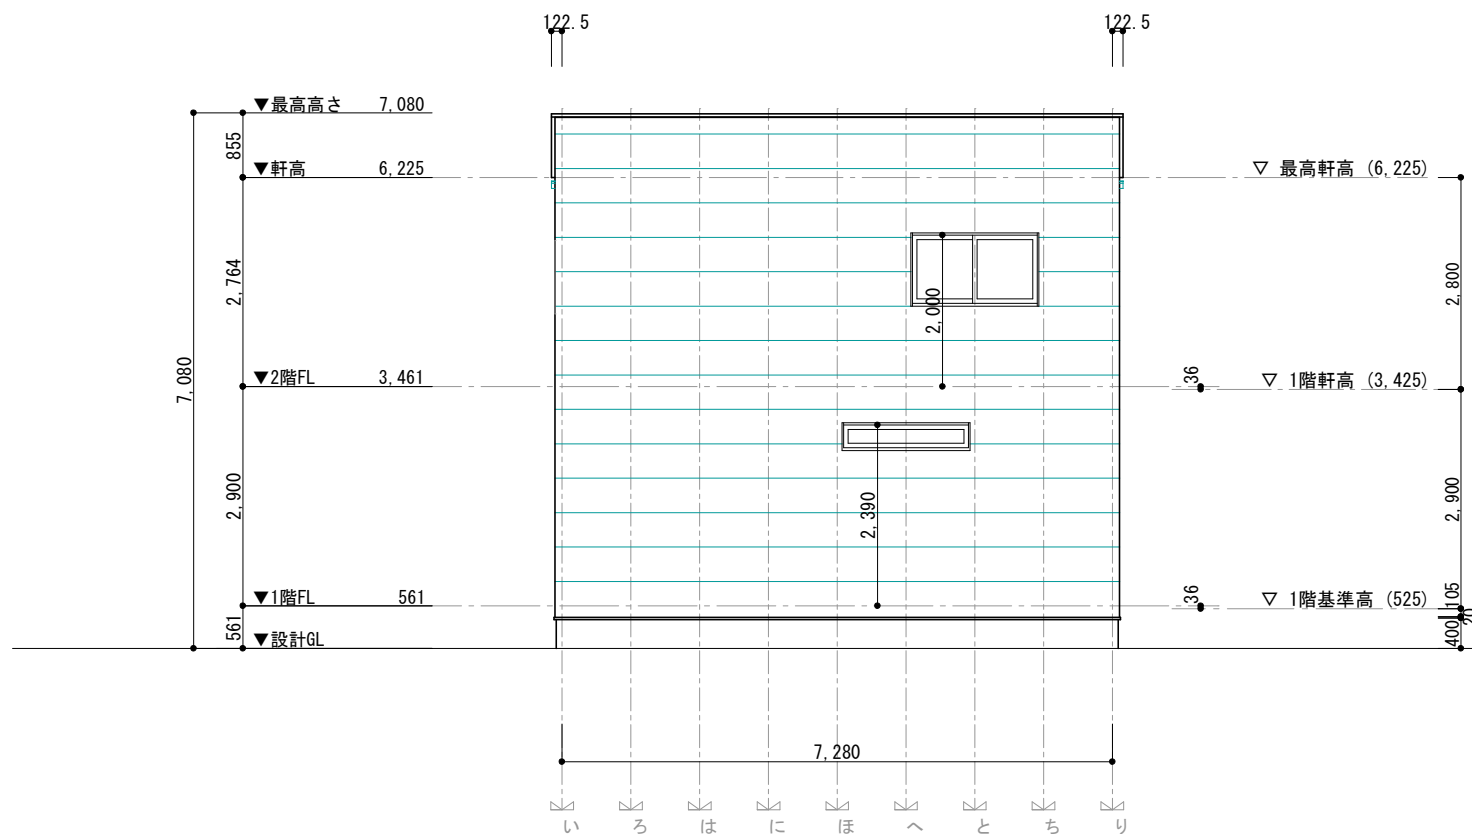


北側立面図 S=1/100

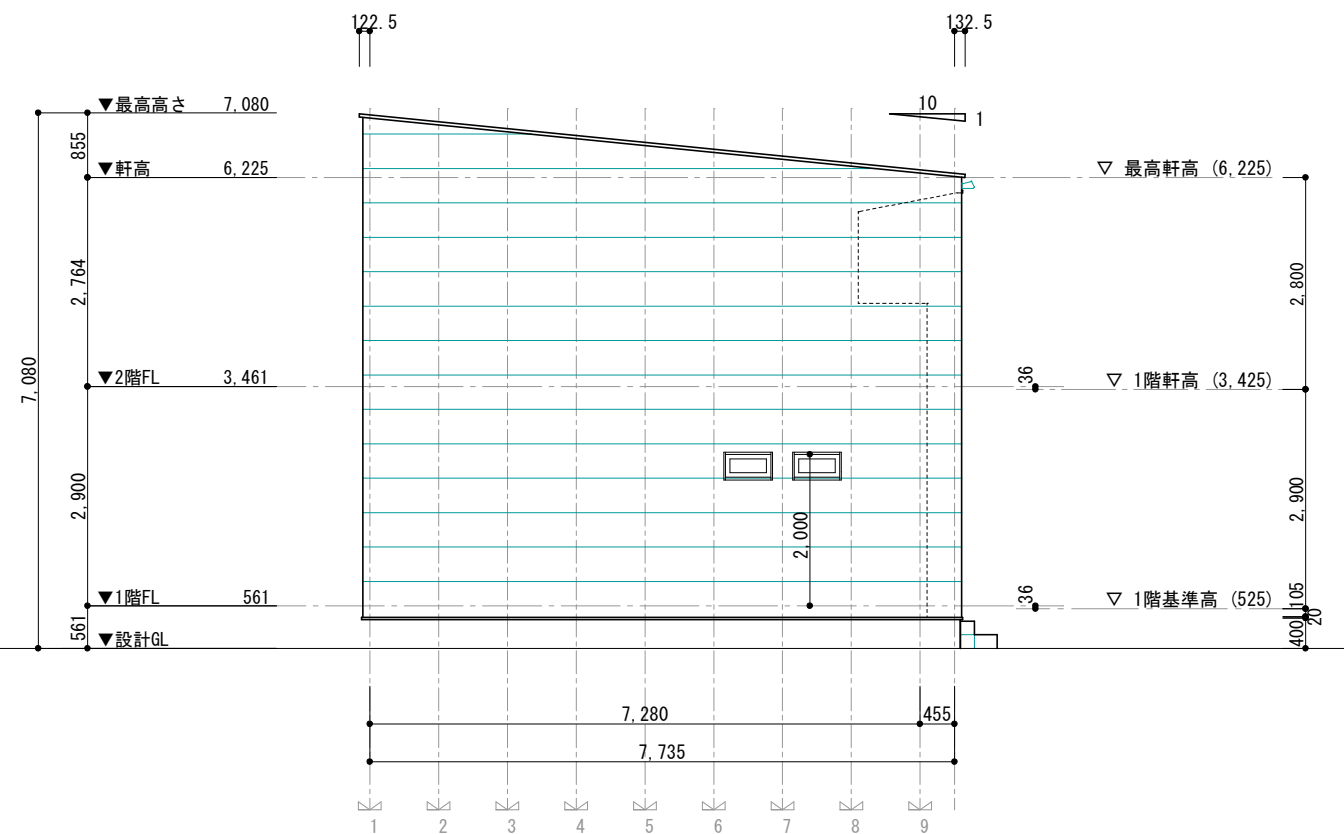


西側立面図 S=1/100


訂 正	浜 岡 一 級 総 合 設 計 事 務 所 一級建築士事務所 静岡県知事登録第 (10) 2441 号 一級建築士 大臣登録第 365879 号 西原利昌	LIFEFUND PG HOUSE	株式会社 LIFEFUND InDesign office 一級建築士事務所 事務所登録 (2) 第7595号 一級建築士登録 第179770号 鈴木 達男 〒432-8023 静岡県浜松市中央区鴨江3丁目70番23号	年 月 日	件 名		設計	IC	工事	図 番
				2024. 7. 15	PG有玉西分譲 新築工事					
				縮 尺	図 名					
				1/100	立面図					

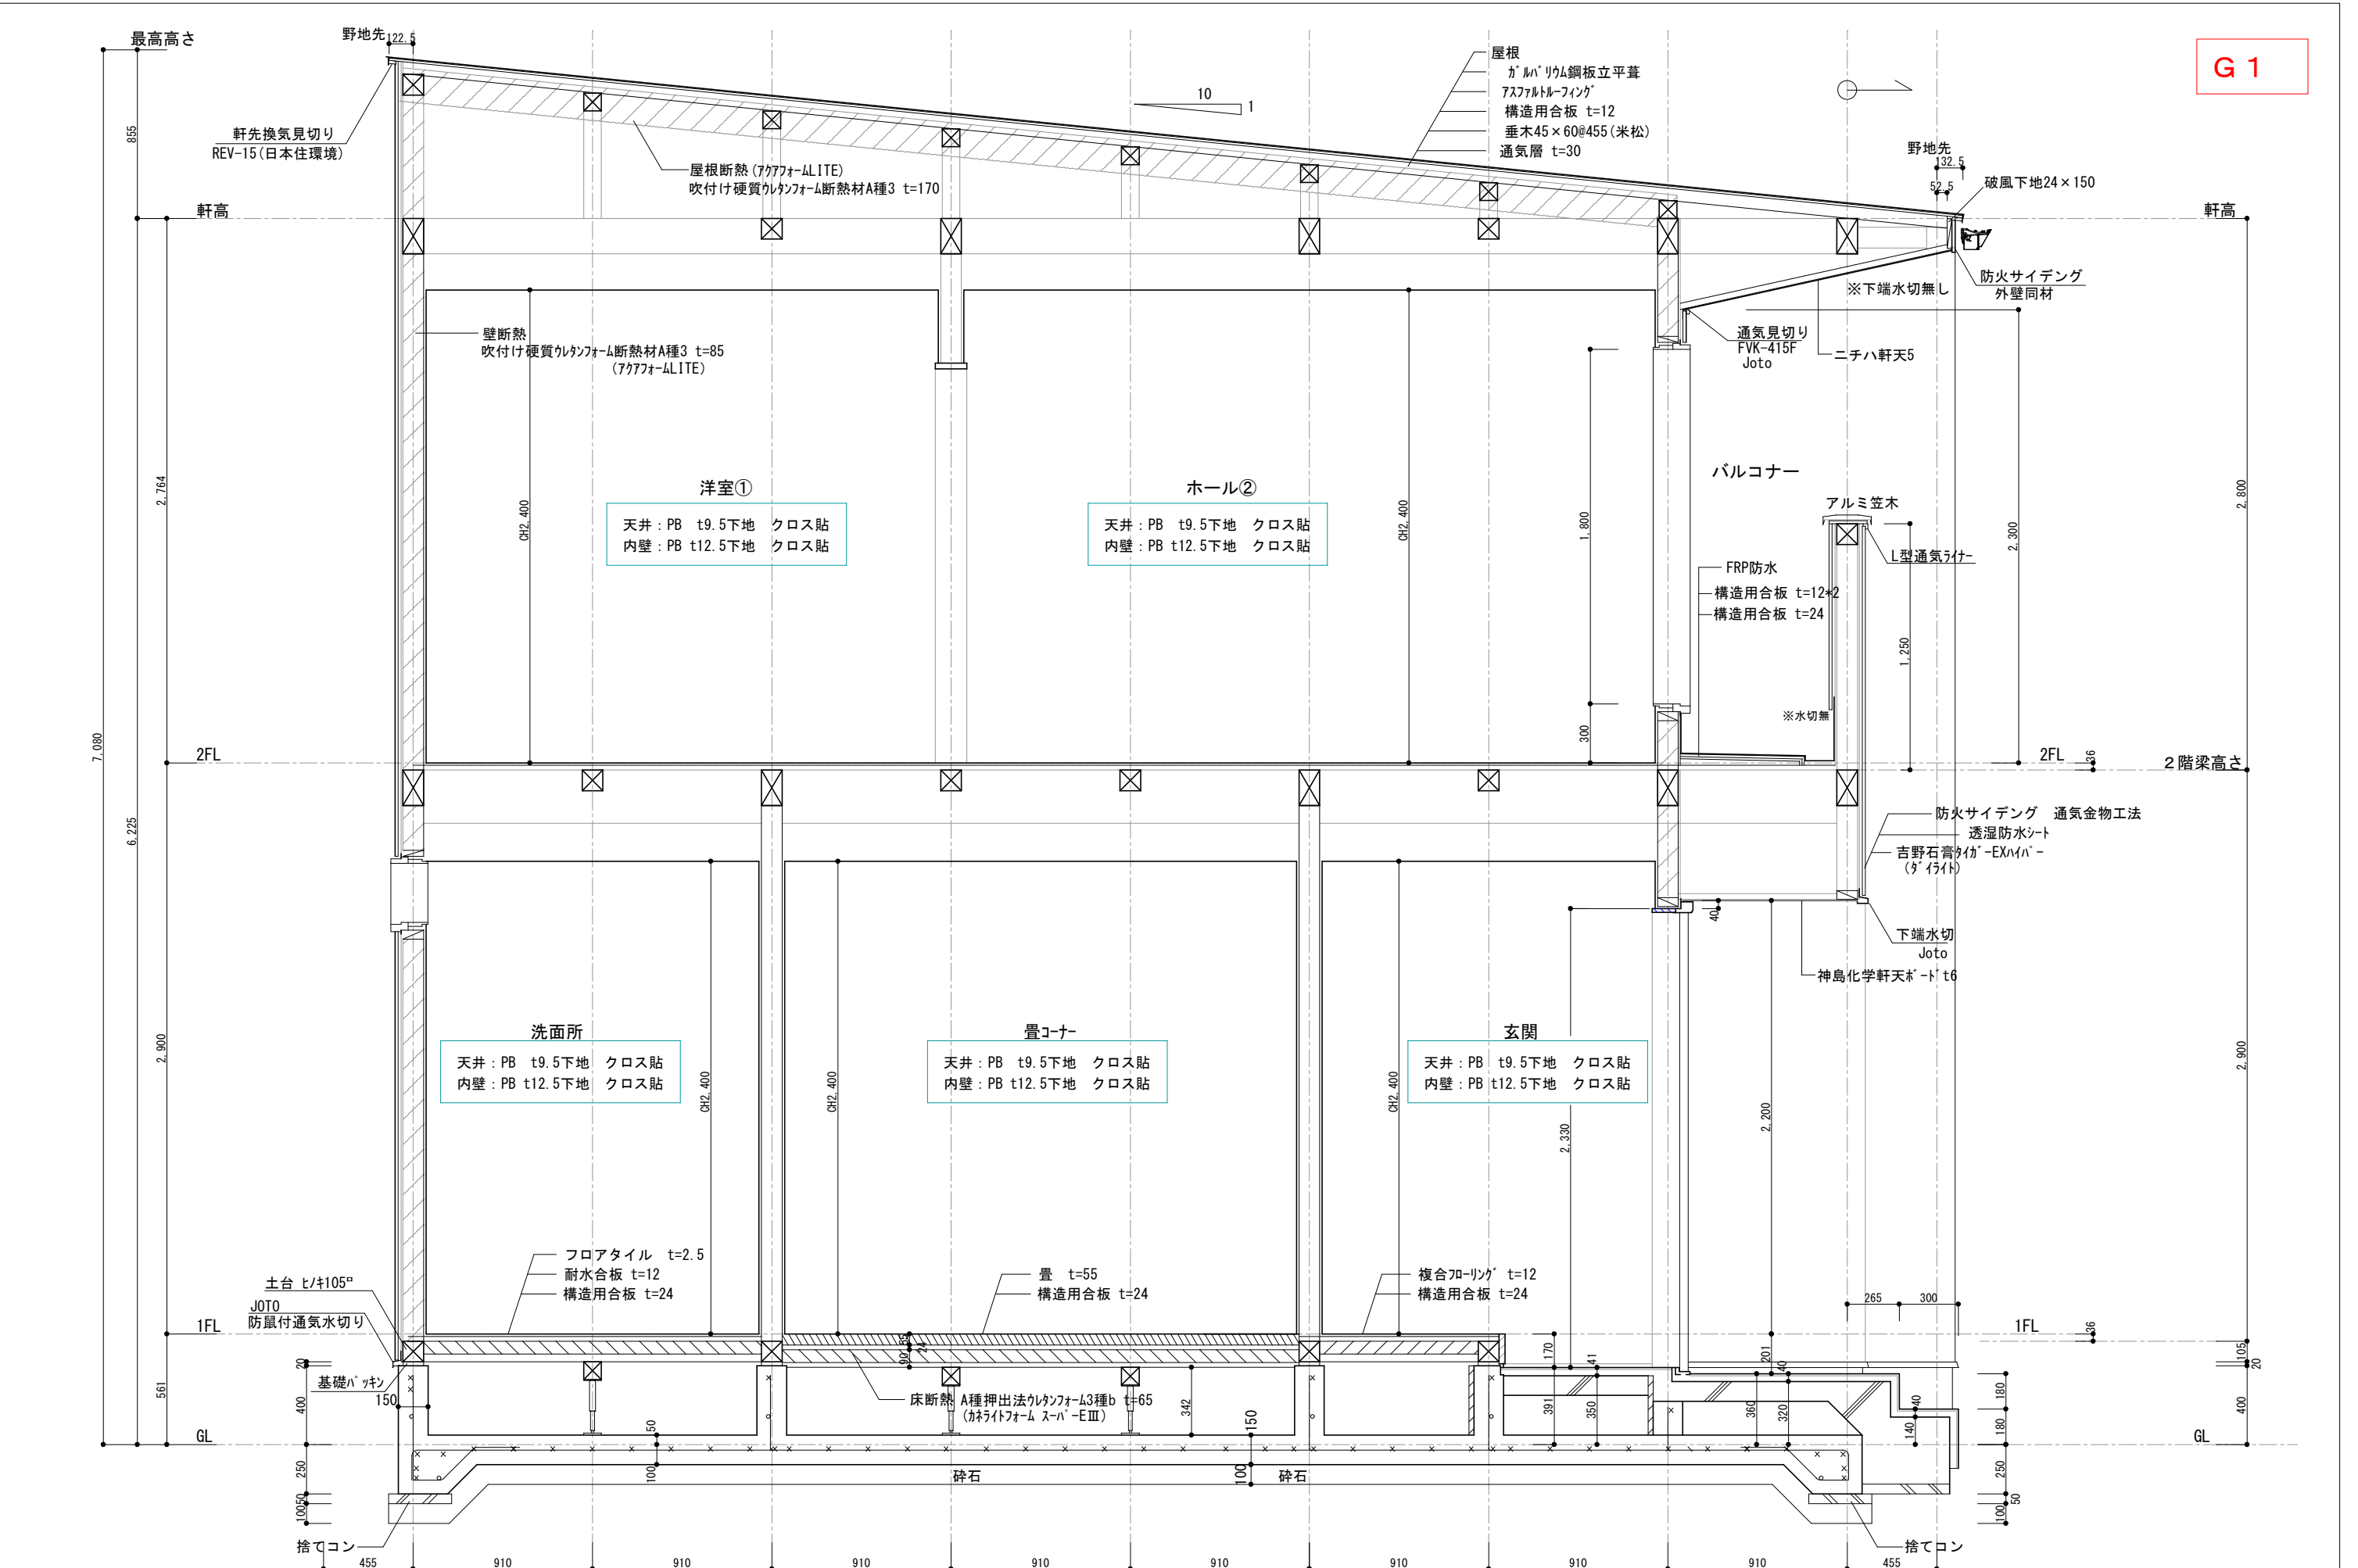


訂正	浜岡一級総合設計事務所 一級建築士事務所 静岡県知事登録第 (10)2441 号 一級建築士 大臣登録第 365879 号 西原利昌	LIFEFUND PG HOUSE	株式会社 LIFEFUND InDesign office 一級建築士事務所 事務所登録 (2)第7595号 一級建築士登録 第179770号 鈴木 達男 〒432-8023 静岡県浜松市中央区鴨江3丁目70番23号	年月日 2024. 7. 15	件名 PG有玉西 分譲 新築工事	設計 倉田	IC	工事 青島	図番 5-1
				縮尺 1/30	図名 矩計図				

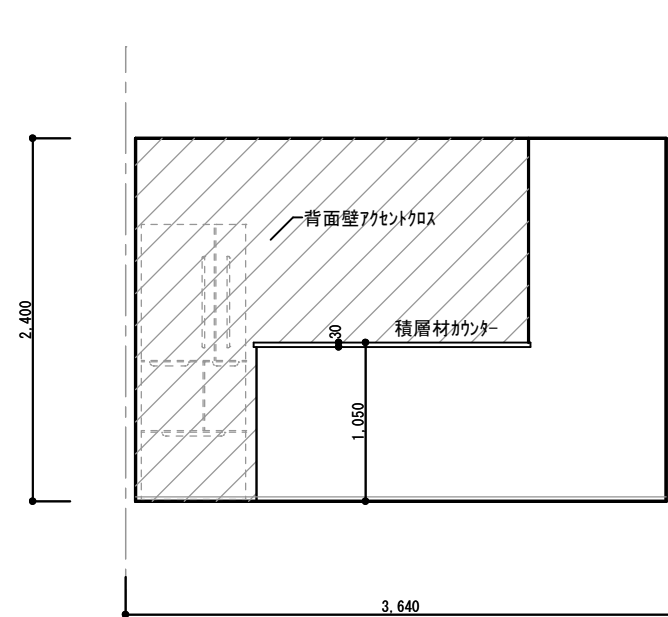


LDK 南面

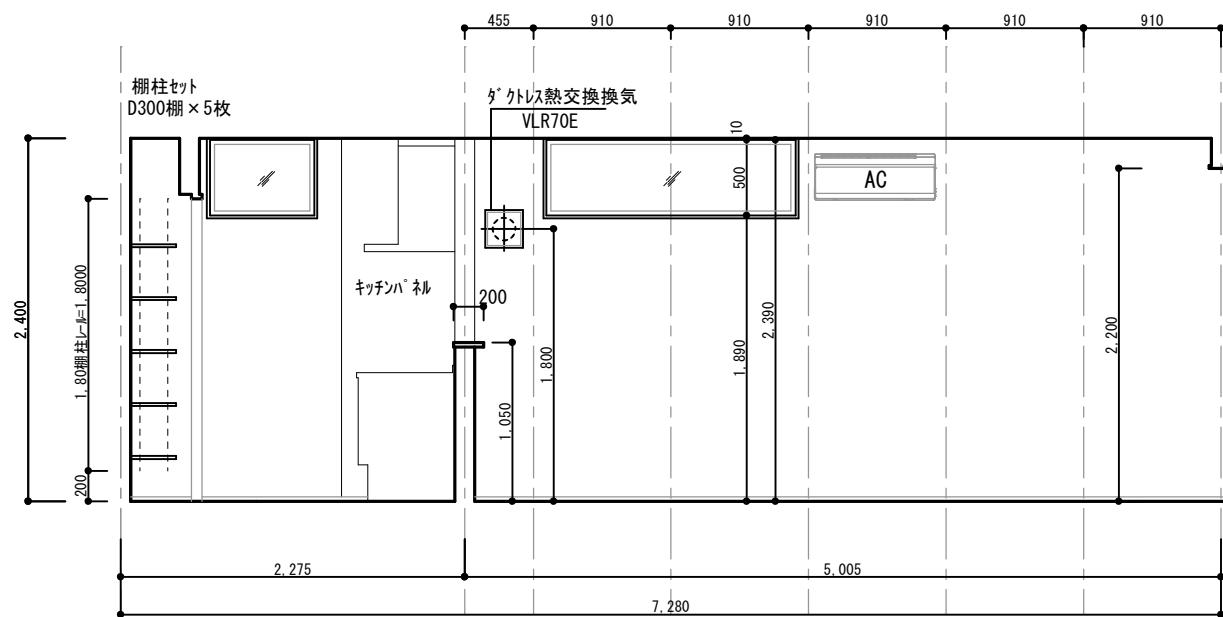


LDK 東面

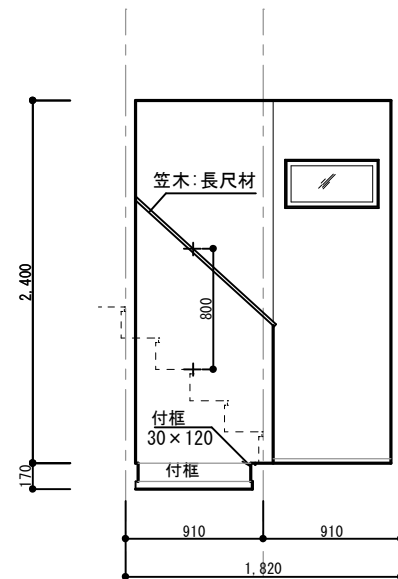


玄関 西面

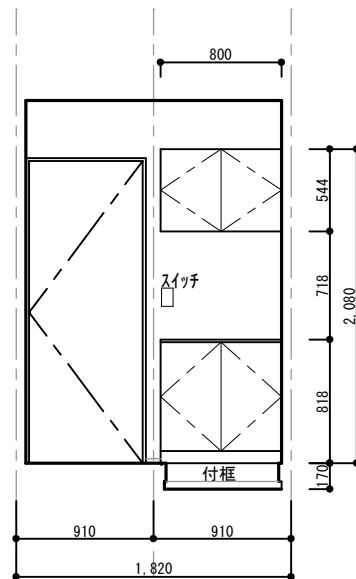


玄関 東面

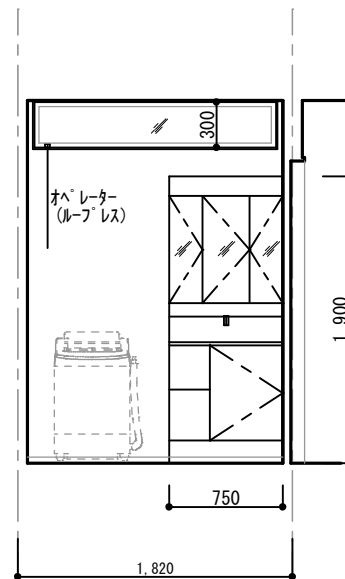


洗面所 北面

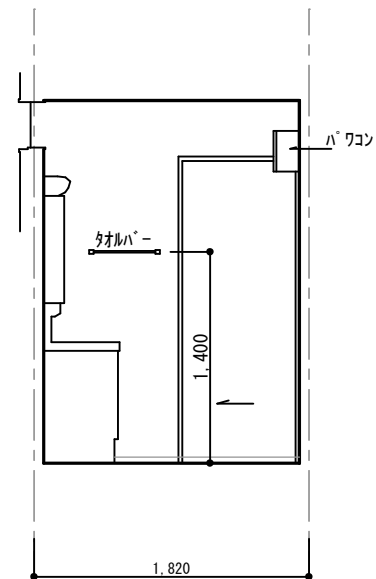


洗面所 東面

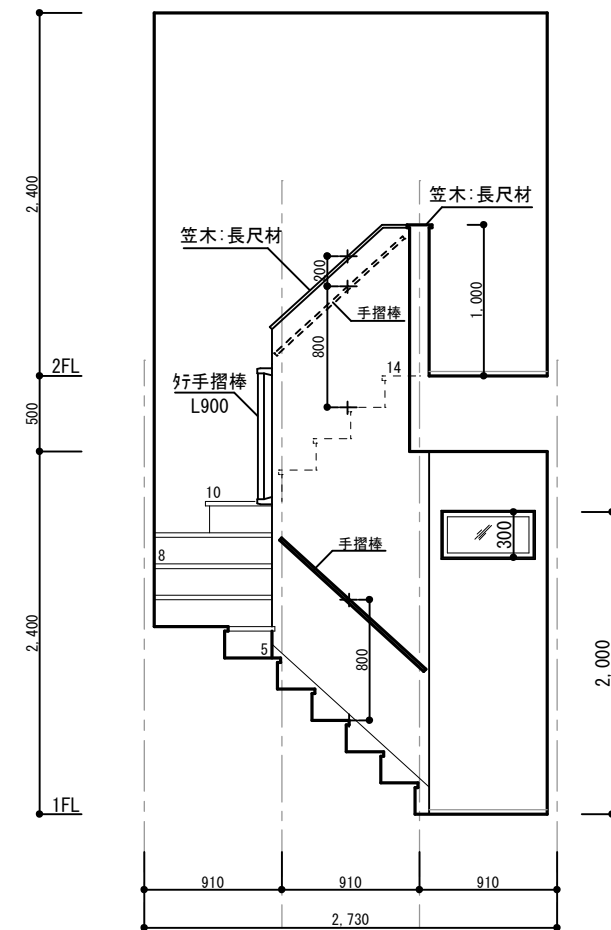


階段 西面

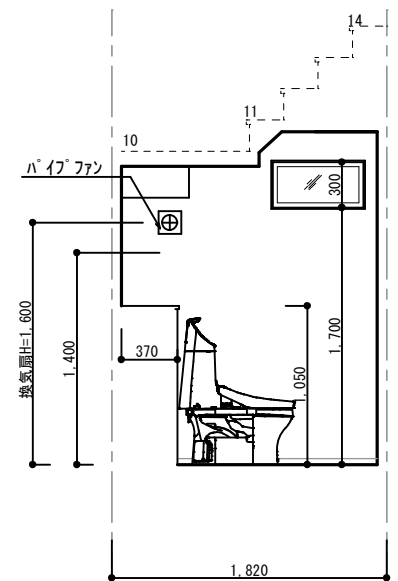


WC② 西面

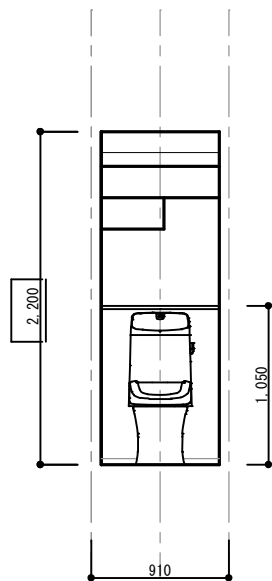


WC① 南面

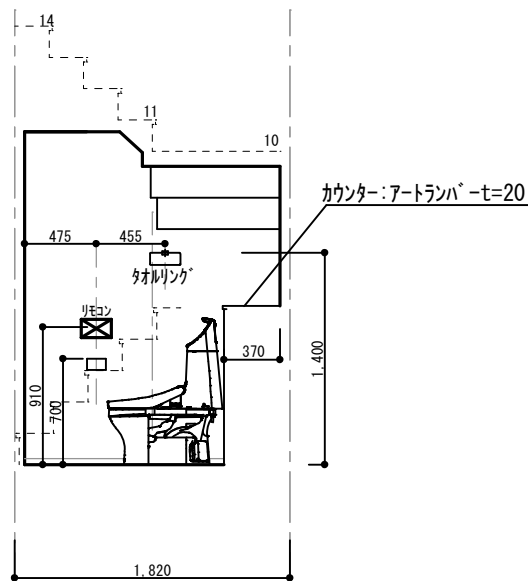

WC② 東面

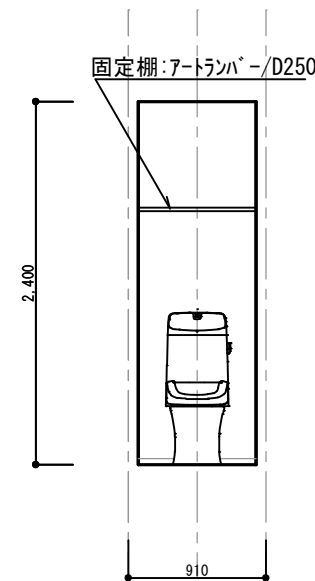



WC② 北面

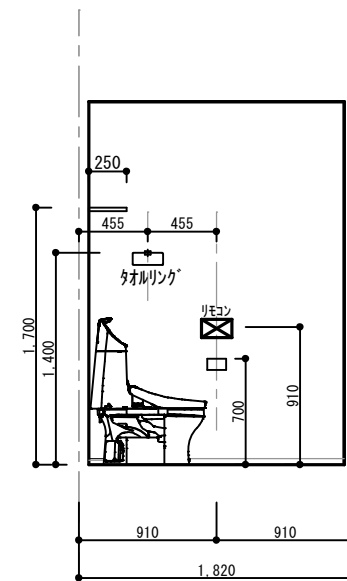


WC② 東面

訂正	浜岡 一級総合設計事務所 一級建築士事務所 静岡県知事登録第 (10)2441 号 一級建築士 大臣登録第 365879 号 西原利晶	LIFEFUND PG HOUSE	株式会社 LIFEFUND InDesign office 一級建築士事務所 事務所登録 (2) 第7595号 一級建築士登録 第179770号 鈴木 達男 〒432-8023 静岡県浜松市中央区鴨江3丁目70番23号	年月日 2024. 07. 15	件名 PG有玉西分譲 新築工事		設計	IC	工事	図番
				縮尺 1/30	図名 展開図 (1)		倉田		青島	6-1

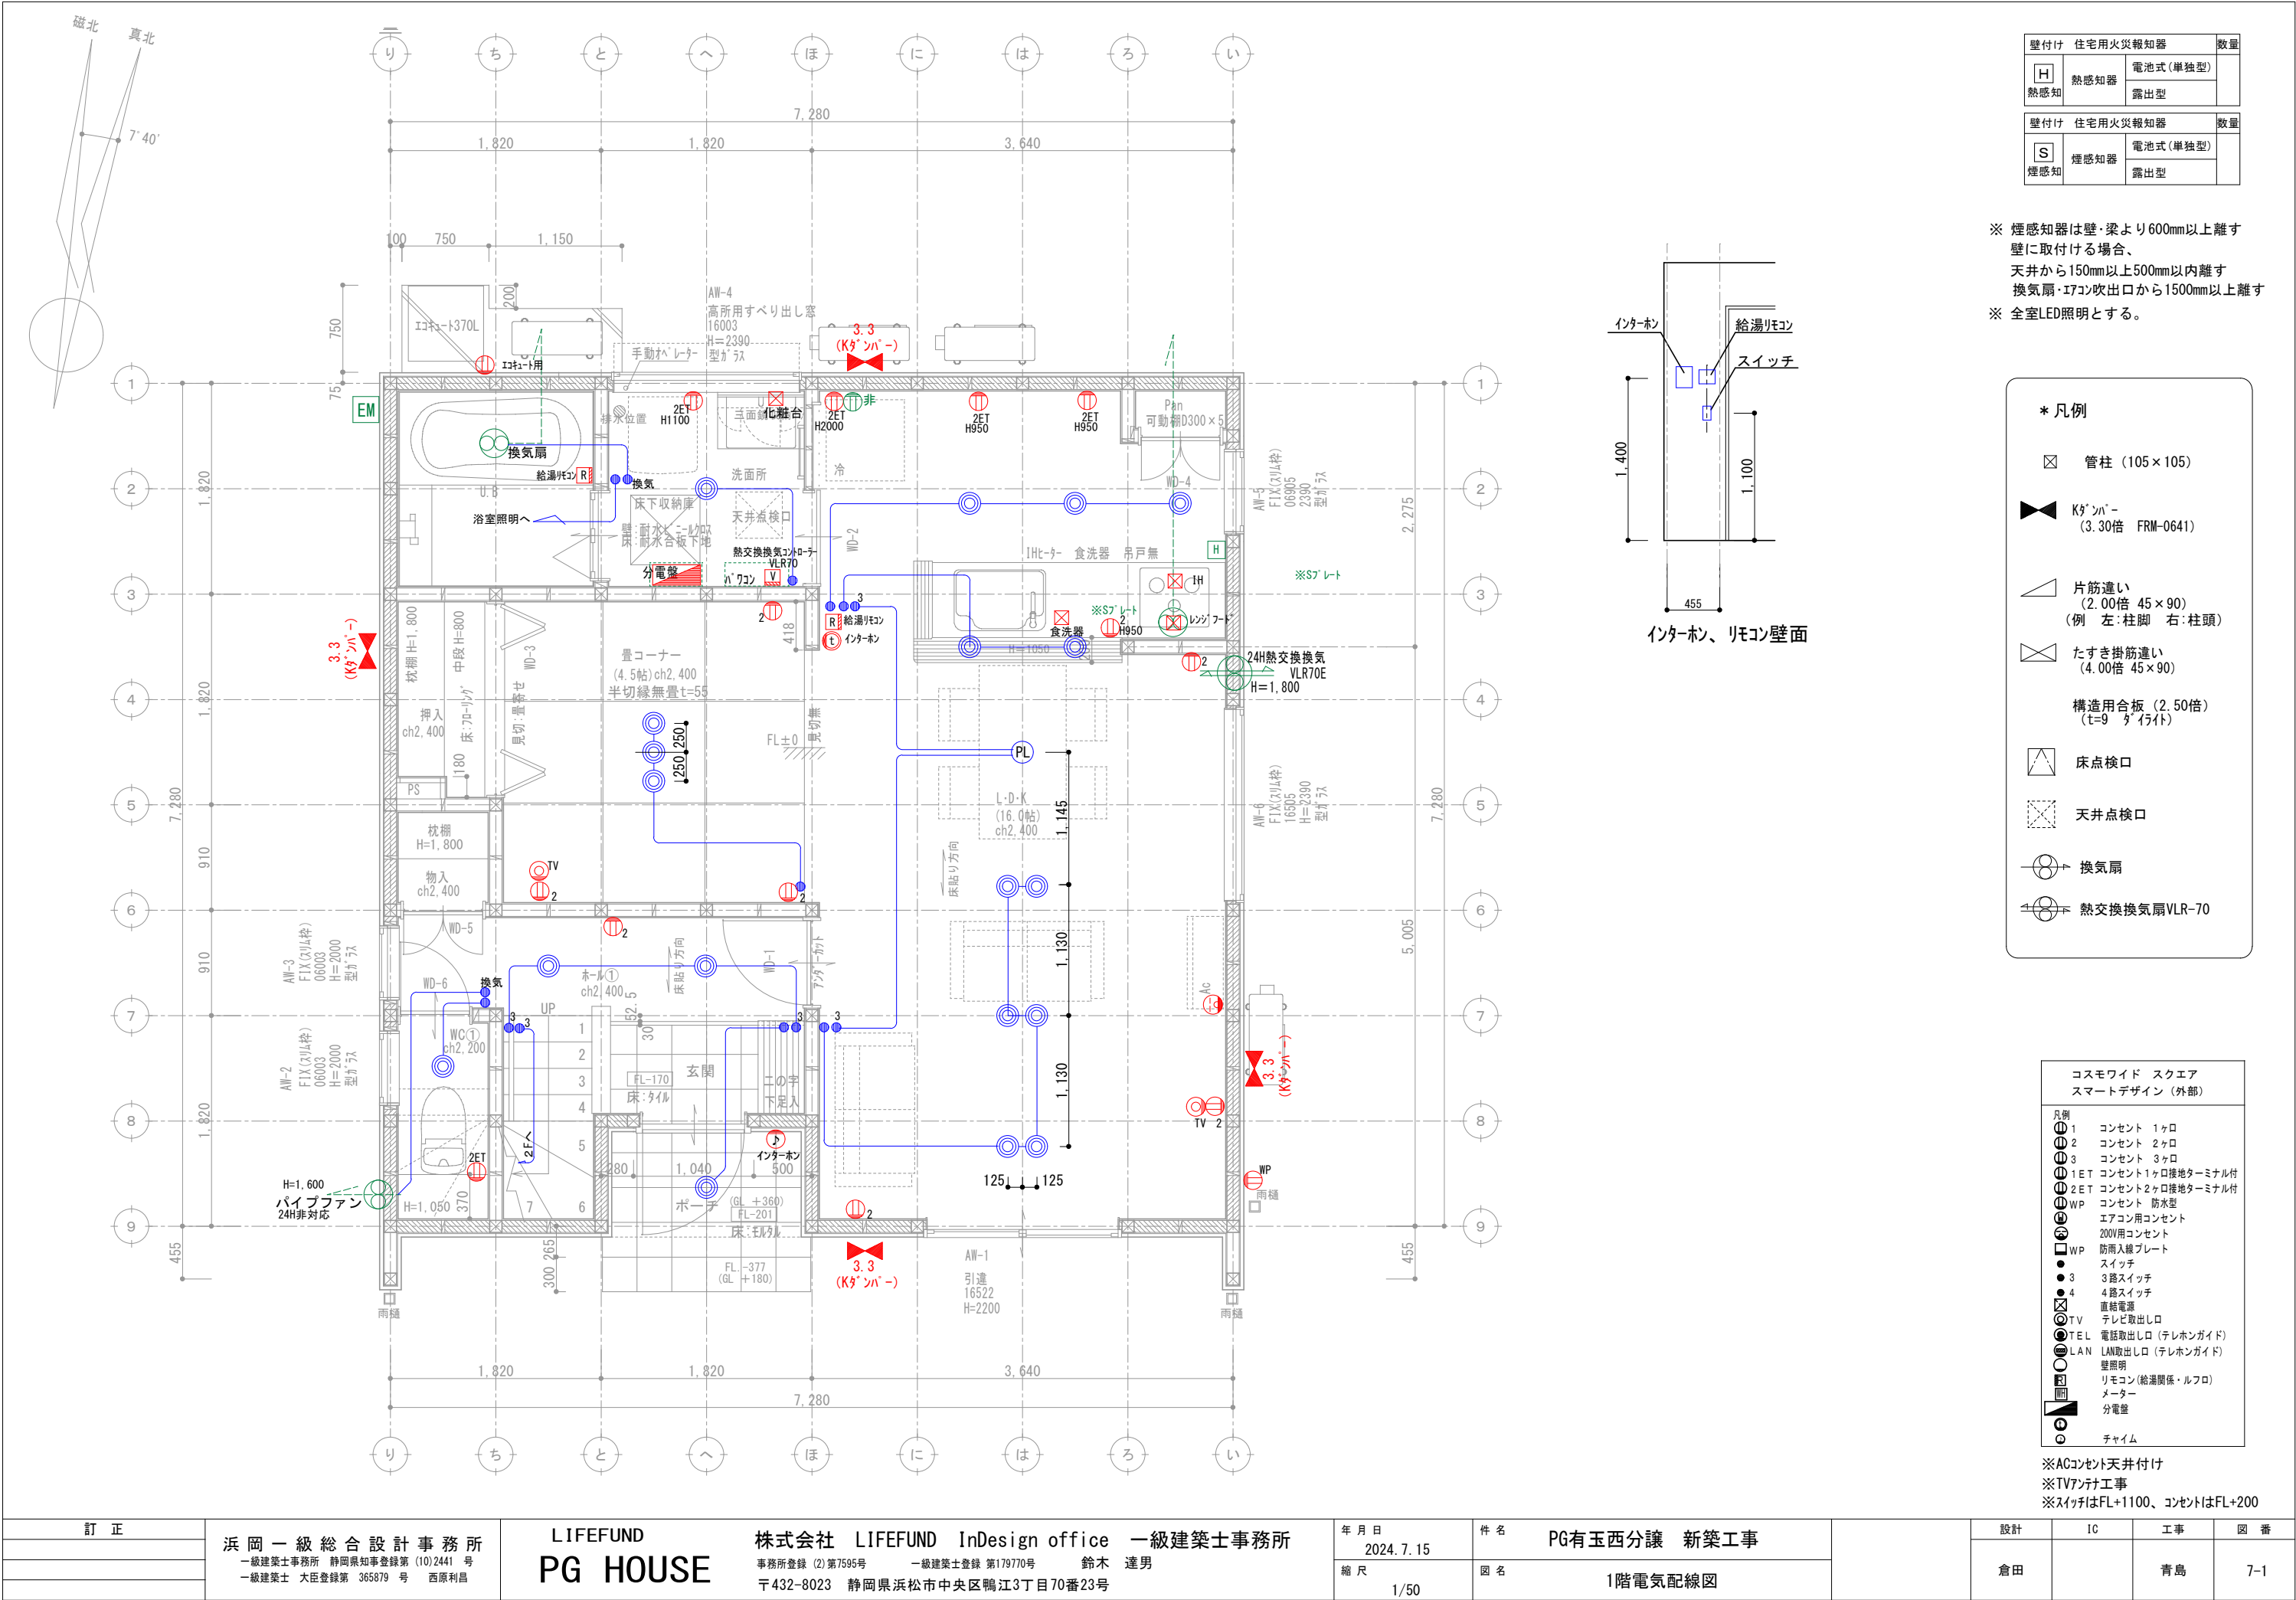

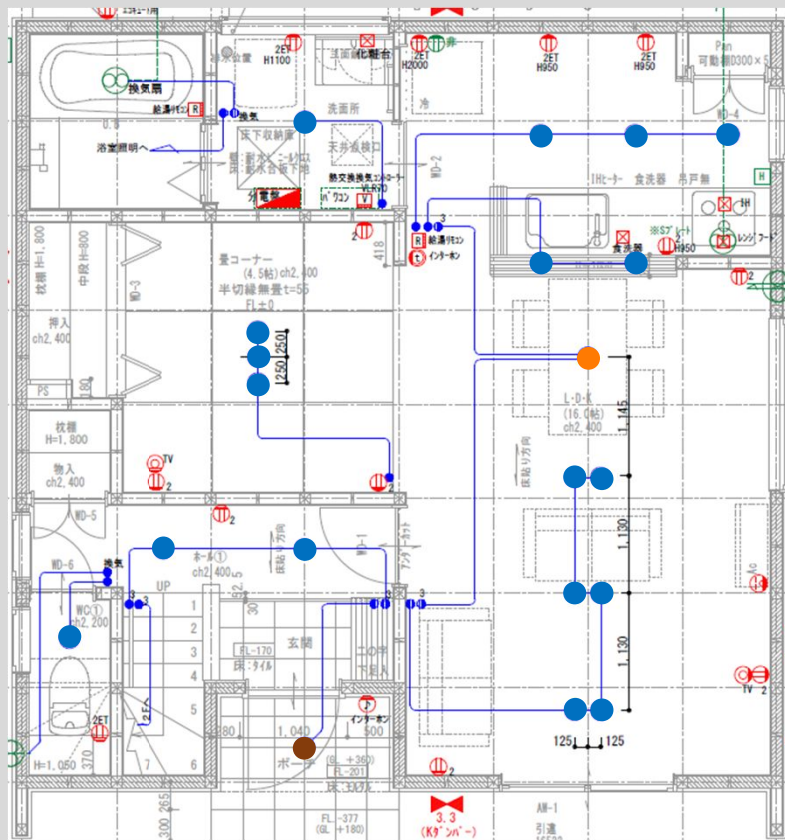


1 階

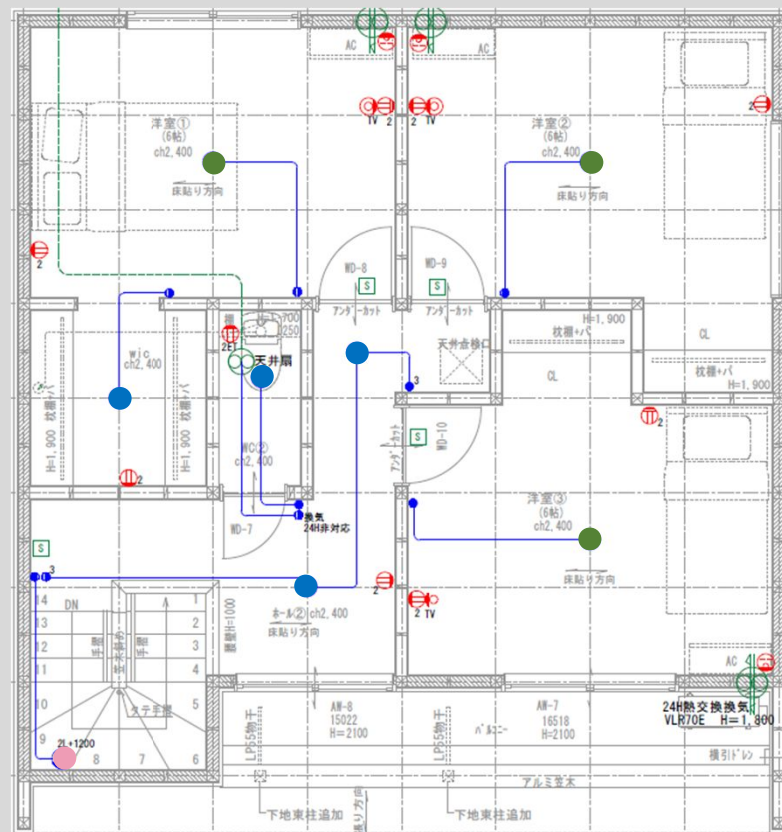

2 階

内部：コスモワイド スクエア(Panasonic)

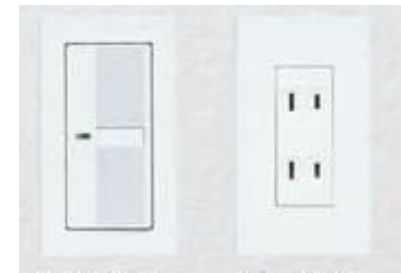

ドアホン：VL-SZ30KL
(Panasonic)



外部：スマートデザインシリーズ (Panasonic)

表情豊かな住まいをつくり出すスマートデザインシリーズ。



ポーチ灯

● × 1

DDL-4496YW



基本照明ダウンライト

● × 22

DDL6102AW



ダイニングペンダント灯

● × 1

DPN41973



洋室①②③ 灯

● × 3

DCL40507




階段灯












● × 1

DBK41544Y



2024.07.15

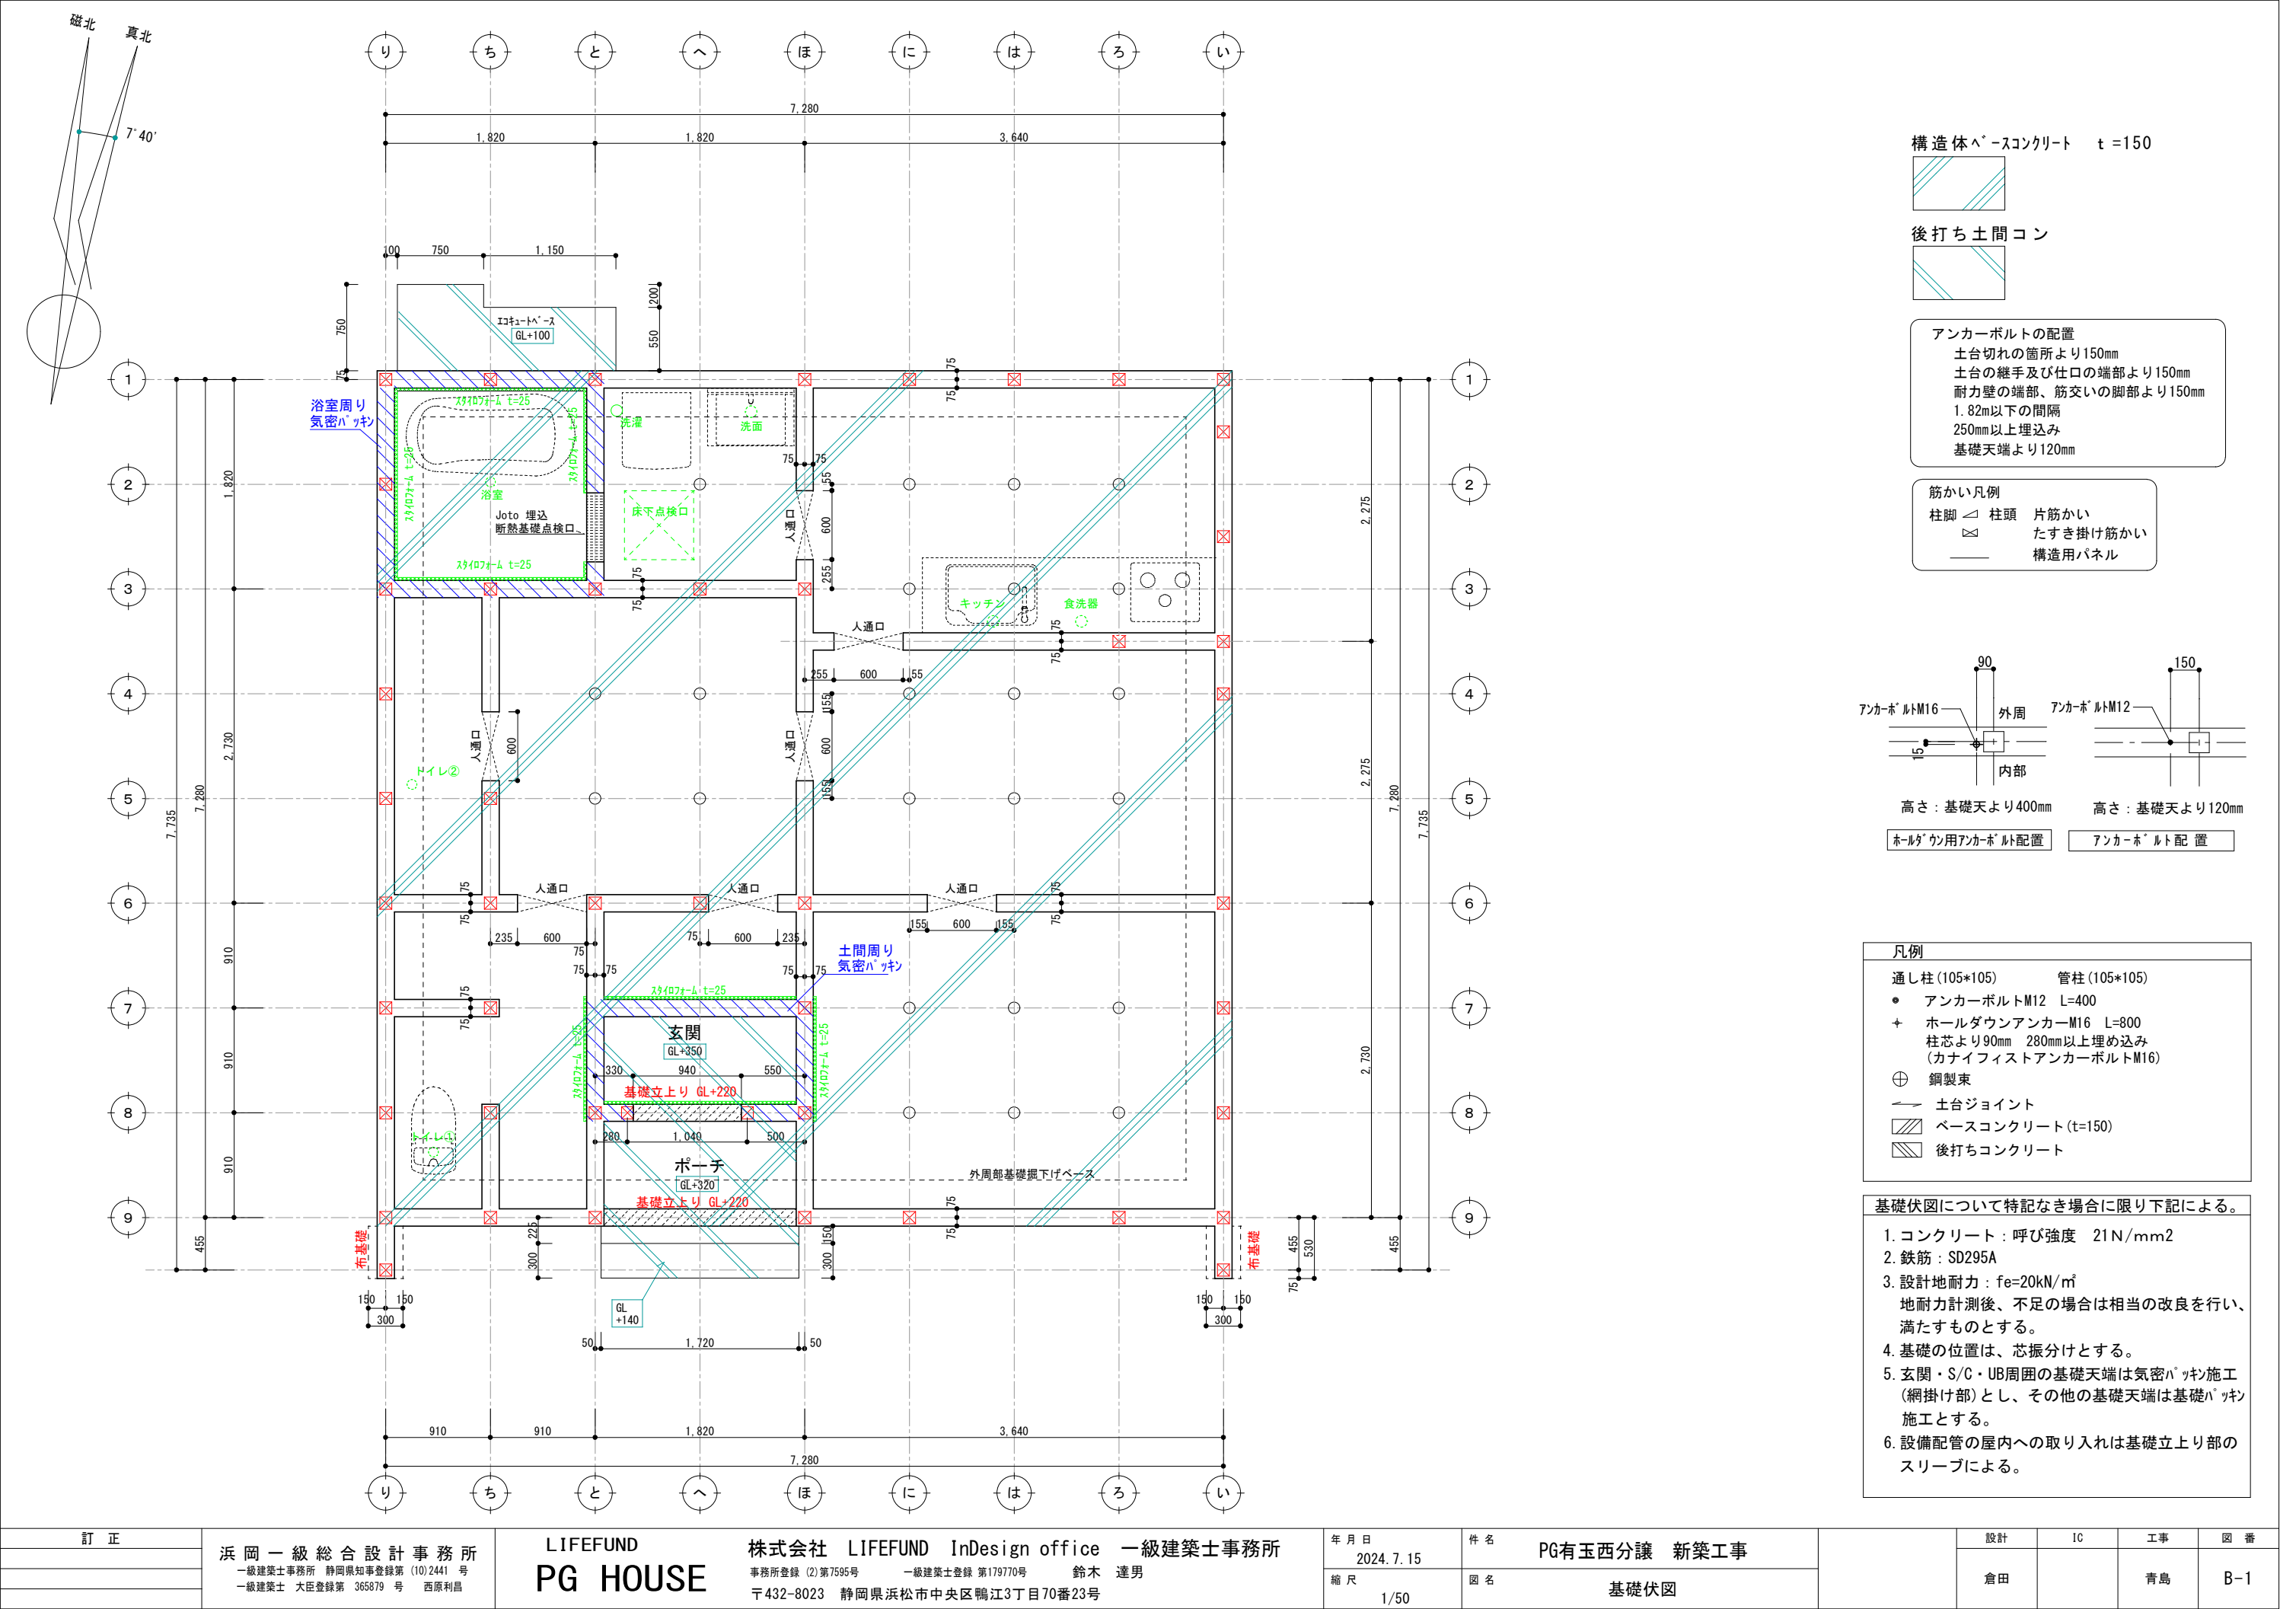

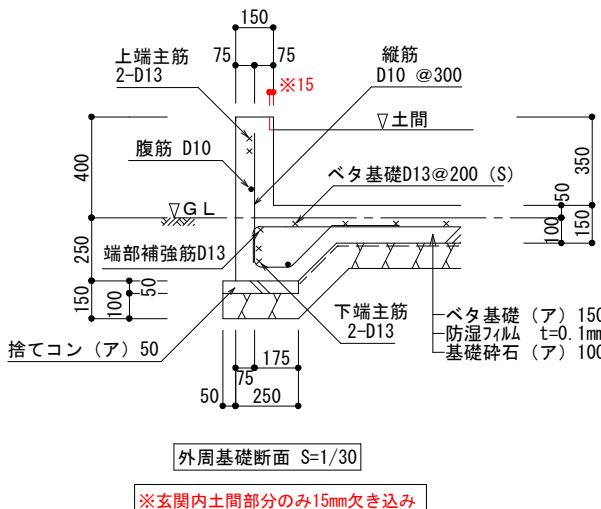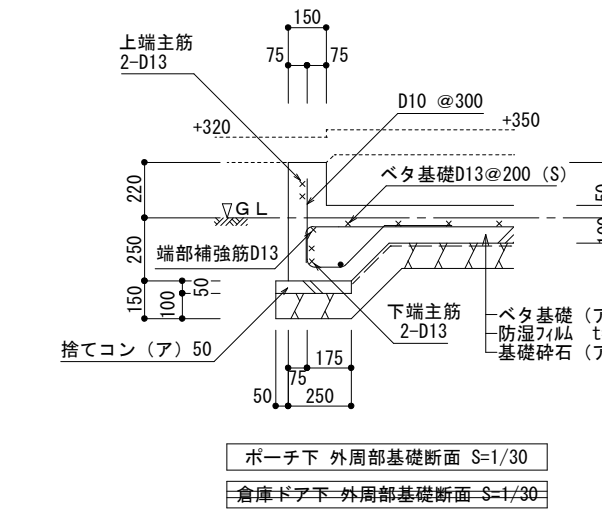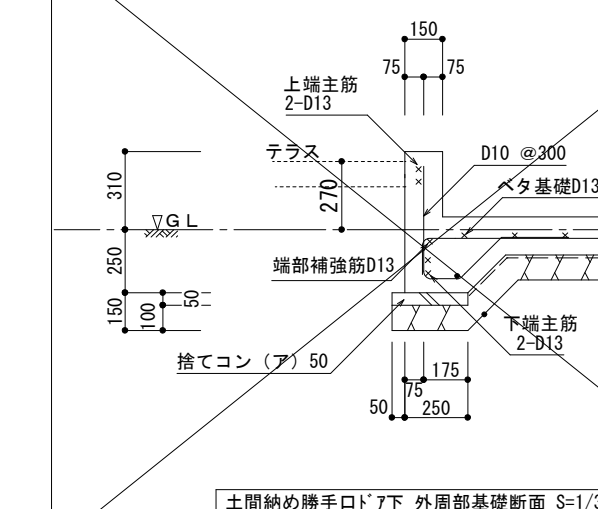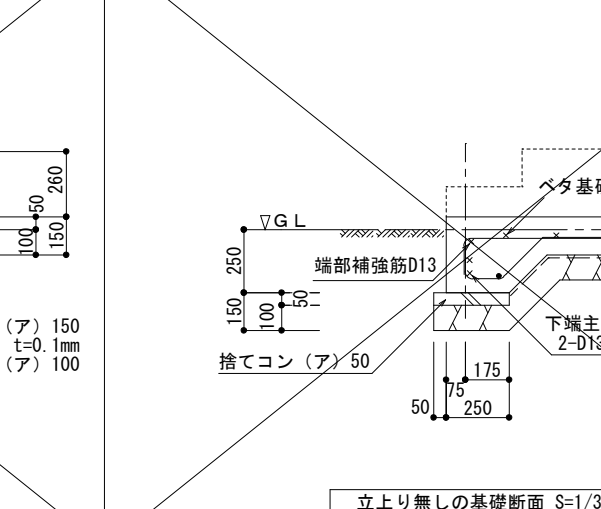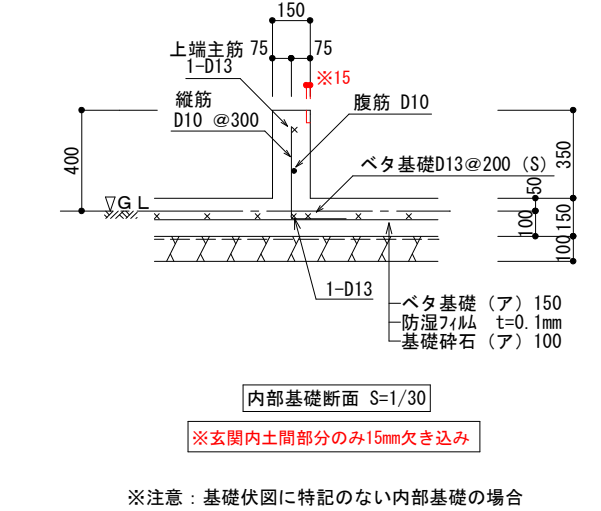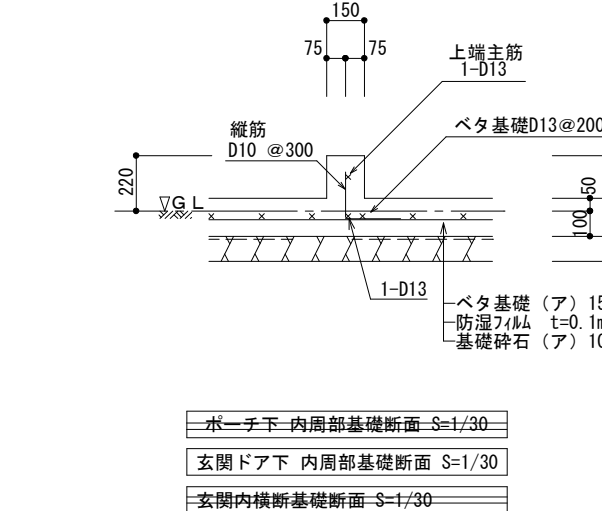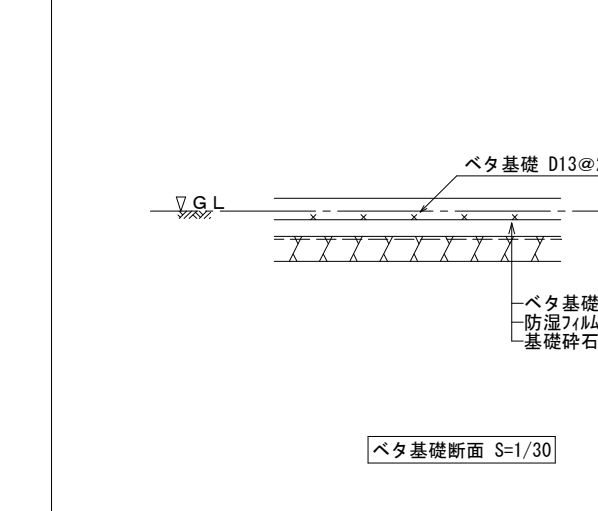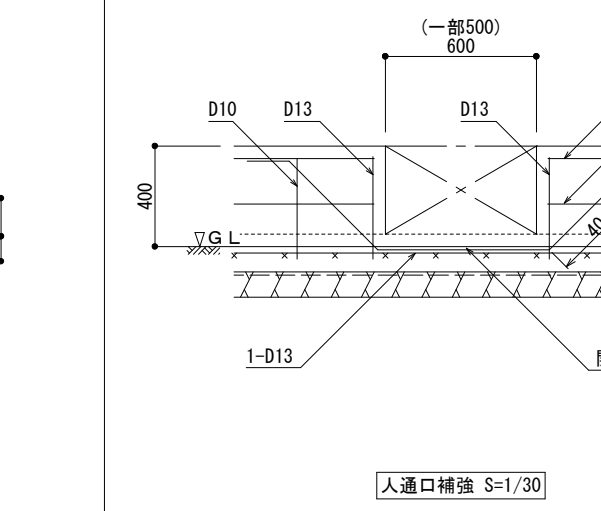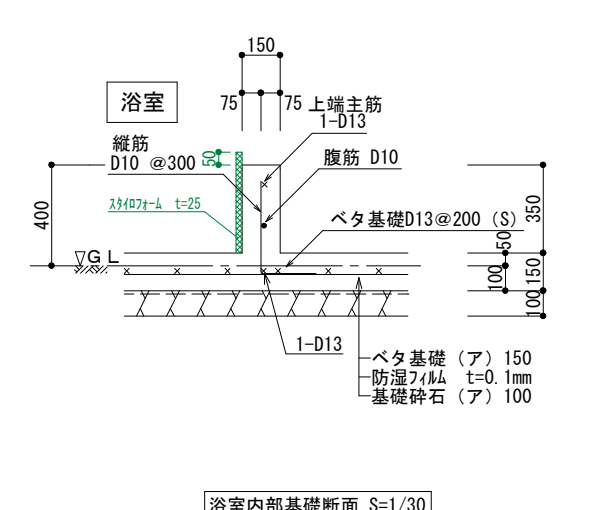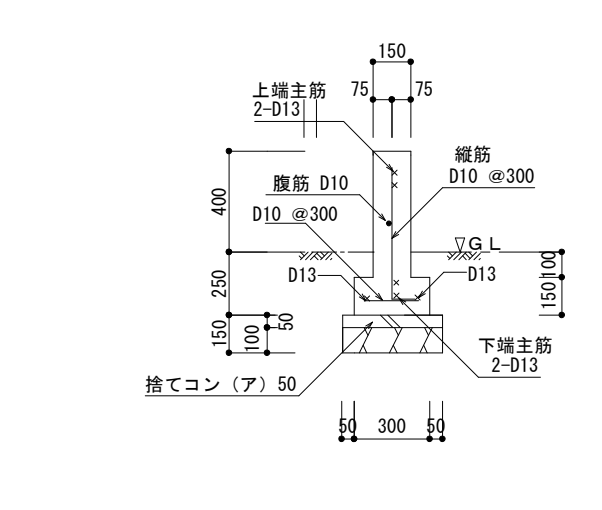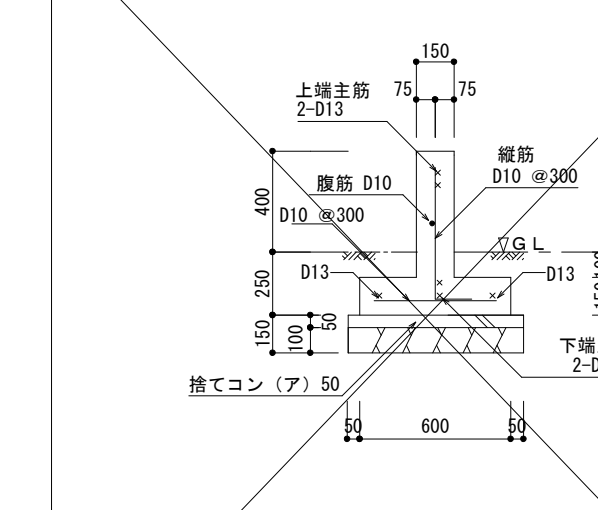 外周基礎断面 S=1/30 ※玄関内土間部分のみ15mm欠き込み	 ポーチ下 外周部基礎断面 S=1/30 倉庫ドア下 外周部基礎断面 S=1/30	 土間納め勝手口ドア下 外周部基礎断面 S=1/30	 立上り無しの基礎断面 S=1/30
 内部基礎断面 S=1/30 ※玄関内土間部分のみ15mm欠き込み ※注意：基礎伏図に特記のない内部基礎の場合	 ポーチ下 内周部基礎断面 S=1/30 玄関ドア下 内周部基礎断面 S=1/30 玄関内横断基礎断面 S=1/30	 ベタ基礎断面 S=1/30	 人通口補強 S=1/30
 浴室内部基礎断面 S=1/30 ※注意：基礎伏図に特記のない内部基礎の場合	 布基礎A：袖壁用 基礎断面 S=1/30	 布基礎B：底用独立 基礎断面 S=1/30	基礎の寸法 及び 配筋の検証方法 基礎立上り配筋は、 (財)日本住宅・木材技術 センター発行のスパン表 (増補版)による。 ベタ基礎スラブ配筋は、 まもりすまい保険設計施工 基準同解説のベタ基礎配筋表 による。具体的な寸法・配 筋は基礎詳細図参照。 鉄筋断面表記 ●・・・D10を示す。 ×・・・D13を示す。 ※使用しない断面は×を記入。

訂 正	浜岡一級総合設計事務所 一級建築士事務所 静岡県知事登録第(10)2441号 一級建築士 大臣登録第365879号 西原利昌	LIFEFUND PG HOUSE	株式会社LIFEFUND InDesign office 一級建築士事務所 事務所登録 (2)第7595号 一級建築士登録 第179770号 鈴木 達男 〒432-8023 静岡県浜松市中央区鴨江3丁目70番23号	年 月 日 2024.07.15 縮 尺 1/30	件 名 PG有玉西分譲 新築工事 図 名 基礎断面リスト		設計 倉田	I C	工務 青島	図 番 B-2
-----	--	----------------------	---	------------------------------------	---------------------------------------	--	----------	-----	----------	------------