


内 部 仕 上 表 （壁下地:石膏ボード12.5mm/天井下地:9.5mm）※脱衣室:床合板特類 下地									
階		床	巾木	壁	品番	廻 縁	天 井	品番	特記事項
1F	ポーチ	LIXILパセオ300/PSO-FIO 4							巾木立上り部はモルタル金鍍仕上
	玄関	LIXILパセオ300/PSO-FIO 4	ライン巾木(W)	ビニルクロス	SLP-250	突付	ビニルクロス	SLP-250	巾木立上り部はモルタル金鍍仕上
	ホール①	イタ銘木フロアーラステックt12 ブラックチェリー3P	ライン巾木(W)	ビニルクロス	SLP-250	突付	ビニルクロス	SLP-250	
	LDK	イタ銘木フロアーラステックt12 ブラックチェリー3P	ライン巾木(W)	ビニルクロス	SLP-250	突付	ビニルクロス	SLP-250	
	畳コーナー	1畳縁ありスタイロ畳 t55	畳寄せ	ビニルクロス	SLP-250	突付	ビニルクロス	SLP-250	畳縁:高田織物 浮No.13
	押入	イタ銘木フロアーラステックt12 ブラックチェリー3P	雑巾摺	ビニルクロス	SLP-250	突付	ビニルクロス	SLP-250	
	洗面所	フロアタイルt2.3 サンゲツIS-2070	H40ソフト巾木W9	ビニルクロス	SLP-250	突付	ビニルクロス	SLP-250	
2F	WC①	フロアタイルt2.3 サンゲツIS-2070	H40ソフト巾木W9	ビニルクロス	SLP-250	突付	ビニルクロス	SLP-250	
	ホール②	イタ銘木フロアーラステックt12 ブラックチェリー3P	ライン巾木(W)	ビニルクロス	SLP-250	突付	ビニルクロス	SLP-250	
	洋室①	イタ銘木フロアーラステックt12 ブラックチェリー3P	ライン巾木(W)	ビニルクロス	SLP-250	突付	ビニルクロス	SLP-250	
	洋室②	イタ銘木フロアーラステックt12 ブラックチェリー3P	ライン巾木(W)	ビニルクロス	SLP-250	突付	ビニルクロス	SLP-250	
	洋室③	イタ銘木フロアーラステックt12 ブラックチェリー3P	ライン巾木(W)	ビニルクロス	SLP-250	突付	ビニルクロス	SLP-250	
	WIC	イタ銘木フロアーラステックt12 ブラックチェリー3P	H40ソフト巾木W9	ビニルクロス	SLP-250	突付	ビニルクロス	SLP-250	
2F	WC②	フロアタイルt2.3 サンゲツIS-2070	H40ソフト巾木W9	ビニルクロス	SLP-250	突付	ビニルクロス	SLP-250	
物入・収納・CL etc		※接続する部屋と同仕様とする							

上框 & 付框	■ LIXILラシッサS 付框30×150 (全周廻し) 色: クリエペール	
階段	■ LIXIL KA 階段	ササラ: プレシヤスホワイト
	段板: クリエペール	蹴込板: プレシヤスホワイト
	ラウンド手摺: クリエペール	手摺金物: プレシヤスホワイト
	上段框: クリエペール	長尺笠木156: LIXIL クリエペール
窓枠	■ YKKap窓枠スルムタイプ	色 ピュアプレーン
※YKKap	※浴室ドア枠 フクビ3方枠	[]
キッチン笠木	■ ゴム集成カウンター(オスモカラー) 色	306270アークリアmatt
カウンター	形状 L型(ジョイント加工)	t=30
天井点検口	■ 天井アルミ点検口枠 450角 TAN45BW	フクビ化学工業 ミルキーホワイト
床下収納庫	■ 高気密型床下点検口断熱型 SPF-R6060 城東テクノ	収納付 (脱衣室) アイボリー(IV)
トイレ棚	■ 2階トイレ D250	アートランバー棚(シェルホワイト)
室内物干し金物	■ なし	
1トイレ	■ アートランバー棚(シェルホワイト) 色	
バックカウンター		t=20
下足入	■ LIXILラシッサS	色 プレシヤスホワイト
	サイズ: W800 D400	形状: 二の字型

支給品	■ 無し
備考	

内 部 建 具 表							
LIXIL		建具色：クリエイペール		枠色 ： 扉同色		※その他、下記特記による	
ラシッサS(標準)		把手 ： スクエアL (シャインニッケル) 丁番 固定枠(156) 外付戸当り ガイドピン床色合せ 引戸のみ上吊Wソフトモーション					
階	No	室名	形式	枠外W サイズ	デザイン	枠色	特記事項
				枠外H サイズ	建具色	把手	
1	1	LDK	片開き戸	—	LGC	—	
	WD			2000	—	—	
	2	洗面所	片引き戸	—	LAA	—	明り窓・表示錠
	WD			2000	—	—	
	3	押入	折れ戸	—	LAD	—	角型Lタテ取付
	WD			2000	—	—	
	4	パントリー	観音開	—	LAA	—	
	WD			2000	—	—	
	5	物入	観音開	—	LAA	—	
	WD			2000	—	—	
	6	WC①	片開き戸	—	LAA	—	明り窓・表示錠
	WD			2000	—	—	
2	7	WC②	片開き戸	—	LAA	—	明り窓・表示錠
	WD			2000	—	—	
	8	洋室①	片開き戸	—	LAA	—	
	WD			2000	—	—	
	9	洋室②	片開き戸	—	LAA	—	
	WD			2000	—	—	
	10	洋室③	片開き戸	—	LAA	—	
	WD			2000	—	—	


	浜 岡 一 級 総 合 設 計 事 務 所 一級建築士事務所 静岡県知事登録第 (10)2441 号 一級建築士 大臣登録第 365879 号 西原利昌	LIFEFUND 株式会社 LIFEFUND InDesign office 一級建築士事務所 事務所登録 (2) 第7595号 一級建築士登録 第179770号 鈴木 達男 〒432-8023 静岡県浜松市中央区鴨江3丁目70番23号	年 月 日 2024.7.16	件名 PG有玉西 分譲		設計	IC	工務	図 番
						倉田	0	青島	1-2
			縮尺	図面 仕上表 2					

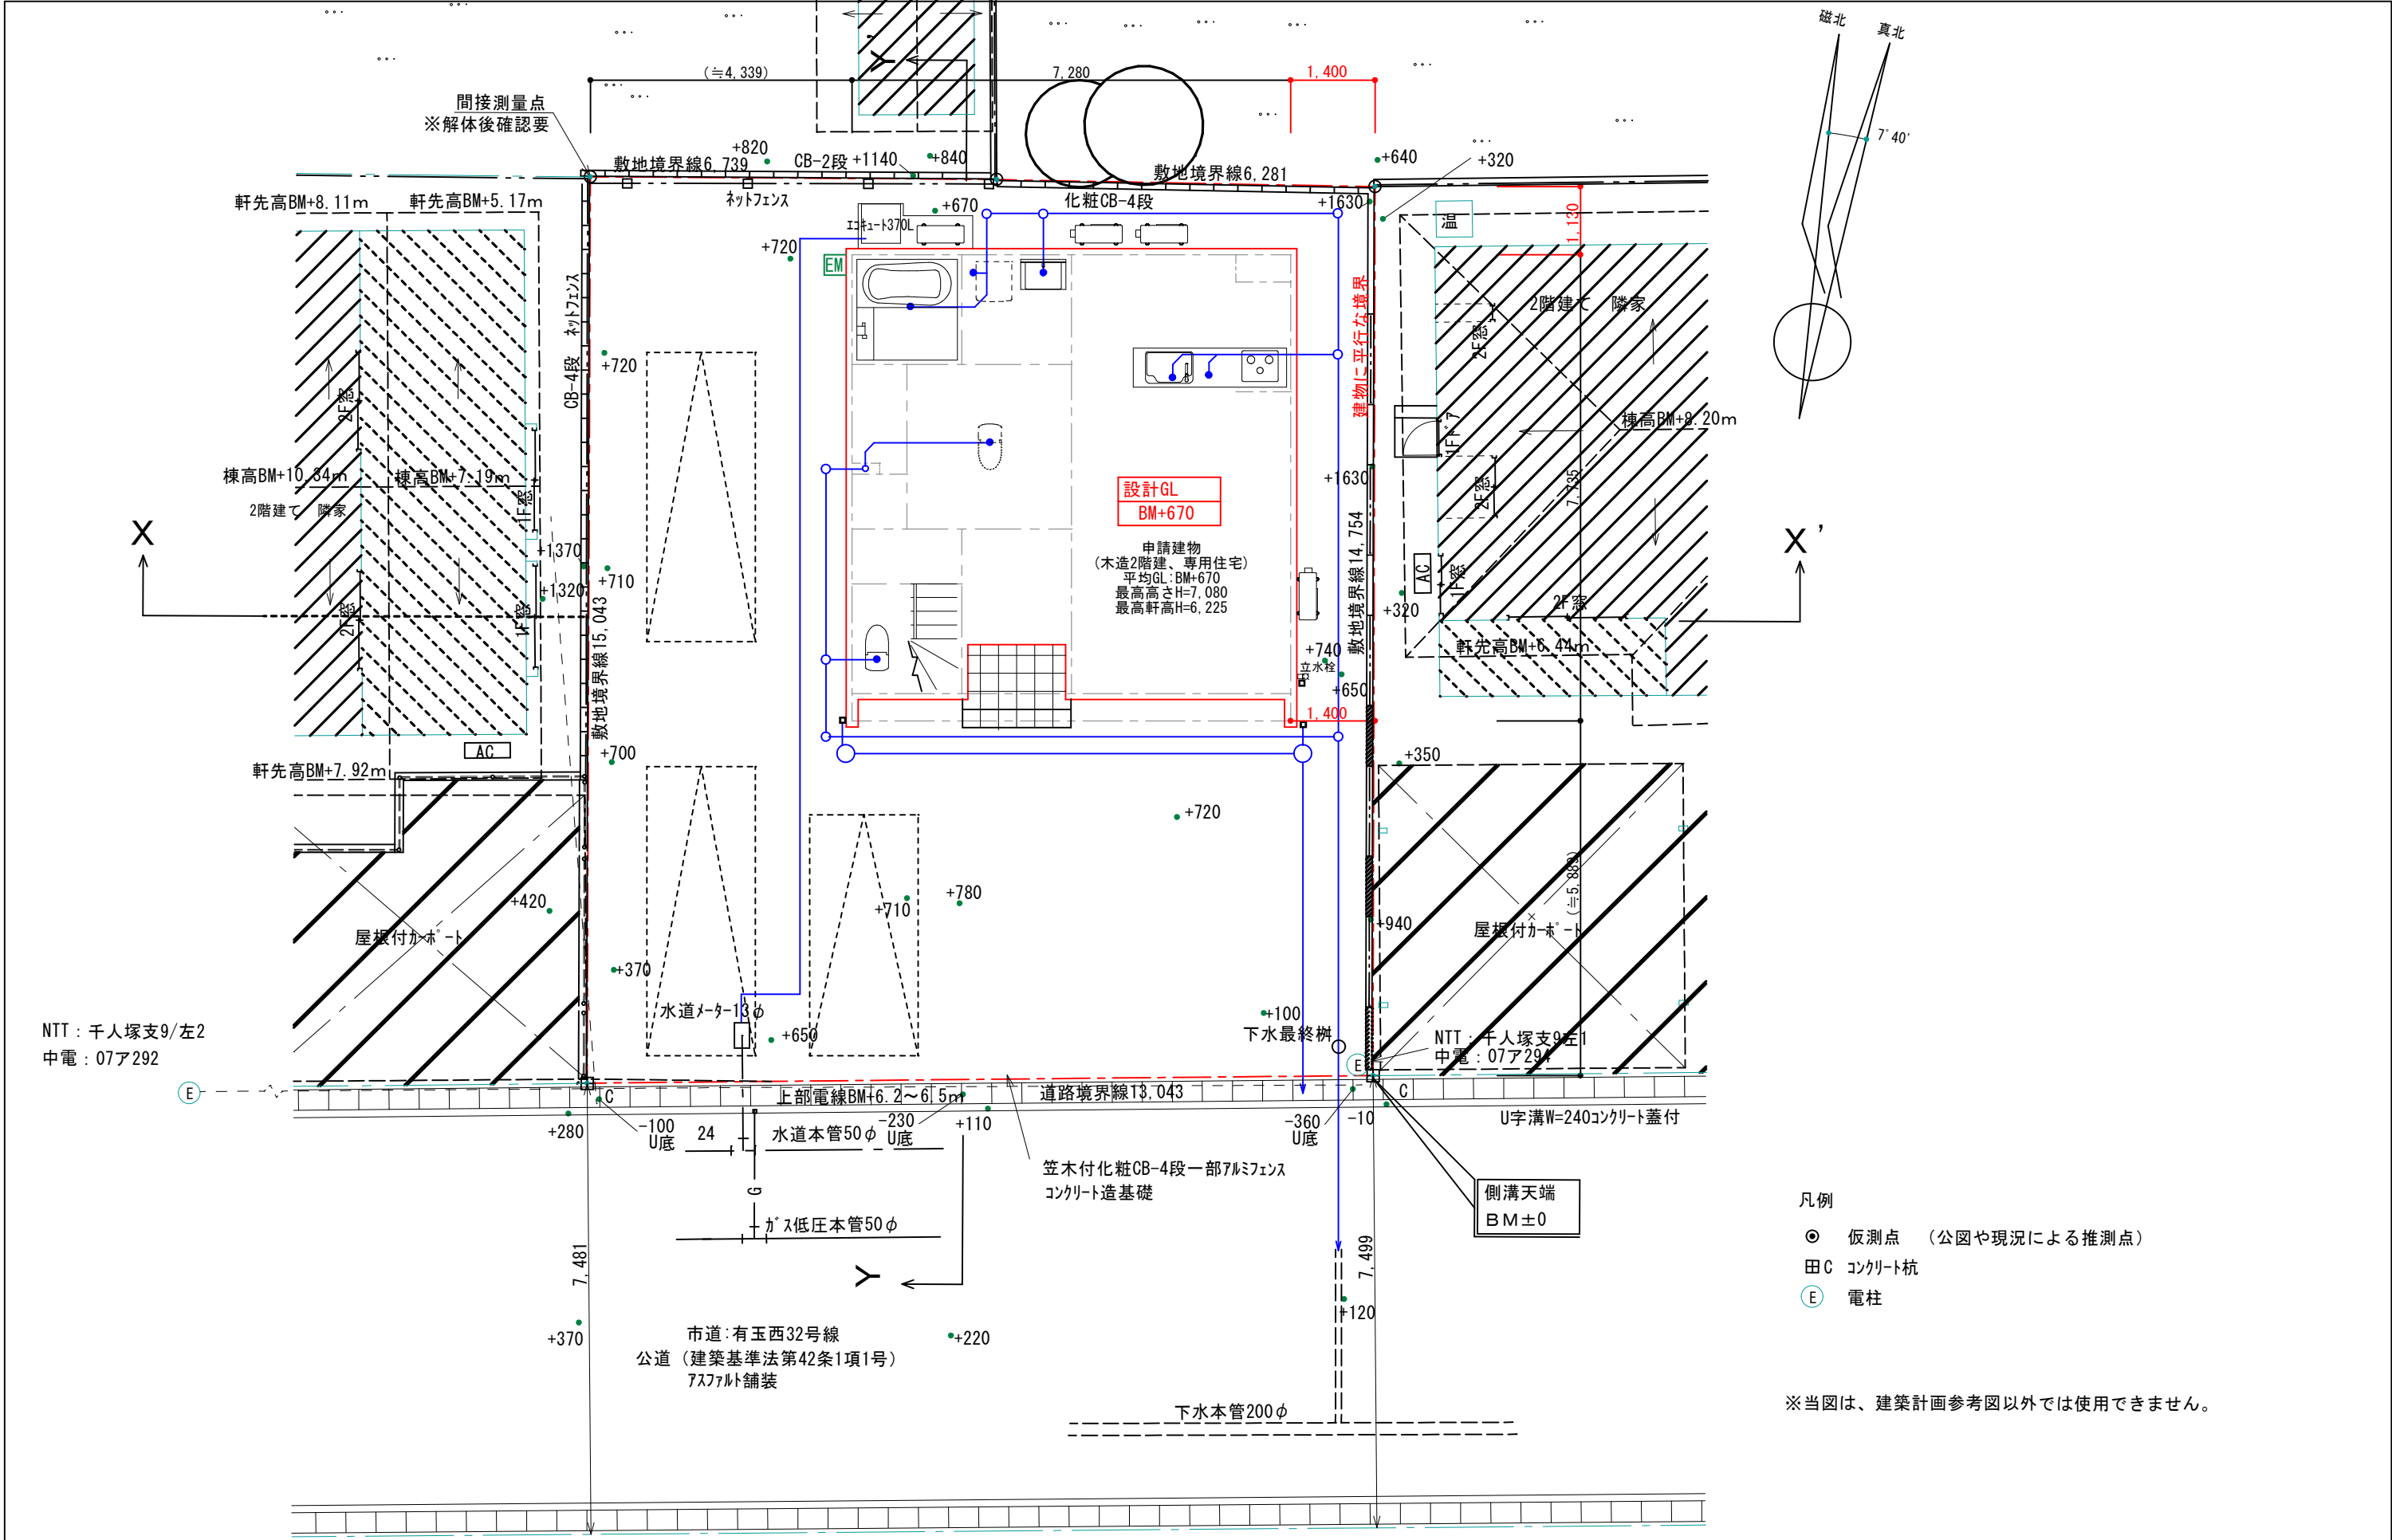

現況平面図 S=1/100

凡例
● 仮測点 (公図や現況による推測点)
田C コンクリート杭
E 電柱
※当図は、建築計画参考図以外では使用できません。

訂正	浜岡一級総合設計事務所 一級建築士事務所 静岡県知事登録第 (10) 2441 号 一級建築士 大臣登録第 365879 号 西原利昌	LIFEFUND PG HOUSE	株式会社 LIFEFUND InDesign office 一級建築士事務所 事務所登録 (2) 第7595号 一級建築士登録 第179770号 鈴木 達男 〒432-8023 静岡県浜松市中央区鴨江3丁目70番23号	年月日 2024. 7. 16	件名 PG有玉西分譲 新築工事		設計	IC	工事	図番
				縮尺 1/50	図名 配置図		倉田		青島	2-1

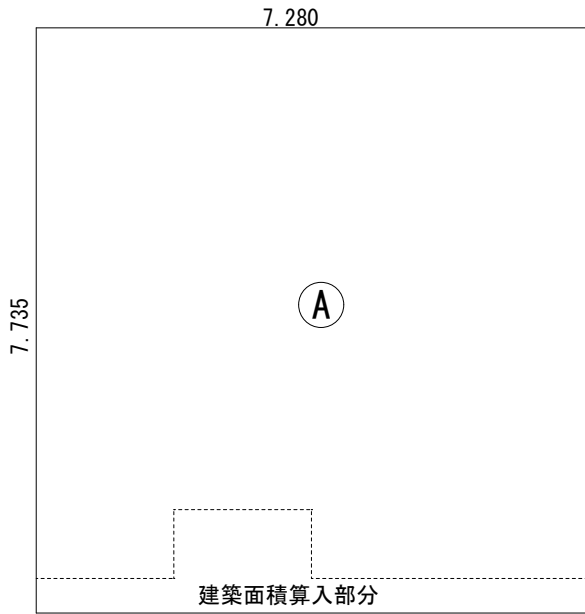


建築面積求積図 S=1/100

建築面積求積表

番号	計算式	面積 (㎡)
①	7.280 × 7.735	56.3108
合計		56.3108 56.31


(17.0坪)

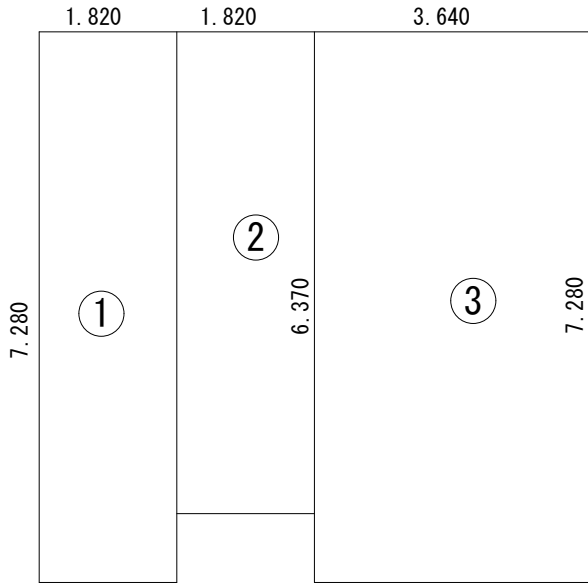

1階床面積図 S=1/100

1階床面積求積表

番号	計算式	面積 (㎡)
①	1.820 × 7.280	13.2496
②	1.820 × 6.370	11.5934
③	3.640 × 7.280	26.4992
合計		51.3422 51.34

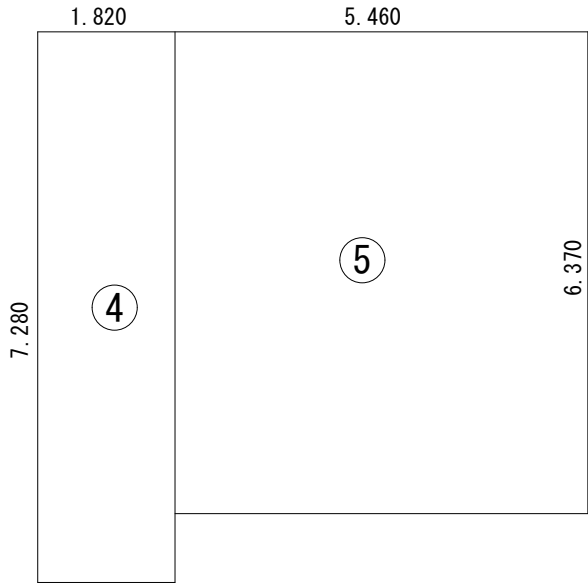

2階床面積図 S=1/100


2階床面積求積表


番号	計算式	面積 (㎡)
④	1.820 × 7.280	13.2496
⑤	5.460 × 6.370	34.7802
合計		48.0298 48.02

延べ床面積表

	番号	面積 (㎡)
1階床面積	① ② ③	51.34
2階床面積	④ ⑤	48.02
合計		99.36

(30.0坪)

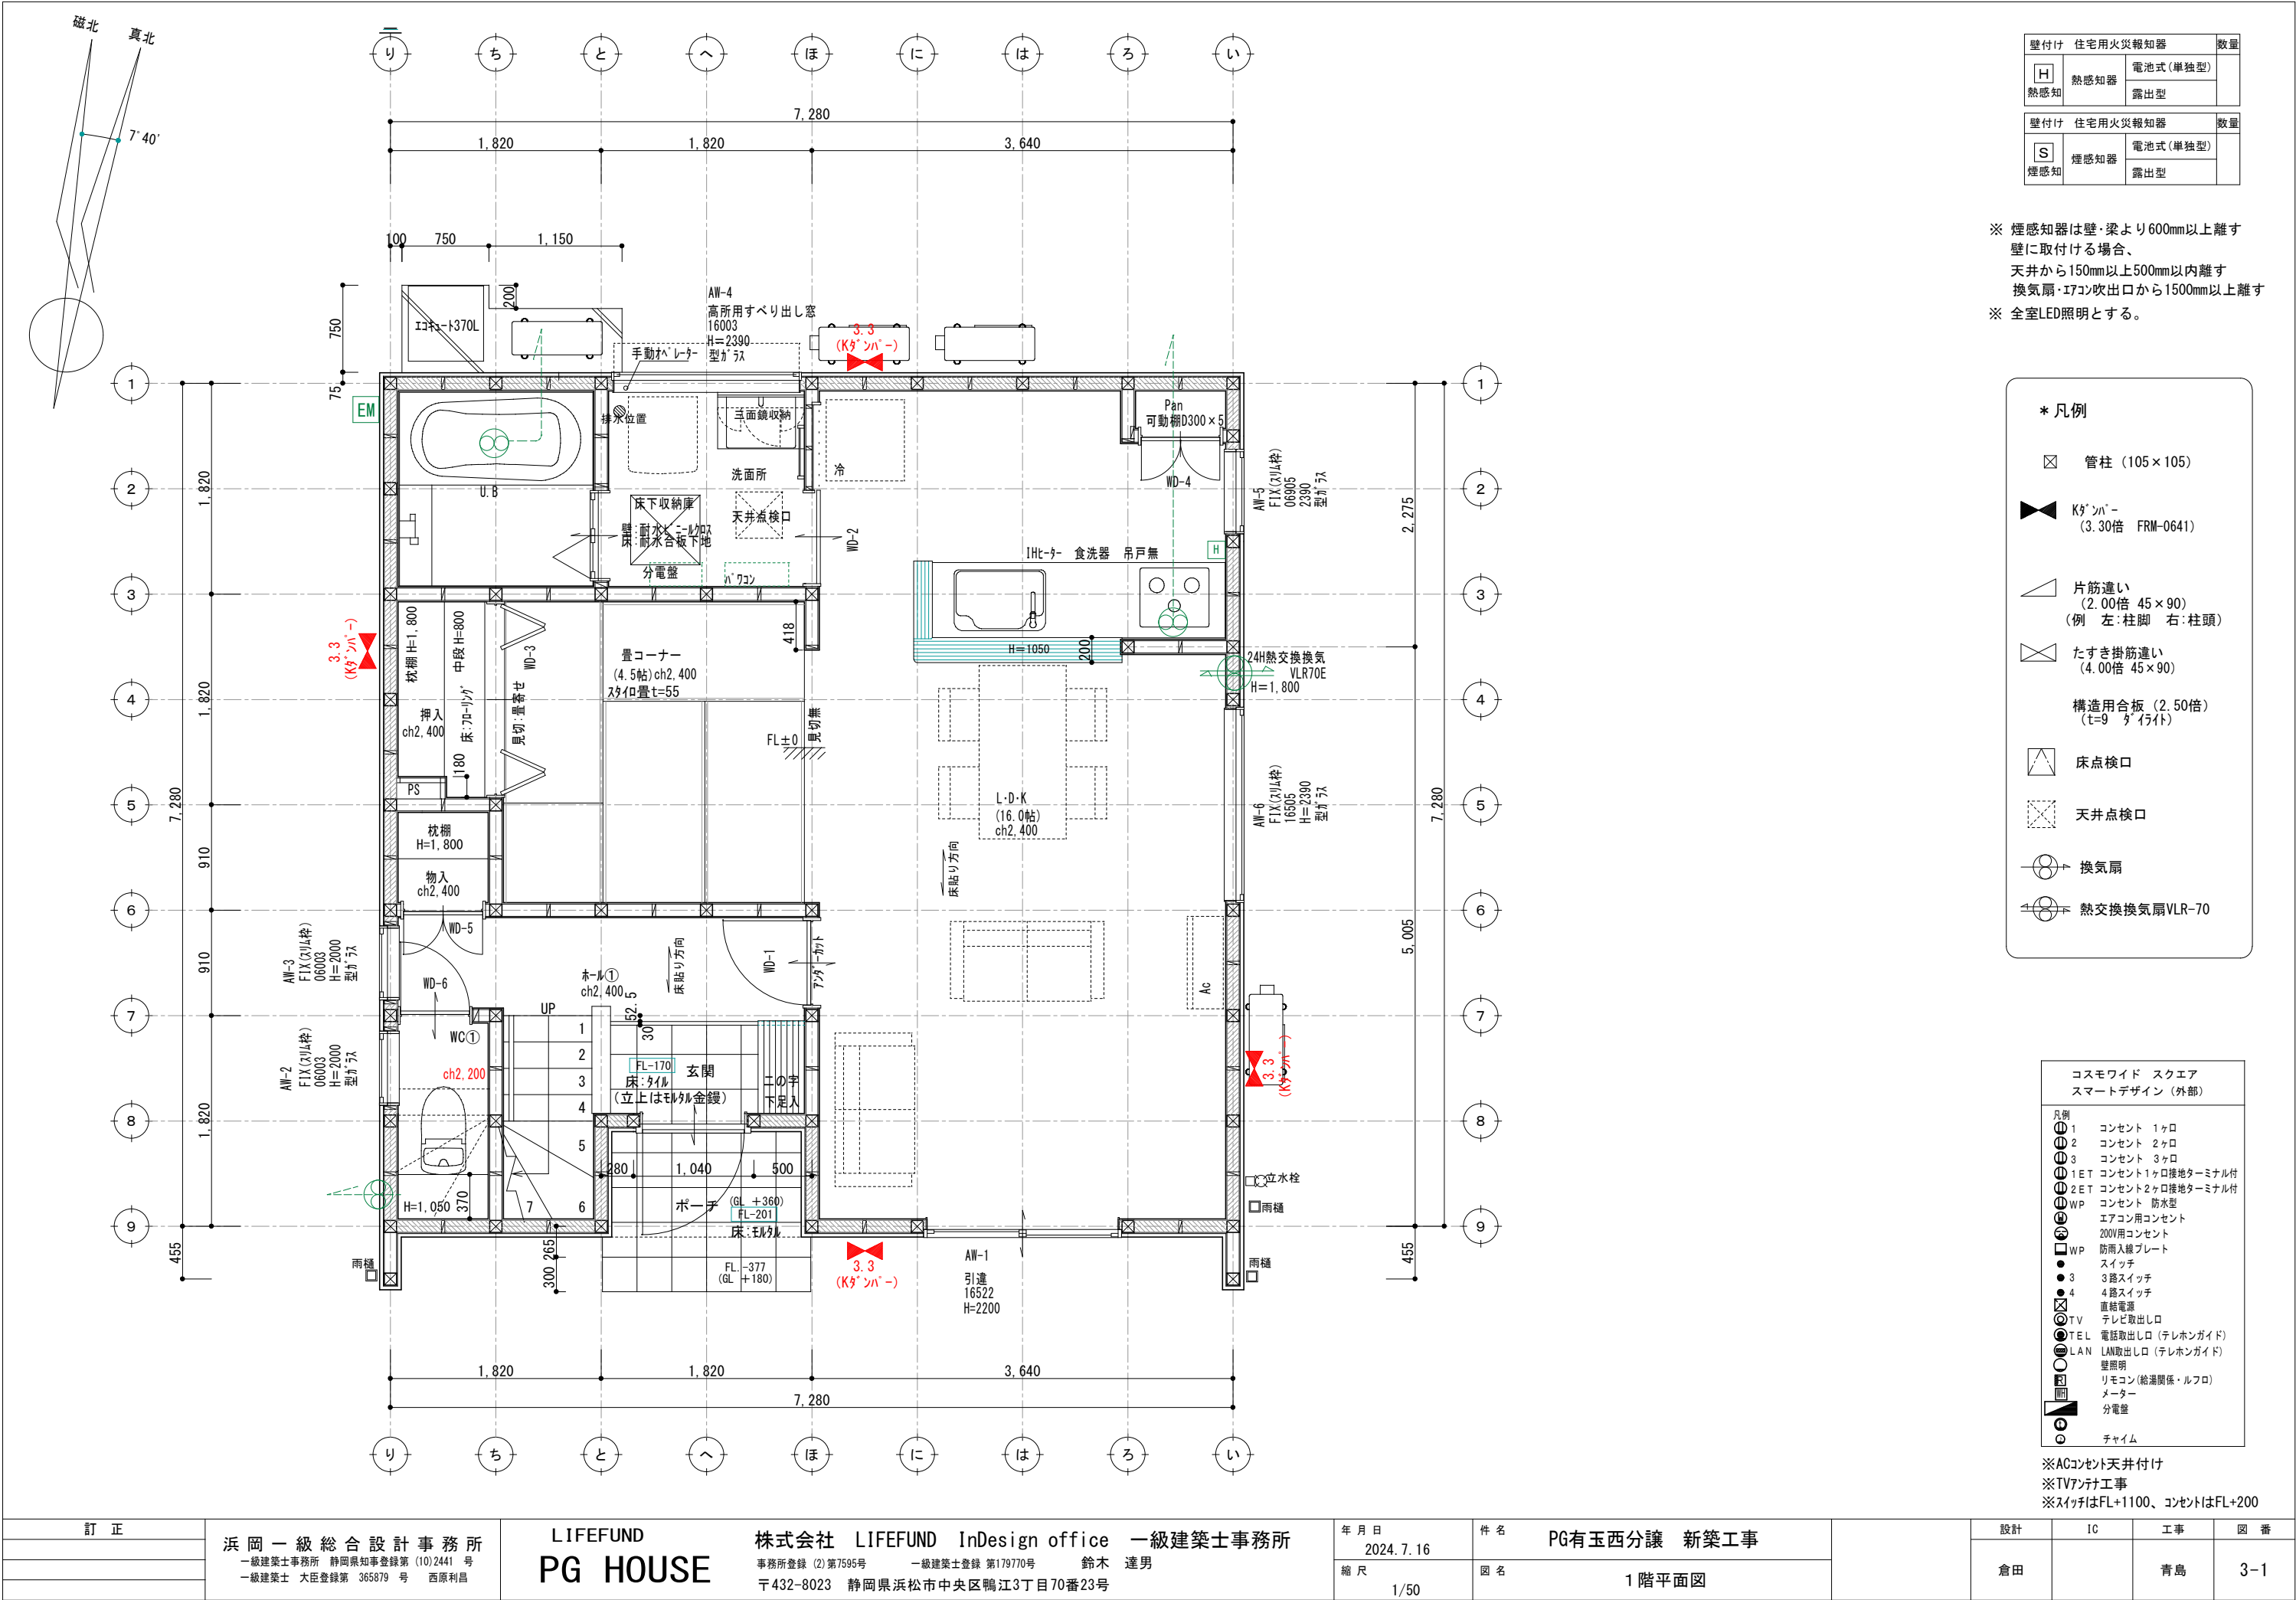

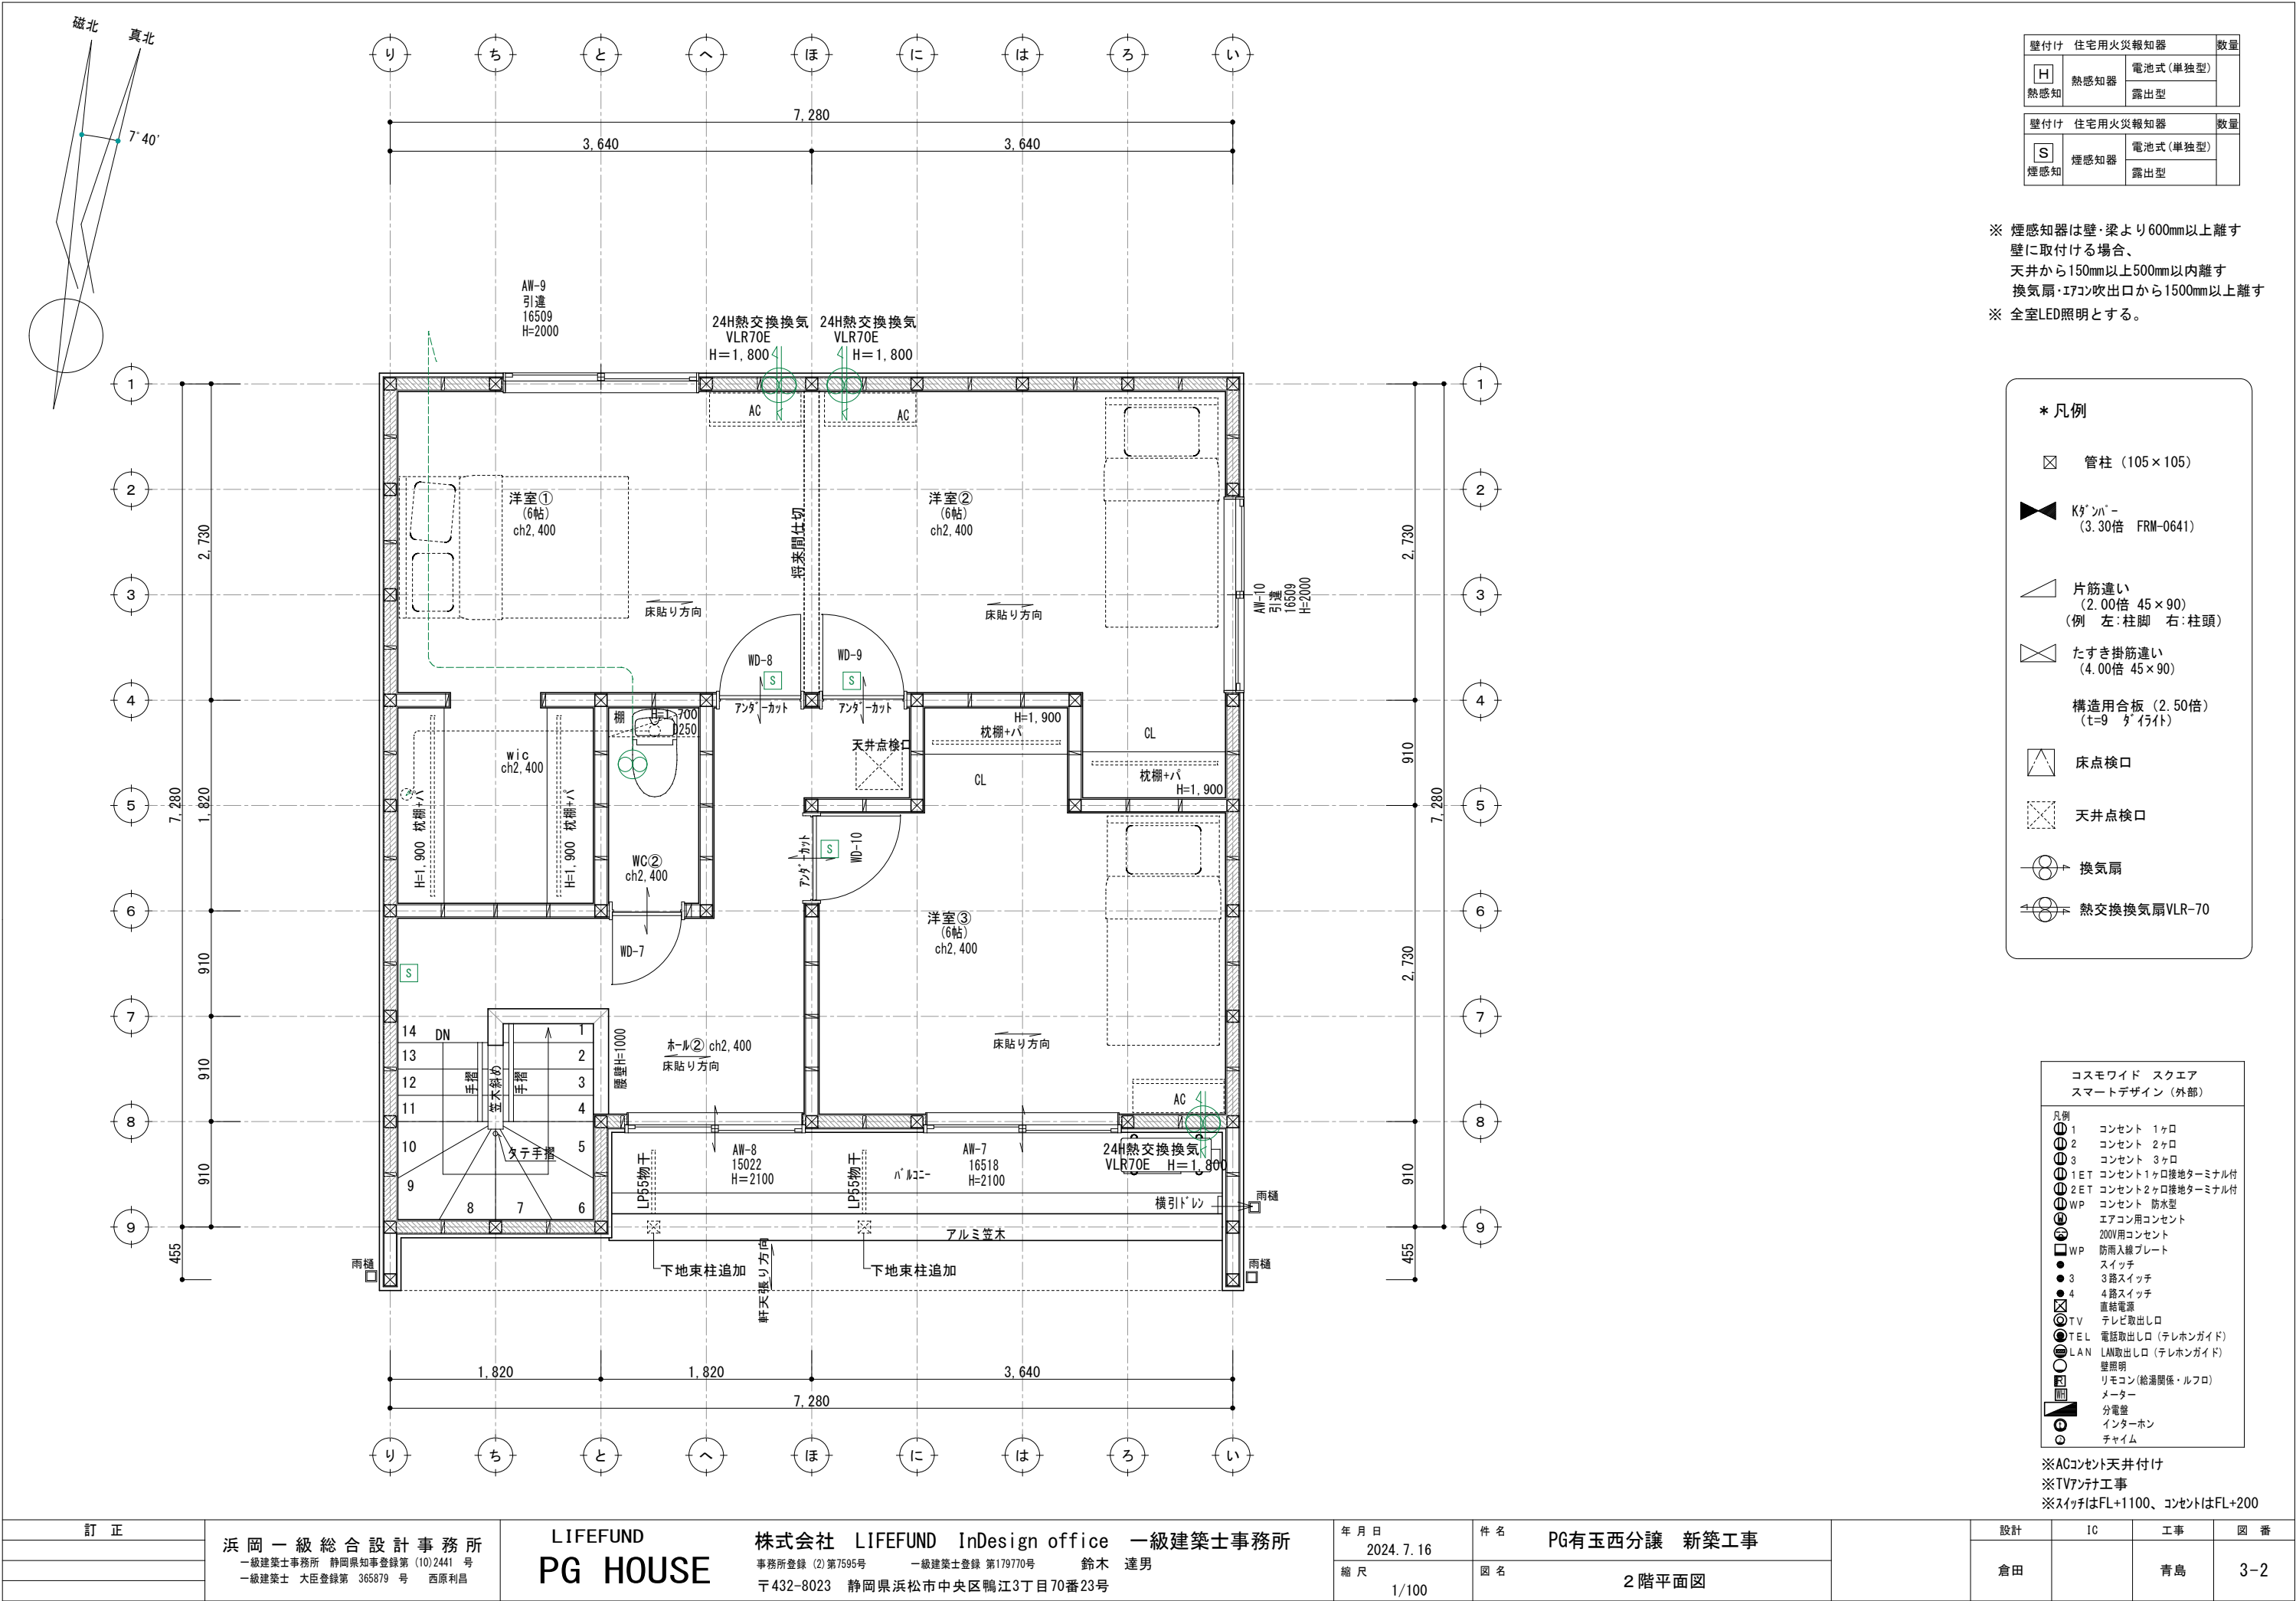

壁付け 住宅用火災報知器			数量
H 熱感知	熱感知器	電池式(単独型)	
		露出型	

壁付け 住宅用火災報知器			数量
S 煙感知	煙感知器	電池式(単独型)	
		露出型	

※ 煙感知器は壁・梁より600mm以上離す壁に取付ける場合、天井から150mm以上500mm以内離す換気扇・エアコン吹出口から1500mm以上離す


※ 全室LED照明とする。

*** 凡例**


- 管柱 (105×105)
- Kダクト (3.30倍 FRM-0641)
- 片筋違い (2.00倍 45×90)
(例 左:柱脚 右:柱頭)
- たすき掛筋違い (4.00倍 45×90)
- 構造用合板 (2.50倍)
(t=9 タイト)
- 床点検口
- 天井点検口
- 換気扇
- 熱交換換気扇VLR-70

コスモワイド スクエア スマートデザイン (外部)			
凡例	1	コンセント	1ヶロ
	2	コンセント	2ヶロ
	3	コンセント	3ヶロ
	1ET	コンセント1ヶロ接地ターミナル付	
	2ET	コンセント2ヶロ接地ターミナル付	
	WP	コンセント 防水型	
		エアコン用コンセント	
		200V用コンセント	
	WP	防雨入線プレート	
		スイッチ	
	3	3路スイッチ	
	4	4路スイッチ	
		直結電源	
	TV	テレビ取出口	
	TEL	電話取出口 (テレホンガイド)	
	LAN	LAN取出口 (テレホンガイド)	
		壁照明	
		リモコン(給湯関係・ルフロ)	
		メーター	
		分電盤	
		インターホン	
		チャイム	

※ACコンセント天井付け
※TVアンテナ工事
※スイッチはFL+1100、コンセントはFL+200

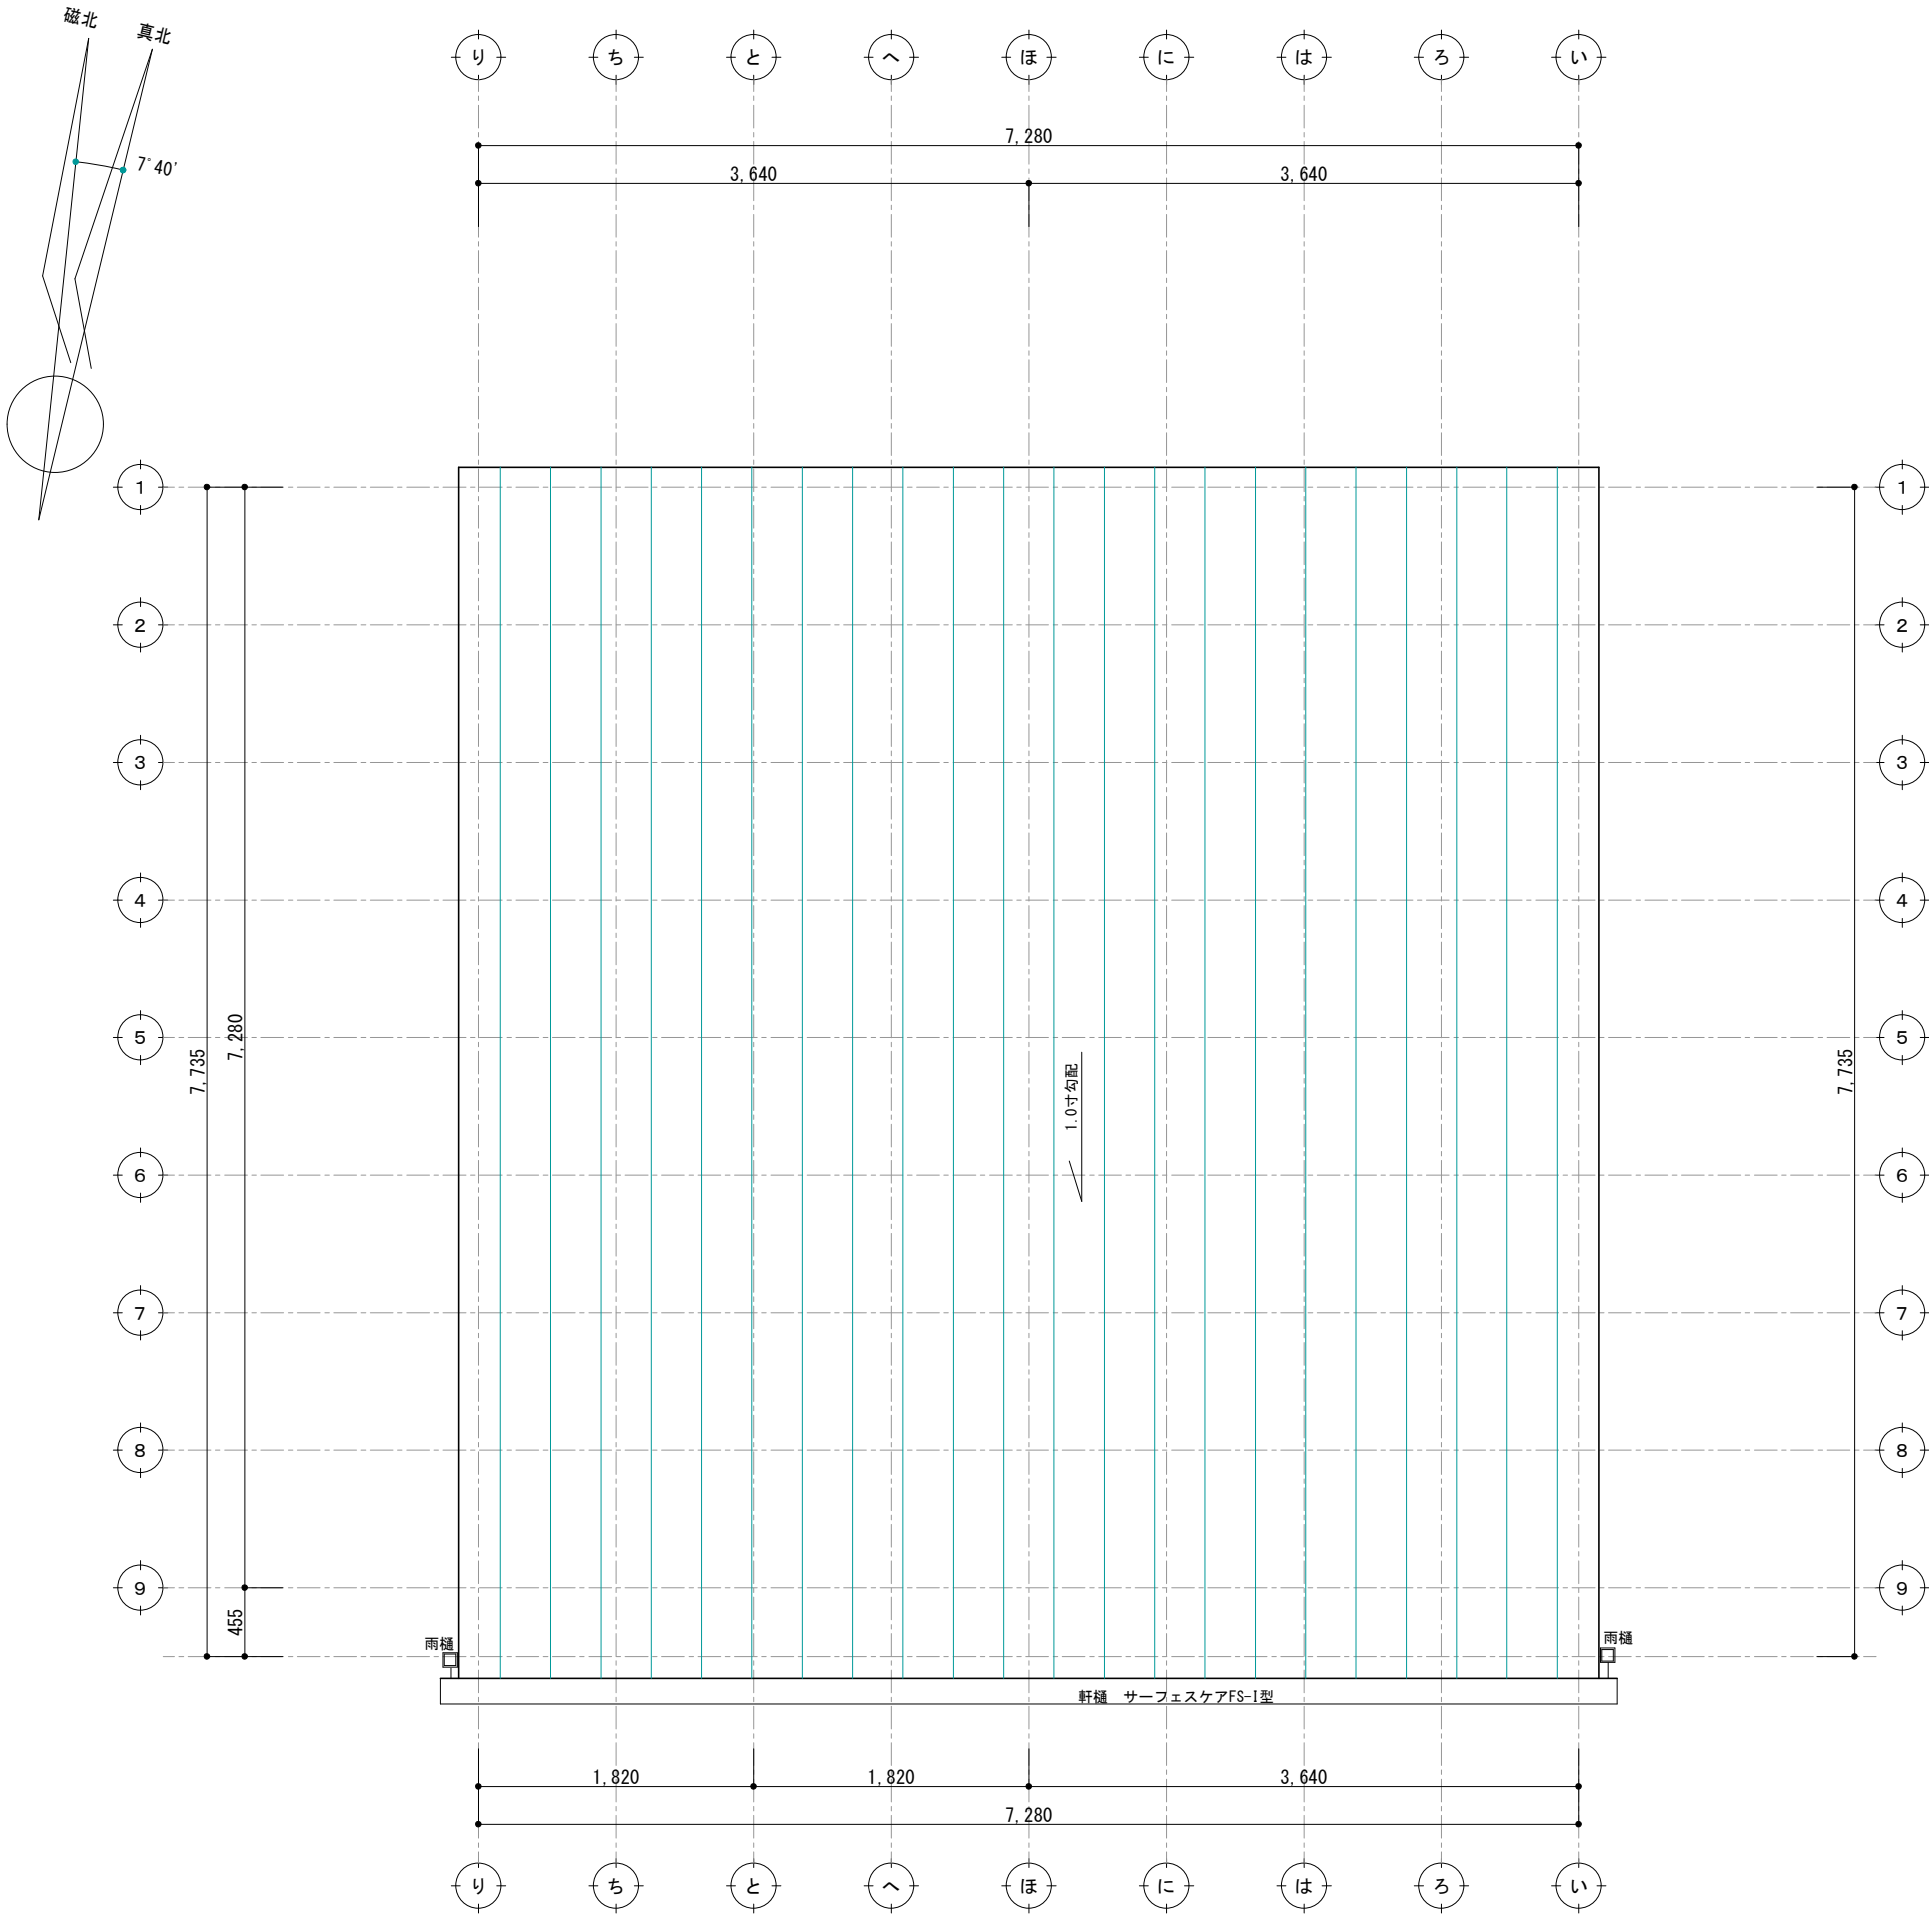


訂 正	浜 岡 一 級 総 合 設 計 事 務 所 一級建築士事務所 静岡県知事登録第 (10)2441 号 一級建築士 大臣登録第 365879 号 西原利昌	LIFEFUND PG HOUSE	株式会社 LIFEFUND InDesign office 一級建築士事務所 事務所登録 (2)第7595号 一級建築士登録 第179770号 鈴木 達男 〒432-8023 静岡県浜松市中央区鴨江3丁目70番23号	年 月 日 2024. 7. 16	件 名 PG有玉西分譲 新築工事		設計	IC	工事	図 番
				縮 尺 1/100	図 名 屋根伏図		倉田		青島	3-3

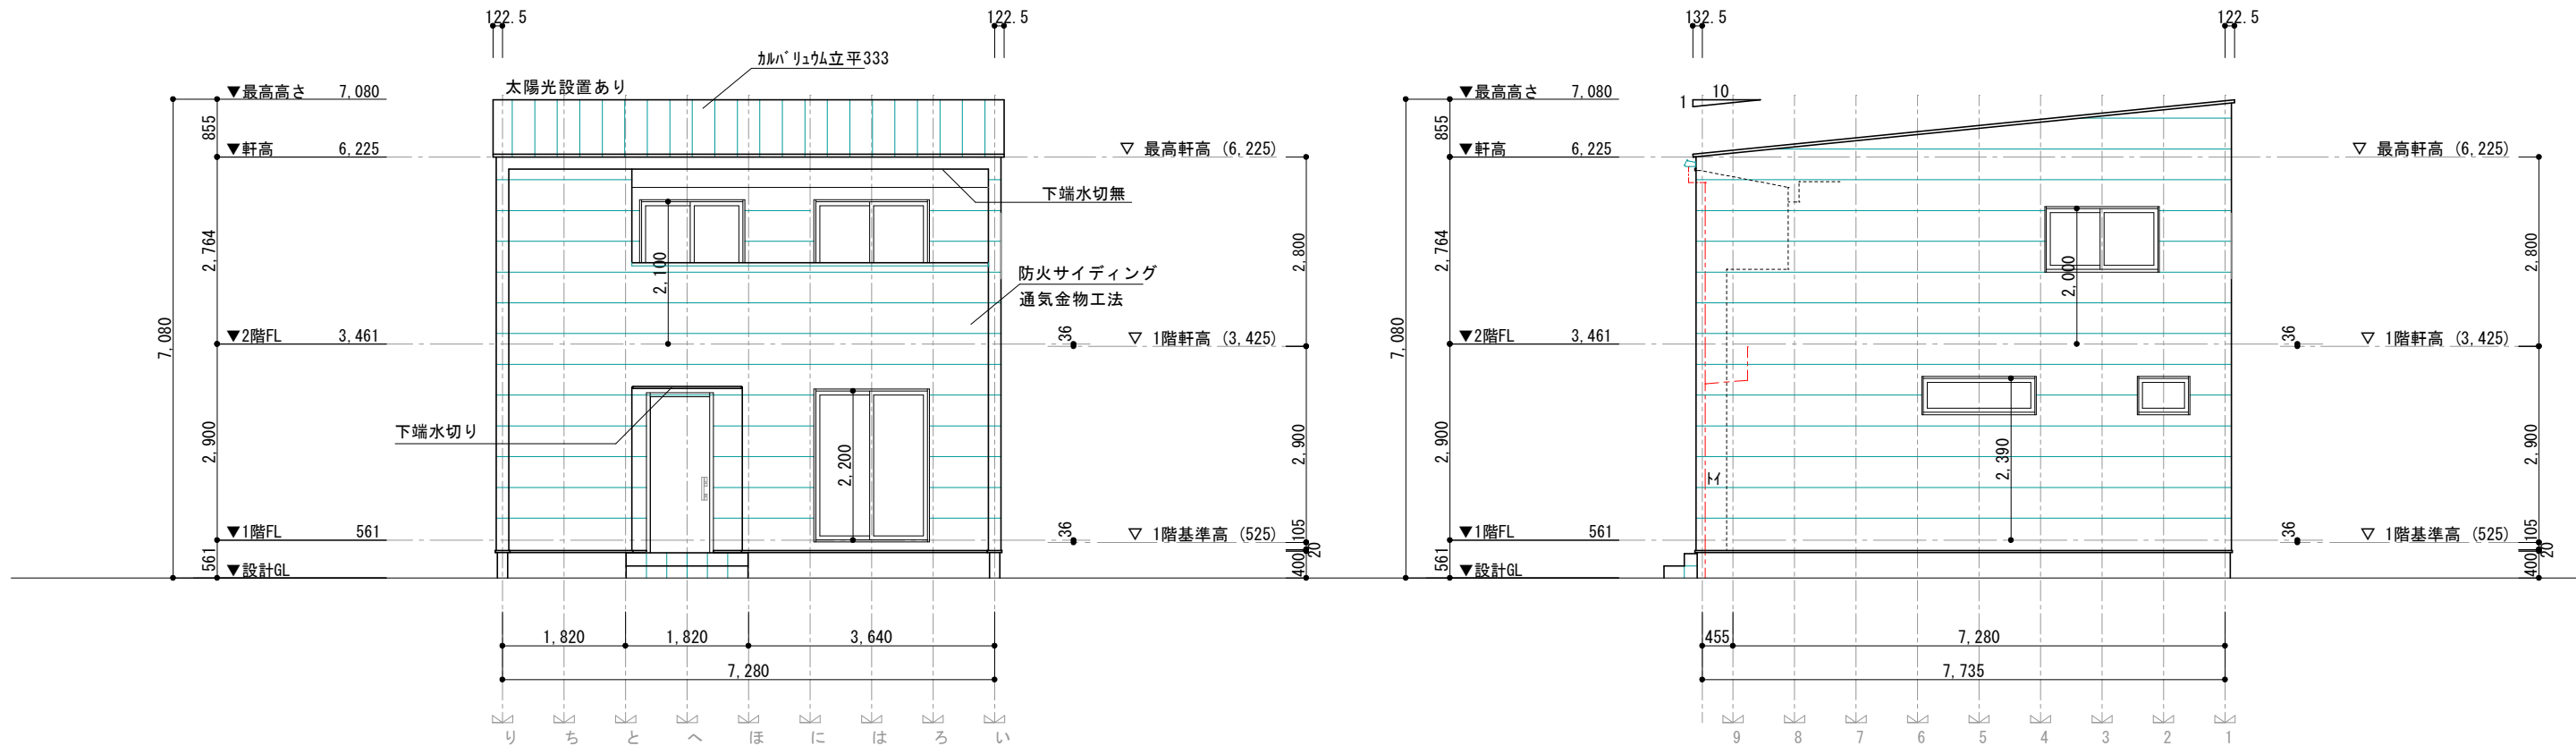

南側立面図 S=1/100


東側立面図 S=1/100

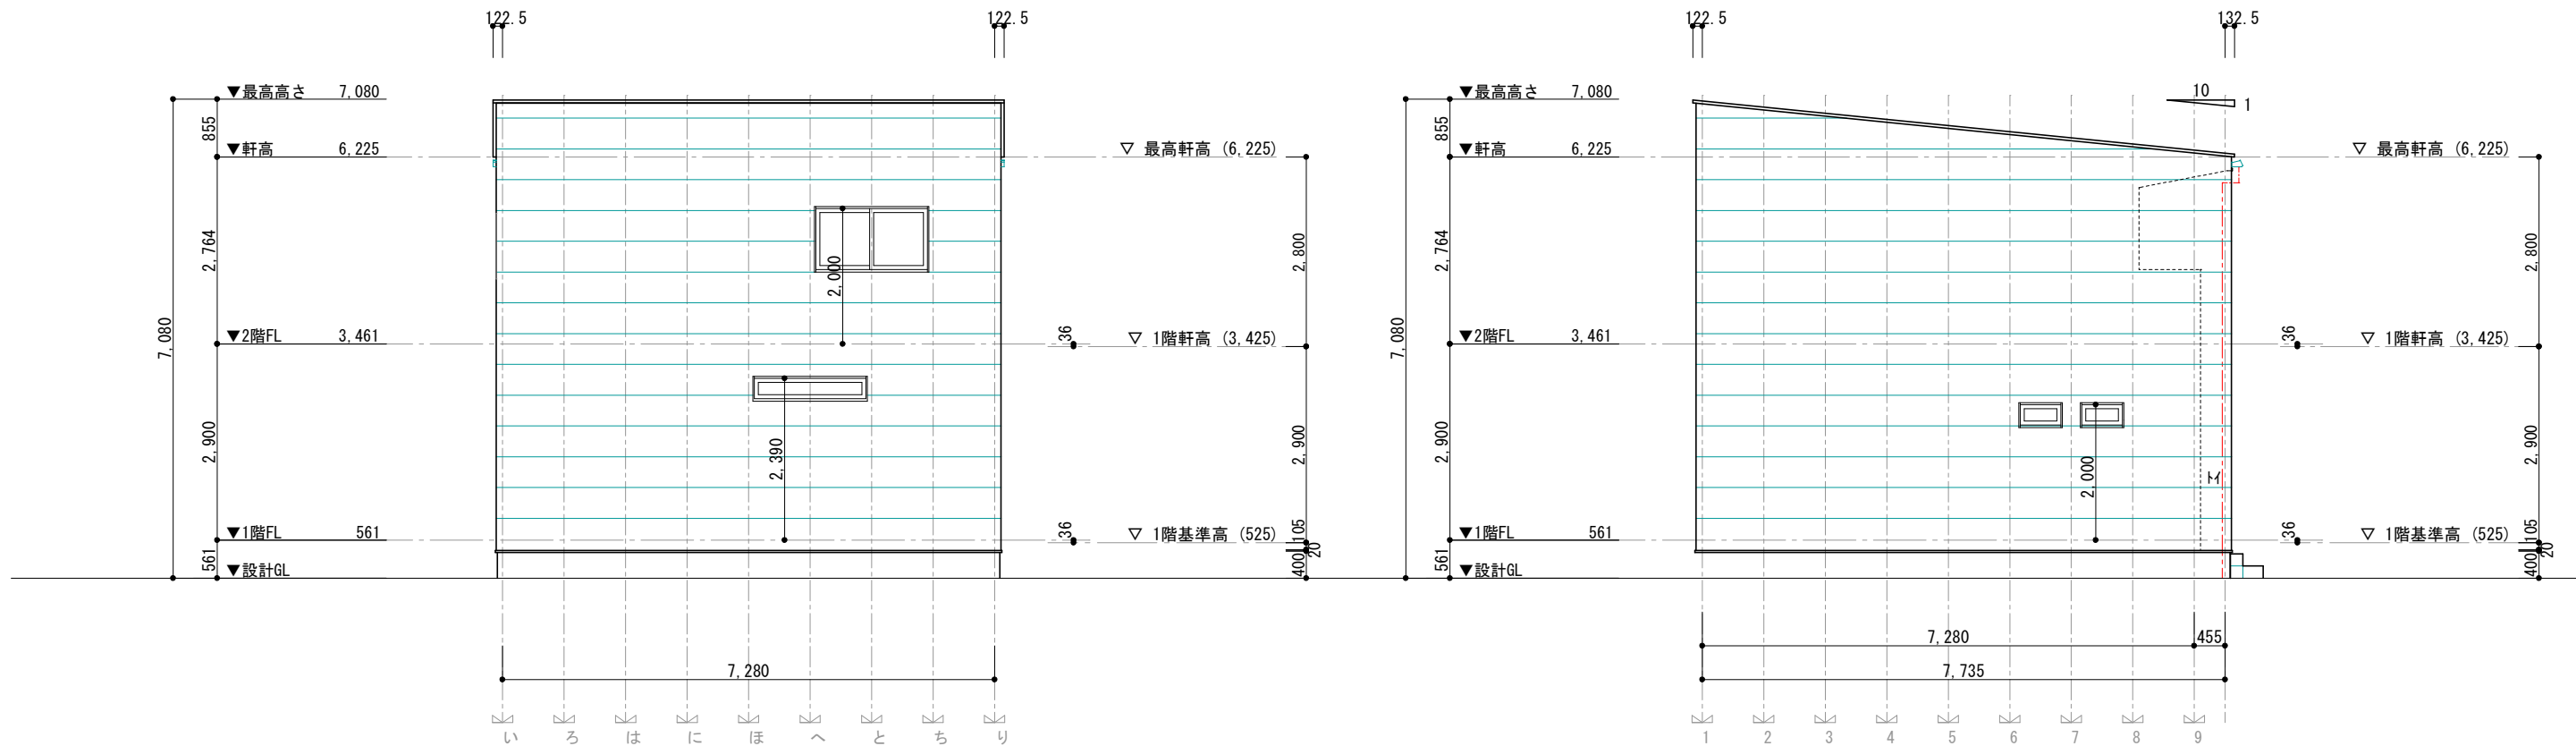


北側立面図 S=1/100

西側立面図 S=1/100


訂 正	浜 岡 一 級 総 合 設 計 事 務 所 一級建築士事務所 静岡県知事登録第 (10)2441 号 一級建築士 大臣登録第 365879 号 西原利昌	LIFEFUND PG HOUSE	株式会社 LIFEFUND InDesign office 一級建築士事務所 事務所登録 (2) 第7595号 一級建築士登録 第179770号 鈴木 達男 〒432-8023 静岡県浜松市中央区鴨江3丁目70番23号	年 月 日	件 名		設計	IC	工事	図 番
				2024. 7. 16	PG有玉西分譲 新築工事					
				縮 尺	図 名					
				1/100	立面図					

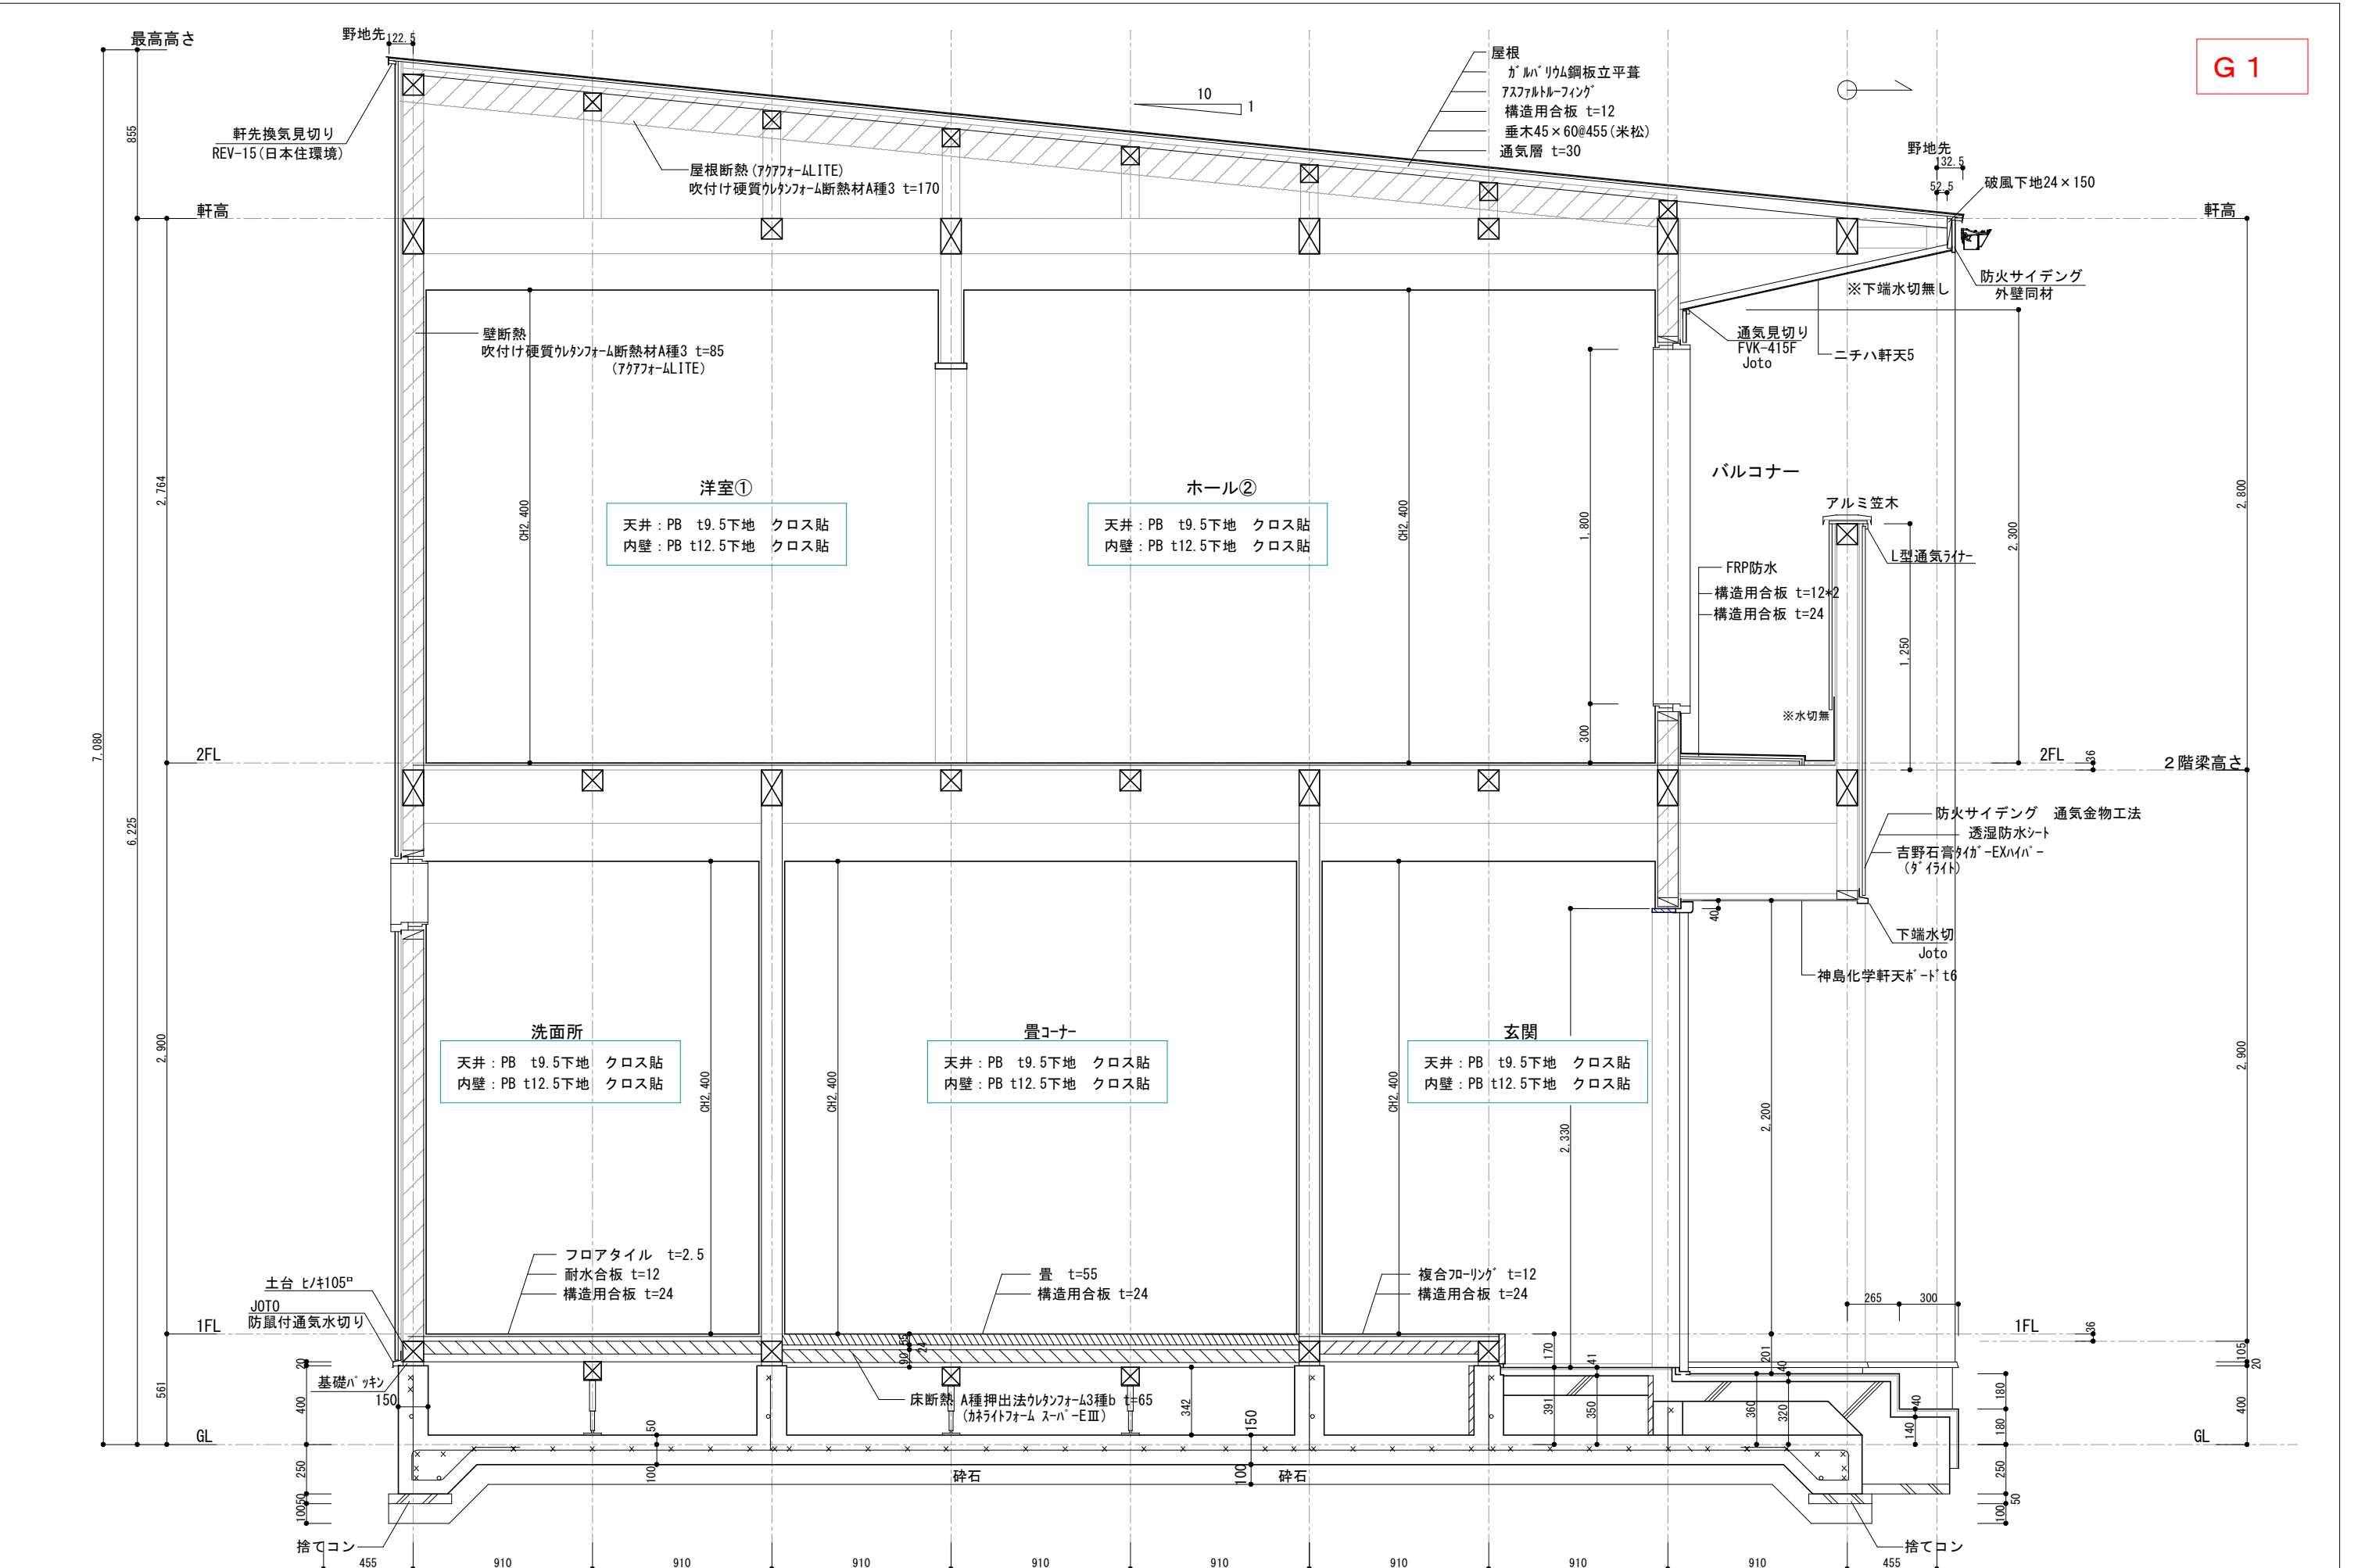


訂正	浜岡一級総合設計事務所 一級建築士事務所 静岡県知事登録第 (10)2441 号 一級建築士 大臣登録第 365879 号 西原利昌	LIFEFUND PG HOUSE	株式会社 LIFEFUND InDesign office 一級建築士事務所 事務所登録 (2)第7595号 一級建築士登録 第179770号 鈴木 達男 〒432-8023 静岡県浜松市中央区鴨江3丁目70番23号	年月日 2024. 7. 16	件名 PG有玉西 分譲 新築工事	設計 倉田	IC	工事 青島	図番 5-1
				縮尺 1/30	図名 矩計図				

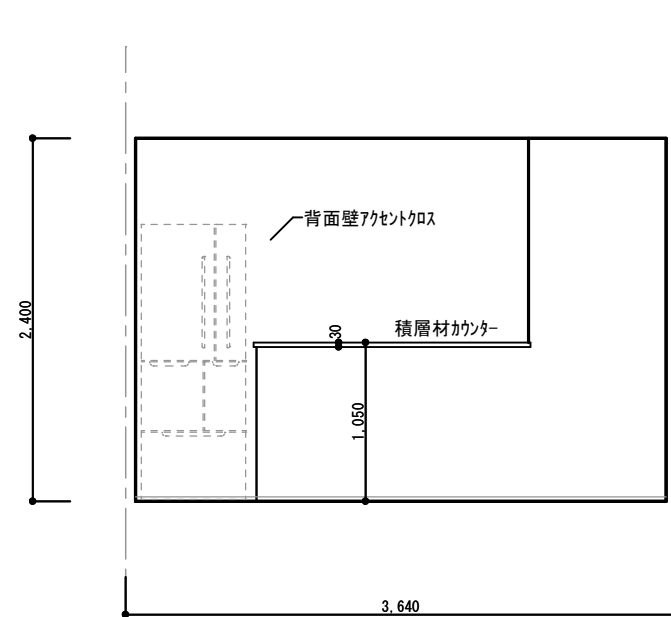


LDK 南面

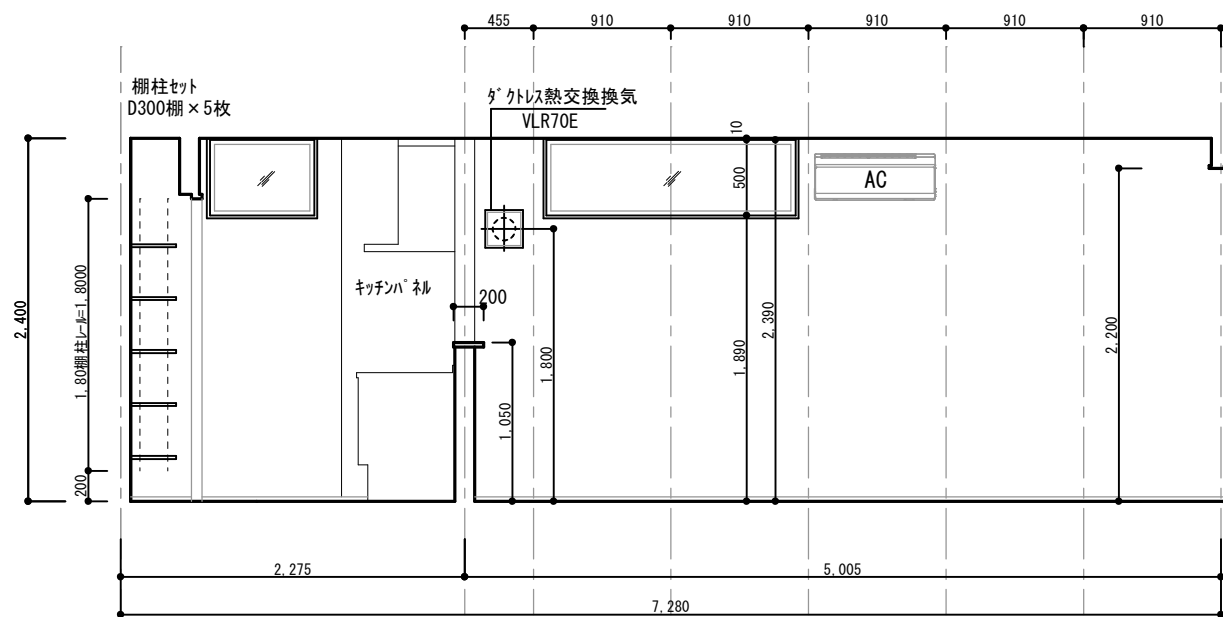


LDK 東面

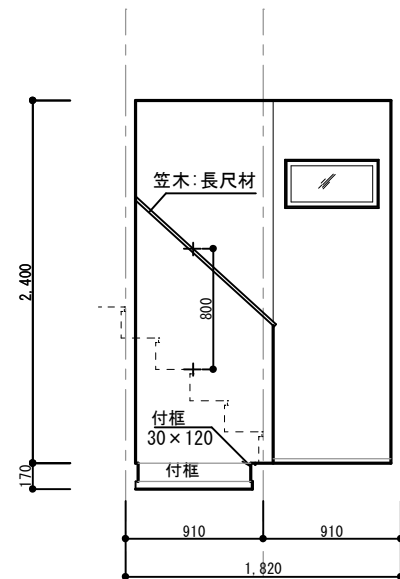


玄関 西面

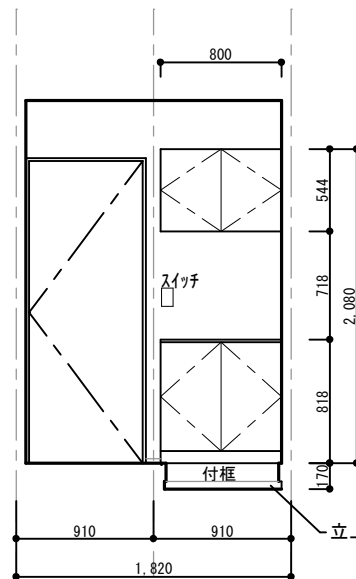


玄関 東面

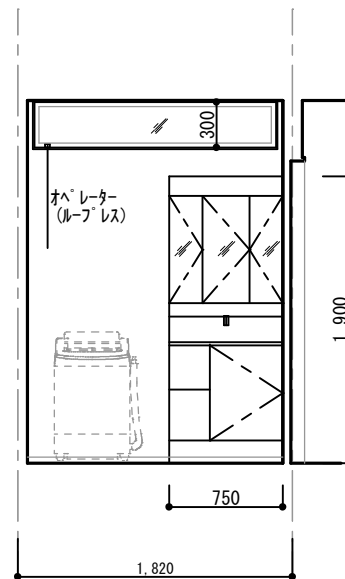


洗面所 北面

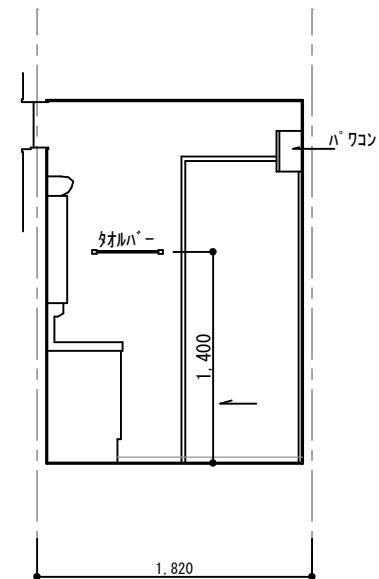


洗面所 東面

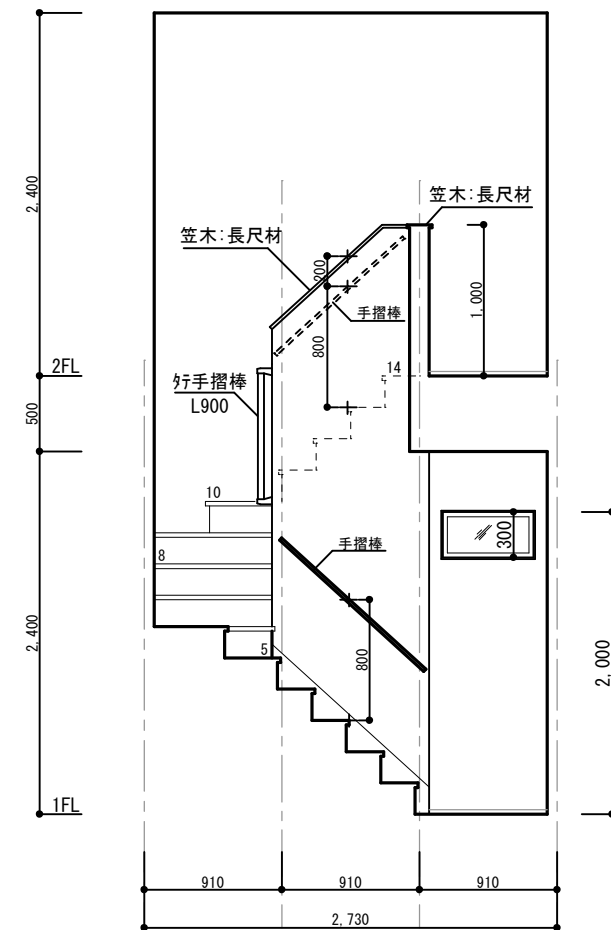


階段 西面

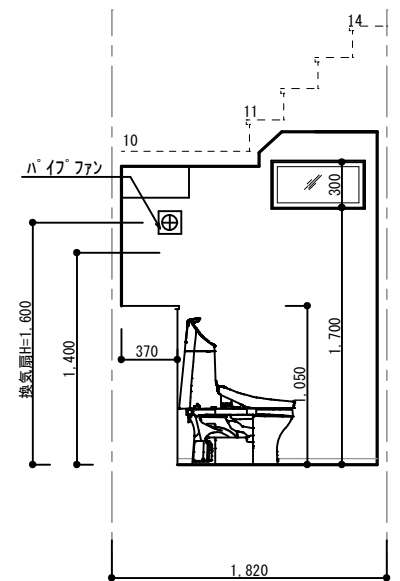


WC② 西面

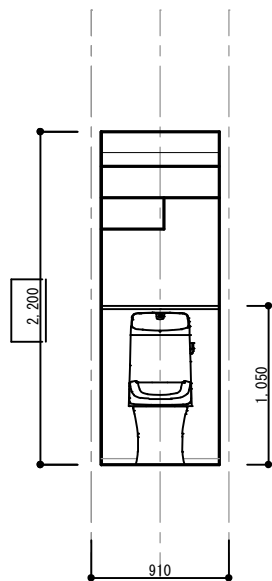


WC① 南面

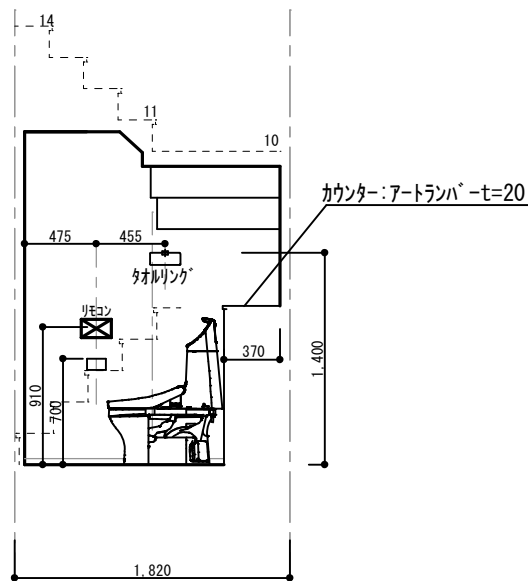

WC② 東面

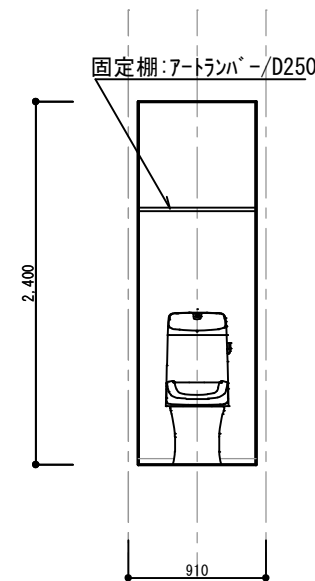



WC② 北面

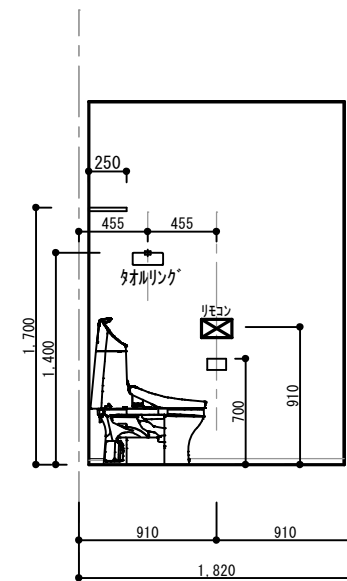

WC② 東面

訂正	浜岡 一級総合設計事務所 一級建築士事務所 静岡県知事登録第 (10)2441 号 一級建築士 大臣登録第 365879 号 西原利晶	LIFEFUND PG HOUSE	株式会社 LIFEFUND InDesign office 一級建築士事務所 事務所登録 (2)第7595号 一級建築士登録 第179770号 鈴木 達男 〒432-8023 静岡県浜松市中央区鴨江3丁目70番23号	年月日 2024.07.16	件名 PG有玉西分譲 新築工事		設計	IC	工事	図番
				縮尺 1/30	図名 展開図(1)		倉田		青島	6-1

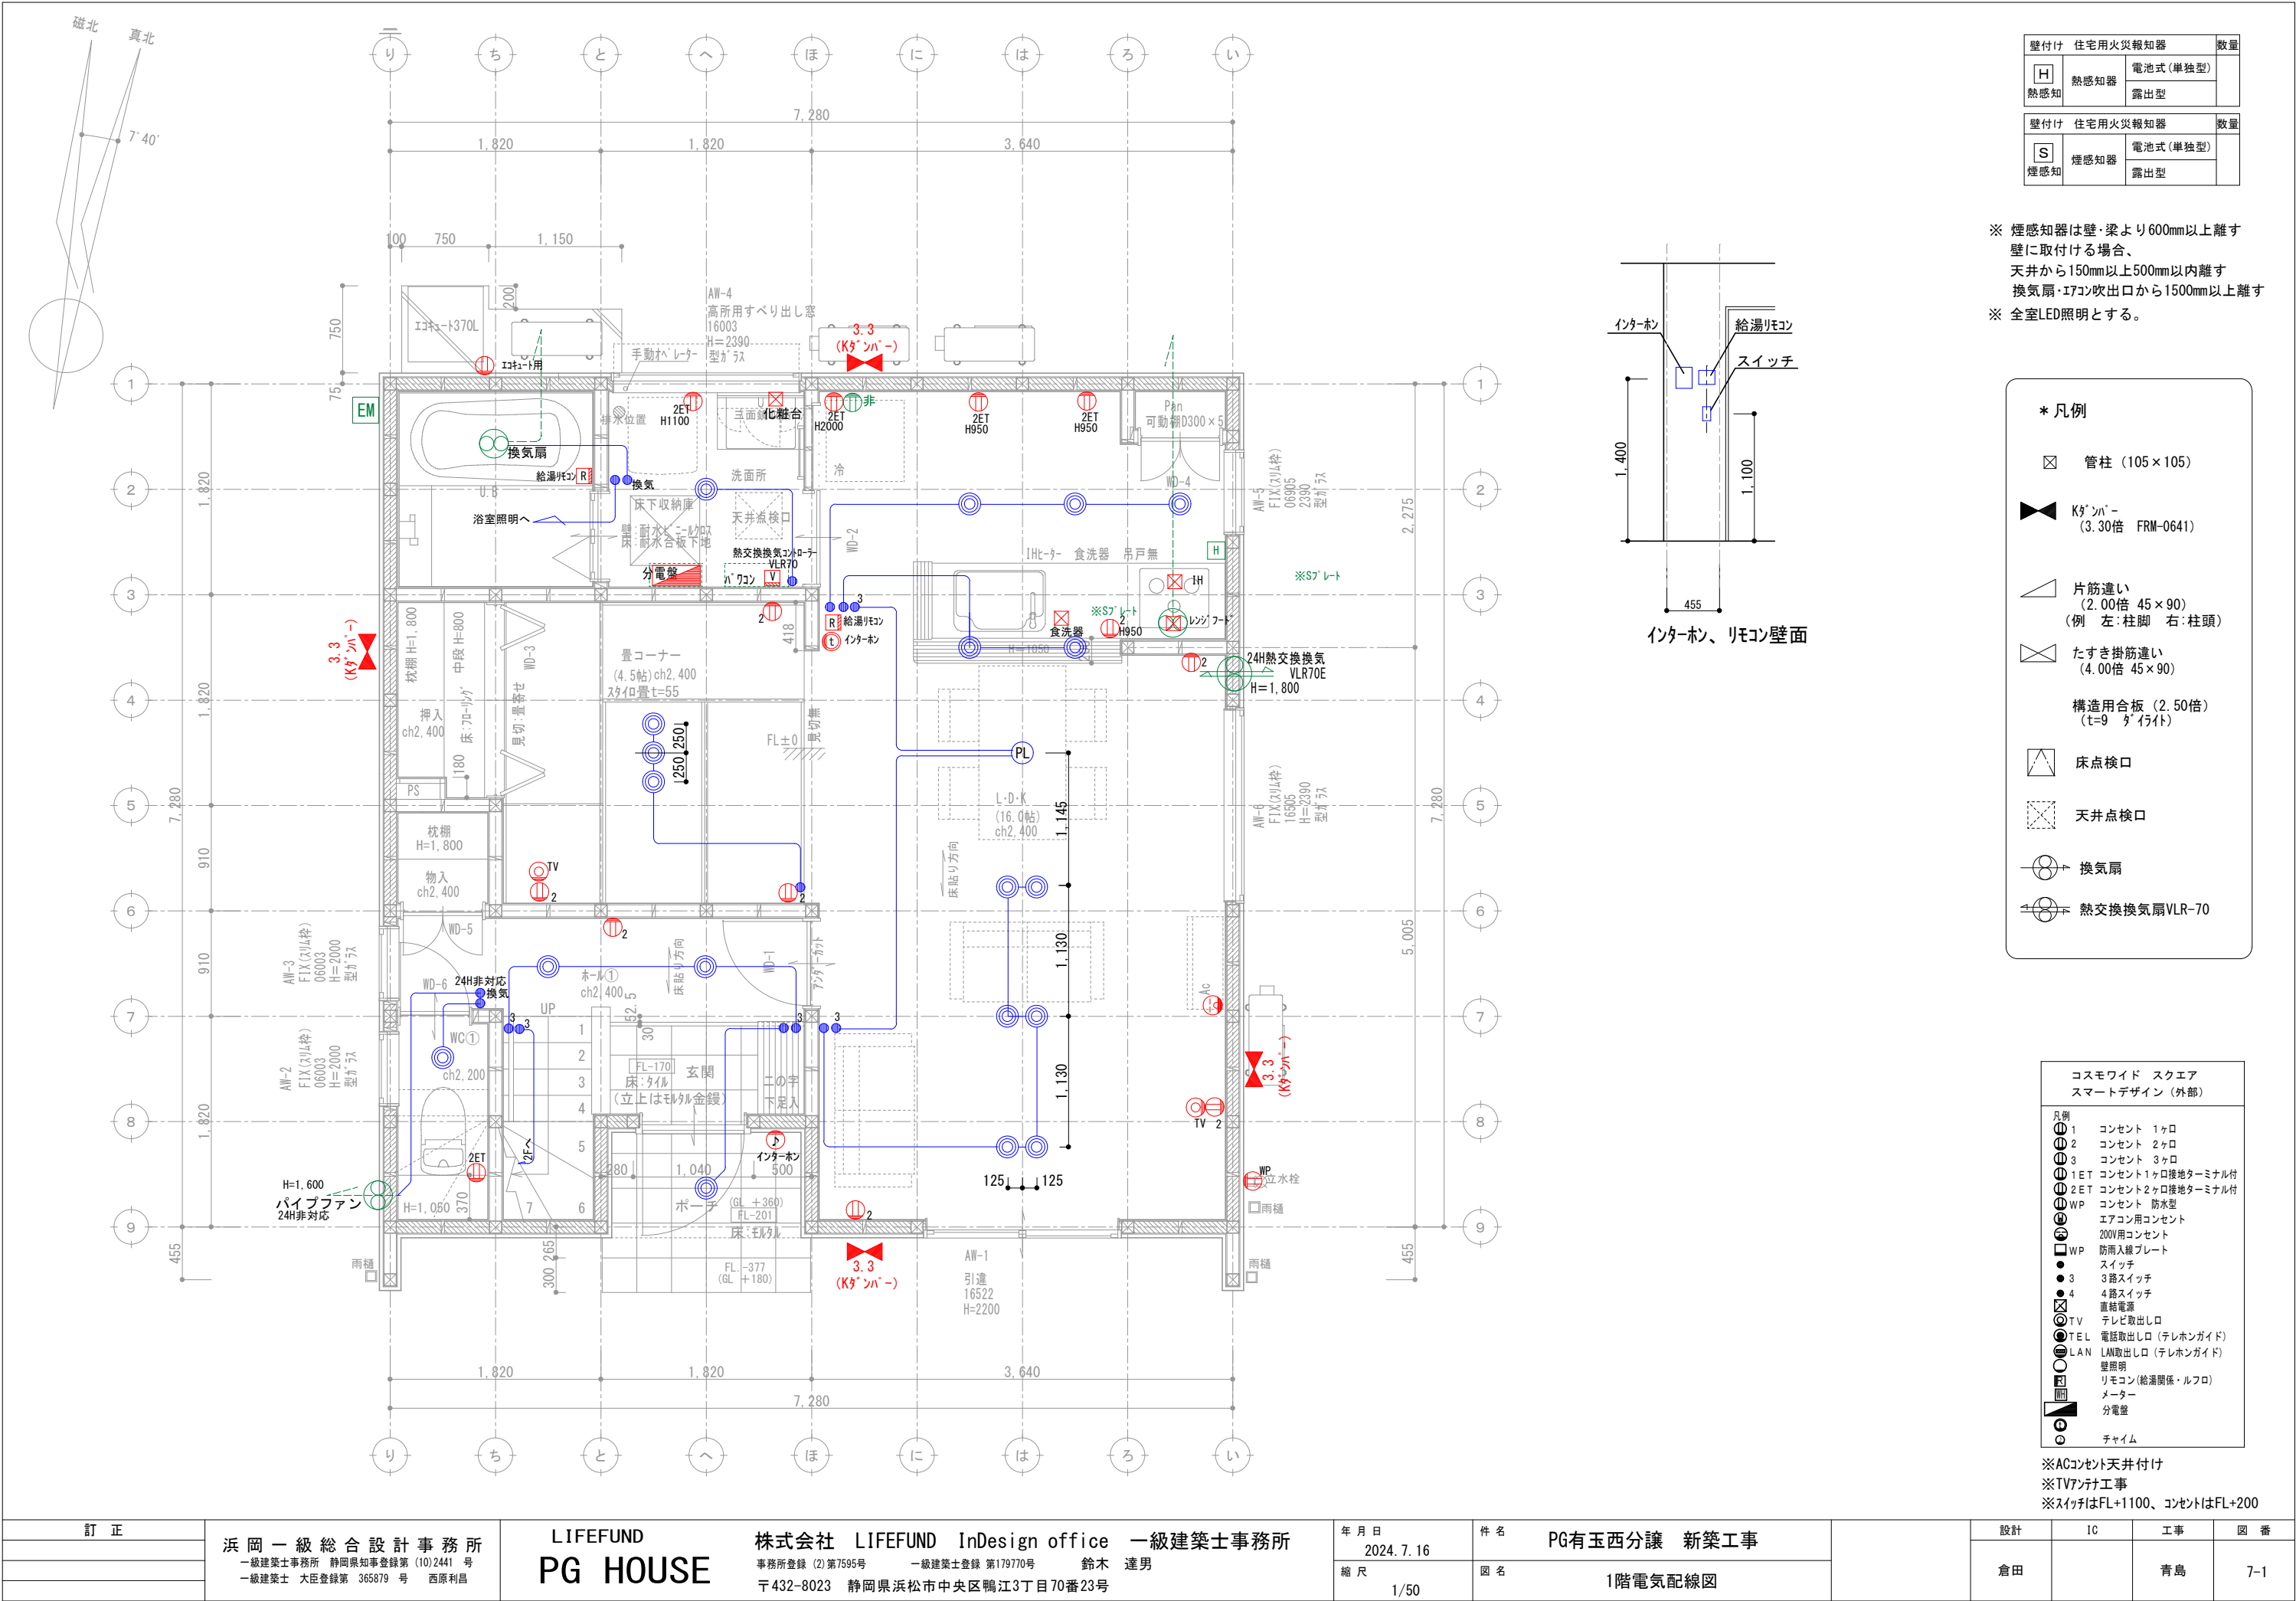

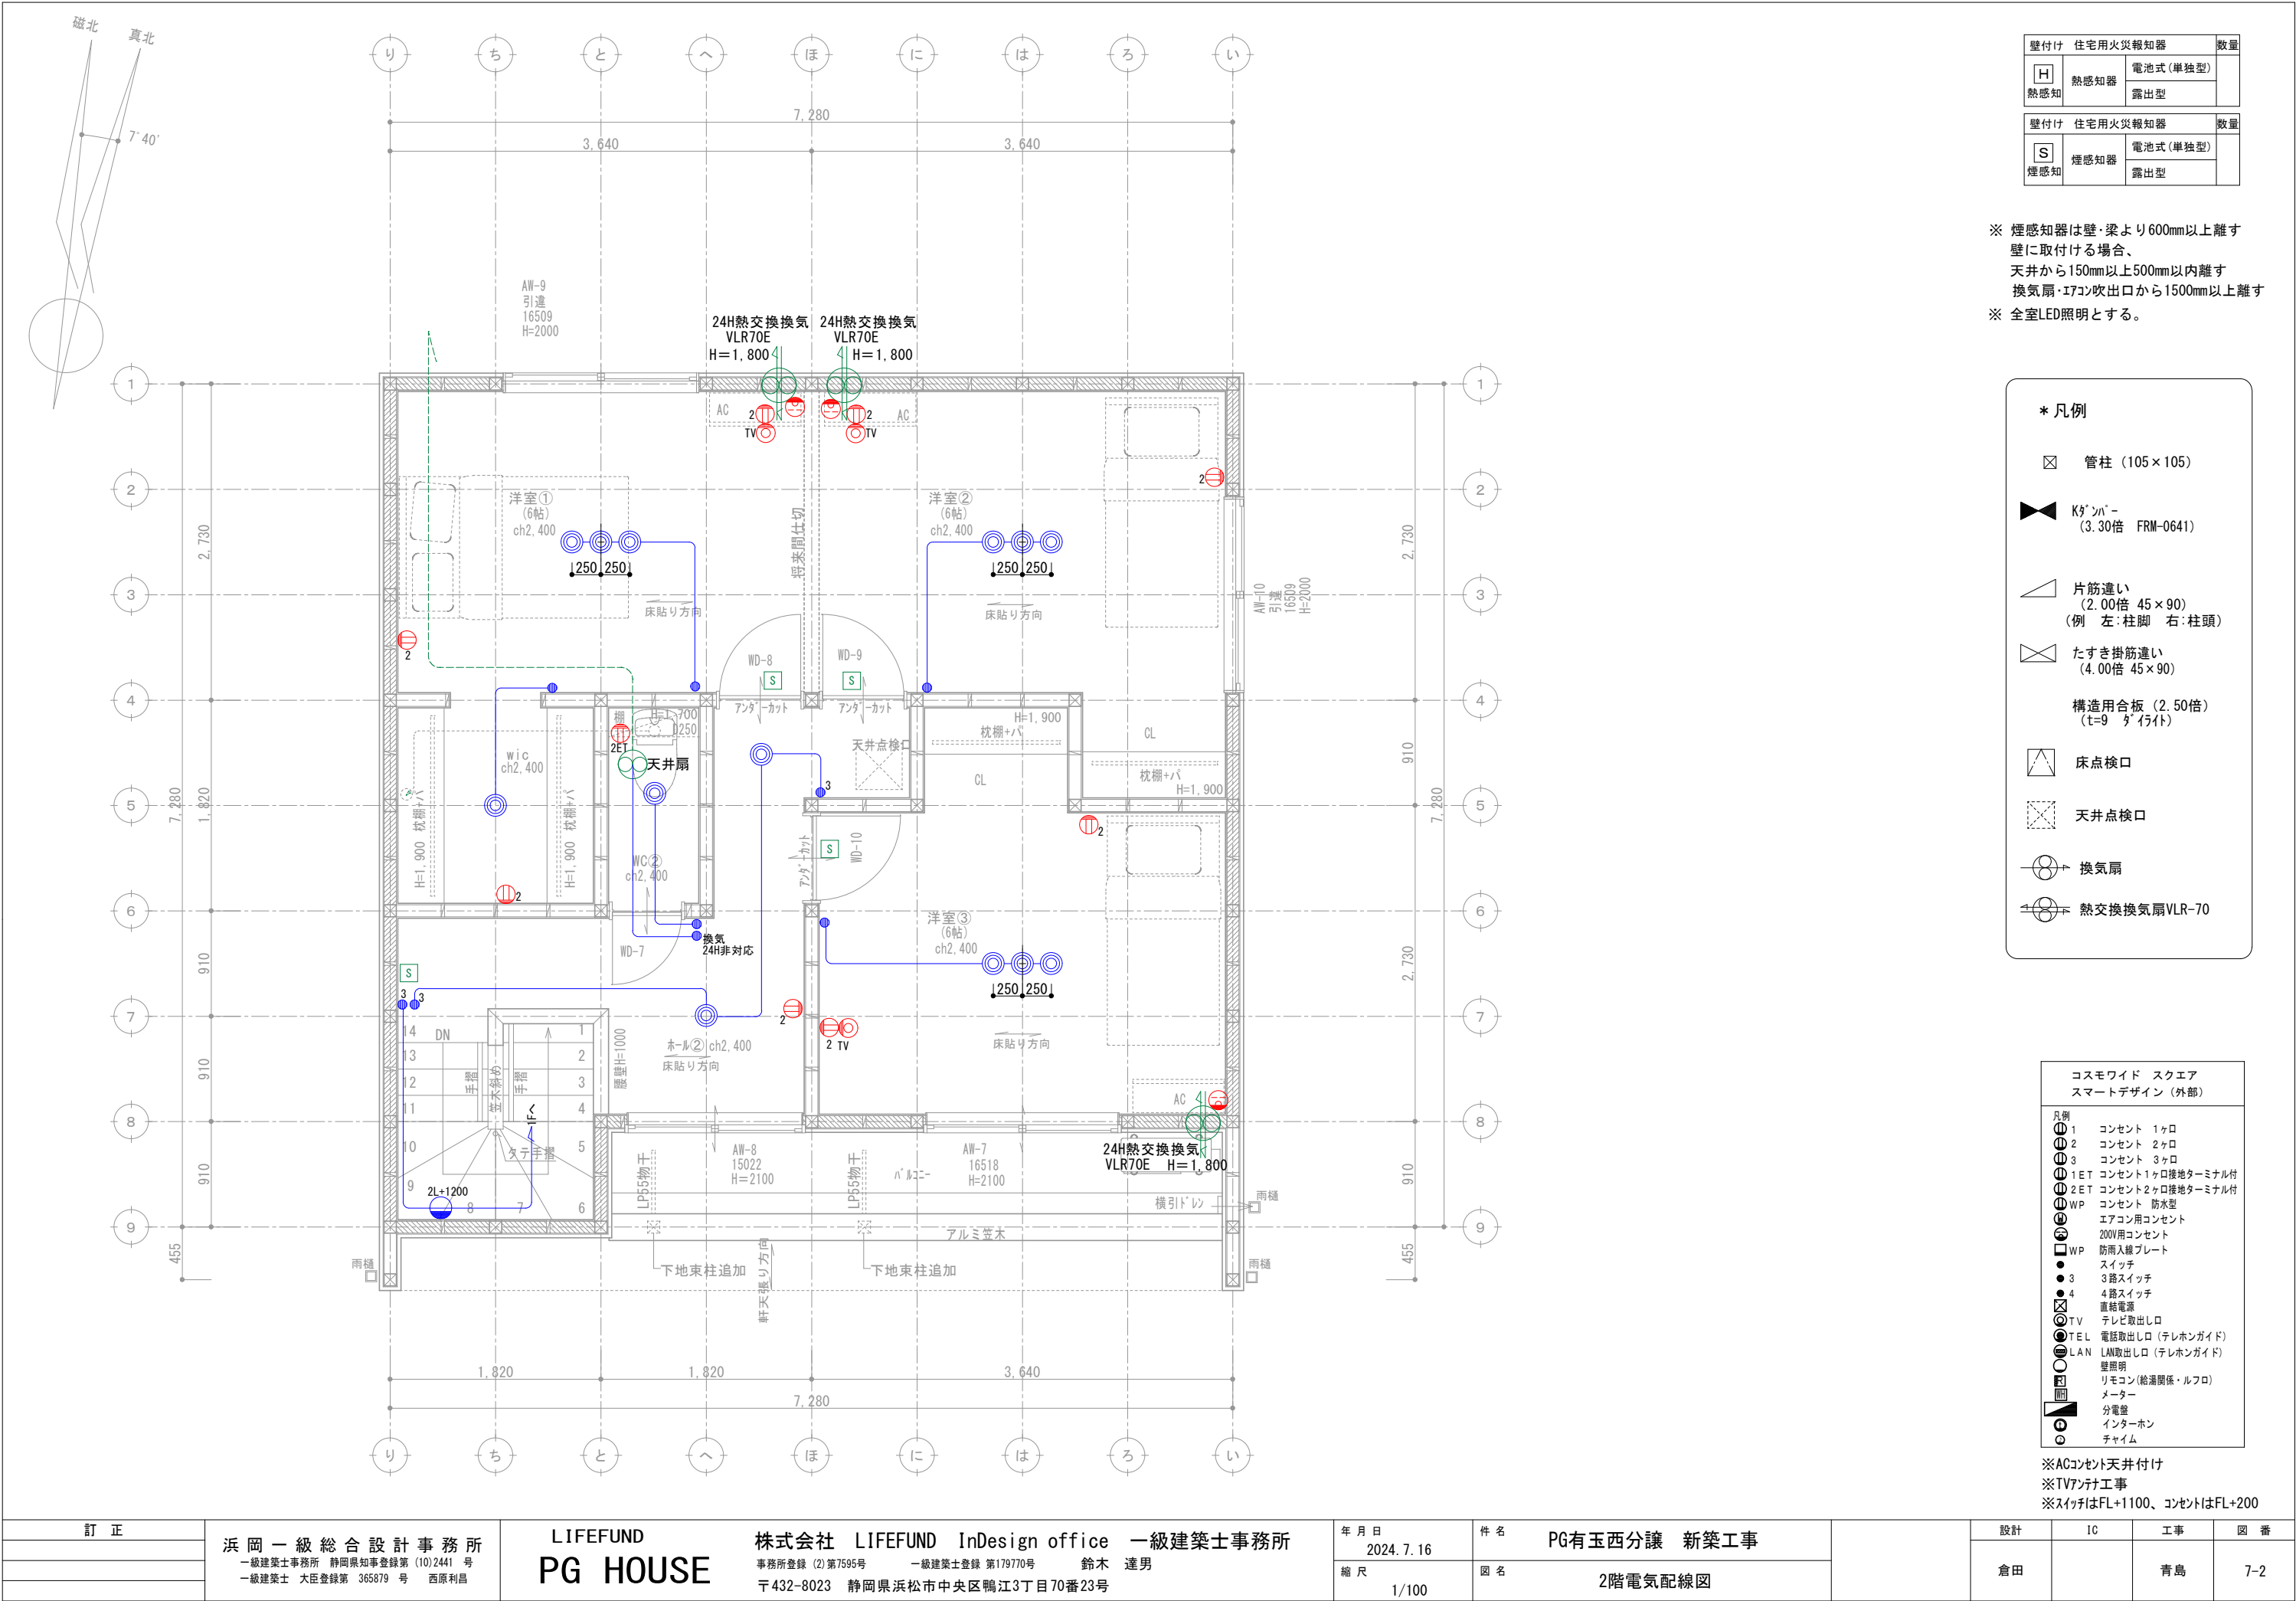

壁付け 住宅用火災報知器			数量
H 熱感知	電池式 (単独型)	露出型	
	露出型		

壁付け 住宅用火災報知器			数量
S 煙感知	電池式 (単独型)	露出型	
	露出型		

※ 煙感知器は壁・梁より600mm以上離す壁に取付ける場合、天井から150mm以上500mm以内離す換気扇・エアコン吹出口から1500mm以上離す

※ 全室LED照明とする。

* 凡例

管柱 (105×105)

Kダクト (3.30倍 FRM-0641)

片筋違い (2.00倍 45×90)
(例 左:柱脚 右:柱頭)

たすき掛筋違い (4.00倍 45×90)

構造用合板 (2.50倍)
(t=9 タイト)

床点検口

天井点検口

換気扇


熱交換換気扇 VLR-70

コスモワイド スクエア スマートデザイン (外部)		
凡例	1	コンセント 1ヶ所
	2	コンセント 2ヶ所
	3	コンセント 3ヶ所
	1ET	コンセント1ヶ所接地ターミナル付
	2ET	コンセント2ヶ所接地ターミナル付
	WP	コンセント 防水型
		エアコン用コンセント
		200V用コンセント
	WP	防雨入線プレート
		スイッチ
	3	3路スイッチ
	4	4路スイッチ
		直結電源
	TV	テレビ取出口
	TEL	電話取出口 (テレホンガイド)
	LAN	LAN取出口 (テレホンガイド)
		壁照明
		リモコン (給湯関係・ルフロ)
		メーター
		分電盤
		インターホン
		チャイム


※ACコンセント天井付け

※TVアンテナ工事

※スイッチはFL+1100、コンセントはFL+200

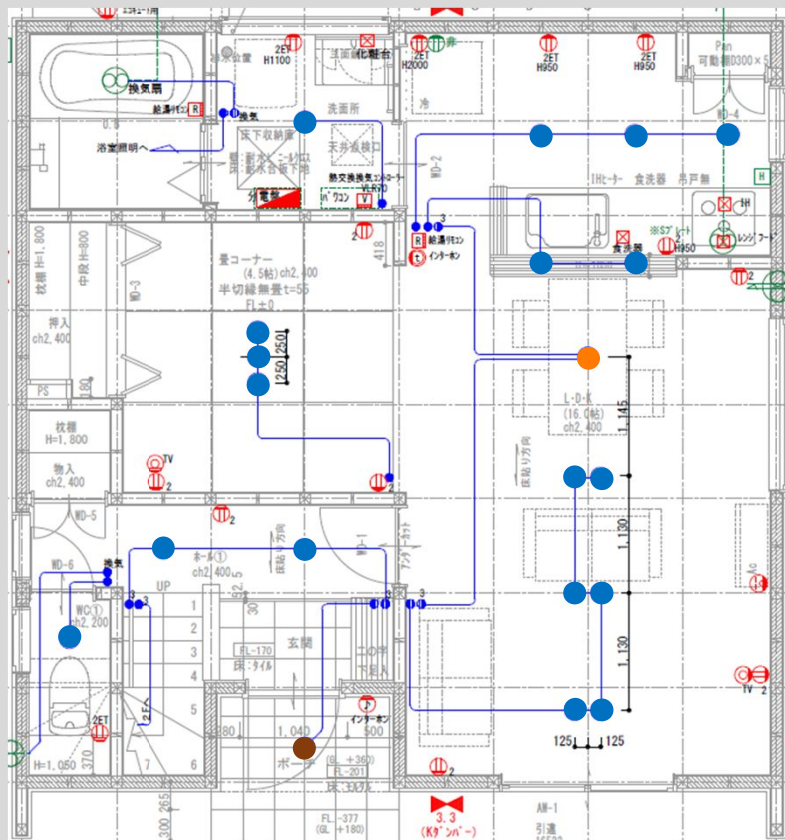

1 階

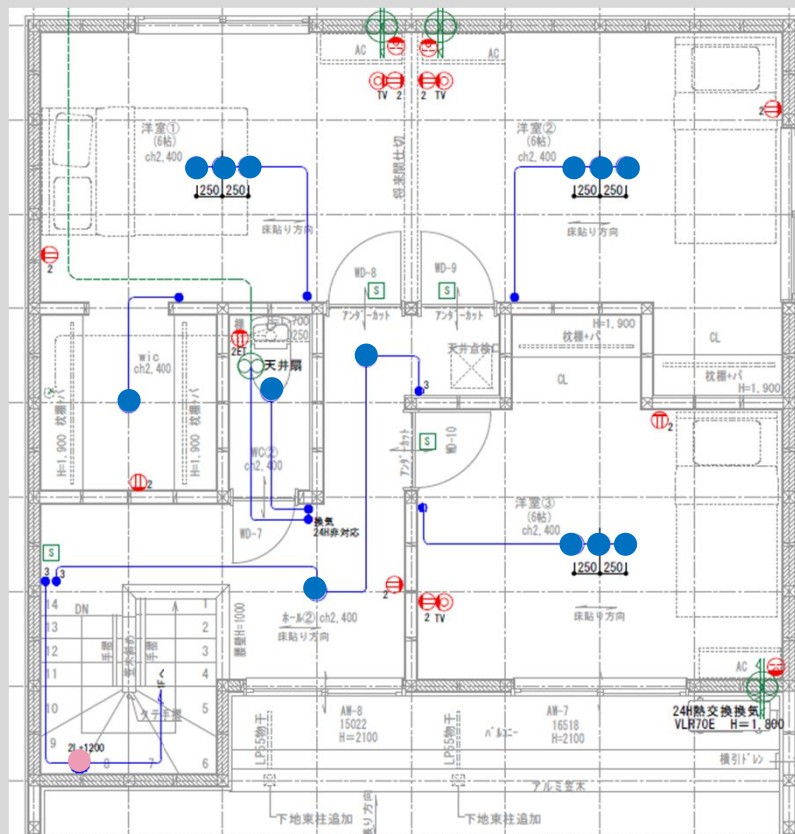

2 階

内部：コスモワイド スクエア(Panasonic)



ドアホン：VL-SZ30KL
(Panasonic)



外部：スマートデザインシリーズ (Panasonic)

表情豊かな住まいをつくり出すスマートデザインシリーズ。



ポーチ灯

● × 1

DDL-4496YW



基本照明ダウンライト

● × 31

DDL6102AW



ダイニングペンダント灯

● × 1

DPN41973




階段灯












● × 1

DBK41544Y



2024.07.16

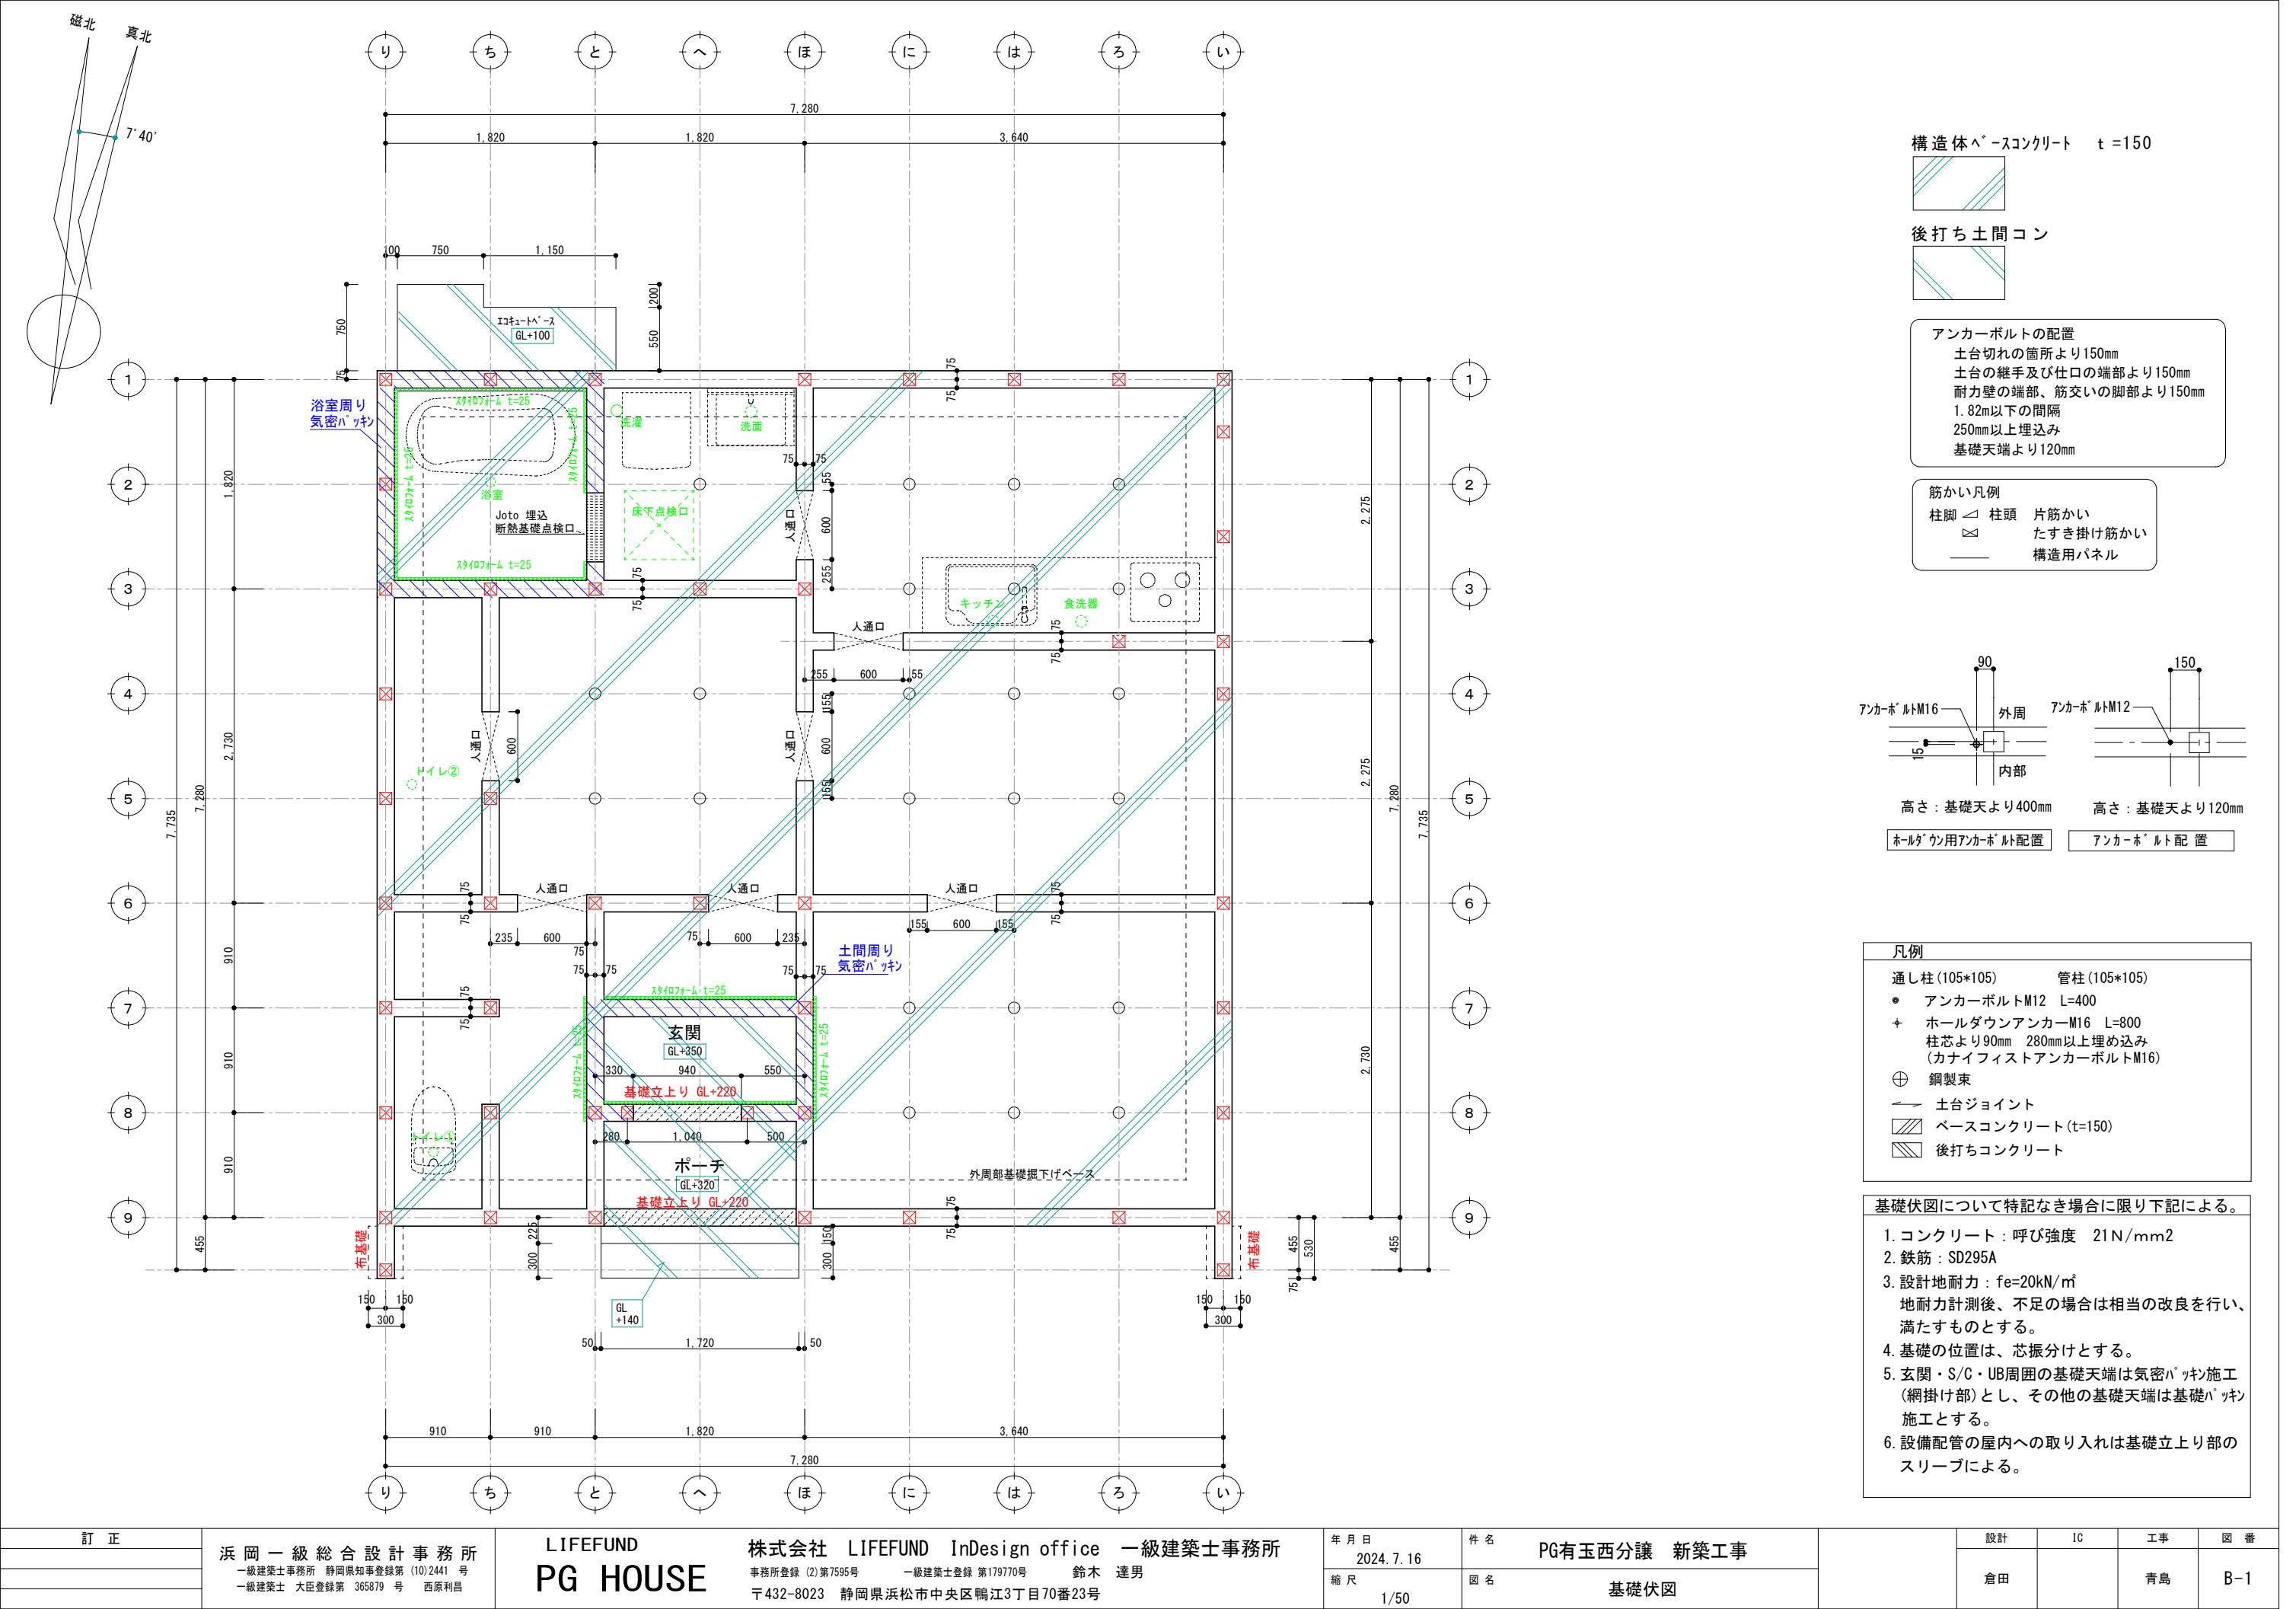

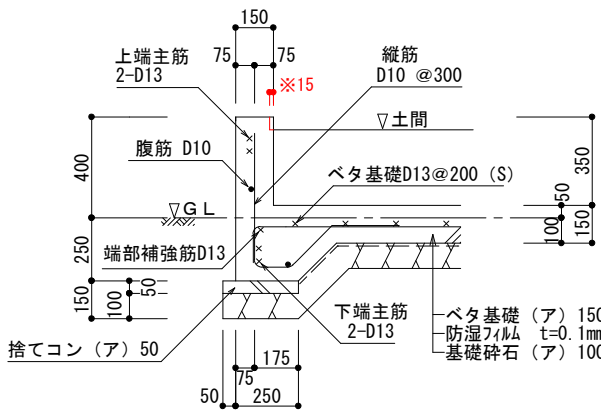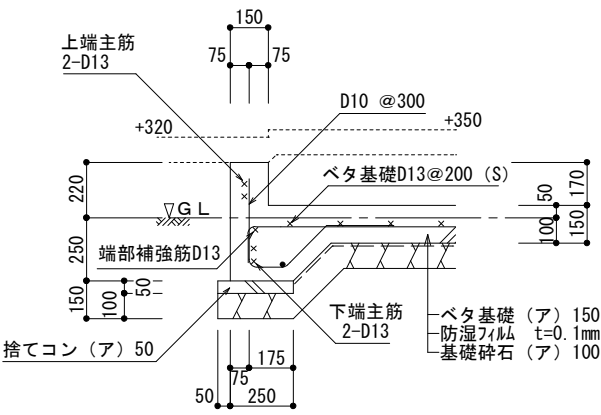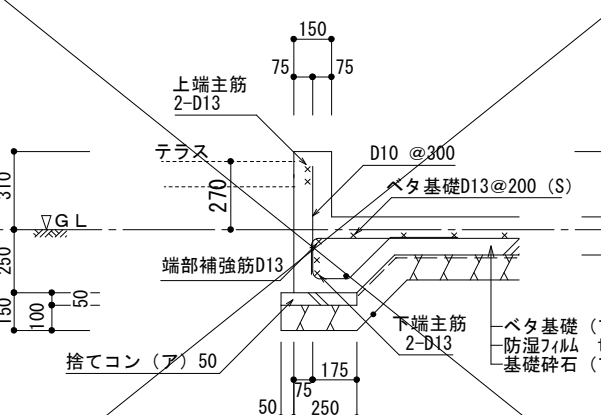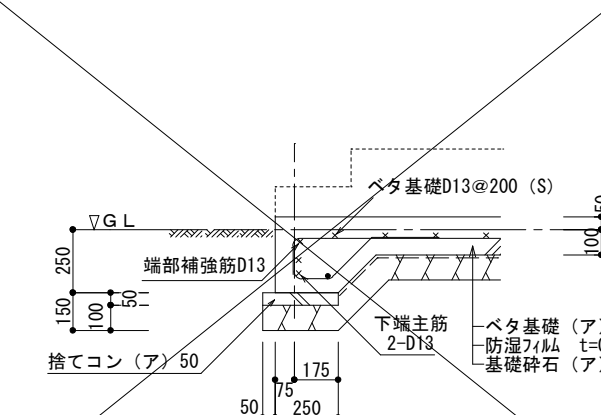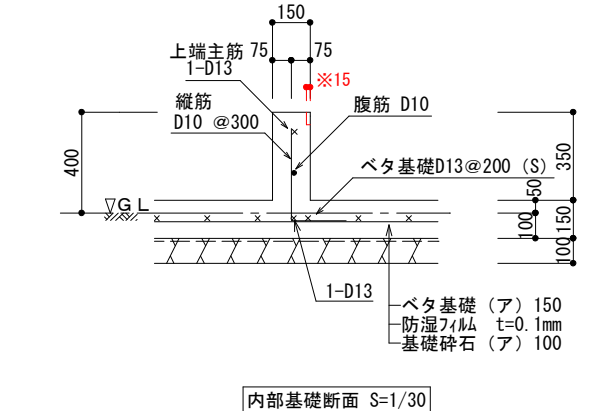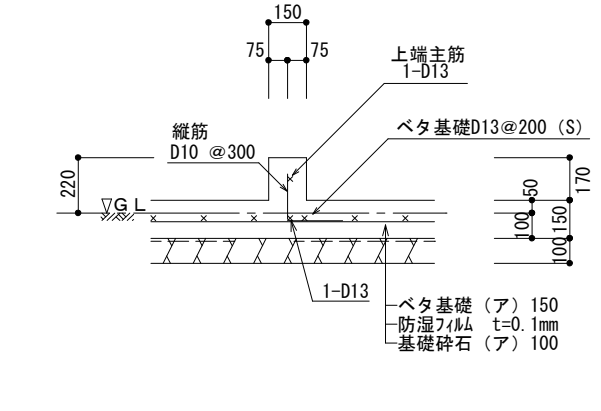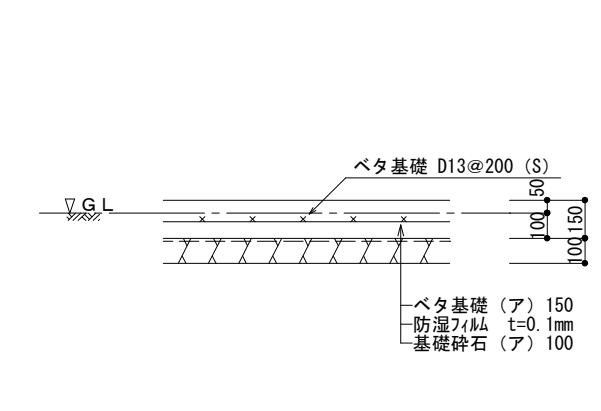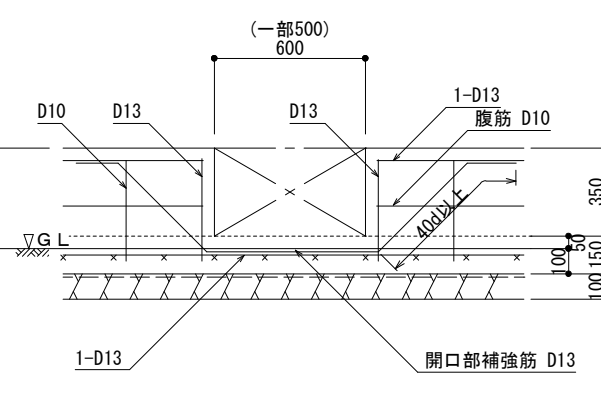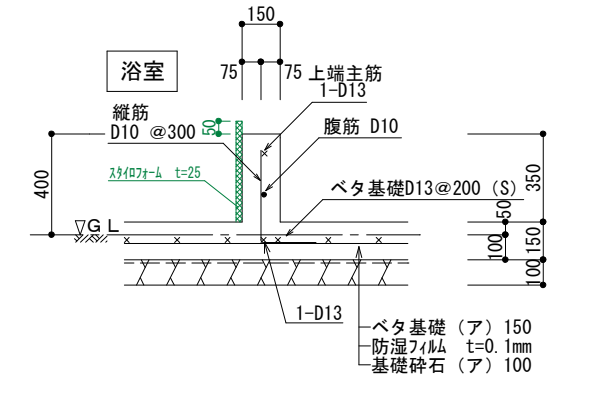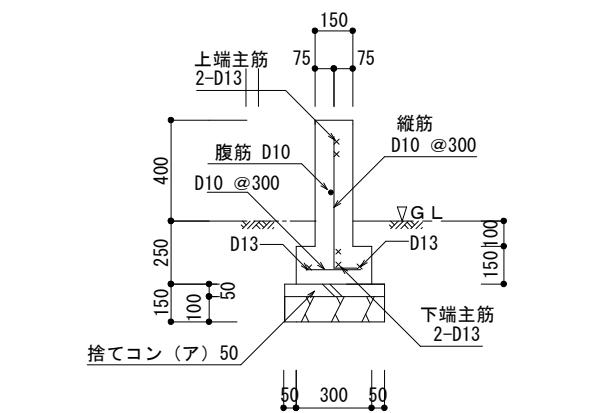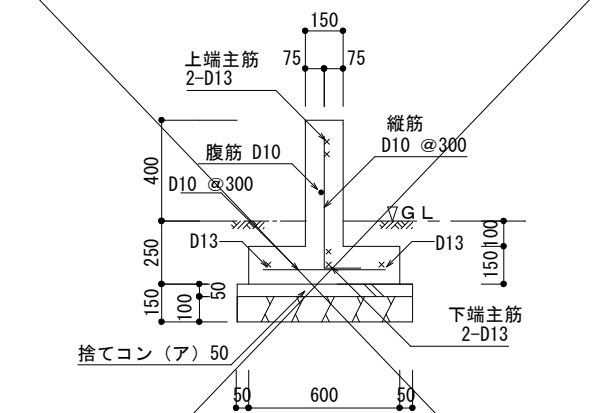 外周基礎断面 S=1/30 ※玄関内土間部分のみ15mm欠き込み	 ポーチ下 外周部基礎断面 S=1/30 倉庫ドア下 外周部基礎断面 S=1/30	 土間納め勝手口ドア下 外周部基礎断面 S=1/30	 立上り無しの基礎断面 S=1/30				
 内部基礎断面 S=1/30 ※玄関内土間部分のみ15mm欠き込み ※注意：基礎伏図に特記のない内部基礎の場合	 ポーチ下 内周部基礎断面 S=1/30 玄関ドア下 内周部基礎断面 S=1/30 玄関内横断基礎断面 S=1/30	 ベタ基礎断面 S=1/30	 人通口補強 S=1/30				
 浴室内部基礎断面 S=1/30 ※注意：基礎伏図に特記のない内部基礎の場合	 布基礎A：袖壁用 基礎断面 S=1/30	 布基礎B：底用独立 基礎断面 S=1/30	<table><tr><td>基礎の寸法 及び 配筋の検証方法</td><td>基礎立上り配筋は、 (財)日本住宅・木材技術 センター発行のスパン表 (増補版)による。 ベタ基礎スラブ配筋は、 まもりすまい保険設計施工 基準同解説のベタ基礎配筋表 による。具体的な寸法・配 筋は基礎詳細図参照。</td></tr></table> 鉄筋断面表記 ●・・・D10を示す。 ×・・・D13を示す。 ※使用しない断面は×を記入。	基礎の寸法 及び 配筋の検証方法	基礎立上り配筋は、 (財)日本住宅・木材技術 センター発行のスパン表 (増補版)による。 ベタ基礎スラブ配筋は、 まもりすまい保険設計施工 基準同解説のベタ基礎配筋表 による。具体的な寸法・配 筋は基礎詳細図参照。		
基礎の寸法 及び 配筋の検証方法	基礎立上り配筋は、 (財)日本住宅・木材技術 センター発行のスパン表 (増補版)による。 ベタ基礎スラブ配筋は、 まもりすまい保険設計施工 基準同解説のベタ基礎配筋表 による。具体的な寸法・配 筋は基礎詳細図参照。						
訂正	浜岡一級総合設計事務所 一級建築士事務所 静岡県知事登録第(10)2441号 一級建築士 大臣登録第365879号 西原利昌	LIFEFUND PG HOUSE	株式会社LIFEFUND InDesign office 一級建築士事務所 事務所登録 (2)第7595号 一級建築士登録 第179770号 鈴木 達男 〒432-8023 静岡県浜松市中央区鴨江3丁目70番23号	年月日 2024.07.16 縮尺 1/30	件名 PG有玉西分譲 新築工事 図名 基礎断面リスト		設計 倉田 I C 工務 青島 図番 B-2

Aritama-model house project



Construction Name

■PG有玉西 分譲

Place

浜松市中央区有玉西町2135-34

Data

Date

2024. 7. 16

Sign

Scale



InDesign office
一級建築士事務所

3-70-23 kamoe-, Hamamatsu Naka-ku, Shizuoka, JAPAN
Tel 053-485-8910 Fax 053-485-8911