

■ 仕 様		■ HEAT20 G1
断熱工事	■ 床:カネライトフォーム t65 ■ 土間床等の外周:スタイロフォームAT t25 ■ 壁:アクアフォームLITE吹付 t85 ■ 天井:アクアフォームLITE吹付 t170	
床下換気	■ 基礎パッキン JOTO (玄関・UB周り:気密基礎パッキン)	
防虫防蟻	■ 土壌処理・木部 ガントナーMC	

■ 外 部 仕 上 表			■ 22条地域
部位		仕上・仕様・メーカー	色番・品番
屋根		■ ガルバリウム鋼板(t0.35)UK立平 ニスクカラーPro GH 軒先 金物 日本住環境REV-15	GHK01 Sブラック
パラペット笠木		■ なし	
破風・鼻隠		■ なし	
雨樋	(軒樋)	■ Panasonic サーフeskエアFS-I型	ミルクホワイト
	(縦樋)	■ Panasonic S30角樋	ミルクホワイト
軒天	屋根軒	■ ニチハ軒天5 木目調 910×1820×5	ライト
	ポーチ軒	■ 神島化学 t= 6mm 軒天ボード エンボス	Wファリーホワイト
	バルコニー軒	■ なし	
オーバーハング水切り		■ ガルバリウム鋼板 ※外壁合わせ JOTO:HF-A3550	ホワイト
外壁	通気金物(15mm)	■メイン ニチハ エモンエクセラード16 Vシリーズ しぶきV	MGバニラホワイトII
	※下地面材:タイガーEXハイパー	■アクセントA なし	
	防火認定 PC030BE-4028	■アクセントB なし	
玄関ポーチ		■ 床 LIXILパセオ300/PSO-FIO 4	-
基礎		■ 立上り巾木: モルタル刷毛引き	-
基礎水切り金物		■ JOTO鋼板製 防鼠材付き水切り JOTO:WMF-N35	ホワイト
バルコニー	床・内壁	■ 床:FRP防水仕上(グレー) 壁:外壁同仕上げ	-
	笠木	■ アルミ笠木	ブラック
外部建具		■ Ykkap APW330 (アルゴンガス日射遮蔽型 断熱タイプLow-E ブルー) ・SD、TSで記載がないものは、オペレーターハンドルとする ・オペレーター付サッシは固定網戸とする ・グレモンハンドル式サッシの選択箇所は可動網戸とする	外観 ブラック 内観 外観色と同じ ※網戸付 樹脂スペーサ
シャッター		■ なし	
壁体通気水切り		FVK-415F JOTO ※軒天換気兼用	ホワイト
玄関扉		■ YKKapヴェナートD30(D2仕様) タグキーx3、非常用キーx2 (電池式) ※ヒョットキー	ドア型: N08N ドア色: ガナッシュウォールナット ハンドル: ストレート 色: ブラック
外部物干し金物		■ 川口技研LP型-550 バルコニー内側壁	ホワイト
換気フード	■ 局所換気扇(トイレ 浴室 キッチンフード) 防火ダンパー無		外気フード: ホワイト
	■ ダクトレス熱交換換気システム (日本スティーベル株式会社) VLR-70E 防火ダンパー無		外気フード: W ホワイト

■ 構 造 概 要			
基礎	■ RCベタ基礎コンクリート		
通し柱・管柱	■ 構造用集成材 105×105		間柱 ■ 集成材
土台	■ 桧 105×105	大引き ■ 桧 90*90	筋交い ■ 構造用製材 火打梁 ■ 鋼製火打(当社基準により米松あり)
桁・梁	■ 構造用製材及び集成材		制震装置 ■ Kダンパー (株)アイ・エム・エー

■ 設 備 装 着 品				
住宅設備	部位	メーカー	商品名 ※ 詳細は見積り、プレゼン参照	見積りNo. (日付)
	キッチン	LIXIL	■ ES I型D650 食洗器 IH 壁付レンジフードASR	見積り番号 : M24074457351-003-2 (日付) 2024.7.25
	バックカウンタ ※オプション	LIXIL	■ なし	見積り番号 : (日付)
	浴室	LIXIL	■ AX1616 ※換気扇	見積り番号 : M24074457351-003-1 (日付) 2024.7.25
	1Fトイレ	LIXIL	■ ベーシアシャワートイレ 白 ● タオル掛け: KF-AA70D(リング) タンク手洗 有り ● 紙巻き器: CF-AA22H /WA	見積り番号 : M24074457351-003-4 (日付) 2024.7.25
	2Fトイレ	LIXIL	■ ベーシアシャワートイレ 白 ● タオル掛け: KF-AA70D(リング) タンク手洗 有り ● 紙巻き器: CF-AA22H /WA	見積り番号 : M24074457351-003-5 (日付) 2024.7.25
	洗面台	LIXIL	■ EV W750(D500タイプ) 扉:グロスホワイト [引出しタイプ シングルハンドシャワー スタンダードLED三面鏡 ● タオル掛け: KF-AA71D(バー)]	見積り番号 : M24074457351-003-3 (日付) 2024.7.25
給排水設備	給湯器		■ エコキュート370L Panasonic NSシリーズ スタンダードモデル 追い焚きフルオート	
	排水		■ 下水	
	外水栓		■ 1 カ所 (平面図参照) ■ 外部立栓柱: PVC製 水栓柱12型【前澤化成工業】	
	外部ガーデンパン		■ 無し	
	その他		■ 洗濯機用単水栓: 緊急止水弁付 ■ 洗濯機用排水:トラップ金物(標準) ■ 排水さや管(長期優良住宅仕様)	
ガス配管設備			■ なし (平面図参照)	
電気設備	インターホン		■ パナソニック VL-SZ30KL	
	TVアンテナ		■ UHF + BS・110度CS／CSアンテナ [2K・4K・8K対応] ■ホワイト	
	エアコン		■ あり 設置場所: LDK 洋室②	
	ソーラー ※標準搭載		■ あり(Qセルズ) 12 枚 5.22 KW Re.RISE-G2 435 (1722×1134×30)	
			■ 蓄電池:無	
その他				

	浜 岡 一 級 総 合 設 計 事 務 所 一級建築士事務所 静岡県知事登録第 (10)2441 号 一級建築士 大臣登録第 365879 号 西原利昌	LIFEFUND 株式会社 LIFEFUND InDesign office 一級建築士事務所 事務所登録 (2)第7595号 一級建築士登録 第179770号 鈴木 達男 〒432-8023 静岡県浜松市中央区鴨江3丁目70番23号	年 月 日	件名		設計	IC	工務	図 番
			2024.7.31	PG有玉西 分譲		倉田		青島	1-1
			縮尺	図面					
				仕上表 1					


内 部 仕 上 表（壁下地:石膏ボード12.5mm/天井下地:9.5mm）※脱衣室:床合板特類 下地									
階		床	巾木	壁	品番	廻 縁	天 井	品番	特記事項
1F	ポーチ	LIXIL/パセオ300/PSO-FIO 4							巾木立上り部はモルタル金鍍仕上
	玄関	LIXIL/パセオ300/PSO-FIO 4	ライン巾木(W)	ビニルクロス	SLP-250	突付	ビニルクロス	SLP-250	巾木立上り部はモルタル金鍍仕上
	ホール①	イタ銘木フロアーラステックt12 ブラックチェリー3P	ライン巾木(W)	ビニルクロス	SLP-250	突付	ビニルクロス	SLP-250	
	LDK	イタ銘木フロアーラステックt12 ブラックチェリー3P	ライン巾木(W)	ビニルクロス	SLP-250	突付	ビニルクロス	SLP-250	
	畳コーナー	1畳縁ありスタイロ畳 t55	畳寄せ	ビニルクロス	SLP-250	突付	ビニルクロス	SLP-250	畳縁:高田織物 浮No.13
	押入	イタ銘木フロアーラステックt12 ブラックチェリー3P	雑巾摺	ビニルクロス	SLP-250	突付	ビニルクロス	SLP-250	
	洗面所	フロアタイルt2.3 サンゲツIS-2070	H40ソフト巾木W97	ビニルクロス	SLP-250	突付	ビニルクロス	SLP-250	
2F	WC①	フロアタイルt2.3 サンゲツIS-2070	H40ソフト巾木W97	ビニルクロス	SLP-250	突付	ビニルクロス	SLP-250	
	ホール②	イタ銘木フロアーラステックt12 ブラックチェリー3P	ライン巾木(W)	ビニルクロス	SLP-250	突付	ビニルクロス	SLP-250	
	洋室①	イタ銘木フロアーラステックt12 ブラックチェリー3P	ライン巾木(W)	ビニルクロス	SLP-250	突付	ビニルクロス	SLP-250	
	洋室②	イタ銘木フロアーラステックt12 ブラックチェリー3P	ライン巾木(W)	ビニルクロス	SLP-250	突付	ビニルクロス	SLP-250	
	洋室③	イタ銘木フロアーラステックt12 ブラックチェリー3P	ライン巾木(W)	ビニルクロス	SLP-250	突付	ビニルクロス	SLP-250	
	WIC	イタ銘木フロアーラステックt12 ブラックチェリー3P	H40ソフト巾木W97	ビニルクロス	SLP-250	突付	ビニルクロス	SLP-250	
	WC②	フロアタイルt2.3 サンゲツIS-2070	H40ソフト巾木W97	ビニルクロス	SLP-250	突付	ビニルクロス	SLP-250	
	物入・収納・CL etc	※接続する部屋と同仕様とする							

上框&付框	■ LIXILラシッサS 付框30×150（全周廻し）色： クリエペール
階段	■ LIXIL KA 階段 ササラ： プレシャスホワイト 段板： クリエペール 蹴込板： プレシャスホワイト ラウト手摺： クリエペール 手摺金物 プレシャスホワイト 上段框： クリエペール 長尺笠木156： LIXIL クリエペール
窓枠 ※YKKap	■ YKKap窓枠スルムタイプ 色 ピュアプレーン ※浴室ドア枠 フクビ3方枠 []
キッチン笠木 カウンター	■ ゴム集成カウンター（オスモカラー）色 3062フロアクリアmatt 形状 L型（ジョイント加工） t=30
天井点検口	■ 天井アルミ点検口枠 450角 TAN45BW フクビ化学工業 ミルキーホワイト
床下収納庫	■ 高気密型床下点検口断熱型 SPF-R6060 城東テクノ 収納付 （脱衣室） アイボリー（IV）
トイレ棚	■ 2階トイレ D250 アートランパー棚（シェルホワイト）
室内物干し金物	■ なし
1トイレ バックカウンター	■ アートランパー棚（シェルホワイト） 色 t=20
下足入	■ LIXILラシッサS 色 プレシャスホワイト サイズ： W800 D400 形状： ニの字型


支給品	■ 無し
備考	

内 部 建 具 表							
LIXIL		建具色： クリエペール		枠色： 扉同色		※その他、下記特記による	
ラシッサS(標準)		把手： スクエアL(シャインニッケル) 丁番 固定枠(156) 外付戸当り ガイドピン床色合せ 引戸のみ上吊W7フタモーション					
階	No	室名	形式	枠外W サイズ	デザイン	枠色	特記事項
				枠外H サイズ	建具色	把手	
1	1	LDK	片開き戸	—	LGC	—	
	WD			2000	—	—	
	2	洗面所	片引き戸	—	LAA	—	明り窓・表示錠
	WD			2000	—	—	
	3	押入	折れ戸	—	LAA	—	角型Lタテ取付
	WD			2000	—	—	
	4	パントリー	観音開	—	LAA	—	
	WD			2000	—	—	
	5	物入	観音開	—	LAA	—	
	WD			2000	—	—	
	6	WC①	片開き戸	—	LAA	—	明り窓・表示錠
	WD			2000	—	—	
2	7	WC②	片開き戸	—	LAA	—	明り窓・表示錠
	WD			2000	—	—	
	8	洋室①	片開き戸	—	LAA	—	
	WD			2000	—	—	
	9	洋室②	片開き戸	—	LAA	—	
	WD			2000	—	—	
	10	洋室③	片開き戸	—	LAA	—	
	WD			2000	—	—	

	浜 岡 一 級 総 合 設 計 事 務 所 一級建築士事務所 静岡県知事登録第 (10)2441 号 一級建築士 大臣登録第 365879 号 西原利昌	LIFEFUND 株式会社 LIFEFUND InDesign office 一級建築士事務所 PG HOUSE 事務所登録 (2) 第7595号 一級建築士登録 第179770号 鈴木 達男 〒432-8023 静岡県浜松市中央区鴨江3丁目70番23号	年 月 日	件名		設計	IC	工務	図 番
			2024.7.31	PG有玉西 分譲		倉田	0	青島	1-2
			縮尺	図面					
				仕上表 2					

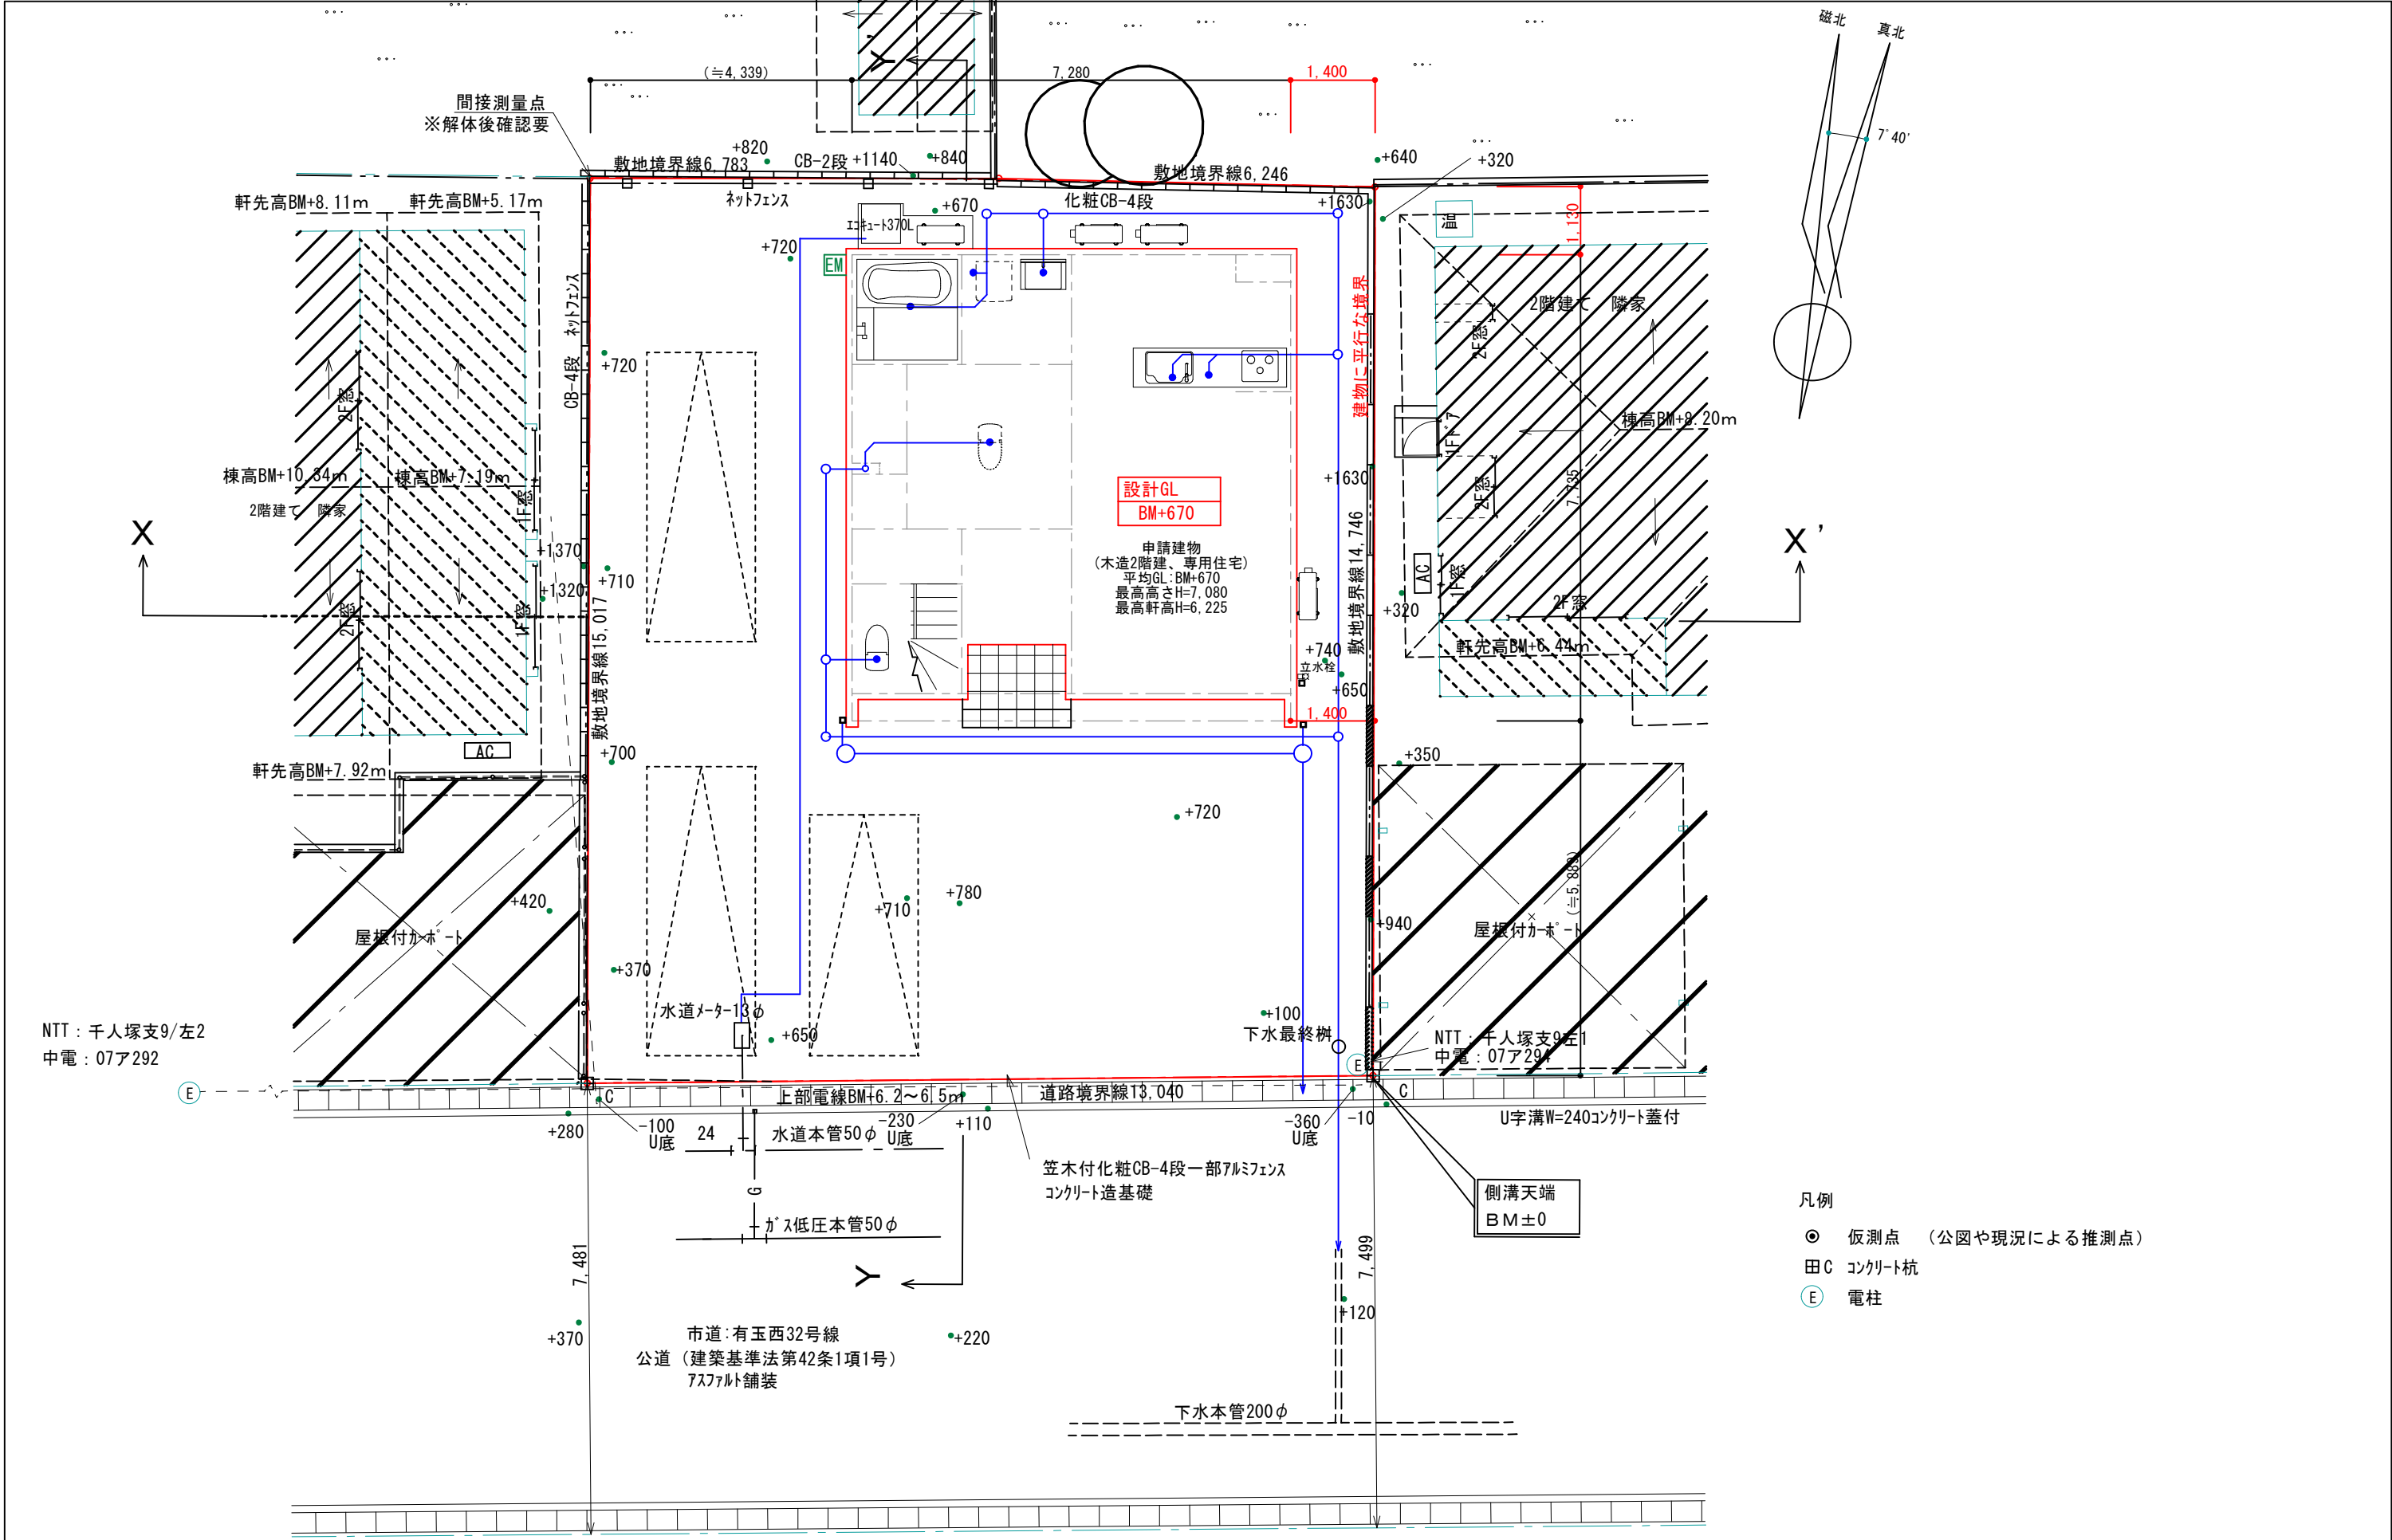

訂正	浜岡一級総合設計事務所 一級建築士事務所 静岡県知事登録第 (10) 2441 号 一級建築士 大臣登録第 365879 号 西原利昌	LIFEFUND PG HOUSE	株式会社 LIFEFUND InDesign office 一級建築士事務所 事務所登録 (2) 第7595号 一級建築士登録 第179770号 鈴木 達男 〒432-8023 静岡県浜松市中央区鴨江3丁目70番23号	年月日 2024. 7. 31	件名 PG有玉西分譲 新築工事		設計	IC	工事	図番
				縮尺 1/50	図名 配置図		倉田		青島	2-1

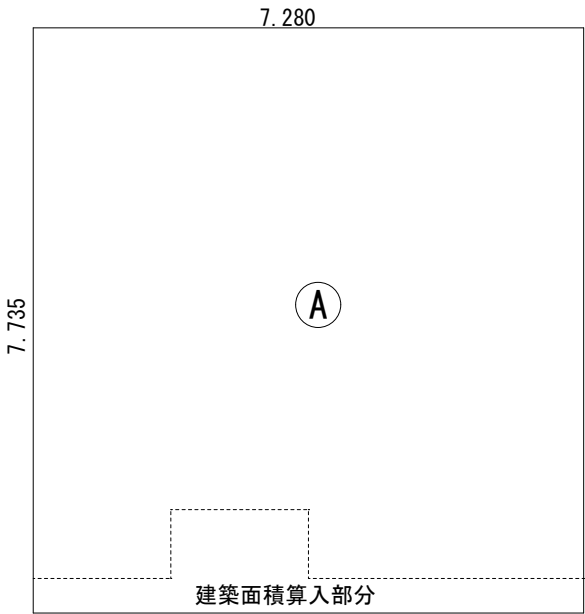


建築面積求積図 S=1/100

建築面積求積表

番号	計算式	(m)	面積 (㎡)
㊦	7.280 × 7.735		56.3108
合計			56.3108 56.31


(17.0坪)

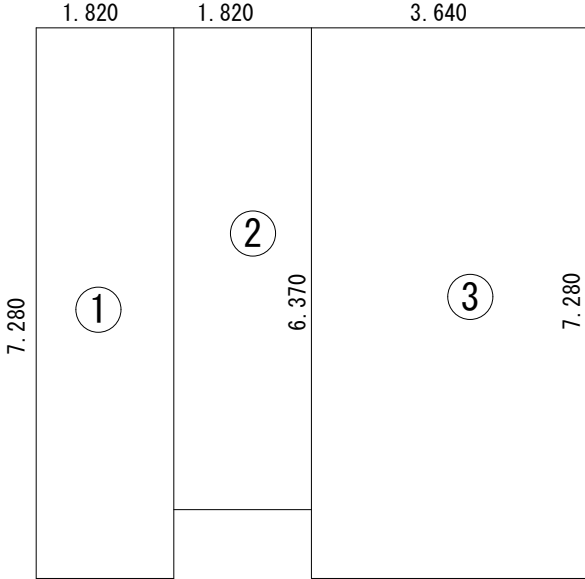

1階床面積図 S=1/100

1階床面積求積表

番号	計算式	(m)	面積 (㎡)
①	1.820 × 7.280		13.2496
②	1.820 × 6.370		11.5934
③	3.640 × 7.280		26.4992
合計			51.3422 51.34

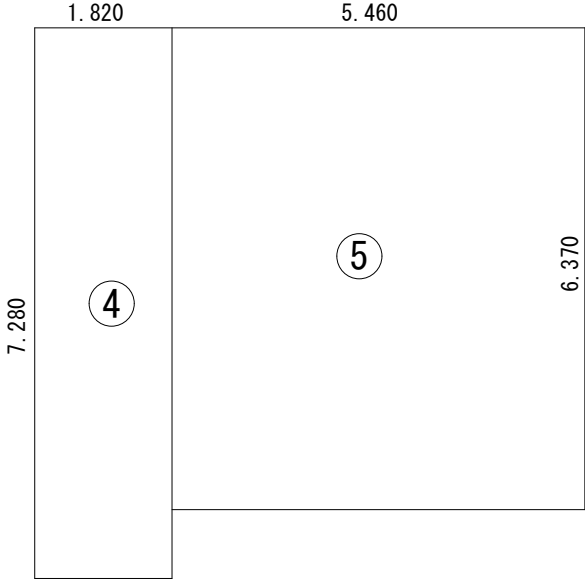

2階床面積図 S=1/100


2階床面積求積表

番号	計算式	(m)	面積 (㎡)
④	1.820 × 7.280		13.2496
⑤	5.460 × 6.370		34.7802
合計			48.0298 48.02

延べ床面積表

	番号	(m)	面積 (㎡)
1階床面積	① ② ③		51.34
2階床面積	④ ⑤		48.02
合計			99.36

(30.0坪)

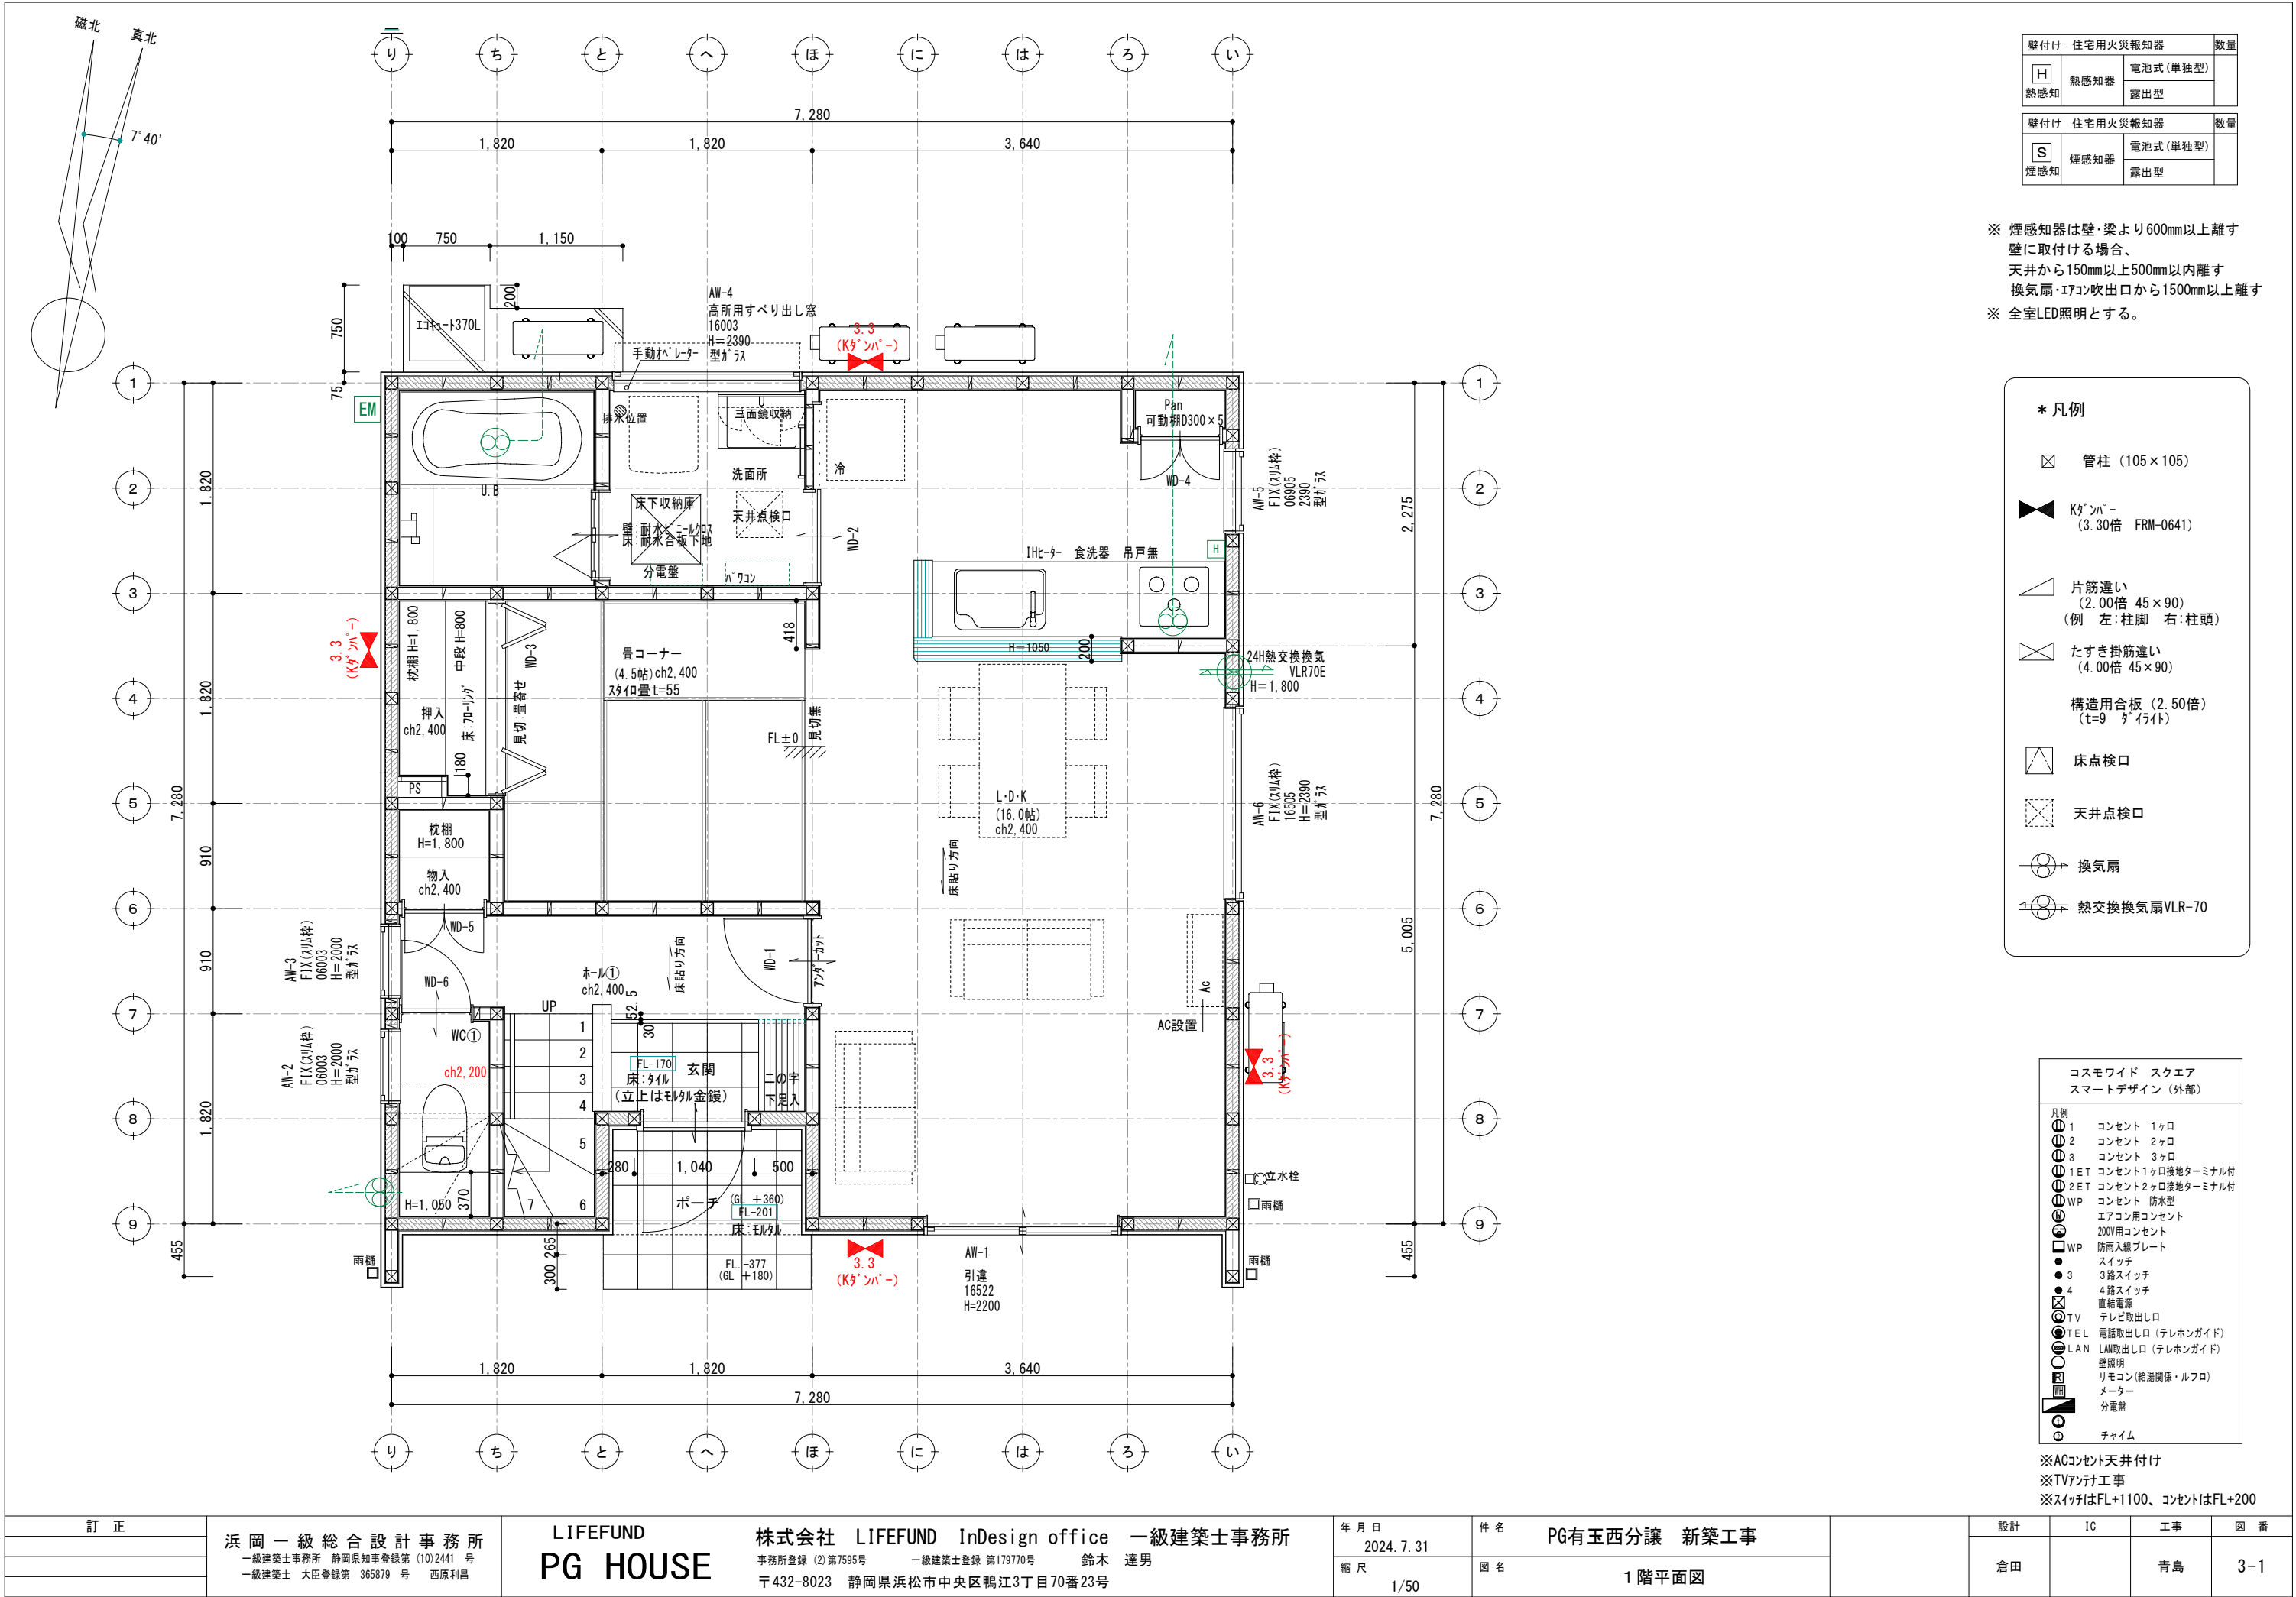

壁付け 住宅用火災報知器			数量
H 熱感知	電池式 (単独型)		
	露出型		
壁付け 住宅用火災報知器			数量
S 煙感知	電池式 (単独型)		
	露出型		

※ 煙感知器は壁・梁より600mm以上離す
壁に取付ける場合、
天井から150mm以上500mm以内離す
換気扇・エアコン吹出口から1500mm以上離す
※ 全室LED照明とする。

*** 凡例**

管柱 (105×105)

Kダクト (3.30倍 FRM-0641)

片筋違い (2.00倍 45×90)
(例 左:柱脚 右:柱頭)

たすき掛筋違い (4.00倍 45×90)

構造用合板 (2.50倍)
(t=9 タイト)

床点検口


天井点検口

換気扇

熱交換換気扇VLR-70

コスモワイド スクエア スマートデザイン (外部)			
凡例	1	コンセント	1ヶ所
2	コンセント	2ヶ所	
3	コンセント	3ヶ所	
1ET	コンセント1ヶ所接地ターミナル付		
2ET	コンセント2ヶ所接地ターミナル付		
WP	コンセント 防水型		
	エアコン用コンセント		
	200V用コンセント		
WP	防雨入線プレート		
	スイッチ		
3	3路スイッチ		
4	4路スイッチ		
	直結電源		
TV	テレビ取出口		
TEL	電話取出口 (テレホンガイド)		
LAN	LAN取出口 (テレホンガイド)		
	壁照明		
	リモコン (給湯関係・ルフロ)		
	メーター		
	分電盤		
	チャイム		

※ACコンセント天井付け
※TVアンテナ工事
※スイッチはFL+1100、コンセントはFL+200

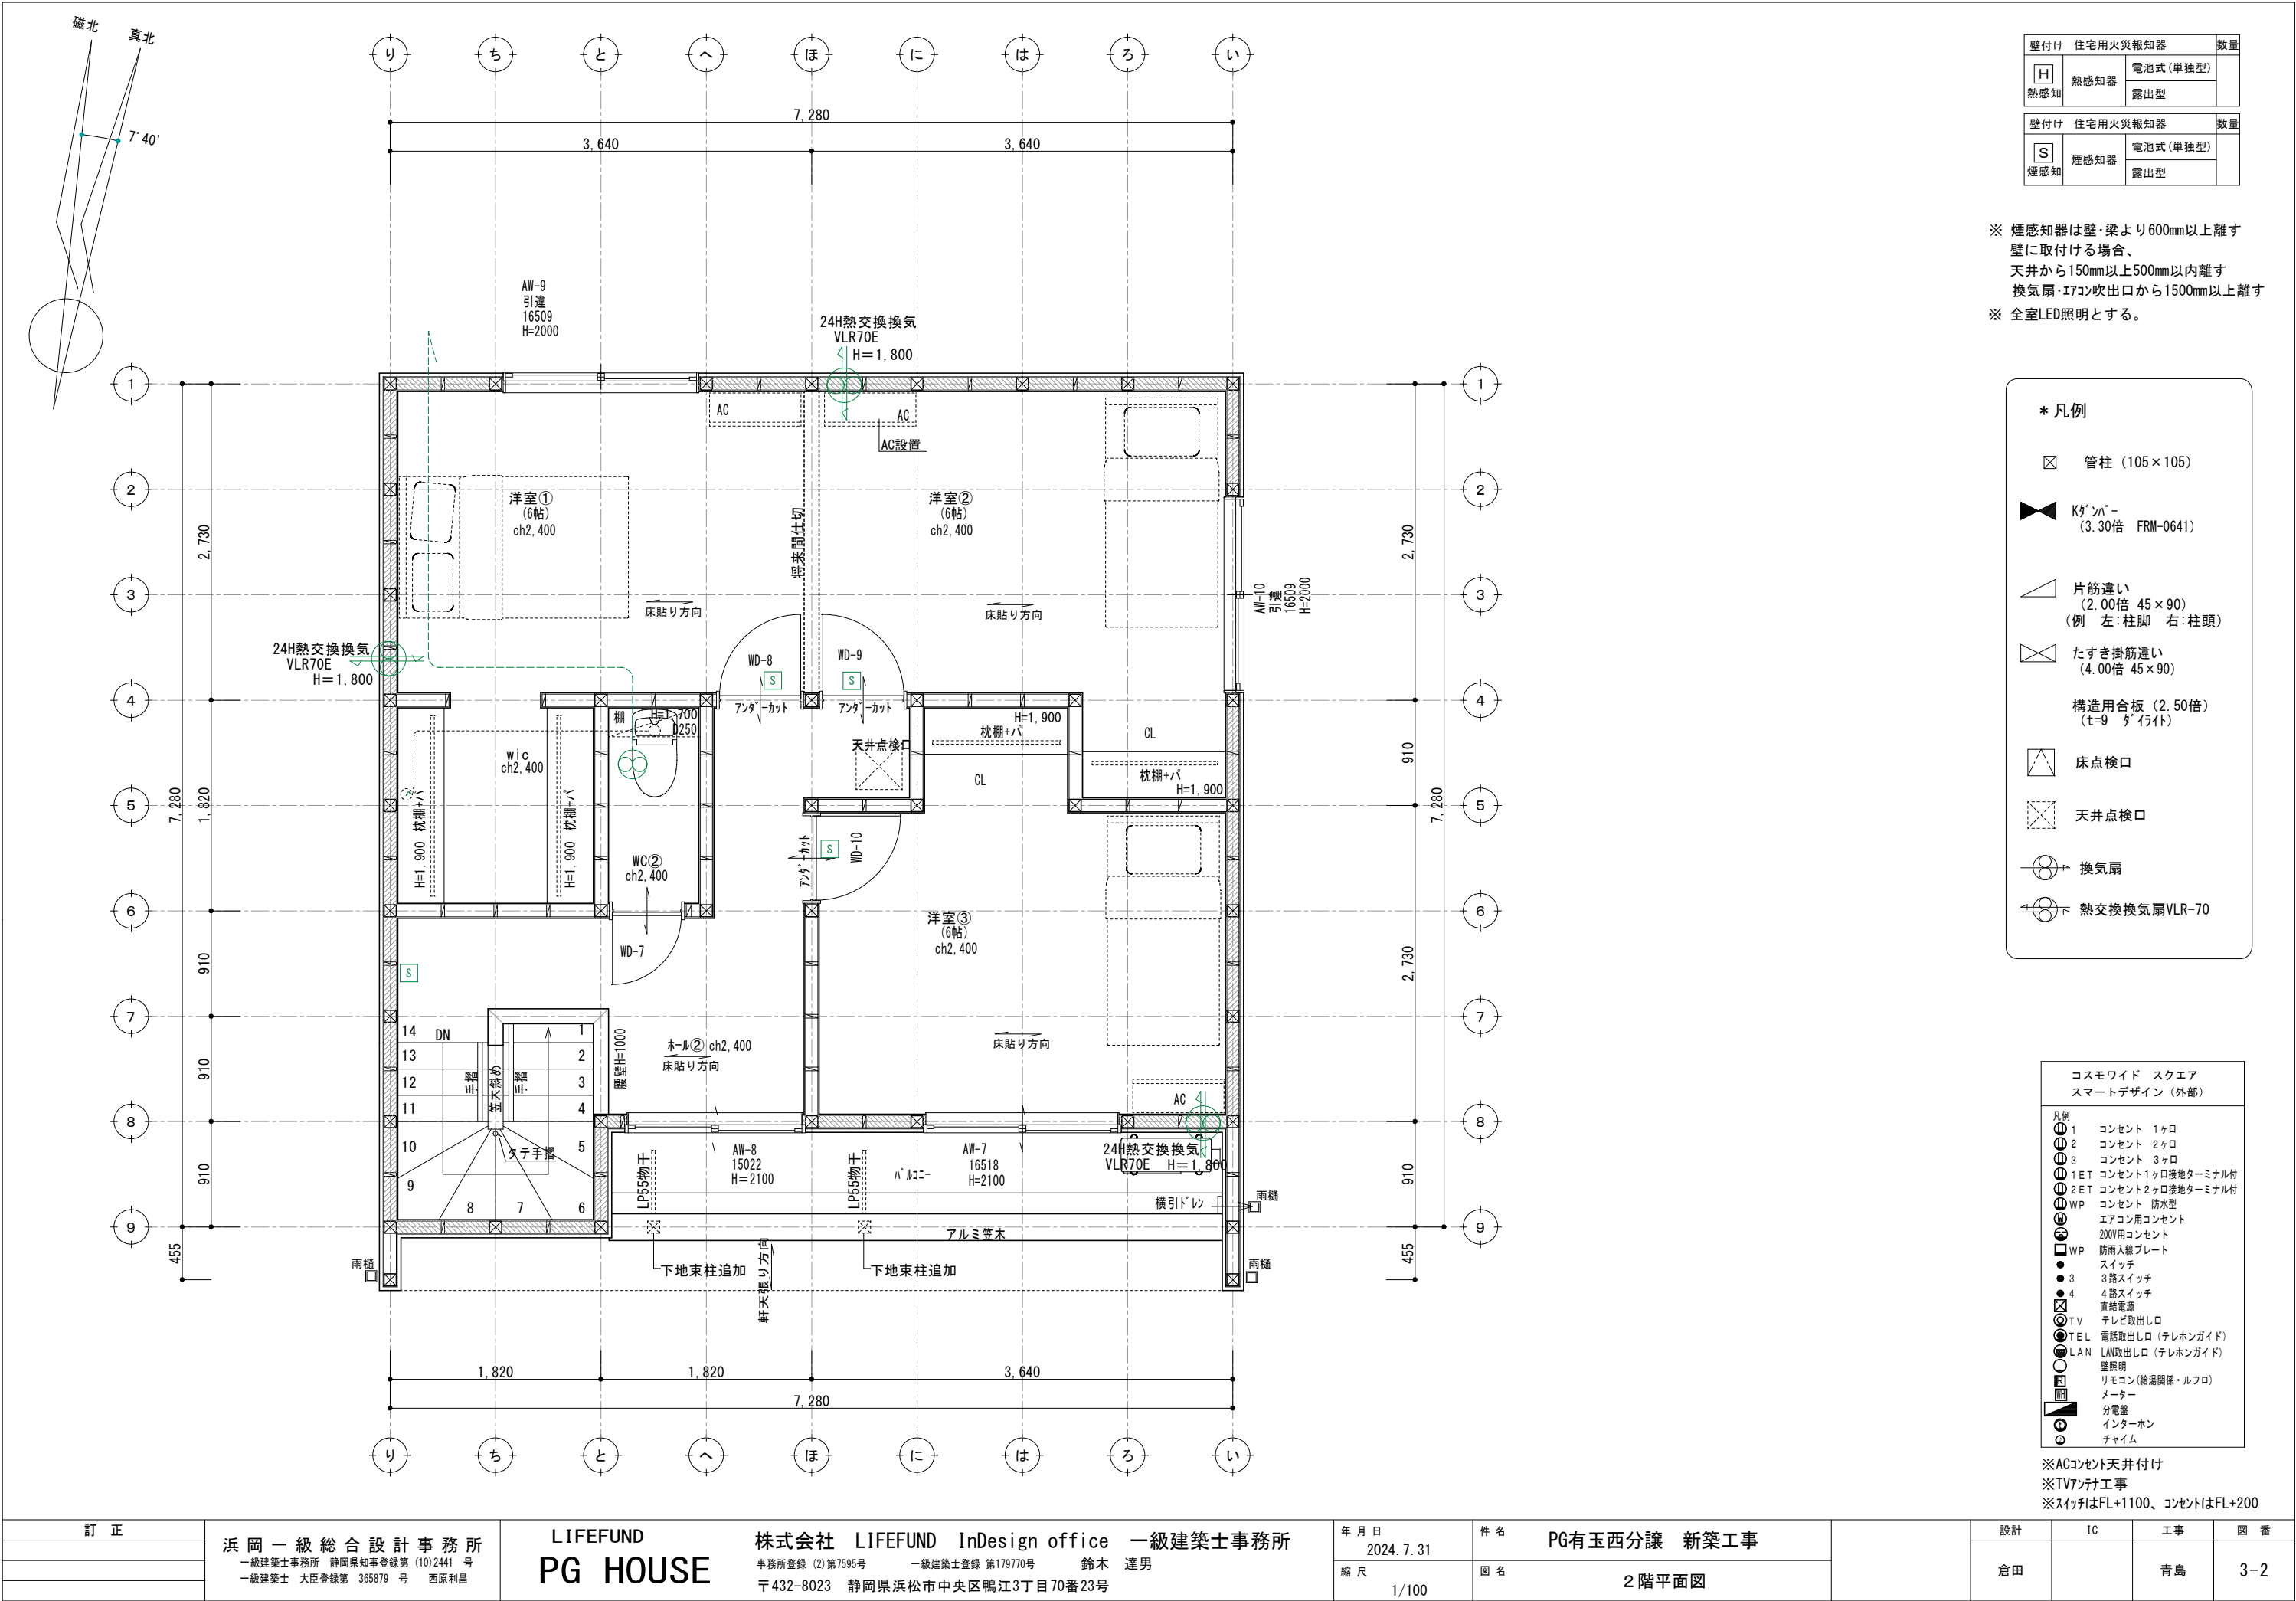

壁付け 住宅用火災報知器			数量
H 熱感知	熱感知器	電池式(単独型)	
		露出型	

壁付け 住宅用火災報知器			数量
S 煙感知	煙感知器	電池式(単独型)	
		露出型	


※ 煙感知器は壁・梁より600mm以上離す壁に取付ける場合、天井から150mm以上500mm以内離す換気扇・エアコン吹出口から1500mm以上離す
※ 全室LED照明とする。

*** 凡例**


- 管柱 (105×105)
- Kダクト (3.30倍 FRM-0641)
- 片筋違い (2.00倍 45×90) (例 左:柱脚 右:柱頭)
- たすき掛筋違い (4.00倍 45×90)
- 構造用合板 (2.50倍) (t=9 タイト)
- 床点検口
- 天井点検口
- 換気扇
- 熱交換換気扇VLR-70

コスモワイド スクエア スマートデザイン (外部)			
凡例	1	コンセント	1ヶロ
	2	コンセント	2ヶロ
	3	コンセント	3ヶロ
	1ET	コンセント1ヶロ接地ターミナル付	
	2ET	コンセント2ヶロ接地ターミナル付	
	WP	コンセント 防水型	
		エアコン用コンセント	
		200V用コンセント	
	WP	防雨入線プレート	
		スイッチ	
	3	3路スイッチ	
	4	4路スイッチ	
		直結電源	
	TV	テレビ取出口	
	TEL	電話取出口 (テレホンガイド)	
	LAN	LAN取出口 (テレホンガイド)	
		壁照明	
		リモコン (給湯関係・ルフロ)	
		メーター	
		分電盤	
		インターホン	
		チャイム	


※ACコンセント天井付け
※TVアンテナ工事
※スイッチはFL+1100、コンセントはFL+200

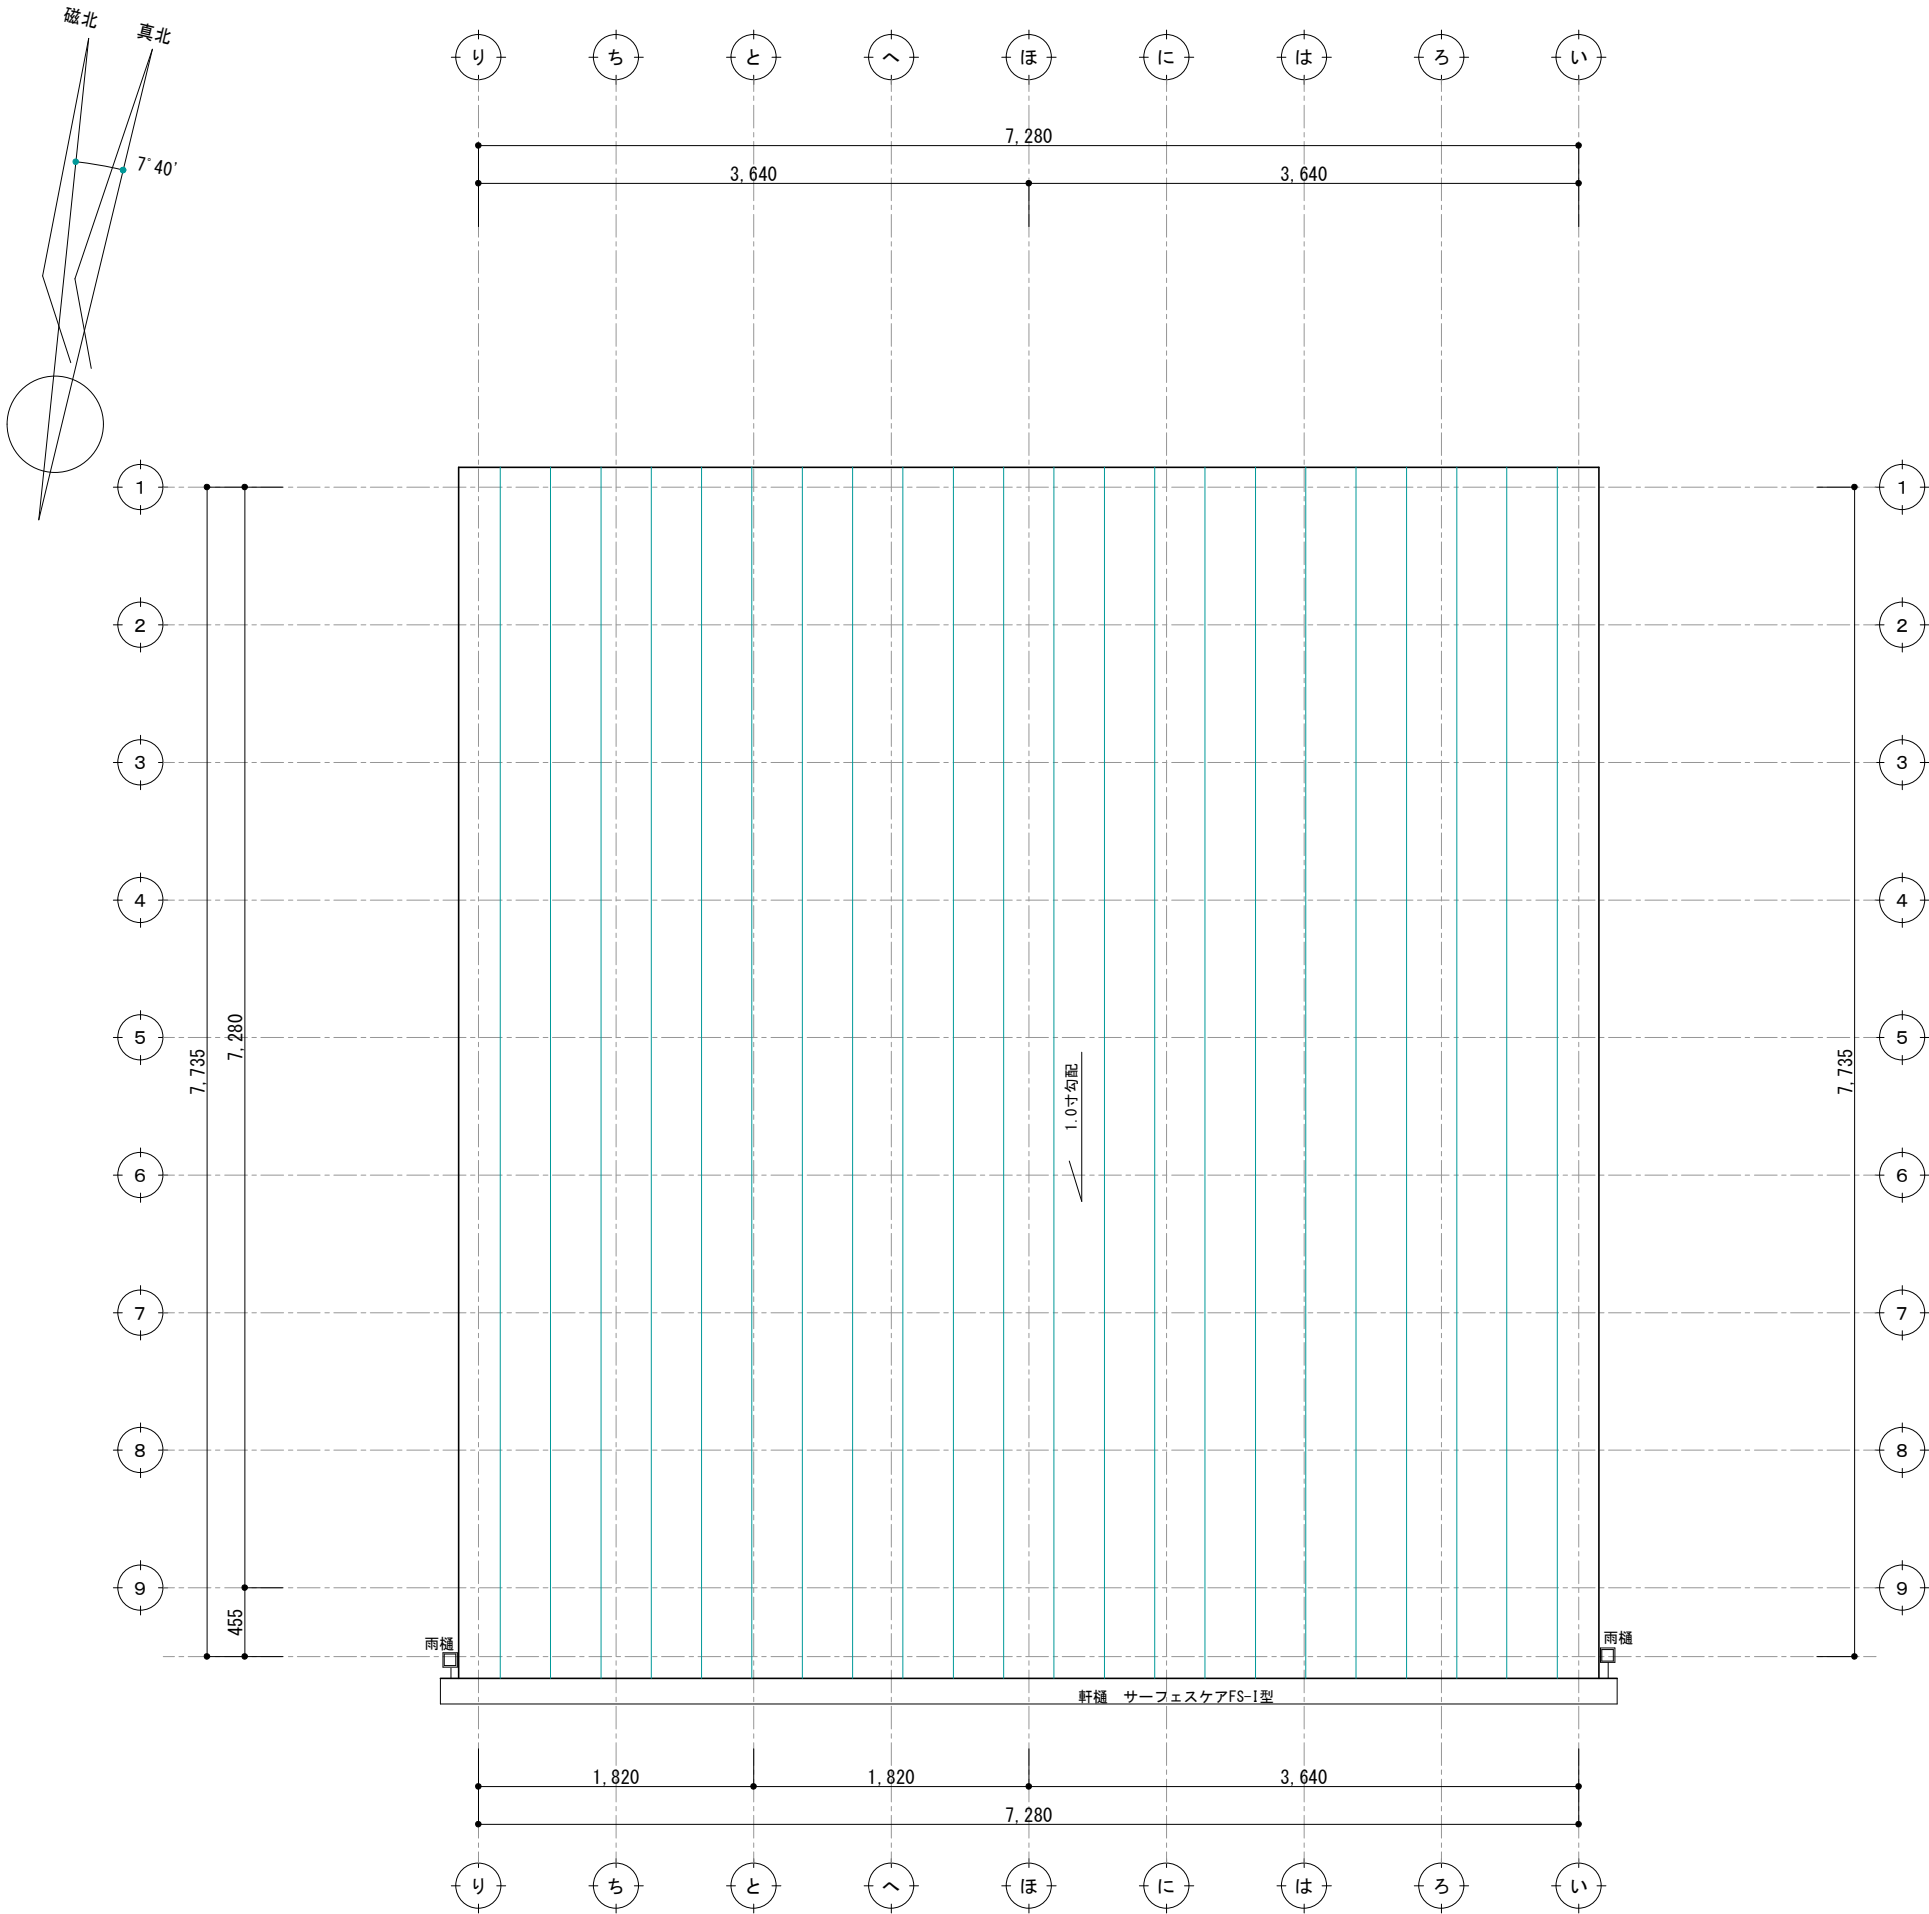


訂 正	浜 岡 一 級 総 合 設 計 事 務 所 一級建築士事務所 静岡県知事登録第 (10)2441 号 一級建築士 大臣登録第 365879 号 西原利昌	LIFEFUND PG HOUSE	株式会社 LIFEFUND InDesign office 一級建築士事務所 事務所登録 (2)第7595号 一級建築士登録 第179770号 鈴木 達男 〒432-8023 静岡県浜松市中央区鴨江3丁目70番23号	年 月 日 2024. 7. 31	件 名 PG有玉西分譲 新築工事		設計	IC	工事	図 番
				縮 尺 1/100	図 名 屋根伏図		倉田		青島	3-3

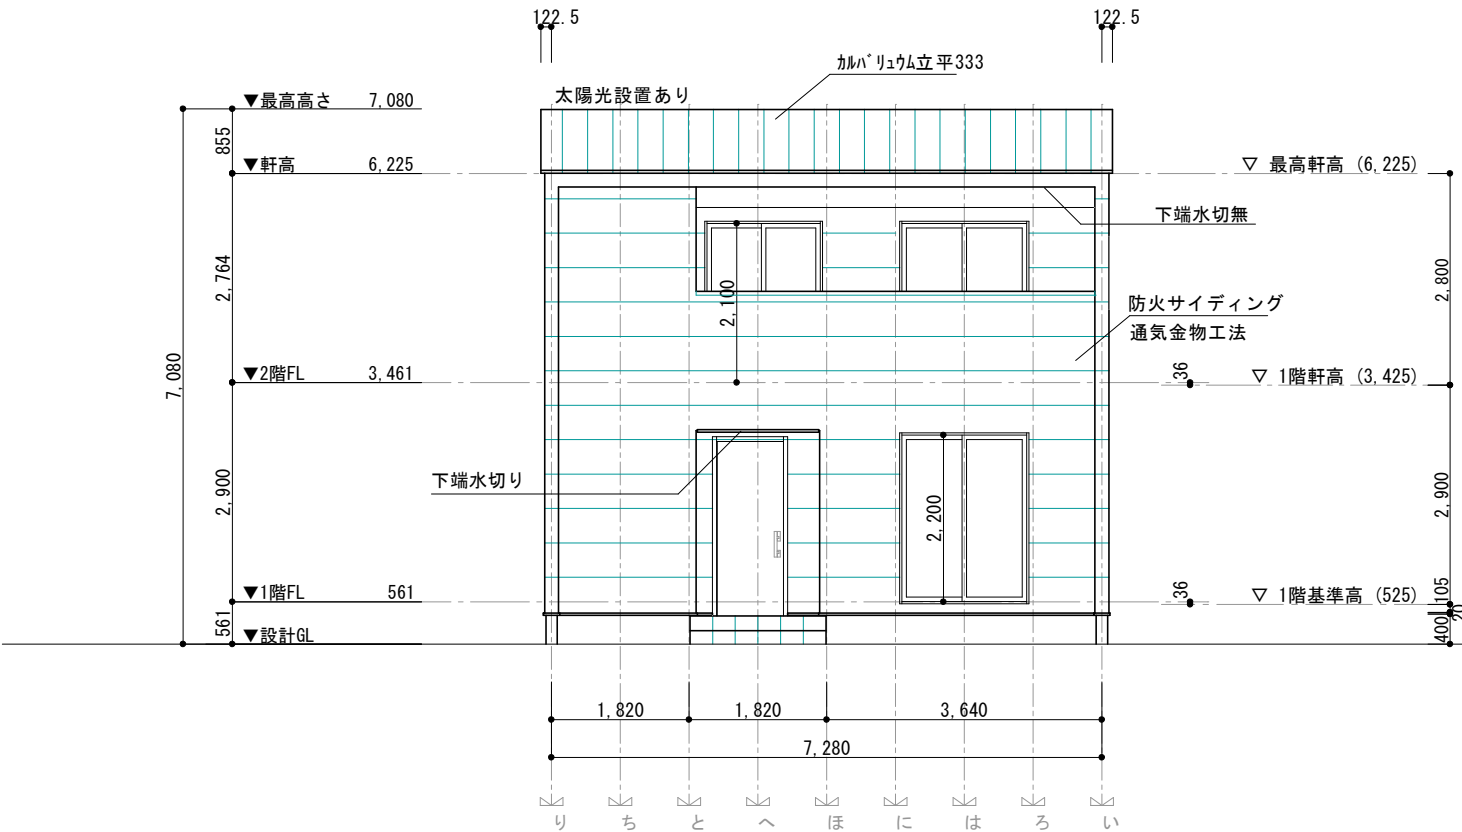


南側立面図 S=1/100

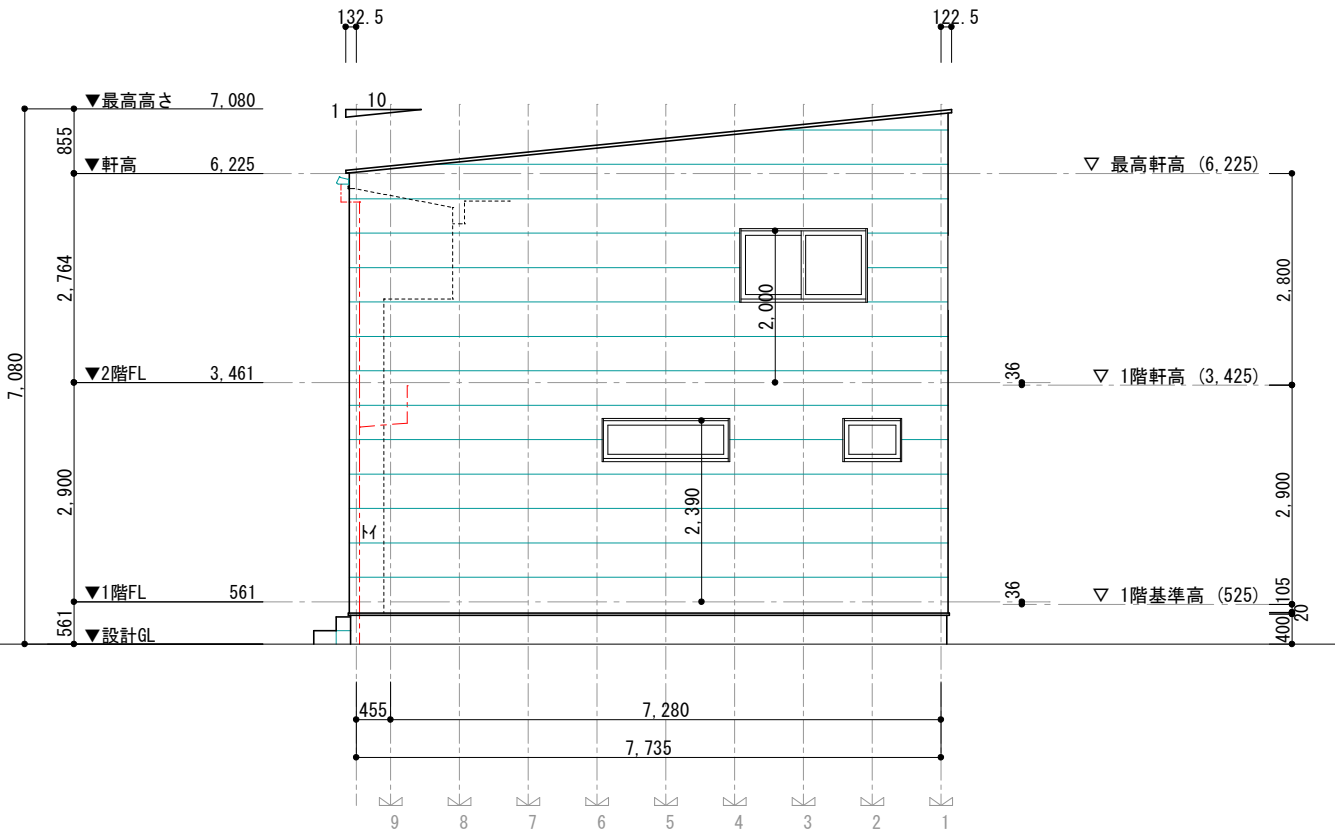

東側立面図 S=1/100

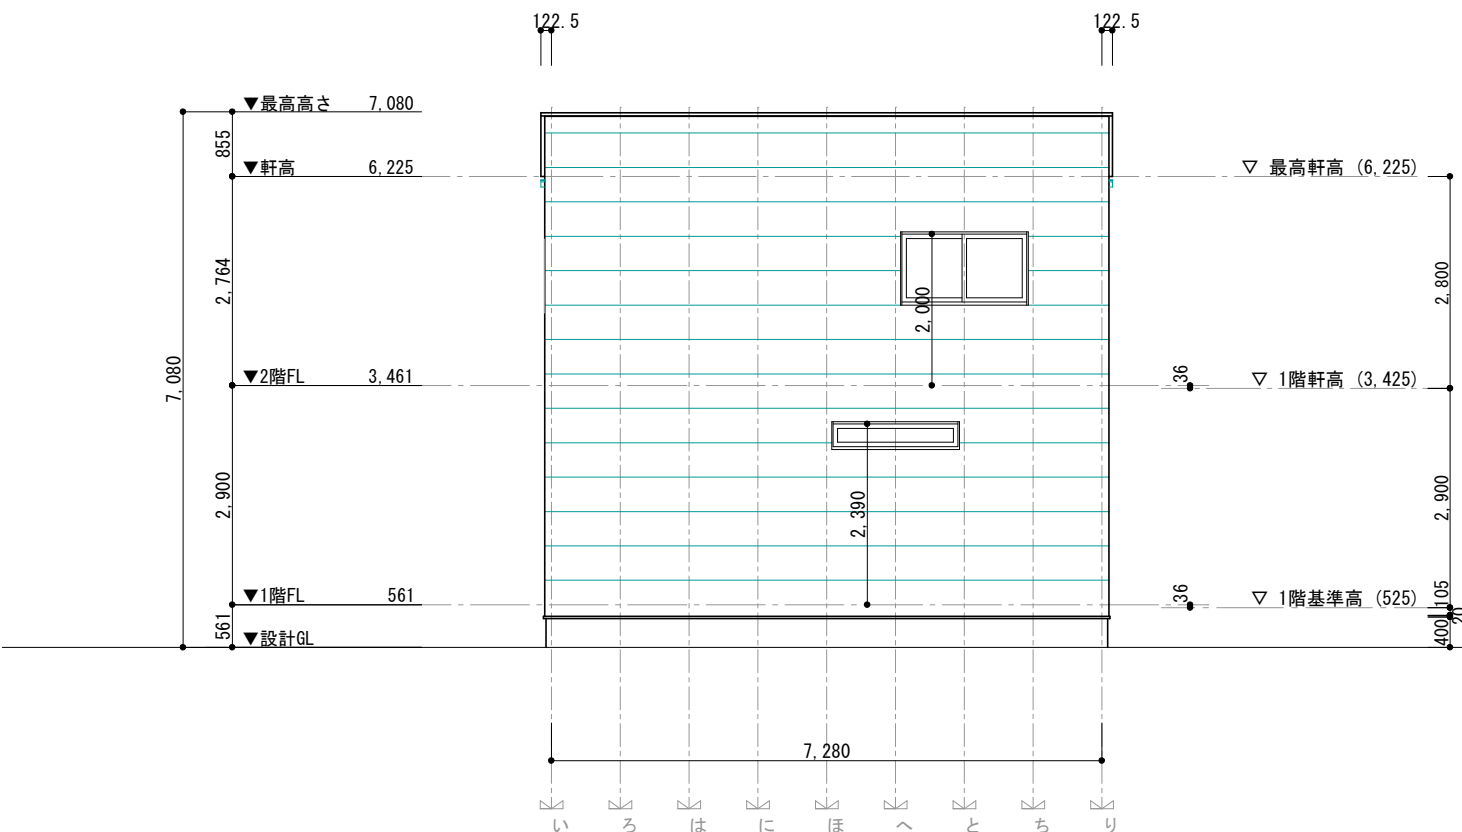


北側立面図 S=1/100

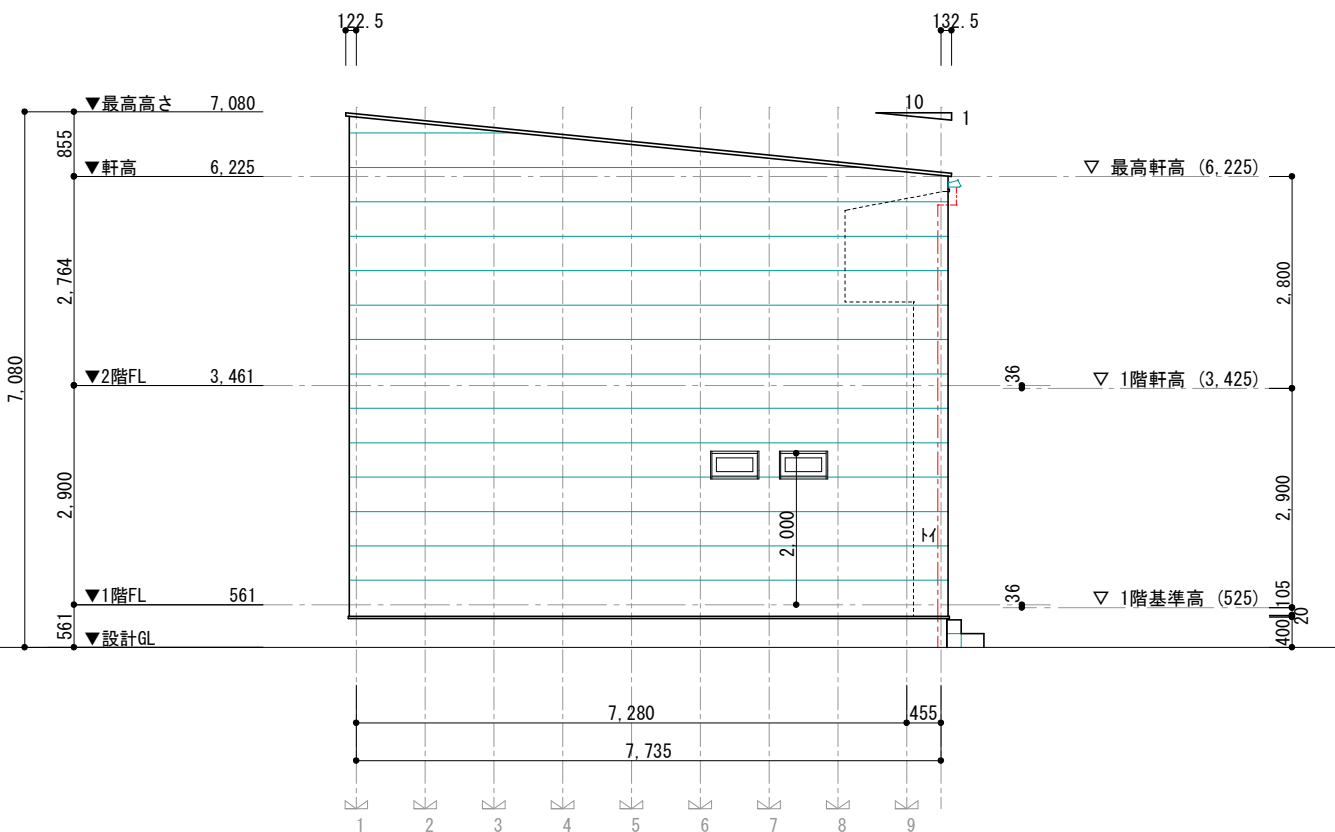


西側立面図 S=1/100


訂正	浜岡一級総合設計事務所	LIFEFUND PG HOUSE	株式会社 LIFEFUND InDesign office 一級建築士事務所 事務所登録(2)第7595号 一級建築士登録第179770号 鈴木 達男 〒432-8023 静岡県浜松市中央区鴨江3丁目70番23号	年月日	件名		設計	IC	工事	図番
	一級建築士事務所 静岡県知事登録第(10)2441号			2024.7.31	PG有玉西分譲 新築工事		倉田		青島	4
	一級建築士 大臣登録第 365879号 西原利昌			縮尺	図名					

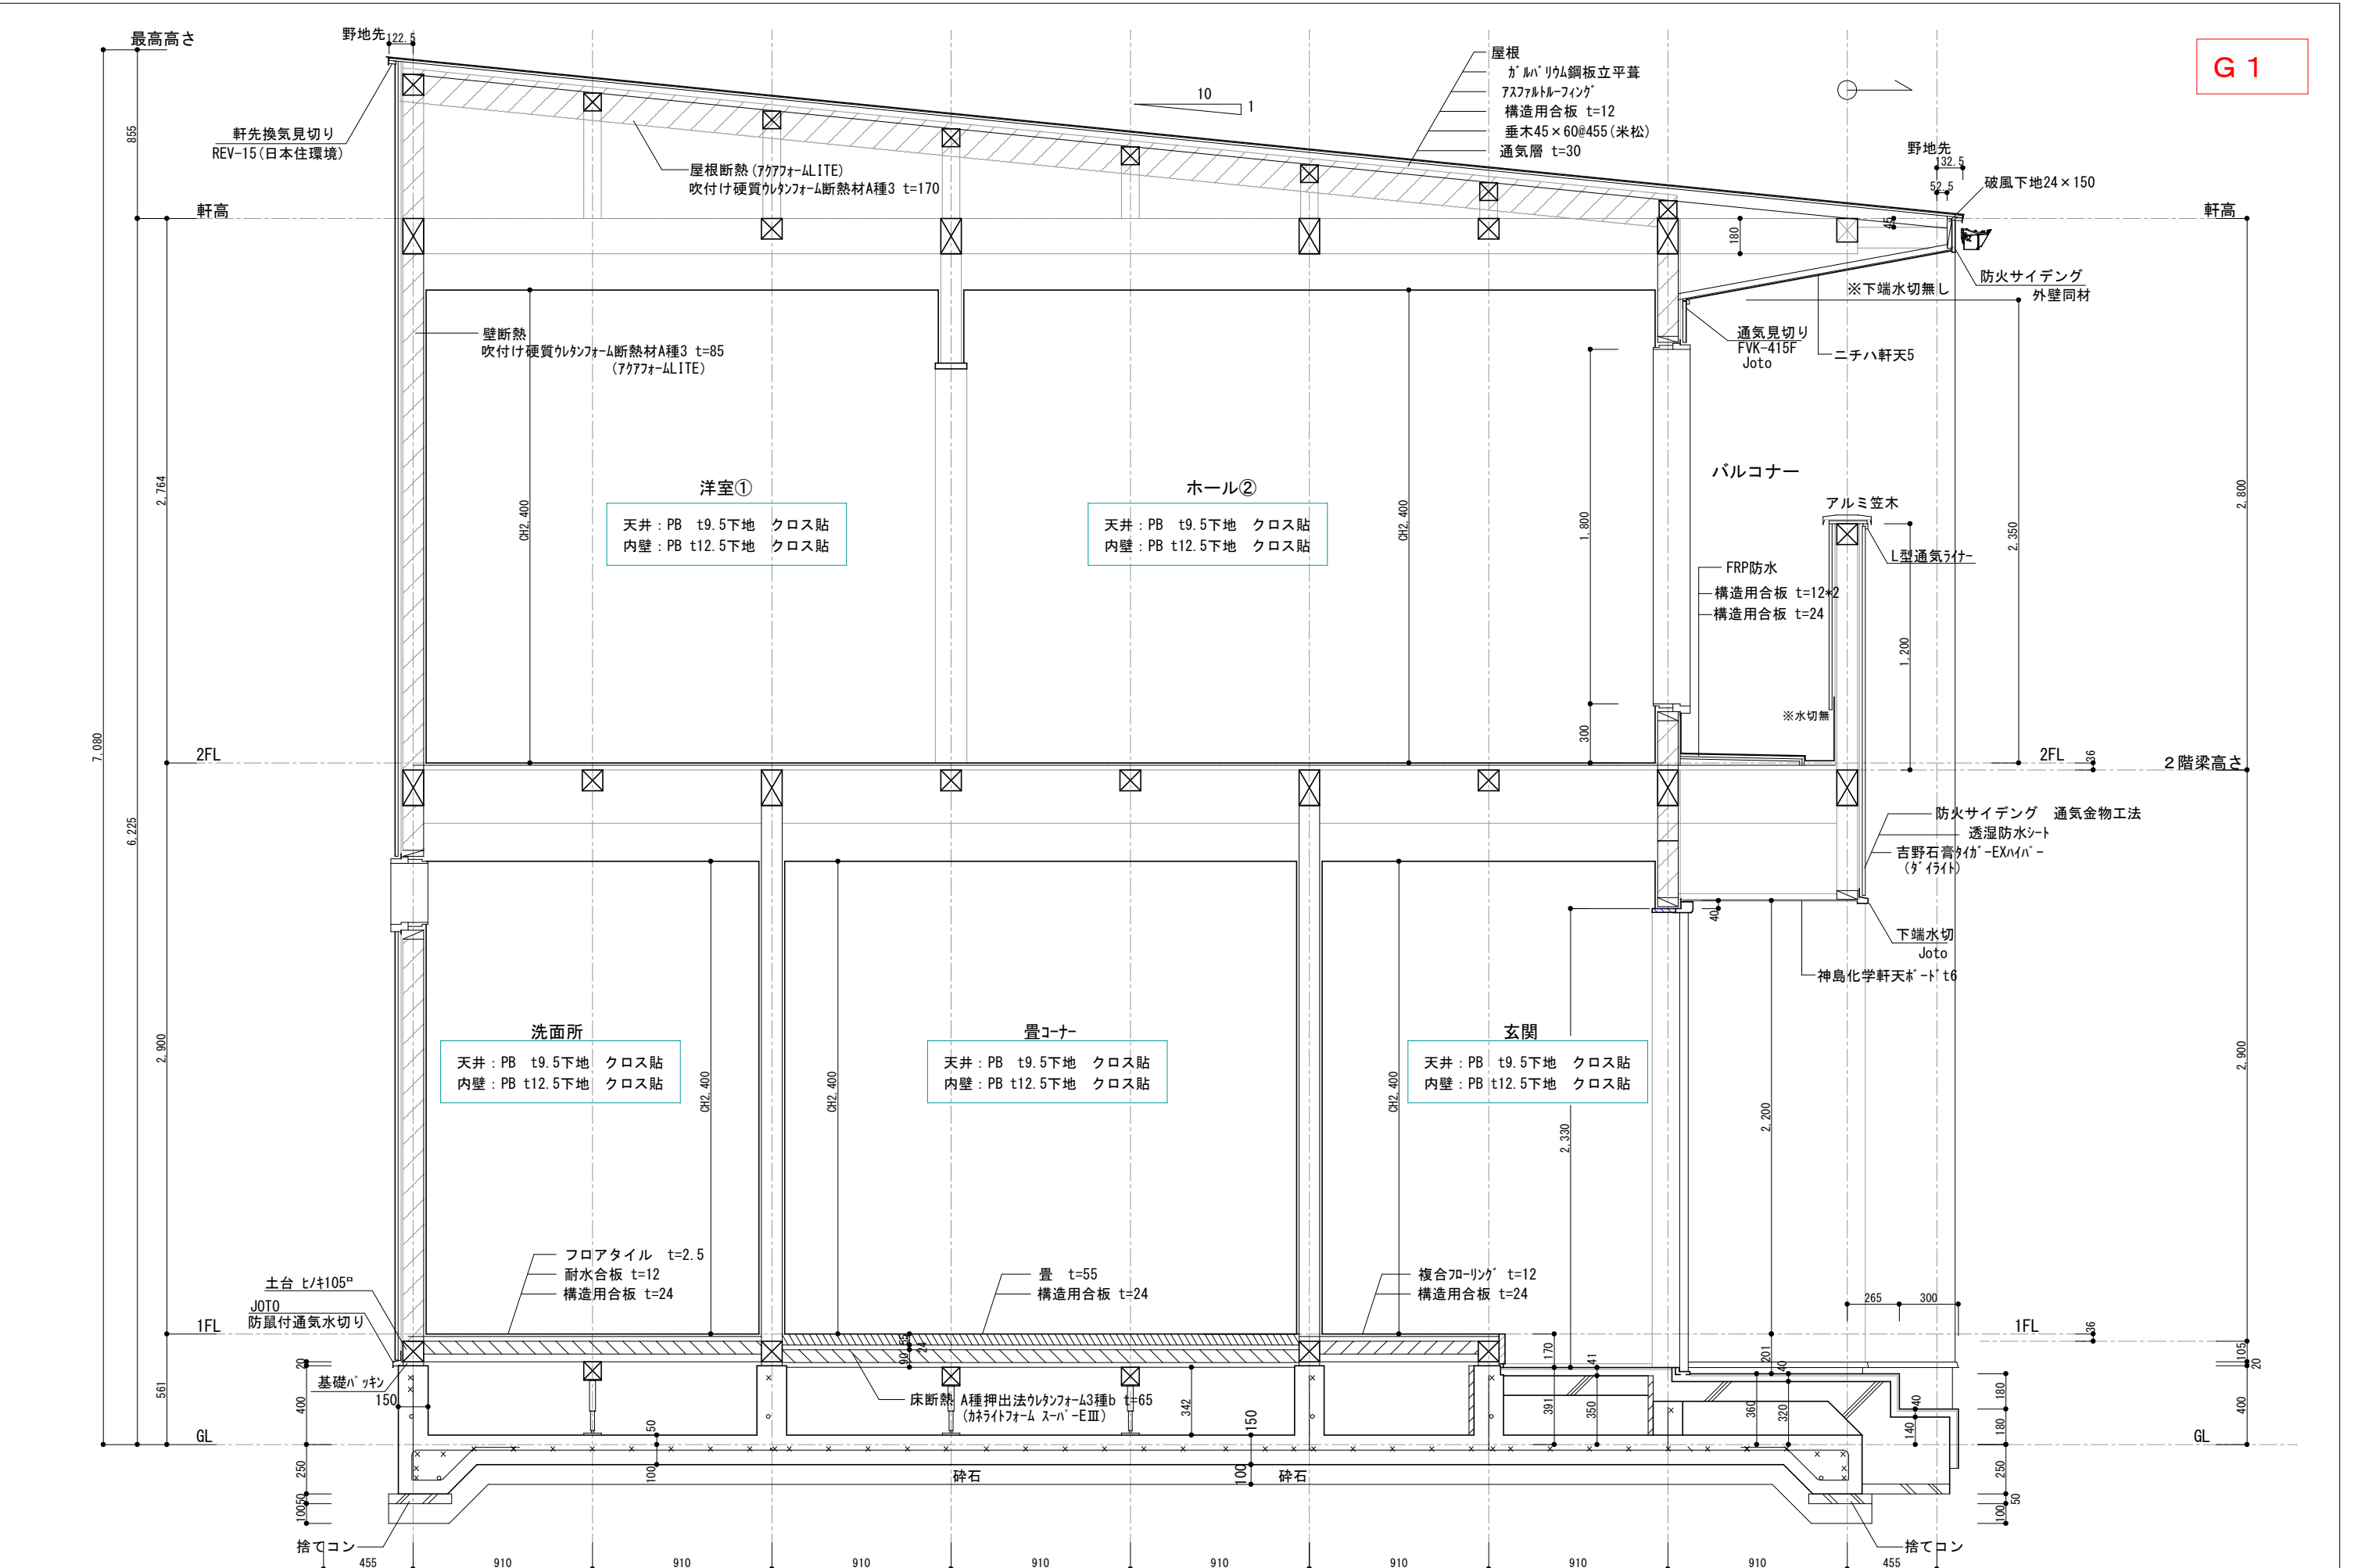


訂正	浜岡一級総合設計事務所 一級建築士事務所 静岡県知事登録第 (10)2441 号 一級建築士 大臣登録第 365879 号 西原利昌	LIFEFUND PG HOUSE	株式会社 LIFEFUND InDesign office 一級建築士事務所 事務所登録 (2)第7595号 一級建築士登録 第179770号 鈴木 達男 〒432-8023 静岡県浜松市中央区鴨江3丁目70番23号	年月日 2024. 7. 31	件名 PG有玉西 分譲 新築工事	設計 倉田	IC	工事 青島	図番 5-1
				縮尺 1/30	図名 矩計図				

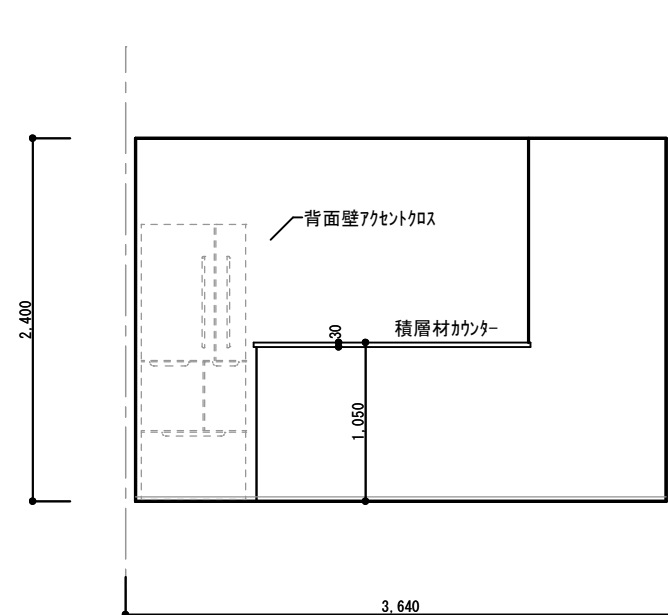


LDK 南面

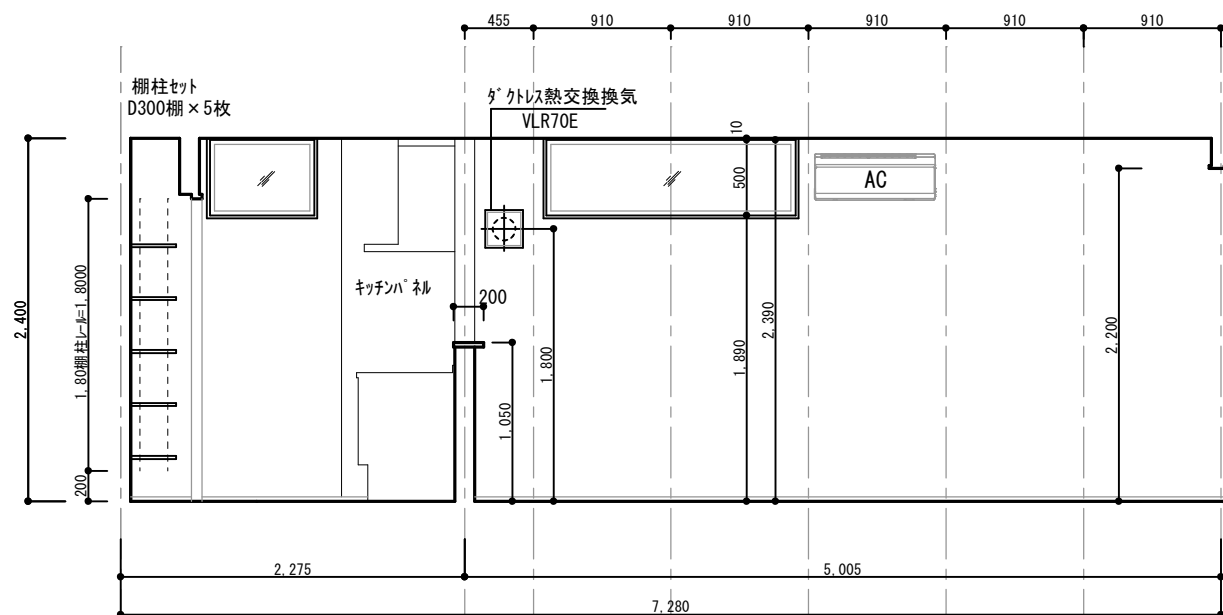


LDK 東面

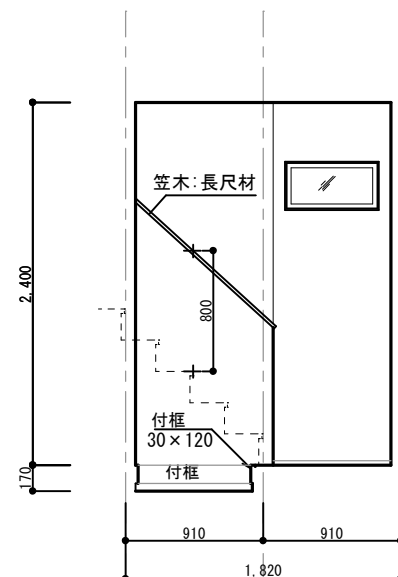


玄関 西面

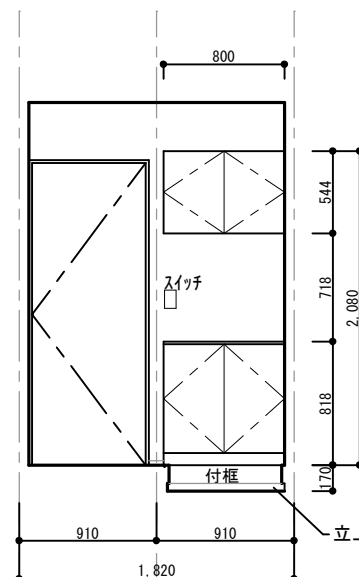


玄関 東面

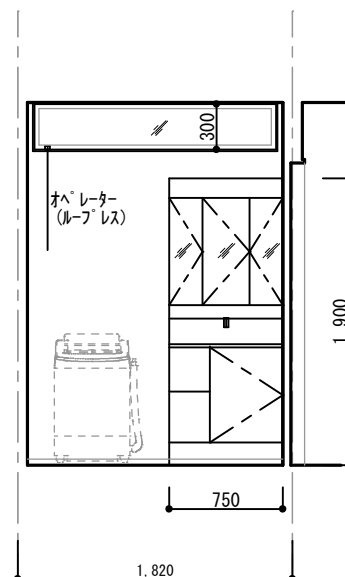


洗面所 北面

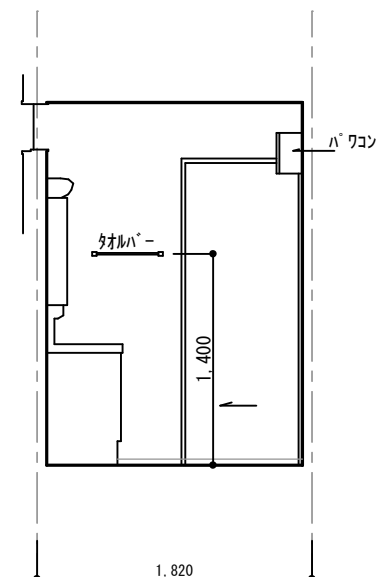


洗面所 東面

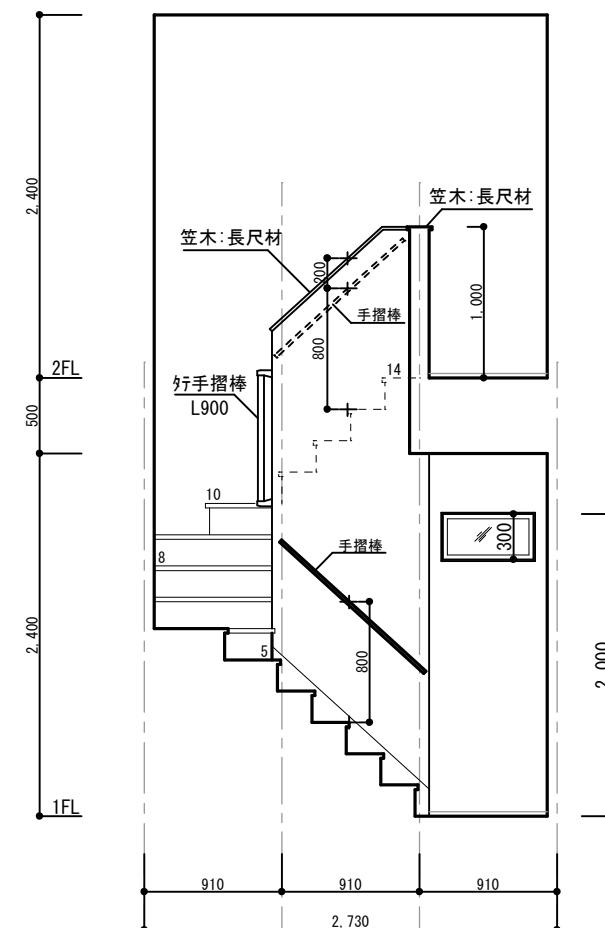


階段 西面

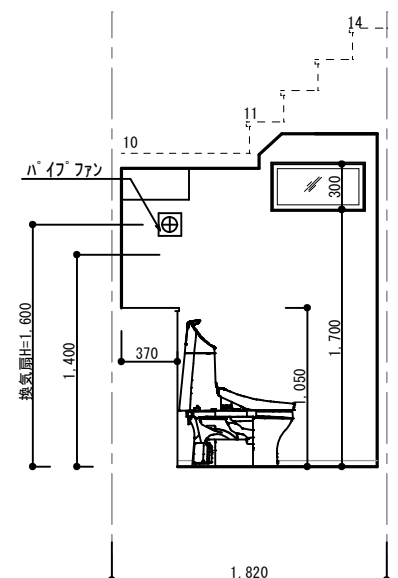


WC② 西面

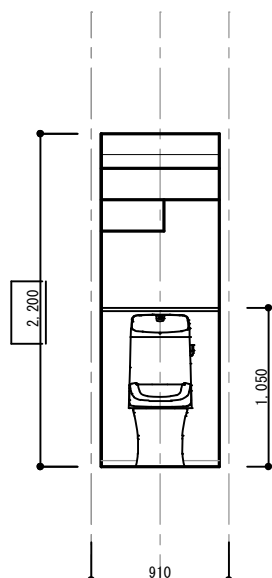


WC① 南面

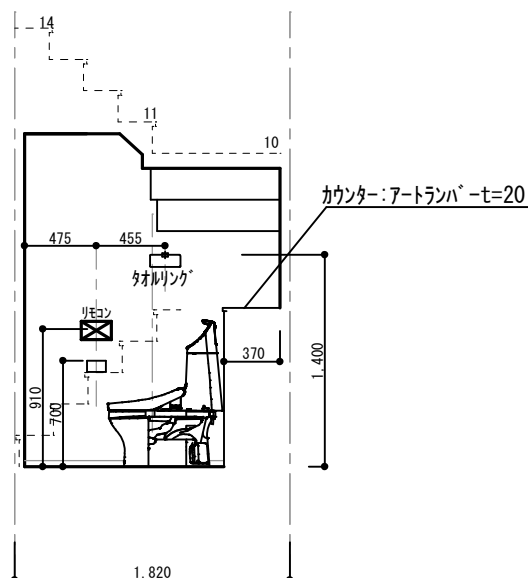

WC② 東面

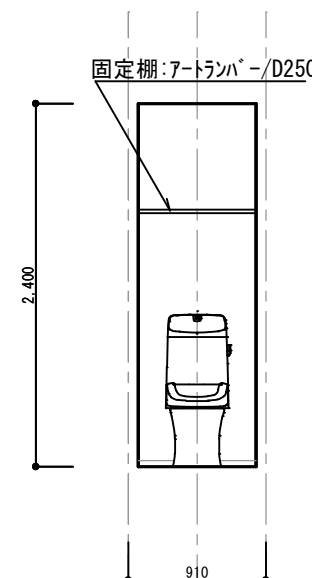


WC② 北面

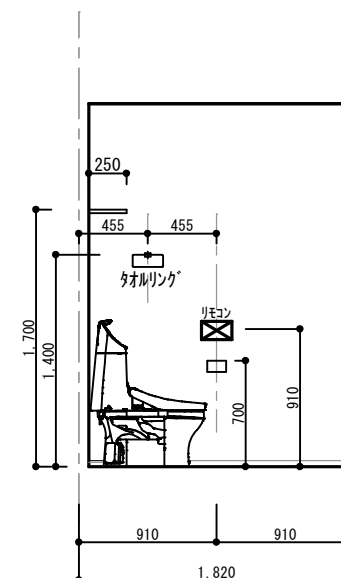

WC② 東面


訂正	浜岡 一級総合設計事務所 一級建築士事務所 静岡県知事登録第 (10)2441 号 一級建築士 大臣登録第 365879 号 西原利晶	LIFEFUND PG HOUSE	株式会社 LIFEFUND InDesign office 一級建築士事務所 事務所登録 (2)第7595号 一級建築士登録 第179770号 鈴木 達男 〒432-8023 静岡県浜松市中央区鴨江3丁目70番23号	年月日 2024.07.31	件名 PG有玉西分譲 新築工事		設計	IC	工事	図番
				縮尺 1/30	図名 展開図(1)		倉田		青島	6-1

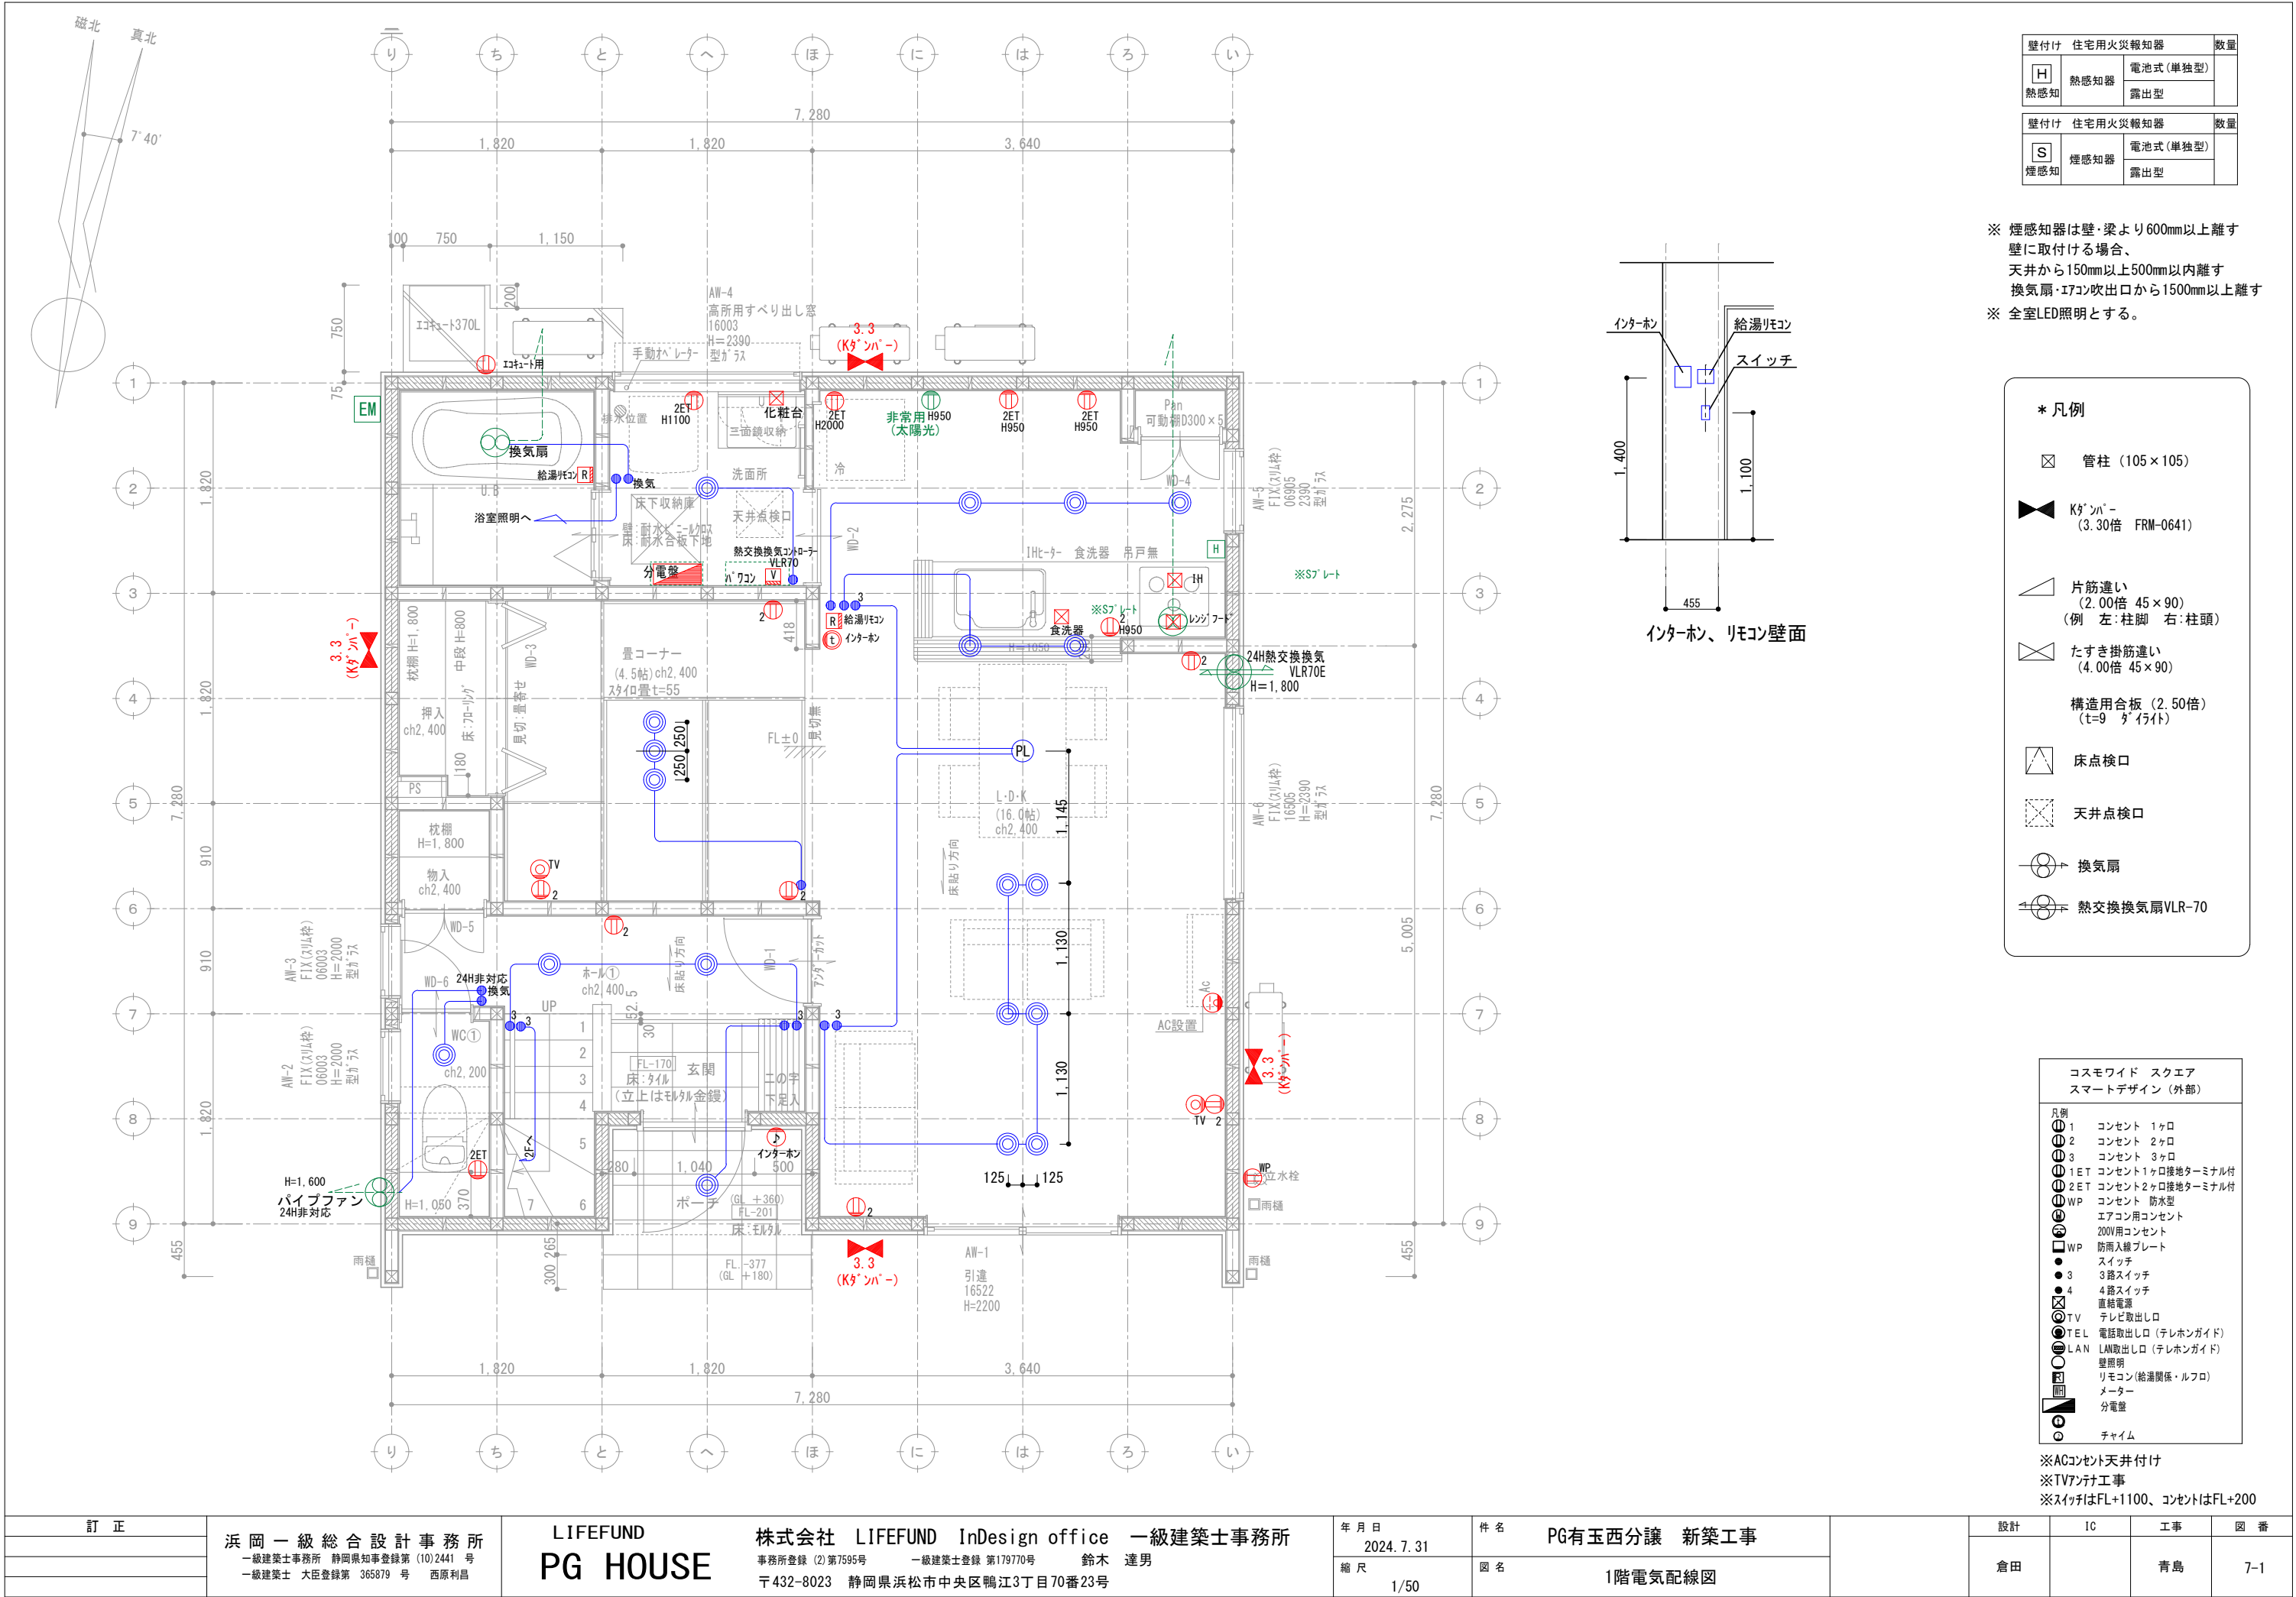

壁付け 住宅用火災報知器			数量
H 熱感知	電池式 (単独型)		
	露出型		
壁付け 住宅用火災報知器			数量
S 煙感知	電池式 (単独型)		
	露出型		

※ 煙感知器は壁・梁より600mm以上離す壁に取付ける場合、天井から150mm以上500mm以内離す換気扇・エアコン吹出口から1500mm以上離す


※ 全室LED照明とする。

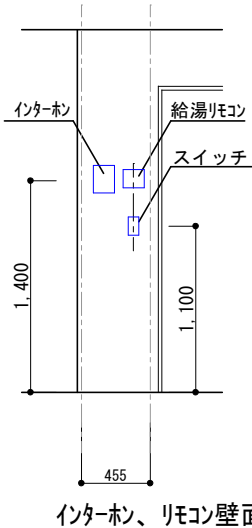


- * 凡例**
- 管柱 (105×105)
 - Kダクト (3.30倍 FRM-0641)
 - 片筋違い (2.00倍 45×90) (例 左:柱脚 右:柱頭)
 - たすき掛筋違い (4.00倍 45×90)
 - 構造用合板 (2.50倍) (t=9 タイライト)
 - 床点検口
 - 天井点検口
 - 換気扇
 - 熱交換換気扇VLR-70


コスモワイド スクエア スマートデザイン (外部)		
凡例		
	1	コンセント 1ヶロ
	2	コンセント 2ヶロ
	3	コンセント 3ヶロ
	1ET	コンセント1ヶロ接地ターミナル付
	2ET	コンセント2ヶロ接地ターミナル付
	WP	コンセント 防水型
		エアコン用コンセント
		200V用コンセント
	WP	防雨入線プレート
		スイッチ
	3	3路スイッチ
	4	4路スイッチ
		直結電源
	TV	テレビ取出口
	TEL	電話取出口 (テレホンガイド)
	LAN	LAN取出口 (テレホンガイド)
		壁照明
		リモコン (給湯関係・ルフロ)
		メーター
		分電盤
		チャイム

※ACコンセント天井付け
※TVアンテナ工事
※スイッチはFL+1100、コンセントはFL+200

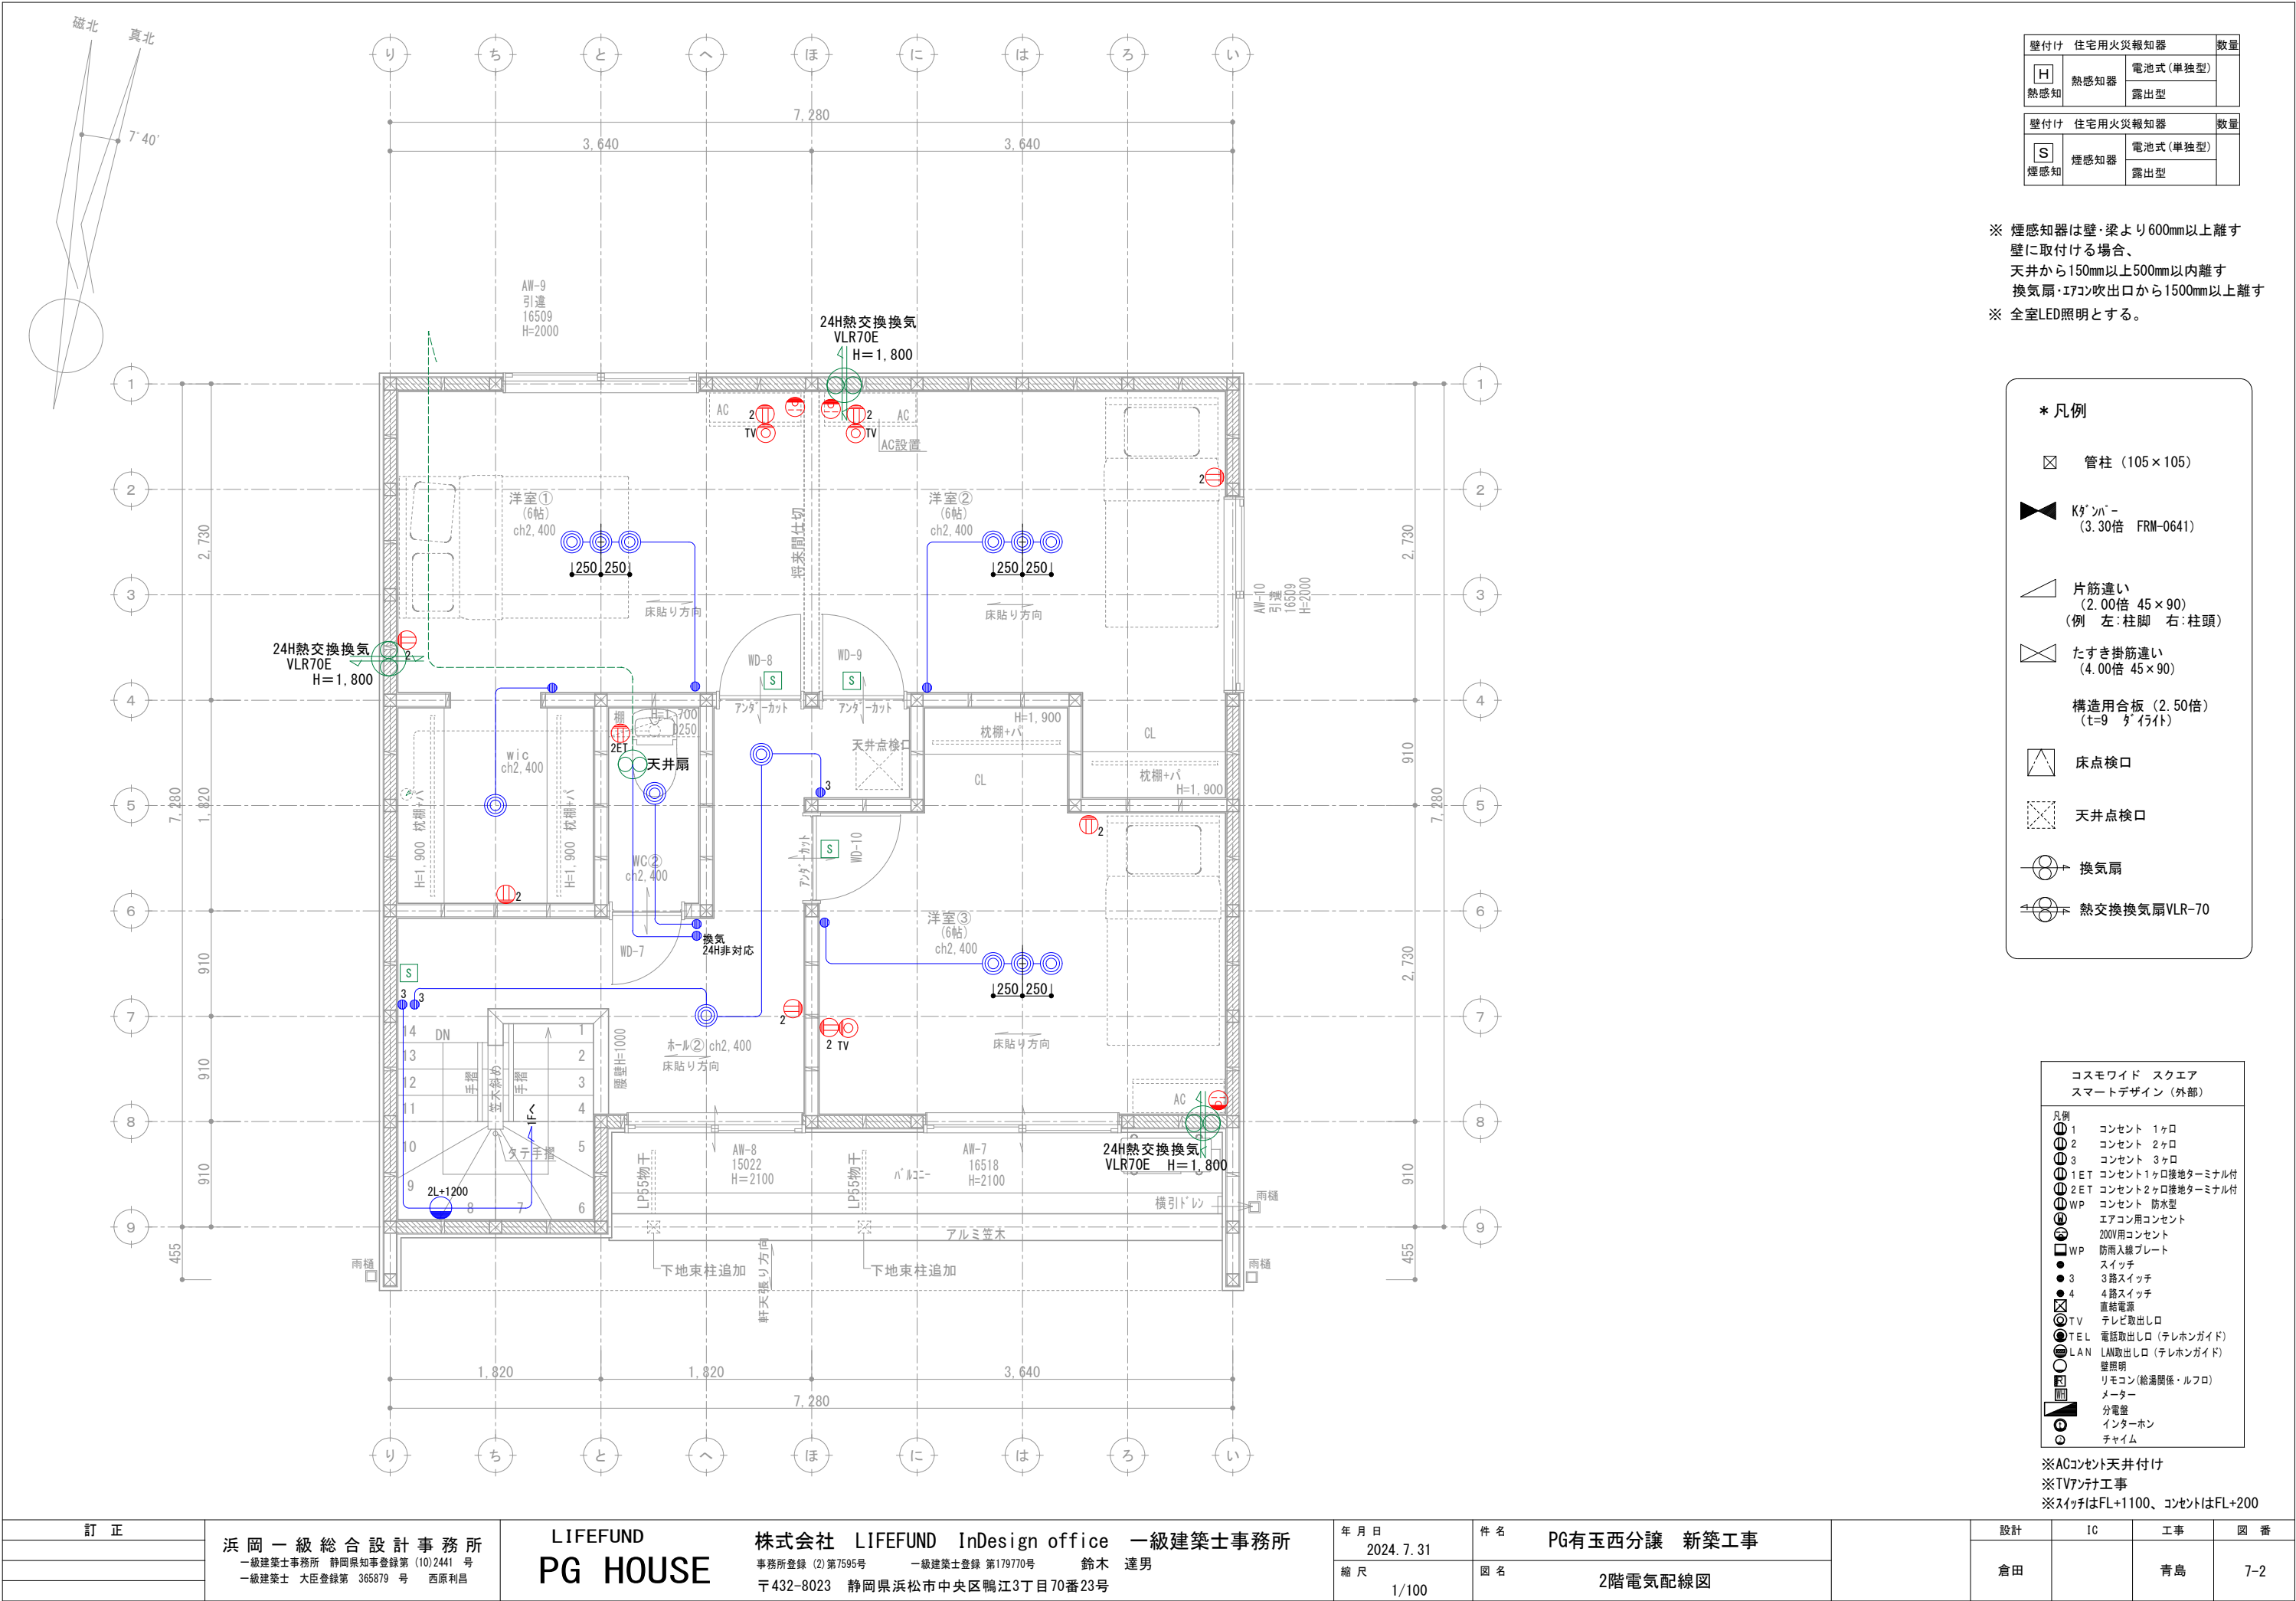

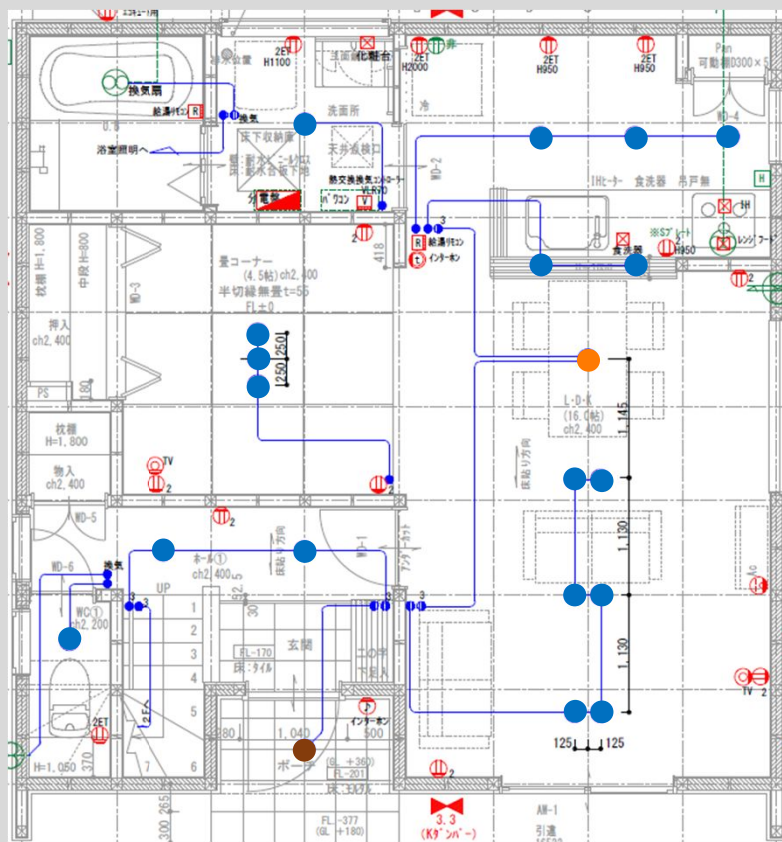


1 階

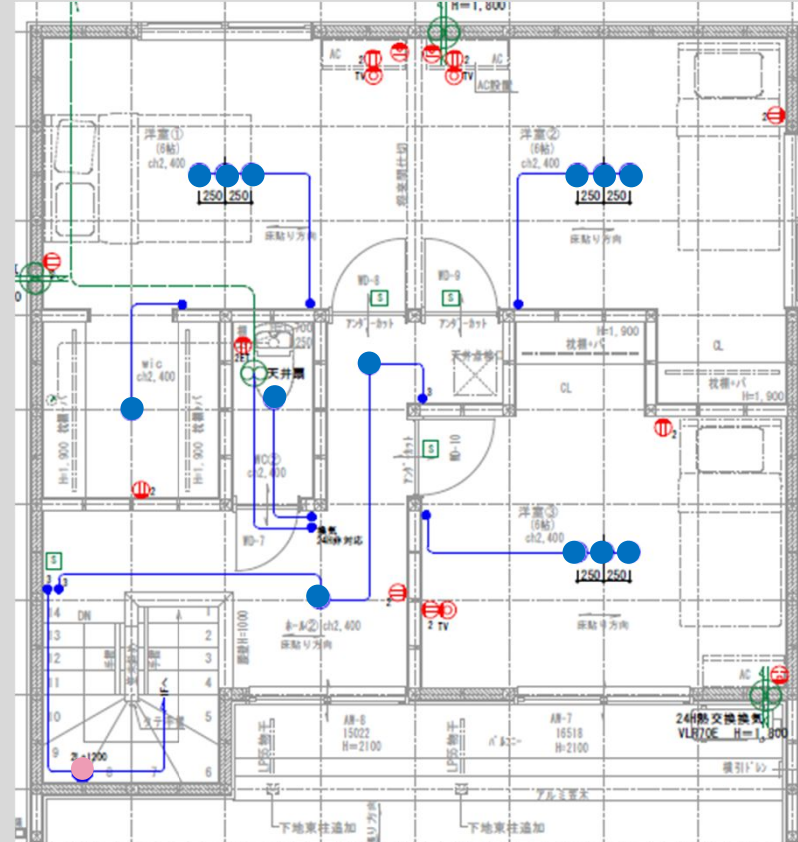

2 階

内部：コスモワイド スクエア(Panasonic)

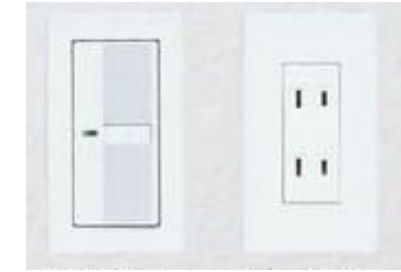

ドアホン：VL-SZ30KL
(Panasonic)



外部：スマートデザインシリーズ (Panasonic)

表情豊かな住まいをつくり出すスマートデザインシリーズ。



ポーチ灯

● × 1

DDL-4496YW



基本照明ダウンライト

● × 31

DDL6102AW



ダイニングペンダント灯

● × 1

DPN41973




階段灯












● × 1

DBK41544Y



2024.07.31

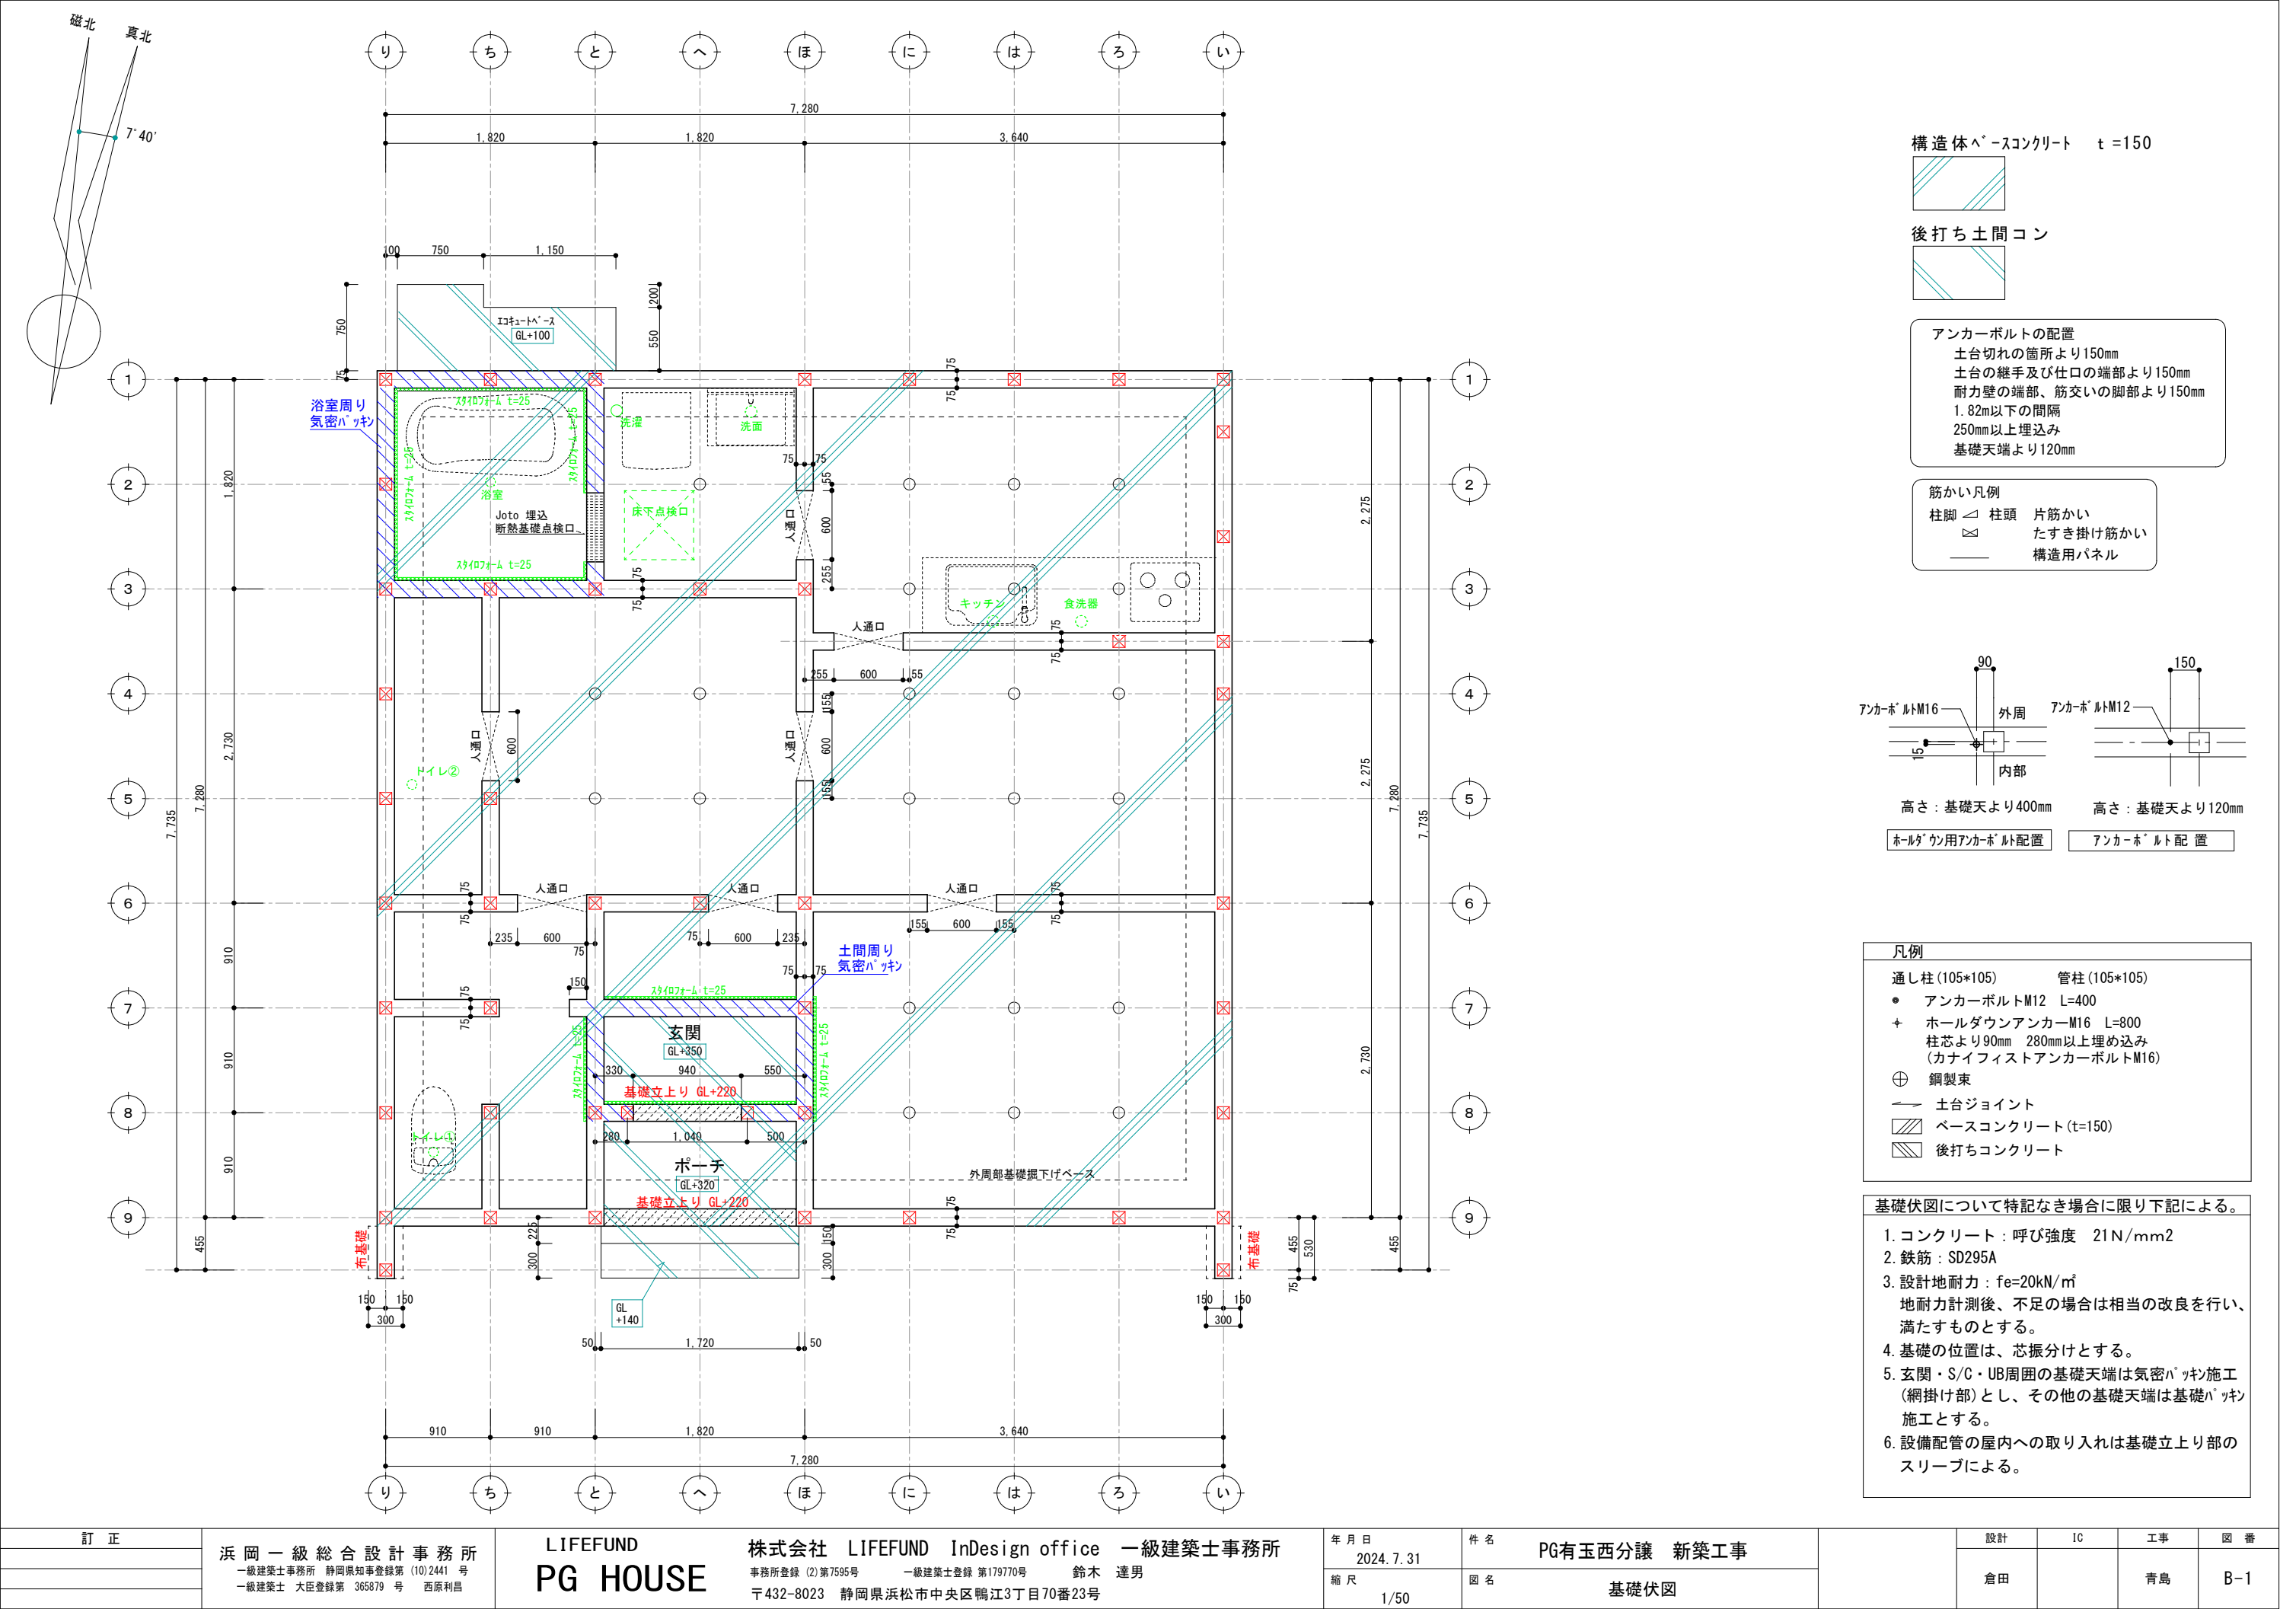

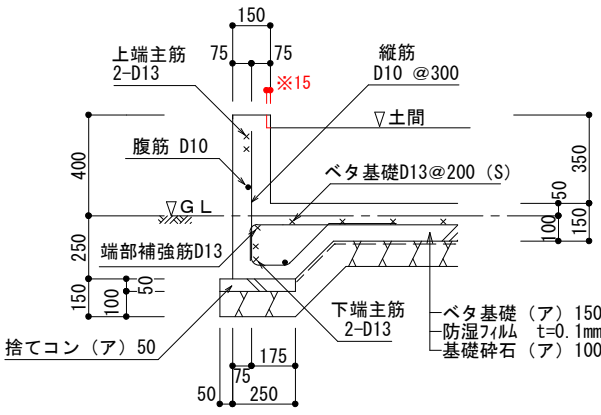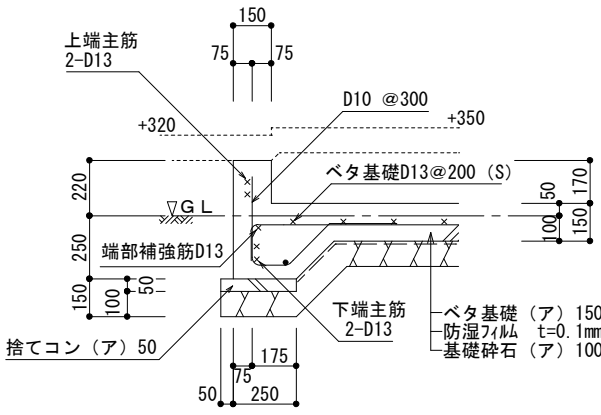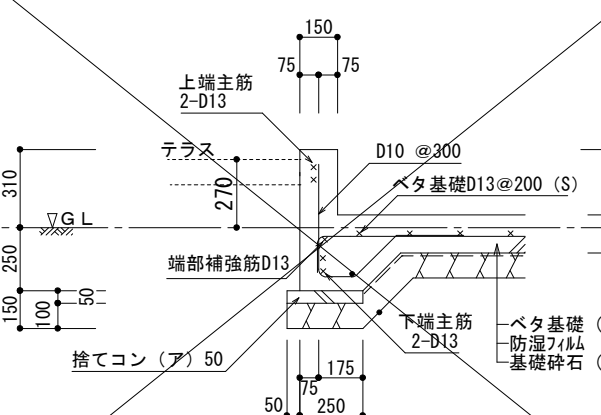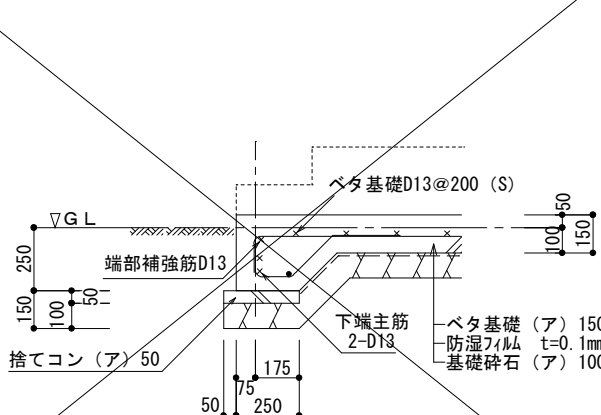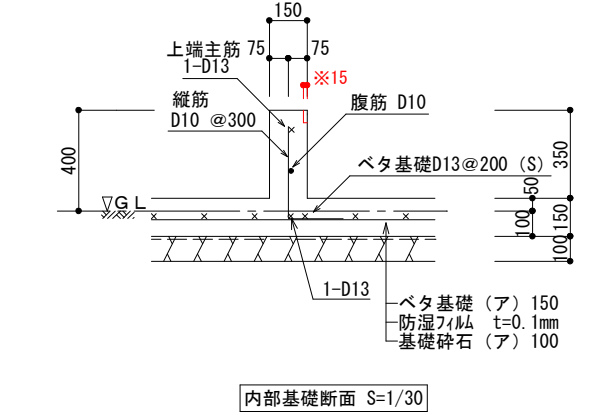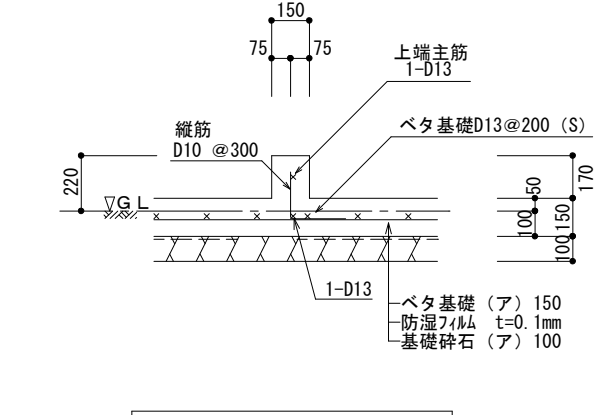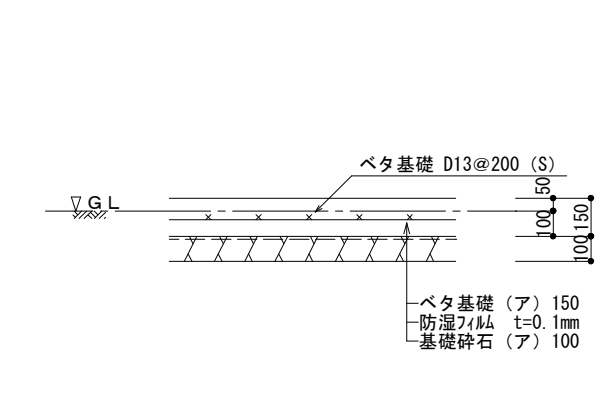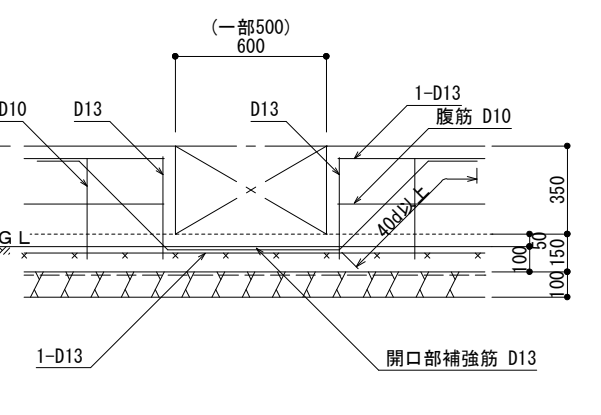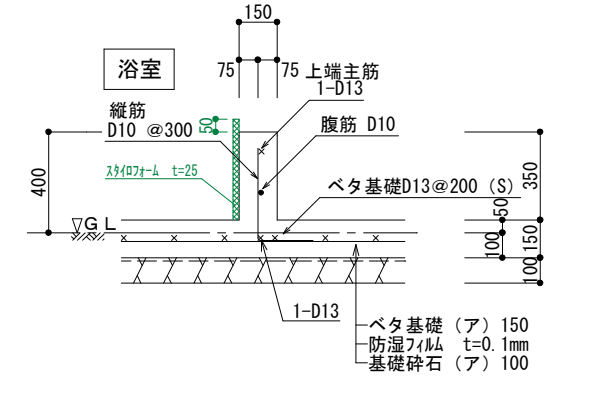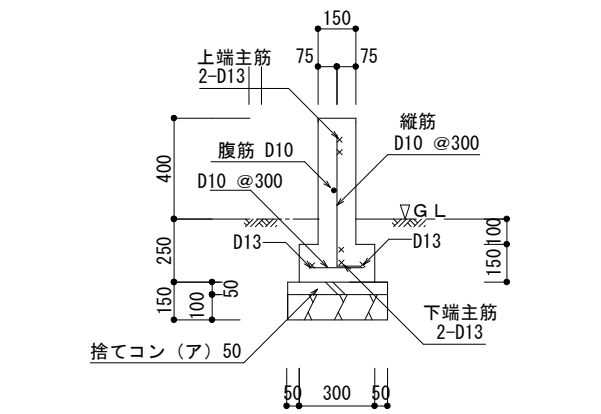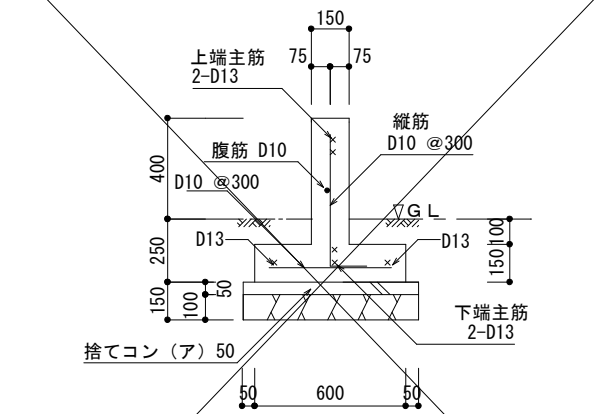 外周基礎断面 S=1/30 ※玄関内土間部分のみ15mm欠き込み		 ポーチ下 外周部基礎断面 S=1/30 倉庫ドア下 外周部基礎断面 S=1/30		 土間納め勝手口ドア下 外周部基礎断面 S=1/30		 立上り無しの基礎断面 S=1/30	
 内部基礎断面 S=1/30 ※玄関内土間部分のみ15mm欠き込み ※注意：基礎伏図に特記のない内部基礎の場合		 ポーチ下 内周部基礎断面 S=1/30 玄関ドア下 内周部基礎断面 S=1/30 玄関内横断基礎断面 S=1/30		 ベタ基礎断面 S=1/30		 人通口補強 S=1/30	
 浴室内部基礎断面 S=1/30 ※注意：基礎伏図に特記のない内部基礎の場合		 布基礎A：袖壁用 基礎断面 S=1/30		 布基礎B：底用独立 基礎断面 S=1/30		基礎の寸法 及び 配筋の検証方法 基礎立上り配筋は、 (財)日本住宅・木材技術 センター発行のスパン表 (増補版)による。 ベタ基礎スラブ配筋は、 まもりすまい保険設計施工 基準同解説のベタ基礎配筋表 による。具体的な寸法・配 筋は基礎詳細図参照。 鉄筋断面表記 ●・・・D10を示す。 ×・・・D13を示す。 ※使用しない断面は×を記入。	

Aritama-model house project



Construction Name

■PG有玉西 分譲

Place

浜松市中央区有玉西町2135-34

Data

Date

2024. 7. 16

Sign

Scale



InDesign office
一級建築士事務所

3-70-23 kamoe-, Hamamatsu Naka-ku, Shizuoka, JAPAN
Tel 053-485-8910 Fax 053-485-8911