

■ 仕 様				■ HEAT20 G1	
断熱工事		■ 床:カネライトフォーム t65 ■ 土間床等の外周:スタイロフォームAT t25 ■ 壁:アクアフォームLITE吹付 t85 ■ 天井:アクアフォームLITE吹付 t170			
床下換気		■ 基礎パッキン JOTO (玄関・UB周り:気密基礎パッキン)			
防虫防蟻		■ 土壌処理・木部 ガントナーMC			
■ 外 部 仕 上 表				■ 22条地域	
部位		仕上・仕様・メーカー		色番・品番	
屋根		■ ガルバリウム鋼板(t0.35)UK立平 ニスクカラーPro GH 軒先通気金物 日本住環境株式会社【REV-15】		GHK01 Sブラック	
パラペット笠木		■ なし			
破風・鼻隠		■ なし			
雨樋		(軒樋) ■ Panasonic サーフeskエアFS-I型		ミルクホワイト	
		(縦樋) ■ Panasonic S30角樋		ミルクホワイト	
軒天	屋根軒	■ ニチハ軒天5 木目調 910×1820×5		ライト	
	ポーチ軒	■ 神島化学 t= 6mm 軒天ボード エンボス		Wファリーホワイト	
	バルコニー軒	■ なし			
オーバーハング水切り		■ ガルバリウム鋼板 ※外壁合わせ JOTO:HF-A3550		ホワイト	
外壁	通気金物(15mm)	■メイン	ニチハ エモンエクセラード16 Vシリーズ しぶきV	MG/パニラホワイトII	
	※下地面材:タイガーEXハイパー	■アクセントA	なし		
	防火認定 PC030BE-4028	■アクセントB	なし		
玄関ポーチ		■ 床 LIXILパセオ300/PSO-FIO 4		-	
基礎		■ 立上り巾木: モルタル刷毛引き		-	
基礎水切り金物		■ JOTO鋼板製 防鼠材付き水切り JOTO:WMF-N35		ホワイト	
バルコニー	床・内壁	■ 床:FRP防水仕上(グレー) 壁:外壁同仕上げ		-	
	笠木	■ アルミ笠木		ブラック	
外部建具		■ Ykkap APW330 (アルゴンガラス日射遮蔽型 断熱タイプLow-E プルーフ) ・SD、TSで記載がないものは、オペレーターハンドルとする ・オペレーター付サッシは固定網戸とする ・グレモンハンドル式サッシの選択箇所は可動網戸とする		外観 ブラック 内観 外観色と同じ ※網戸付 樹脂スペーサ	
シャッター		■ なし			
軒天通気金物		日本住環境株式会社 SEV-15		ホワイト	
玄関扉		■ YKKapヴェナートD30(D2仕様) タグキーx3、非常用キーx2 (電池式) ※ピタットキー		ドア型: N08N ドア色: ガッシュウォールナット ハンドル: ストレート 色 ブラック	
外部物干し金物		■ 川口技研LP型-550 バルコニー内側壁		ホワイト	
換気フード		■ 局所換気扇(トイレ 浴室 キッチンフード) 防火ダンパー無		外気フード: ホワイト	
		■ ダクトレス熱交換換気システム (日本スティーベル株式会社) VLR-70E 防火ダンパー無		外気フード: W ホワイト	

■ 構 造 概 要					
基礎	■ RCベタ基礎コンクリート				
通し柱・管柱	■ 構造用集成材 105×105		間柱	■ 集成材	
土台	■ 桧 105×105	大引き	■ 桧 90*90	筋交い	■ 構造用製材 火打梁 ■ 鋼製火打(当社基準により米松あり)
桁・梁	■ 構造用製材及び集成材		制震装置	■ Kダンパー (株)アイ・エム・エー	
■ 設 備 装 着 品					
住宅設備	部位	メーカー	商品名 ※ 詳細は見積り、プレゼン参照	見積りNo.	(日付)
	キッチン	LIXIL	■ ES I型D650 食洗器 IH 壁付レンジフードASR	見積り番号 : M24074457351-003-2 (日付) 2024.7.25	
	バックカウンタ ※オプション	LIXIL	■ なし	見積り番号 : (日付)	
	浴室	LIXIL	■ AX1616 ※換気扇	見積り番号 : M24074457351-003-1 (日付) 2024.7.25	
	1Fトイレ	LIXIL	■ ベーシアシャワートイレ 白 ● タオル掛け: KF-AA70D(リング) タンク手洗 有り ● 紙巻き器: CF-AA22H /WA	見積り番号 : M24074457351-003-4 (日付) 2024.7.25	
	2Fトイレ	LIXIL	■ ベーシアシャワートイレ 白 ● タオル掛け: KF-AA70D(リング) タンク手洗 有り ● 紙巻き器: CF-AA22H /WA	見積り番号 : M24074457351-003-5 (日付) 2024.7.25	
	洗面台	LIXIL	■ EV W750(D500タイプ) 扉:グロスホワイト [引出しタイプ シングルハンドシャワー スタンダードLED三面鏡 ● タオル掛け: KF-AA71D(バー)	見積り番号 : M24074457351-003-3 (日付) 2024.7.25	
給排水設備	給湯器	■ エコキュート370L Panasonic NSシリーズ スタンダードモデル 追い焚きフルオート			
	排水	■ 下水			
	外水栓	■ 1 カ所 (平面図参照)	■ 外部立栓柱: PVC製 水栓柱12型【前澤化成工業】		
	外部ガーデンパン	■ 無し			
	その他	■ 洗濯機用単水栓: 緊急止水弁付 ■ 洗濯機用排水:トラップ金物(標準) ■ 排水さや管(長期優良住宅仕様)			
ガス配管設備	■ なし (平面図参照)				
電気設備	インターホン	■ パナソニック VL-SZ30KL			
	TVアンテナ	■ UHF + BS・110度CS／CSアンテナ [2K・4K・8K対応] ■ホワイト			
	エアコン	■ あり 設置場所: LDK 洋室②			
	ソーラー ※標準搭載	■ あり(Qセルズ) 12 枚 5.22 KW Re.RISE-G2 435 (1722×1134×30) ■ 蓄電池:無			
	その他				

	浜 岡 一 級 総 合 設 計 事 務 所 一級建築士事務所 静岡県知事登録第 (10)2441 号 一級建築士 大臣登録第 365879 号 西原利昌	LIFEFUND PG HOUSE	株式会社 LIFEFUND InDesign office 一級建築士事務所 事務所登録 (2)第7595号 一級建築士登録 第179770号 鈴木 達男 〒432-8023 静岡県浜松市中央区鴨江3丁目70番23号	年 月 日	件名		設計	IC	工務	図 番
				2024.8.10	PG有玉西 分譲		倉田		青島	1-1
				縮尺	図面					
					仕上表 1					


内 部 仕 上 表 （壁下地:石膏ボード12.5mm/天井下地:9.5mm）※脱衣室:床合板特類 下地									
階		床	巾木	壁	品番	廻 縁	天 井	品番	特記事項
1F	ポーチ	LIXILパセオ300/PSO-FIO 4							巾木立上り部はモルタル金鍍仕上
	玄関	LIXILパセオ300/PSO-FIO 4	ライン巾木(W)	ビニルクロス	SLP-250	突付	ビニルクロス	SLP-250	巾木立上り部はモルタル金鍍仕上
	ホール①	イタ銘木フロアーラステックt12 ブラックチェリー3P	ライン巾木(W)	ビニルクロス	SLP-250	突付	ビニルクロス	SLP-250	
	LDK	イタ銘木フロアーラステックt12 ブラックチェリー3P	ライン巾木(W)	ビニルクロス	SLP-250	突付	ビニルクロス	SLP-250	
	畳コーナー	1畳縁ありスタイロ畳 t55	畳寄せ	ビニルクロス	SLP-250	突付	ビニルクロス	SLP-250	畳縁:高田織物 浮No.13
	押入	イタ銘木フロアーラステックt12 ブラックチェリー3P	雑巾摺	ビニルクロス	SLP-250	突付	ビニルクロス	SLP-250	
	洗面所	フロアタイルt2.3 サンゲツIS-2070	H40ソフト巾木W97	ビニルクロス	SLP-250	突付	ビニルクロス	SLP-250	
2F	WC①	フロアタイルt2.3 サンゲツIS-2070	H40ソフト巾木W97	ビニルクロス	SLP-250	突付	ビニルクロス	SLP-250	
	ホール②	イタ銘木フロアーラステックt12 ブラックチェリー3P	ライン巾木(W)	ビニルクロス	SLP-250	突付	ビニルクロス	SLP-250	
	洋室①	イタ銘木フロアーラステックt12 ブラックチェリー3P	ライン巾木(W)	ビニルクロス	SLP-250	突付	ビニルクロス	SLP-250	
	洋室②	イタ銘木フロアーラステックt12 ブラックチェリー3P	ライン巾木(W)	ビニルクロス	SLP-250	突付	ビニルクロス	SLP-250	
	洋室③	イタ銘木フロアーラステックt12 ブラックチェリー3P	ライン巾木(W)	ビニルクロス	SLP-250	突付	ビニルクロス	SLP-250	
	WIC	イタ銘木フロアーラステックt12 ブラックチェリー3P	H40ソフト巾木W97	ビニルクロス	SLP-250	突付	ビニルクロス	SLP-250	
	WC②	フロアタイルt2.3 サンゲツIS-2070	H40ソフト巾木W97	ビニルクロス	SLP-250	突付	ビニルクロス	SLP-250	
物入・収納・CL etc		※接続する部屋と同仕様とする							

上框 & 付框	■ LIXILラシッサS 付框30×150 (全周廻し) 色: クリエペール		
階段	■ LIXIL KA 階段	ササラ:	プレシャスホワイト
	段板:	クリエペール	蹴込板: プレシャスホワイト
	ラウンド手摺:	クリエペール	手摺金物 プレシャスホワイト
	上段框:	クリエペール	長尺笠木156: LIXIL クリエペール
窓枠 ※YKKap	■ YKKap窓枠スルムタイプ	色	ピュアプレーン
	※浴室ドア枠 フクビ3方枠	[]	
キッチン笠木 カウンター	■ ゴム集成カウンター(オスモカラー)	色	30627ロアーグリアmatt
	形状 L型(ジョイント加工)	t=30	
天井点検口	■ 天井アルミ点検口枠 450角	TAN45BW	フクビ化学工業 ミルキーホワイト
床下収納庫	■ 高気密型床下点検口断熱型 SPF-R6060 城東テクノ	収納付	(脱衣室) アイボリー(IV)
トイレ棚	■ 2階トイレ	D250	アートランバー棚(シェルホワイト)
室内物干し金物	■ なし		
1トイレ バックカウンター	■ アートランバー棚(シェルホワイト)	色	t=20
下足入	■ LIXILラシッサS	色	プレシャスホワイト
	サイズ: W800 D400	形状:	二の字型

支給品	■ 無し
備考	

内 部 建 具 表								
LIXIL		建具色：クリエイペール		枠色 ： 扉同色		※その他、下記特記による		
ラシッサS(標準)		把手 ： スクエアL (シャインニッケル) 丁番 固定枠(156) 外付戸当り ガイドピン床色合せ 引戸のみ上吊Wソフトモーション						
階	No	室名	形式	枠外W サイズ	デザイン	枠色	特記事項	
				枠外H サイズ	建具色	把手		
1	1	LDK	片開き戸	—	LGC	—		
	WD			2000	—	—		
	2	洗面所	片引き戸	—	LAA	—	明り窓・表示錠	
	WD			2000	—	—		
	3	押入	折れ戸	—	LAA	—	角型Lタテ取付	
	WD			2000	—	—		
	4	パントリー	観音開	—	LAA	—		
	WD			2000	—	—		
	5	物入	観音開	—	LAA	—		
	WD			2000	—	—		
	6	WC①	片開き戸	—	LAA	—	明り窓・表示錠	
	WD			2000	—	—		
2	7	WC②	片開き戸	—	LAA	—	明り窓・表示錠	
	WD			2000	—	—		
	8	洋室①	片開き戸	—	LAA	—		
	WD			2000	—	—		
	9	洋室②	片開き戸	—	LAA	—		
	WD			2000	—	—		
	10	洋室③	片開き戸	—	LAA	—		
	WD			2000	—	—		

	浜 岡 一 級 総 合 設 計 事 務 所	LIFEFUND 株式会社 LIFEFUND InDesign office 一級建築士事務所 PG HOUSE 事務所登録 (2) 第7595号 一級建築士登録 第179770号 鈴木 達男 〒432-8023 静岡県浜松市中央区鴨江3丁目70番23号	年月日	件名		設計	IC	工務	図 番
			2024.8.10	PG有玉西 分譲		倉田	0	青島	1-2
			縮尺	図面	仕上表 2				

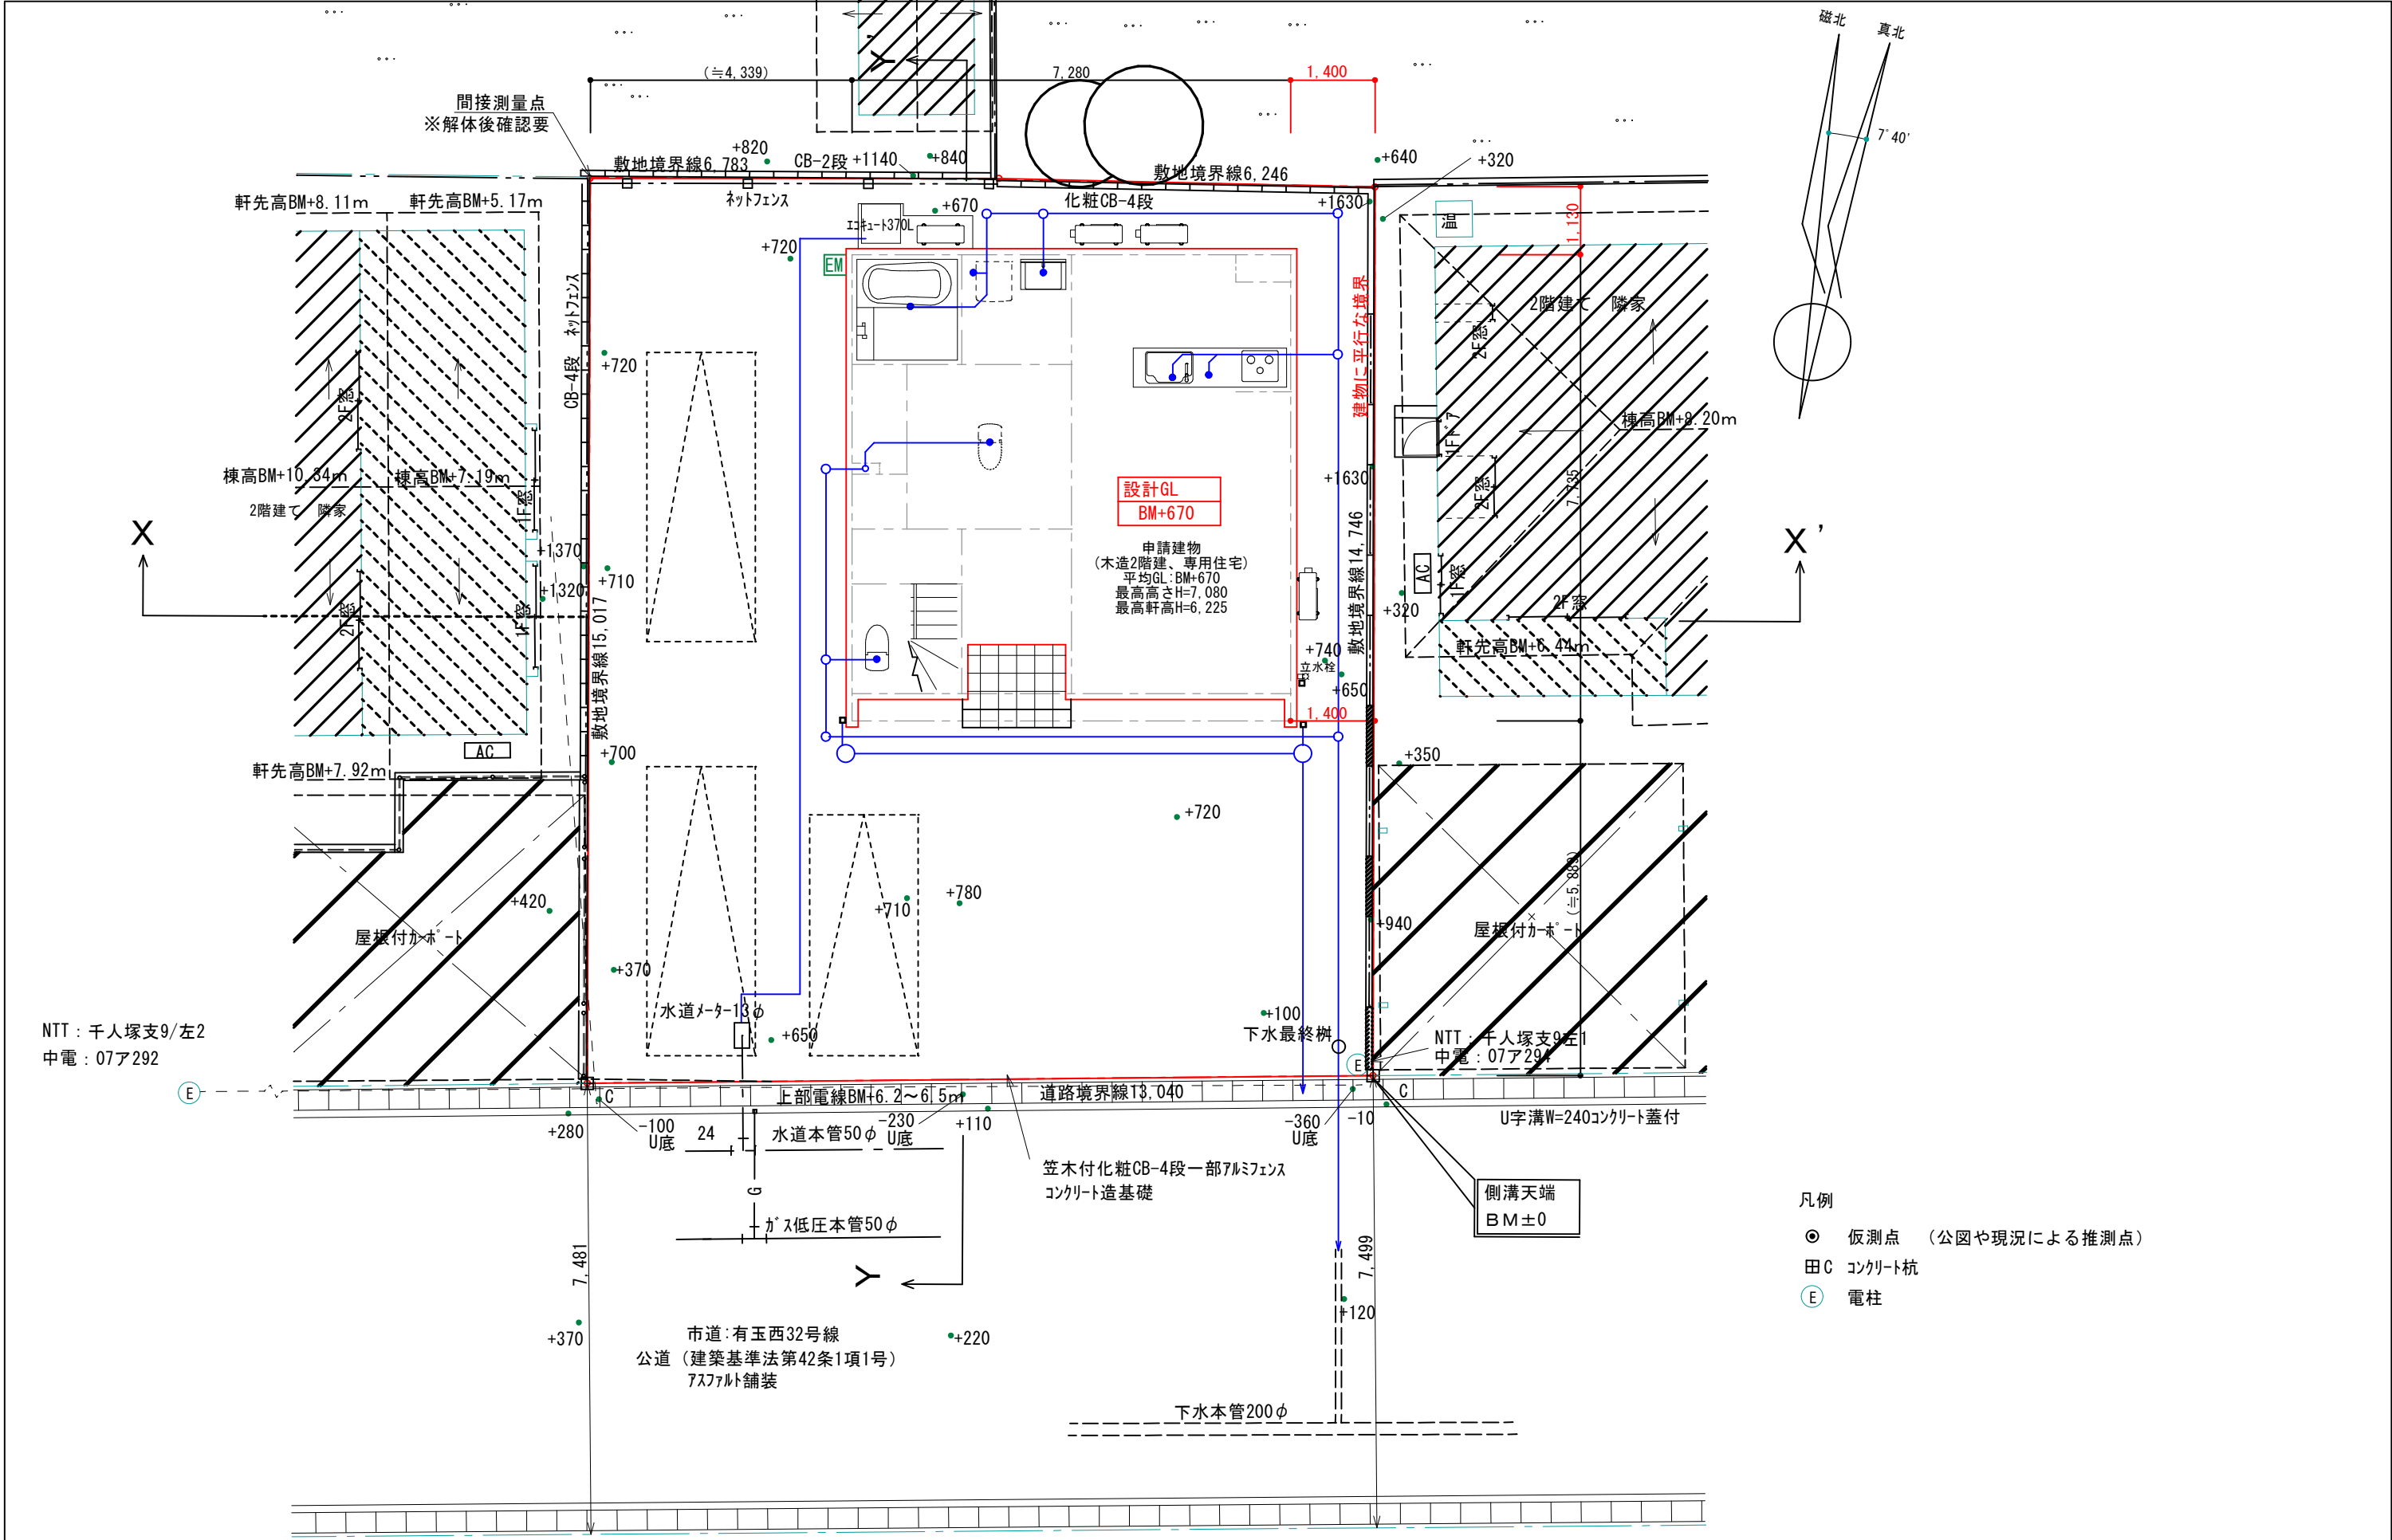

訂正	浜岡一級総合設計事務所 一級建築士事務所 静岡県知事登録第 (10) 2441 号 一級建築士 大臣登録第 365879 号 西原利昌	LIFEFUND PG HOUSE	株式会社 LIFEFUND InDesign office 一級建築士事務所 事務所登録 (2) 第7595号 一級建築士登録 第179770号 鈴木 達男 〒432-8023 静岡県浜松市中央区鴨江3丁目70番23号	年月日 2024. 8. 10	件名 PG有玉西分譲 新築工事		設計	IC	工事	図番
				縮尺 1/50	図名 配置図		倉田		青島	2-1

7.280

7.735

A

建築面積算入部分

建築面積求積図 S=1/100

建築面積求積表

番号	計算式	(m)	面積 (㎡)
A	7.280 × 7.735		56.3108
合計			56.3108 56.31 (17.0坪)

1.8201.8203.640

7.280

①②③

6.3707.280

1階床面積図 S=1/100

1階床面積求積表

番号	計算式	(m)	面積 (㎡)
①	1.820 × 7.280		13.2496
②	1.820 × 6.370		11.5934
③	3.640 × 7.280		26.4992
合計			51.3422 51.34

1.8205.460

7.280

④⑤

6.370

2階床面積図 S=1/100

2階床面積求積表

番号	計算式	(m)	面積 (㎡)
④	1.820 × 7.280		13.2496
⑤	5.460 × 6.370		34.7802
合計			48.0298 48.02

延べ床面積表

	番号	(m)	面積 (㎡)
1階床面積	①②③		51.34
2階床面積	④⑤		48.02
合計			99.36 (30.0坪)

訂正

浜岡一級総合設計事務所
一級建築士事務所 静岡県知事登録第 (10)2441 号
一級建築士 大臣登録第 365879 号 西原利昌

LIFEFUND
PG HOUSE

株式会社 LIFEFUND InDesign office 一級建築士事務所
事務所登録 (2) 第7595号 一級建築士登録 第179770号 鈴木 達男
〒432-8023 静岡県浜松市中央区鴨江3丁目70番23号

年月日
2024.8.10
縮尺
1/100


件名
PG有玉西分譲 新築工事
図名
求積図


設計
倉田


IC

工事
青島


図番
2-2

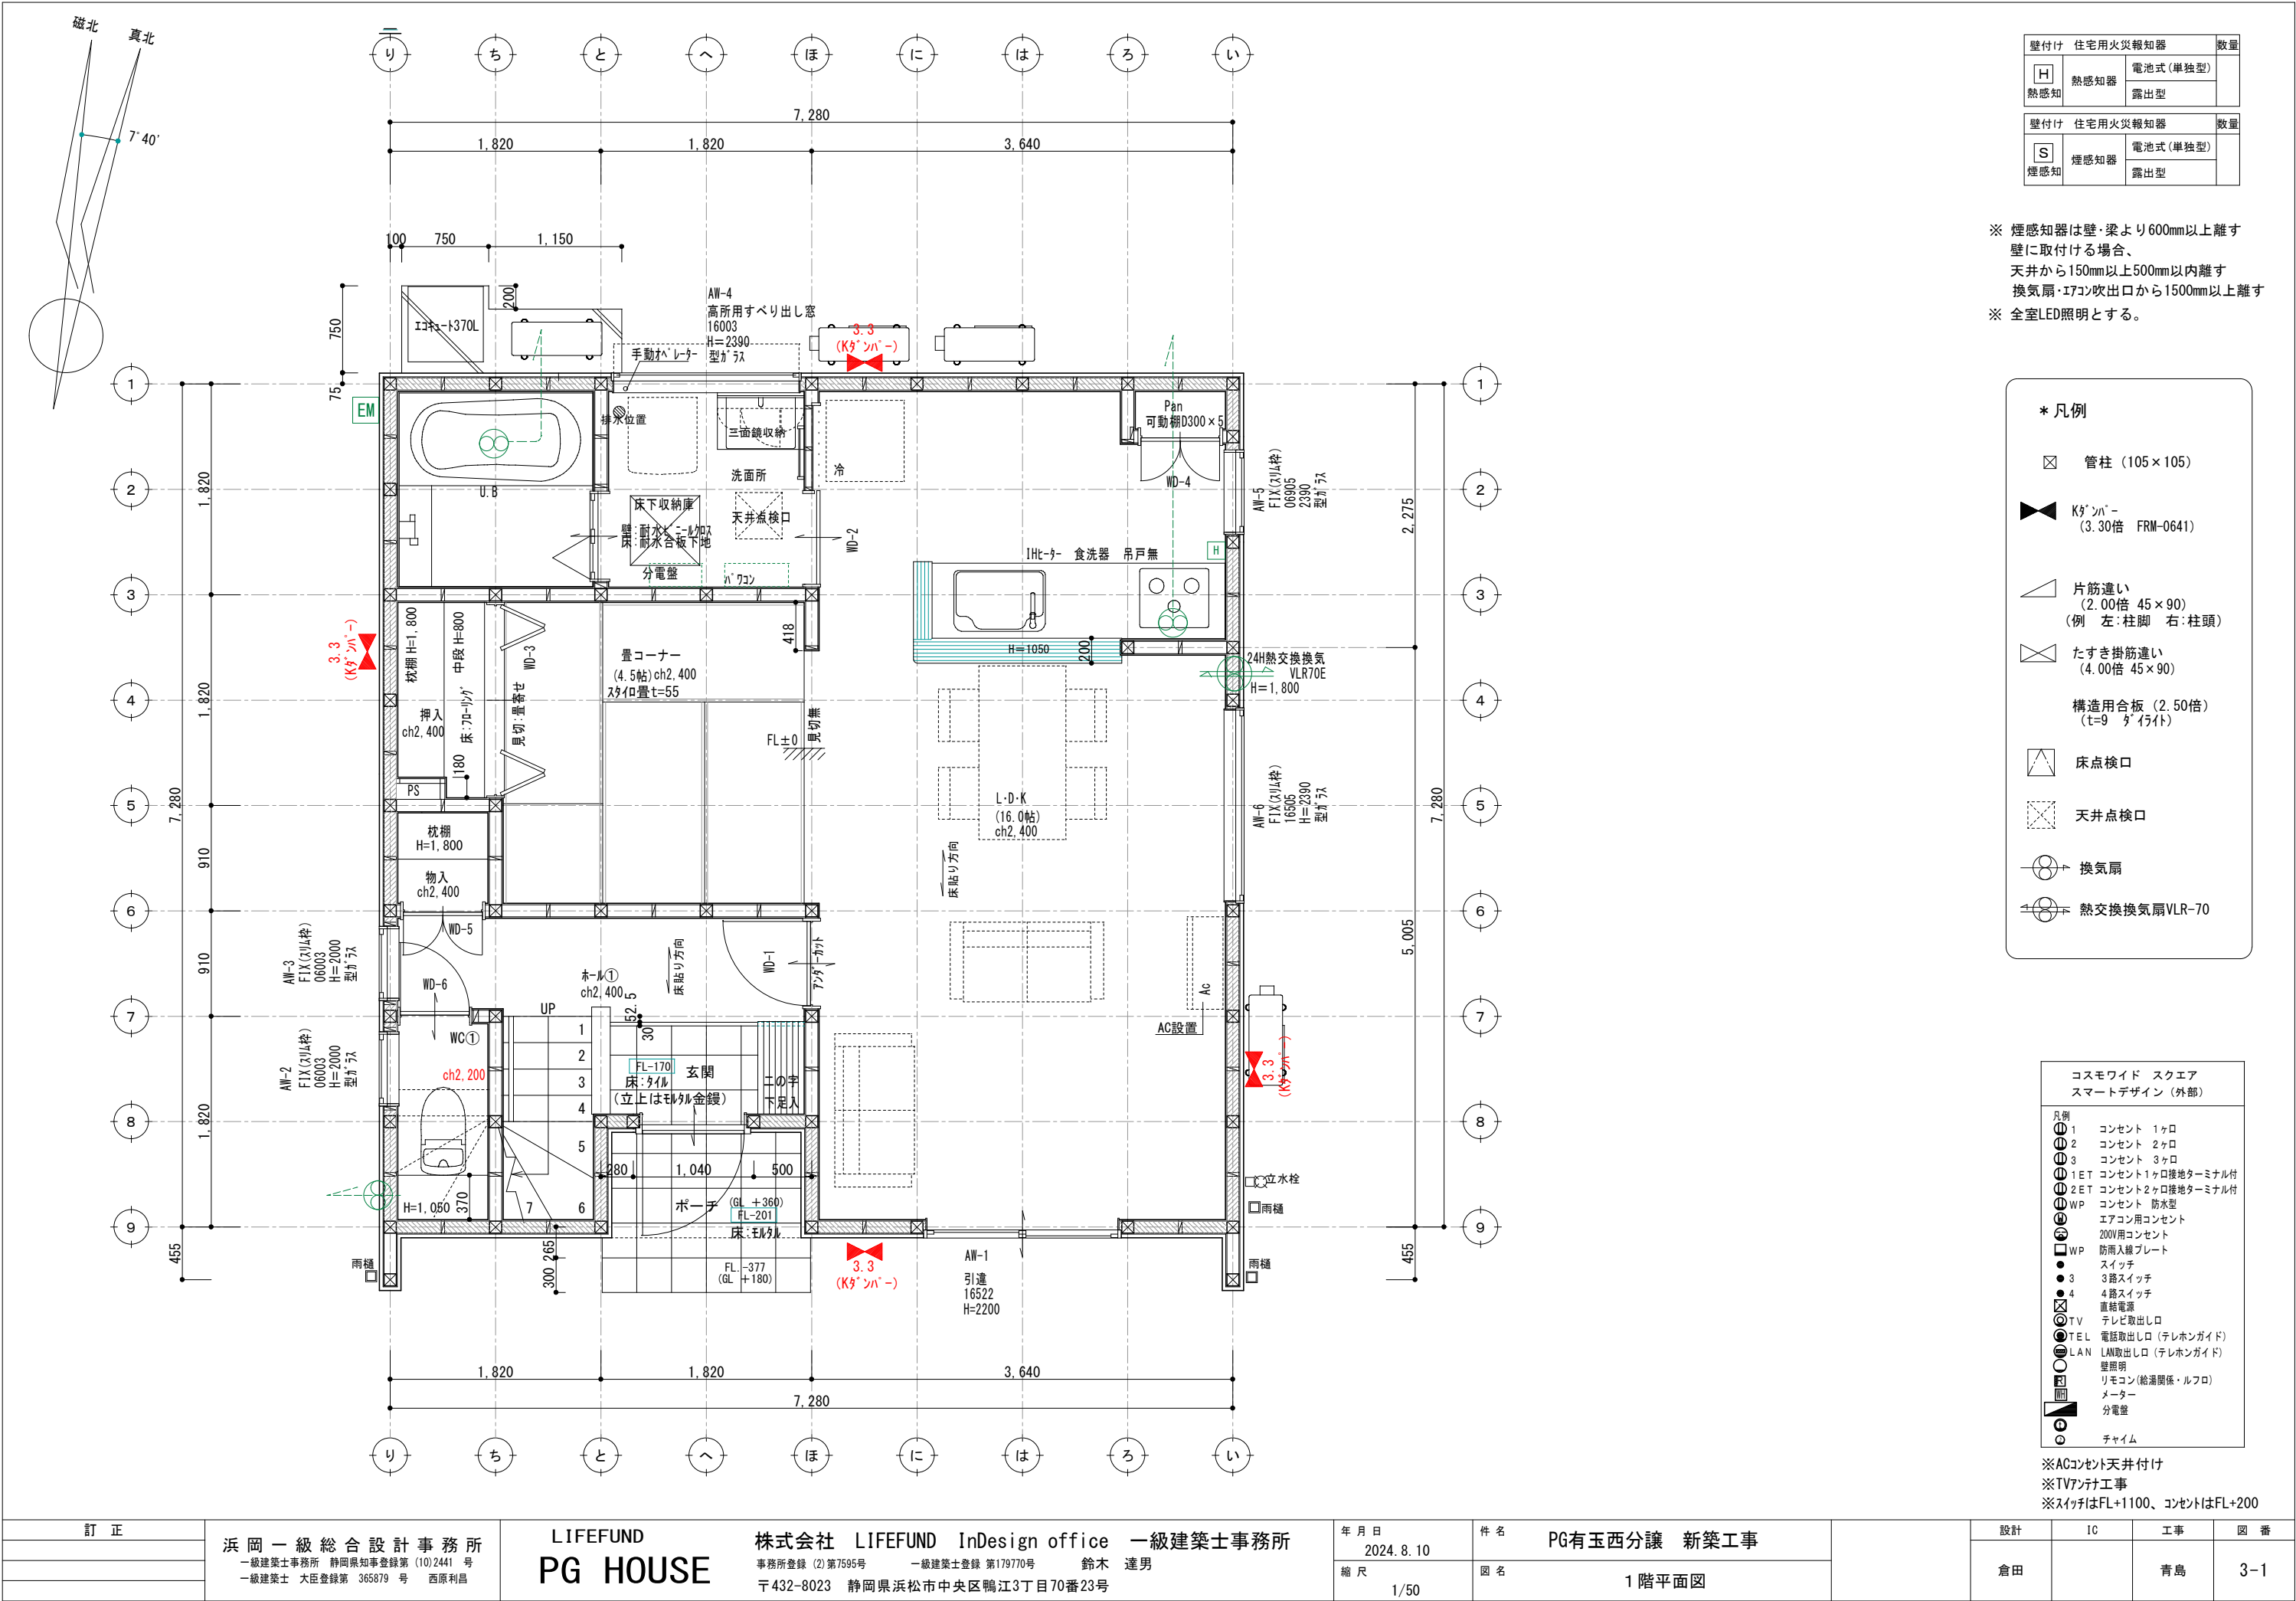

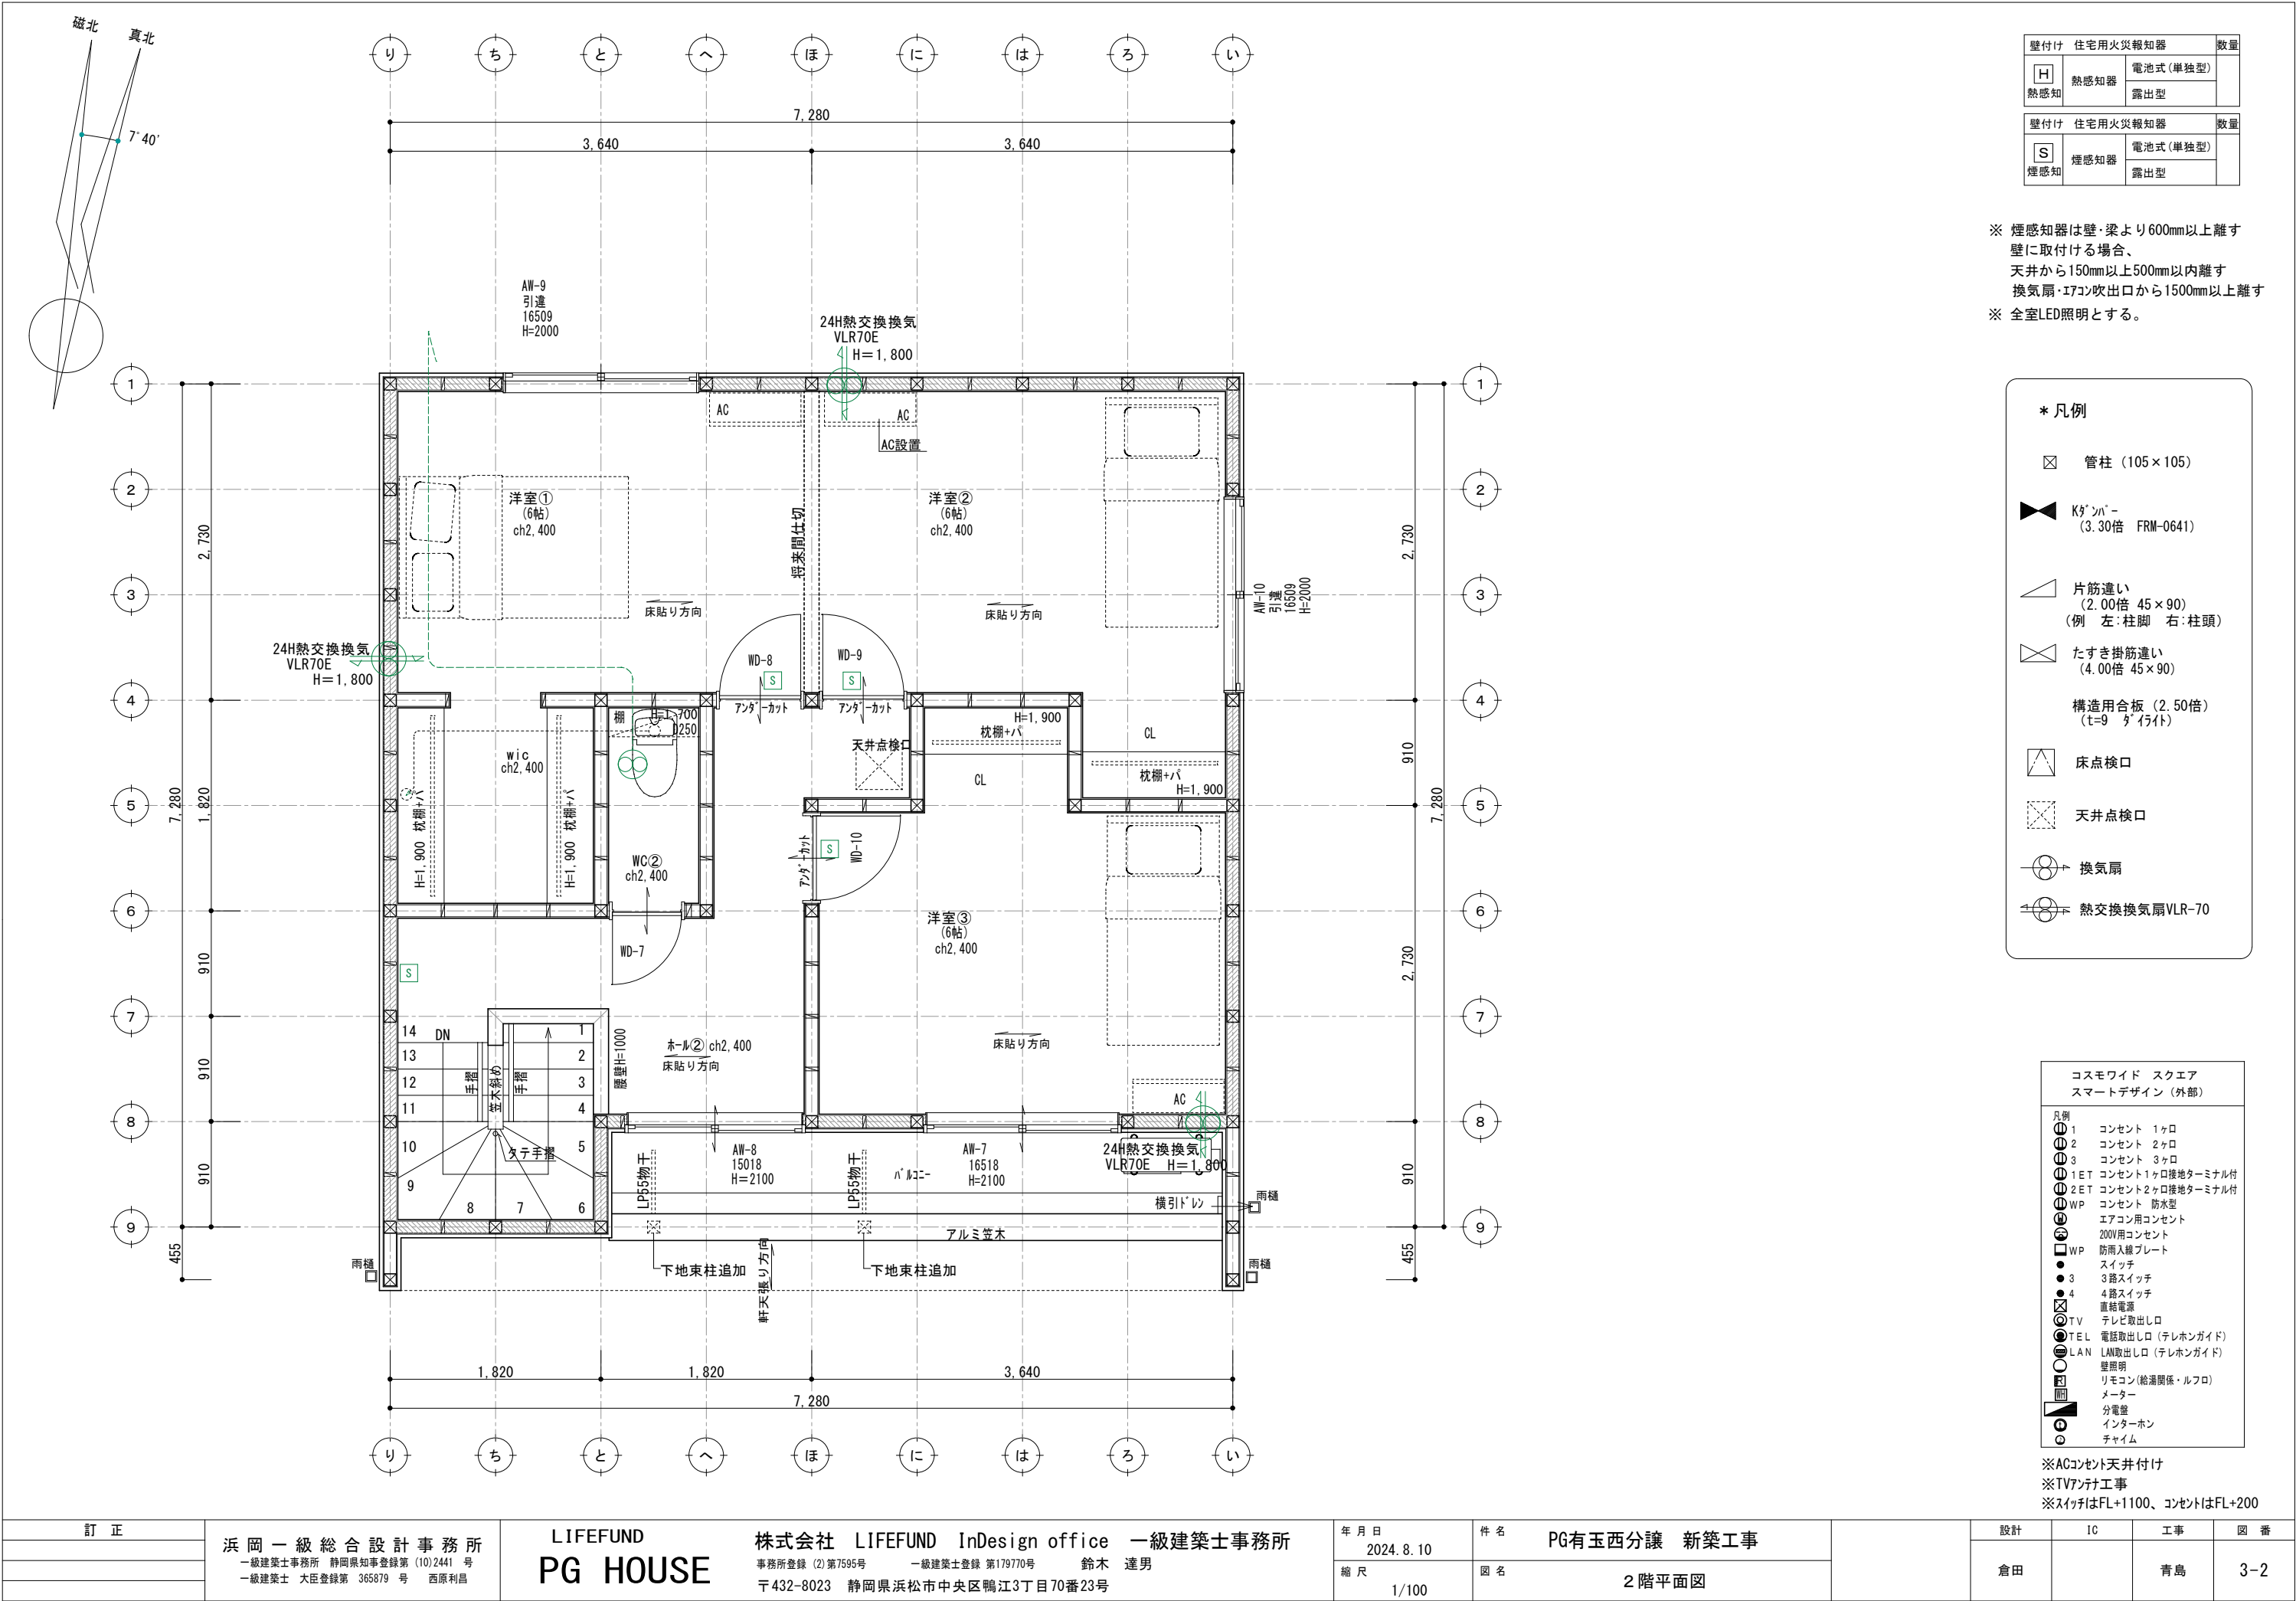


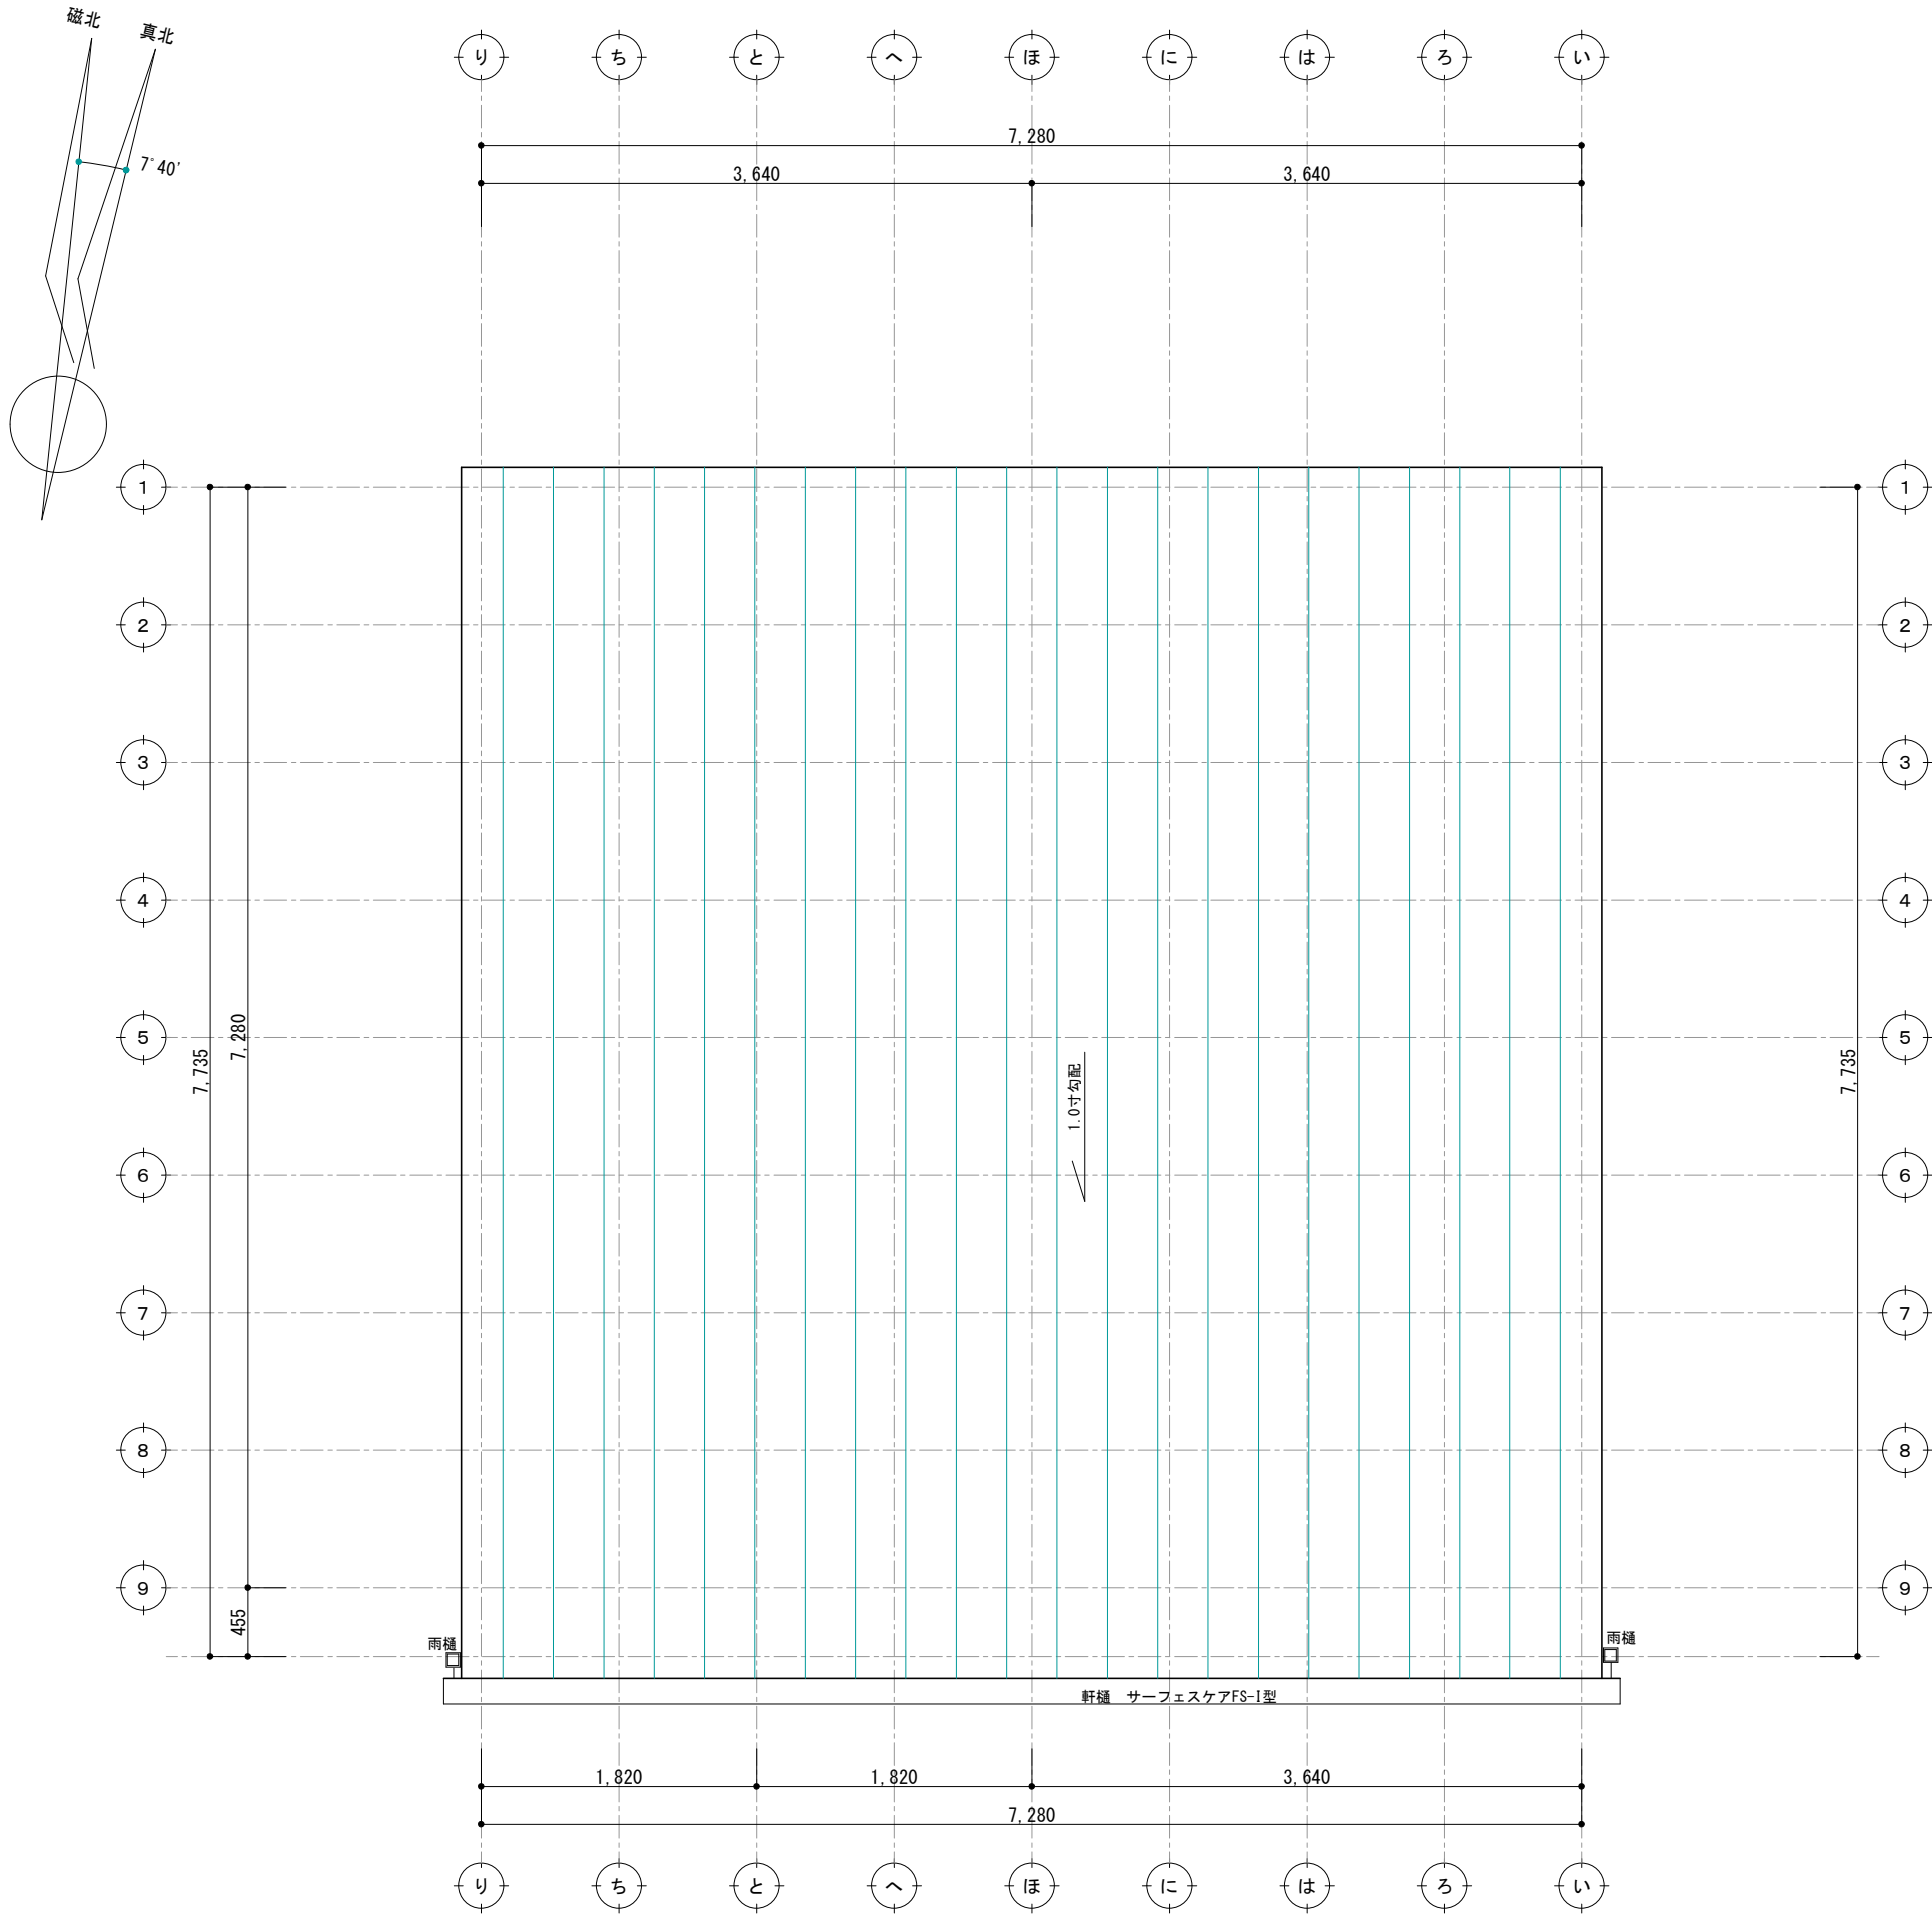


訂 正	浜 岡 一 級 総 合 設 計 事 務 所 一級建築士事務所 静岡県知事登録第 (10)2441 号 一級建築士 大臣登録第 365879 号 西原利昌	LIFEFUND PG HOUSE	株式会社 LIFEFUND InDesign office 一級建築士事務所 事務所登録 (2)第7595号 一級建築士登録 第179770号 鈴木 達男 〒432-8023 静岡県浜松市中央区鴨江3丁目70番23号	年 月 日 2024. 8. 10	件 名 PG有玉西分譲 新築工事		設計	IC	工事	図 番
				縮 尺 1/100	図 名 屋根伏図		倉田		青島	3-3

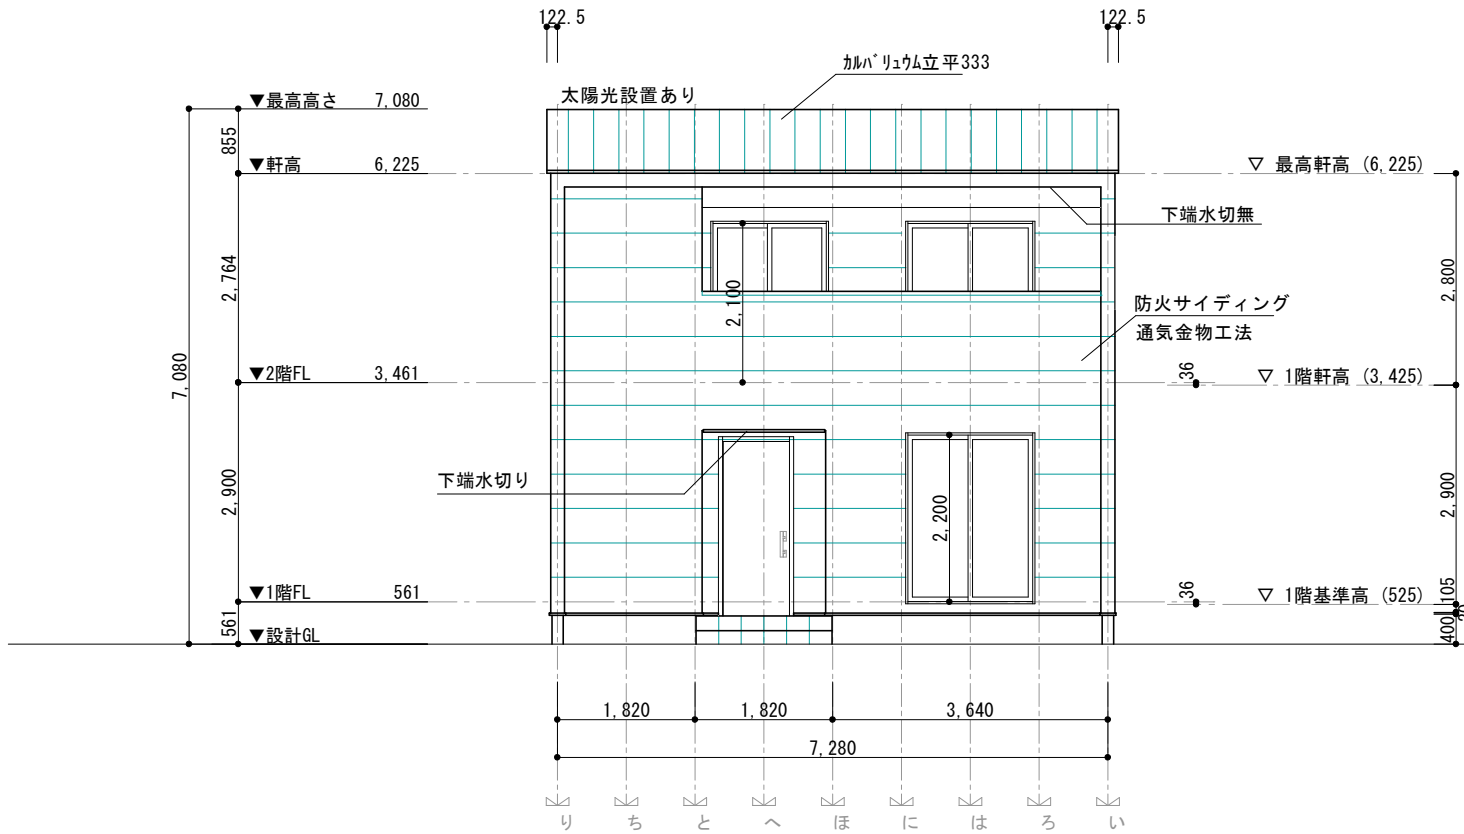


南側立面図 S=1/100

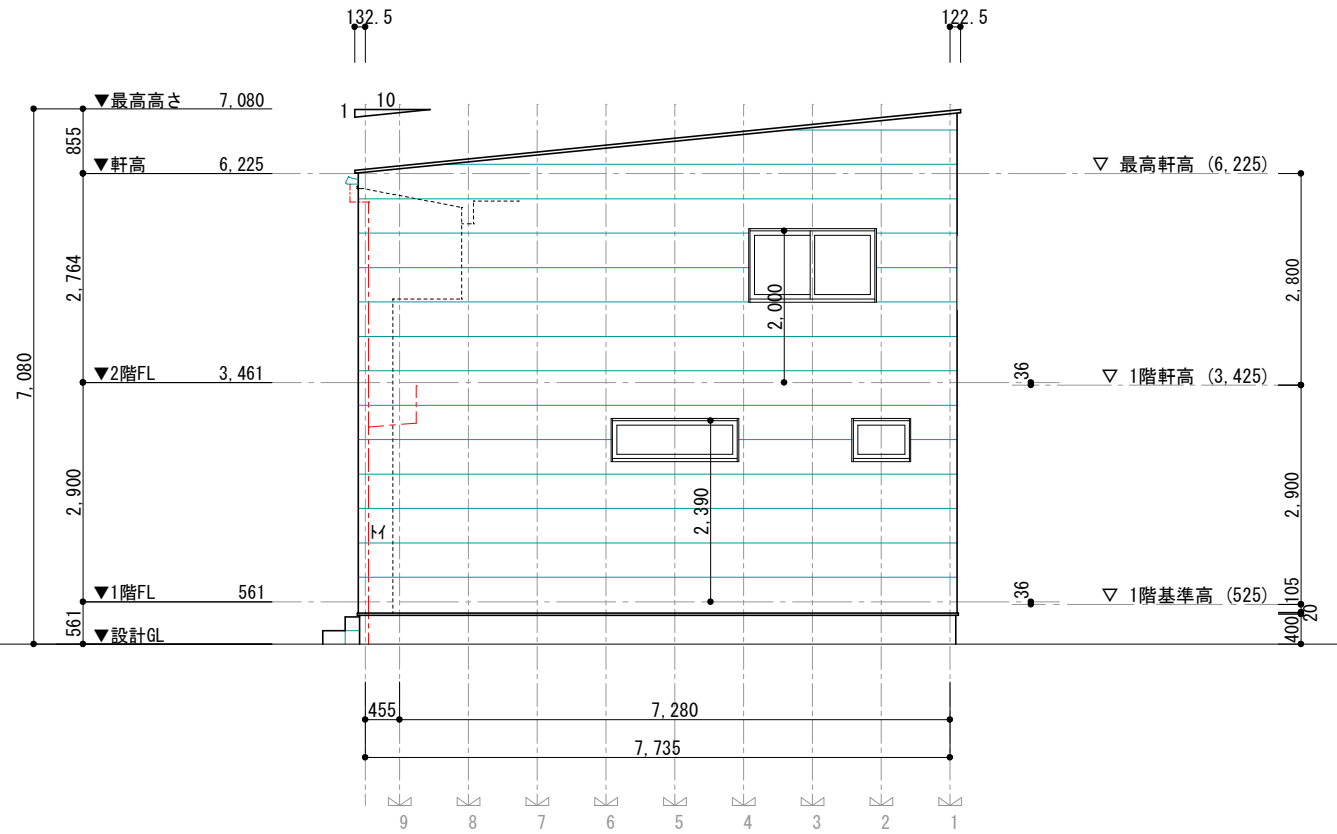

東側立面図 S=1/100

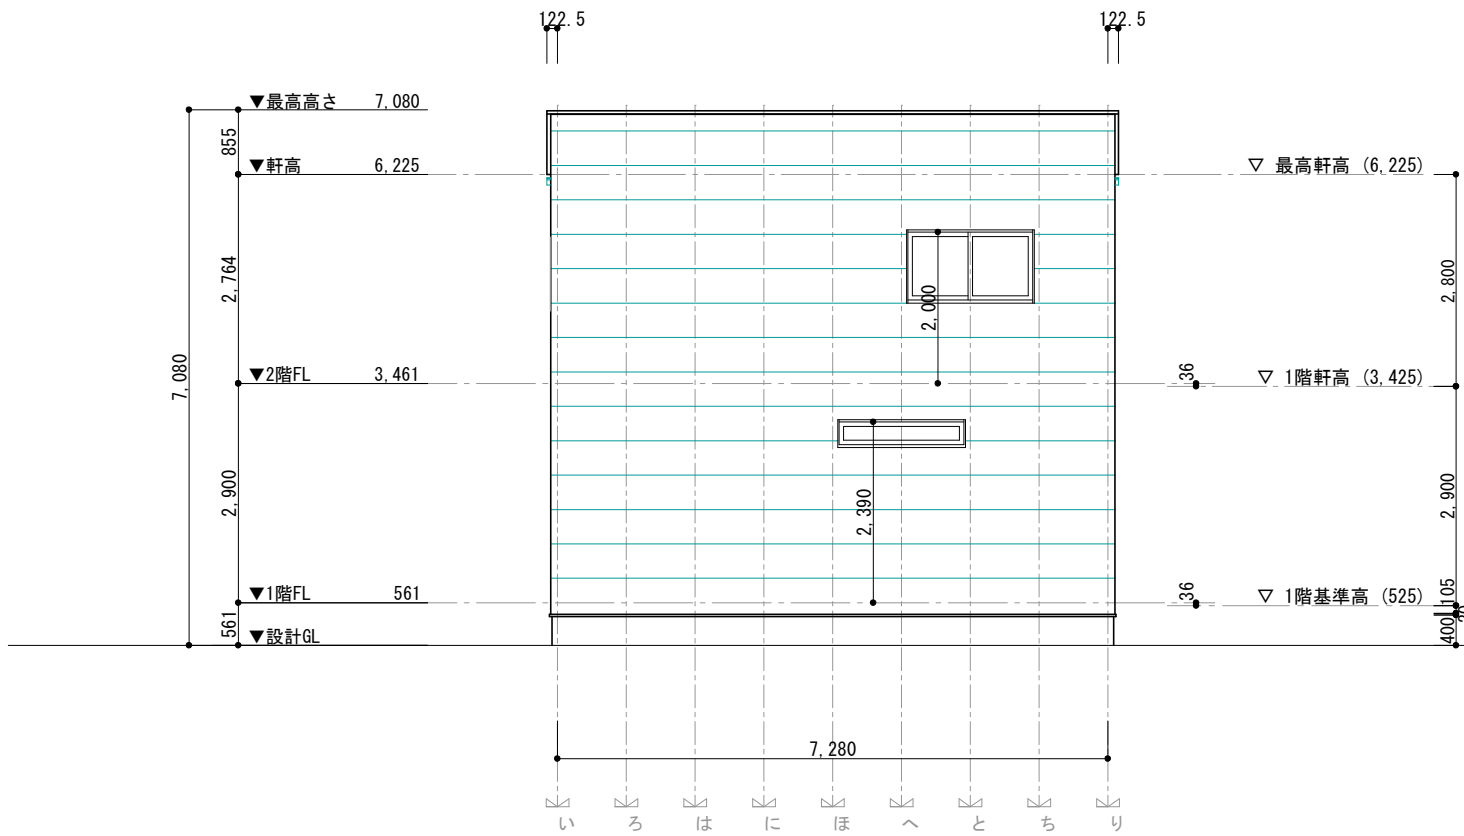


北側立面図 S=1/100

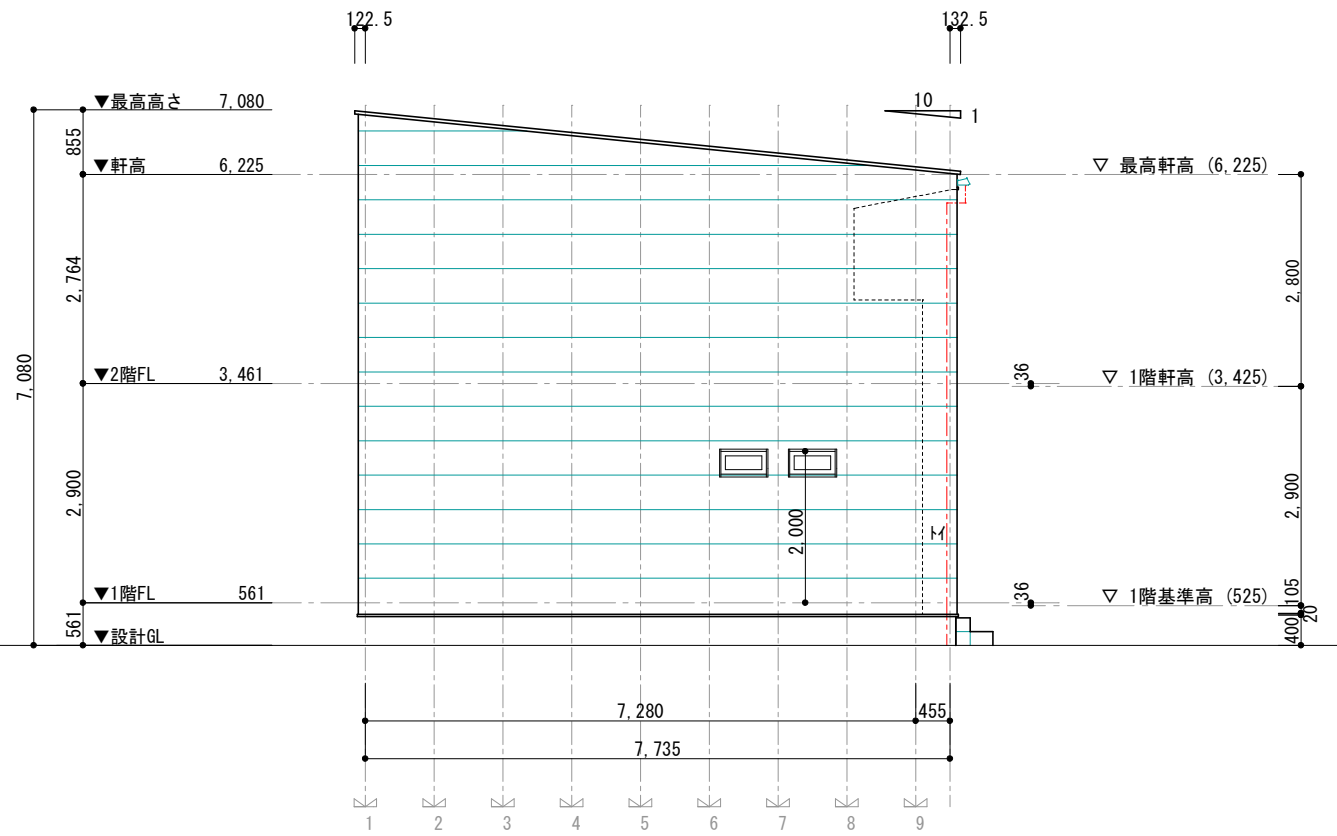


西側立面図 S=1/100


訂正	浜岡一級総合設計事務所 一級建築士事務所 静岡県知事登録第(10)2441号 一級建築士 大臣登録第 365879号 西原利昌	LIFEFUND PG HOUSE	株式会社 LIFEFUND InDesign office 一級建築士事務所 事務所登録(2)第7595号 一級建築士登録 第179770号 鈴木 達男 〒432-8023 静岡県浜松市中央区鴨江3丁目70番23号	年月日 2024.8.10	件名 PG有玉西分譲 新築工事		設計	IC	工事	図番
				縮尺 1/100	図名 立面図		倉田		青島	4

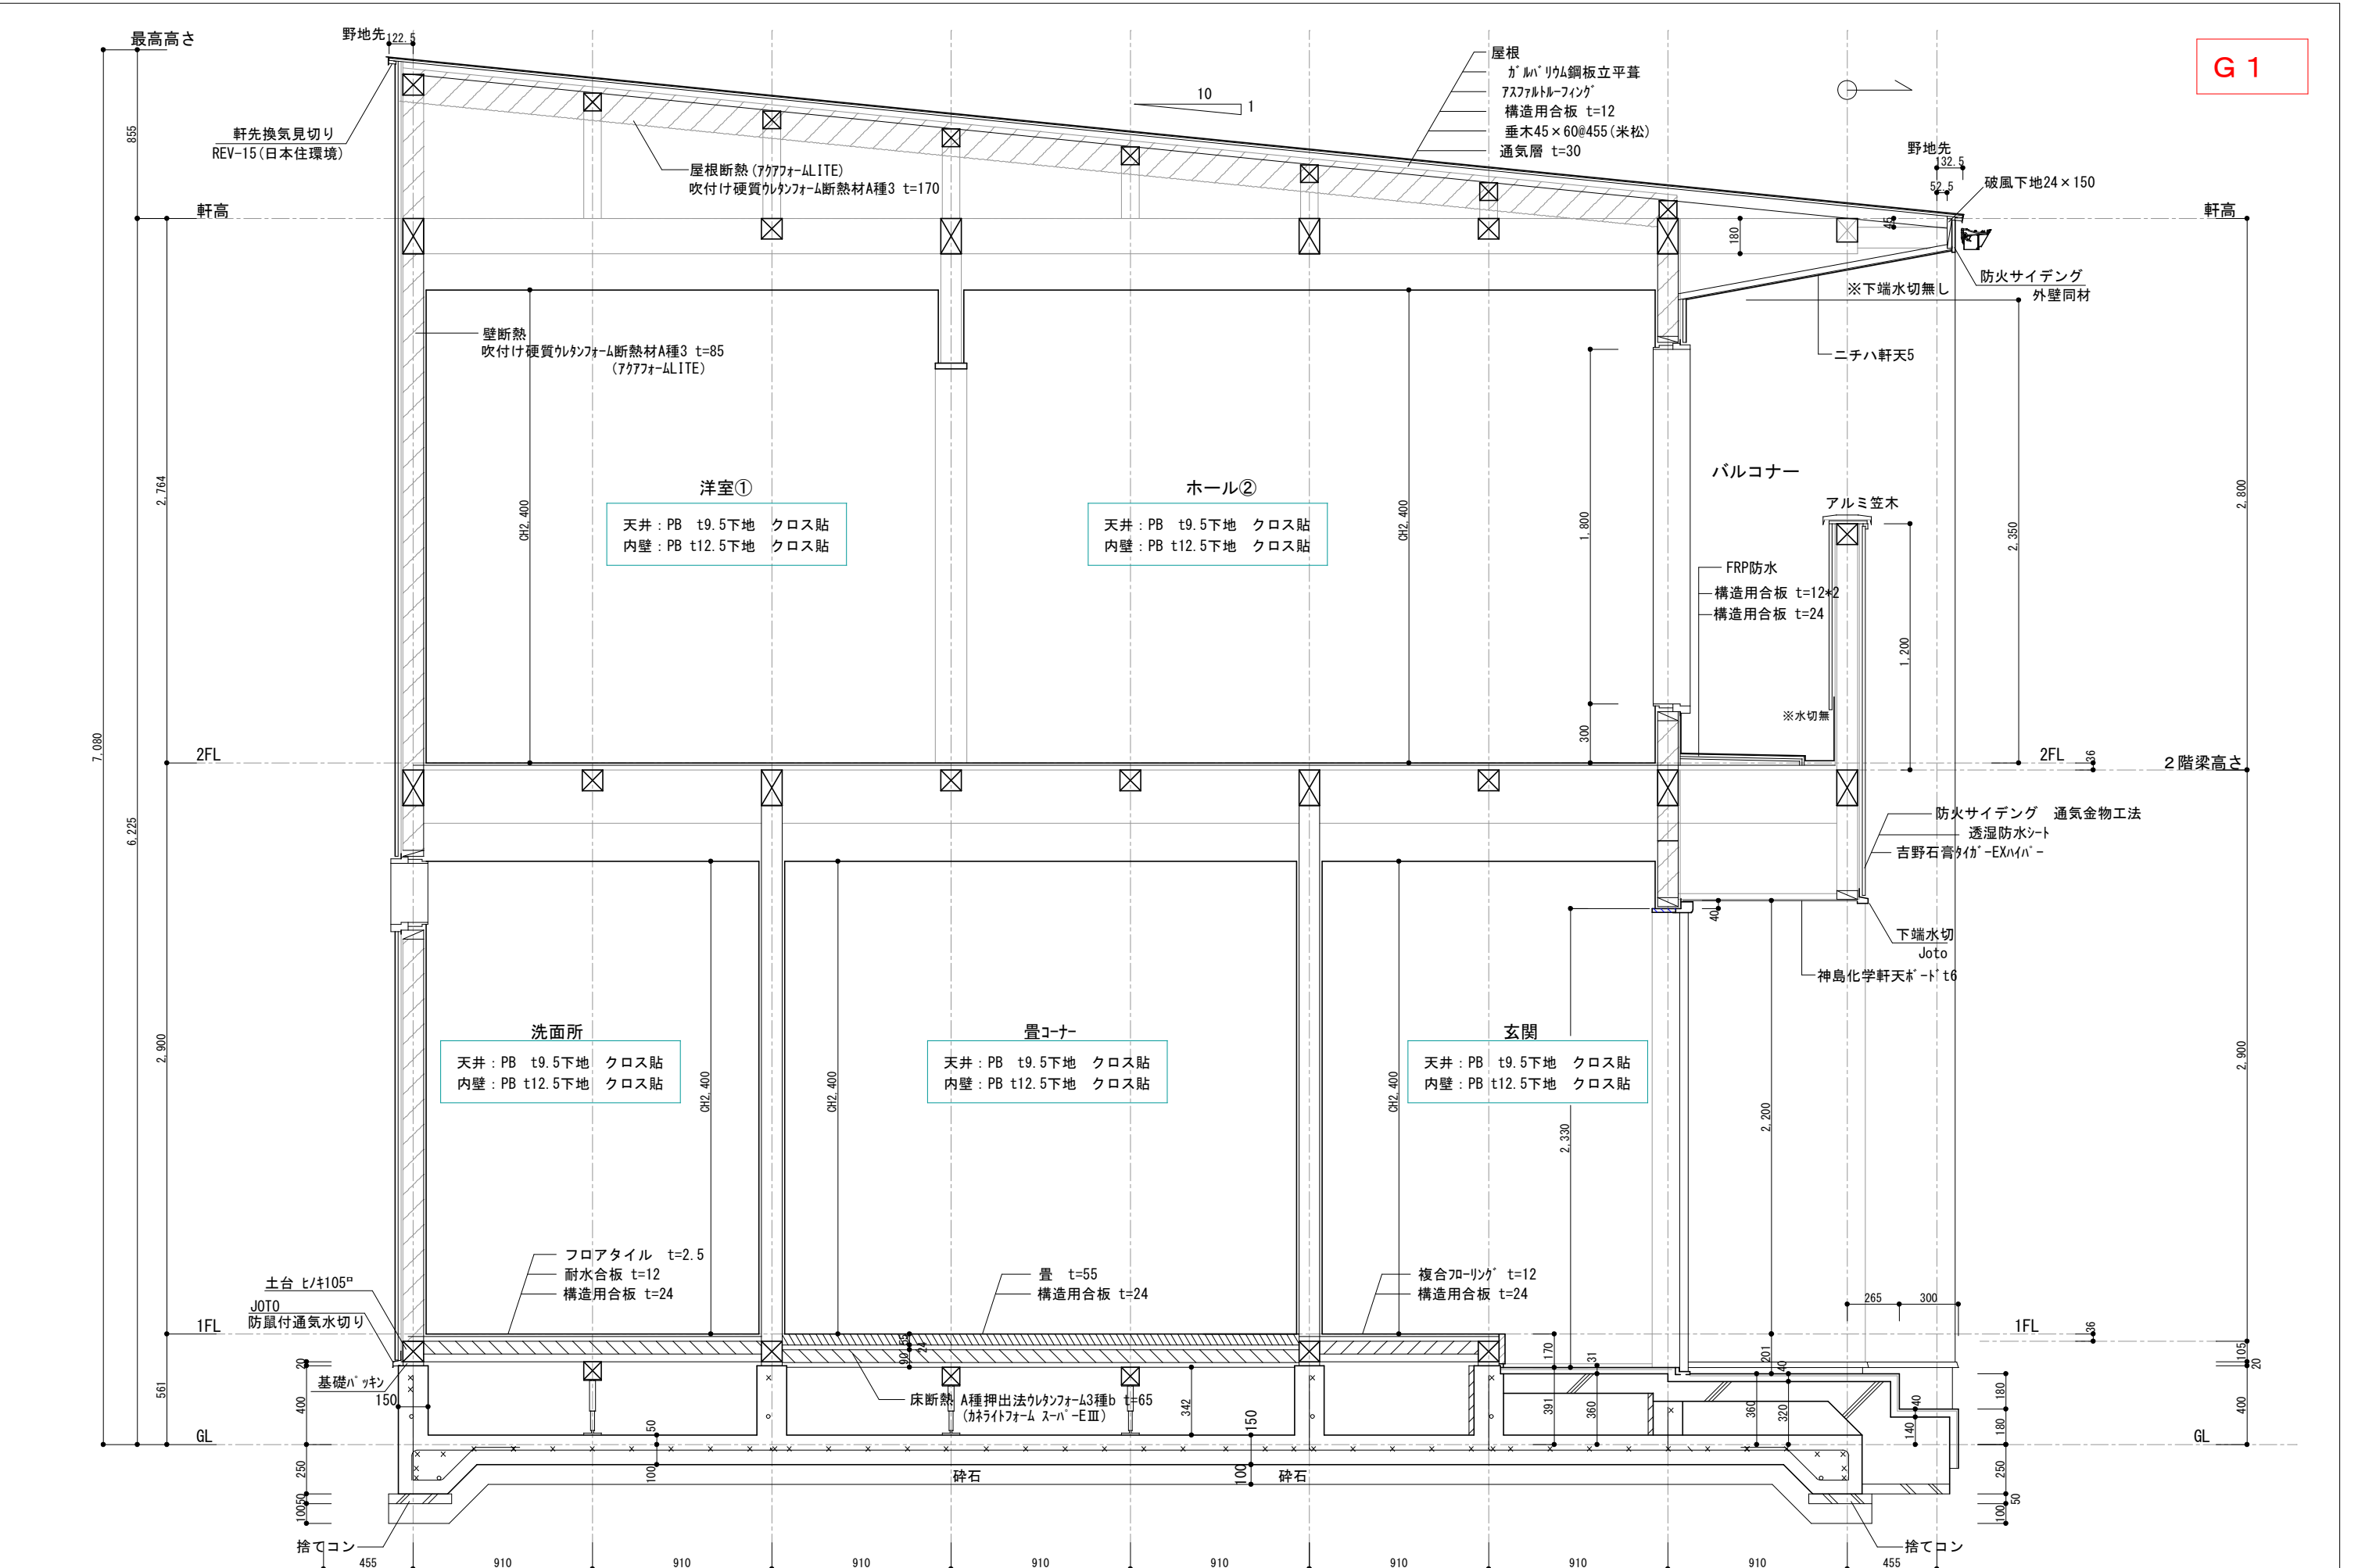


訂正	浜岡一級総合設計事務所 一級建築士事務所 静岡県知事登録第 (10)2441 号 一級建築士 大臣登録第 365879 号 西原利昌	LIFEFUND PG HOUSE	株式会社 LIFEFUND InDesign office 一級建築士事務所 事務所登録 (2)第7595号 一級建築士登録 第179770号 鈴木 達男 〒432-8023 静岡県浜松市中央区鴨江3丁目70番23号	年月日 2024. 8. 10	件名 PG有玉西 分譲 新築工事	設計 倉田	IC	工事 青島	図番 5-1
				縮尺 1/30	図名 矩計図				

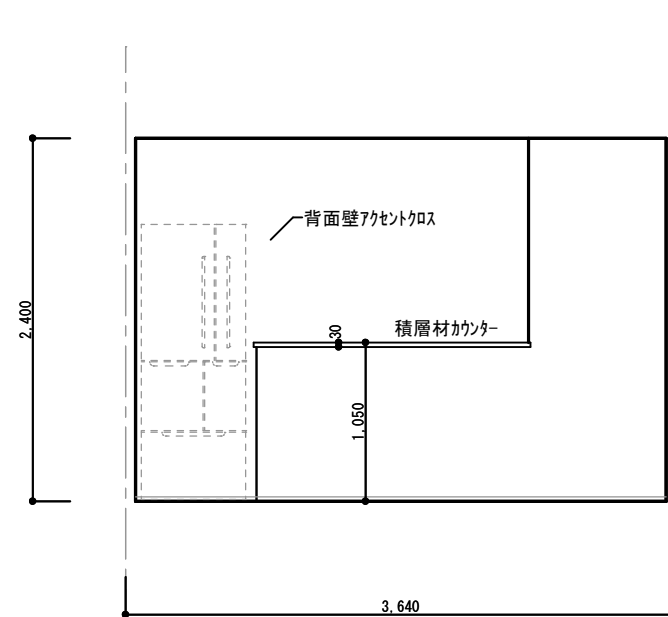


LDK 南面

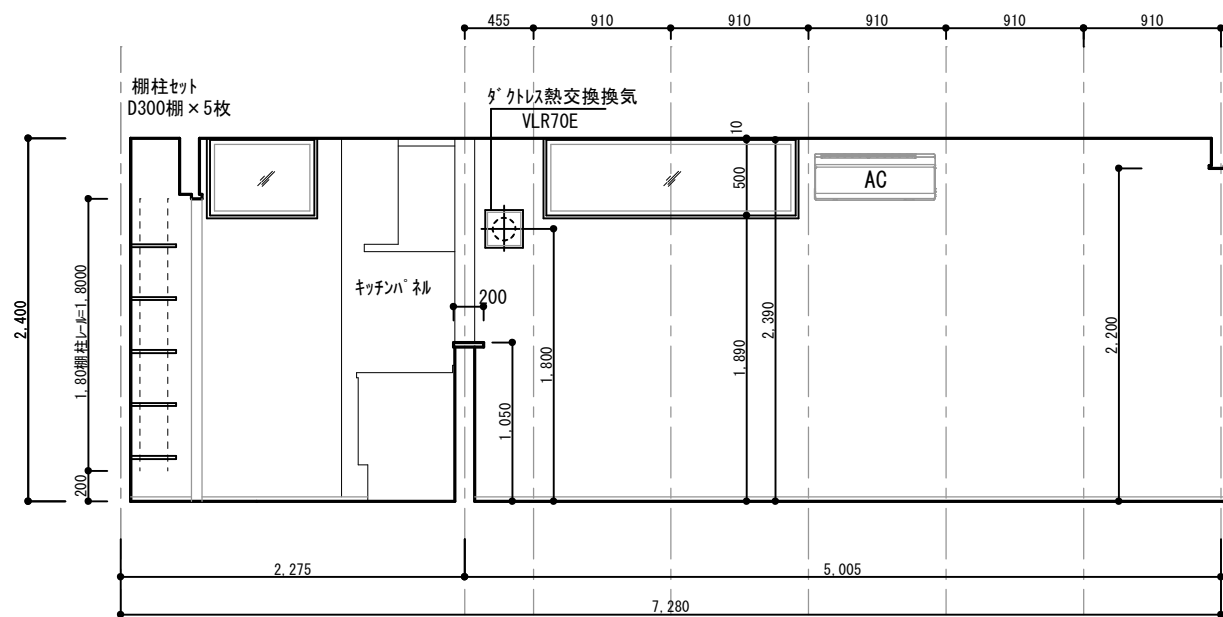


LDK 東面

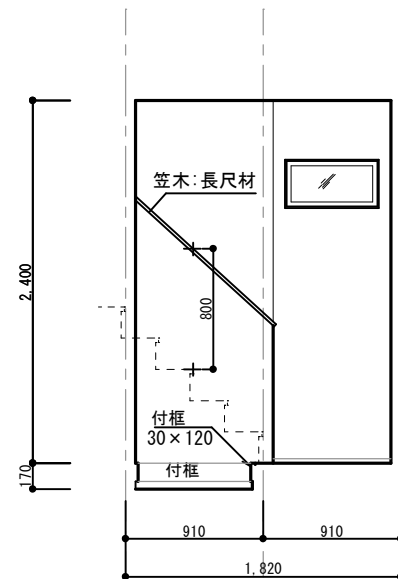


玄関 西面

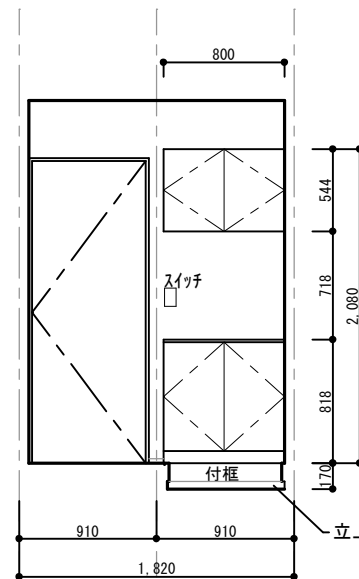


玄関 東面

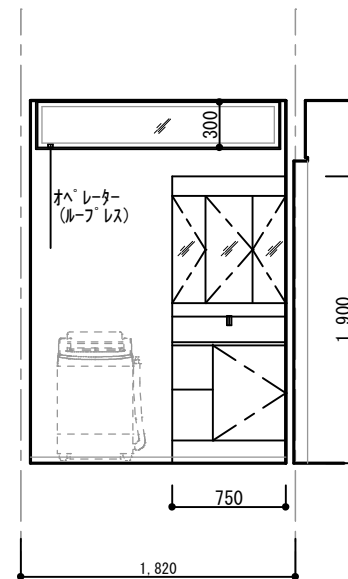


洗面所 北面

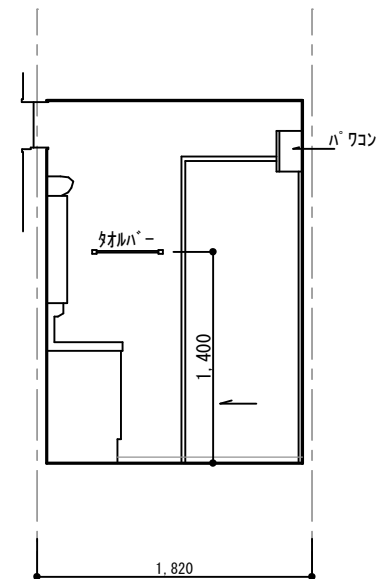


洗面所 東面

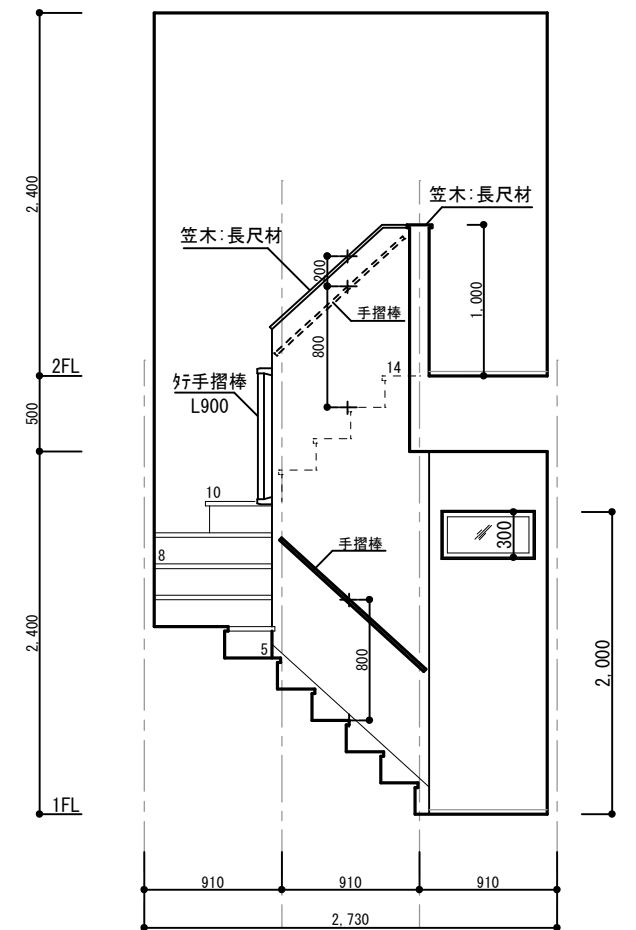


階段 西面

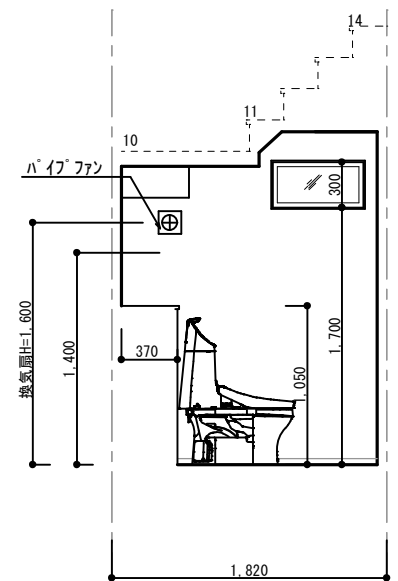


WC② 西面

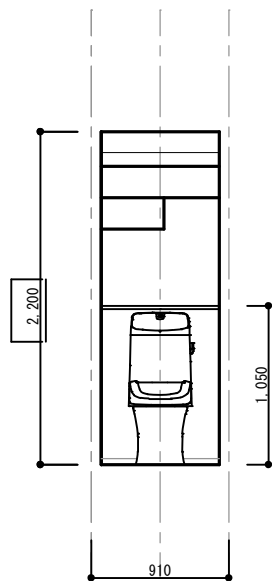


WC① 南面

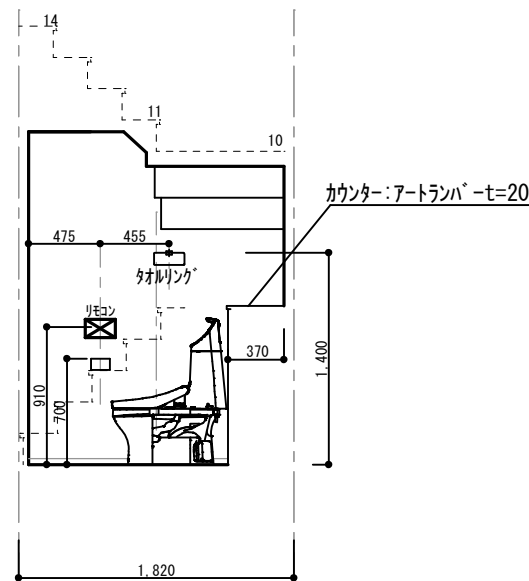

WC② 東面

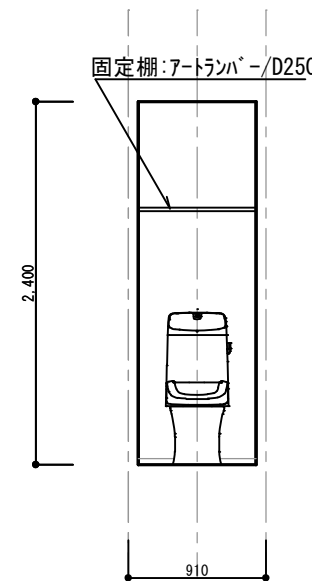


WC② 北面

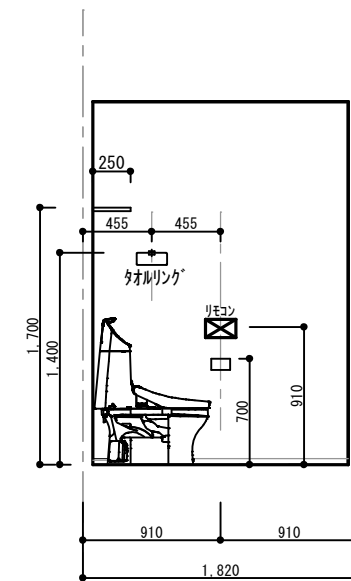


WC② 東面

訂正	浜岡 一級総合設計事務所 一級建築士事務所 静岡県知事登録第 (10)2441 号 一級建築士 大臣登録第 365879 号 西原利晶	LIFEFUND PG HOUSE	株式会社 LIFEFUND InDesign office 一級建築士事務所 事務所登録 (2)第7595号 一級建築士登録 第179770号 鈴木 達男 〒432-8023 静岡県浜松市中央区鴨江3丁目70番23号	年月日 2024.8.10	件名 PG有玉西分譲 新築工事		設計	IC	工事	図番
				縮尺 1/30	図名 展開図		倉田		青島	6-1

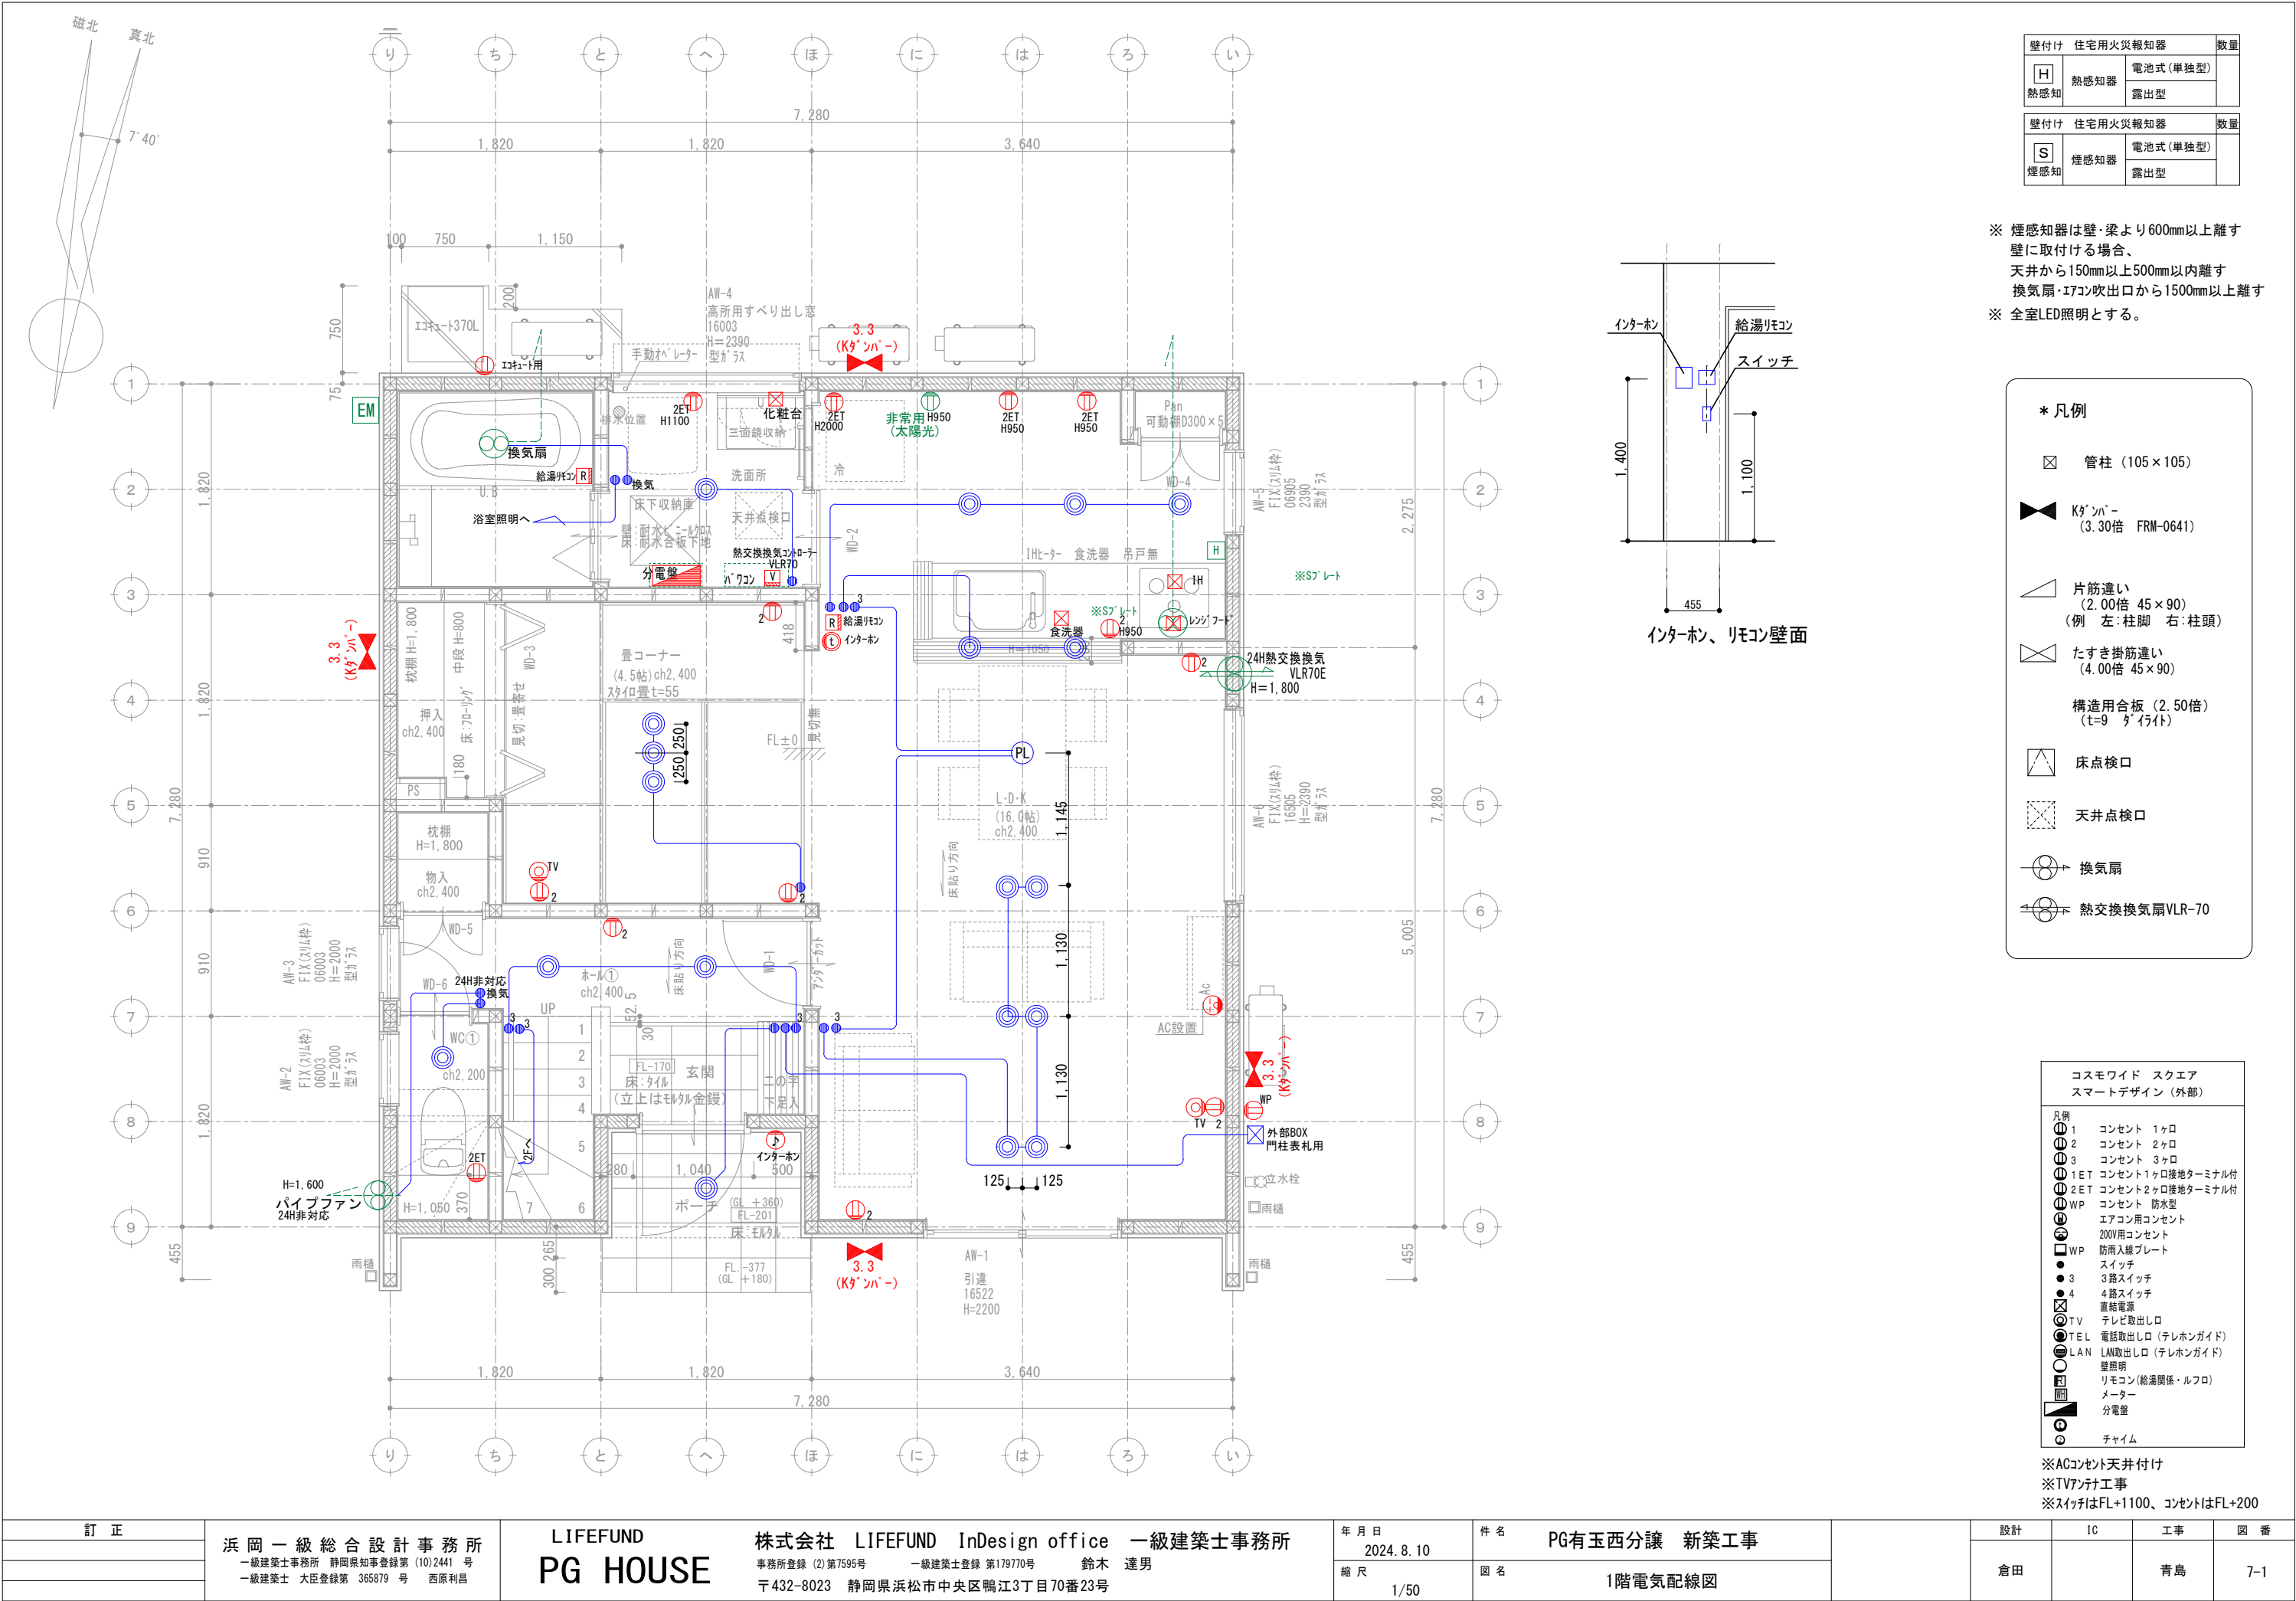

壁付け 住宅用火災報知器			数量
H 熱感知	電池式 (単独型)		
	露出型		
壁付け 住宅用火災報知器			数量
S 煙感知	電池式 (単独型)		
	露出型		


※ 煙感知器は壁・梁より600mm以上離す壁に取付ける場合、天井から150mm以上500mm以内離す換気扇・エアコン吹出口から1500mm以上離す
※ 全室LED照明とする。

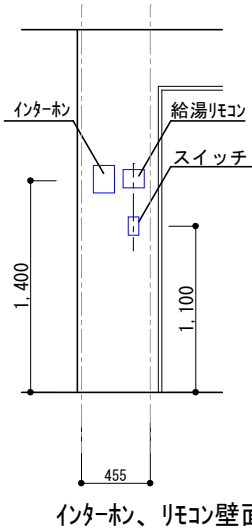


- * 凡例**
- 管柱 (105×105)
 - Kダクト (3.30倍 FRM-0641)
 - 片筋違い (2.00倍 45×90) (例 左:柱脚 右:柱頭)
 - たすき掛筋違い (4.00倍 45×90)
 - 構造用合板 (2.50倍) (t=9 タイライト)
 - 床点検口
 - 天井点検口
 - 換気扇
 - 熱交換換気扇VLR-70


コスモワイド スクエア スマートデザイン (外部)	
凡例	
1	コンセント 1ヶ所
2	コンセント 2ヶ所
3	コンセント 3ヶ所
1ET	コンセント1ヶ所接地ターミナル付
2ET	コンセント2ヶ所接地ターミナル付
WP	コンセント 防水型
Ⓐ	エアコン用コンセント
200V	200V用コンセント
WP	防雨入線プレート
●	スイッチ
●3	3路スイッチ
●4	4路スイッチ
⊗	直結電源
TV	テレビ取出口
TEL	電話取出口 (テレホンガイド)
LAN	LAN取出口 (テレホンガイド)
壁照明	壁照明
リモコン	リモコン (給湯関係・ルフロ)
メーター	メーター
分電盤	分電盤
チャイム	チャイム

※ACコンセント天井付け
※TVアンテナ工事
※スイッチはFL+1100、コンセントはFL+200

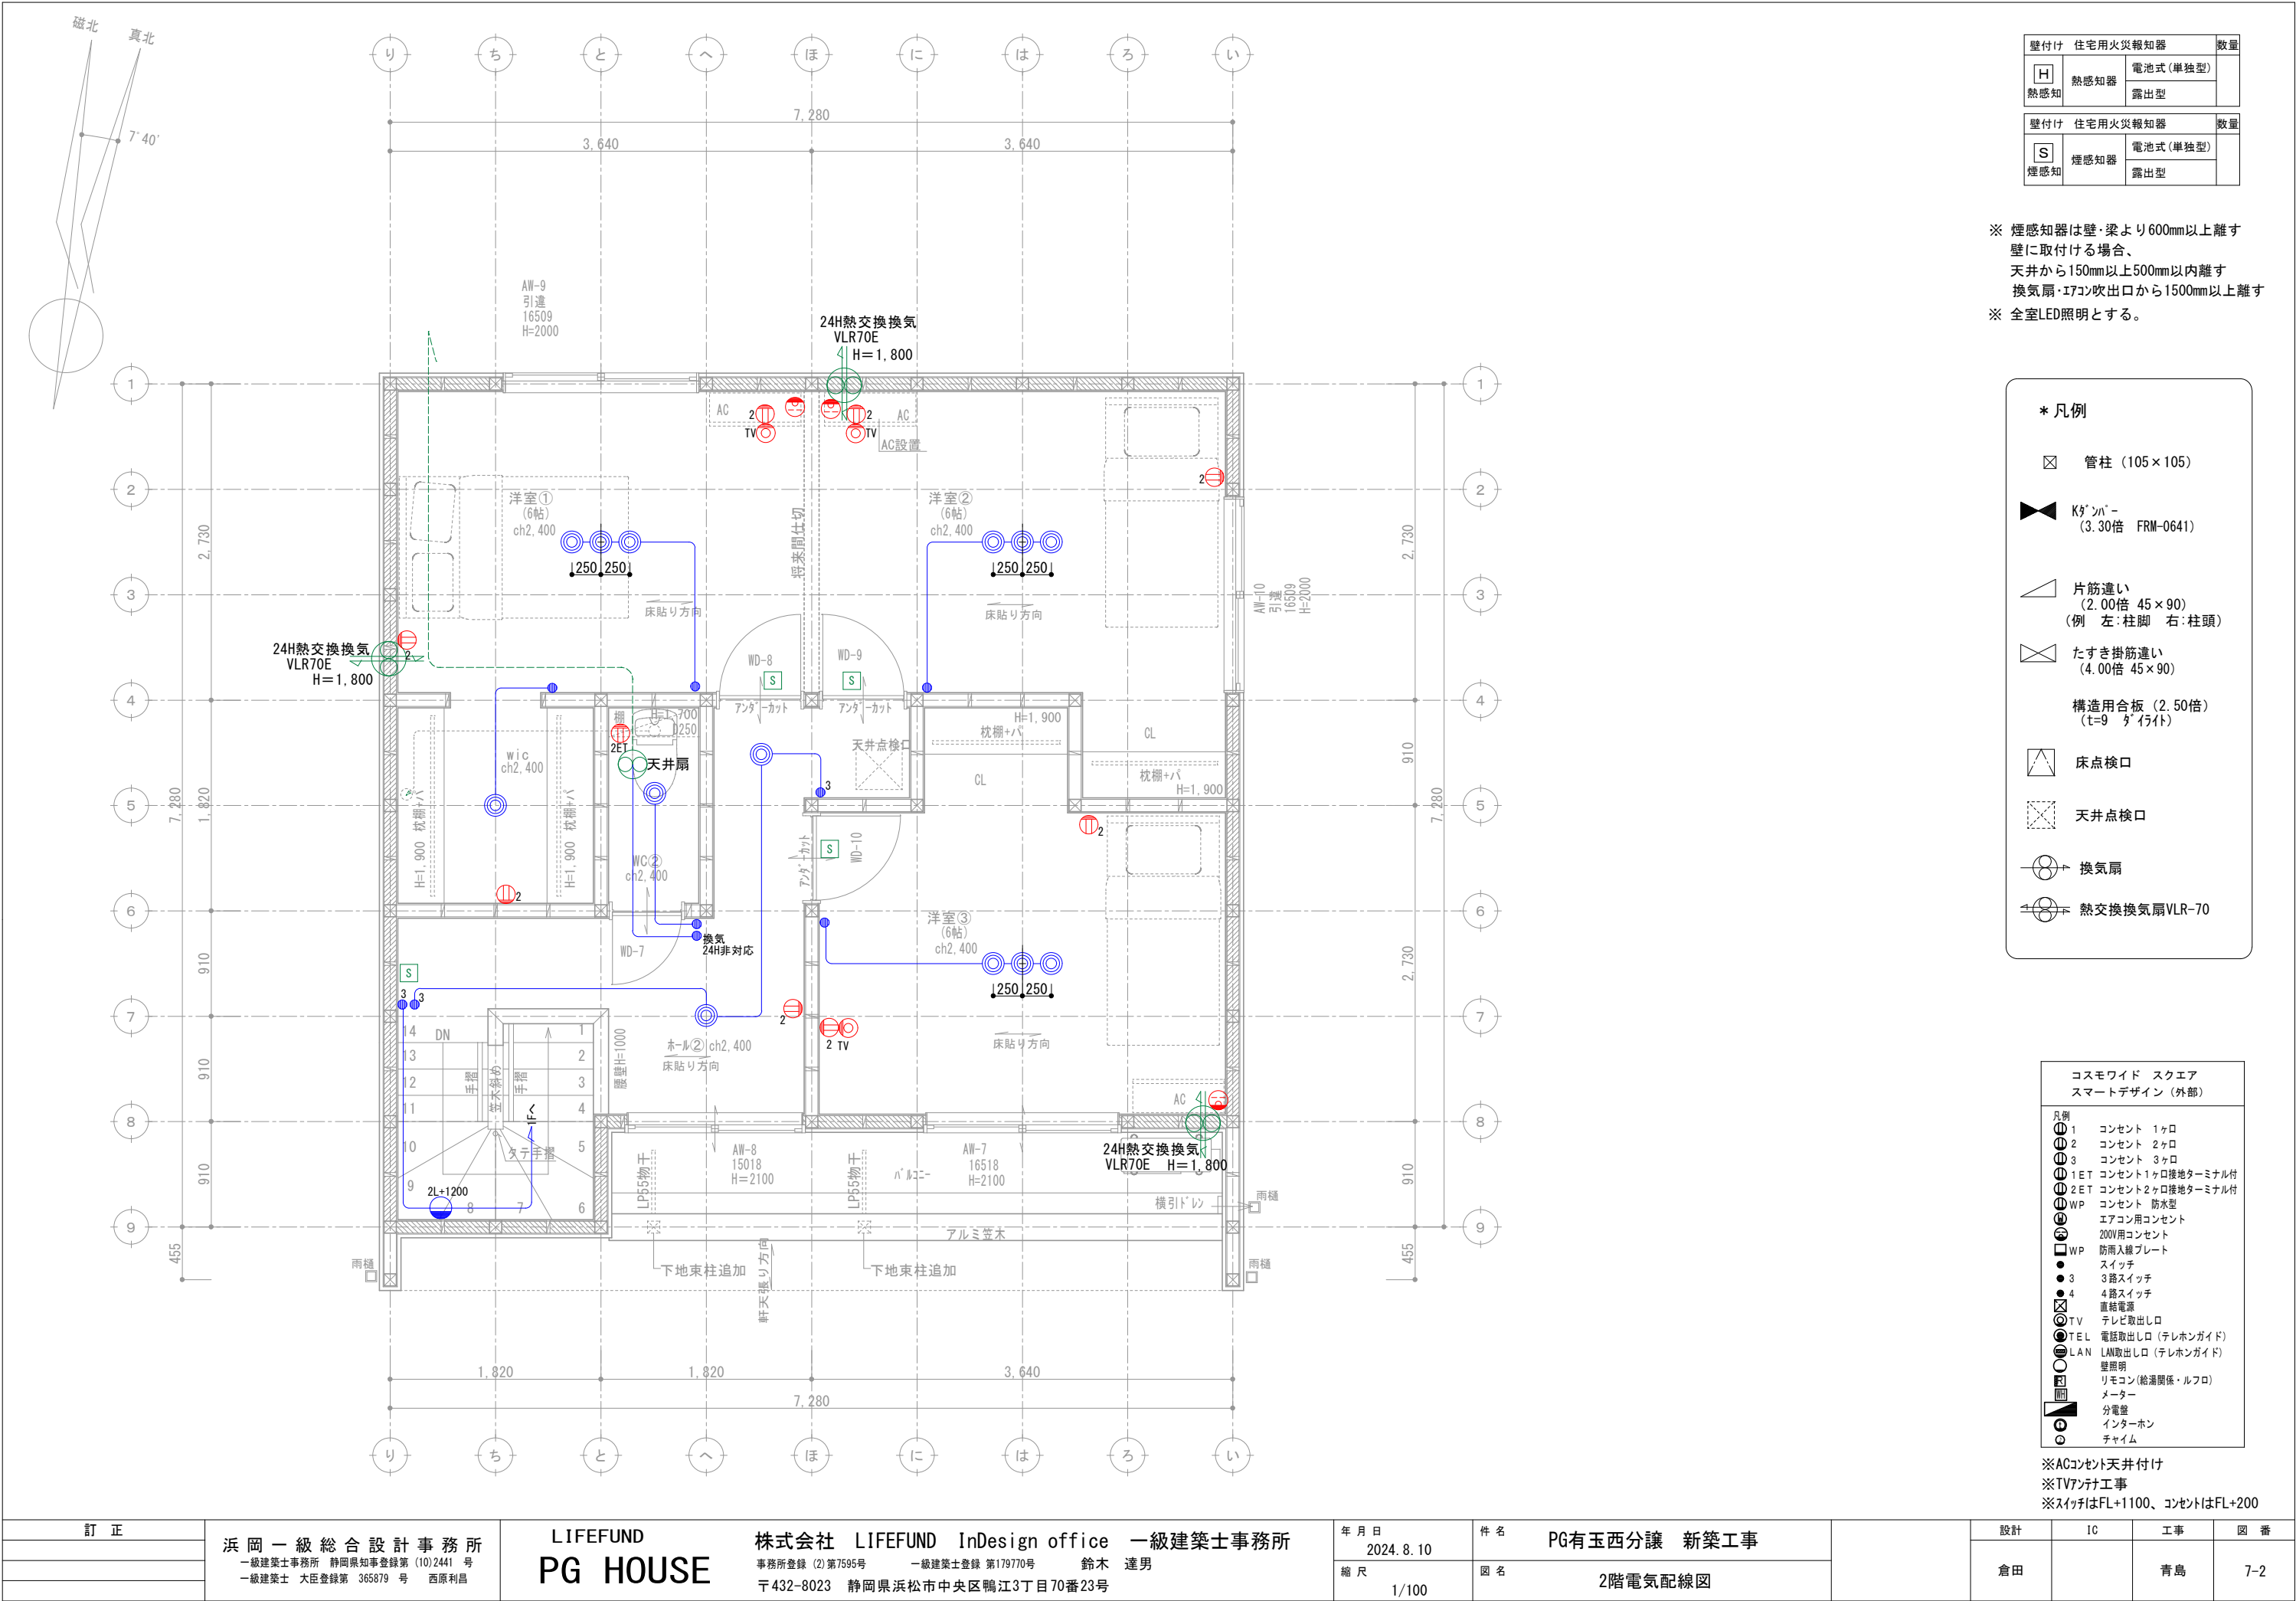

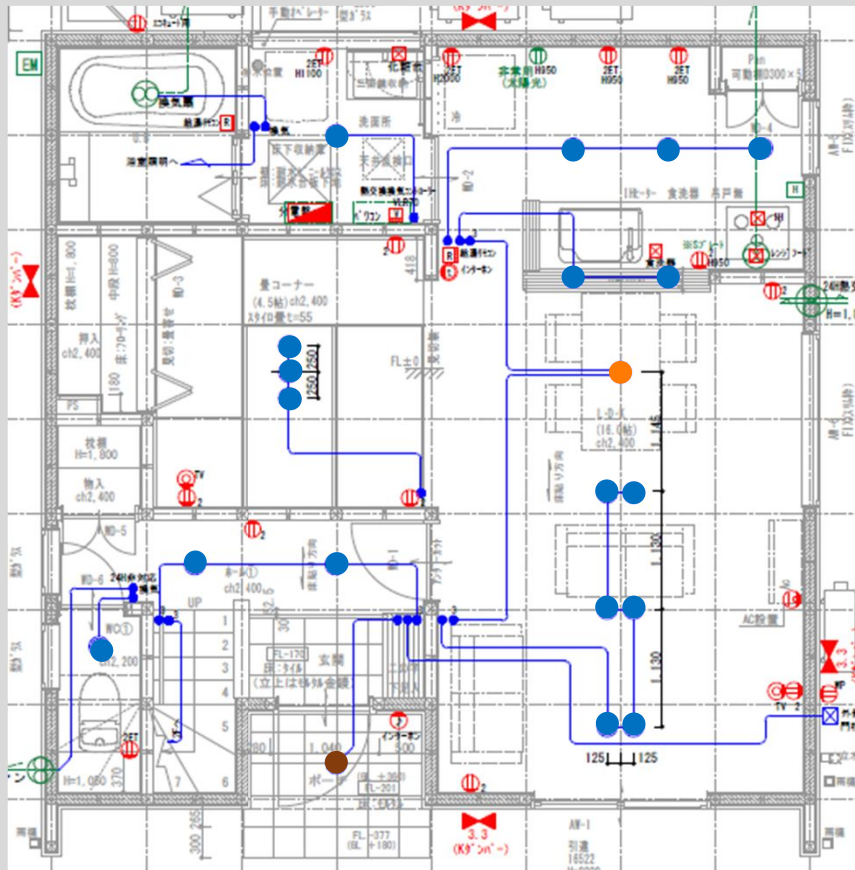


1階

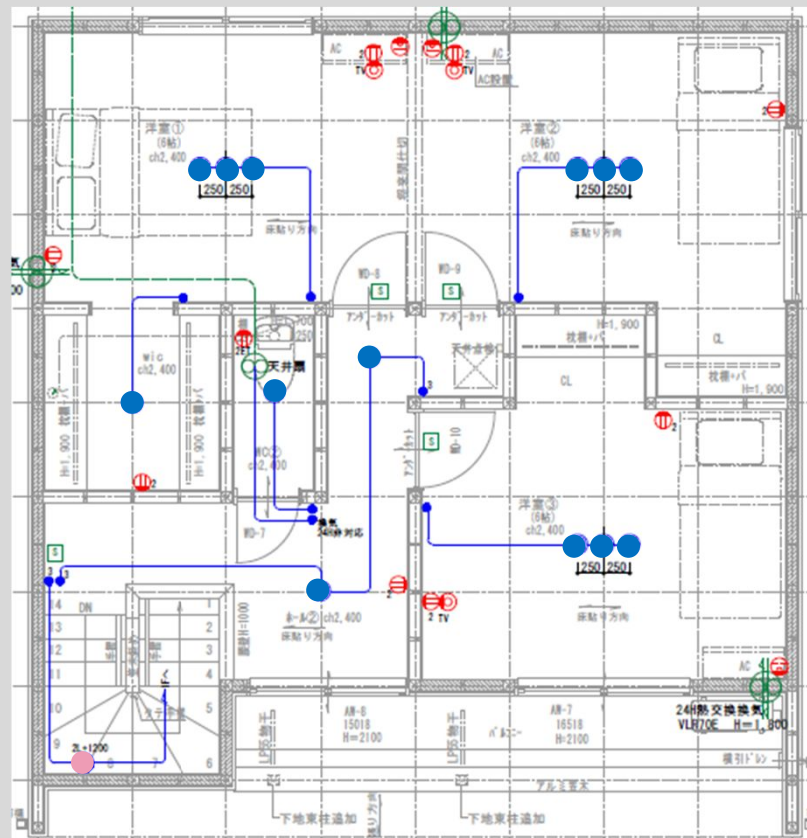

2階

内部：コスモワイド スクエア(Panasonic)

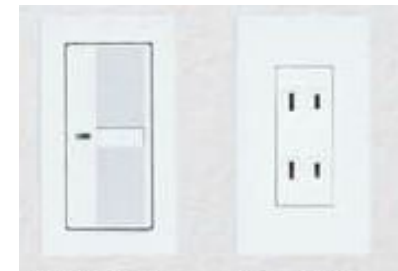

ドアホン：VL-SZ30KL
(Panasonic)



外部：スマートデザインシリーズ (Panasonic)

表情豊かな住まいをつくり出すスマートデザインシリーズ。



ポーチ灯

● × 1

DDL-4496YW



基本照明ダウンライト

● × 31

DDL6102AW



ダイニングペンダント灯

● × 1

DPN41973




階段灯












● × 1

DBK41544Y



2024.8.10

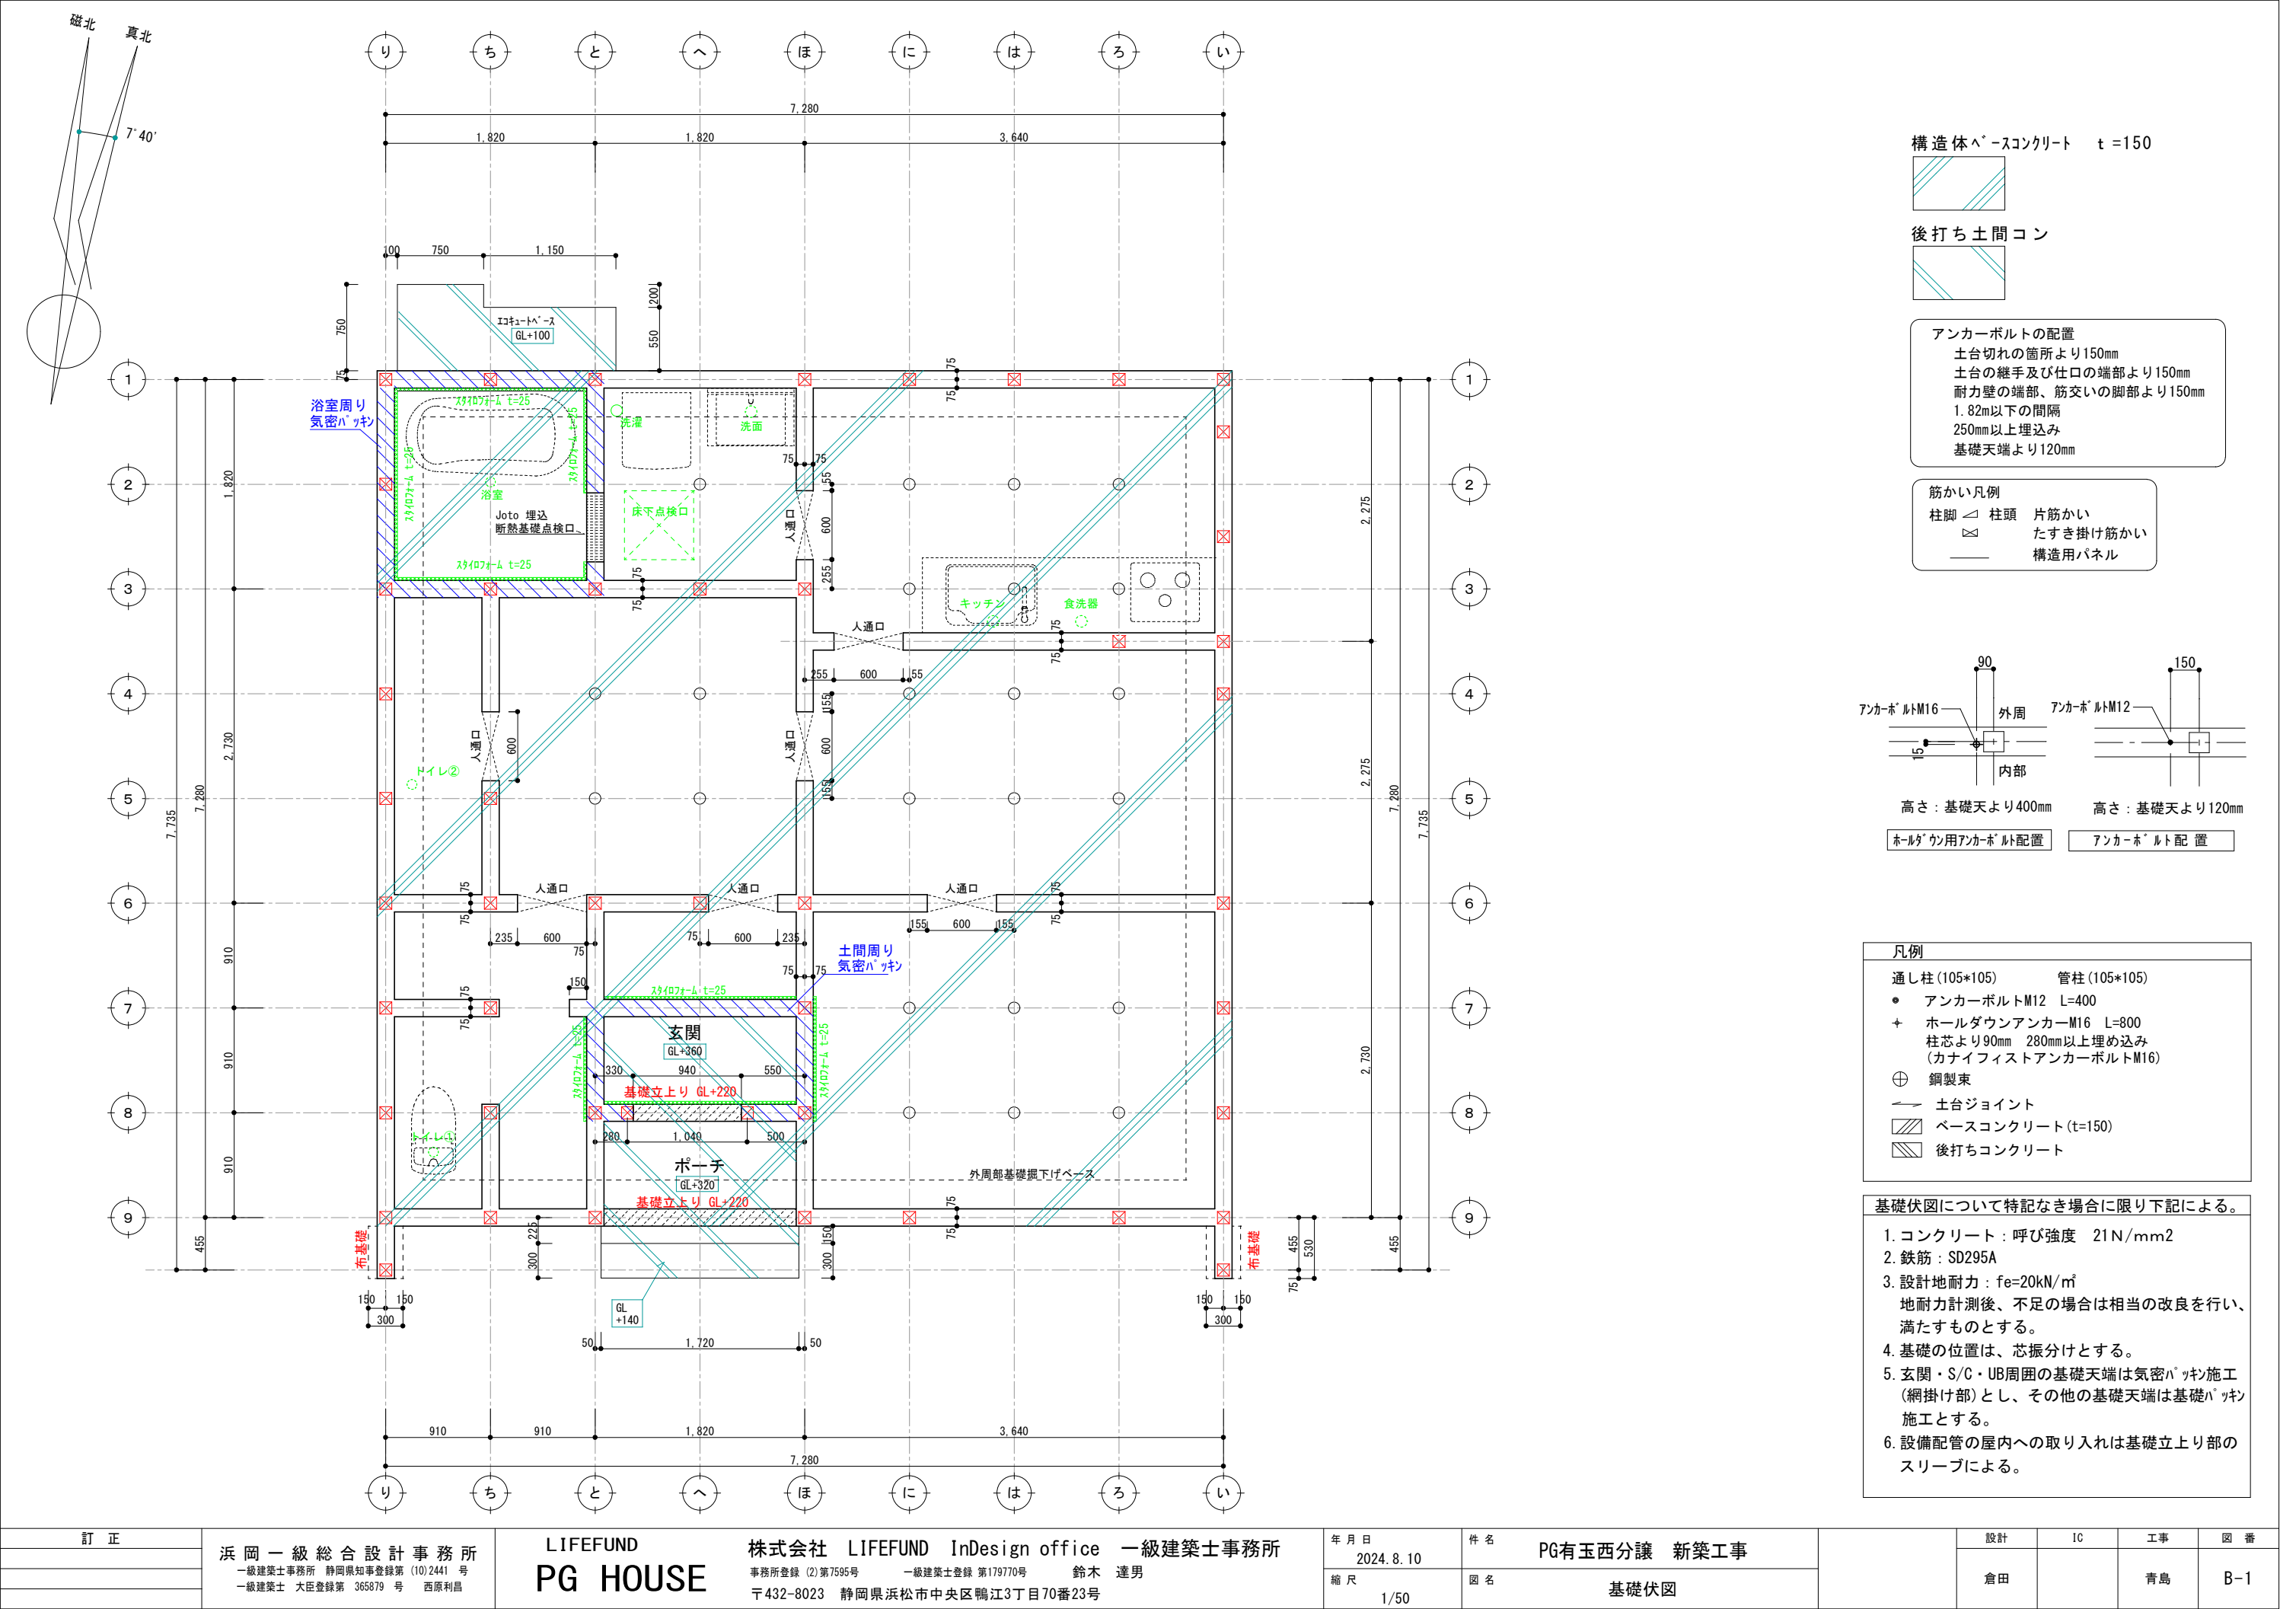

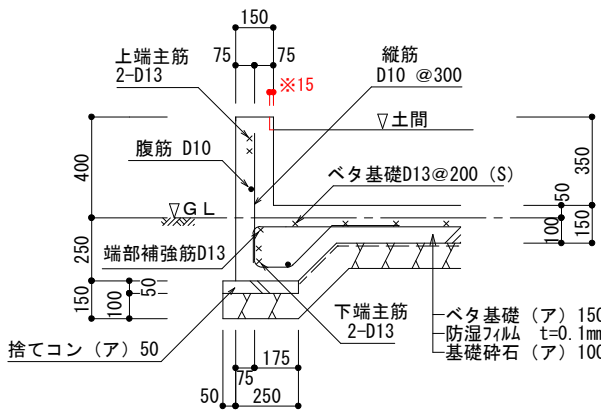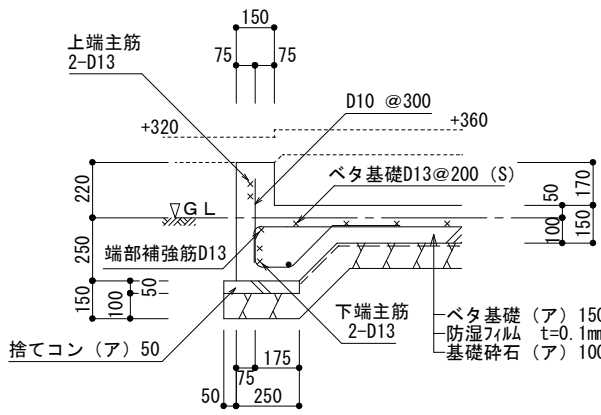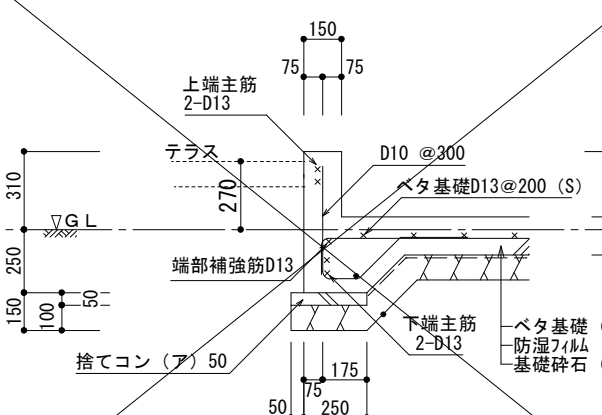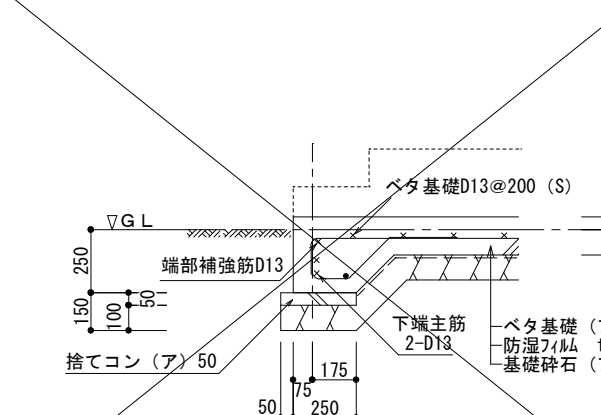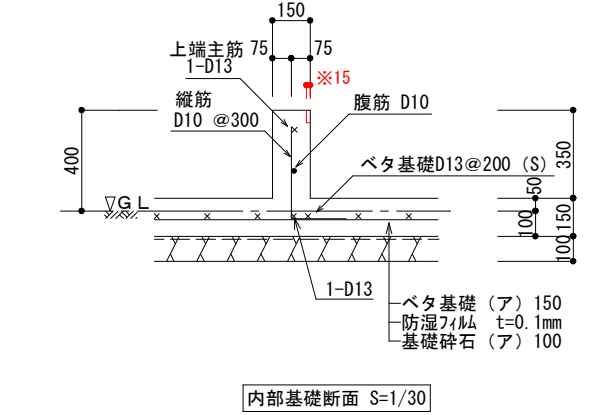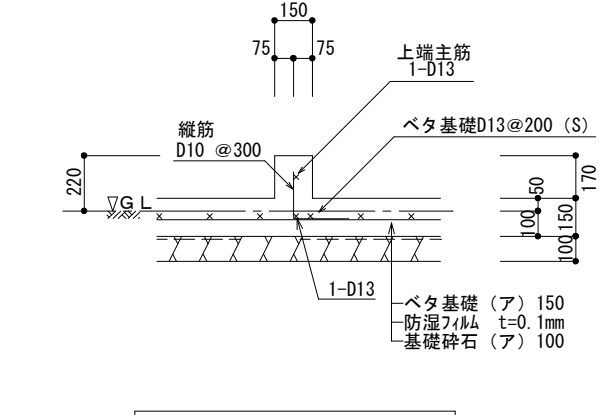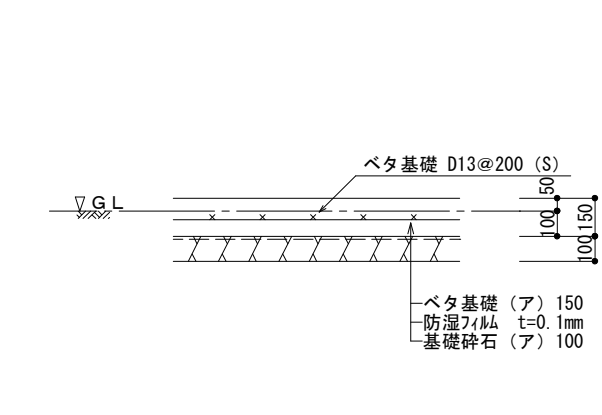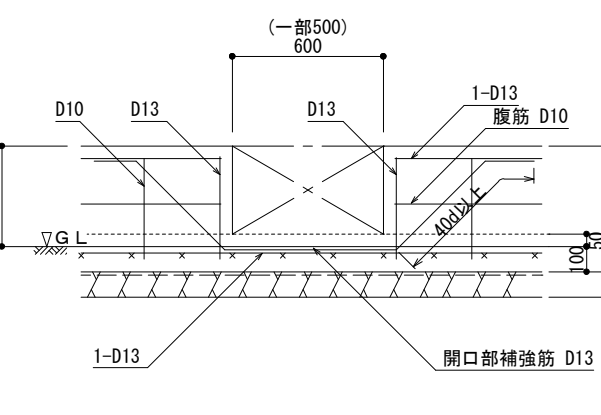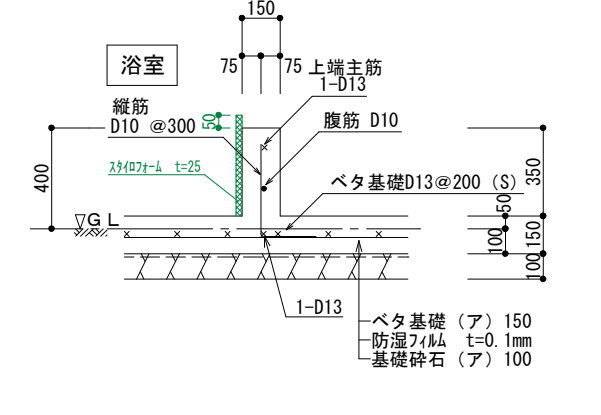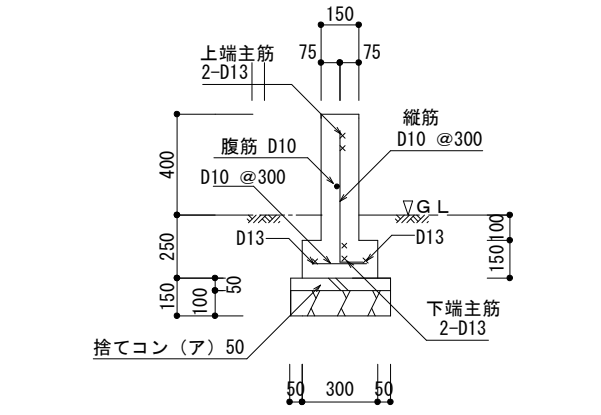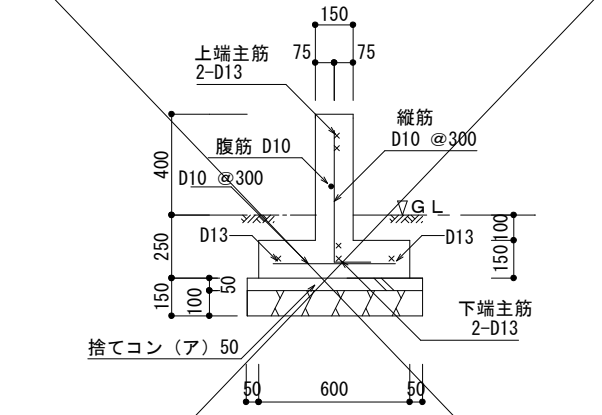 外周基礎断面 S=1/30 ※玄関内土間部分のみ15mm欠き込み	 ポーチ下 外周部基礎断面 S=1/30 倉庫ドア下 外周部基礎断面 S=1/30	 土間納め勝手口ドア下 外周部基礎断面 S=1/30	 立上り無しの基礎断面 S=1/30			
 内部基礎断面 S=1/30 ※玄関内土間部分のみ15mm欠き込み ※注意：基礎伏図に特記のない内部基礎の場合	 ポーチ下 内周部基礎断面 S=1/30 玄関ドア下 内周部基礎断面 S=1/30 玄関内横断基礎断面 S=1/30	 ベタ基礎断面 S=1/30	 人通口補強 S=1/30			
 浴室内部基礎断面 S=1/30 ※注意：基礎伏図に特記のない内部基礎の場合	 布基礎A：袖壁用 基礎断面 S=1/30	 布基礎B：底用独立 基礎断面 S=1/30	基礎の寸法 及び 配筋の検証方法 基礎立上り配筋は、 (財)日本住宅・木材技術 センター発行のスパン表 (増補版)による。 ベタ基礎スラブ配筋は、 まもりすまい保険設計施工 基準同解説のベタ基礎配筋表 による。具体的な寸法・配 筋は基礎詳細図参照。 鉄筋断面表記 ●・・・D10を示す。 ×・・・D13を示す。 ※使用しない断面は×を記入。			
訂正	浜岡一級総合設計事務所 一級建築士事務所 静岡県知事登録第(10)2441号 一級建築士 大臣登録第365879号 西原利昌	LIFEFUND PG HOUSE	株式会社LIFEFUND InDesign office 一級建築士事務所 事務所登録 (2)第7595号 一級建築士登録 第179770号 鈴木 達男 〒432-8023 静岡県浜松市中央区鴨江3丁目70番23号	年月日 2024.8.10 縮尺 1/30	件名 PG有玉西分譲 新築工事 図名 基礎断面リスト	設計 倉田 I C 工務 青島 図番 B-2