

敷地調査報告書

調査日：令和6年 6月29日

(物件名) PG有玉西モデルハウス 様邸新築工事

(建築地) 浜松市中央区有玉西町字北平2135番34

株式会社 LIFE FUND


規制項目		規制内容	
都市計画		内（市街化調整区域）	用途地域 指定なし
防火指定		無し（22条、23条指定地域）	
建ぺい率		60%	容積率 200%
道路斜線		1.5A	北側斜線 無し
高さ制限		10m	高度地区 無し
日影規制		最高の高さ10m超えると有	
壁面後退		無し	
道路		市道：有玉西32号線	
事前申請	都計法	第60条適合証明申請	
	計画道路	無し	
	埋蔵文化	無し	
	農地法等	無し	
	建築協定	無し	
	建築基準	無し	
その他		宅地造成工事規制区域内 航空法制限表面区域内	
設備		水道本管50φ、下水本管200φ、都市ガス本管50φ	

〒422-8057 静岡県静岡市駿河区見瀬239-1


報国エンジニアリング株式会社静岡支店

TEL 054-292-5488

FAX 054-292-5490

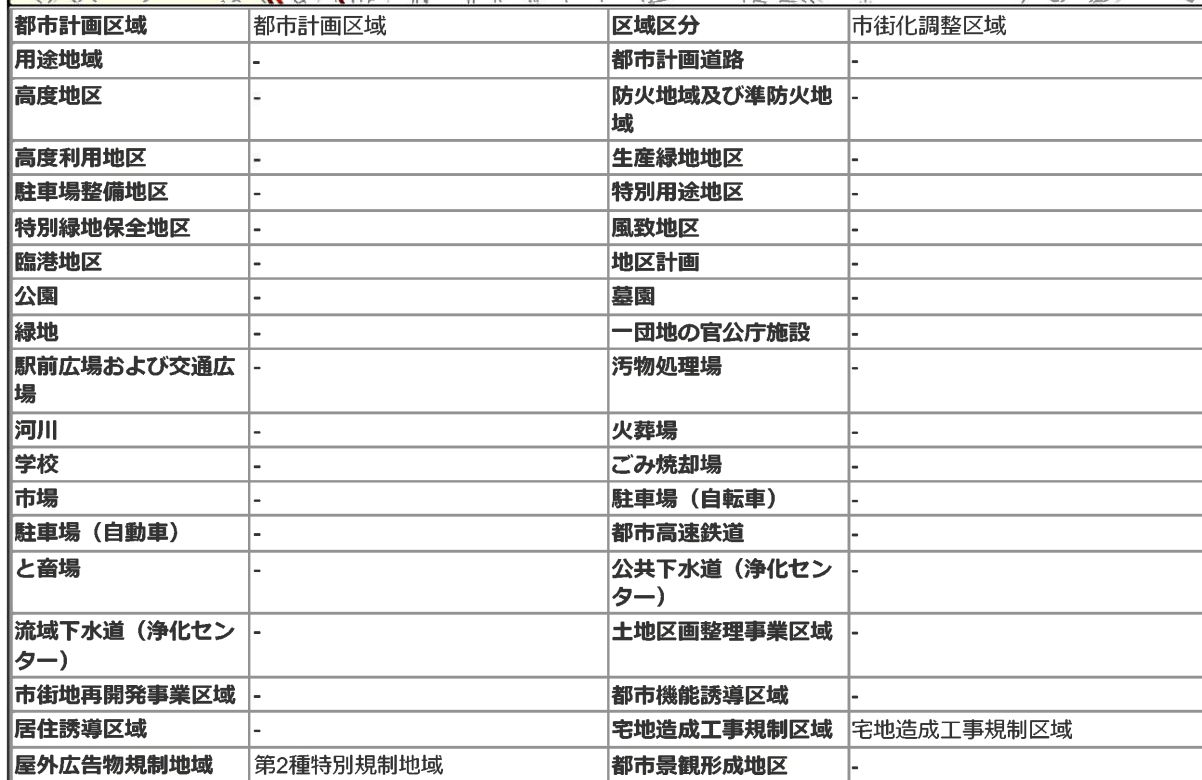

この図画は、都市計画などの内容を証明するものではありません。概略位置を表示した参考図としてご利用ください。
境界線付近では操作上の誤差により隣接区域の情報を表示する場合があります。
浜松市は、本サイトの利用によって発生する直接又は間接の損失、損害及び障害等について一切責任を負いません。権利義務等が発生するおそれのある重要な事項等への使用については、必ず所管課へご相談ください。
浜松市都市計画マップに関する問合せ先は都市計画課（中央区元城町103-2 Tel:053-457-2371・Fax:050-3737-6815）です。
このシステムで表示している都市計画のうち、お調べの地点（旗の根元）に関係するものは上記のとおりです。

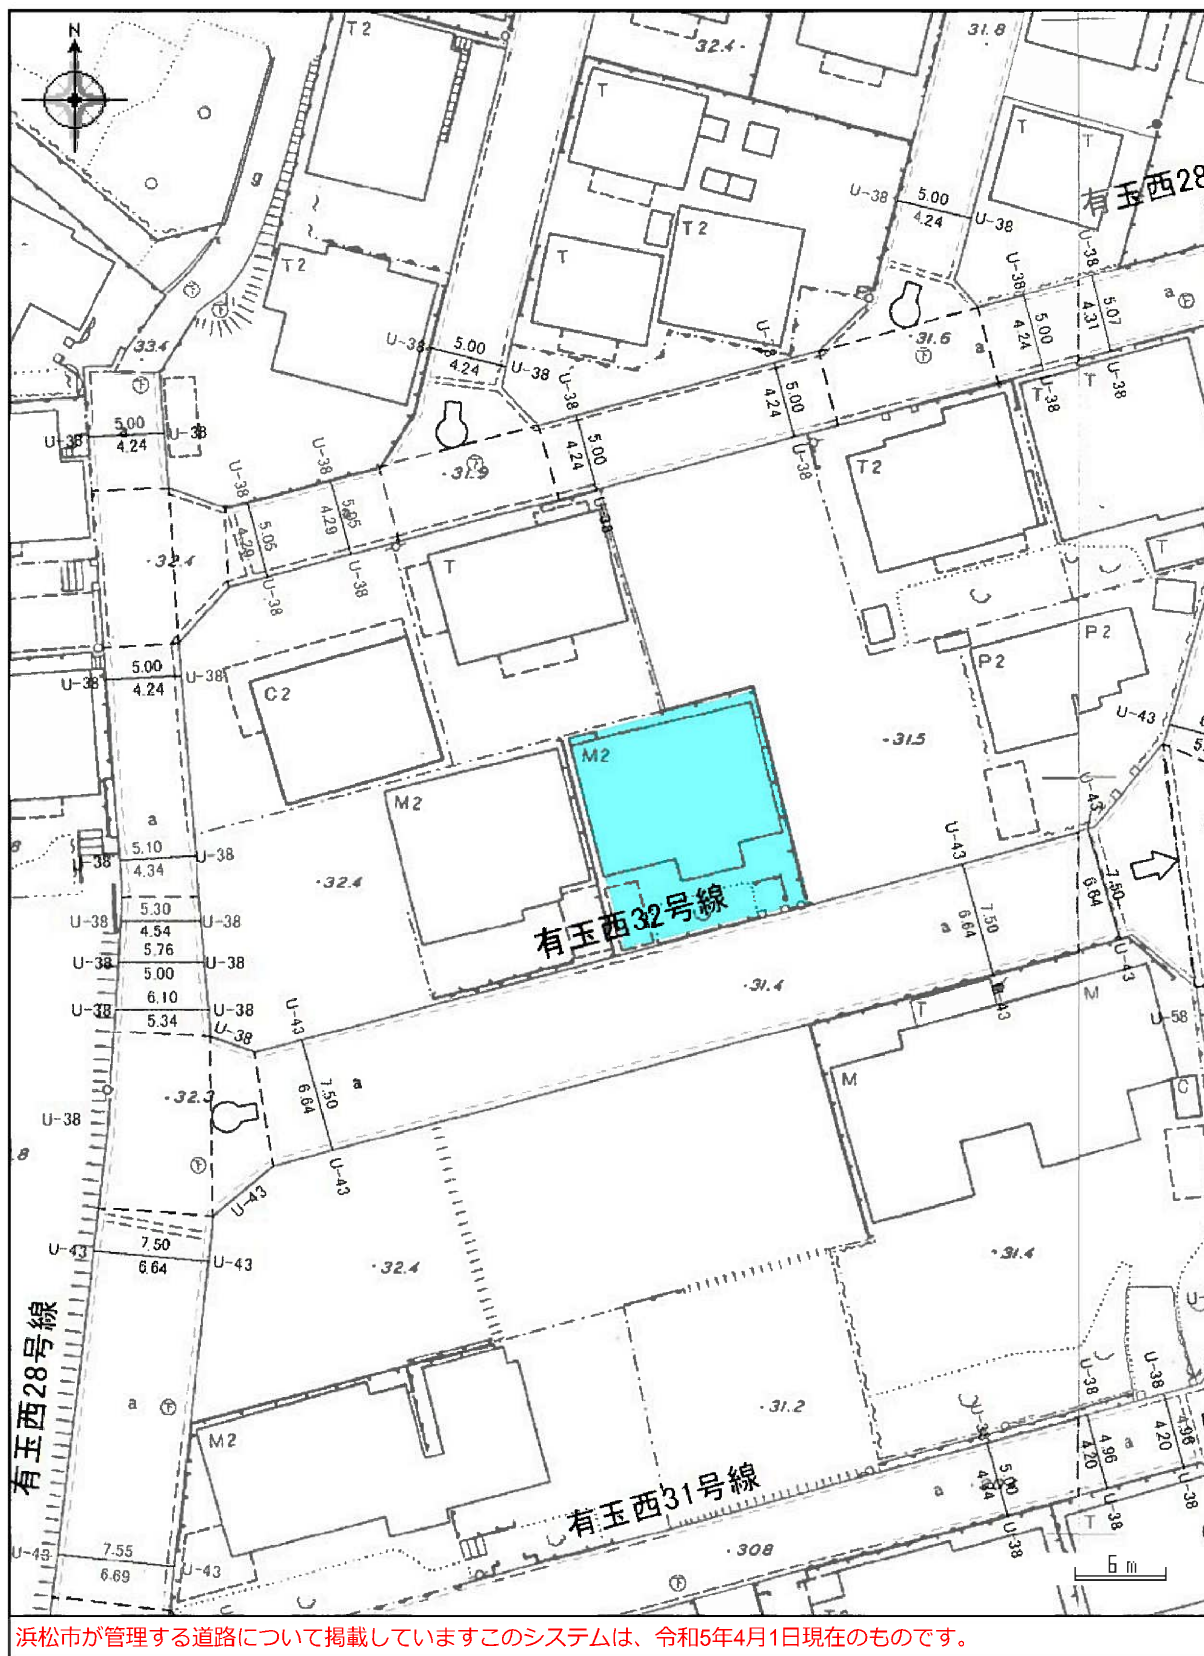

浜松市が管理する道路について掲載していますこのシステムは、令和5年4月1日現在のものです。





2024/06/19 08:33 現在の情報です。

表 題 部 (土地の表示)		調製	平成19年1月15日	不動産番号	0804005287182
地図番号	余 白	筆界特定	余 白		
所 在	浜松市有玉西町字北平			余 白	
	浜松市東区有玉西町字北平			平成19年4月1日変更 平成19年8月21日登記	
	浜松市中央区有玉西町字北平			令和6年1月1日変更 令和6年3月12日登記	
① 地 番	②地 目	③ 地 積	㎡	原因及びその日付〔登記の日付〕	
2135番34	宅地	191:39		2135番2から分筆 〔昭和43年11月26日〕	
余 白	余 白	余 白	:	平成17年法務省令第18号附則第3条第2項 の規定により移記 平成19年1月15日	

権 利 部 (甲 区) (所有権に関する事項)			
順位番号	登 記 の 目 的	受付年月日・受付番号	権 利 者 そ の 他 の 事 項
1	所有権移転	昭和44年5月21日 第5517号	原因 昭和44年5月19日売買 所有者 掛川市葛川1068番地の4 中 西 和 男 順位2番の登記を移記
	余 白	余 白	平成17年法務省令第18号附則第3条第2項 の規定により移記 平成19年1月15日
2	所有権移転	令和4年7月19日 第31241号	原因 令和4年5月27日相続 所有者 浜松市東区有玉西町2135番地の3 4 中 西 政 子

- * 「登記の目的」欄に「相続人申告」と記載されている登記は、所有権の登記名義人（所有者）の相続人からの申出に基づき、登記官が職権で、申出があった相続人の住所・氏名等を付記したものであり、権利関係を公示するものではない。
- * 下線のあるものは抹消事項であることを示す。

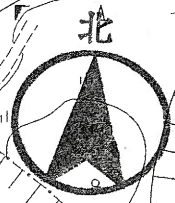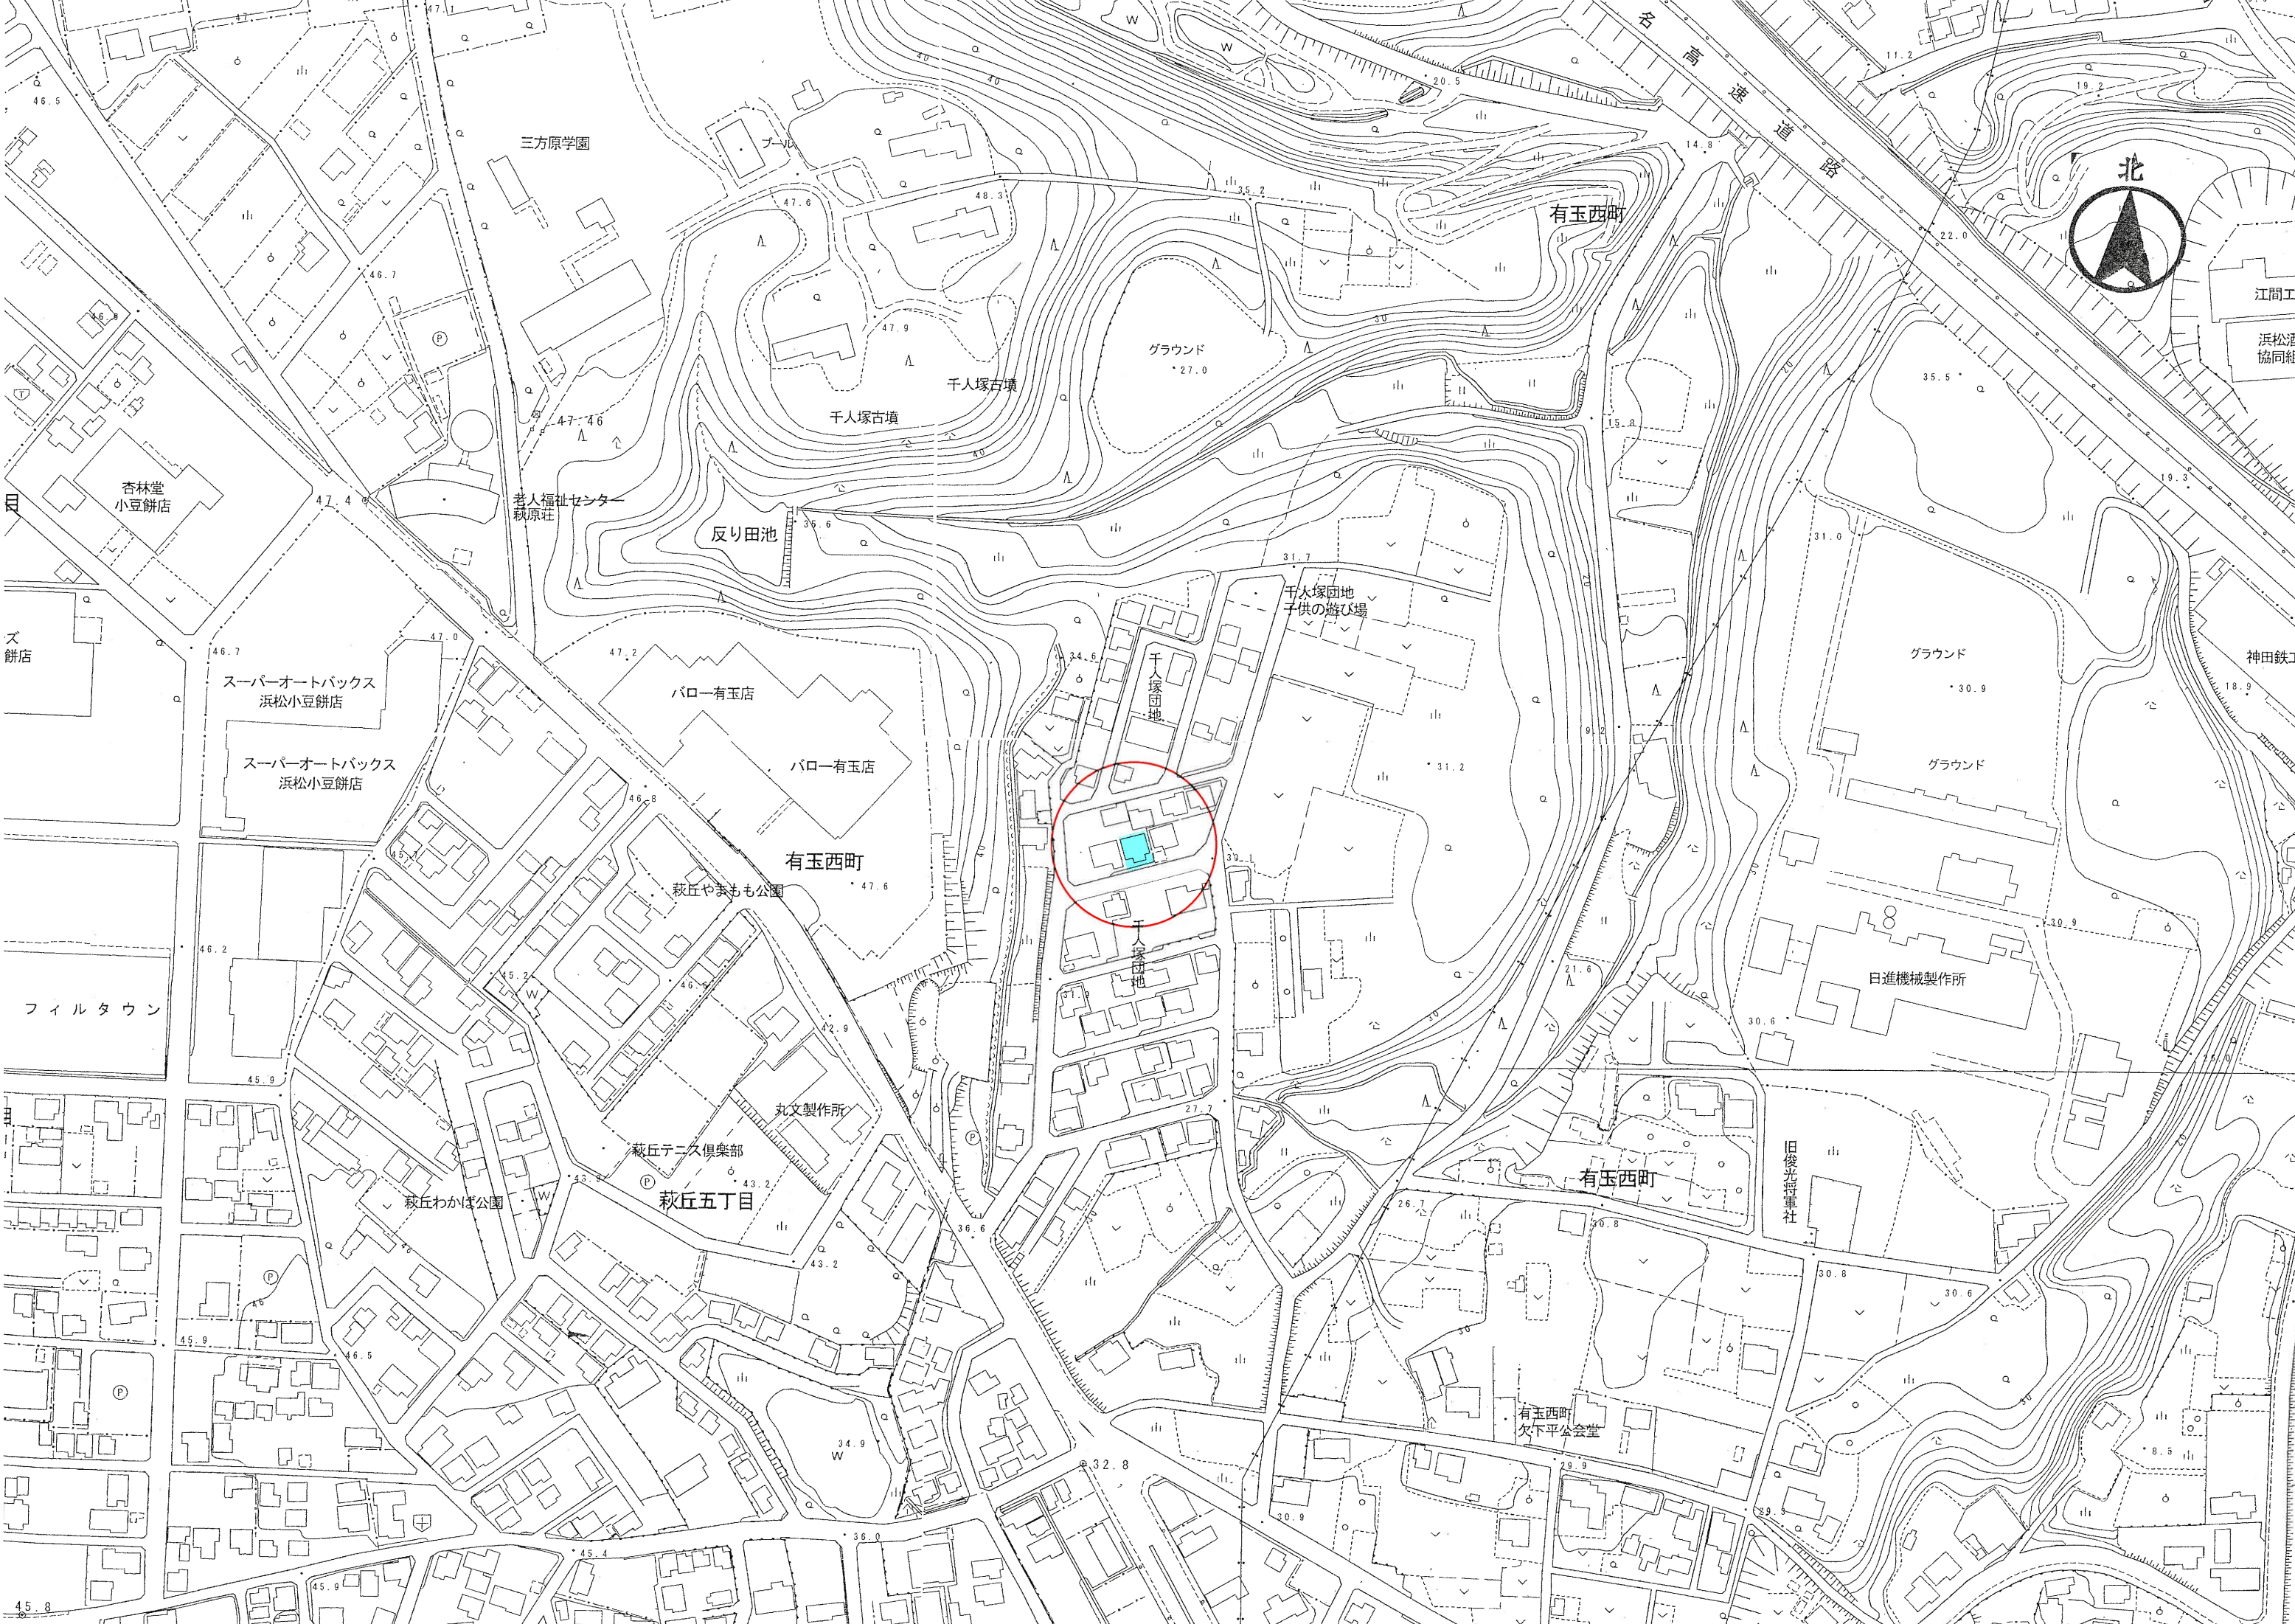

江間工業
浜松酒則
協同組合

神田鉄工

日進機械製作所

旧俊光将軍社

有玉西町
欠下平公会堂

有玉西町

有玉西町

千人塚古墳

千人塚古墳

千人塚団地
子供の遊び場

グラウンド
・27.0

グラウンド
・30.9

グラウンド

反り田池

パロー有玉店

パロー有玉店

有玉西町

萩丘やまも公園

丸文製作所

萩丘テニス倶楽部

萩丘五丁目

萩丘わかば公園

スーパーオートバックス
浜松小豆餅店

スーパーオートバックス
浜松小豆餅店

杏林堂
小豆餅店

フィルタウン

ズ餅店

三方原学園

プール

老人福祉センター
萩原荘

千人塚団地

32.8

34.9

43.2

43.2

46.8

47.2

47.0

47.4

46.7

46.7

47.1

45.8

45.9

45.4

36.0

32.8

30.9

30.8

30.8

30.6

30.6

30.6

31.2

31.2

31.7

31.7


31.7

31.7

31.7

31.7


31.7

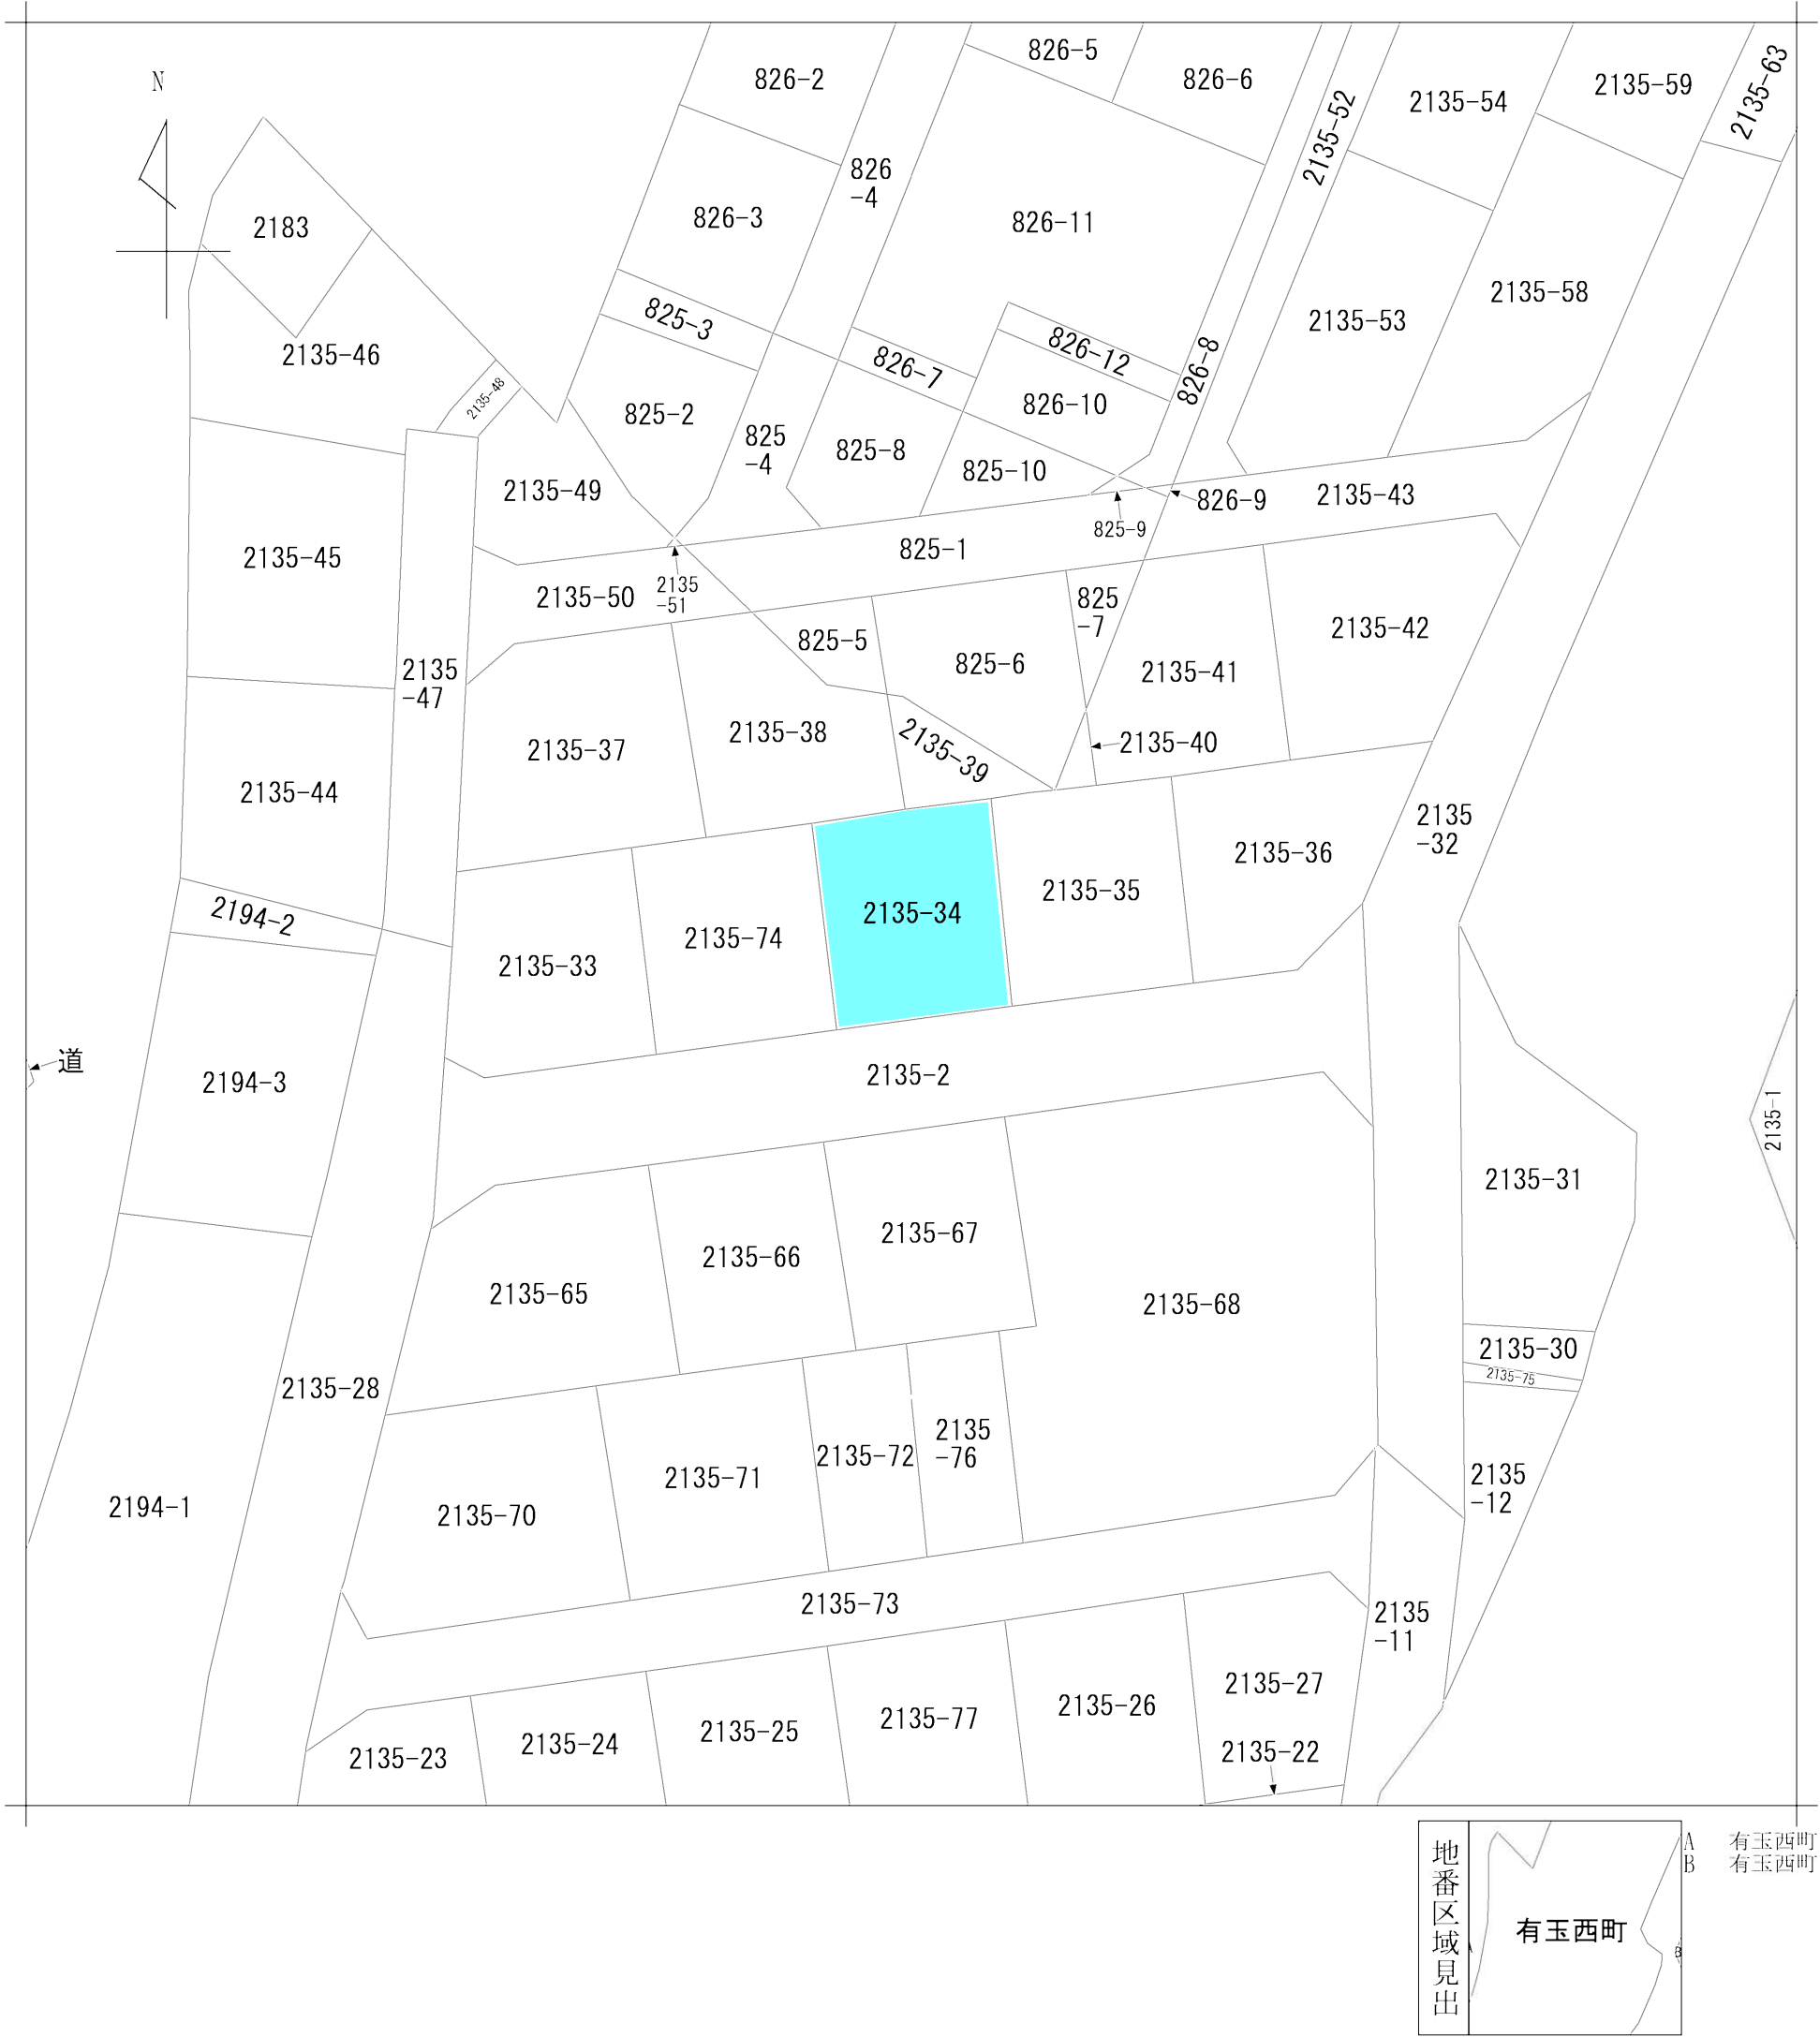

請 求 部 分	所 在	浜松市中央区有玉西町字北平					地 番	2135番34		
出 力 縮 尺	1/500	精 度 区 分		座 標 系 番 号 又 は 記 号		分 類	地図に準ずる図面		種 類	旧土地台帳附属地図
作 成 年 月 日					備 付 年 月 日 (原図)			補 記 事 項		

水道管網図


中心地 | 浜松市中央区有玉西町 付近

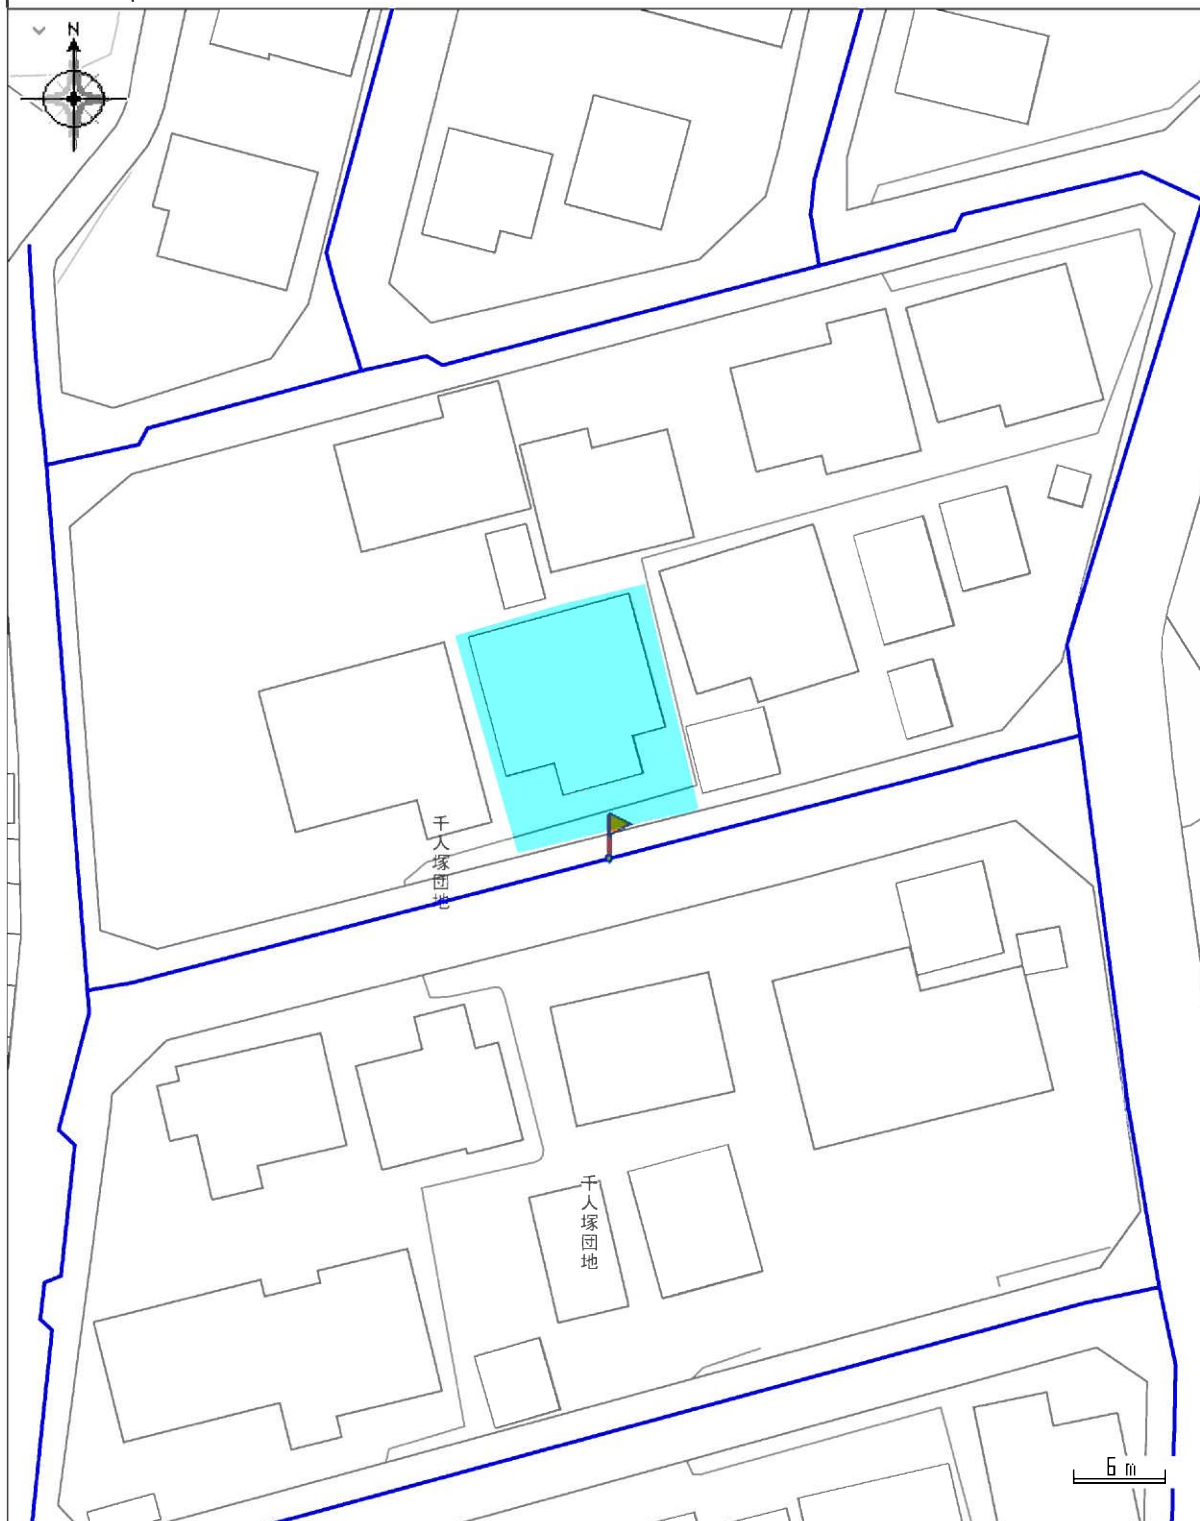

凡例	属性	
— 口径350mm以下	管種	HPE
	口径	50
	布設年度	2007


下水道管網図

中心地 | 浜松市中央区有玉西町 付近

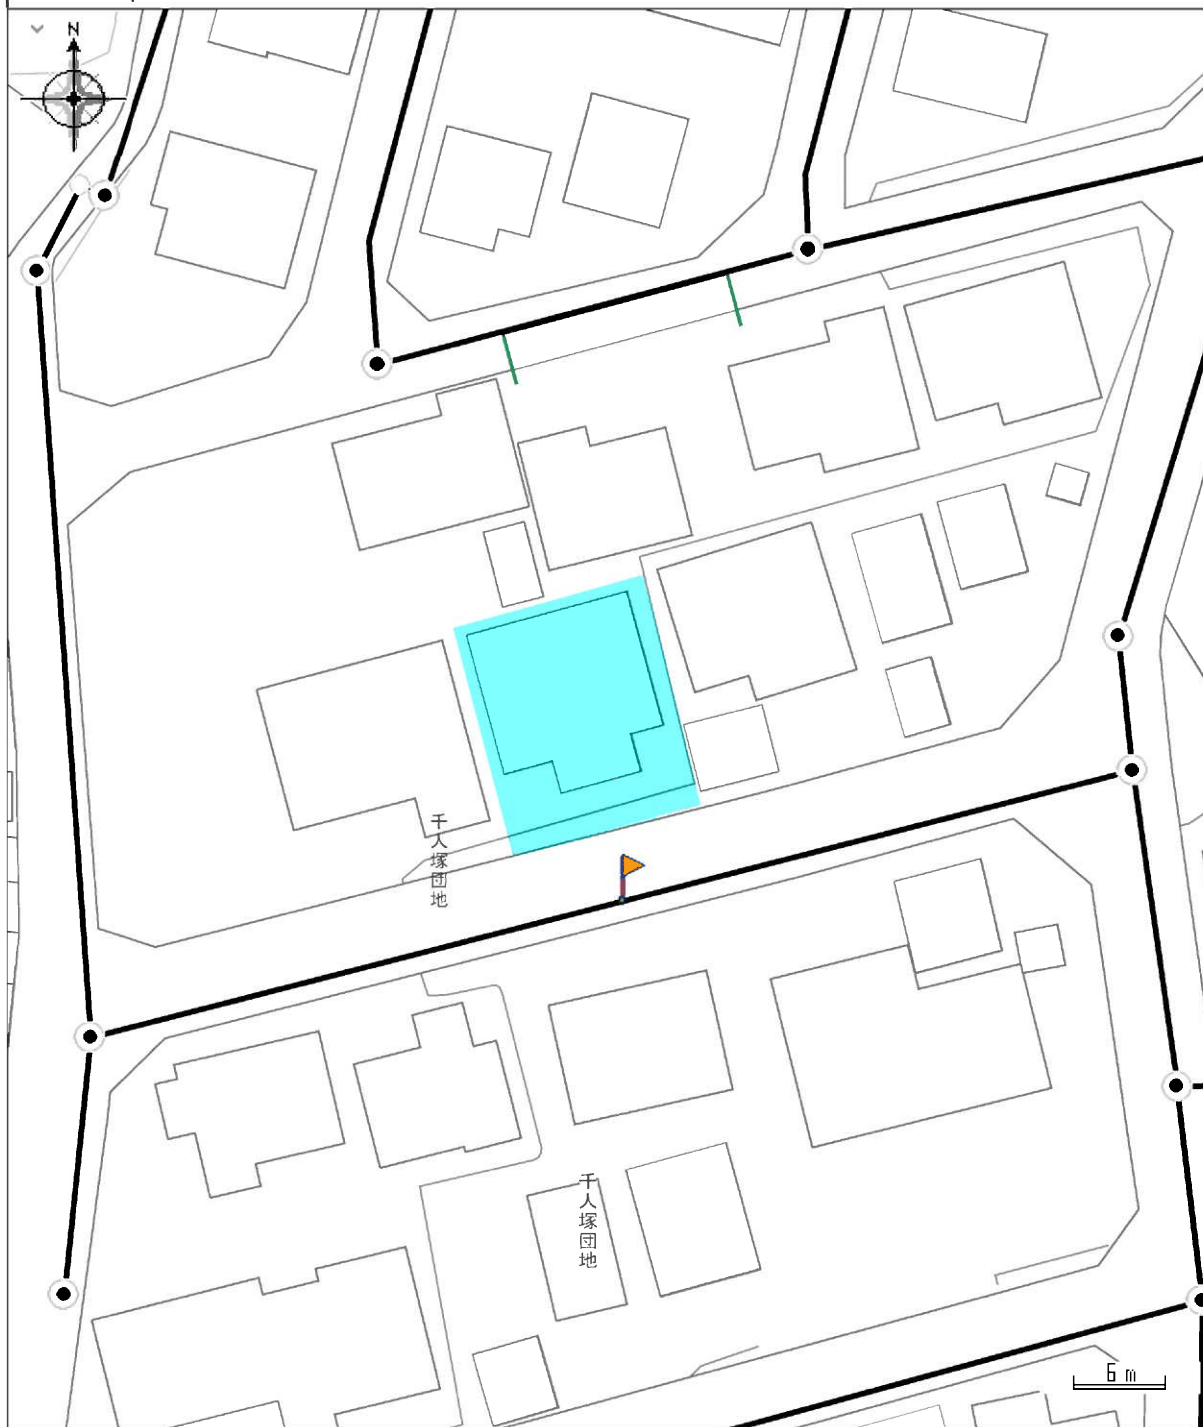

凡例		属性	
— 枝線	— 取付管	管区分	枝線
● 1号マンホール (内径90cm円形)		管種	硬質ポリ塩化ビニル管
○ Y号マンホール		口径	200
		分合流区域	分流
		処理区	西遠

サーラエナジー株式会社 都市ガス本管確認サービス 回答図

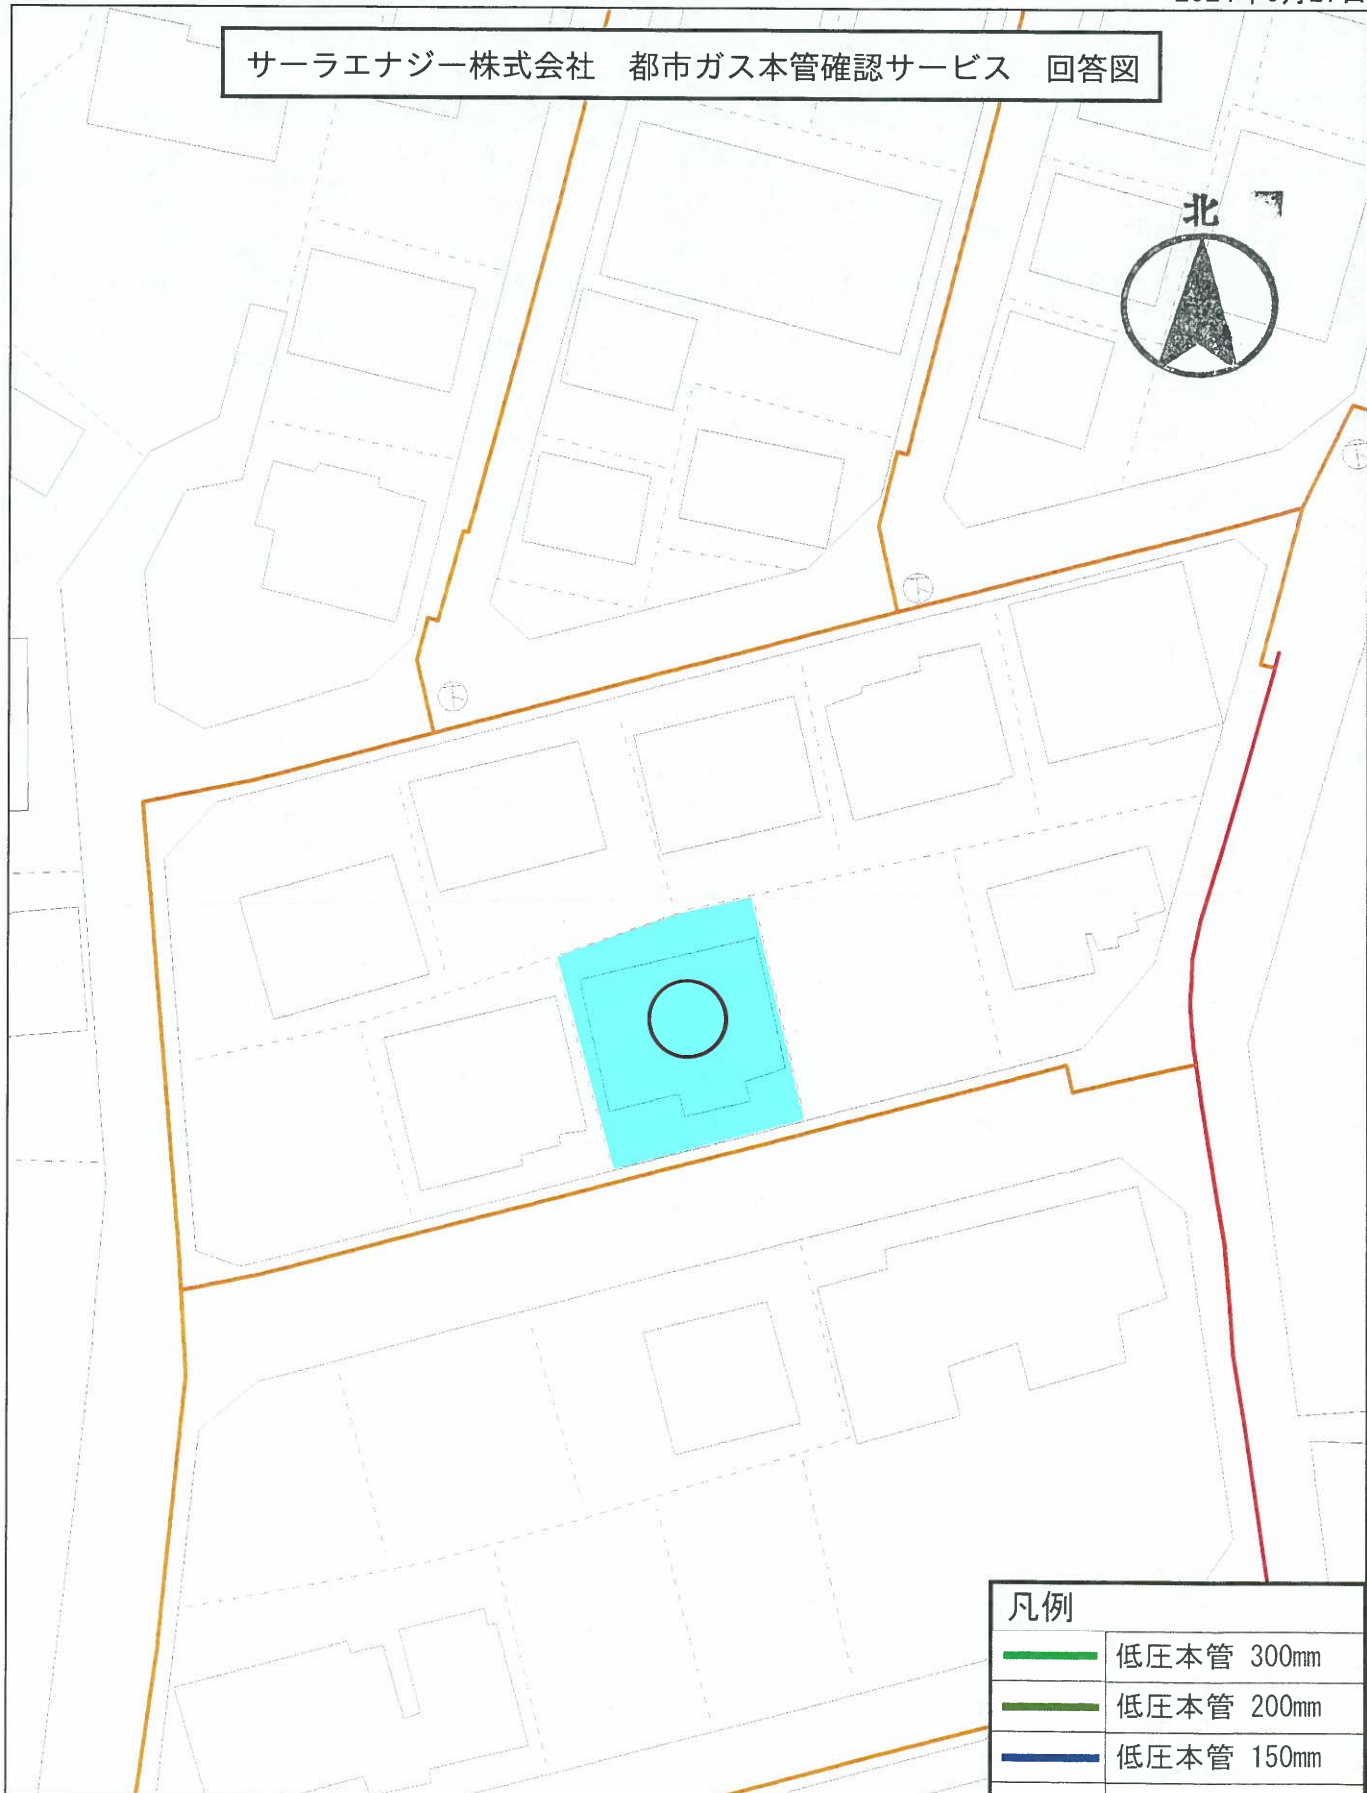

【注意事項】

- ・表示される情報は、低圧本管の有無と口径です。（工事予定ルートは点線で表示します。）
- ・引込管・中圧本管・高圧本管・LPGガス管は表示していません。
- ・低圧本管および道路・建物等の形状は、実際と異なることがあります。
- ・本サービスにより損害が生じた際も、一切責任を負いかねますのでご了承ください。
- ・本図面を掘削工事の資料として利用することは、固く禁止します。

凡例

	低圧本管 300mm
	低圧本管 200mm
	低圧本管 150mm
	低圧本管 100mm
	低圧本管 75mm
	低圧本管 50mm
	工事予定ルート
	調査依頼箇所

現況写真



① 敷地全景（南西）



② 敷地全景（南東）



③ 東側方向



④ 西側方向



⑤ 南側方向



⑥ 北側方向



⑦ 東側境界




⑧ 東側境界



⑨ 西側境界



⑩ 西側境界

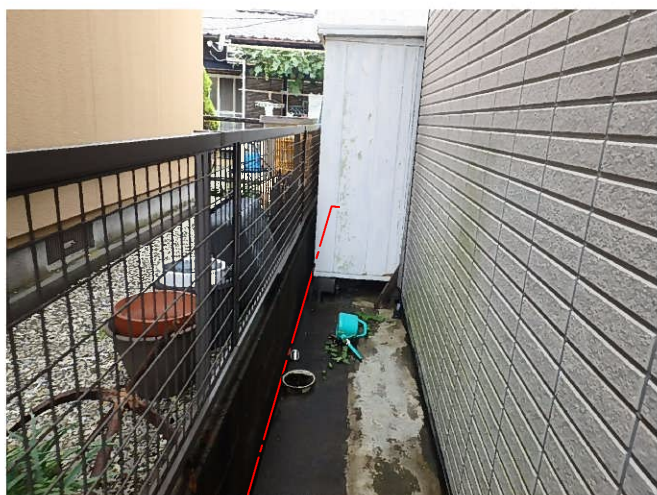

⑪ 西側境界




⑫ 南側道路境界



⑬ 南側道路境界



⑭ 北側境界

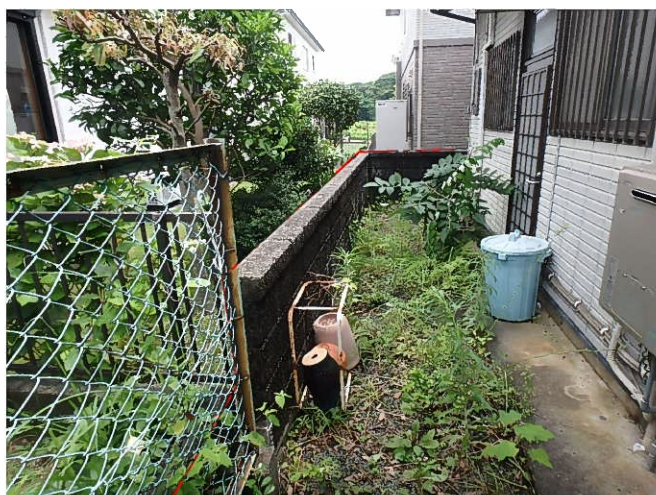

⑮ 北側境界



⑯ 北側境界



⑰ 境界点①



⑱ 境界点②、側溝天端 (BM±0)



⑲ 境界点③



⑳ 境界点④付近



②① 境界点⑤付近



②② 水道メーター13φ



②③ 下水最終枳



②④ ガス引込シール




②⑤ 電柱




②⑥ 上部電線

NTT：千人塚支9/左2
中電：07ア292

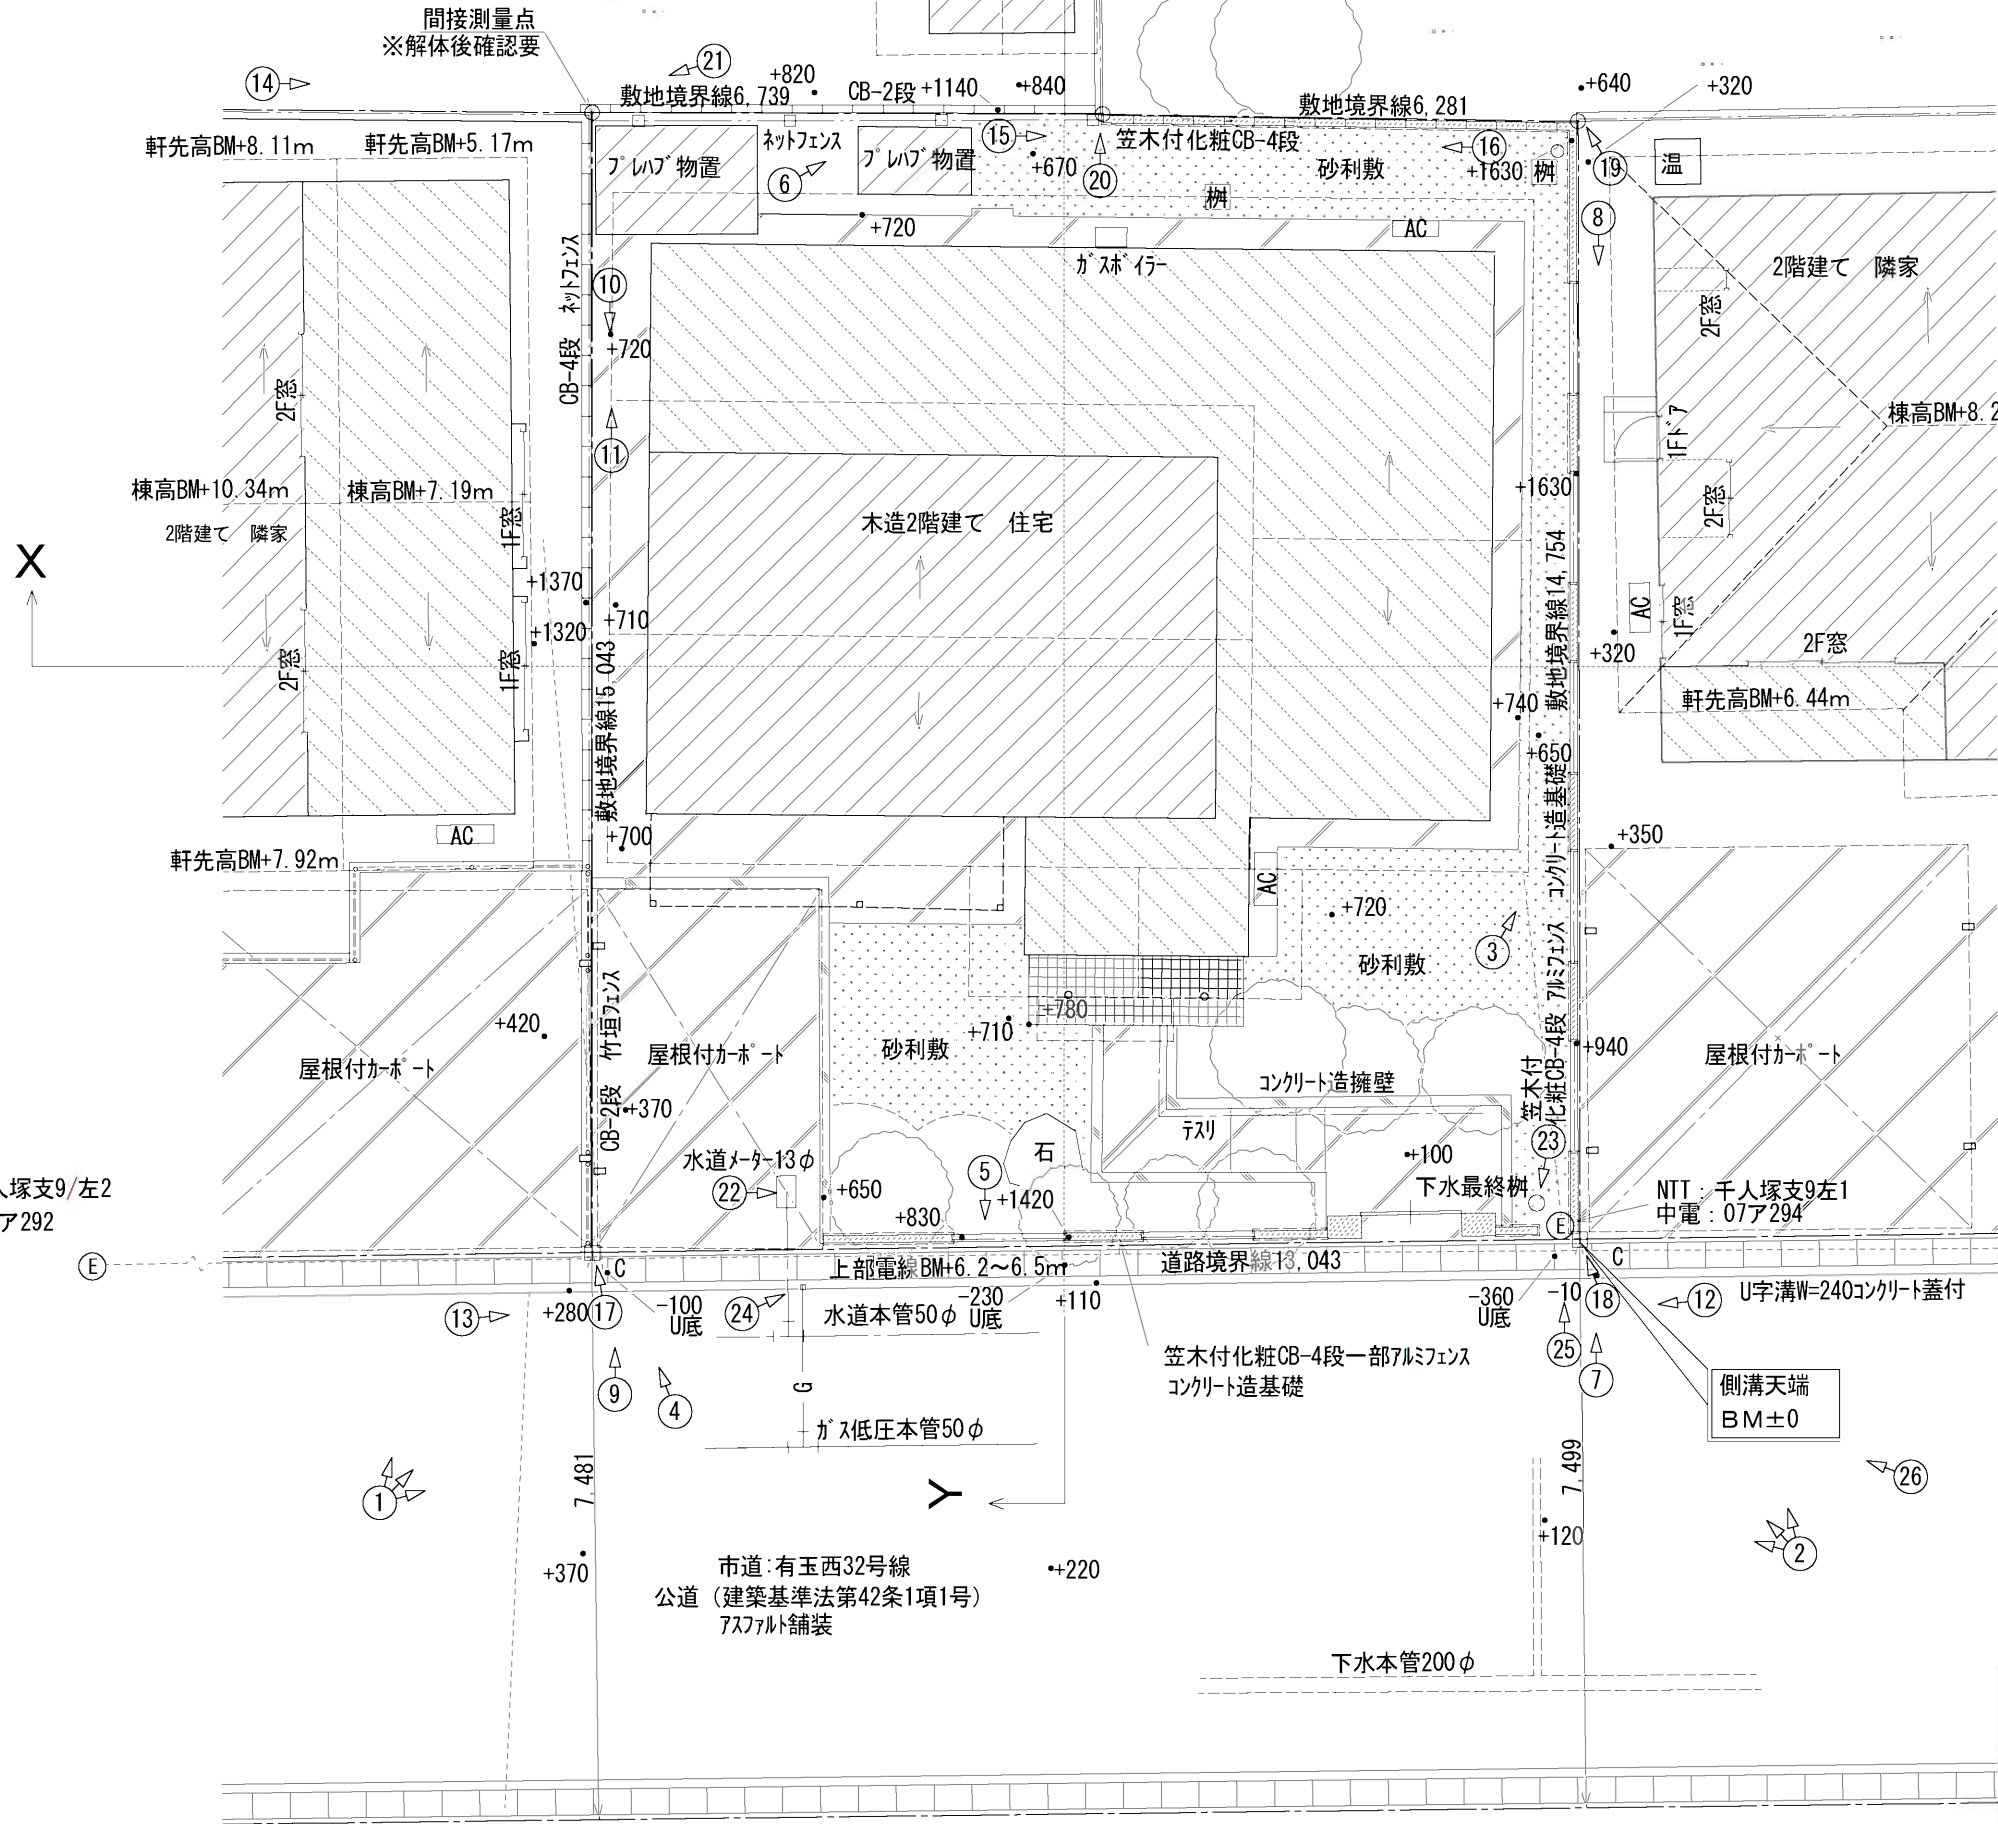

現況平面図 S=1/100

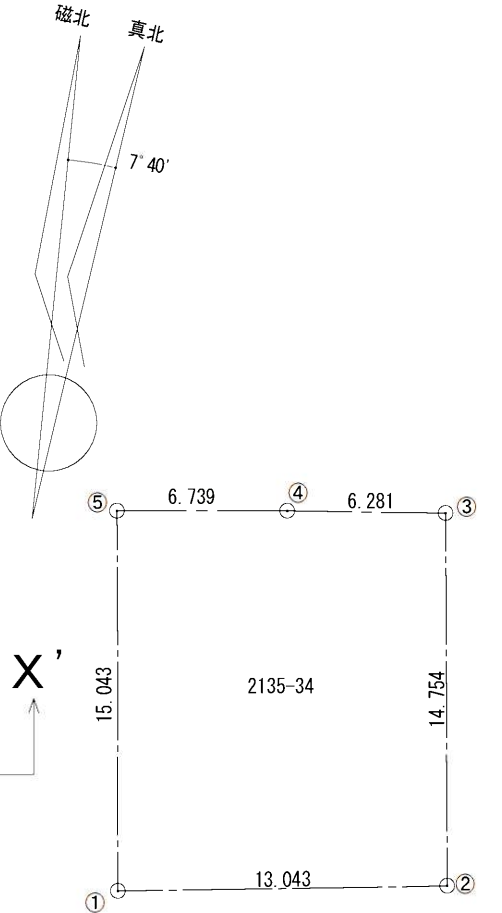

敷地面積求積図 S=1/300

座標面積計算表

座標点	Xn(m)	Yn(m)	(Xn+1 - Xn-1)・Yn
①	0.000	0.000	0.000000
②	13.042	0.205	2.656005
③	12.987	14.959	-94.765064
④	6.707	15.040	-195.821267
⑤	-0.033	15.043	-100.886689
敷地面積 194.40 m ²	倍面積	面積	388.817015 194.408507


登記面積：191.39m²

凡例


- 仮測点 (公図や現況による推測点)
- 田C コンクリート杭
- ⓔ 電柱
- ↑ 写真方向

※当図は、建築計画参考図以外では使用できません。

件名	P G有玉西行ビル様 邸	
図名	現況測量図	
縮尺=1:100 縮尺=1:300	令和6年06月29日	

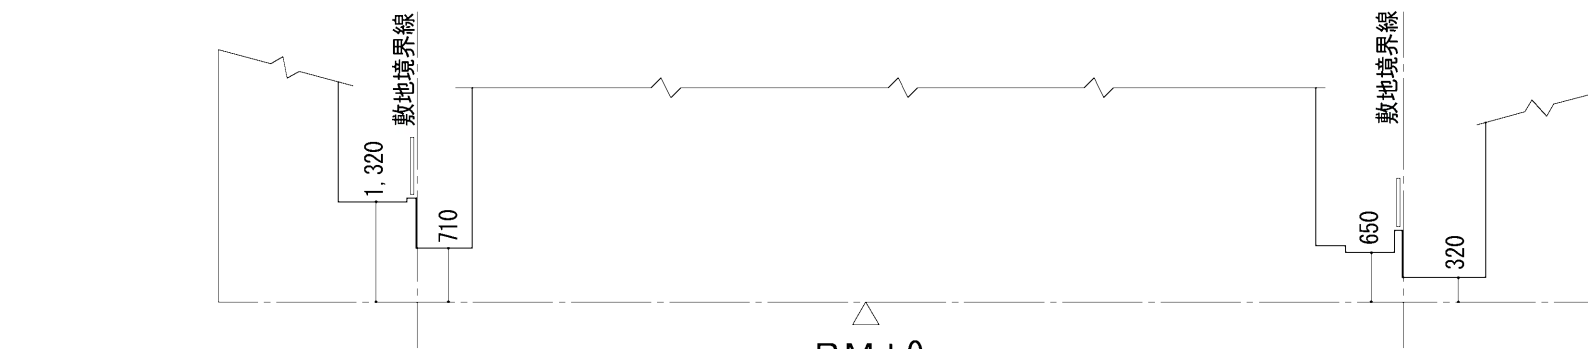

横断面図 (X-X') S=1/100

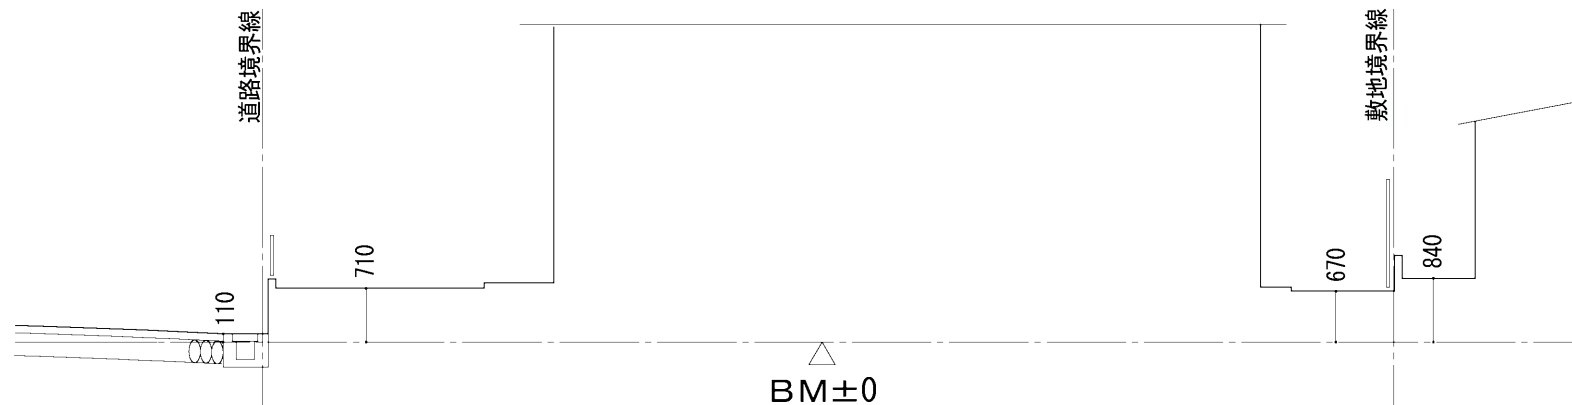

横断面図 (Y-Y') S=1/100

件 名	PG有玉西行`ルウス 様 邸	
図 名	現況測量断面図	
縮尺= 1 : 1 0 0	令和6年06月29日	