


内 部 仕 上 表 （壁下地:石膏ボード12.5mm/天井下地:9.5mm）※脱衣室:床合板特類 下地									
階		床	巾木	壁	品番	廻 縁	天 井	品番	特記事項
1F	ポーチ	LIXILパセオ300/PSO-FIO 4							巾木立上り部はモルタル金鍍仕上
	玄関	LIXILパセオ300/PSO-FIO 4	ライン巾木(W)	ビニルクロス	SLP-250	突付	ビニルクロス	SLP-250	巾木立上り部はモルタル金鍍仕上
	ホール①	イタ銘木フロアーラステックt12 ブラックチェリー3P	ライン巾木(W)	ビニルクロス	SLP-250	突付	ビニルクロス	SLP-250	
	LDK	イタ銘木フロアーラステックt12 ブラックチェリー3P	ライン巾木(W)	ビニルクロス	SLP-250	突付	ビニルクロス	SLP-250	
	畳コーナー	1畳縁ありスタイロ畳 t55	畳寄せ	ビニルクロス	SLP-250	突付	ビニルクロス	SLP-250	畳縁:高田織物 浮No.13
	押入	イタ銘木フロアーラステックt12 ブラックチェリー3P	雑巾摺	ビニルクロス	SLP-250	突付	ビニルクロス	SLP-250	
	洗面所	フロアタイルt2.3 サンゲツIS-2070	H40ソフト巾木W9	ビニルクロス	SLP-250	突付	ビニルクロス	SLP-250	
2F	WC①	フロアタイルt2.3 サンゲツIS-2070	H40ソフト巾木W9	ビニルクロス	SLP-250	突付	ビニルクロス	SLP-250	
	ホール②	イタ銘木フロアーラステックt12 ブラックチェリー3P	ライン巾木(W)	ビニルクロス	SLP-250	突付	ビニルクロス	SLP-250	
	洋室①	イタ銘木フロアーラステックt12 ブラックチェリー3P	ライン巾木(W)	ビニルクロス	SLP-250	突付	ビニルクロス	SLP-250	
	洋室②	イタ銘木フロアーラステックt12 ブラックチェリー3P	ライン巾木(W)	ビニルクロス	SLP-250	突付	ビニルクロス	SLP-250	
	洋室③	イタ銘木フロアーラステックt12 ブラックチェリー3P	ライン巾木(W)	ビニルクロス	SLP-250	突付	ビニルクロス	SLP-250	
	WIC	イタ銘木フロアーラステックt12 ブラックチェリー3P	H40ソフト巾木W9	ビニルクロス	SLP-250	突付	ビニルクロス	SLP-250	
	WC②	フロアタイルt2.3 サンゲツIS-2070	H40ソフト巾木W9	ビニルクロス	SLP-250	突付	ビニルクロス	SLP-250	
物入・収納・CL etc		※接続する部屋と同仕様とする							

上框 & 付框	■ LIXILラシッサS 付框30×150(全周廻し) 色: クリエペール	
階段	■ LIXIL KA 階段	ササラ: プレシャスホワイト
	段板: クリエペール	蹴込板: プレシャスホワイト
	ラウンド手摺: クリエペール	手摺金物: プレシャスホワイト
	上段框: クリエペール	長尺笠木156: LIXIL クリエペール
窓枠 ※YKKap	■ YKKap窓枠スルムタイプ 色: ピュアプレーン	
	※浴室ドア枠 フクビ3方枠 []	
キッチン笠木 カウンター	■ ゴム集成カウンター(オスモカラー) 色: 30627ロアーグリアmatt	
	形状 L型(ジョイント加工)	t=30
天井点検口	■ 天井アルミ点検口枠 450角 TAN45BW	フクビ化学工業 ミルキーホワイト
床下収納庫	■ 高気密型床下点検口断熱型 SPF-R6060 城東テクノ	収納付 (脱衣室) アイボリー(IV)
トイレ棚	■ 2階トイレ D250	アートランバー棚(シェルホワイト)
室内物干し金物	■ なし	
1トイレ バックカウンター	■ アートランバー棚(シェルホワイト) 色:	t=20
下足入	■ LIXILラシッサS 色: プレシャスホワイト	
	サイズ: W800 D400 形状: 二の字型	

支給品	■ 無し
備考	

内 部 建 具 表							
LIXIL		建具色：クリエイペール		枠色 ： 扉同色		※その他、下記特記による	
ラシッサS(標準)		把手 ： スクエアL (シャインニッケル) 丁番 固定枠(156) 外付戸当り ガイドピン床色合せ 引戸のみ上吊Wソフトモーション					
階	No	室名	形式	枠外W サイズ	デザイン	枠色	特記事項
				枠外H サイズ	建具色	把手	
1	1	LDK	片開き戸	—	LGC	—	
	WD			2000	—	—	
	2	洗面所	片引き戸	—	LAA	—	明り窓・表示錠
	WD			2000	—	—	
	3	押入	折れ戸	—	LAD	—	角型Lタテ取付
	WD			2000	—	—	
	4	パントリー	観音開	—	LAA	—	
	WD			2000	—	—	
	5	物入	観音開	—	LAA	—	
	WD			2000	—	—	
	6	WC①	片開き戸	—	LAA	—	明り窓・表示錠
	WD			2000	—	—	
2							
	7	WC②	片開き戸	—	LAA	—	明り窓・表示錠
	WD			2000	—	—	
	8	洋室①	片開き戸	—	LAA	—	
	WD			2000	—	—	
	9	洋室②	片開き戸	—	LAA	—	
	WD			2000	—	—	
	10	洋室③	片開き戸	—	LAA	—	
	WD			2000	—	—	


	浜 岡 一 級 総 合 設 計 事 務 所 一級建築士事務所 静岡県知事登録第 (10)2441 号 一級建築士 大臣登録第 365879 号 西原利昌	LIFEFUND 株式会社 LIFEFUND InDesign office 一級建築士事務所 事務所登録 (2) 第7595号 一級建築士登録 第179770号 鈴木 達男 〒432-8023 静岡県浜松市中央区鴨江3丁目70番23号	年 月 日 2024.7.16	件名 PG有玉西 分譲		設計	IC	工務	図 番
						倉田	0	青島	1-2
			縮尺	図面 仕上表 2					

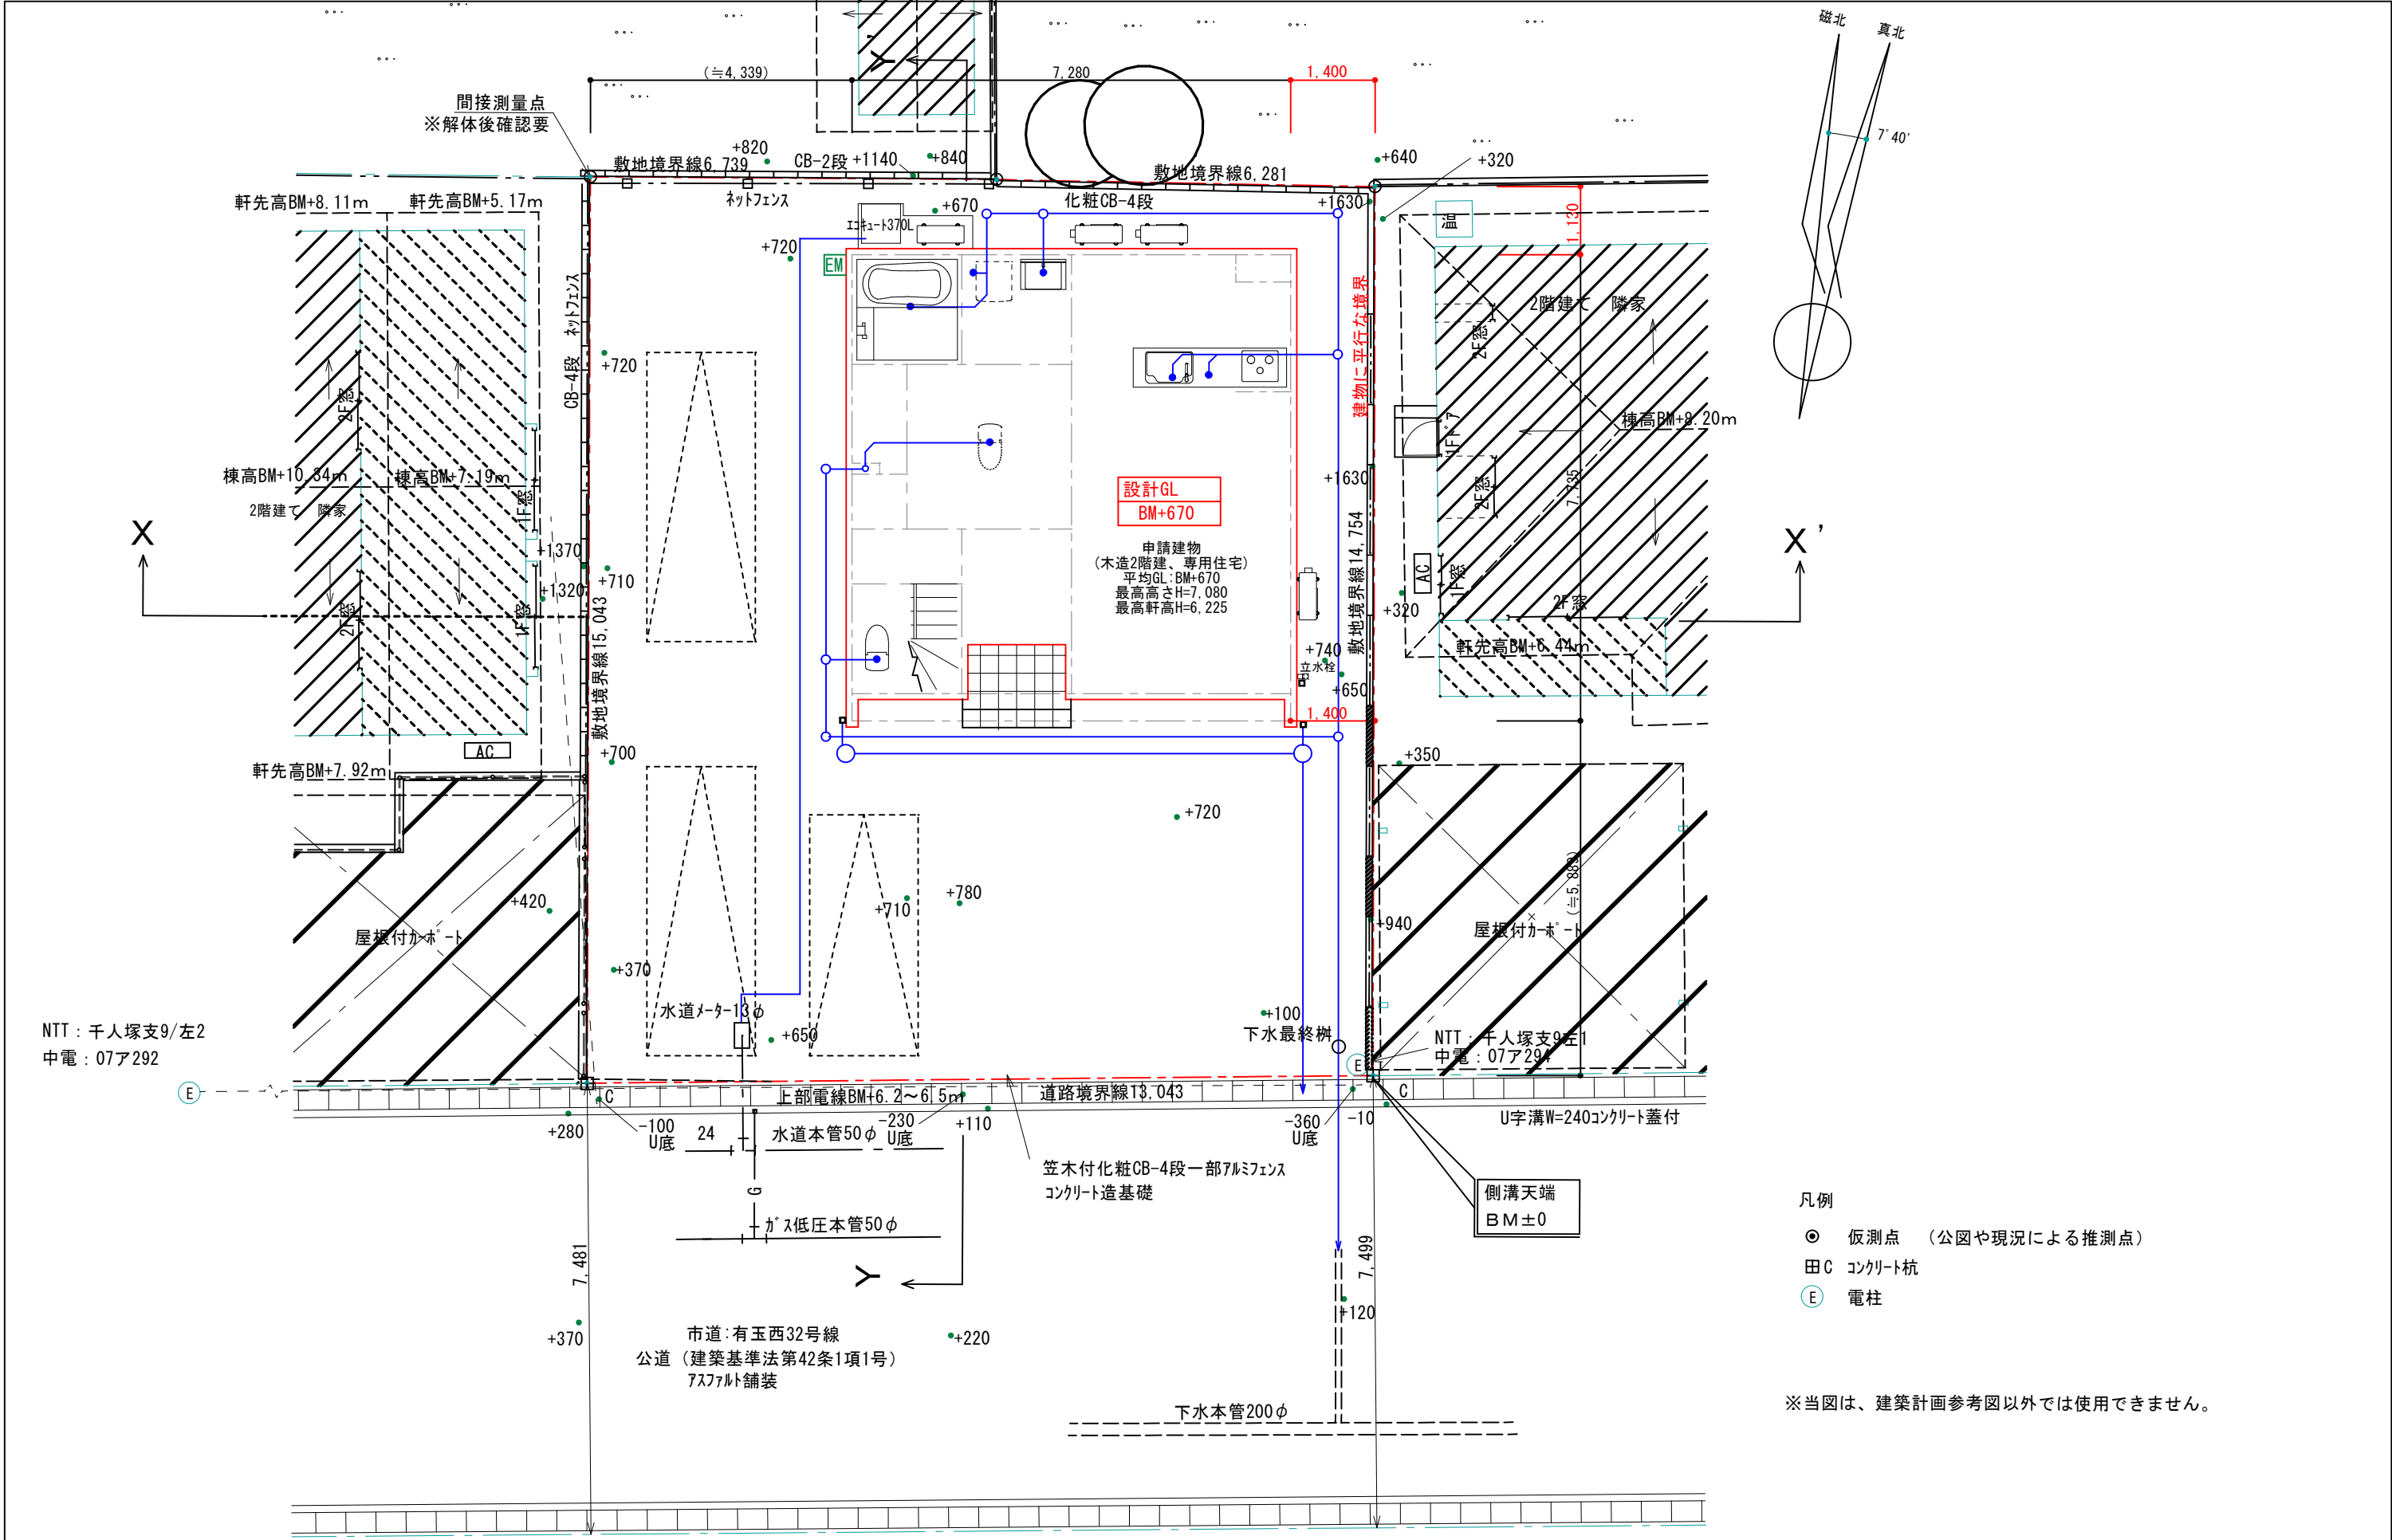

現況平面図 S=1/100

凡例
● 仮測点 (公図や現況による推測点)
田C コンクリート杭
E 電柱
※当図は、建築計画参考図以外では使用できません。

訂正	浜岡一級総合設計事務所 一級建築士事務所 静岡県知事登録第 (10) 2441 号 一級建築士 大臣登録第 365879 号 西原利昌	LIFEFUND PG HOUSE	株式会社 LIFEFUND InDesign office 一級建築士事務所 事務所登録 (2) 第7595号 一級建築士登録 第179770号 鈴木 達男 〒432-8023 静岡県浜松市中央区鴨江3丁目70番23号	年月日 2024. 7. 16	件名 PG有玉西分譲 新築工事		設計	IC	工事	図番
				縮尺 1/50	図名 配置図		倉田		青島	2-1

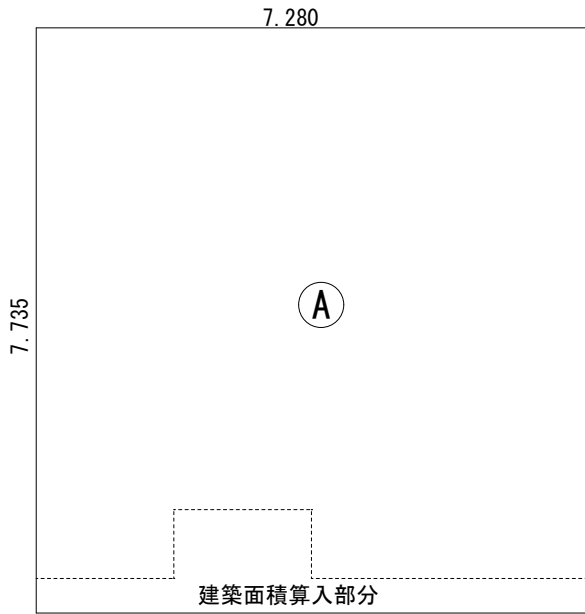


建築面積求積図 S=1/100

建築面積求積表

番号	計算式	(m)	面積 (㎡)
Ⓐ	7.280 × 7.735		56.3108
合計			56.3108 56.31


(17.0坪)

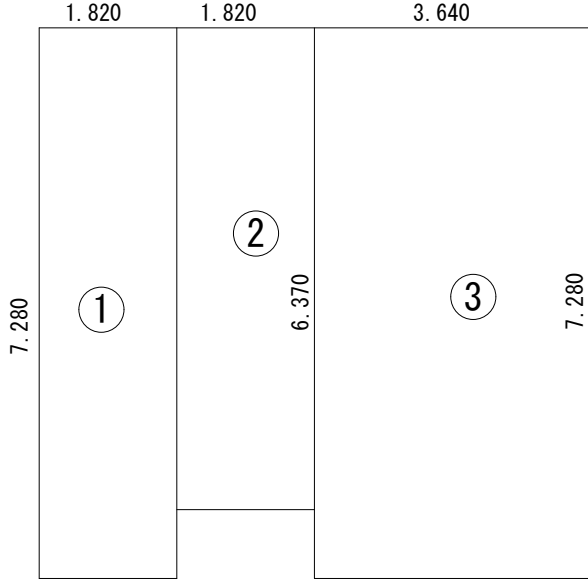

1階床面積図 S=1/100

1階床面積求積表

番号	計算式	(m)	面積 (㎡)
①	1.820 × 7.280		13.2496
②	1.820 × 6.370		11.5934
③	3.640 × 7.280		26.4992
合計			51.3422 51.34

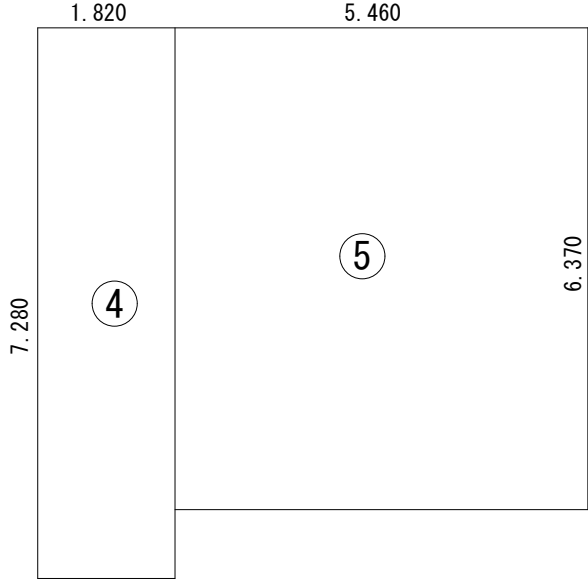

2階床面積図 S=1/100


2階床面積求積表

番号	計算式	(m)	面積 (㎡)
④	1.820 × 7.280		13.2496
⑤	5.460 × 6.370		34.7802
合計			48.0298 48.02

延べ床面積表

	番号	(m)	面積 (㎡)
1階床面積	① ② ③		51.34
2階床面積	④ ⑤		48.02
合計			99.36

(30.0坪)

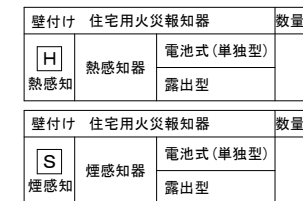

※ 煙感知器は壁・梁より600mm以上離す
壁に取付ける場合、
天井から150mm以上500mm以内離す
換気扇・エアコン吹出口から1500mm以上離す
※ 全室LED照明とする。

* 凡例


-  管柱 (105 × 105)
-  K^h・^h -
(3.30倍 FRM-0641)
-  片筋違
(2.00倍 45 × 90)
(例 左:柱脚 右:柱頭)
-  たすき掛筋違
(4.00倍 45 × 90)
- 構造用合板 (2.50倍)
(t=9 タイライト)
-  床点検口
-  天井点検口
-  換気扇
-  熱交換換気扇

コスモワイド スクエア
スマートデザイン (外部)

- | | | |
|-------|-------------------|-----|
| 1 | コンセント | 1ヶ所 |
| 2 | コンセント | 2ヶ所 |
| 3 | コンセント | 3ヶ所 |
| 1 E T | コンセント1ヶ所接地ターミナル | |
| 2 E T | コンセント2ヶ所接地ターミナル | |
| WP | 防水型 | |
| | エアコン用コンセント | |
| | 200V用コンセント | |
| WP | 防雨入線プレート | |
| | スイッチ | |
| 3 | 3路スイッチ | |
| 4 | 4路スイッチ | |
| | 直結電源 | |
| TV | テレビ取出し口 | |
| TEL | 電話取出し口 (テレホンガイド) | |
| LAN | LAN取出し口 (テレホンガイド) | |
| | 壁照明 | |
| | リモコン (給湯遠隔・ルーフ) | |
| | メーター | |
| | 分電盤 | |
| | インターホン | |
| | チャーム | |


※ACコンセント天井付け
※TVアンテナ工事
※スイッチはFL+1100、コンセントはFL+200

訂 正	浜 岡 一 級 総 合 設 計 事 務 所 一級建築士事務所 静岡県知事登録第 (10)2441 号 一級建築士 大丘登録第 365879 号 西原利昌	LIFEFUND PG HOUSE	株式会社 LIFEFUND InDesign office 一級建築士事務所 事務所登録 (2)第7595号 一級建築士登録 第179770号 鈴木 達男 〒432-8023 静岡県浜松市中央区鴨江3丁目70番23号	年 月 日	件 名	PG有玉西分譲 新築工事		設計	IC	工事	図 番
				縮 尺				図 名	倉 田		青 島
							2024. 7. 16		2 階平面図		

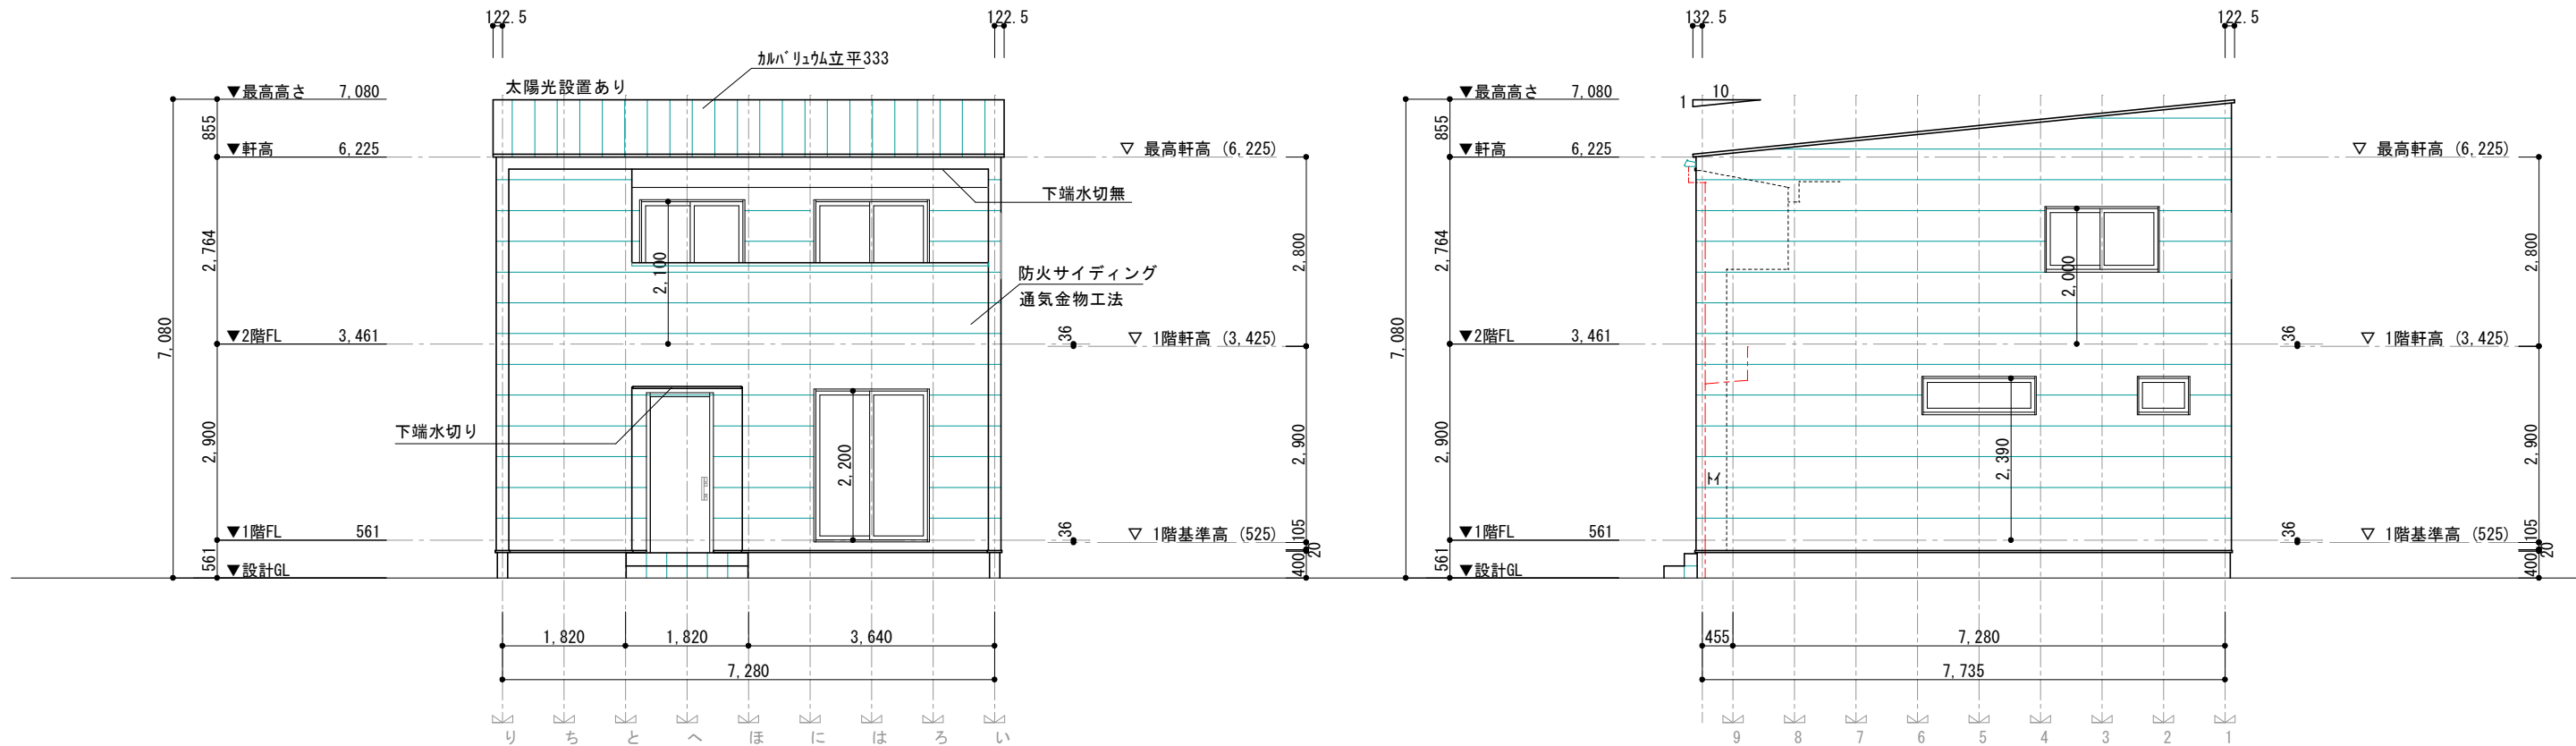


南側立面図 S=1/100


東側立面図 S=1/100

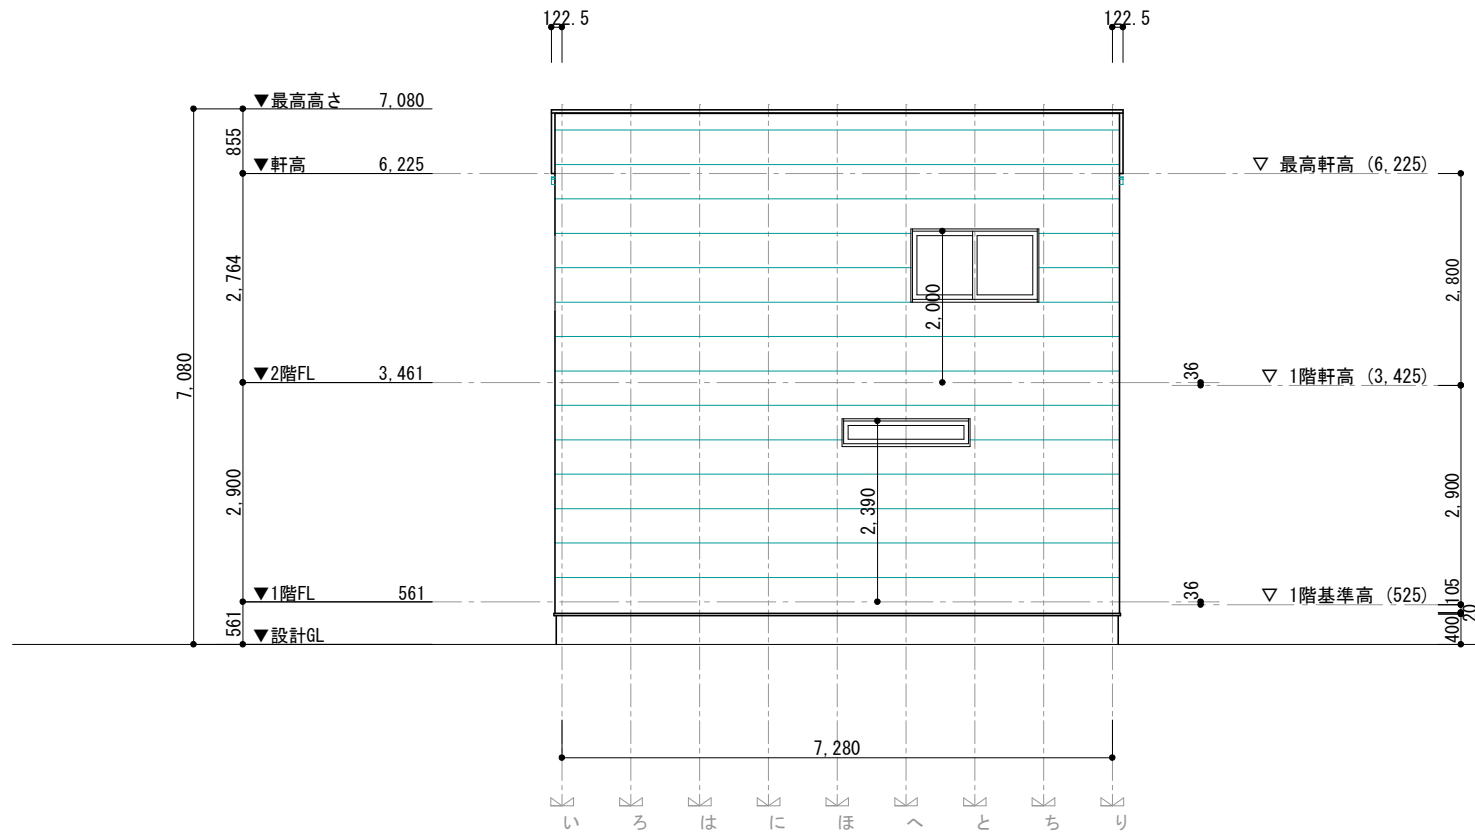


北側立面図 S=1/100

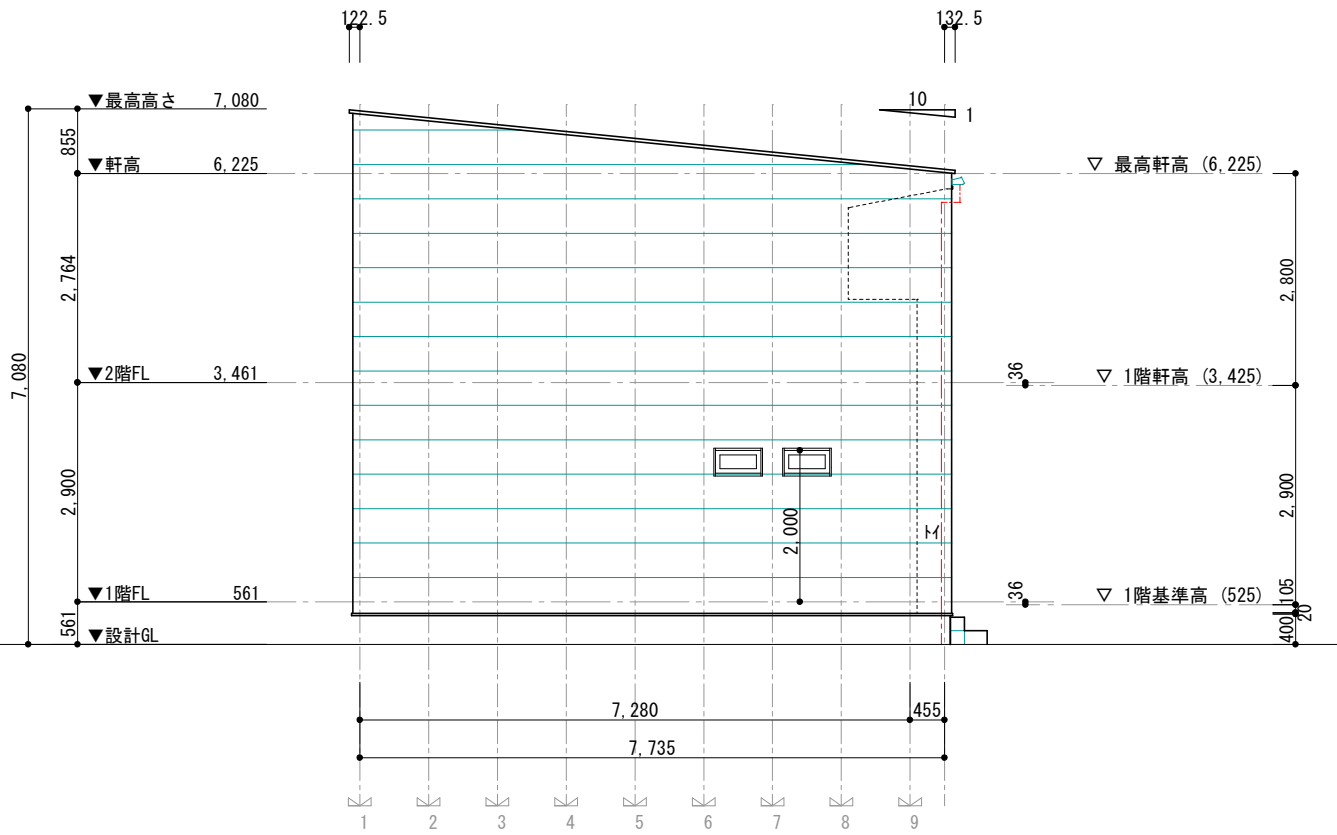


西側立面図 S=1/100

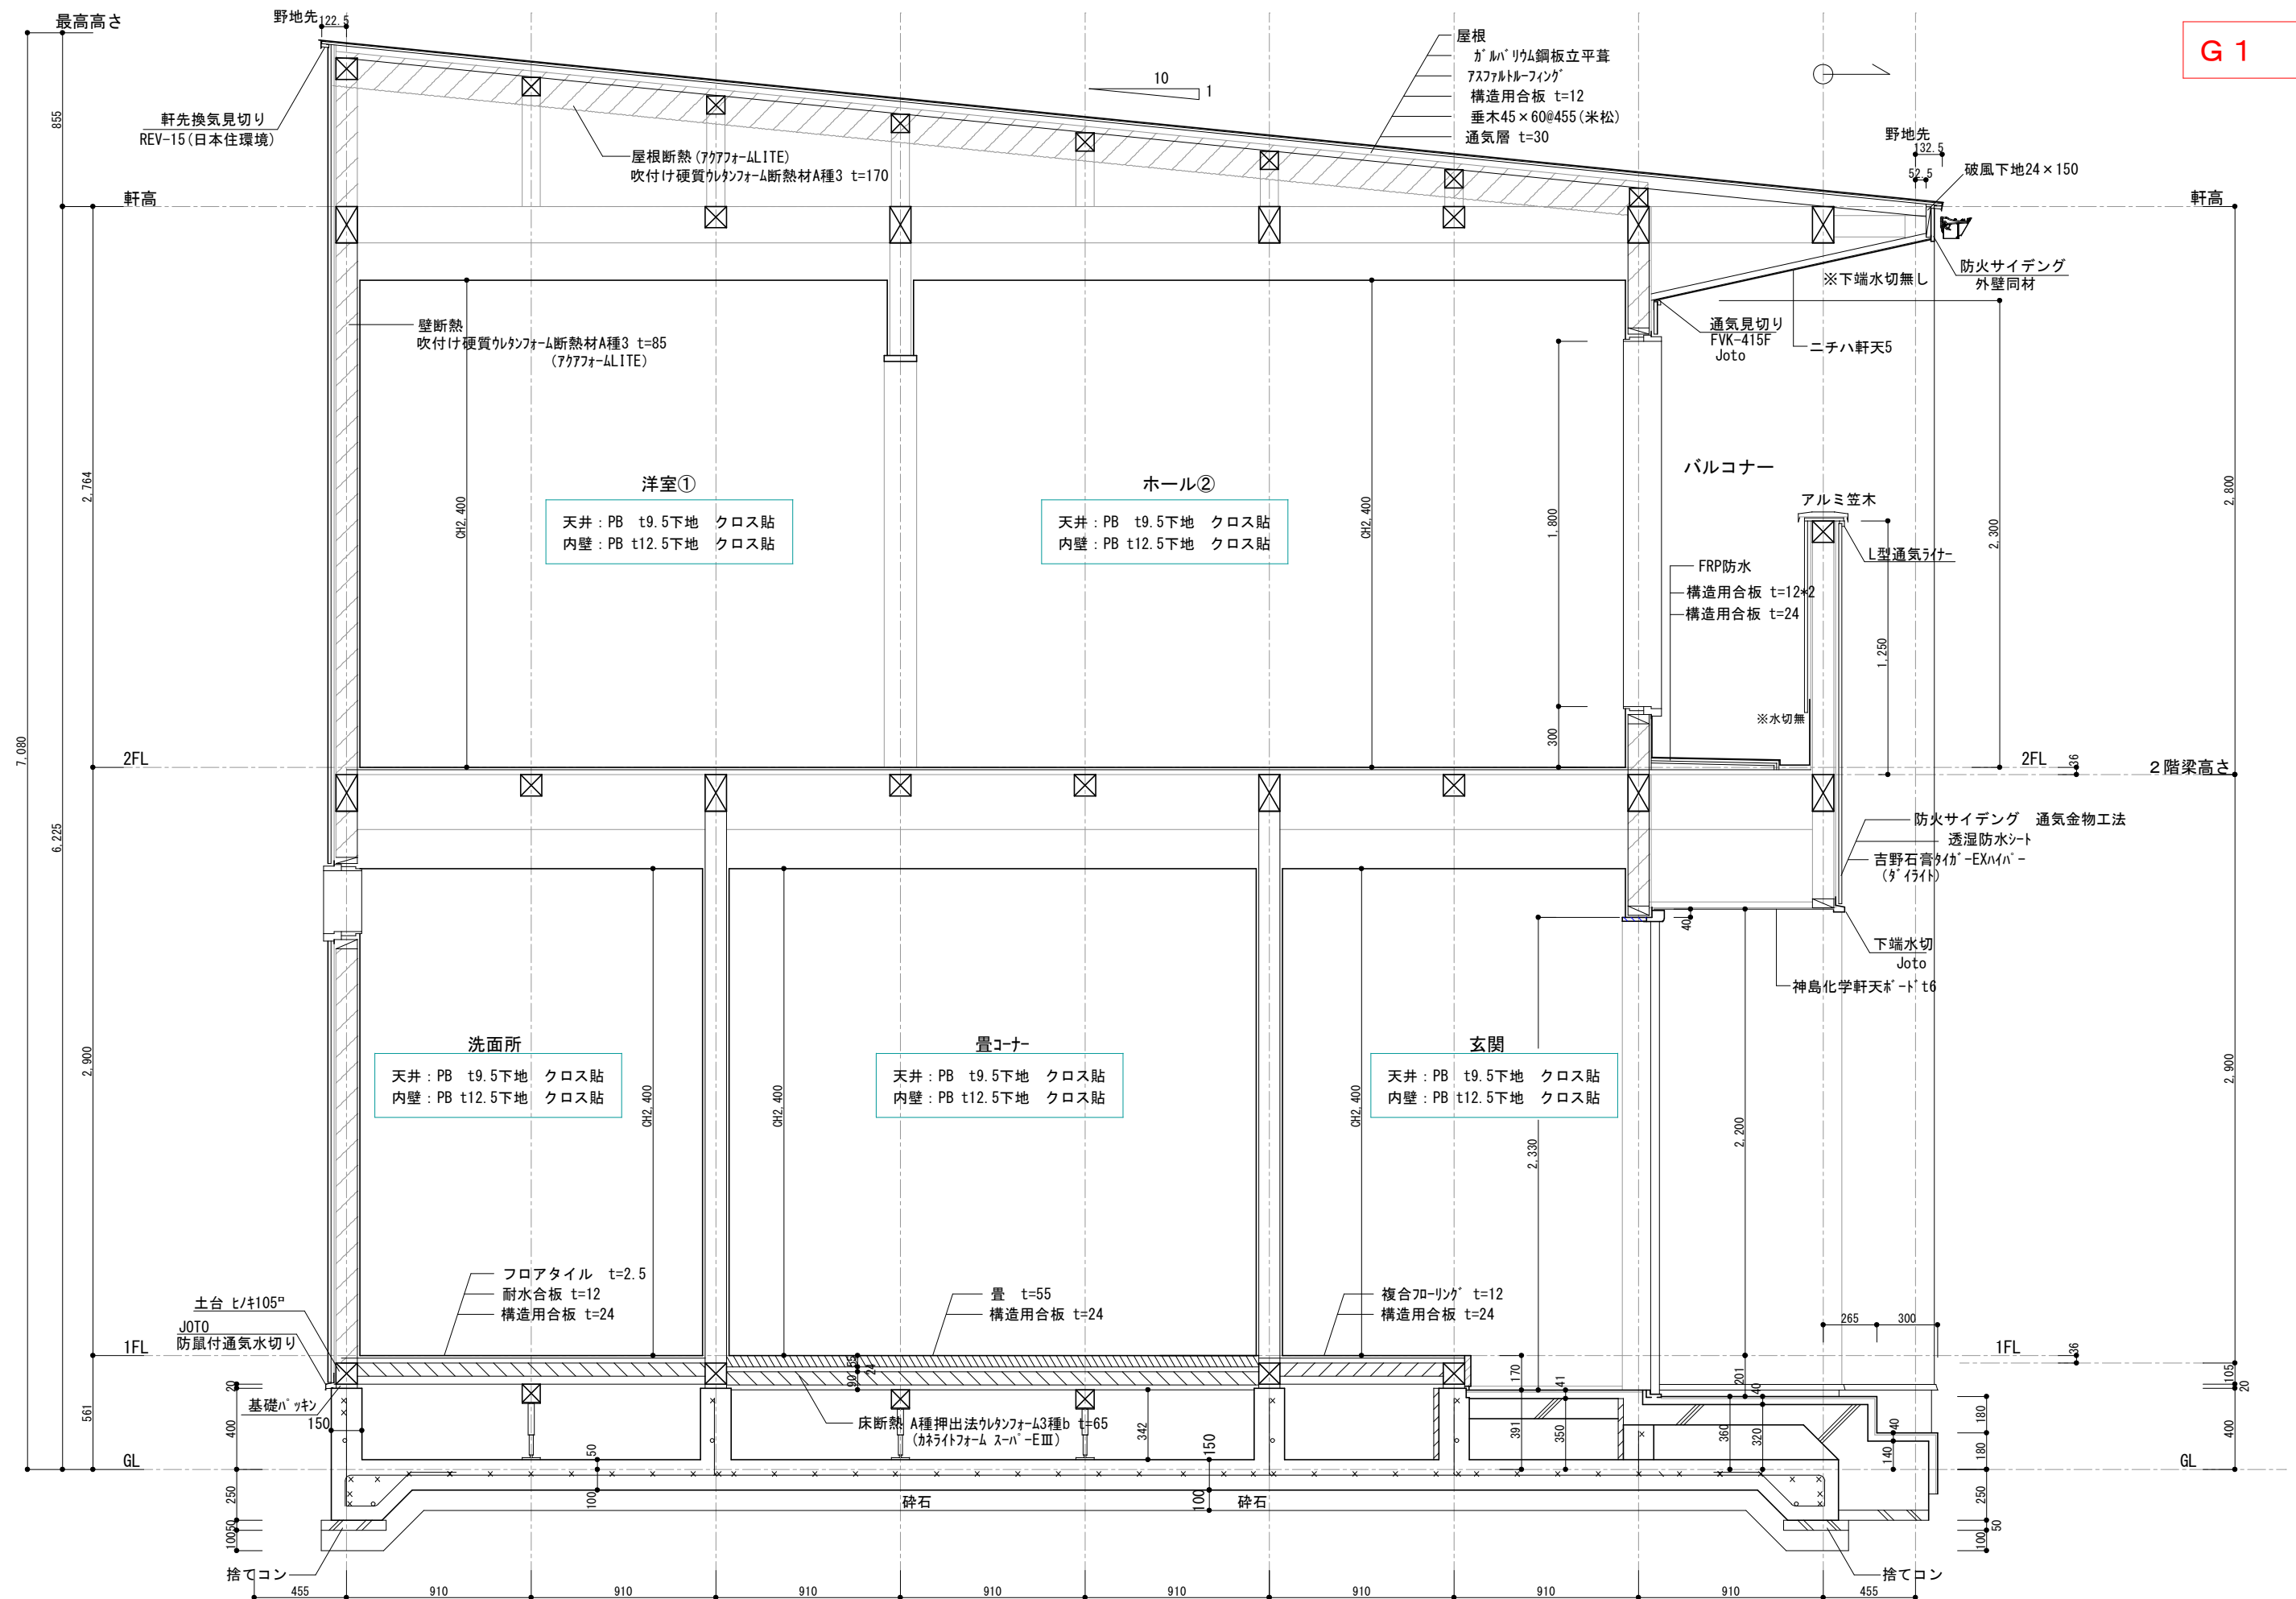


訂 正	浜 岡 一 級 総 合 設 計 事 務 所 一級建築士事務所 静岡県知事登録第 (10)2441 号 一級建築士 大臣登録第 365879 号 西原利昌	LIFEFUND PG HOUSE	株式会社 LIFEFUND InDesign office 一級建築士事務所 事務所登録 (2)第7595号 一級建築士登録 第179770号 鈴木 達男 〒432-8023 静岡県浜松市中央区鴨江3丁目70番23号	年 月 日	件 名		設 計	IC	工 事	図 番
				2024. 7. 16	PG有玉西 分譲 新築工事		倉 田		青 島	5-1
				縮 尺	図 名					
				1/30	矩計図					

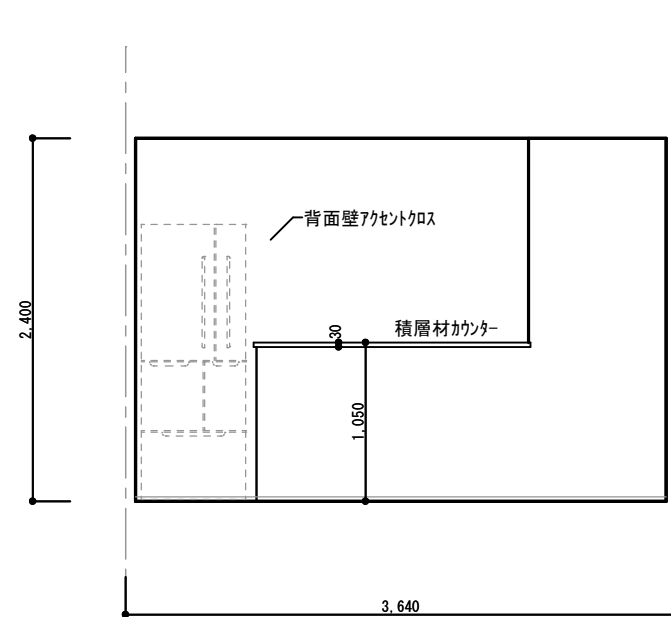


LDK 南面

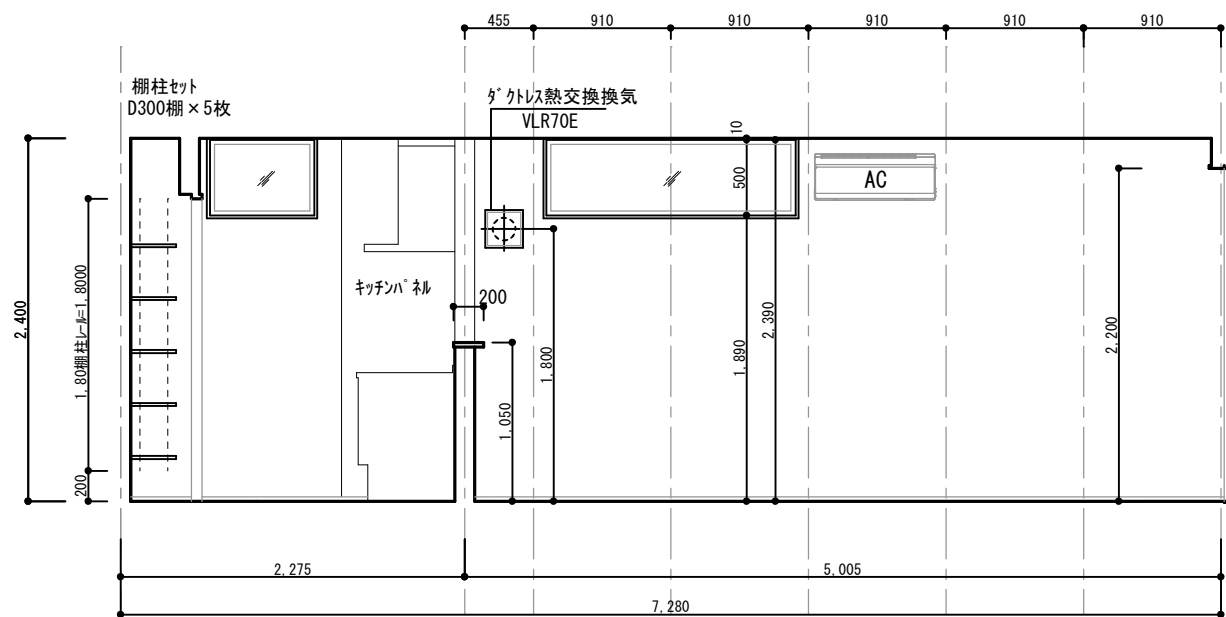


LDK 東面

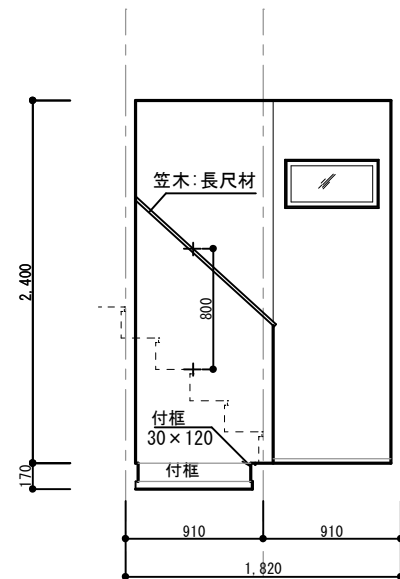


玄関 西面

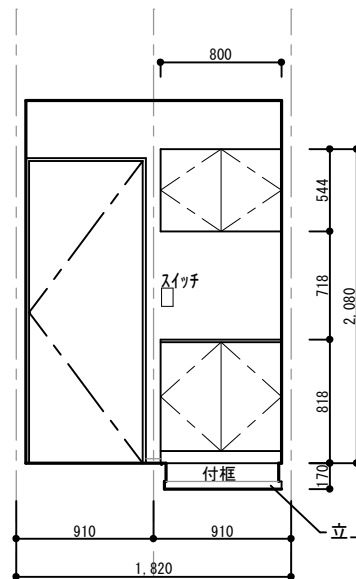


玄関 東面

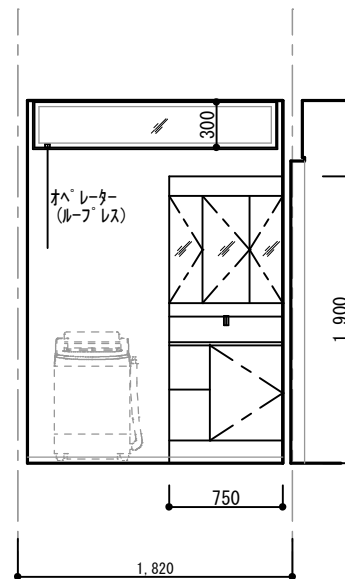


洗面所 北面

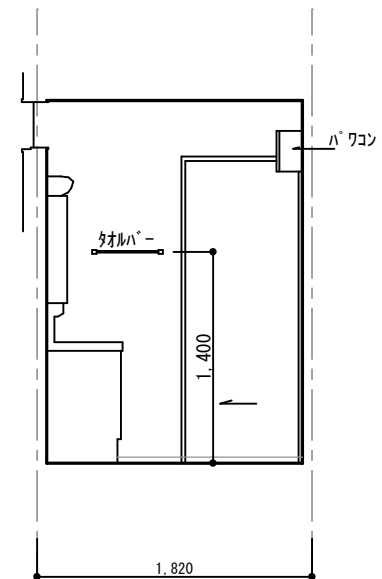


洗面所 東面

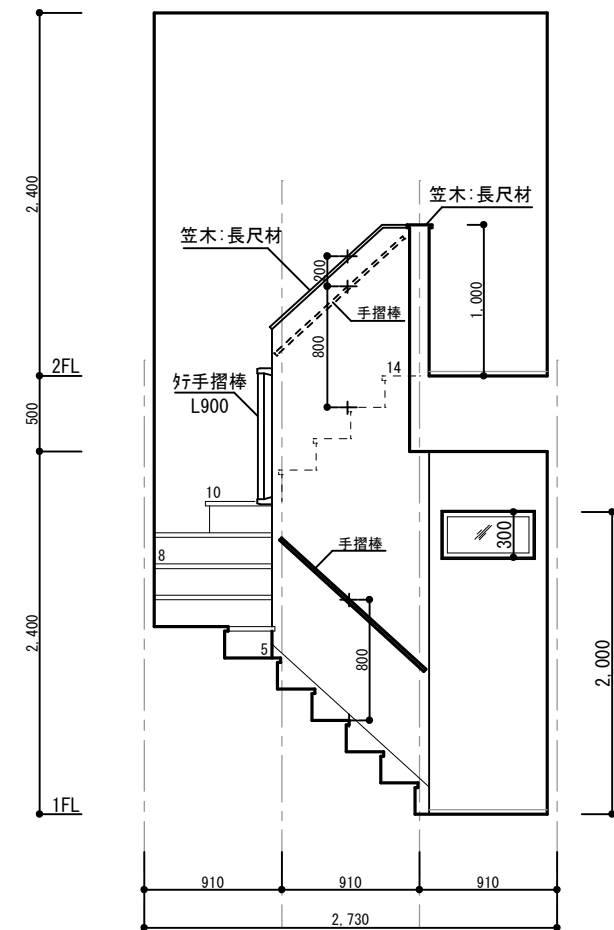


階段 西面

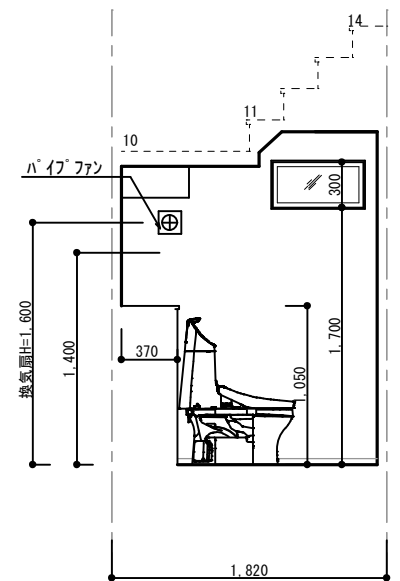


WC② 西面

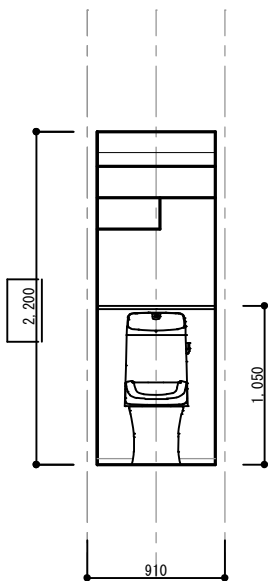


WC① 南面

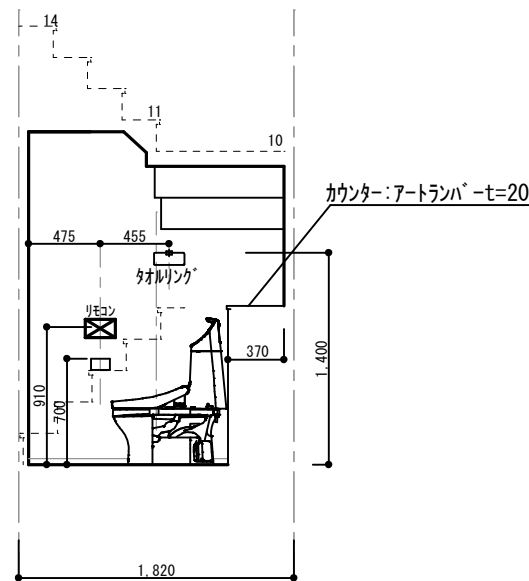

WC② 東面

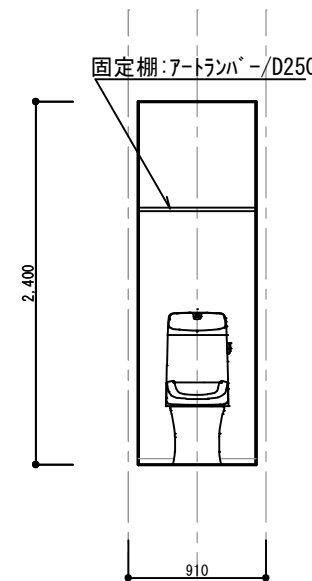


WC② 北面

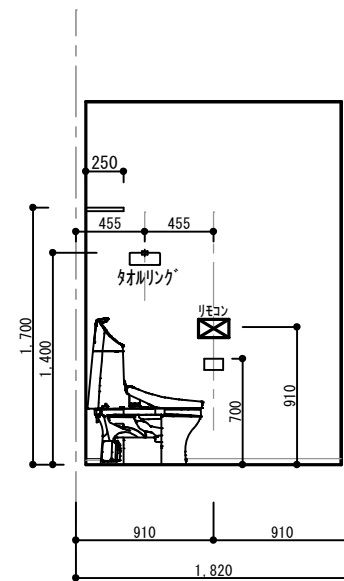

WC② 東面

訂正	浜岡 一級総合設計事務所 一級建築士事務所 静岡県知事登録第 (10)2441 号 一級建築士 大臣登録第 365879 号 西原利晶	LIFEFUND PG HOUSE	株式会社 LIFEFUND InDesign office 一級建築士事務所 事務所登録 (2)第7595号 一級建築士登録 第179770号 鈴木 達男 〒432-8023 静岡県浜松市中央区鴨江3丁目70番23号	年月日 2024.07.16	件名 PG有玉西分譲 新築工事		設計	IC	工事	図番
				縮尺 1/30	図名 展開図(1)		倉田		青島	6-1

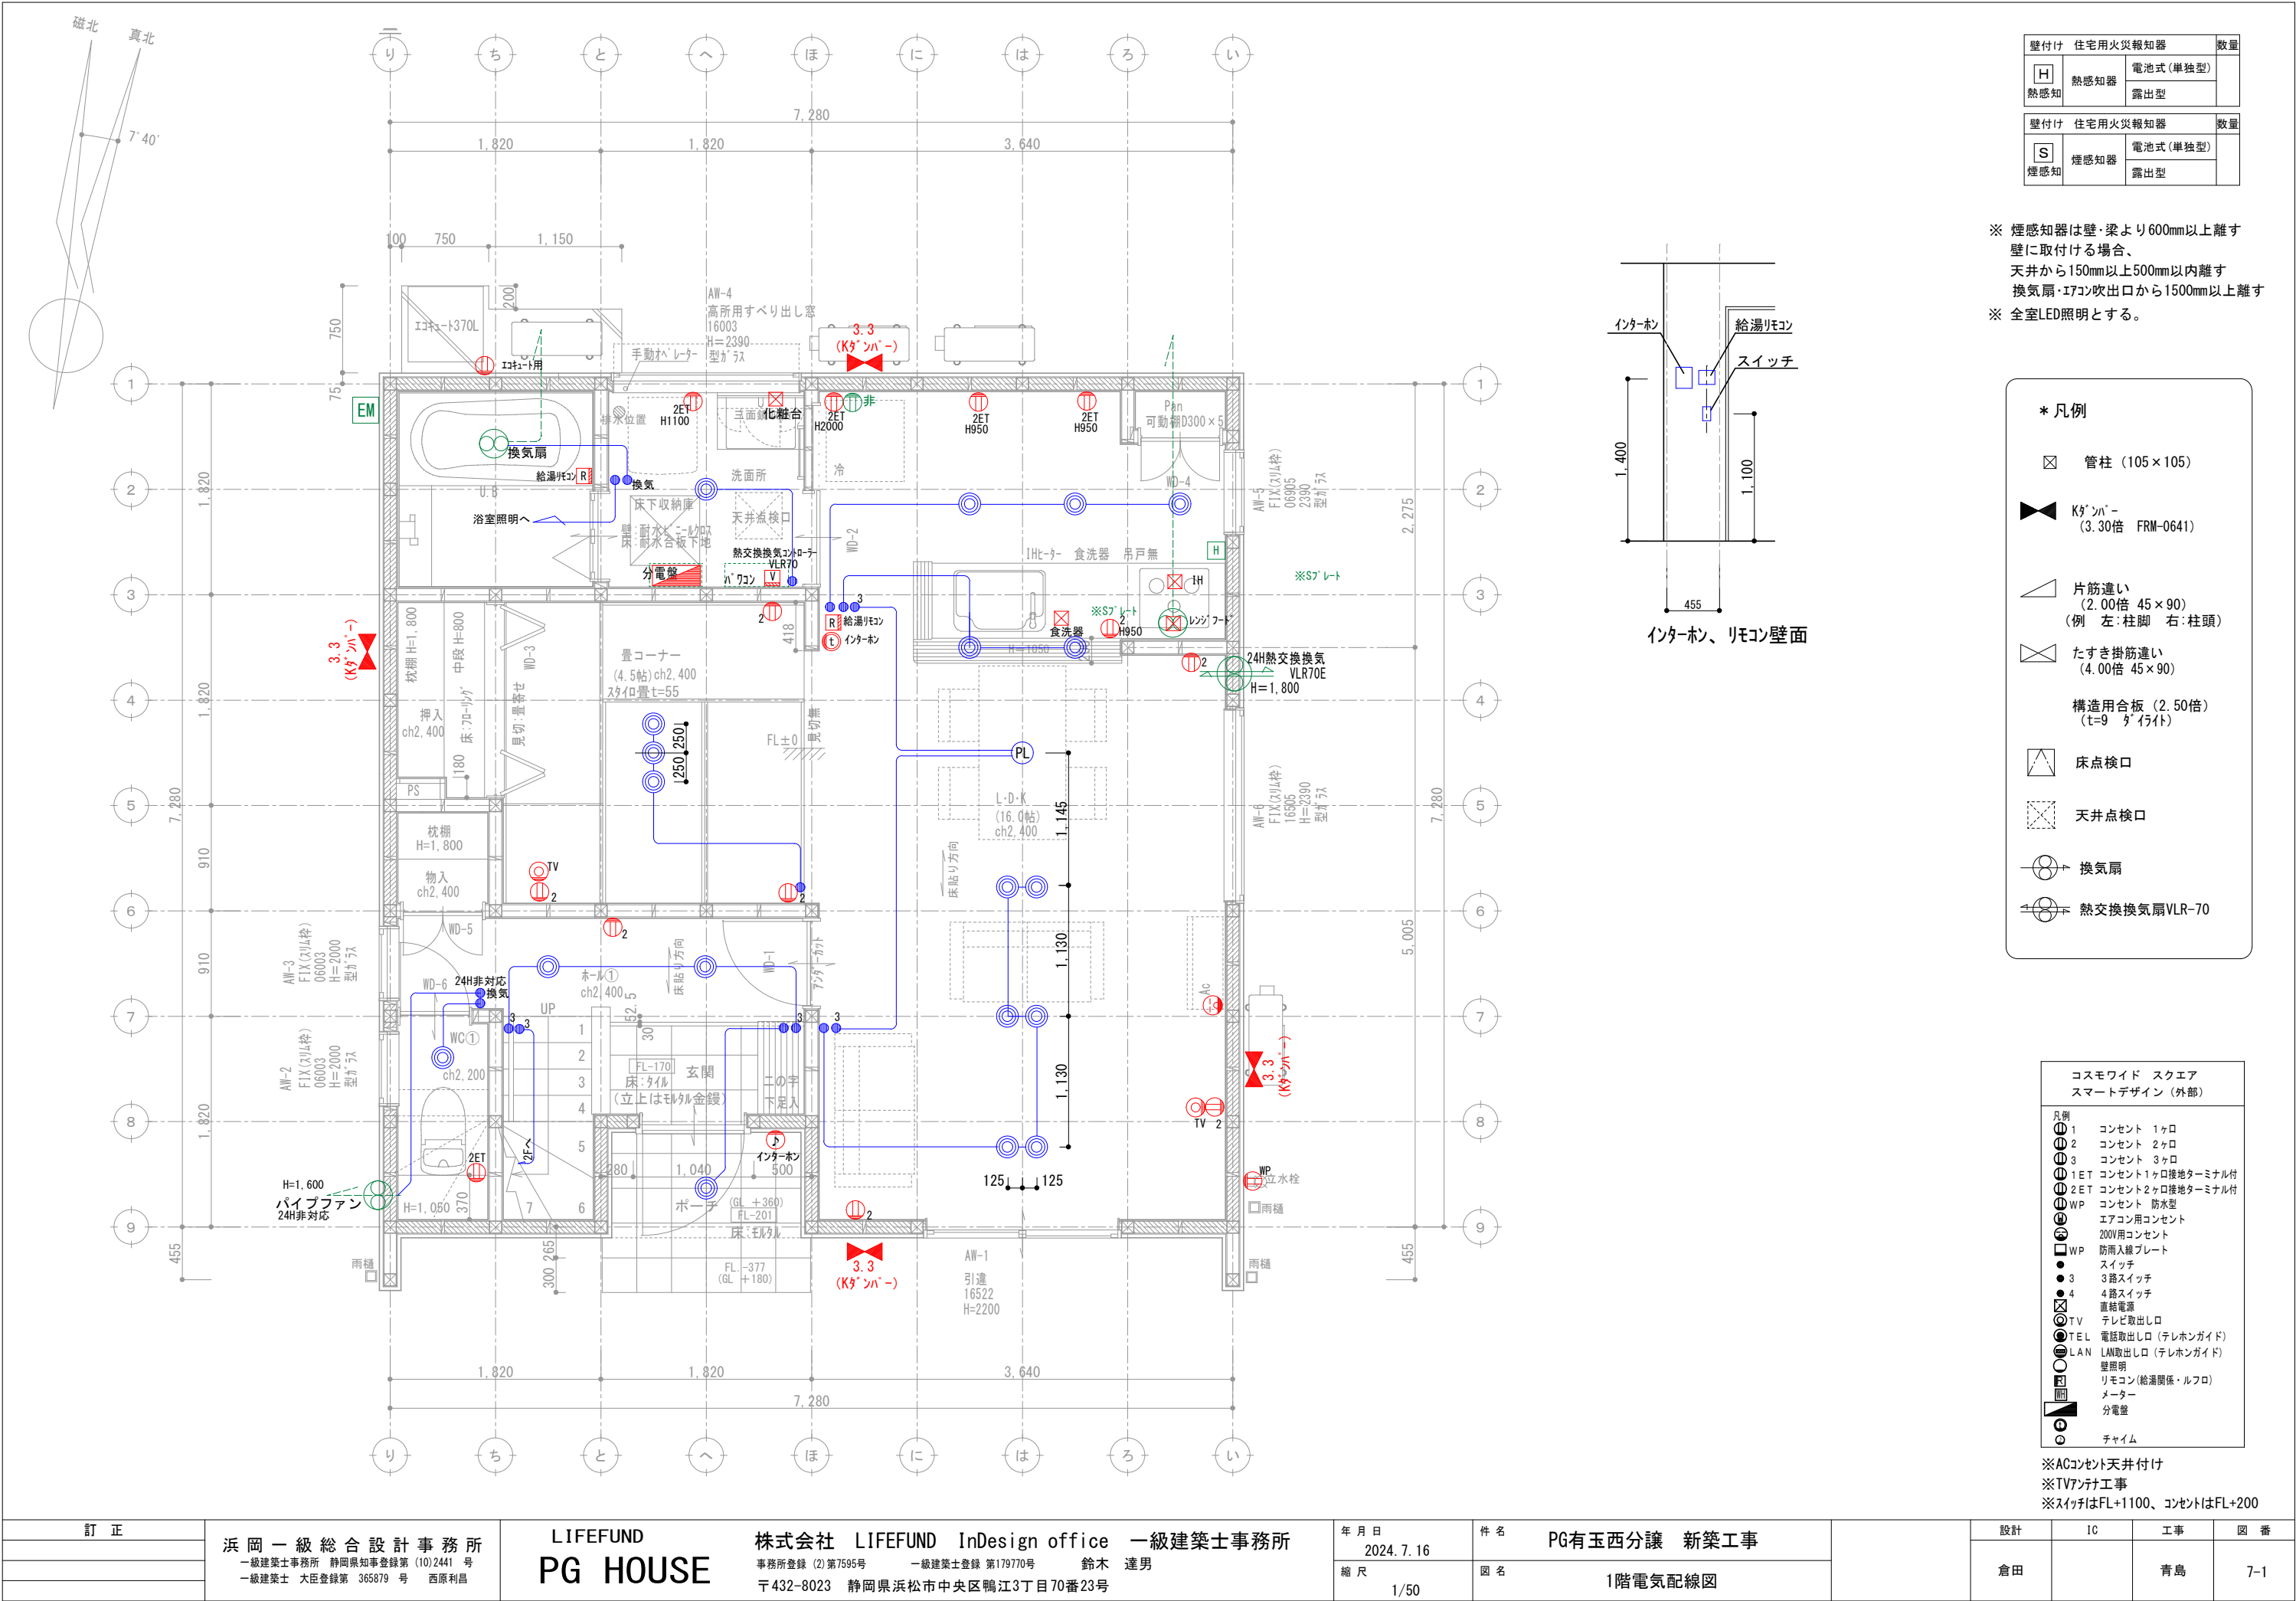


壁付け 住宅用火災報知器			数量
H 熱感知	熱感知器	電池式 (単独型)	
		露出型	

壁付け 住宅用火災報知器			数量
S 煙感知	煙感知器	電池式 (単独型)	
		露出型	

※ 煙感知器は壁・梁より600mm以上離す壁に取付ける場合、天井から150mm以上500mm以内離す換気扇・エアコン吹出口から1500mm以上離す

※ 全室LED照明とする。

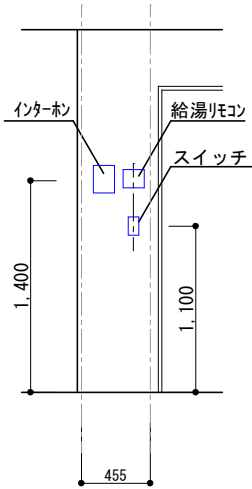


インターホン、リモコン壁面

*** 凡例**

- 管柱 (105×105)
- Kダクト (3.30倍 FRM-0641)
- 片筋違い (2.00倍 45×90) (例 左:柱脚 右:柱頭)
- たすき掛筋違い (4.00倍 45×90)
- 構造用合板 (2.50倍) (t=9 タイライト)
- 床点検口
- 天井点検口
- 換気扇
- 熱交換換気扇VLR-70

コスモワイド スクエア スマートデザイン (外部)		
凡例	1	コンセント 1ヶロ
2	コンセント 2ヶロ	
3	コンセント 3ヶロ	
1ET	コンセント1ヶロ接地ターミナル付	
2ET	コンセント2ヶロ接地ターミナル付	
WP	コンセント 防水型	
エア	エアコン用コンセント	
200V	200V用コンセント	
WP	防雨入線プレート	
スイッチ	スイッチ	
3	3路スイッチ	
4	4路スイッチ	
直結	直結電源	
TV	テレビ取出口	
TEL	電話取出口 (テレホンガイド)	
LAN	LAN取出口 (テレホンガイド)	
壁照明	壁照明	
リモコン	リモコン (給湯関係・ルフロ)	
メーター	メーター	
分電盤	分電盤	
チャイム	チャイム	

※ACコンセント天井付け
※TVアンテナ工事
※スイッチはFL+1100、コンセントはFL+200

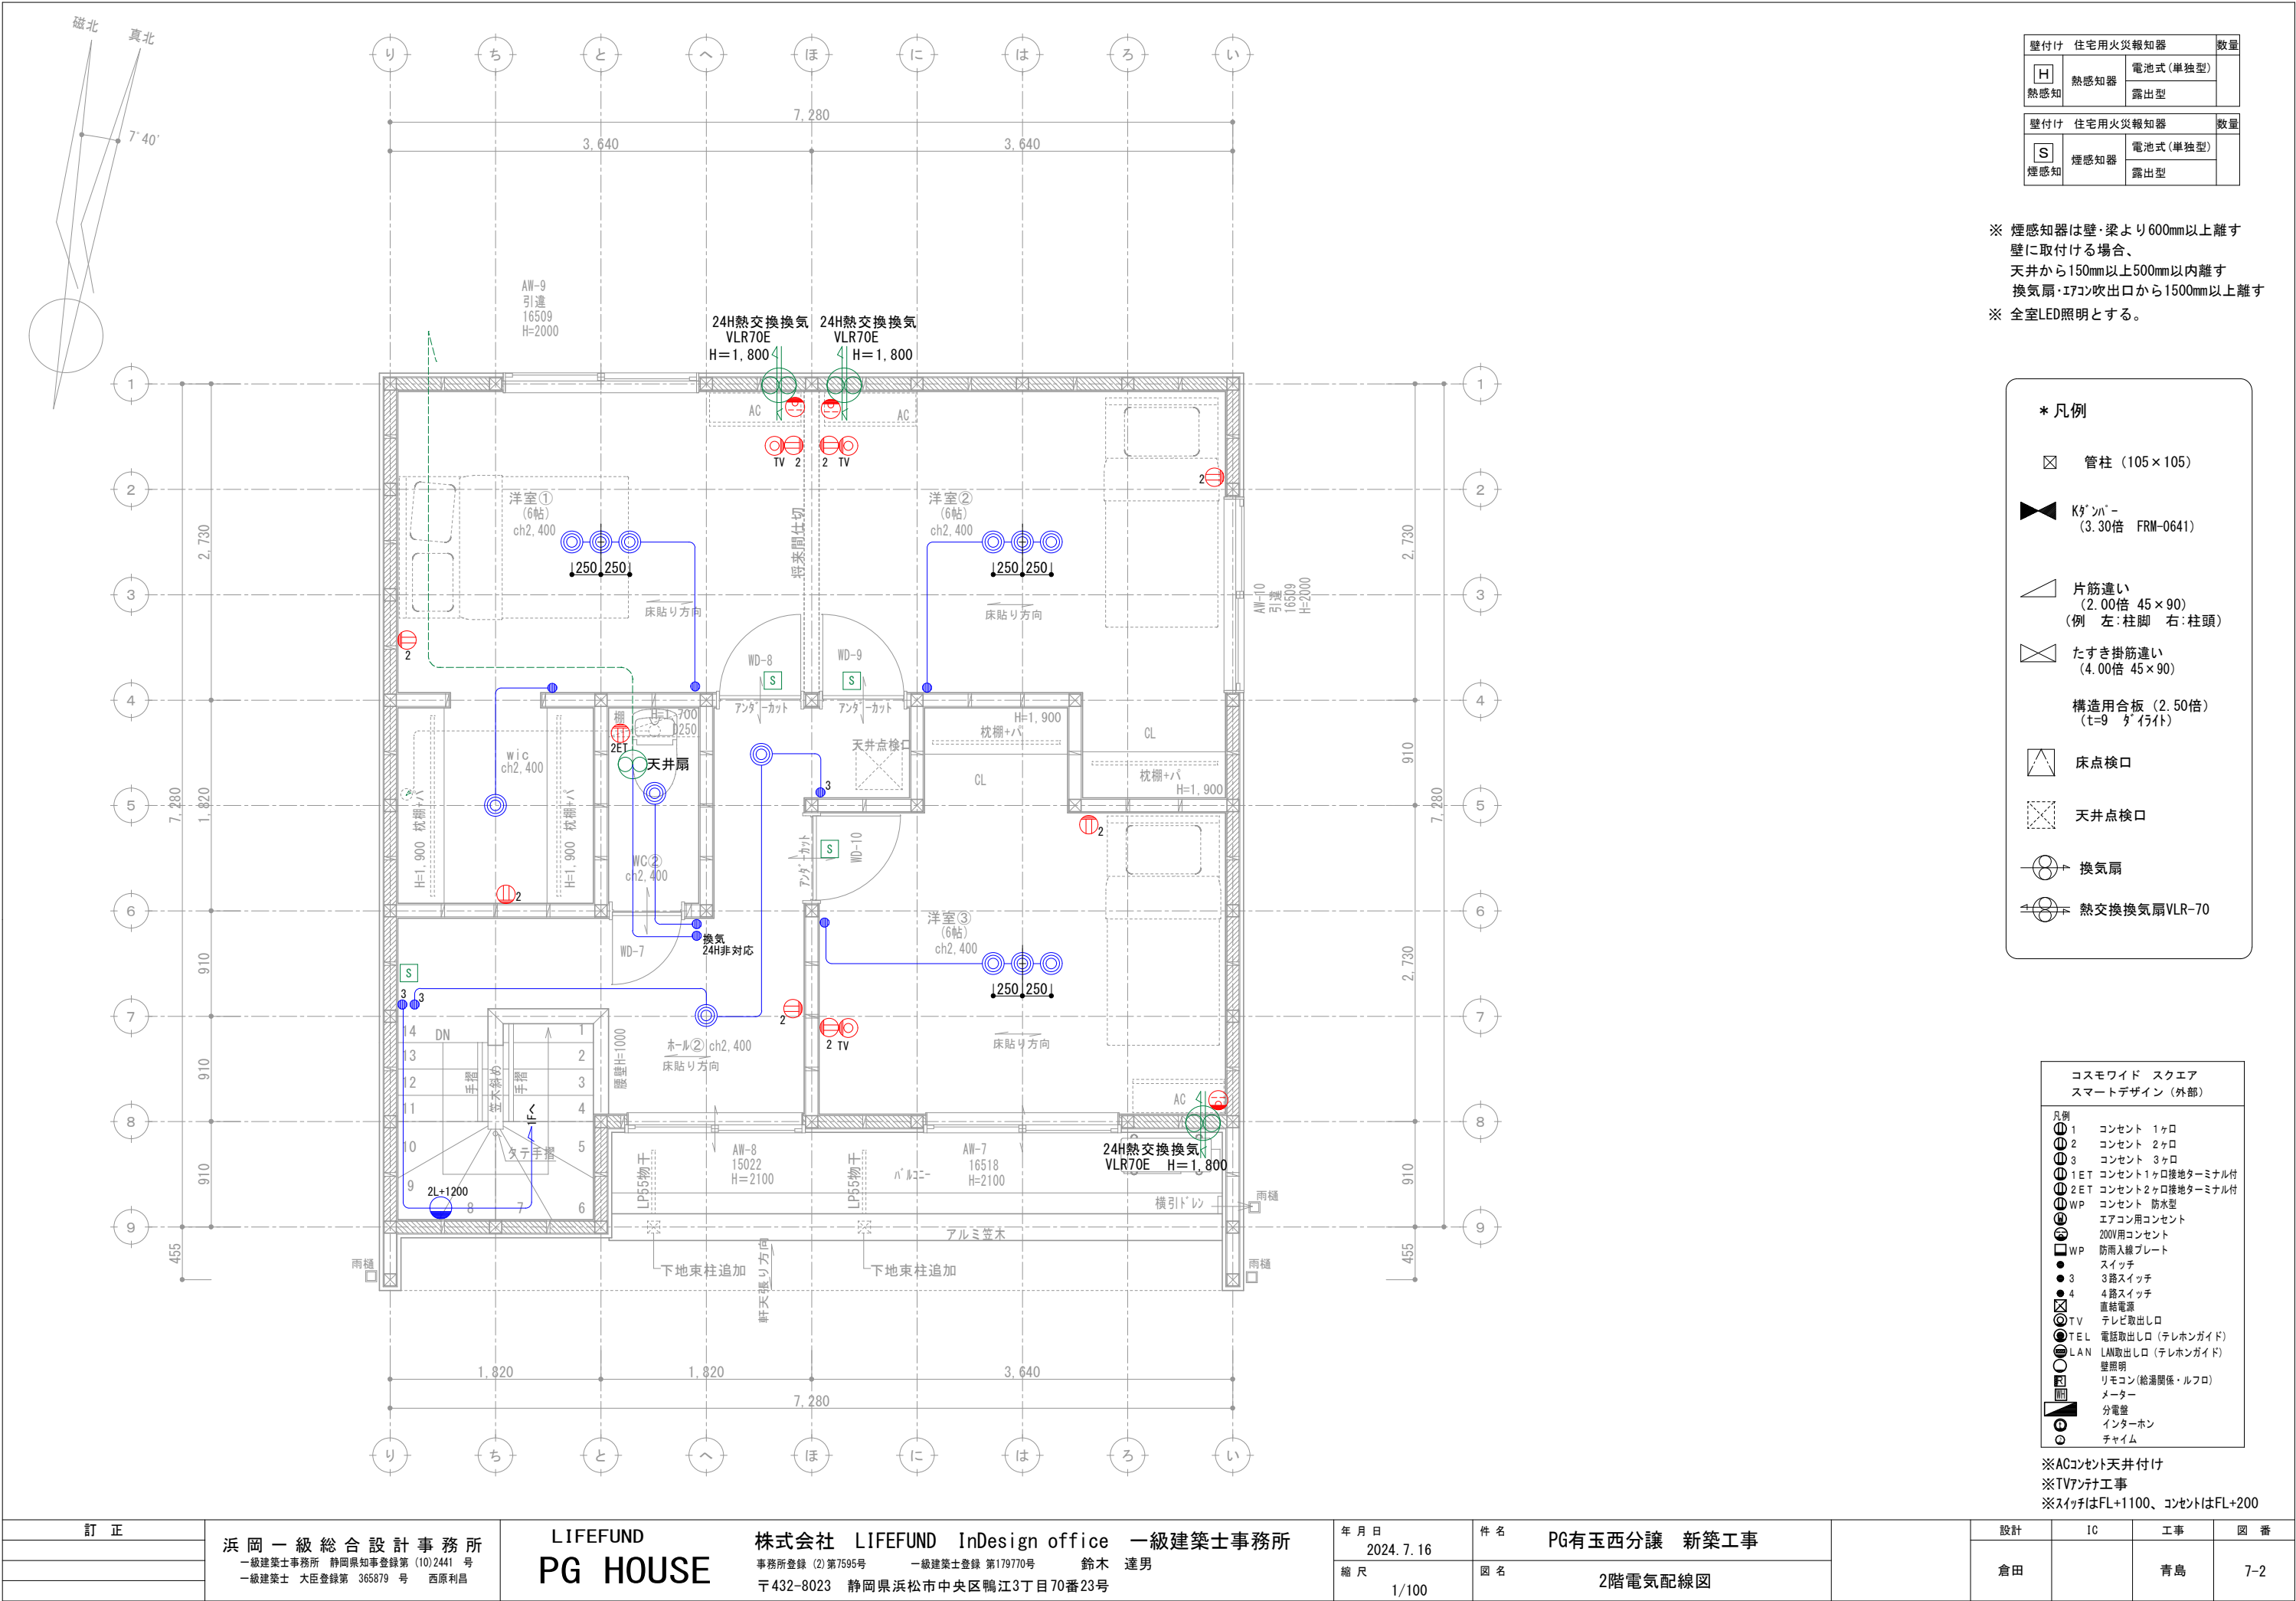

壁付け 住宅用火災報知器			数量
H 熱感知	熱感知器	電池式 (单独型)	
		露出型	
壁付け 住宅用火災報知器			数量
S 煙感知	煙感知器	電池式 (单独型)	
		露出型	

※ 煙感知器は壁・梁より600mm以上離す壁に取付ける場合、天井から150mm以上500mm以内離す換気扇・エアコン吹出口から1500mm以上離す

※ 全室LED照明とする。

*** 凡例**

管柱 (105×105)

Kダクト (3.30倍 FRM-0641)

片筋違い (2.00倍 45×90)
(例 左:柱脚 右:柱頭)

たすき掛筋違い (4.00倍 45×90)

構造用合板 (2.50倍)
(t=9 タイト)

床点検口


天井点検口

換気扇


熱交換換気扇 VLR-70

コスモワイド スクエア スマートデザイン (外部)	
凡例	
1	コンセント 1ヶロ
2	コンセント 2ヶロ
3	コンセント 3ヶロ
1ET	コンセント1ヶロ接地ターミナル付
2ET	コンセント2ヶロ接地ターミナル付
WP	コンセント 防水型
⊕	エアコン用コンセント
⊕	200V用コンセント
WP	防雨入線プレート
●	スイッチ
●	3路スイッチ
●	4路スイッチ
⊗	直結電源
TV	テレビ取出口
TEL	電話取出口 (テレホンガイド)
LAN	LAN取出口 (テレホンガイド)
壁照明	壁照明
リモコン	リモコン (給湯関係・ルフロ)
メーター	メーター
分電盤	分電盤
インターホン	インターホン
チャイム	チャイム

※ACコンセント天井付け
※TVアンテナ工事
※スイッチはFL+1100、コンセントはFL+200

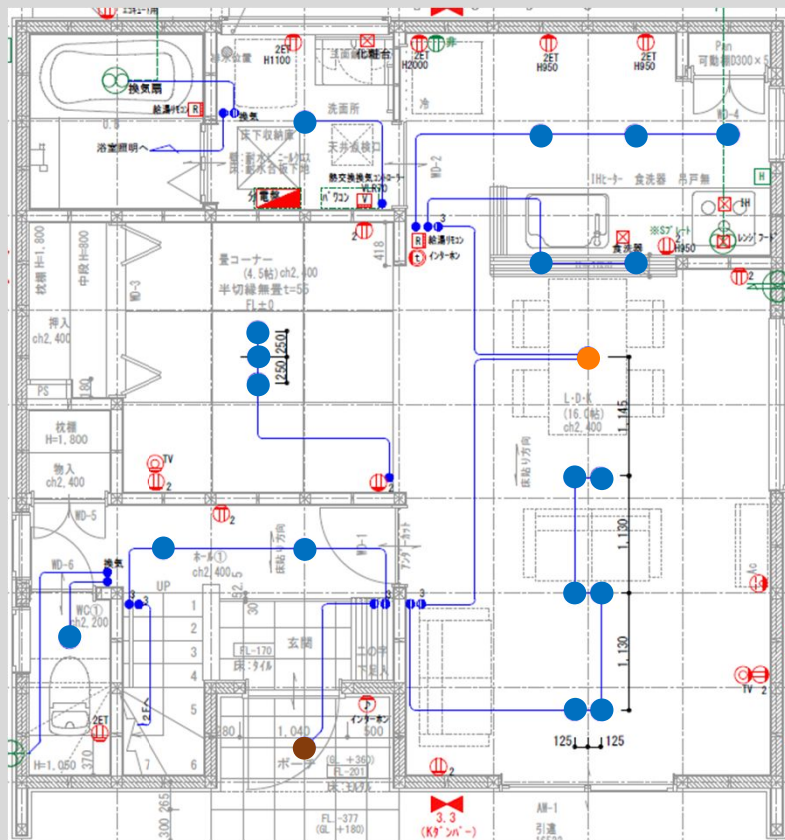

1 階

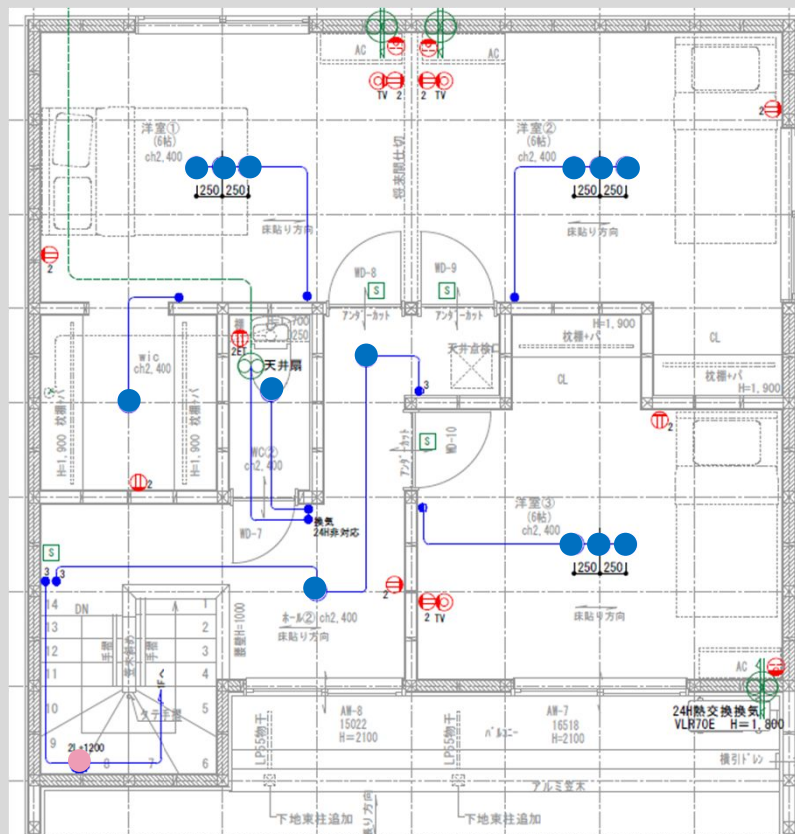

2 階

内部：コスモワイド スクエア(Panasonic)



ドアホン：VL-SZ30KL
(Panasonic)



外部：スマートデザインシリーズ (Panasonic)

表情豊かな住まいをつくり出すスマートデザインシリーズ。



ポーチ灯

● × 1

DDL-4496YW



基本照明ダウンライト

● × 31

DDL6102AW



ダイニングペンダント灯

● × 1

DPN41973



階段灯

● × 1

DBK41544Y



2024.07.16