

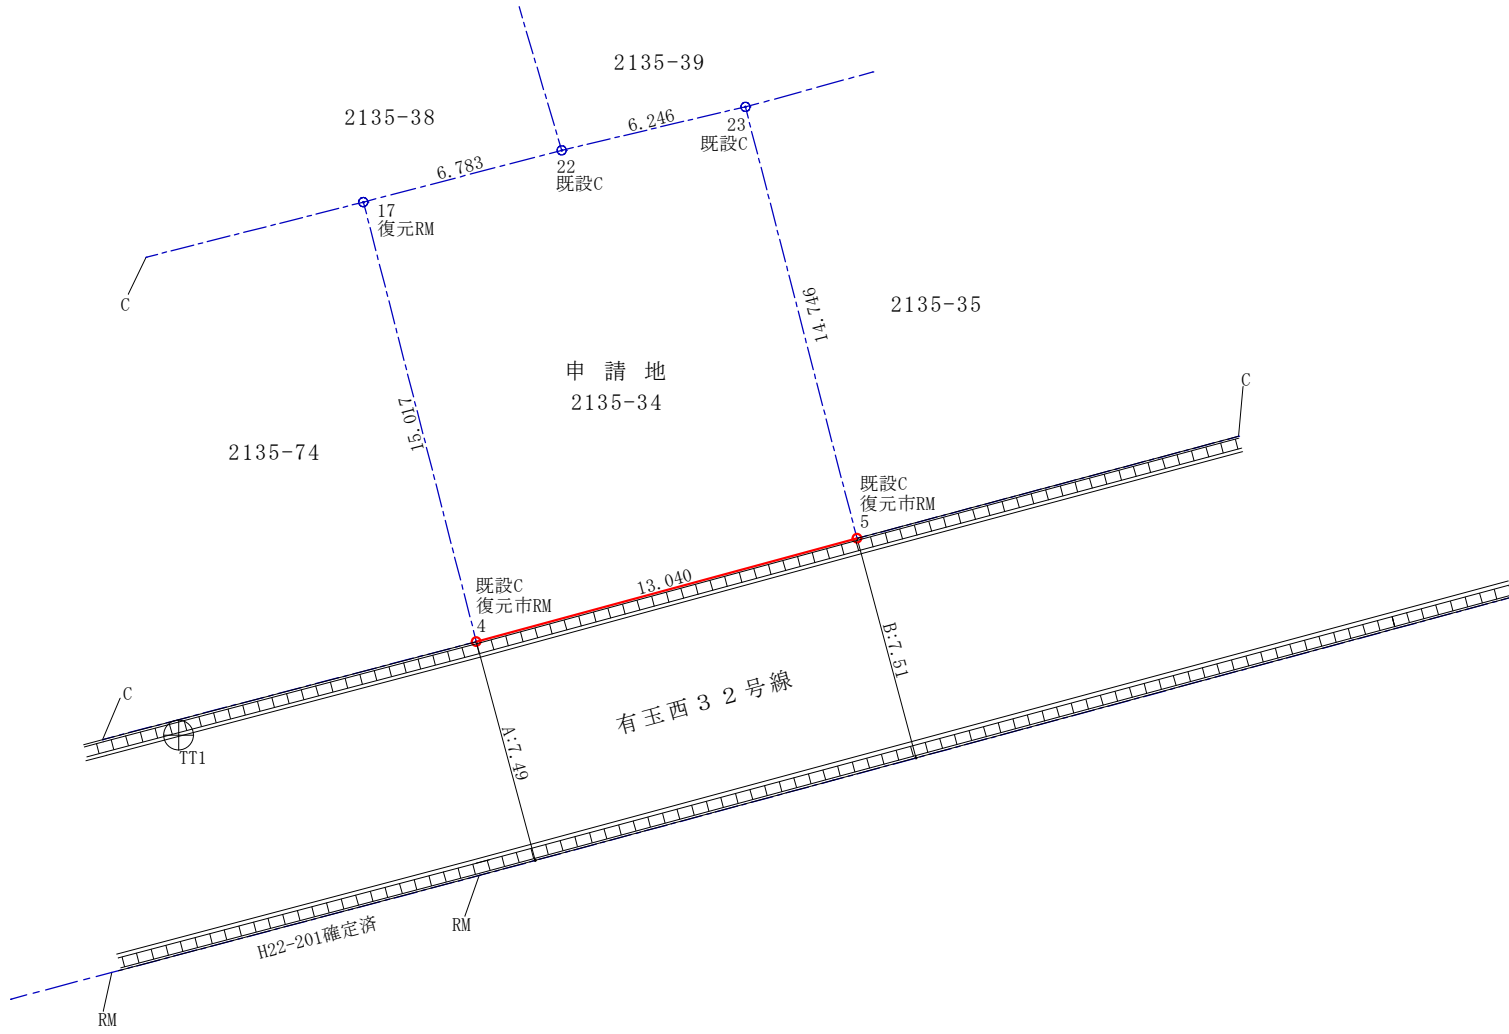


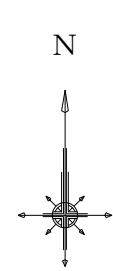

2135番34
登記簿面積
191.39㎡
実測面積
194.45㎡
面積誤差範囲
精度区分なし(甲三): ±2.41㎡
(188.98㎡～193.80㎡)

平面図 S = 1 : 2 5 0

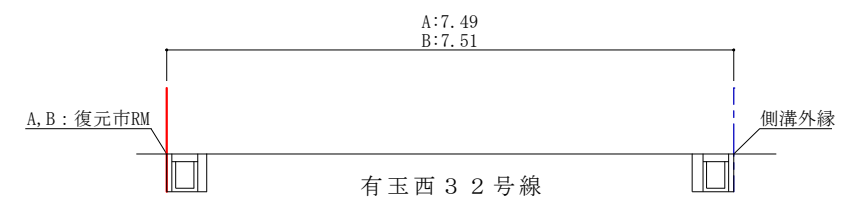

断面図 S = 1 : 1 0 0



求積表

地 番	2135-34			
N0	Xn	Yn	Yn+1-Yn-1	Xn・(Yn+1-Yn-1)
17	-138043.243	-69916.603	2.818	-389005.858774
22	-138041.530	-69910.040	12.642	-1745121.022260
23	-138040.095	-69903.961	9.767	-1348237.607865
5	-138054.372	-69900.273	-8.897	1228269.747684
4	-138057.786	-69912.858	-16.330	2254483.645380
合 計				388.904165
合 計 面 積				194.4520825
地 積				194.45 ㎡

地 番	面 積
2135-34	194.45 ㎡

座標点	X	Y
TT1	-138060.883	-69922.709
1A088	-138050.753	-69870.070
10B33	-138160.058	-69865.500

凡 例

C : コンクリート杭
P : プラスチック杭
RM : 金属標
市RM : 浜松市支給金属標

R : 金属鋸
M : 刻み
TT : 基準点

土地家屋調査士 登録第1852号
藤 田 大 貴
浜松市中央区萩丘四丁目10番24号
TEL 053-488-4373