



加工承認書

2024年7月18日

拝啓 貴社益々ご繁栄のこととお慶び申し上げます。平素は、格別のご配慮をいただき厚くお礼申し上げます。
さて、この度貴社よりご依頼のありましたプレカット図面を送付致します。
つきましては、送付図面の内容確認及び加工のご承認を本紙にて、ご回答を頂きますようお願い申し上げます。

ハイビック(株) CADセンター

発注 (株)LIFEFUND 御中
担当者 ご担当者 様
物件名 PG有玉西町分譲住宅
FAX

浜松CAD室 担当:鈴木淳
携帯 070-3173-7584


浜松市浜名区宮口2461 TEL 053-582-3711
FAX 053-582-3701

プレカット販売店:浜松店 営業担当:大久保

■伏図確認進捗状況

第1回送信日 / 枚送信	1 便 目	上 棟 日
お世話になっております。 プレカット伏図を作成致しました。 御確認宜しくお願い致します。	/	
第2回送信日 / 枚送信	1 便 目	上 棟 日
第3回送信日 / 枚送信	1 便 目	上 棟 日
第4回送信日 / 枚送信	1 便 目	上 棟 日
第5回送信日 / 枚送信	1 便 目	上 棟 日
第6回送信日 / 枚送信	1 便 目	上 棟 日
第7回送信日 / 枚送信	1 便 目	上 棟 日

■矩計寸法確認

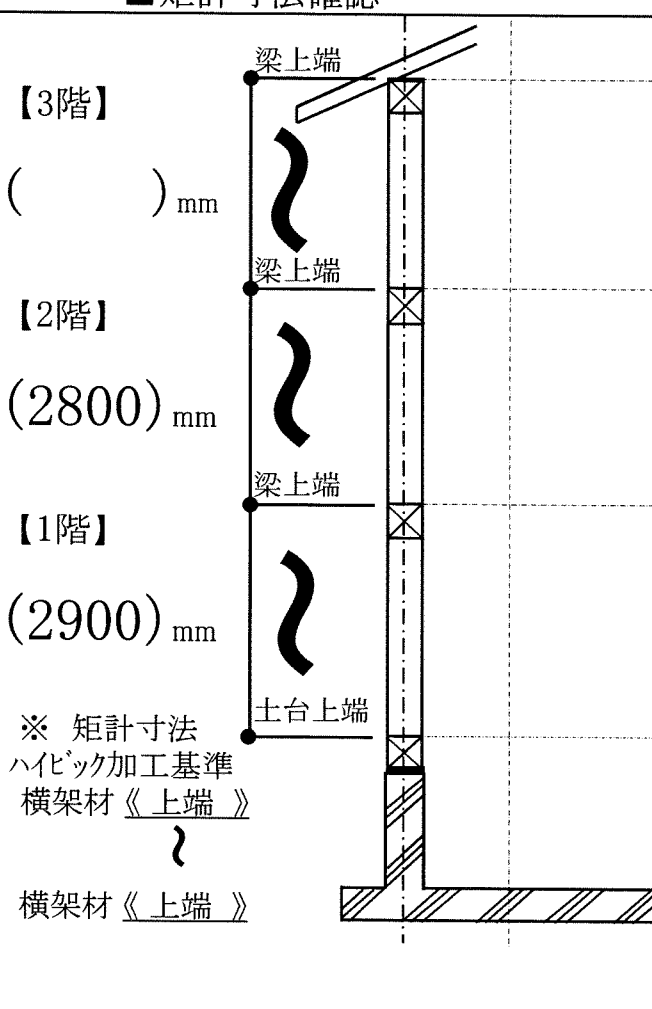

承認期限

月 日

※承認期限までにご承認お願い致します。

※ 月 日送付の図面一式にて、加工承認する。

- ・ご承認を頂いた後は工場の生産工程に合わせ、随時加工に入らせて頂きます。
- ・ご承認後の変更は内容によって有料となる場合がありますのでご了承願います。
- ・化粧材について、松系の材料にはブルーステインの混入の可能性が御座います。

加工承認日 (※承認期限までにご承認お願い致します。)

※ 年 月 日 ※承認者名

様


※

印

※部分は必ずご記入下さい(電子印はご遠慮願います様ご協力下さい)

2017.6.12改訂

るぬりちとへほにほろいZ

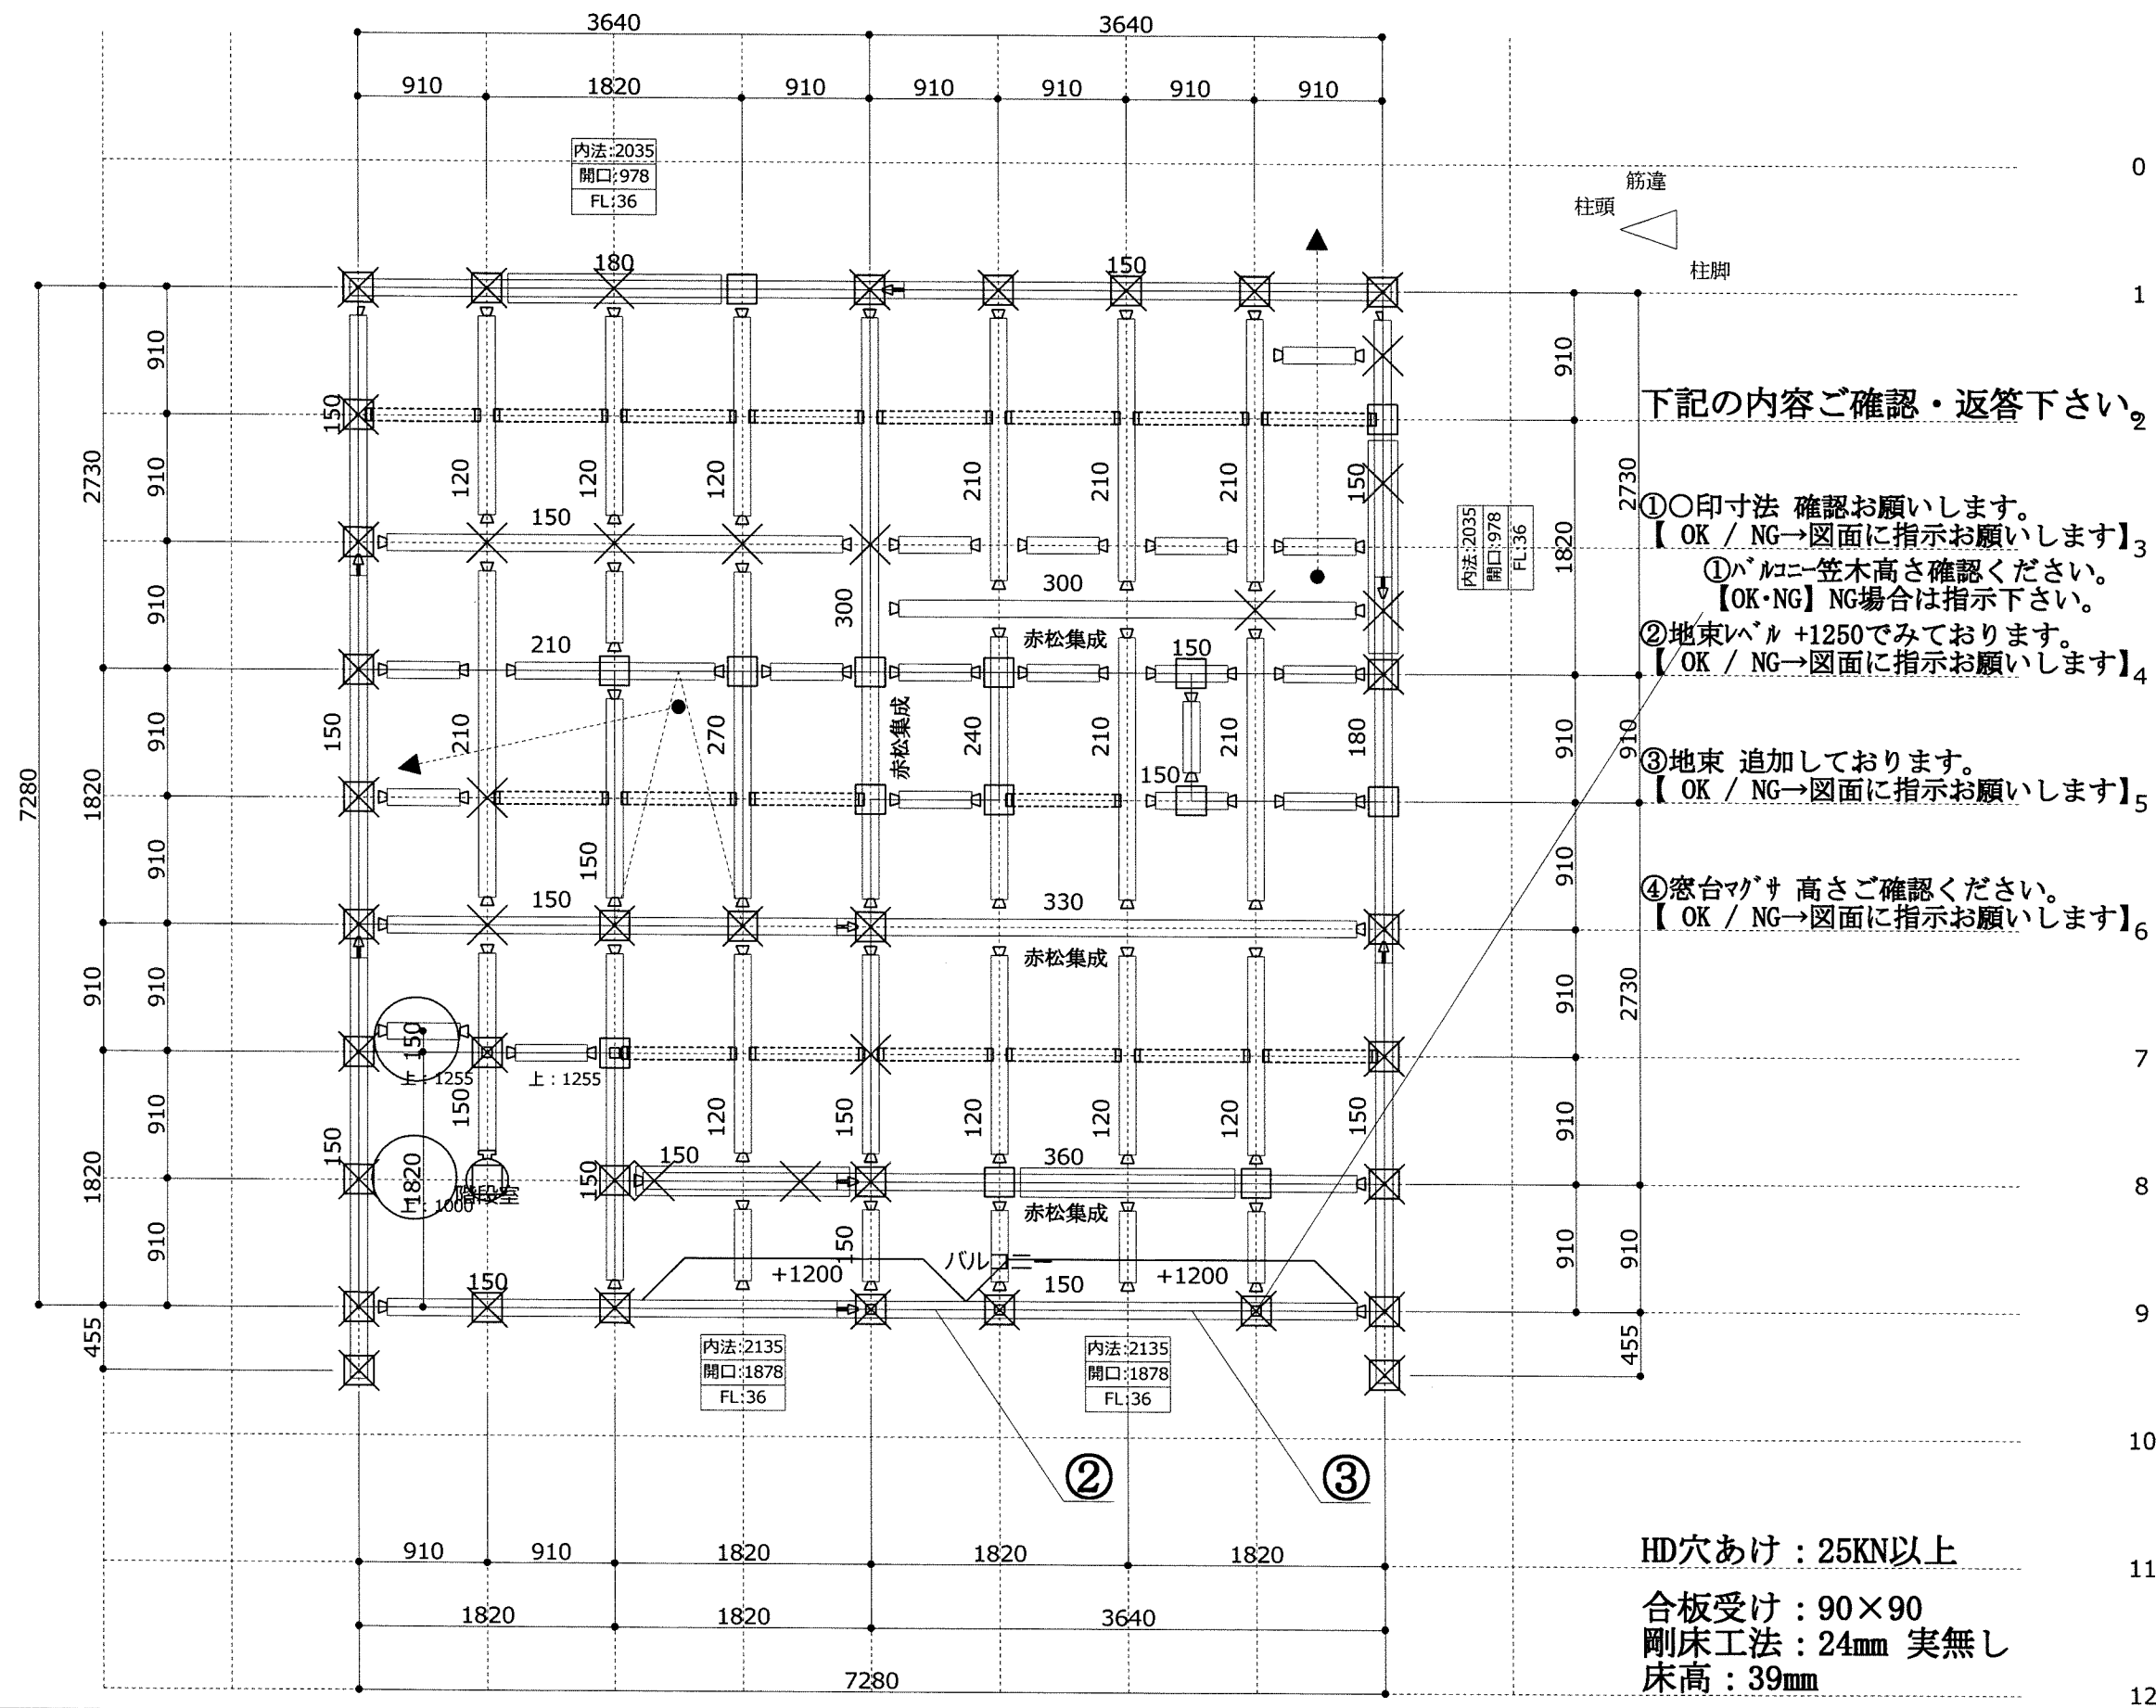

凡 例			
材 種	樹種・等級・材寸		
梁	米松 乾燥特等 105×105		
通し柱	未指定 未指定		
管 柱	杉集成 構造用 105		
小屋束	檜 支給材 90		
火打梁	鉄アングル 乾燥特等 90×90		
登 梁	米松 乾燥特等 105×105		
化粧管柱	床 柱	階段柱	ポーチ柱
地 束	吊 束		
間 柱			
根 太			
蟻			
寄 蟻			
逆 蟻			
大入れ			
大引き			
兜			
茶 臼			
鎌 継			
蟻 継			
桁差ホゾ			
胴差ホゾ			

HD穴あけ：25KN以上

合板受け：90×90
剛床工法：24mm 実無し
床高：39mm

～ 見積用 伏図 ～

■検印

■モデル	910	mm
■桁 高	2800	mm
■屋根勾配	1.0	寸

■工事名称
株LIFEFUND様 PG有玉西町分譲住宅様

■印刷日時
2024年 7月24日

■縮尺
1 / 50


■図面名称
2階床伏図

■物件番号
HHS0385

TEL :

FAX :

るぬりちとへほにはろいZ

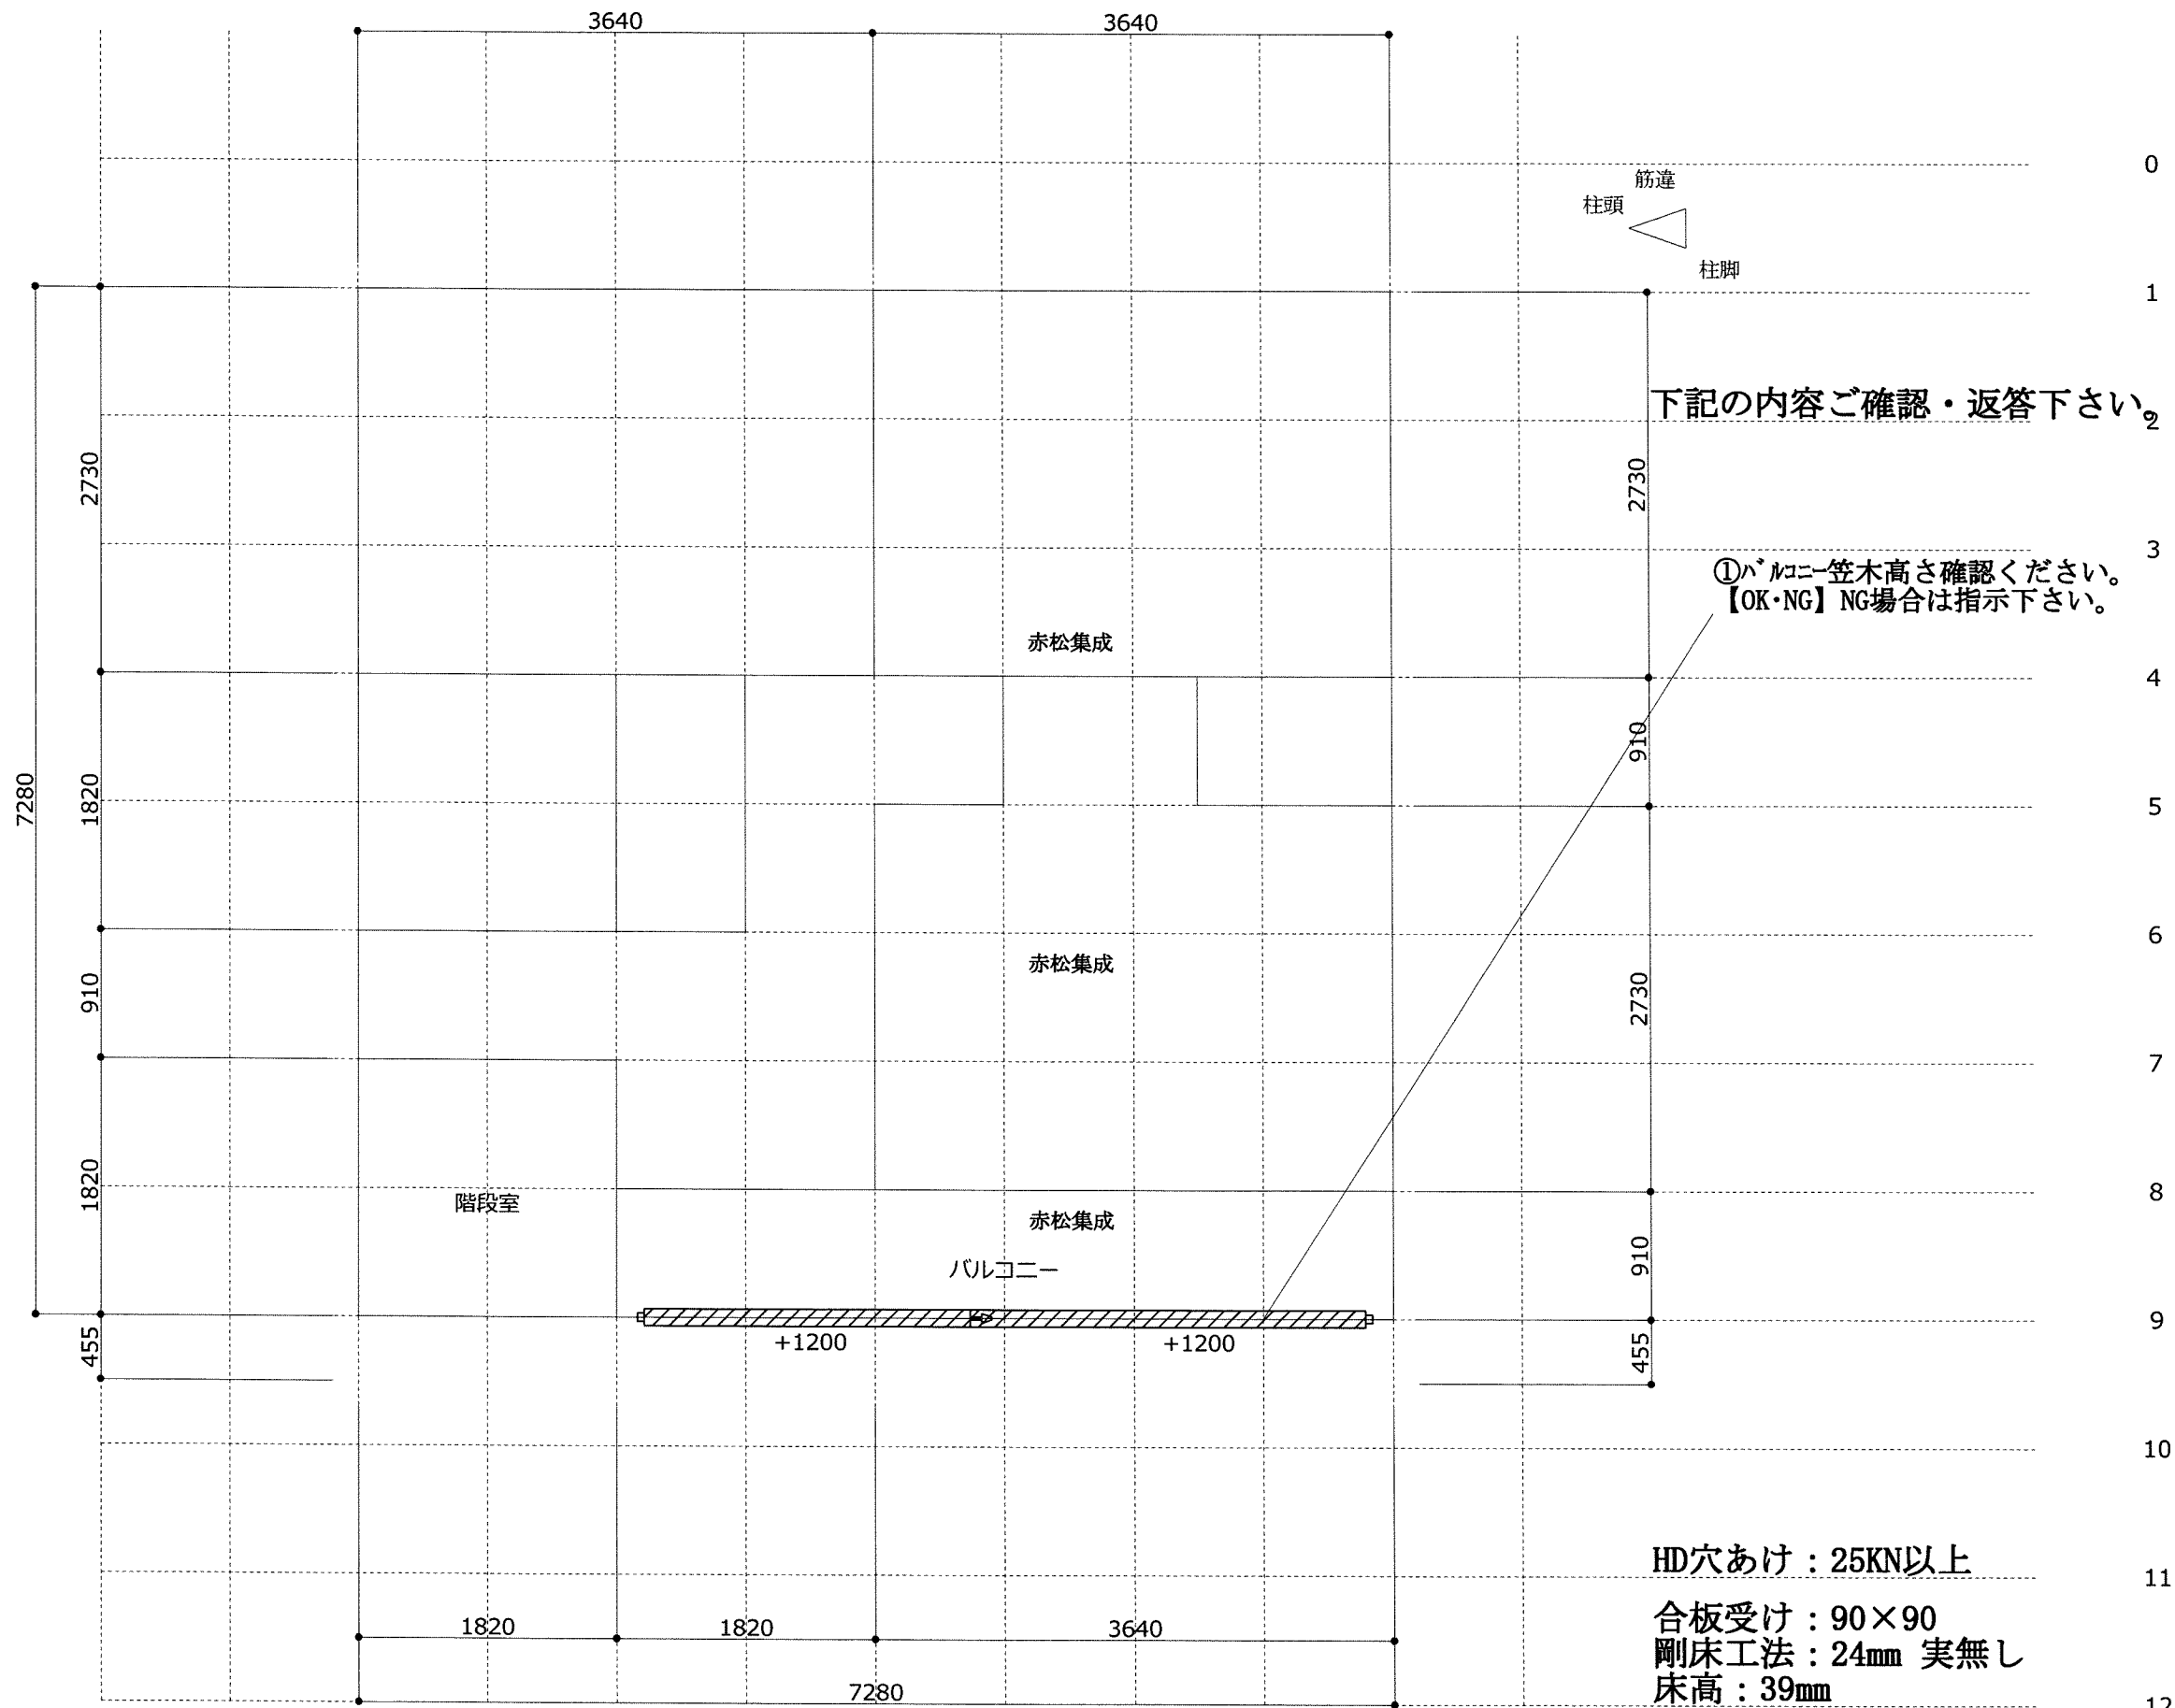

下記の内容ご確認・返答下さい

①バルコニー笠木高さ確認ください。
【OK・NG】NG場合は指示下さい。

HD穴あけ：25KN以上

合板受け：90×90
剛床工法：24mm 実無し
床高：39mm

凡 例

材 種	樹種・等級・材寸		
梁	米松 乾燥特等 105×105		
通し柱	未指定 未指定		
管 柱	杉集成 構造用 105		
小屋束	檜 支給材 90		
火打梁	鉄アングル 乾燥特等 90×90		
登 梁	米松 乾燥特等 105×105		
化粧管柱	化粧管柱	床 柱	
階 段 柱	階段柱	ポーチ柱	
地 束	地束	吊 束	
間 柱			
根 太			
蟻			
寄 蟻			
逆 蟻			
大入れ			
大引き			
兜			
茶 臼			
鎌 継			
蟻 継			
桁差ホゾ			
胴差ホゾ			

～ 見積用 伏図 ～

■検印

■モジュール	910	mm
■桁 高	2800	mm
■屋根勾配	1.0	寸

■工事名称
株LIFEFUND様 PG有玉西町分譲住宅様

■印刷日時
2024年 7月24日

■縮尺
1 / 50



■図面名称
2階床伏図 (サブレイヤ1)

■物件番号
HHS0385

TEL :

FAX :

るぬりちとへほにはろいZ

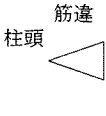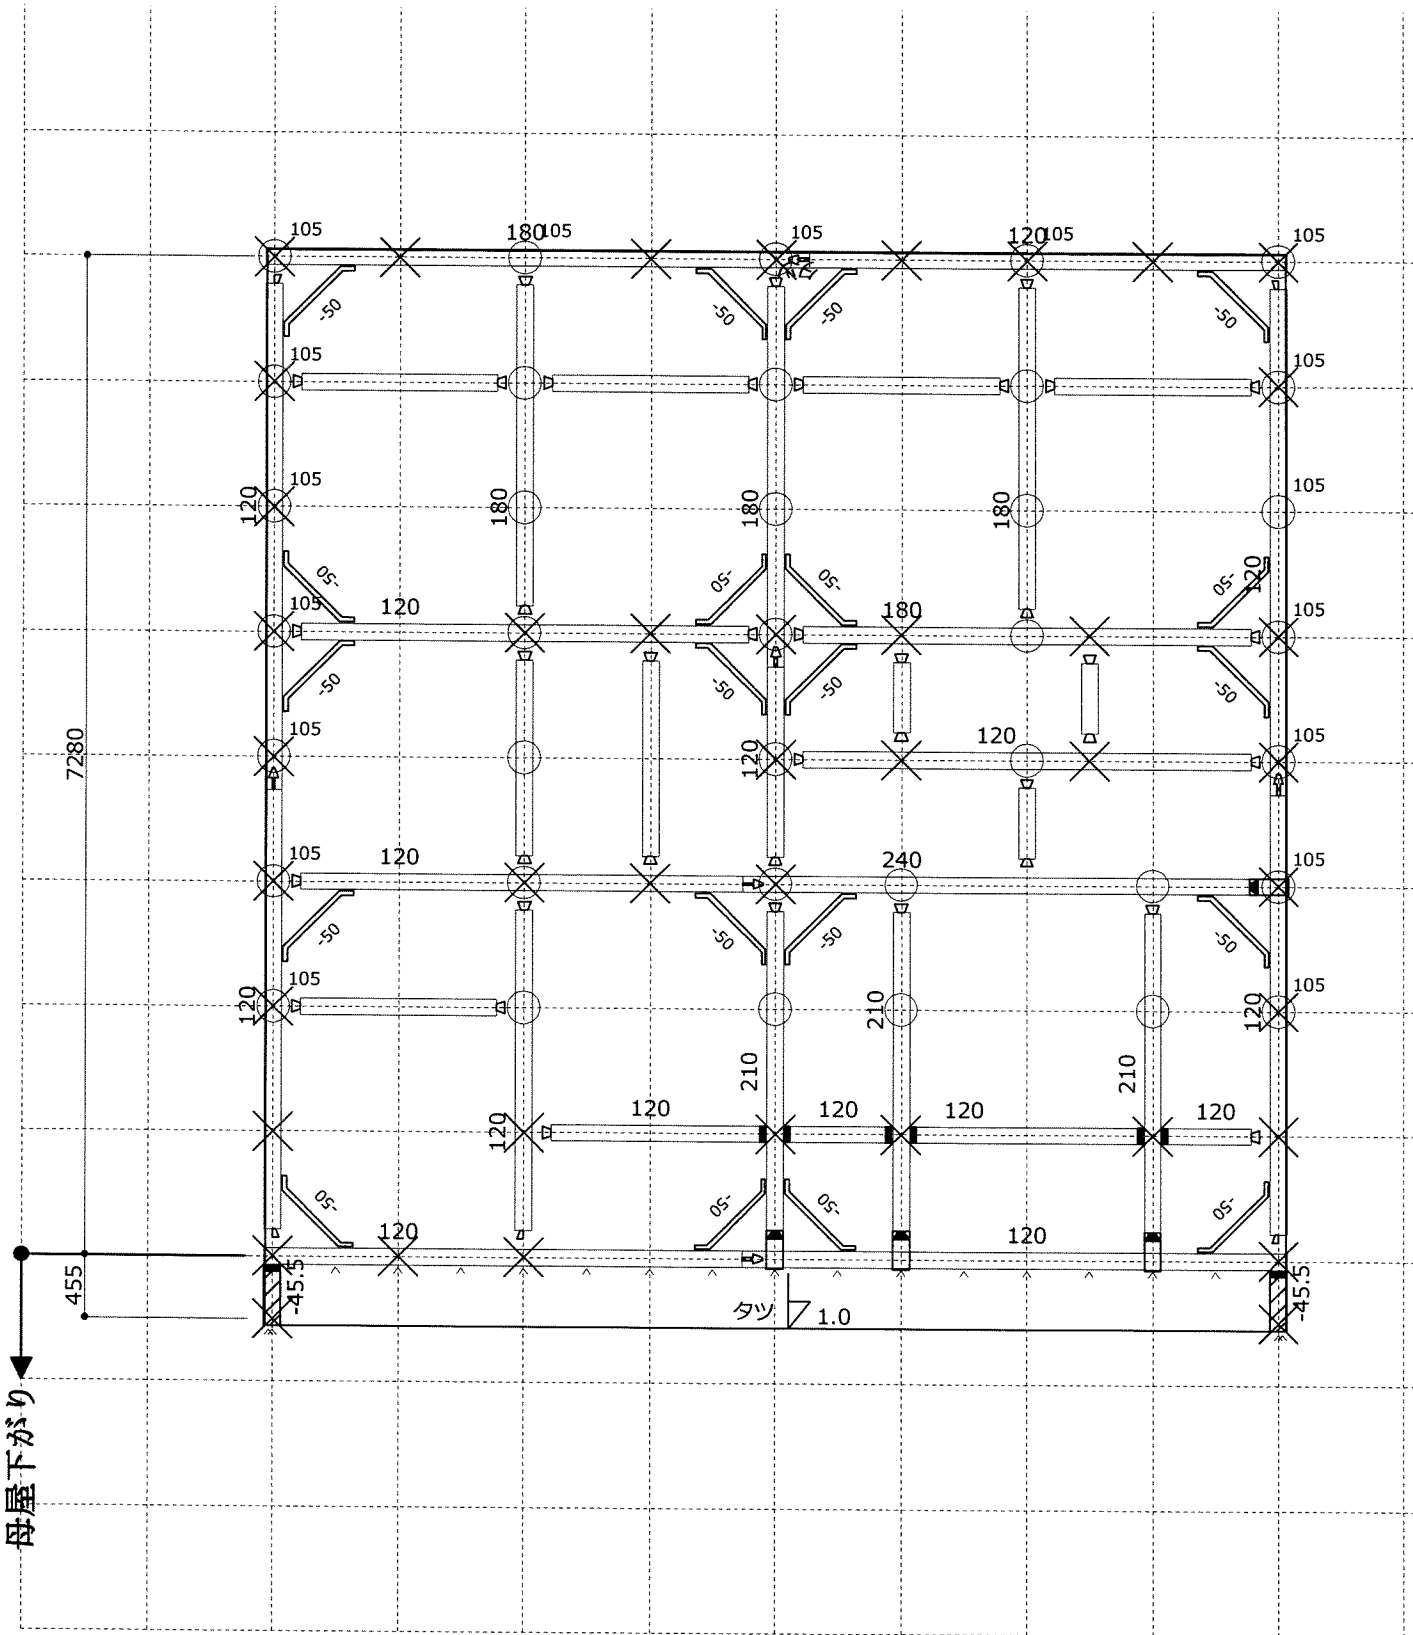

下記の内容ご確認・返答下さい。

金物火打：ビス止め

HD穴あけ：25KN以上

凡 例			
材 種		樹種・等級・材寸	
梁		米松 乾燥特等 105×105	
○ 小屋束		檜 支給材 90	
火打梁		鉄アングル 乾燥特等 90×90	
⊠ 登 梁		米松 乾燥特等 105×105	
⊘	化粧管柱	⊙	床 柱
⊖	階 段 柱	⊞	ポーチ柱
□	地 束	▣	吊 束
⎓		間 柱	
-----		根 太	
⎓		蟻	
⎓		寄 蟻	
⎓		逆 蟻	
⎓		大入れ	
⎓		大引き	
⎓		兜	
⎓		茶 臼	
⎓		鎌 継	
⎓		蟻 継	
⎓		桁差ホゾ	
⎓		胴差ホゾ	

母屋下がり

7280

455

52.5

910

105

105x105

+728

+637

+546

+455

+364

+273

+182

+91

タツ 1.0

野地カット寸法

軒先：水下出寸法（垂木先端）より +90mm（水平寸法）

軒先：水上出寸法（垂木先端）より +80 mm（水平寸法）


妻側：妻の出寸法（母屋先端）より +80mm

①軒妻の出寸法 確認をお願いします。
 (軒は桁芯より垂木先端) 3
 (妻は桁芯より母屋先端)
【 OK / NG→図面に指示をお願いします】

野地カット寸法


軒先：水下出寸法（垂木先端）より	+90mm（水平寸法）
軒先：水上出寸法（垂木先端）より	+80 mm（水平寸法）
妻側：妻の出寸法（母屋先端）より	+80mm

～ 見積用 伏図 ～ TEL : FAX :	■ 検印				■ モジュール	910	mm	■ 工事名称 (株) LIFEFUND様 PG有玉西町分譲住宅様	■ 図面名称 2 階母屋伏図
					■ 桁 高	2800	mm		
					■ 屋根勾配	1.0	寸		
								■ 印刷日時	2024年 7月24日

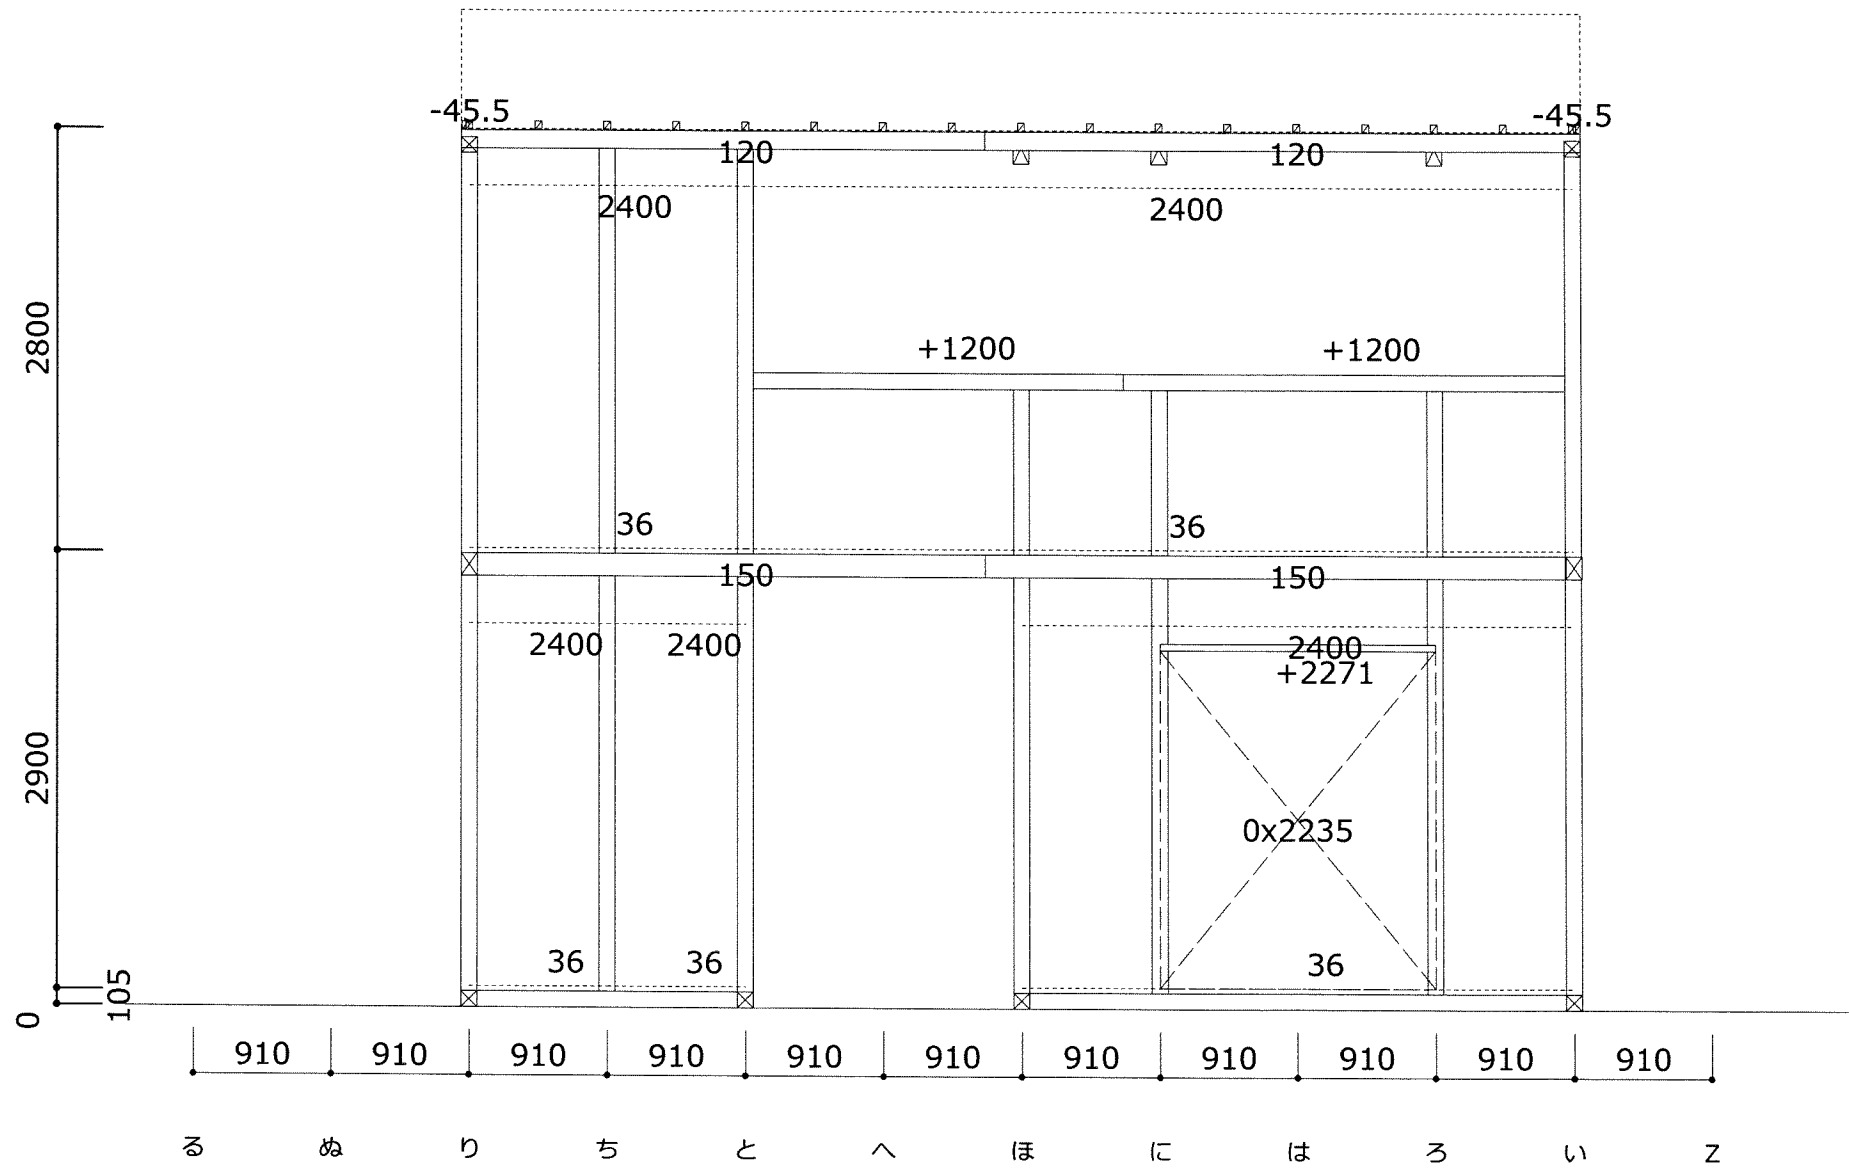


9通り 南面

～ 見積用 伏図 ～				■検印		■モジュール 910 mm		■工事名称 (株)LIFEFUND様 PG有玉西町分譲住宅様		■図面名称 軸組断面図	
TEL :				FAX :		■桁 高 mm		■印刷日時 2024年 7月24日		■縮尺 1 / 50	
						■屋根勾配 寸				■物件番号 HHS0385	

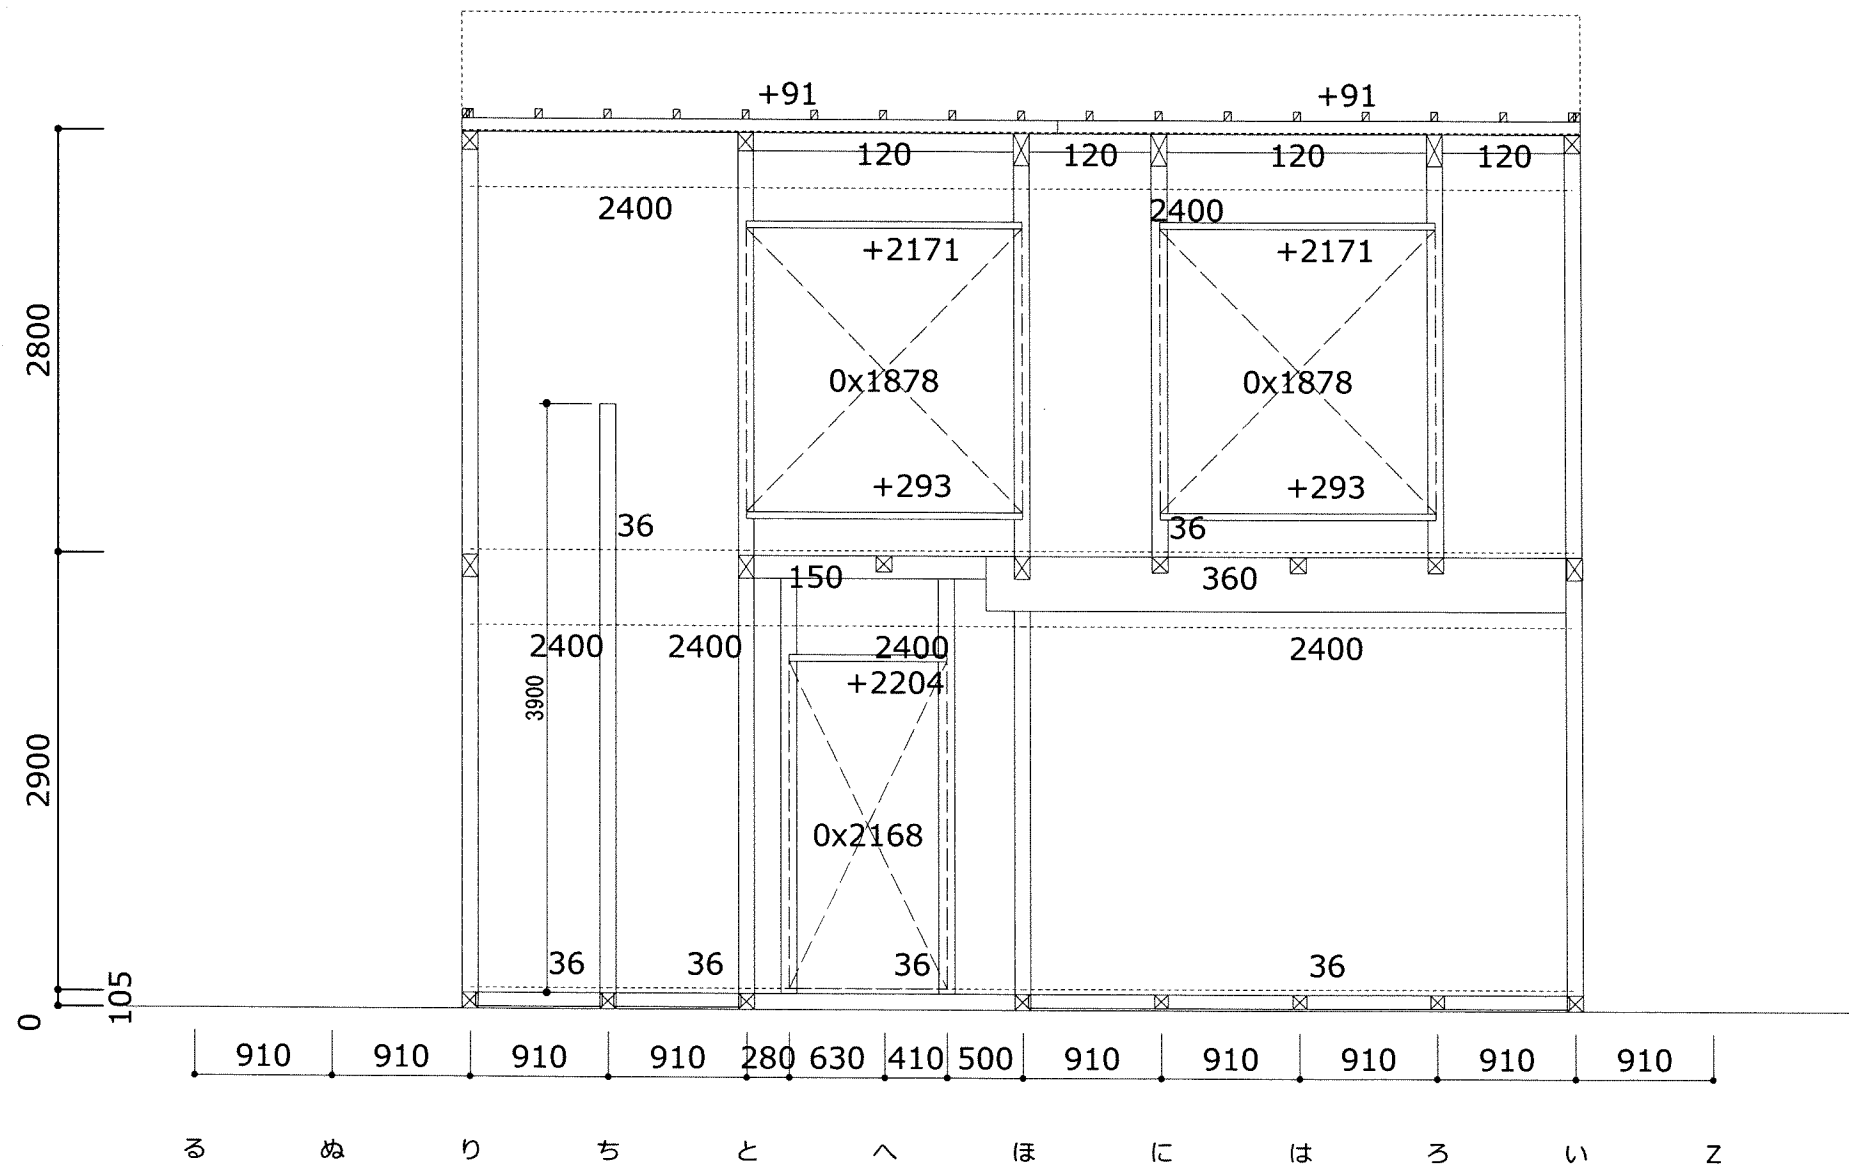


8通り 南面

～ 見積用 伏図 ～				■検印		■モジュール 910 mm		■工事名称 株式会社LIFEFUND様 PG有玉西町分譲住宅様		■図面名称 軸組断面図	
TEL :				FAX :		■桁 高 mm		■印刷日時 2024年 7月24日		■縮尺 1 / 50	
						■屋根勾配 寸				■物件番号 HHS0385	

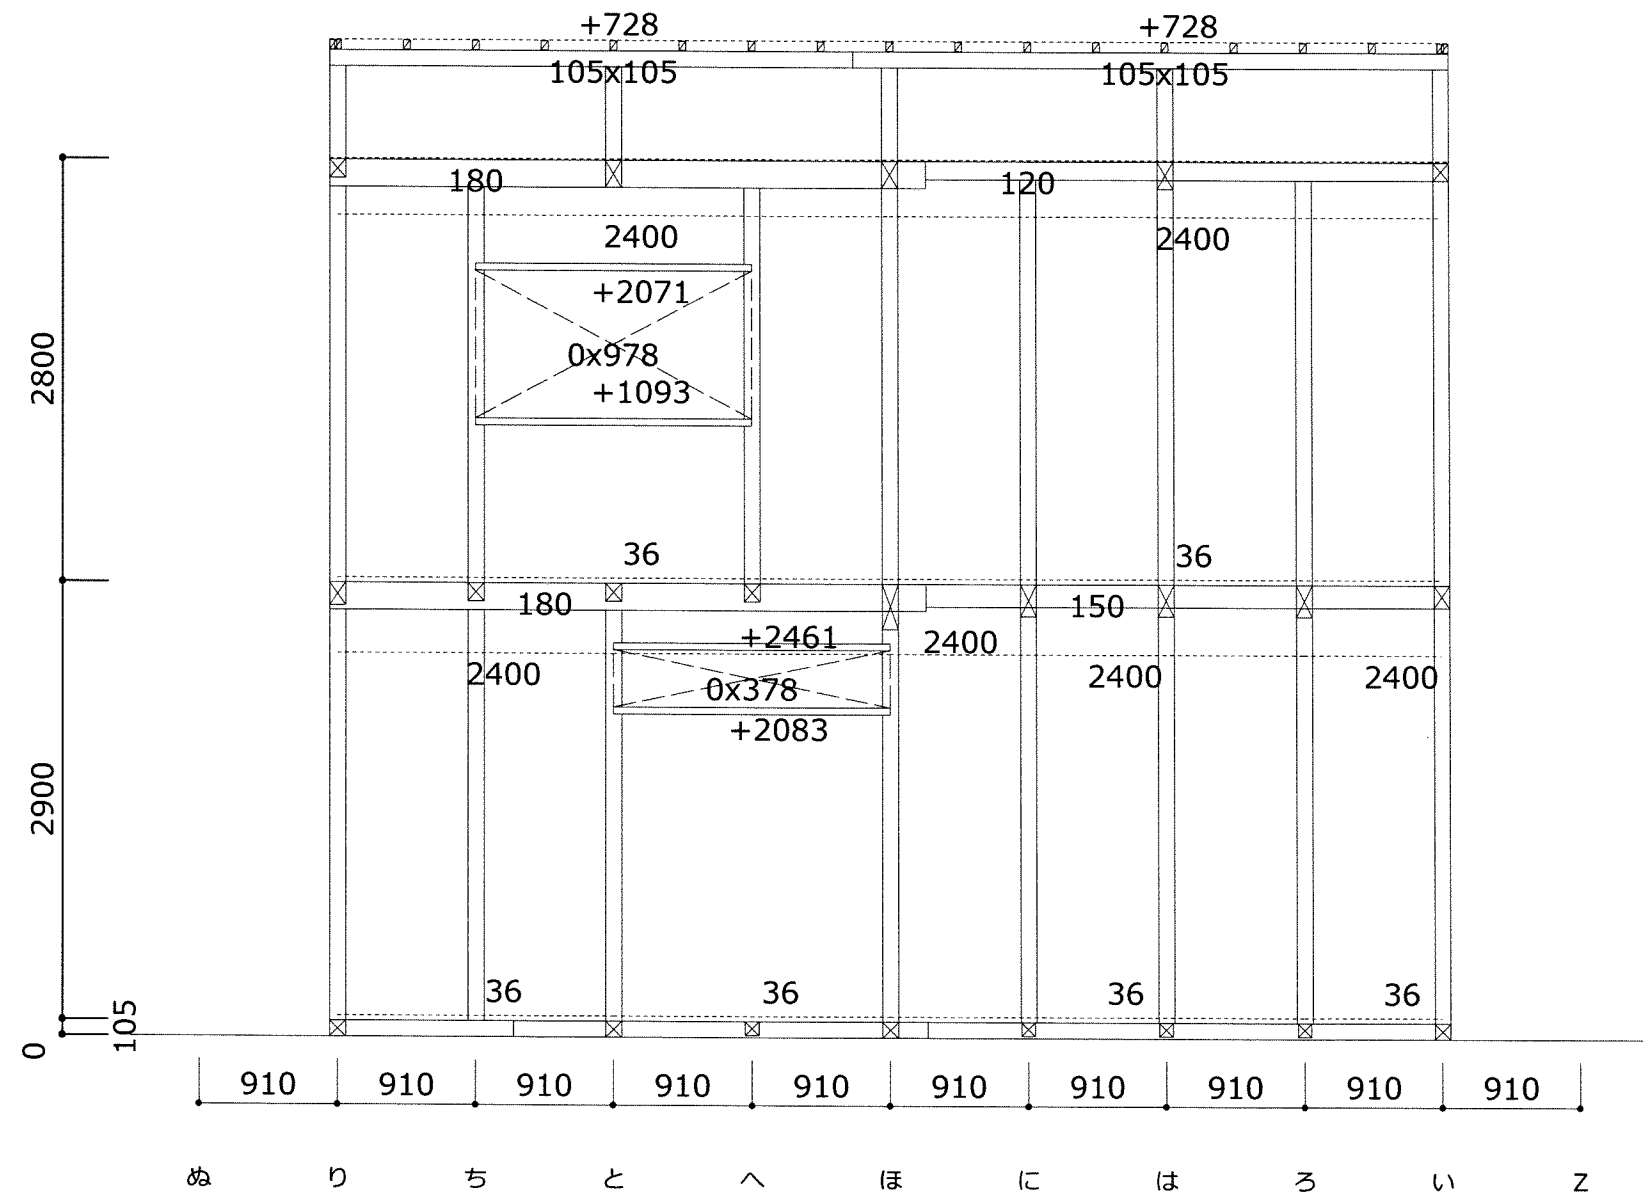


1通り 南面

～ 見積用 伏図 ～			■検印			■モジュール		910	mm	■工事名称		■図面名称			
						■桁 高			mm	(株)LIFEFUND様 PG有玉西町分譲住宅様		軸組断面図			
						■屋根勾配			寸	■印刷日時		■縮尺		■物件番号	
										2024年 7月24日		1 / 50		HHS0385	
TEL :			FAX :												

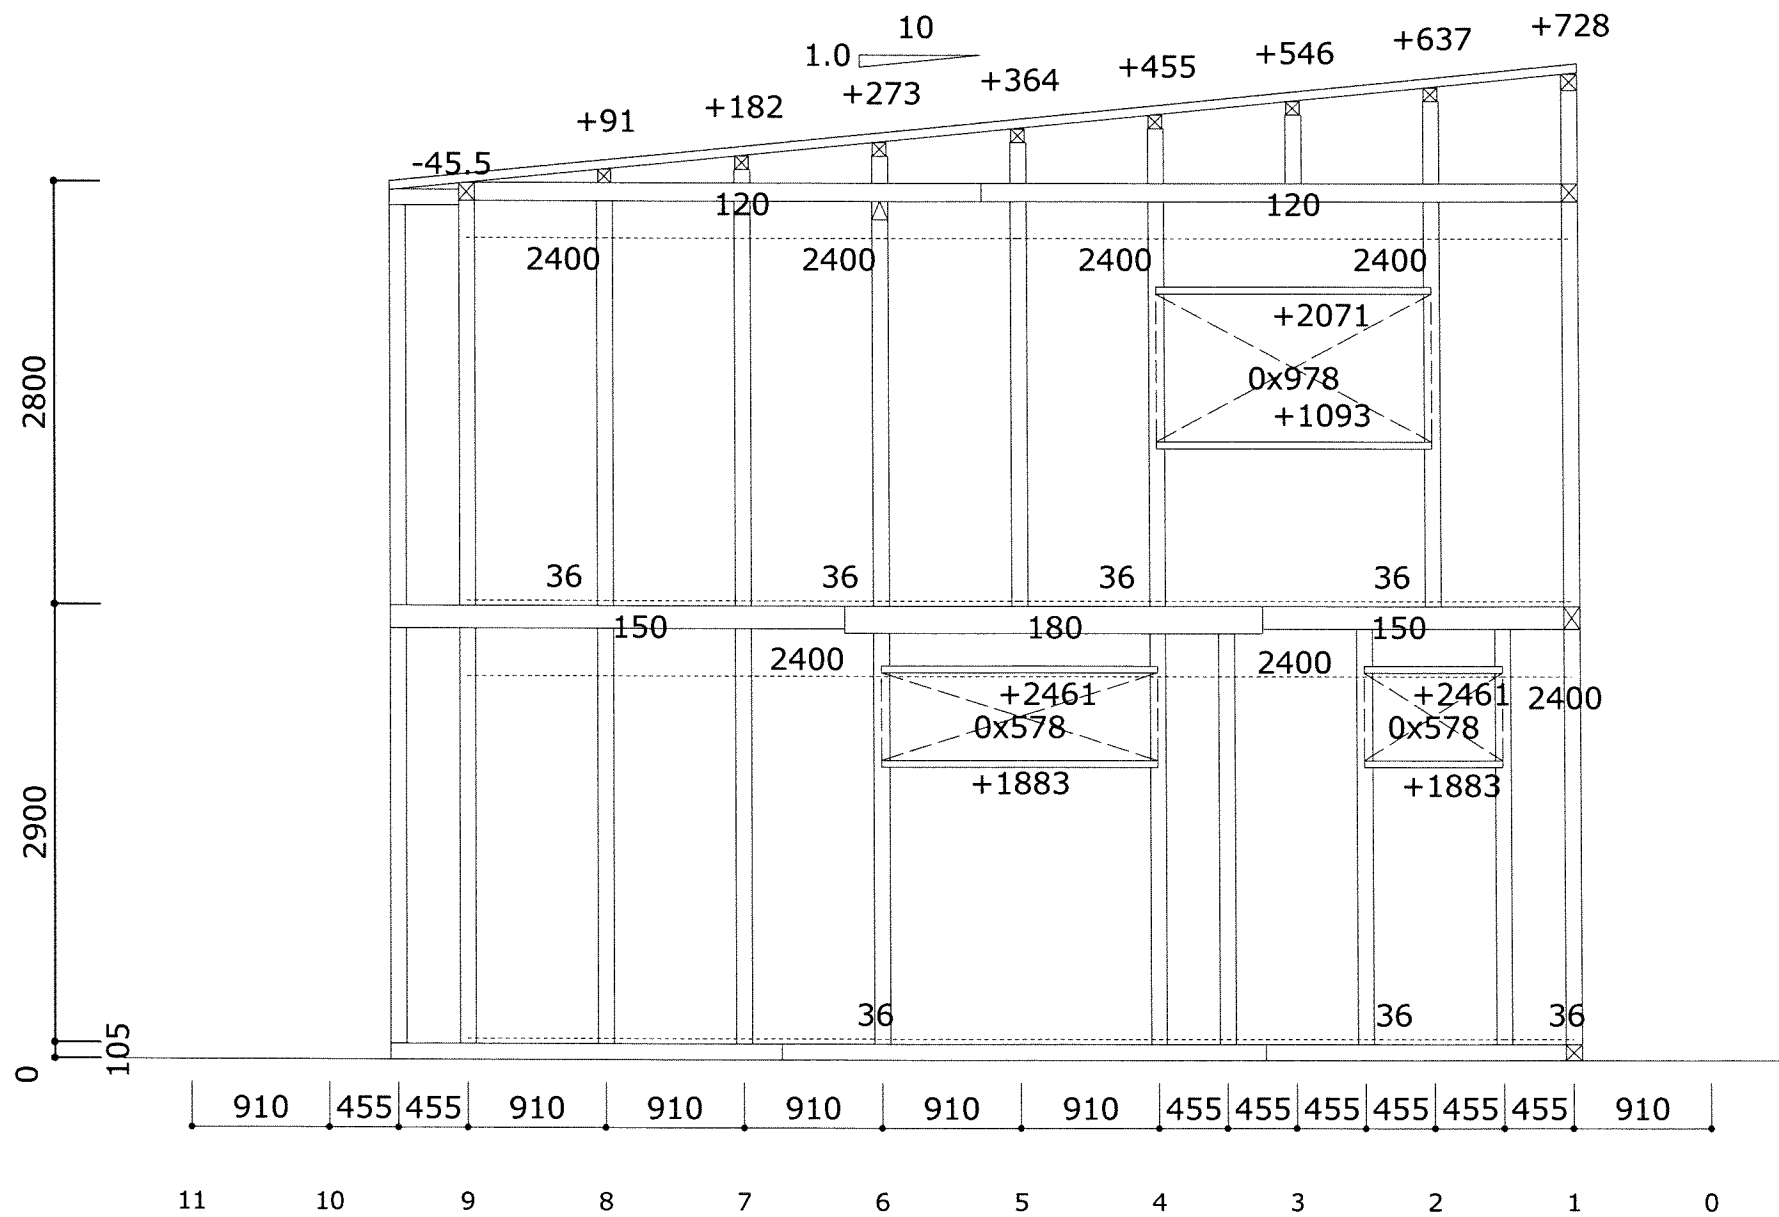

い通り 東面

～ 見積用 伏図 ～				■ 検印			■ モジュール 910 mm		■ 工事名称 (株)LIFEFUND様 PG有玉西町分譲住宅様		■ 図面名称 軸組断面図	
TEL :		FAX :					■ 桁 高 mm					
							■ 印刷日時		■ 縮尺		■ 物件番号 HHS0385	
							2024年 7月24日		1 / 50			
							■ 屋根勾配 寸					

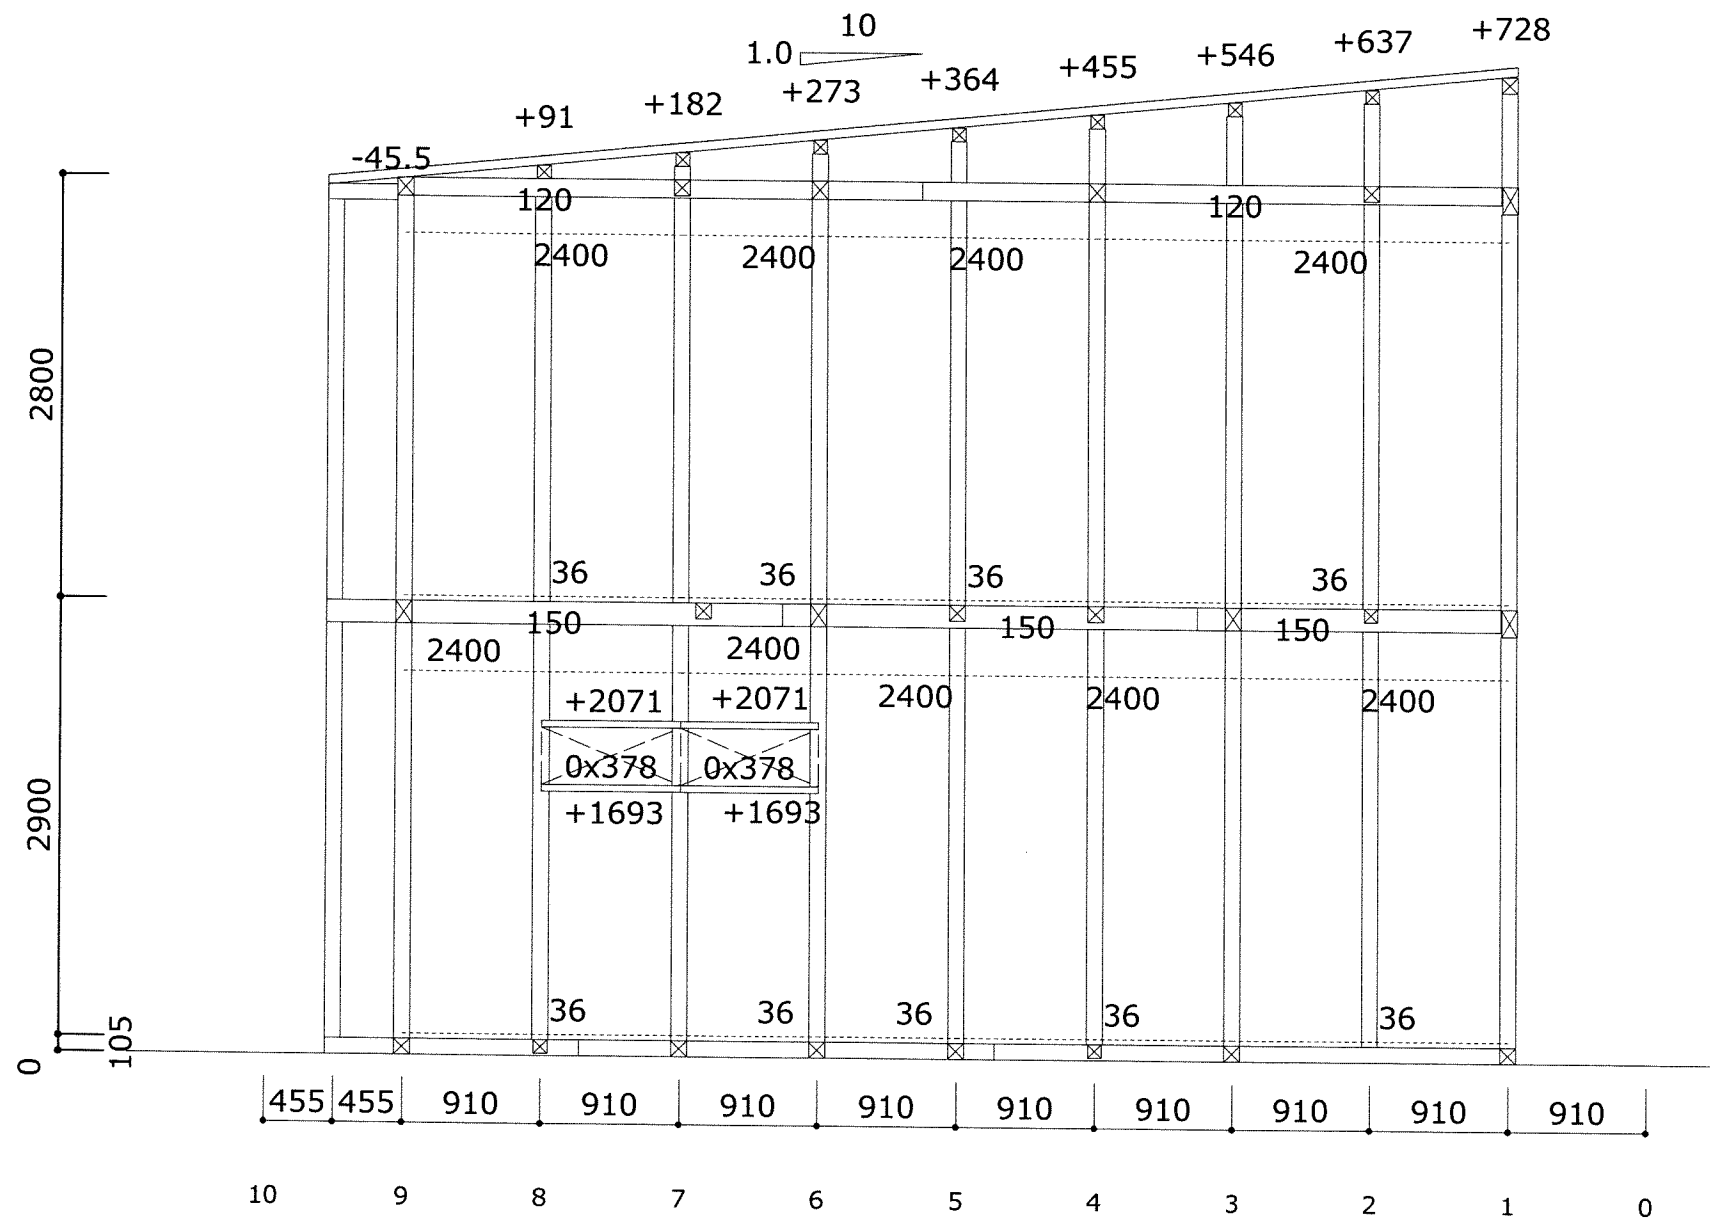

り通り 東面

～ 見積用 伏図 ～				■検印		■仕様		■工事名称		■図面名称	
						910		mm		軸組断面図	
						■桁 高		mm		PG有玉西町分譲住宅様	
						■屋根勾配		寸		■印刷日時	
TEL :				FAX :				2024年 7月24日		■縮尺	
								1 / 50		■物件番号	
										HHS0385	