

| ■ 仕 様                                       |            |   | ■ HEAT20 G1                     |                                                      |  |
|---------------------------------------------|------------|---|---------------------------------|------------------------------------------------------|--|
| 断熱工事                                        |            | ■ 床:カネライトフォーム t65                      ■ 土間床等の外周:スタイロフォームAT t25<br>■ 壁:アクアフォームLITE吹付 t85              ■ 天井:アクファフォームLITE吹付 t170 |                                 |                                                      |  |
| 床下換気                                        |            | ■ 基礎パッキン                      JOTO              (玄関・UB周り:気密基礎パッキン)                                                             |                                 |                                                      |  |
| 防虫防蟻                                        |            | ■ 土壌処理・木部                      ガントナーMC                                                                                         |                                 |                                                      |  |
| ■ 外 部 仕 上 表                                 |            |   | ■ 22条地域                         |                                                      |  |
| 部位                                          |            | 仕上・仕様・メーカー   |                                 | 色番・品番                                                |  |
| 屋根                                          |            | ■ ガルバリウム鋼板(t0.35)UK立平 ニスクカラーPro GH<br>軒先通気金物 日本住環境株式会社【REV-15】                                                                 |                                 | GHK01 Sブラック                                          |  |
| パラペット笠木                                     |            | ■ なし   |                                 |                                                      |  |
| 破風・鼻隠                                       |            | ■ なし   |                                 |                                                      |  |
| 雨樋                                          | (軒樋)       | ■ Panasonic サーフেসケアFS-I型   |                                 | ブラック                                                 |  |
|                                             | (縦樋)       | ■ Panasonic S30角樋   |                                 | ブラック                                                 |  |
| 軒天                                          | 屋根軒        | ■ なし   |                                 |                                                      |  |
|                                             | ポーチ軒       | ■ 神島化学 t= 6mm 軒天ボード エンボス   |                                 | Wチャコールブラック                                           |  |
|                                             | バルコニー軒     | ■ なし   |                                 |                                                      |  |
| オーバーハング水切り                                  |            | ■ ガルバリウム鋼板 ※外壁合わせ JOTO:HF-A3550                                                                                                |                                 | ブラック                                                 |  |
| 外壁<br>※下地面材:タイガーEXハイパー<br>防火認定 PC030BE-4028 | 通気金物(15mm) | ■メイン   | ニチハ エモンエクセラード16 Vシリーズ リーガストーン調V | ランダムMGブラック                                           |  |
|                                             |            | ■アクセントA   | なし                              |                                                      |  |
|                                             |            | ■アクセントB   | なし                              |                                                      |  |
| 玄関ポーチ                                       |            | ■ 床 玄関タイルに同じ   |                                 | -                                                    |  |
| 基礎                                          |            | ■ 立上り巾木: モルタル刷毛引き   |                                 | -                                                    |  |
| 基礎水切り金物                                     |            | ■ JOTO鋼板製 防鼠材付き水切り JOTO:WMF-N35                                                                                                |                                 | ブラック                                                 |  |
| バルコニー                                       | 床・内壁       | ■ なし   |                                 | -                                                    |  |
|                                             | 笠木         | ■ なし   |                                 |                                                      |  |
| 外部建具                                        |            | ■ LIXIL EW(アルゴンガス高遮熱仕様LowE複層ガラス グリーン)<br>・SD、TSで記載がないものは、オペレーターハンドルとする<br>・オペレーター付サッシは固定網戸とする<br>・グレモンハンドル式サッシの選択箇所は可動網戸とする    |                                 | 外観 ブラック<br>内観 ホワイト<br>※樹脂パッキン・網戸付                    |  |
| シャッター                                       |            | ■ なし   |                                 |                                                      |  |
|                                             |            |   |                                 |                                                      |  |
| 玄関扉                                         |            | ■ LIXIL ジエスタ2 K2仕様<br>LIXILファミロック タグキー×3 (電池式)                                                                                 |                                 | ドア型: M17 型<br>ドア色: カームブラック<br>ハンドル: S型ハンドル<br>色 ブラック |  |
|                                             |            |   |                                 |                                                      |  |
| 外部物干し金物                                     |            | ■   |                                 |                                                      |  |
|                                             |            |   |                                 |                                                      |  |
|                                             |            |   |                                 |                                                      |  |
| 換気フード                                       |            | ■ 局所換気扇(トイレ 浴室 キッチンフード)<br>防火ダンパー無                                                                                             |                                 | 外気フード: ブラック                                          |  |
|                                             |            | ■ ダクトレス熱交換換気システム (日本スティーベル株式会社)<br>VLR-70E<br>防火ダンパー無                                                                          |                                 | 外気フード: B ブラック                                        |  |


| ■ 構 造 概 要   |                   |                                                                  |   |                                                   |                                 |
|-------------|-------------------|------------------------------------------------------------------|---|---------------------------------------------------|---------------------------------|
| 基礎          | ■ RCベタ基礎コンクリート    |                                                                  |   |                                                   |                                 |
| 通し柱・管柱      | ■ 構造用集成材 105×105  |                                                                  | 間柱   | ■ 集成材                                             |                                 |
| 土台          | ■ 桧 105×105       | 大引き                                                              | ■ 桧 90*90                                                                                                   | 筋交い                                               | ■ 構造用製材 火打梁 ■ 鋼製火打(当社基準により米松あり) |
| 桁・梁         | ■ 構造用製材及び集成材      |                                                                  | 制震装置   | ■ 無                                               |                                 |
| ■ 設 備 装 着 品 |                   |                                                                  |   |                                                   |                                 |
| 住宅設備        | 部位                | メーカー                                                             | 商品名 ※ 詳細は見積り、プレゼン参照                                                                                         | 見積りNo.                                            | (日付)                            |
|             | キッチン              | LIXIL                                                            | ■ ES ペニンシュラ型<br>スライドストッカー (扉 3色の内未決)                                                                        | 見積り番号 : A24105290035-004-3<br>(日付) 2024.10.11     |                                 |
|             | バックカウンタ<br>※オプション | LIXIL                                                            | ■ ES L1800(W900スライドストッカー+マルチスペース)<br>引き出しTレール仕様 吊戸棚H500(フレーションorライトグレン)                                     | 見積り番号 : A24105290035-004-(5,7)<br>(日付) 2024.10.11 |                                 |
|             | 浴室                | LIXIL                                                            | ■ AX1620 洗い場広タイプ ドア仕様                                                                                       | 見積り番号 : A24105290035-004-1<br>(日付) 2024.10.11     |                                 |
|             | 1Fトイレ             | LIXIL                                                            | ■ ベーシアシャワートイレ 白 ● タオル掛け: KF-AA70D(リング)<br>タンク手洗 無し ● 紙巻き器: CF-AA22H /WA                                     | 見積り番号 : A24105290035-004-9<br>(日付) 2024.10.11     |                                 |
|             | 2Fトイレ             | LIXIL                                                            | ■ ベーシアシャワートイレ 白 ● タオル掛け: KF-AA70D(リング)<br>タンク手洗 有り ● 紙巻き器: CF-AA22H /WA                                     | 見積り番号 : A24105290035-004-10<br>(日付) 2024.10.11    |                                 |
|             | 洗面台               | LIXIL                                                            | ■ EV W900(D500タイプ) 扉:グロスホワイト<br>[ 引出しタイプ シングルハンドシャワー スタンダードLED三面鏡<br>その他 トールキャビネット300 ● タオル掛け: KF-AA71D(バー) | 見積り番号 : A24105290035-004-8<br>(日付) 2024.10.11     |                                 |
|             | スロップシンク           | LIXIL                                                            | ■ S-17/BW1 シングルバー混合水栓SF-WM435SY(170)                                                                        | A24105290035-004-11<br>2024.10.11                 |                                 |
|             |                   |                                                                  |   |                                                   |                                 |
|             |                   |                                                                  |   |                                                   |                                 |
| 給排水設備       | 給湯器               | ■ エコキュート370L Panasonic NSシリーズ スタンダードモデル 追い焚きフルオート                |   |                                                   |                                 |
|             | 排水                | ■ 合併浄化槽 5人槽 ポンプアップ無                                              |   |                                                   |                                 |
|             | 外水栓               | ■ 1 カ所 (平面図参照)                                                   | ■ 外部立栓柱: PVC製 水栓柱12型【前澤化成工業】                                                                                |                                                   |                                 |
|             | 外部ガーデンパン          | ■ 無し                                                             |   |                                                   |                                 |
|             | その他               | ■ 洗濯機用単水栓: 緊急止水弁付 ■ 洗濯機用排水: トラップ金物(標準)<br>■ 排水さや管(長期優良住宅仕様)      |   |                                                   |                                 |
| ガス配管設備      |                   | ■ あり(LPG) (配置図・平面図参照 ※乾太くん用)                                     |   |                                                   |                                 |
| 電気設備        | インターホン            | ■ パナソニック VL-SZ30KL                                               |   |                                                   |                                 |
|             | TVアンテナ            | ■ UHF + BS・110度CS／CSアンテナ [2K・4K・8K対応] ■ブラック ※電波状況によりホワイトになる可能性あり |   |                                                   |                                 |
|             | エアコン              | ■ 設置場所:                                                          |   |                                                   |                                 |
|             | ソーラー              | ■ あり(Qセルズ) 12 枚 5.22 KW Re.RISE-G2 435 (1722×1134×30)            |   |                                                   |                                 |
|             | ※標準搭載             | ※メーカーのモデルチェンジ等で後継品に変更される可能性あり<br>■ 屋外パワコン 西面                     |   |                                                   |                                 |
| その他         |                   |                                                                  |   |                                                   |                                 |

|  |                                                                                    |                                                                                               |   |                    |                    |       |    |    |    |     |
|--|------------------------------------------------------------------------------------|-----------------------------------------------------------------------------------------------|---|--------------------|--------------------|-------|----|----|----|-----|
|  | 浜 岡 一 級 総 合 設 計 事 務 所<br>一級建築士事務所 静岡県知事登録第 (10)2441 号<br>一級建築士 大臣登録第 365879 号 西原利昌 |  PG HOUSE | 株式会社 LIFEFUND InDesign office 一級建築士事務所<br>事務所登録 (2)第7595号 一級建築士登録 第179770号 鈴木 達男<br>〒432-8023 静岡県浜松市中央区鴨江3丁目70番23号 | 年 月 日<br>2024.11.8 | 件名<br>伊藤友章 様邸 新築工事 |       | 設計 | IC | 工務 | 図 番 |
|  |                                                                                    |                                                                                               |   |                    |                    |       | 倉田 |    | 青島 | 1-1 |
|  |                                                                                    |                                                                                               |   | 縮尺                 | 図面                 | 仕上表 1 |    |    |    |     |
|  |                                                                                    |                                                                                               |   |                    |                    |       |    |    |    |     |


| ■ 仕 様                                       |                                                       |   | ■ HEAT20 G1                     |                                                      |
|---------------------------------------------|-------------------------------------------------------|---|---------------------------------|------------------------------------------------------|
| 断熱工事                                        |                                                       | ■ 床:カネライトフォーム t65                      ■ 土間床等の外周:スタイロフォームAT t25<br>■ 壁:アクアフォームLITE吹付 t85              ■ 天井:アクファフォームLITE吹付 t170 |                                 |                                                      |
| 床下換気                                        |                                                       | ■ 基礎パッキン                      JOTO              (玄関・UB周り:気密基礎パッキン)                                                             |                                 |                                                      |
| 防虫防蟻                                        |                                                       | ■ 土壌処理・木部                      ガントナーMC                                                                                         |                                 |                                                      |
| ■ 外 部 仕 上 表                                 |                                                       |   | ■ 22条地域                         |                                                      |
| 部位                                          |                                                       | 仕上・仕様・メーカー   |                                 | 色番・品番                                                |
| 屋根                                          |                                                       | ■ ガルバリウム鋼板(t0.35)UK立平 ニスクカラーPro GH<br>軒先通気金物 日本住環境株式会社【REV-15】                                                                 |                                 | GHK01 Sブラック                                          |
| パラペット笠木                                     |                                                       | ■ なし   |                                 |                                                      |
| 破風・鼻隠                                       |                                                       | ■ なし   |                                 |                                                      |
| 雨樋                                          | (軒樋)                                                  | ■ Panasonic サーフেসケアFS-I型   |                                 | ブラック                                                 |
|                                             | (縦樋)                                                  | ■ Panasonic S30角樋   |                                 | ブラック                                                 |
| 軒天                                          | 屋根軒                                                   | ■ なし   |                                 |                                                      |
|                                             | ポーチ軒                                                  | ■ 神島化学 t= 6mm 軒天ボード エンボス   |                                 | Wチャコールブラック                                           |
|                                             | バルコニー軒                                                | ■ なし   |                                 |                                                      |
| オーバーハング水切り                                  |                                                       | ■ ガルバリウム鋼板 ※外壁合わせ JOTO:HF-A3550                                                                                                |                                 | ブラック                                                 |
| 外壁<br>※下地面材:タイガーEXハイパー<br>防火認定 PC030BE-4028 | 通気金物(15mm)                                            | ■メイン   | ニチハ エモンエクセラード16 Vシリーズ リーガストーン調V | ランダムMGブラック                                           |
|                                             |                                                       | ■アクセントA   | なし                              |                                                      |
|                                             |                                                       | ■アクセントB   | なし                              |                                                      |
| 玄関ポーチ                                       |                                                       | ■ 床 玄関タイルに同じ   |                                 | -                                                    |
| 基礎                                          |                                                       | ■ 立上り巾木: モルタル刷毛引き   |                                 | -                                                    |
| 基礎水切り金物                                     |                                                       | ■ JOTO鋼板製 防鼠材付き水切り JOTO:WMF-N35                                                                                                |                                 | ブラック                                                 |
| バルコニー                                       | 床・内壁                                                  | ■ なし   |                                 | -                                                    |
|                                             | 笠木                                                    | ■ なし   |                                 |                                                      |
| 外部建具                                        |                                                       | ■ LIXIL EW(アルゴンガス高遮熱仕様LowE複層ガラス グリーン)<br>・SD、TSで記載がないものは、オペレーターハンドルとする<br>・オペレーター付サッシは固定網戸とする<br>・グレモンハンドル式サッシの選択箇所は可動網戸とする    |                                 | 外観 ブラック<br>内観 ホワイト<br>※樹脂パッキン・網戸付                    |
| シャッター                                       |                                                       | ■ なし   |                                 |                                                      |
|                                             |                                                       |   |                                 |                                                      |
| 玄関扉                                         |                                                       | ■ LIXIL ジエスタ2 K2仕様<br>LIXILファミロック タグキー×3 (電池式)                                                                                 |                                 | ドア型: M17 型<br>ドア色: カームブラック<br>ハンドル: S型ハンドル<br>色 ブラック |
|                                             |                                                       |   |                                 |                                                      |
| 外部物干し金物                                     |                                                       | ■   |                                 |                                                      |
|                                             |                                                       |   |                                 |                                                      |
|                                             |                                                       |   |                                 |                                                      |
| 換気フード                                       | ■ 局所換気扇(トイレ 浴室 キッチンフード)<br>防火ダンパー無                    |   | 外気フード: ブラック                     |                                                      |
|                                             | ■ ダクトレス熱交換換気システム (日本スティーベル株式会社)<br>VLR-70E<br>防火ダンパー無 |   | 外気フード: B ブラック                   |                                                      |

| ■ 構 造 概 要   |                             |                                                                  |   |                                                   |                                 |
|-------------|-----------------------------|------------------------------------------------------------------|---|---------------------------------------------------|---------------------------------|
| 基礎          | ■ RCベタ基礎コンクリート              |                                                                  |   |                                                   |                                 |
| 通し柱・管柱      | ■ 構造用集成材 105×105            |                                                                  | 間柱   | ■ 集成材                                             |                                 |
| 土台          | ■ 桧 105×105                 | 大引き                                                              | ■ 桧 90*90                                                                                                   | 筋交い                                               | ■ 構造用製材 火打梁 ■ 鋼製火打(当社基準により米松あり) |
| 桁・梁         | ■ 構造用製材及び集成材                |                                                                  | 制震装置   | ■ 無                                               |                                 |
| ■ 設 備 装 着 品 |                             |                                                                  |   |                                                   |                                 |
| 住宅設備        | 部位                          | メーカー                                                             | 商品名 ※ 詳細は見積り、プレゼン参照                                                                                         | 見積りNo.                                            | (日付)                            |
|             | キッチン                        | LIXIL                                                            | ■ ES ペニンシュラ型<br>スライドストッカー (扉 3色の内未決)                                                                        | 見積り番号 : A24105290035-004-3<br>(日付) 2024.10.11     |                                 |
|             | バックカウンタ<br>※オプション           | LIXIL                                                            | ■ ES L1800(W900スライドストッカー+マルチスペース)<br>引き出しTレール仕様 吊戸棚H500(フレーションorライトグレン)                                     | 見積り番号 : A24105290035-004-(5,7)<br>(日付) 2024.10.11 |                                 |
|             | 浴室                          | LIXIL                                                            | ■ AX1620 洗い場広タイプ ドア仕様                                                                                       | 見積り番号 : A24105290035-004-1<br>(日付) 2024.10.11     |                                 |
|             | 1Fトイレ                       | LIXIL                                                            | ■ ベーシアシャワートイレ 白 ● タオル掛け: KF-AA70D(リング)<br>タンク手洗 無し ● 紙巻き器: CF-AA22H /WA                                     | 見積り番号 : A24105290035-004-9<br>(日付) 2024.10.11     |                                 |
|             | 2Fトイレ                       | LIXIL                                                            | ■ ベーシアシャワートイレ 白 ● タオル掛け: KF-AA70D(リング)<br>タンク手洗 有り ● 紙巻き器: CF-AA22H /WA                                     | 見積り番号 : A24105290035-004-10<br>(日付) 2024.10.11    |                                 |
|             | 洗面台                         | LIXIL                                                            | ■ EV W900(D500タイプ) 扉:グロスホワイト<br>[ 引出しタイプ シングルハンドシャワー スタンダードLED三面鏡<br>その他 トールキャビネット300 ● タオル掛け: KF-AA71D(バー) | 見積り番号 : A24105290035-004-8<br>(日付) 2024.10.11     |                                 |
|             | スロップシンク                     | LIXIL                                                            | ■ S-17/BW1 シングルバー混合水栓SF-WM435SY(170)                                                                        | A24105290035-004-11<br>2024.10.11                 |                                 |
|             |                             |                                                                  |   |                                                   |                                 |
|             |                             |                                                                  |   |                                                   |                                 |
| 給排水設備       | 給湯器                         | ■ エコキュート370L Panasonic NSシリーズ スタンダードモデル 追い焚きフルオート                |   |                                                   |                                 |
|             | 排水                          | ■ 合併浄化槽 5人槽 ポンプアップ無                                              |   |                                                   |                                 |
|             | 外水栓                         | ■ 1 カ所 (平面図参照)                                                   | ■ 外部立栓柱: PVC製 水栓柱12型【前澤化成工業】                                                                                |                                                   |                                 |
|             | 外部ガーデンパン                    | ■ 無し                                                             |   |                                                   |                                 |
|             | その他                         | ■ 洗濯機用単水栓: 緊急止水弁付 ■ 洗濯機用排水: トラップ金物(標準)<br>■ 排水さや管(長期優良住宅仕様)      |   |                                                   |                                 |
| ガス配管設備      | ■ あり(LPG) (配置図・平面図参照 ※乾太くん用 |                                                                  |   |                                                   |                                 |
| 電気設備        | インターホン                      | ■ パナソニック VL-SZ30KL                                               |   |                                                   |                                 |
|             | TVアンテナ                      | ■ UHF + BS・110度CS／CSアンテナ [2K・4K・8K対応] ■ブラック ※電波状況によりホワイトになる可能性あり |   |                                                   |                                 |
|             | エアコン                        | ■ 設置場所:                                                          |   |                                                   |                                 |
|             | ソーラー                        | ■ あり(Qセルズ) 12 枚 5.22 KW Re.RISE-G2 435 (1722×1134×30)            |   |                                                   |                                 |
|             | ※標準搭載                       | ※メーカーのモデルチェンジ等で後継品に変更される可能性あり<br>■ 屋外パワコン 西面                     |   |                                                   |                                 |
| その他         |                             |                                                                  |   |                                                   |                                 |

|  |                                                                                    |                                                                                               |   |                      |  |                      |  |  |    |    |    |     |  |
|--|------------------------------------------------------------------------------------|-----------------------------------------------------------------------------------------------|---|----------------------|--|----------------------|--|--|----|----|----|-----|--|
|  | 浜 岡 一 級 総 合 設 計 事 務 所<br>一級建築士事務所 静岡県知事登録第 (10)2441 号<br>一級建築士 大臣登録第 365879 号 西原利昌 |  PG HOUSE | 株式会社 LIFEFUND InDesign office 一級建築士事務所<br>事務所登録 (2)第7595号      一級建築士登録 第179770号      鈴木 達男<br>〒432-8023 静岡県浜松市中央区鴨江3丁目70番23号 | 年 月 日      2024.11.8 |  | 件名      伊藤友章 様邸 新築工事 |  |  | 設計 | IC | 工務 | 図 番 |  |
|  |                                                                                    |                                                                                               |   | 縮尺                   |  | 図面      仕上表 1        |  |  | 倉田 |    | 青島 | 1-1 |  |
|  |                                                                                    |                                                                                               |   |                      |  |                      |  |  |    |    |    |     |  |
|  |                                                                                    |                                                                                               |   |                      |  |                      |  |  |    |    |    |     |  |

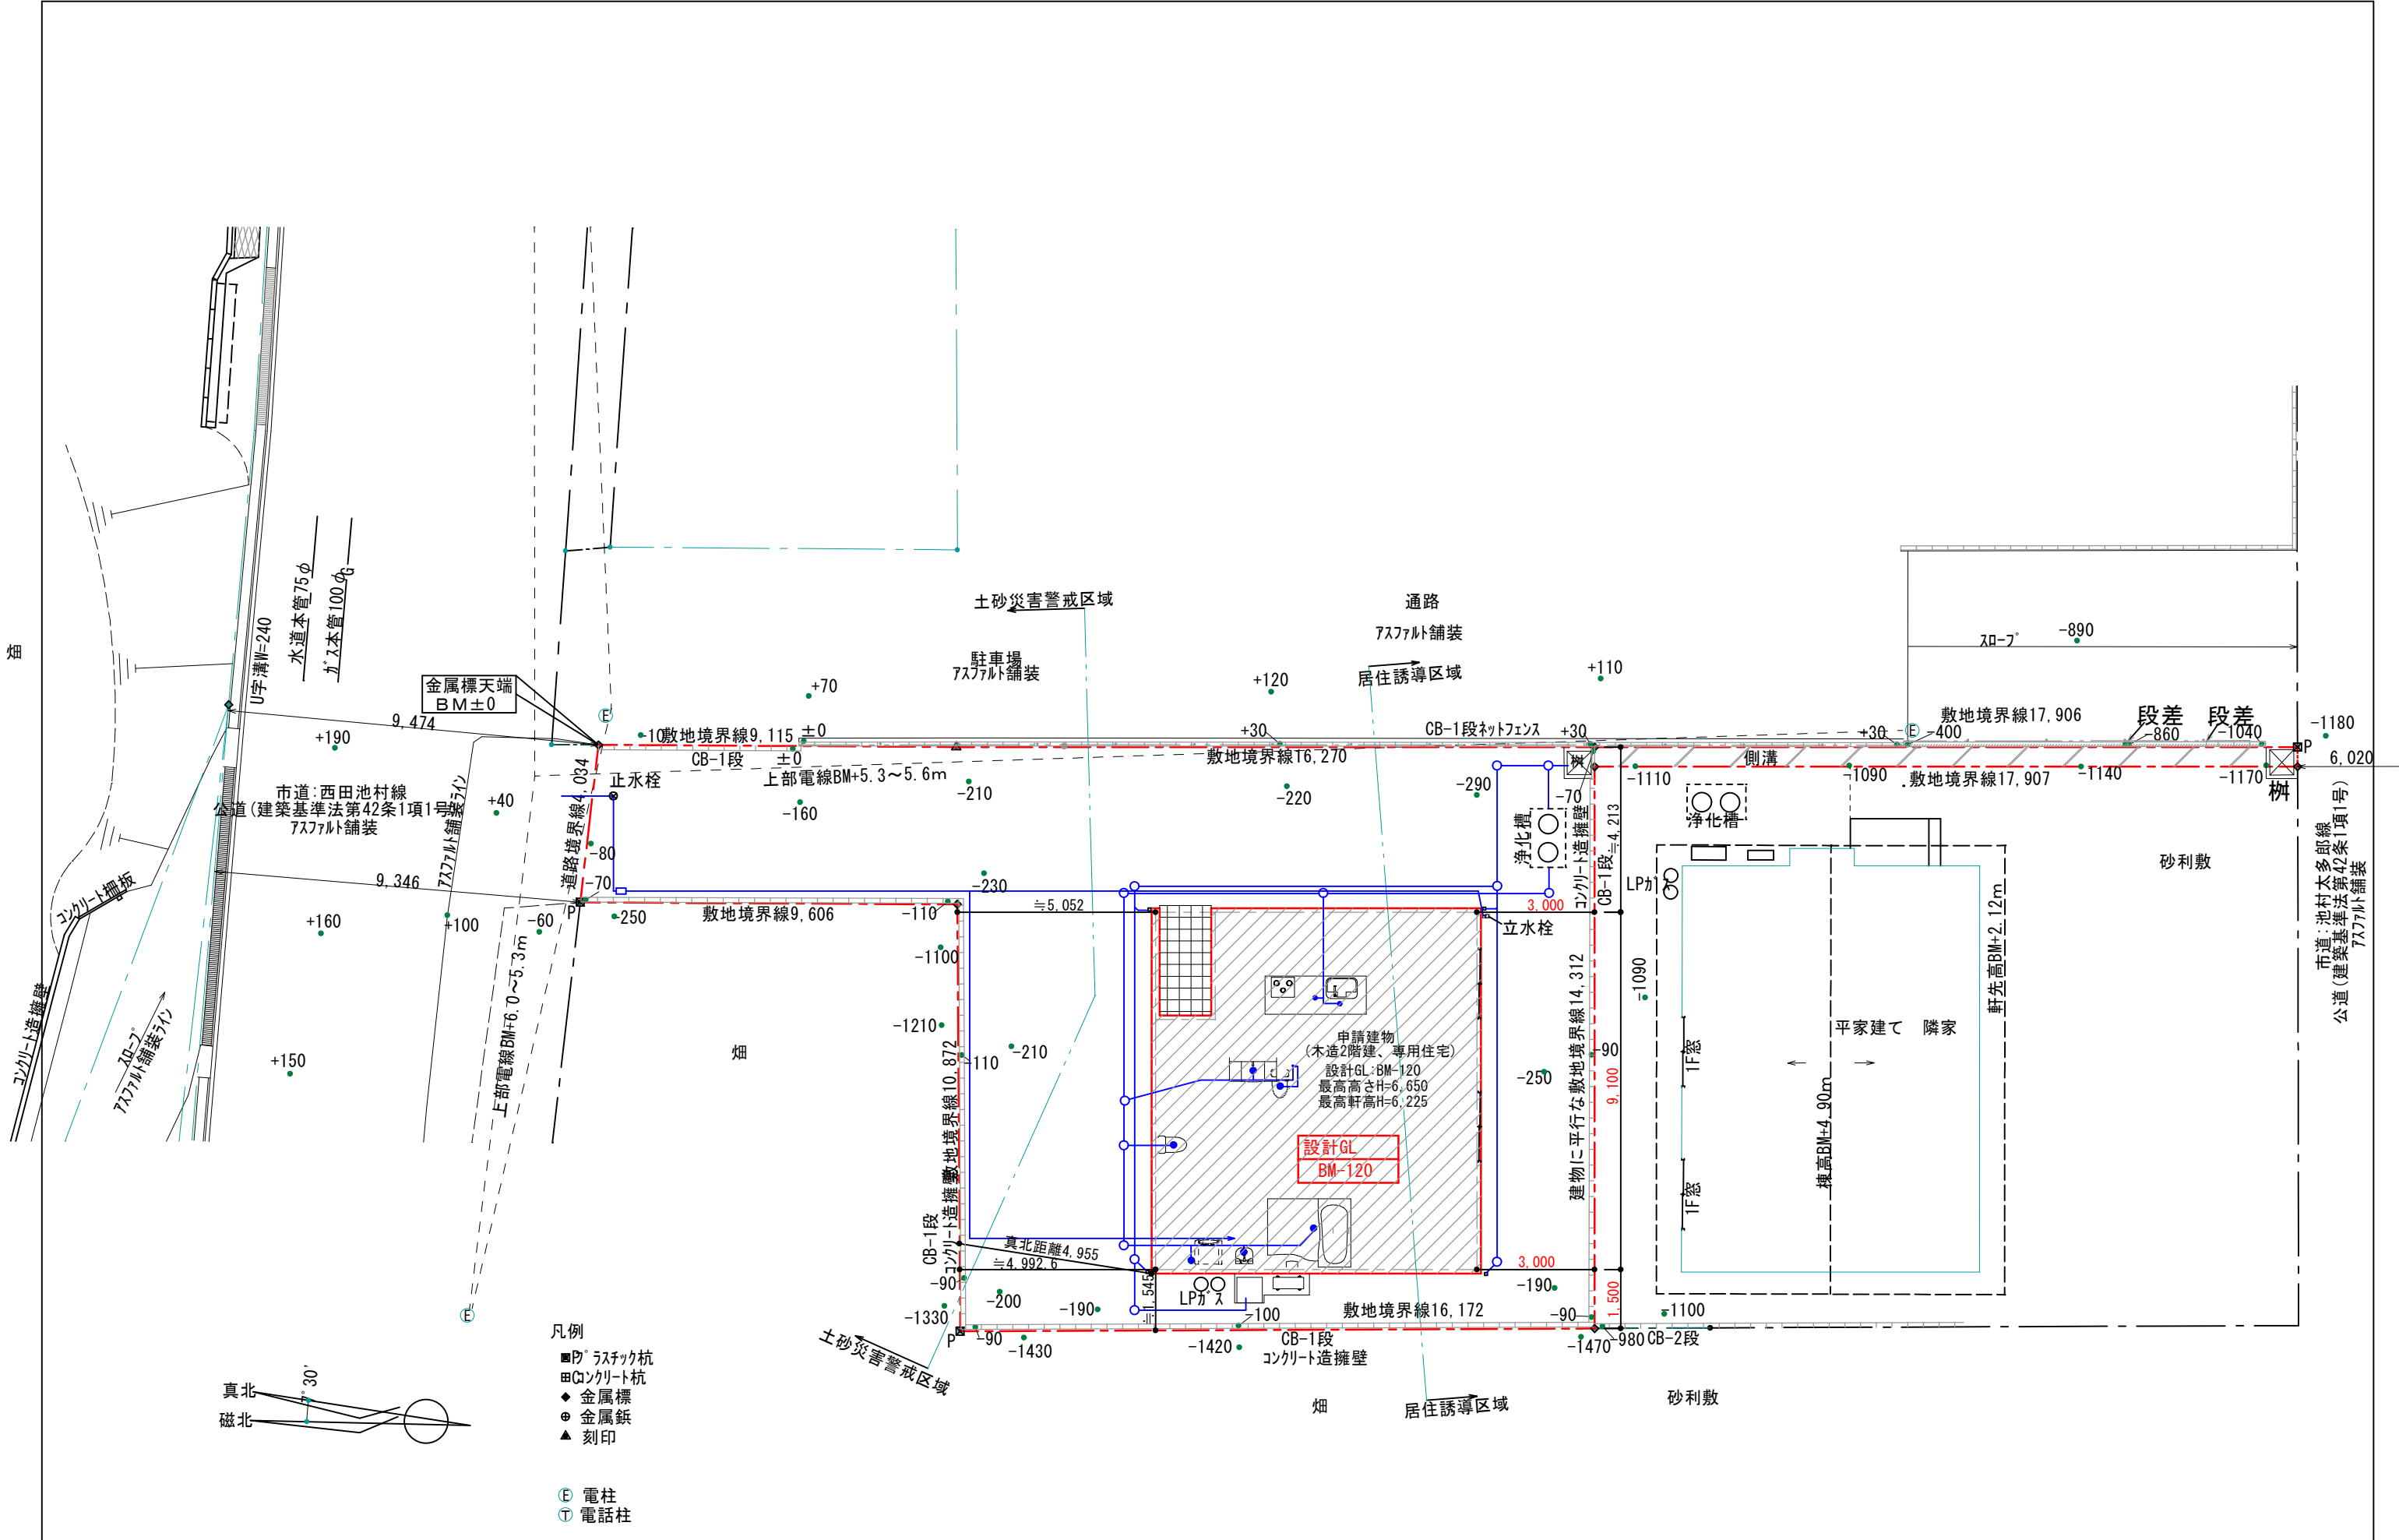

|    |                                                                            |                      |   |                     |                    |  |    |    |    |     |
|----|----------------------------------------------------------------------------|----------------------|---|---------------------|--------------------|--|----|----|----|-----|
| 訂正 | 浜岡 一級総合設計事務所<br>一級建築士事務所 静岡県知事登録第 (10) 2441 号<br>一級建築士 大臣登録第 365879 号 西原利昌 | LIFEFUND<br>PG HOUSE | 株式会社 LIFEFUND InDesign office 一級建築士事務所<br>事務所登録 (2) 第7595号 一級建築士登録 第179770号 鈴木 達男<br>〒432-8023 静岡県浜松市中央区鴨江3丁目70番23号 | 年月日<br>2024. 11. 08 | 件名<br>PG有玉西分譲 新築工事 |  | 設計 | IC | 工事 | 図番  |
|    |                                                                            |                      |   | 縮尺<br>1/150         | 図名<br>配置図          |  | 倉田 |    | 青島 | 2-1 |
|    |                                                                            |                      |   |                     |                    |  |    |    |    |     |

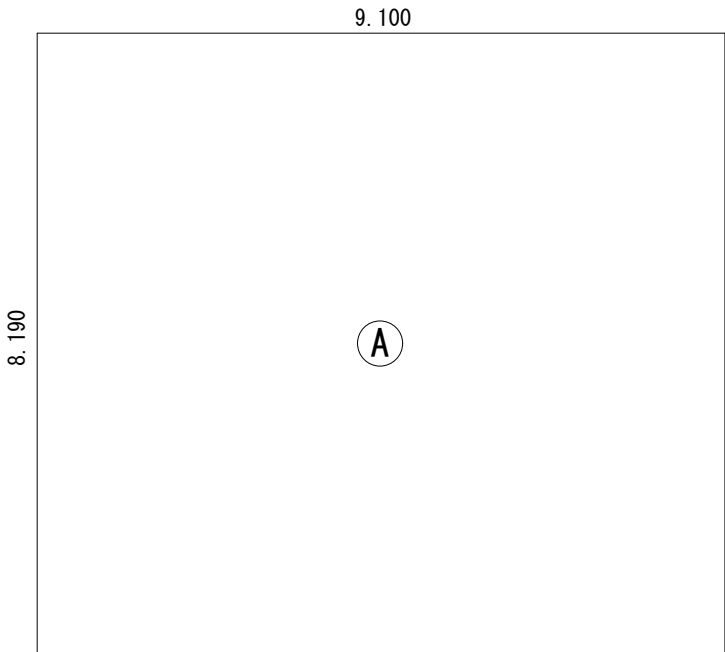


建築面積求積図 S=1/100

建築面積求積表

| 番号 | 計算式           | (m) | 面積 (㎡)          |
|----|---------------|-----|-----------------|
| Ⓐ  | 9.100 × 8.190 |     | 74.529          |
|    |               |     |                 |
|    |               |     |                 |
| 合計 |               |     | 74.529<br>74.52 |

(22.5坪)

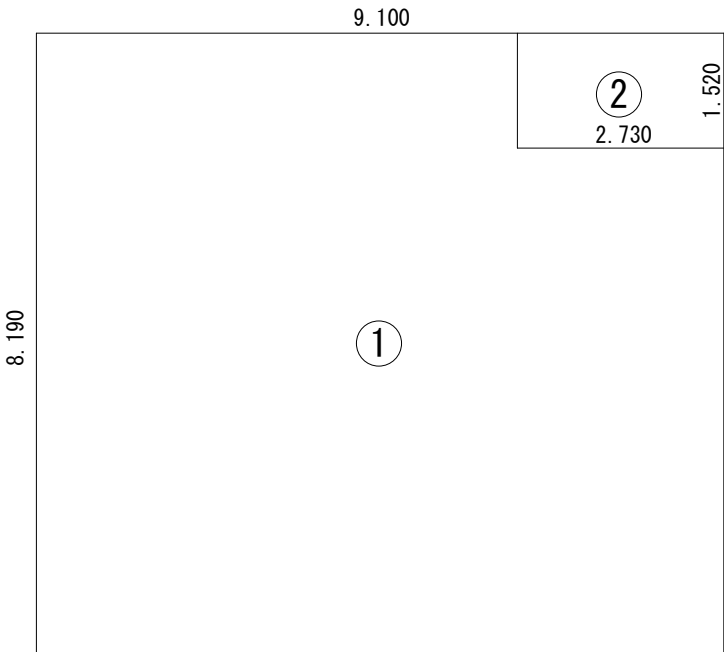


1階床面積図 S=1/100

1階床面積求積表

| 番号 | 計算式           | (m) | 面積 (㎡)           |
|----|---------------|-----|------------------|
| ①  | 9.100 × 8.190 |     | 74.529           |
| ②  | 1.520 × 2.730 |     | -4.1496          |
|    |               |     |                  |
| 合計 |               |     | 70.3794<br>70.37 |

(21.2坪)

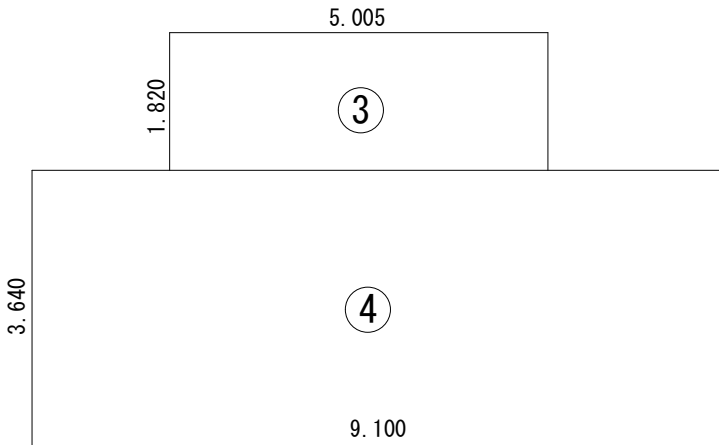

2階床面積図 S=1/100

2階床面積求積表

| 番号 | 計算式           | (m) | 面積 (㎡)           |
|----|---------------|-----|------------------|
| ③  | 5.005 × 1.820 |     | 9.1091           |
| ④  | 3.640 × 3.640 |     | 33.124           |
|    |               |     |                  |
| 合計 |               |     | 42.2331<br>42.23 |

(12.7坪)

延べ床面積表

|       | 番号    | (m) | 面積 (㎡) |
|-------|-------|-----|--------|
| 1階床面積 | ① - ② |     | 70.37  |
| 2階床面積 | ③ + ④ |     | 42.23  |
| 合計    |       |     | 112.60 |

(34.0坪)





| 壁付け 住宅用火災報知器 |           |  | 数量 |
|--------------|-----------|--|----|
| H<br>熱感知     | 電池式 (単独型) |  |    |
|              | 露出型       |  |    |
| 壁付け 住宅用火災報知器 |           |  | 数量 |
| S<br>煙感知     | 電池式 (単独型) |  |    |
|              | 露出型       |  |    |


※ 煙感知器は壁・梁より600mm以上離す  
壁に取付ける場合、  
天井から150mm以上500mm以内離す  
換気扇・エアコン吹出口から1500mm以上離す  
※ 全室LED照明とする。  
※ 標準天井高さ2,400


\* 凡例

- 管柱 (105×105)
- Kダクト (3.30倍 FRM-0641)
- 片筋違い (2.00倍 45×90)  
(例 左:柱脚 右:柱頭)
- たすき掛筋違い (4.00倍 45×90)
- 構造用合板 (2.50倍)  
(t=9 タイライト)
- 床点検口
- 天井点検口
- 換気扇
- 熱交換換気扇VLR-70



| コスモワイド スクエア<br>スマートデザイン (外部) |                  |       |     |
|------------------------------|------------------|-------|-----|
| 凡例                           | 1                | コンセント | 1ヶ所 |
| 2                            | コンセント            | 2ヶ所   |     |
| 3                            | コンセント            | 3ヶ所   |     |
| 1ET                          | コンセント1ヶ所接地ターミナル付 |       |     |
| 2ET                          | コンセント2ヶ所接地ターミナル付 |       |     |
| WP                           | コンセント            | 防水型   |     |
|                              | エアコン用コンセント       |       |     |
|                              | 200V用コンセント       |       |     |
| WP                           | 防雨入線プレート         |       |     |
|                              | スイッチ             |       |     |
| 3                            | 3路スイッチ           |       |     |
| 4                            | 4路スイッチ           |       |     |
|                              | 直結電源             |       |     |
| TV                           | テレビ取出口           |       |     |
| TEL                          | 電話取出口 (テレホンガイド)  |       |     |
| LAN                          | LAN取出口 (テレホンガイド) |       |     |
|                              | 壁照明              |       |     |
|                              | リモコン (給湯関係・ルフロ)  |       |     |
|                              | メーター             |       |     |
|                              | 分電盤              |       |     |
|                              | チャイム             |       |     |

※ACコンセント天井付け  
※TVアンテナ工事  
※スイッチはFL+1100、コンセントはFL+200

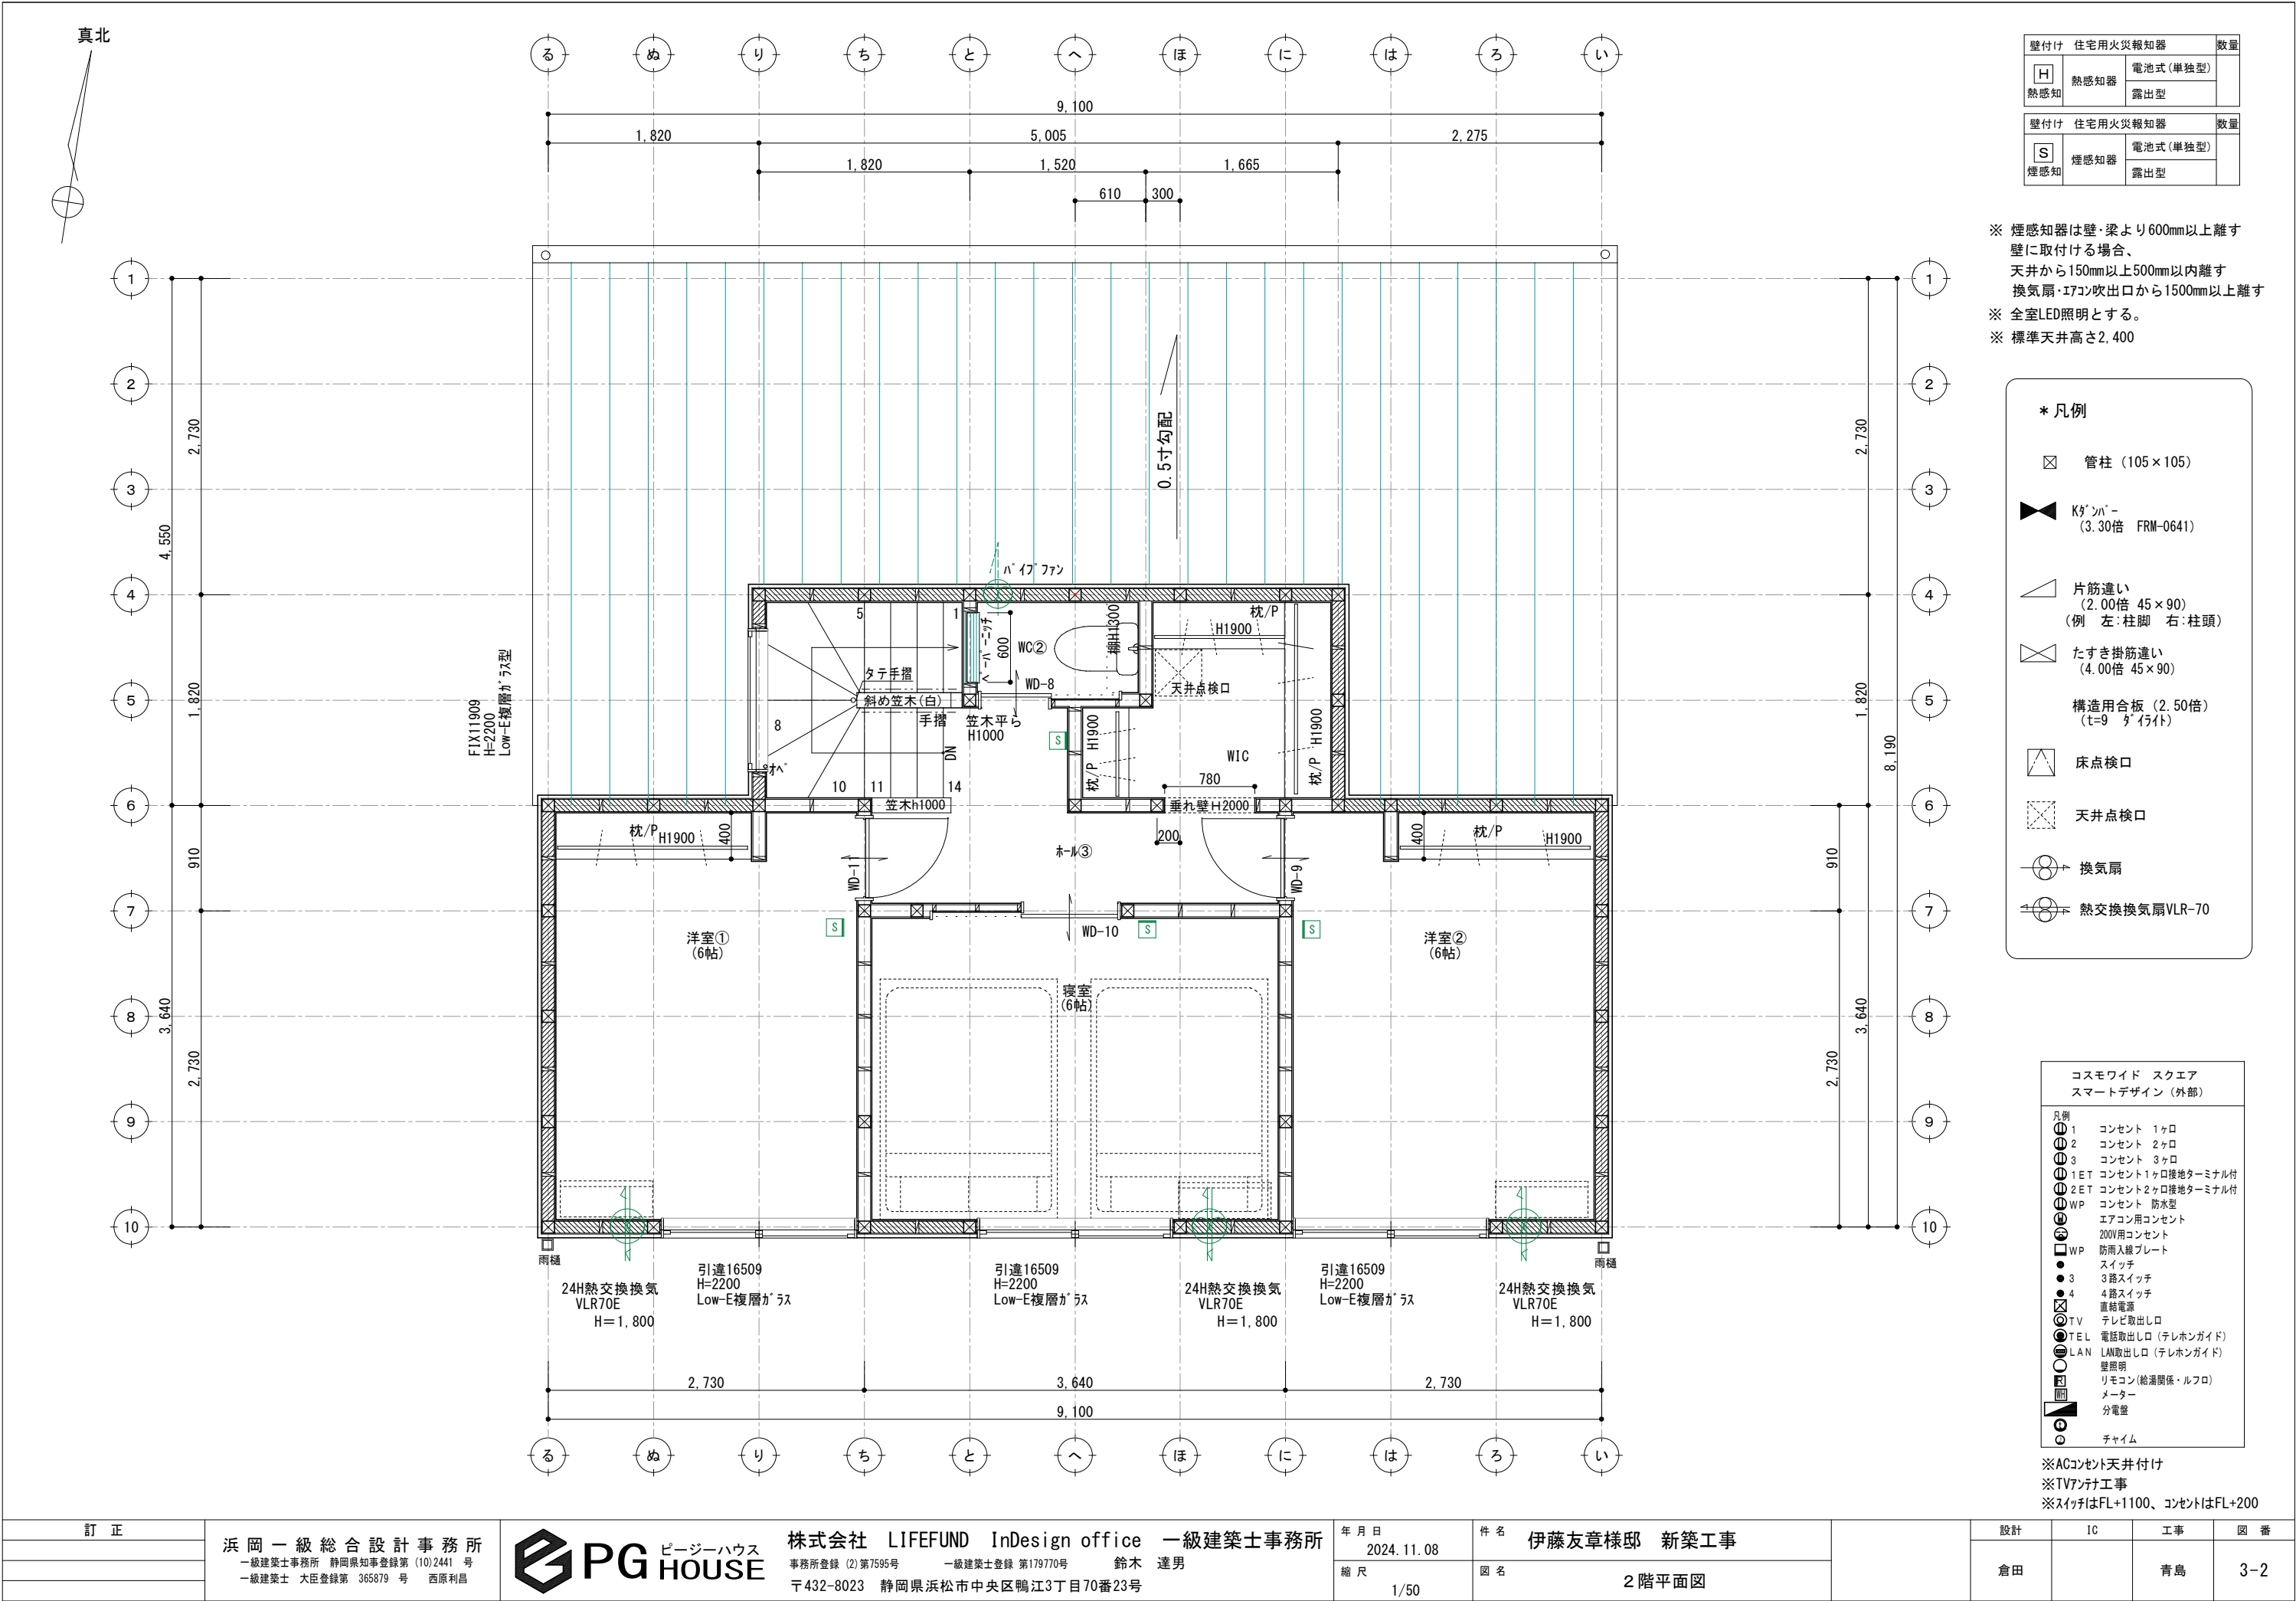


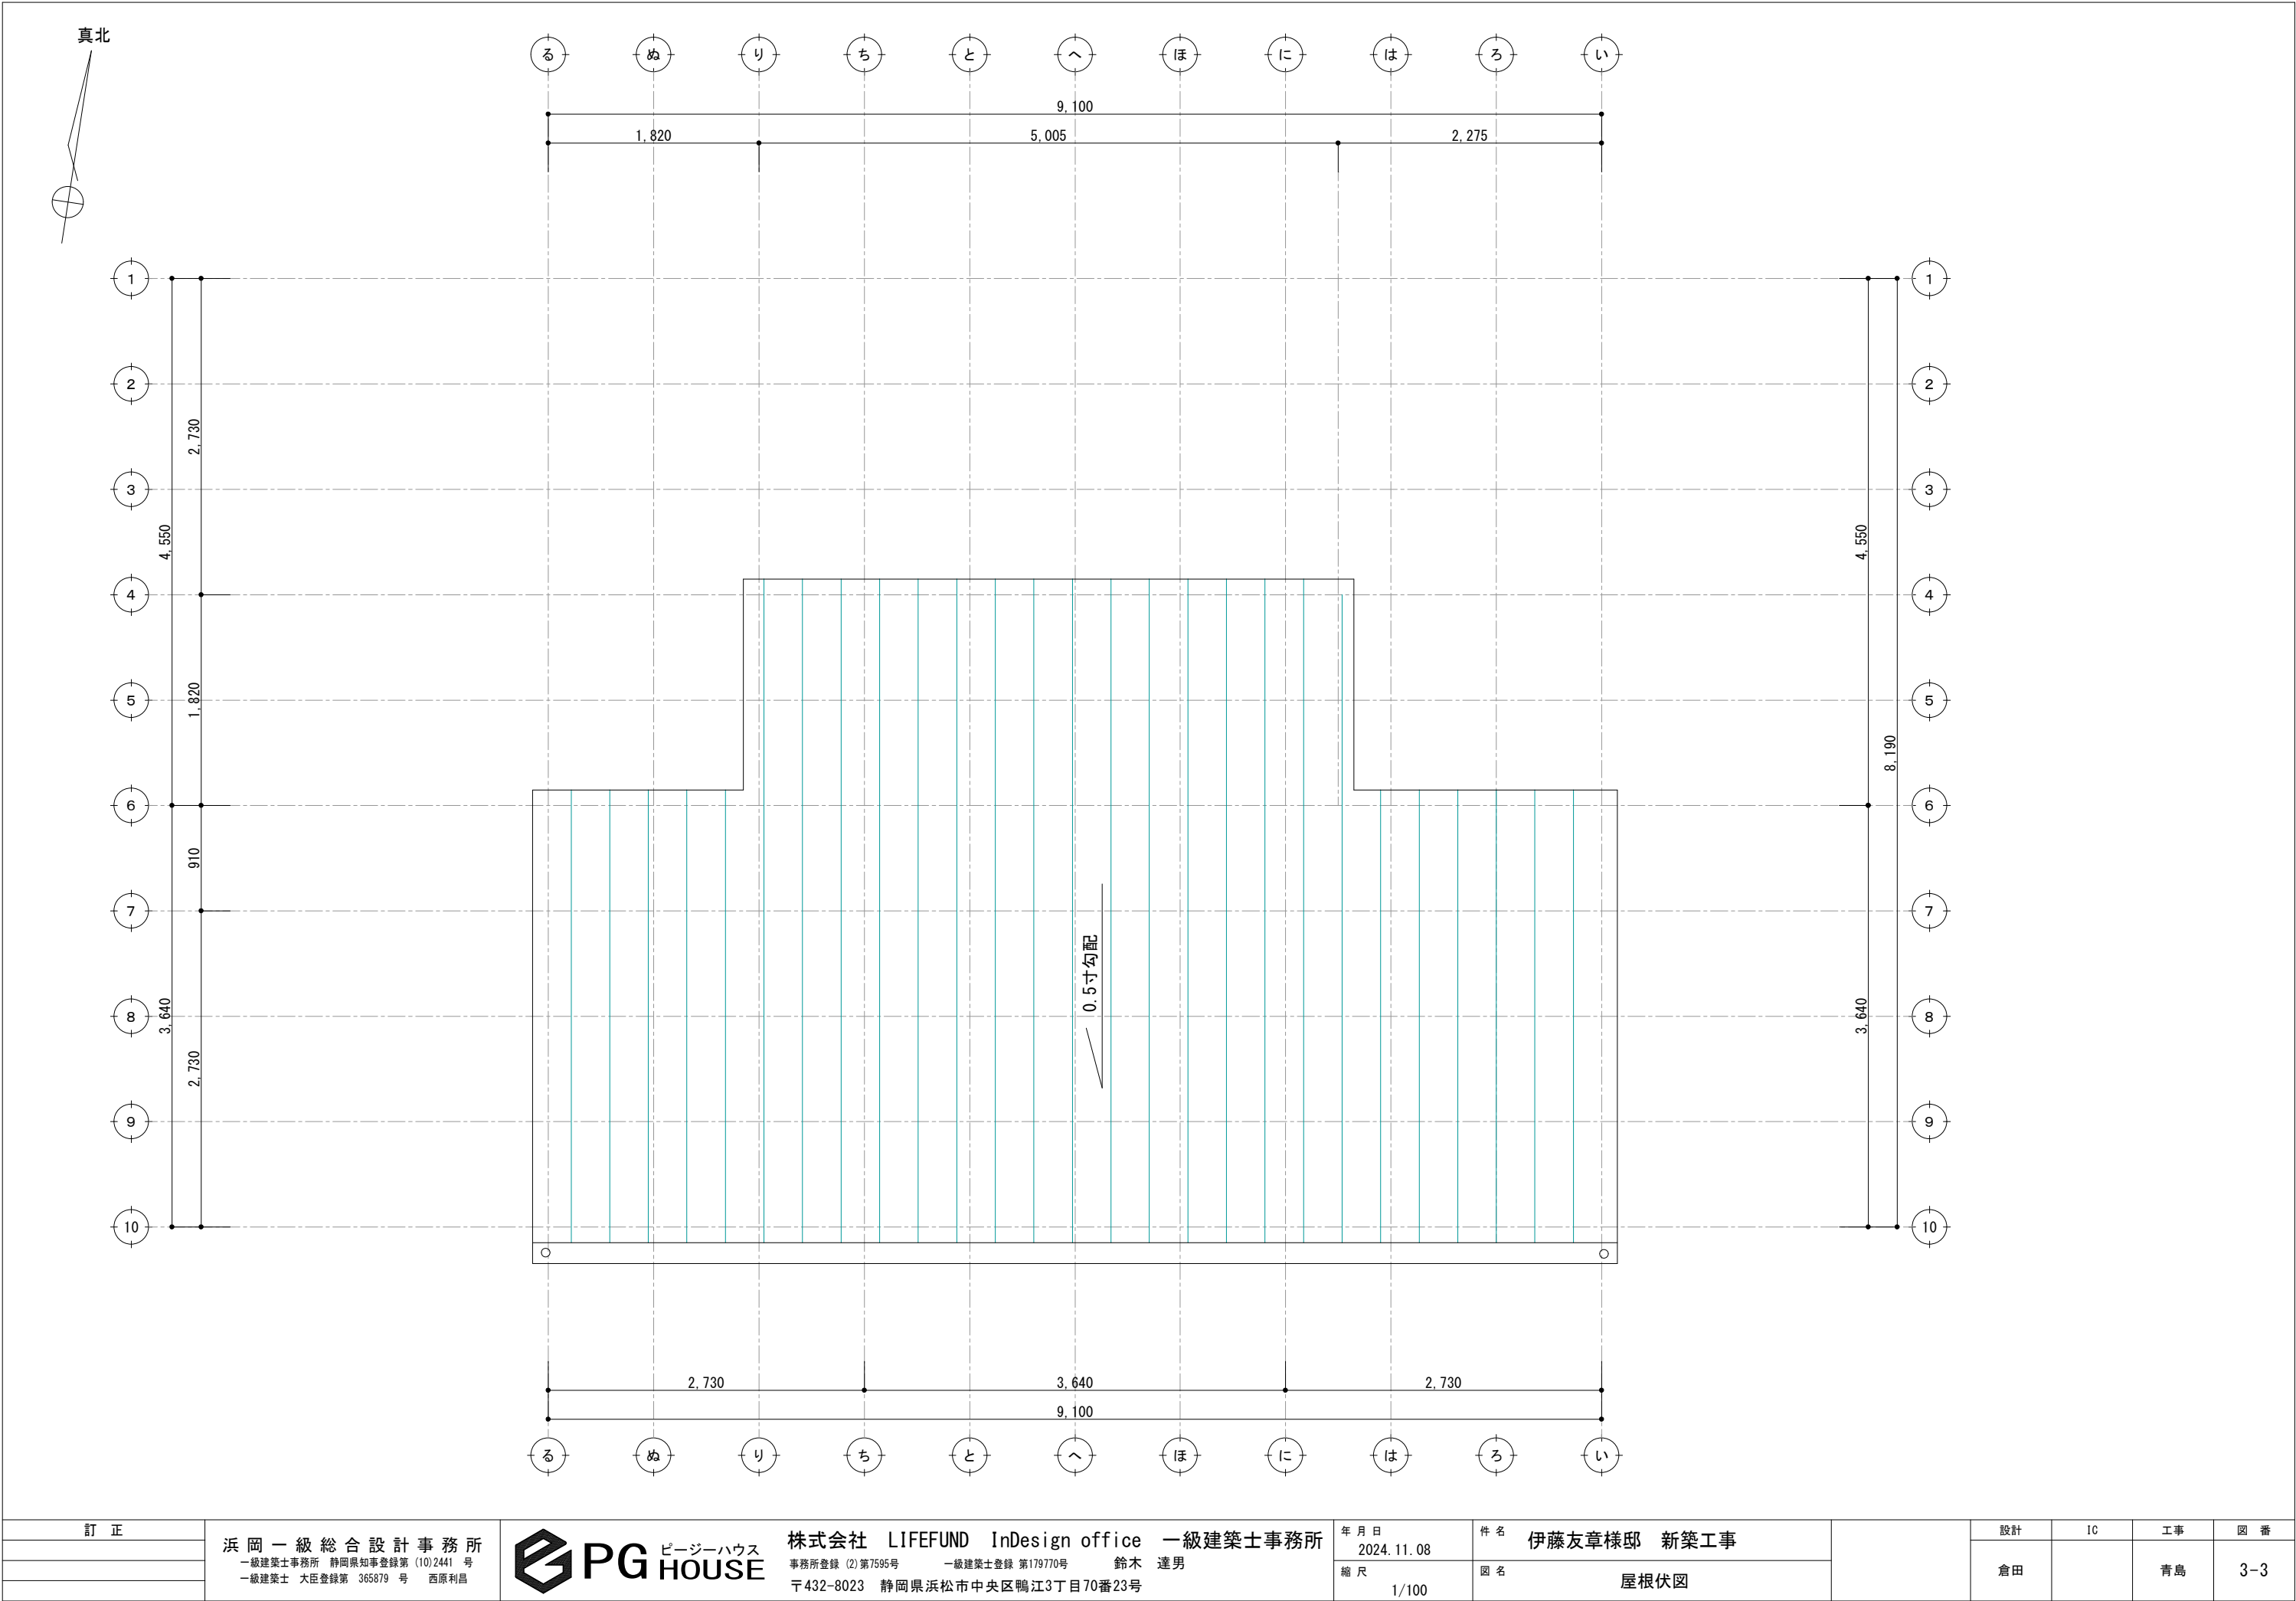





|     |                                                                                    |                                                                                               |   |              |             |  |    |    |    |     |
|-----|------------------------------------------------------------------------------------|-----------------------------------------------------------------------------------------------|---|--------------|-------------|--|----|----|----|-----|
| 訂 正 | 浜 岡 一 級 総 合 設 計 事 務 所<br>一級建築士事務所 静岡県知事登録第 (10)2441 号<br>一級建築士 大臣登録第 365879 号 西原利昌 |  PG HOUSE | 株式会社 LIFEFUND InDesign office 一級建築士事務所<br>事務所登録 (2) 第7595号 一級建築士登録 第179770号 鈴木 達男<br>〒432-8023 静岡県浜松市中央区鴨江3丁目70番23号 | 年 月 日        | 件 名         |  | 設計 | IC | 工事 | 図 番 |
|     |                                                                                    |                                                                                               |   | 2024. 11. 08 | 伊藤友章様邸 新築工事 |  |    |    |    |     |
|     |                                                                                    |                                                                                               |   | 縮 尺          | 図 名         |  |    |    |    |     |
|     |                                                                                    |                                                                                               |   | 1/100        | 屋根伏図        |  | 倉田 |    | 青島 | 3-3 |

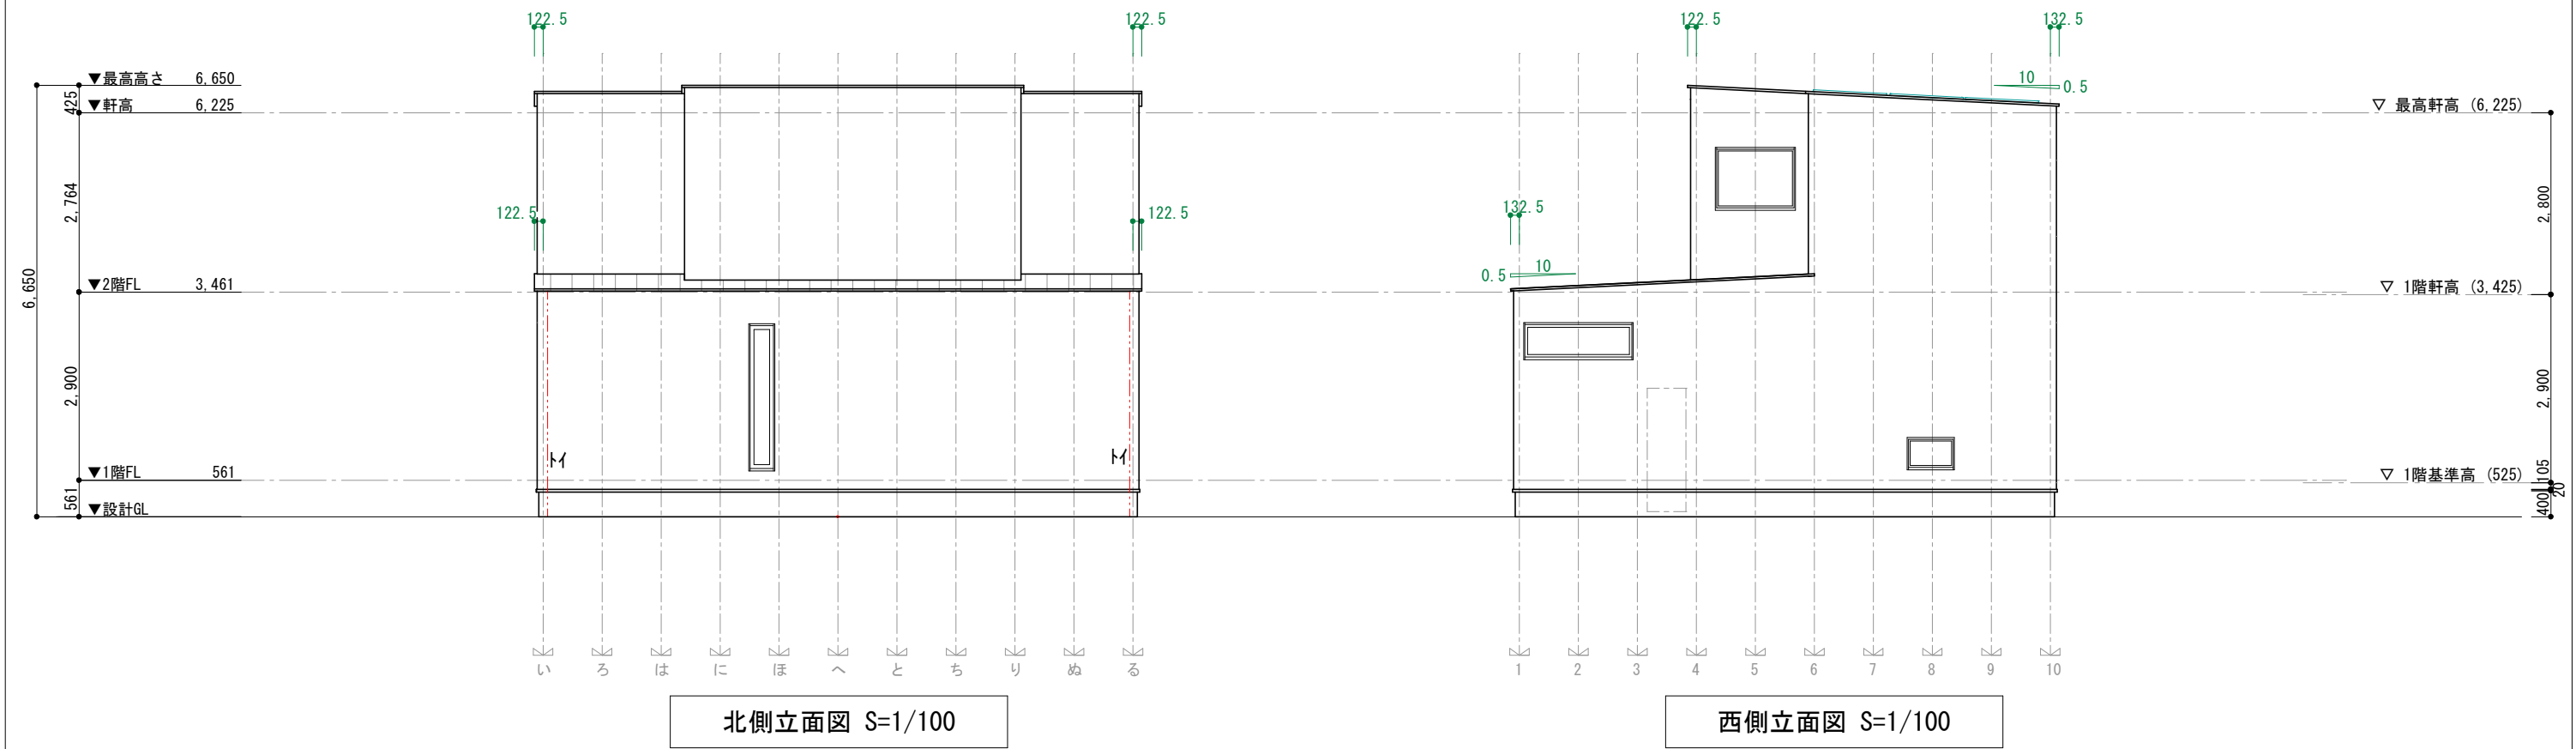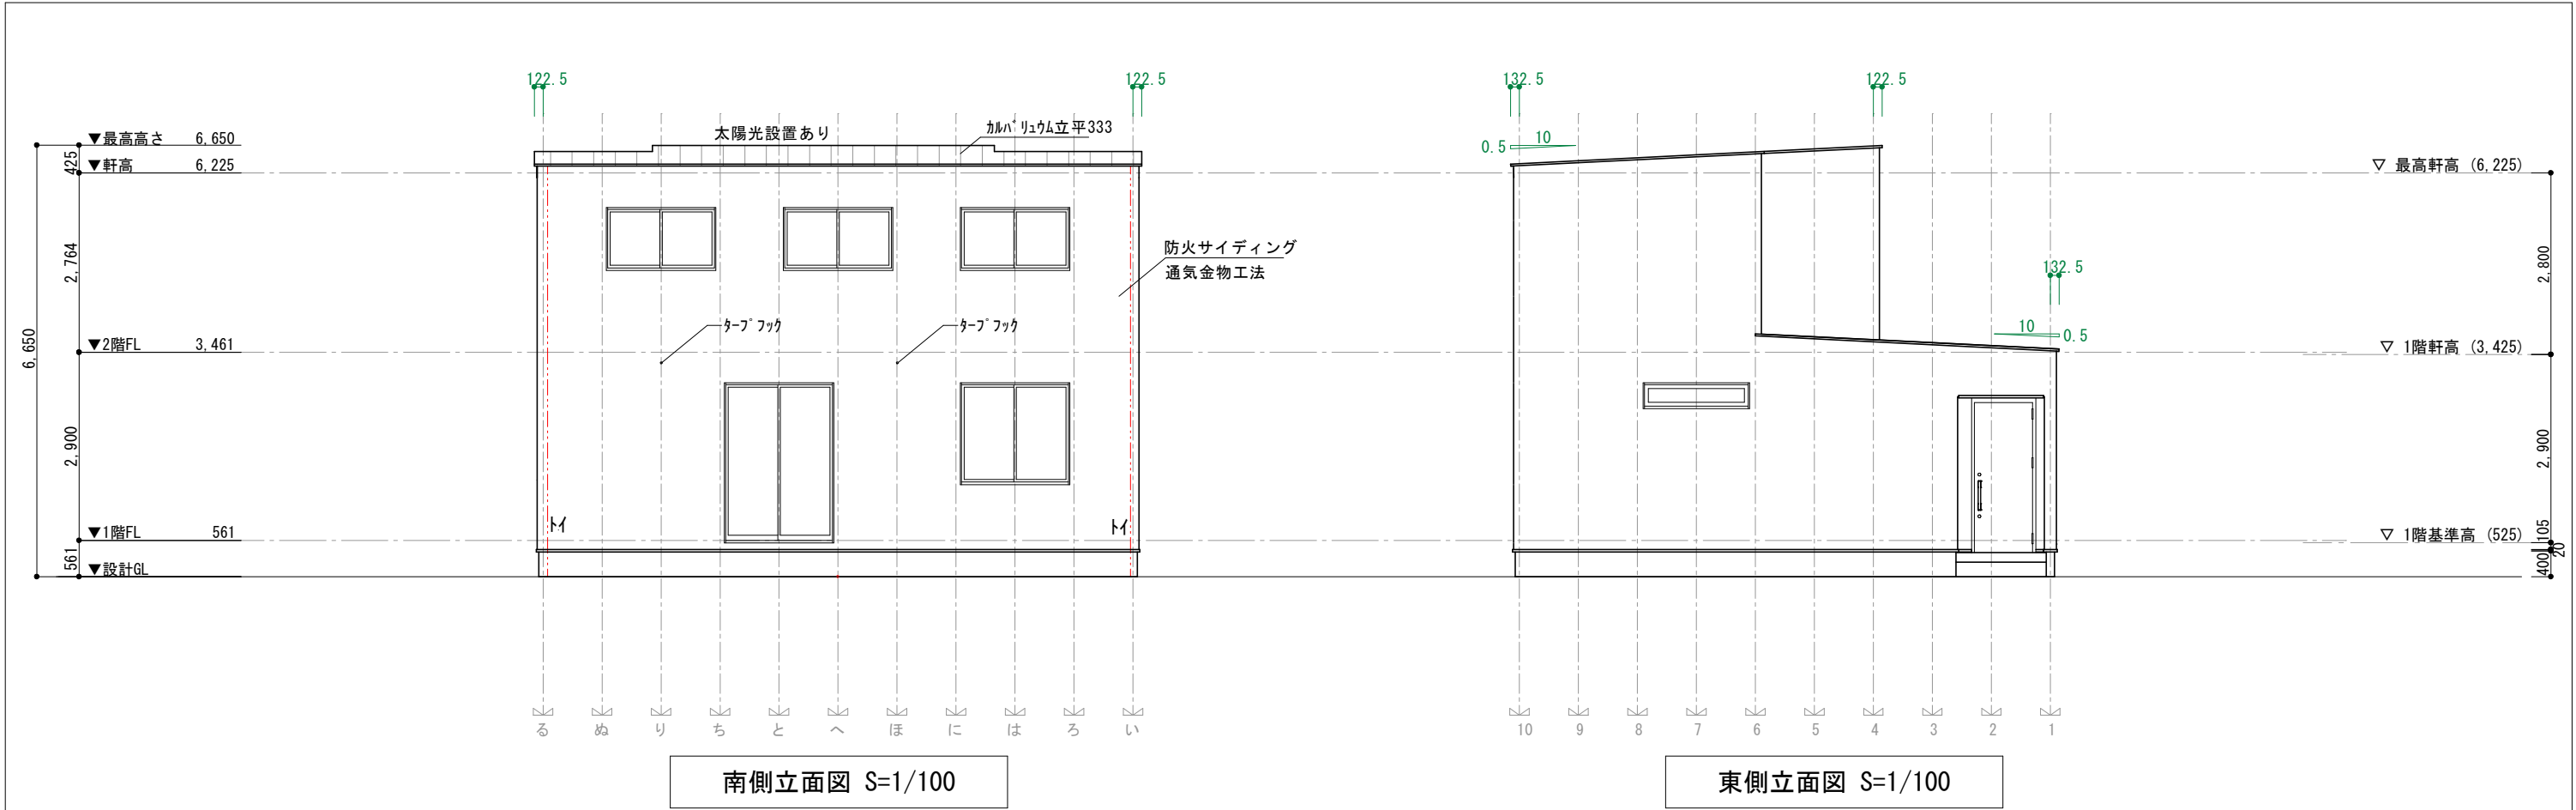



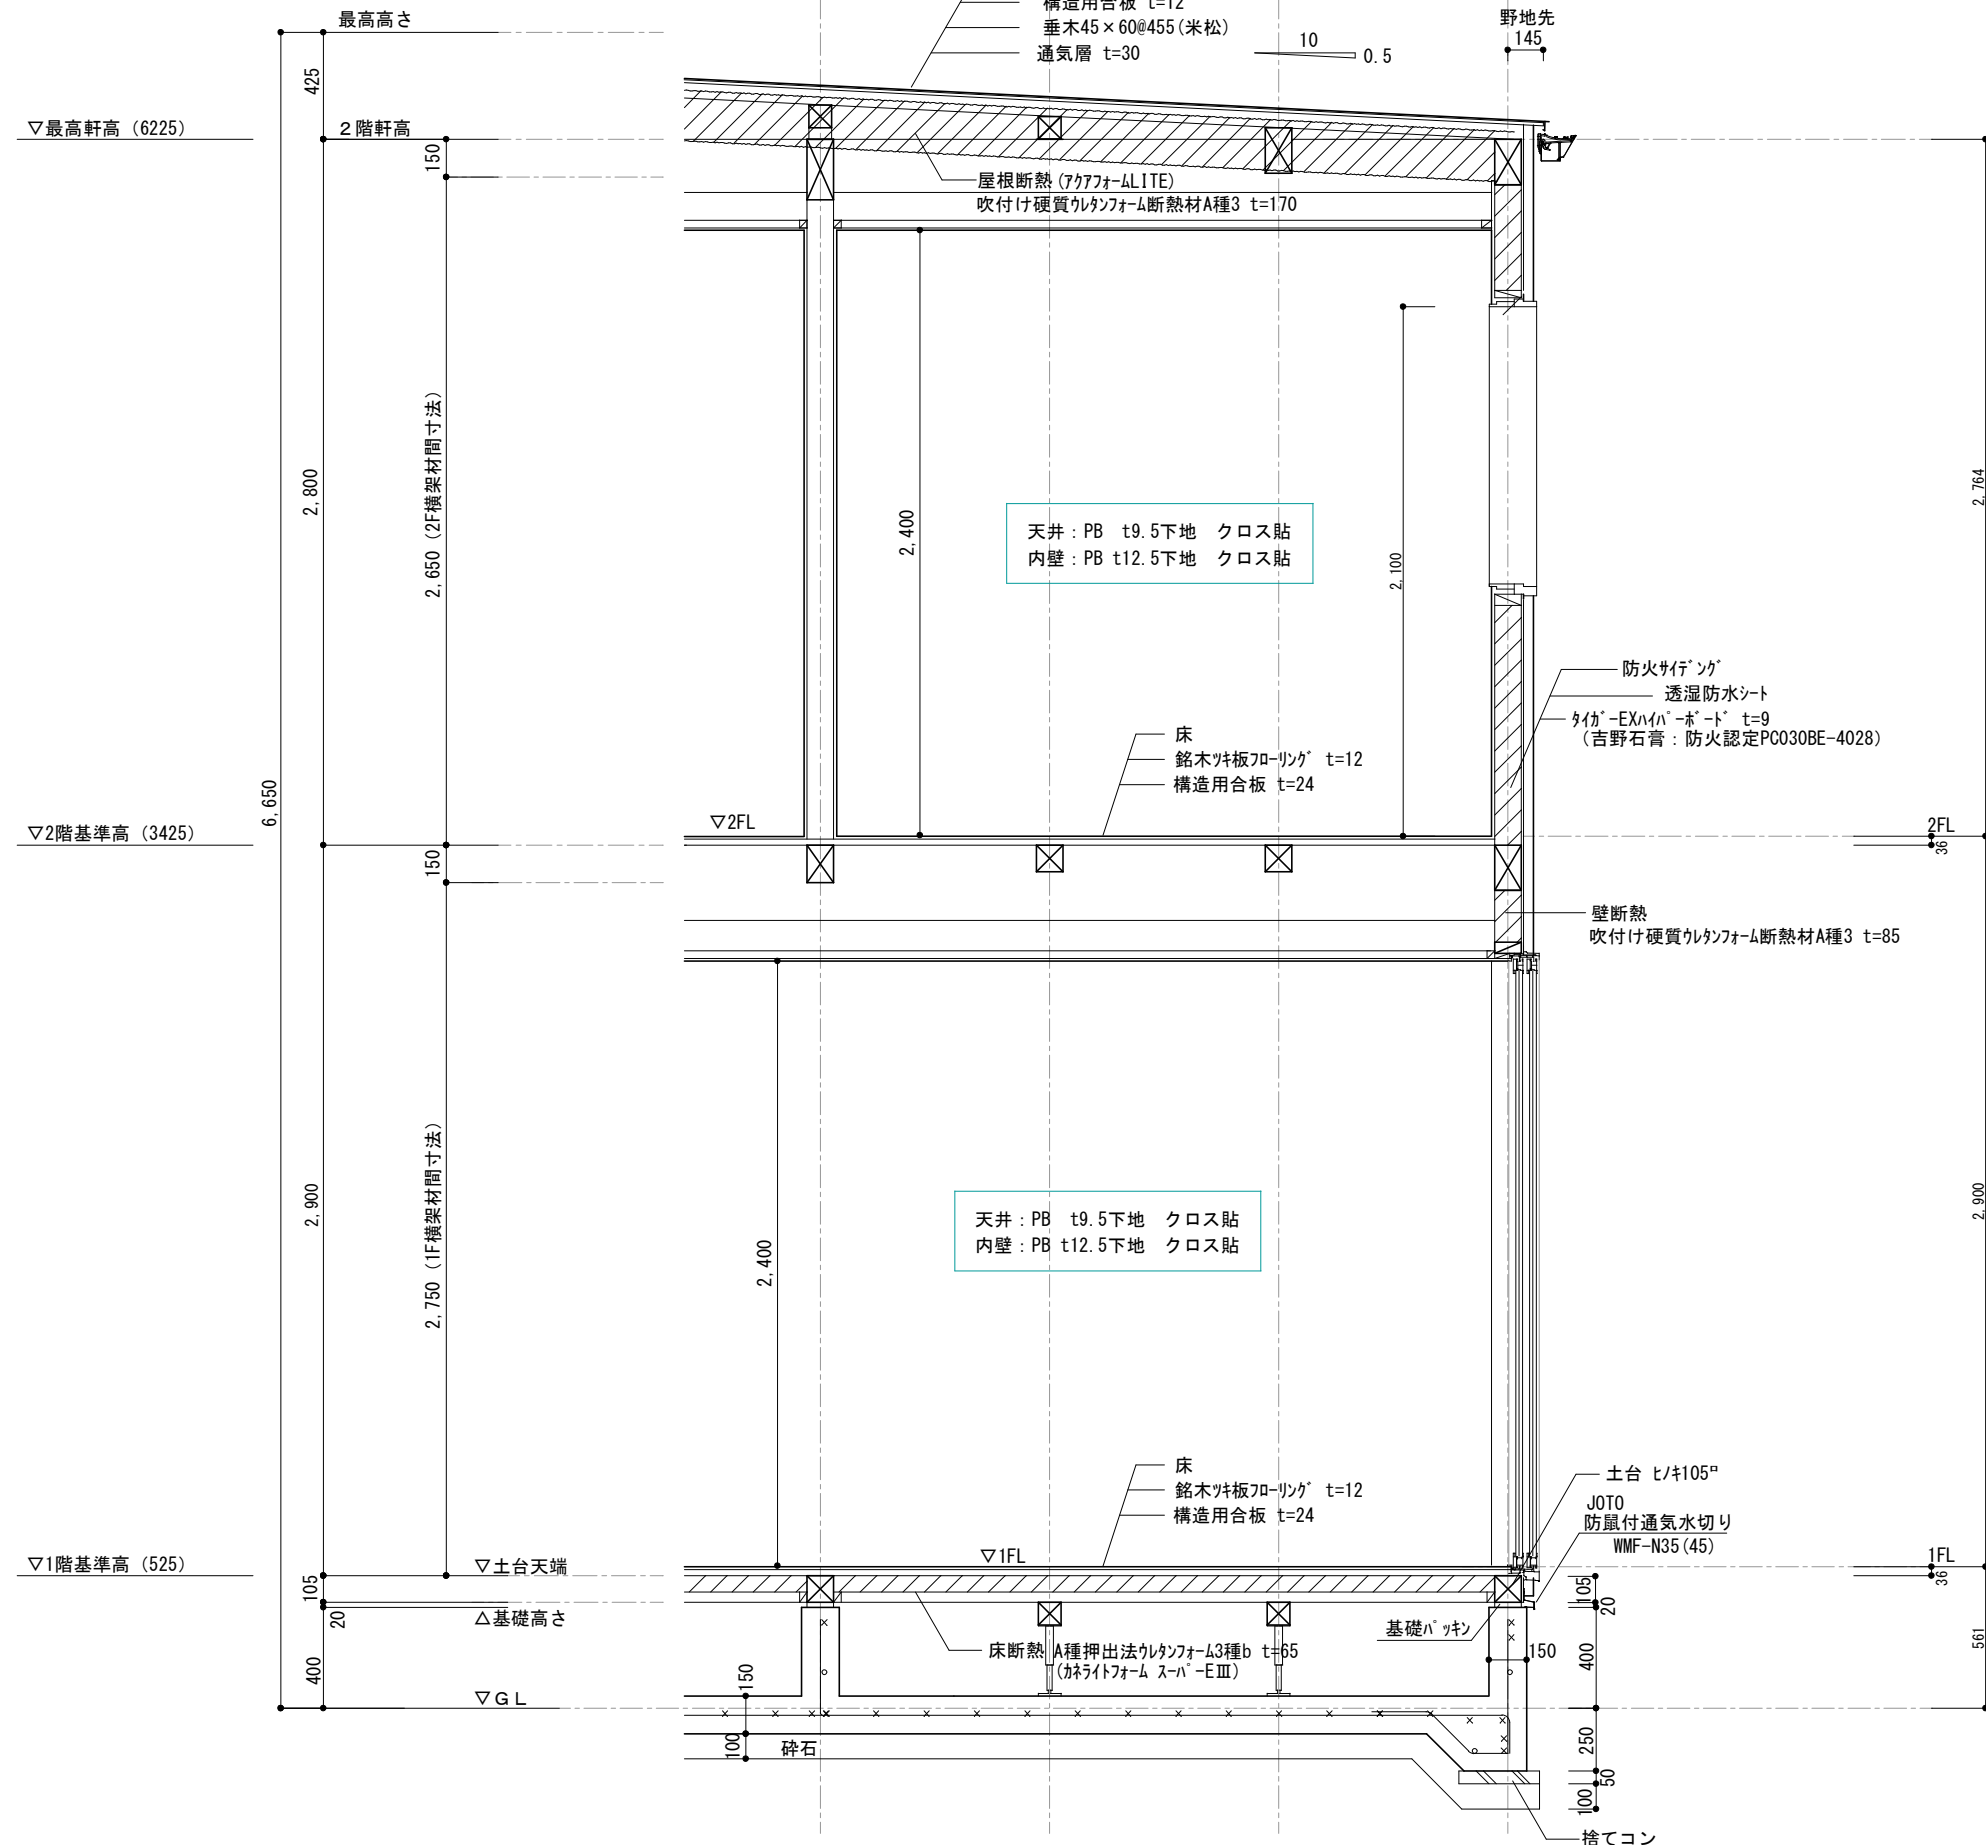

|    |                                                                          |                                                                                     |   |                   |                   |  |    |    |    |     |
|----|--------------------------------------------------------------------------|-------------------------------------------------------------------------------------|---|-------------------|-------------------|--|----|----|----|-----|
| 訂正 | 浜岡一級総合設計事務所<br>一級建築士事務所 静岡県知事登録第 (10)2441 号<br>一級建築士 大臣登録第 365879 号 西原利昌 |  | 株式会社 LIFEFUND InDesign office 一級建築士事務所<br>事務所登録 (2) 第7595号 一級建築士登録 第179770号 鈴木 達男<br>〒432-8023 静岡県浜松市中央区鴨江3丁目70番23号 | 年月日<br>2024.11.08 | 件名<br>伊藤友章様邸 新築工事 |  | 設計 | IC | 工事 | 図番  |
|    |                                                                          |                                                                                     |   | 縮尺<br>1/100       | 図名<br>矩計図         |  | 倉田 |    | 青島 | A-5 |
|    |                                                                          |                                                                                     |   |                   |                   |  |    |    |    |     |

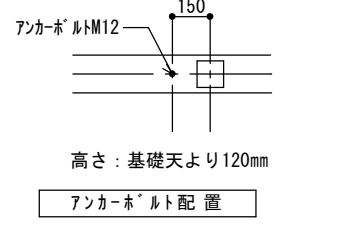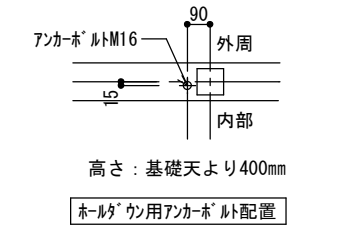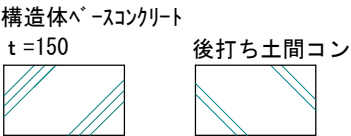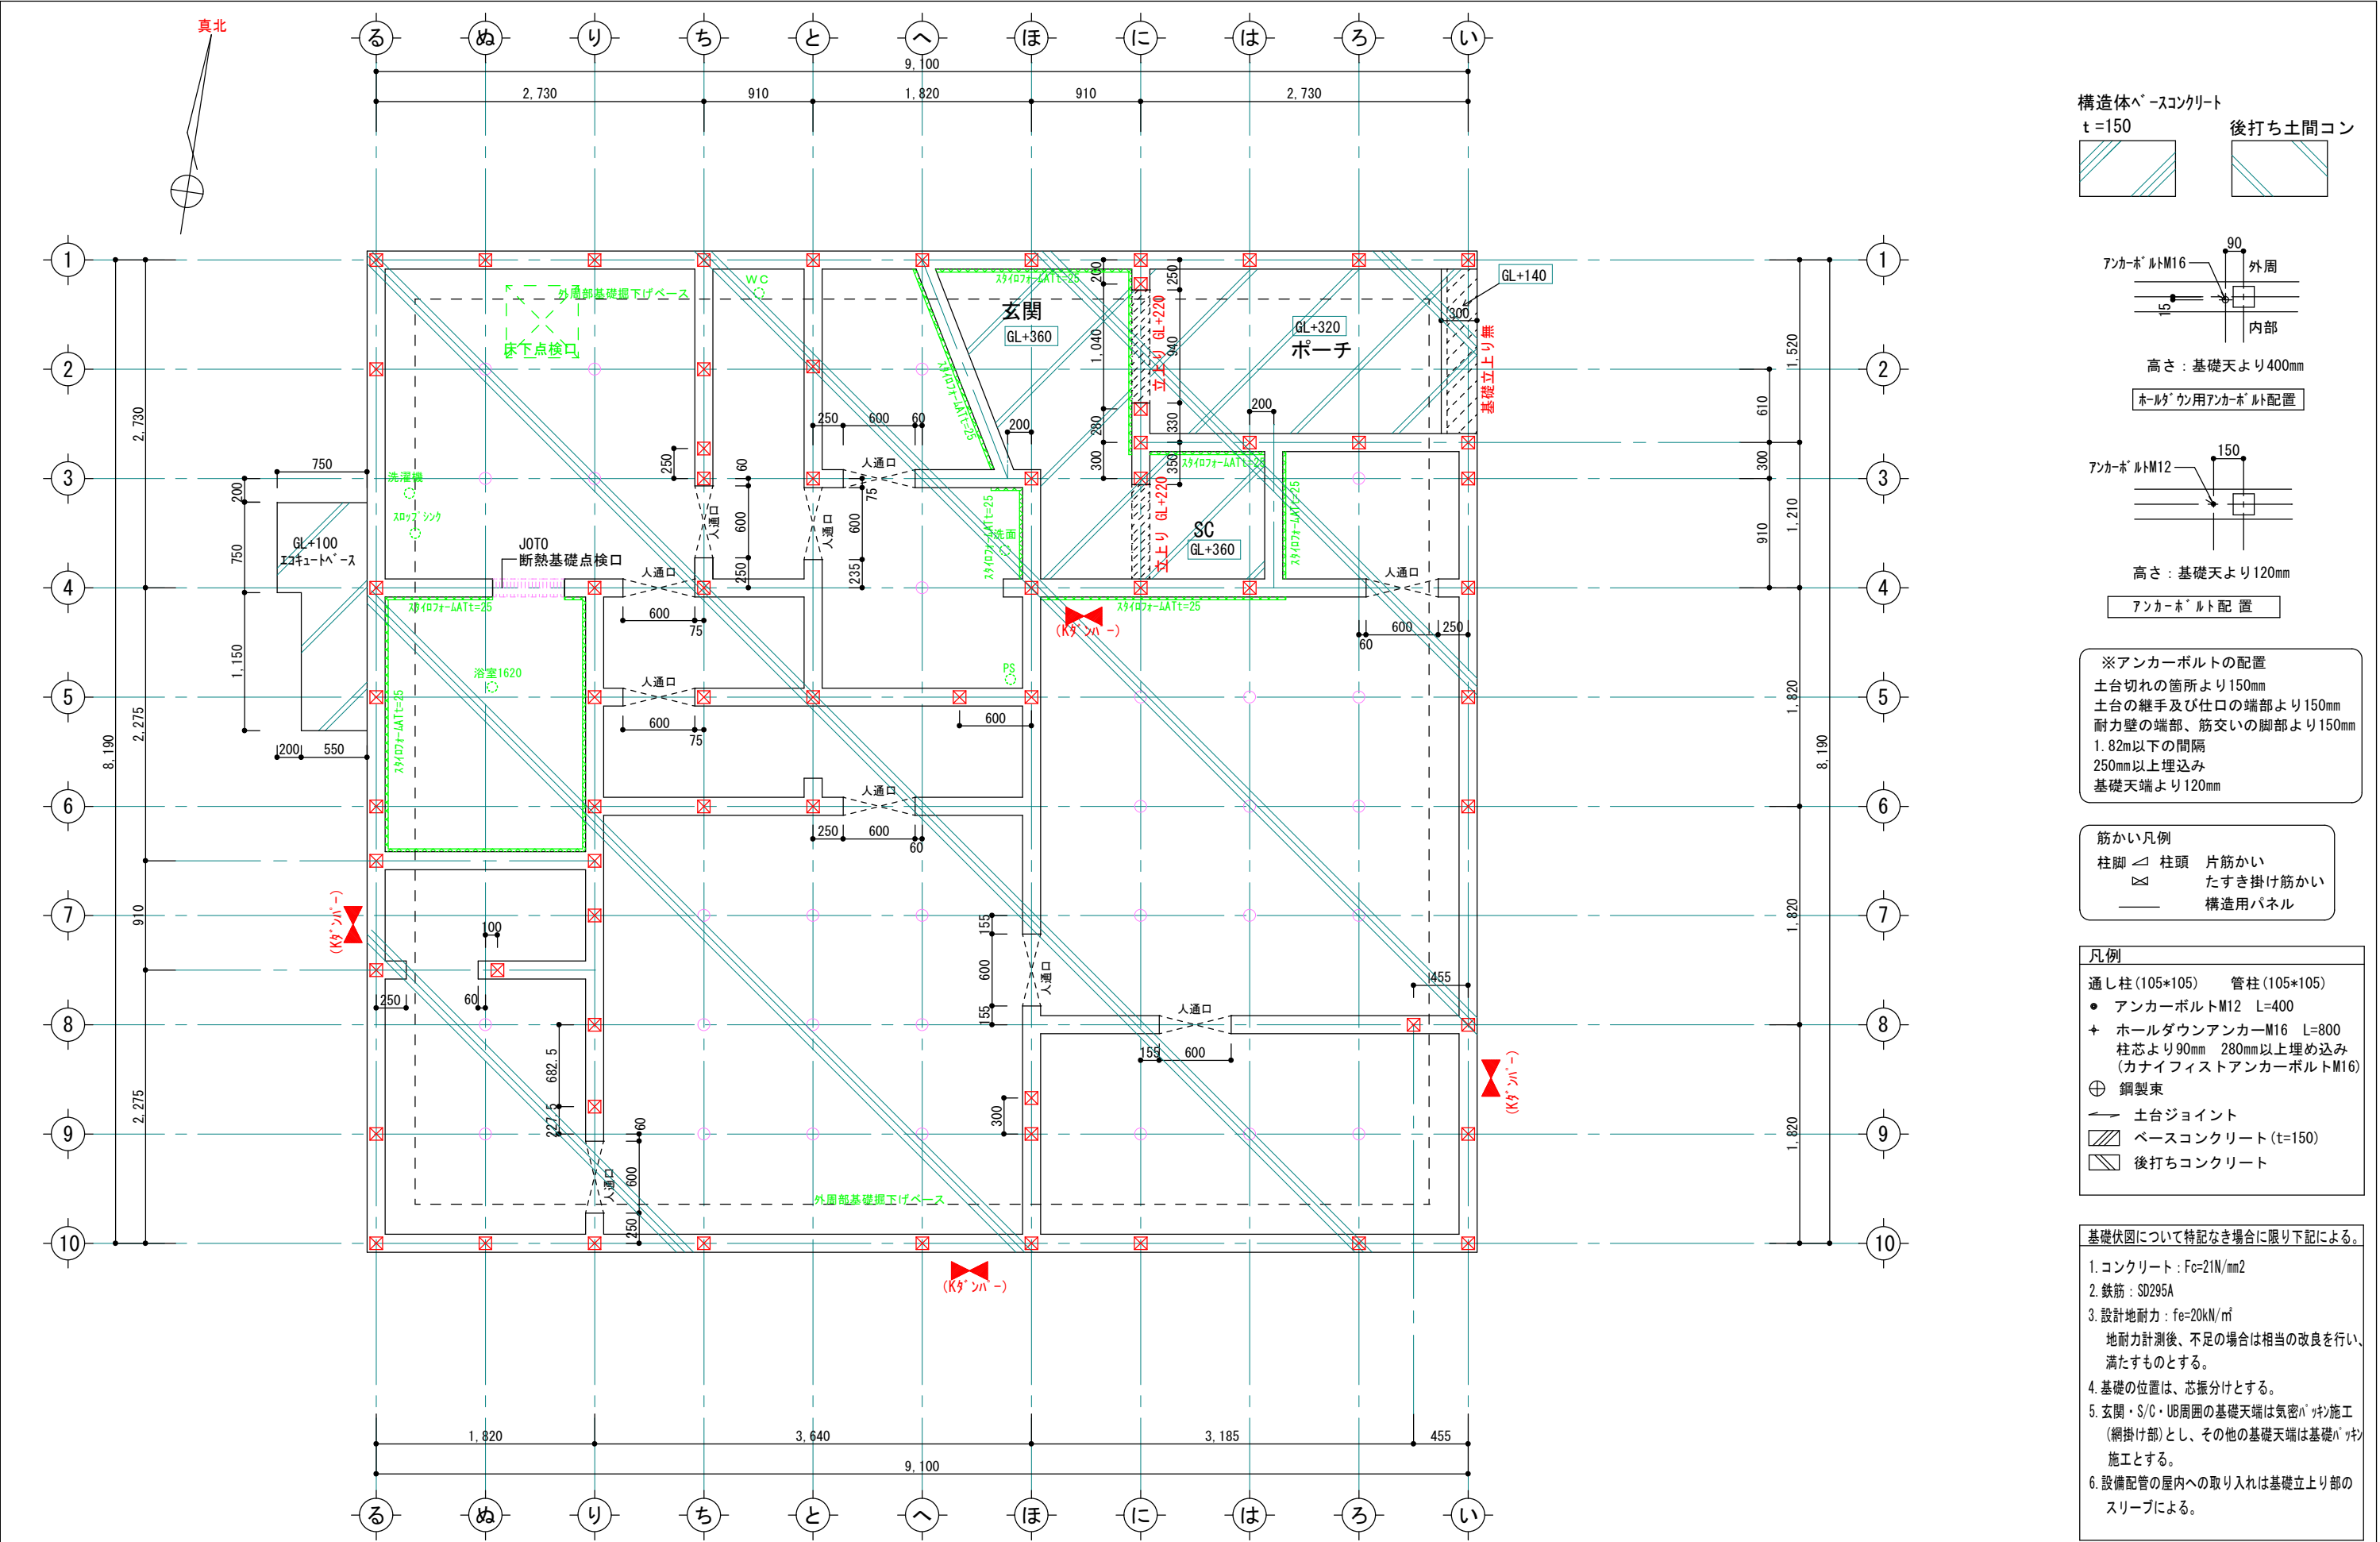

※アンカーボルトの配置  
土台切れの箇所より150mm  
土台の継手及び仕口の端部より150mm  
耐力壁の端部、筋交いの脚部より150mm  
1.82m以下の間隔  
250mm以上埋込み  
基礎天端より120mm

筋かい凡例  
柱脚 柱頭 筋かい  
たすき掛け筋かい  
構造用パネル

凡例  
通し柱 (105\*105) 管柱 (105\*105)  
● アンカーボルトM12 L=400  
+ ホールダウンアンカーM16 L=800  
柱芯より90mm 280mm以上埋め込み  
(カナイフイストアンカーボルトM16)  
⊕ 鋼製束  
→ 土台ジョイント  
ベースコンクリート (t=150)  
後打ちコンクリート

基礎伏図について特記なき場合に限り下記による。

1. コンクリート :  $F_c=21N/mm^2$
2. 鉄筋 : SD295A
3. 設計地耐力 :  $f_e=20kN/m^2$   
地耐力計測後、不足の場合は相当の改良を行い、満たすものとする。
4. 基礎の位置は、芯振分けとする。
5. 玄関・S/C・UB周囲の基礎天端は気密パッキン施工 (網掛け部)とし、その他の基礎天端は基礎パッキン施工とする。
6. 設備配管の屋内への取り入れは基礎立上り部のスリーブによる。

