


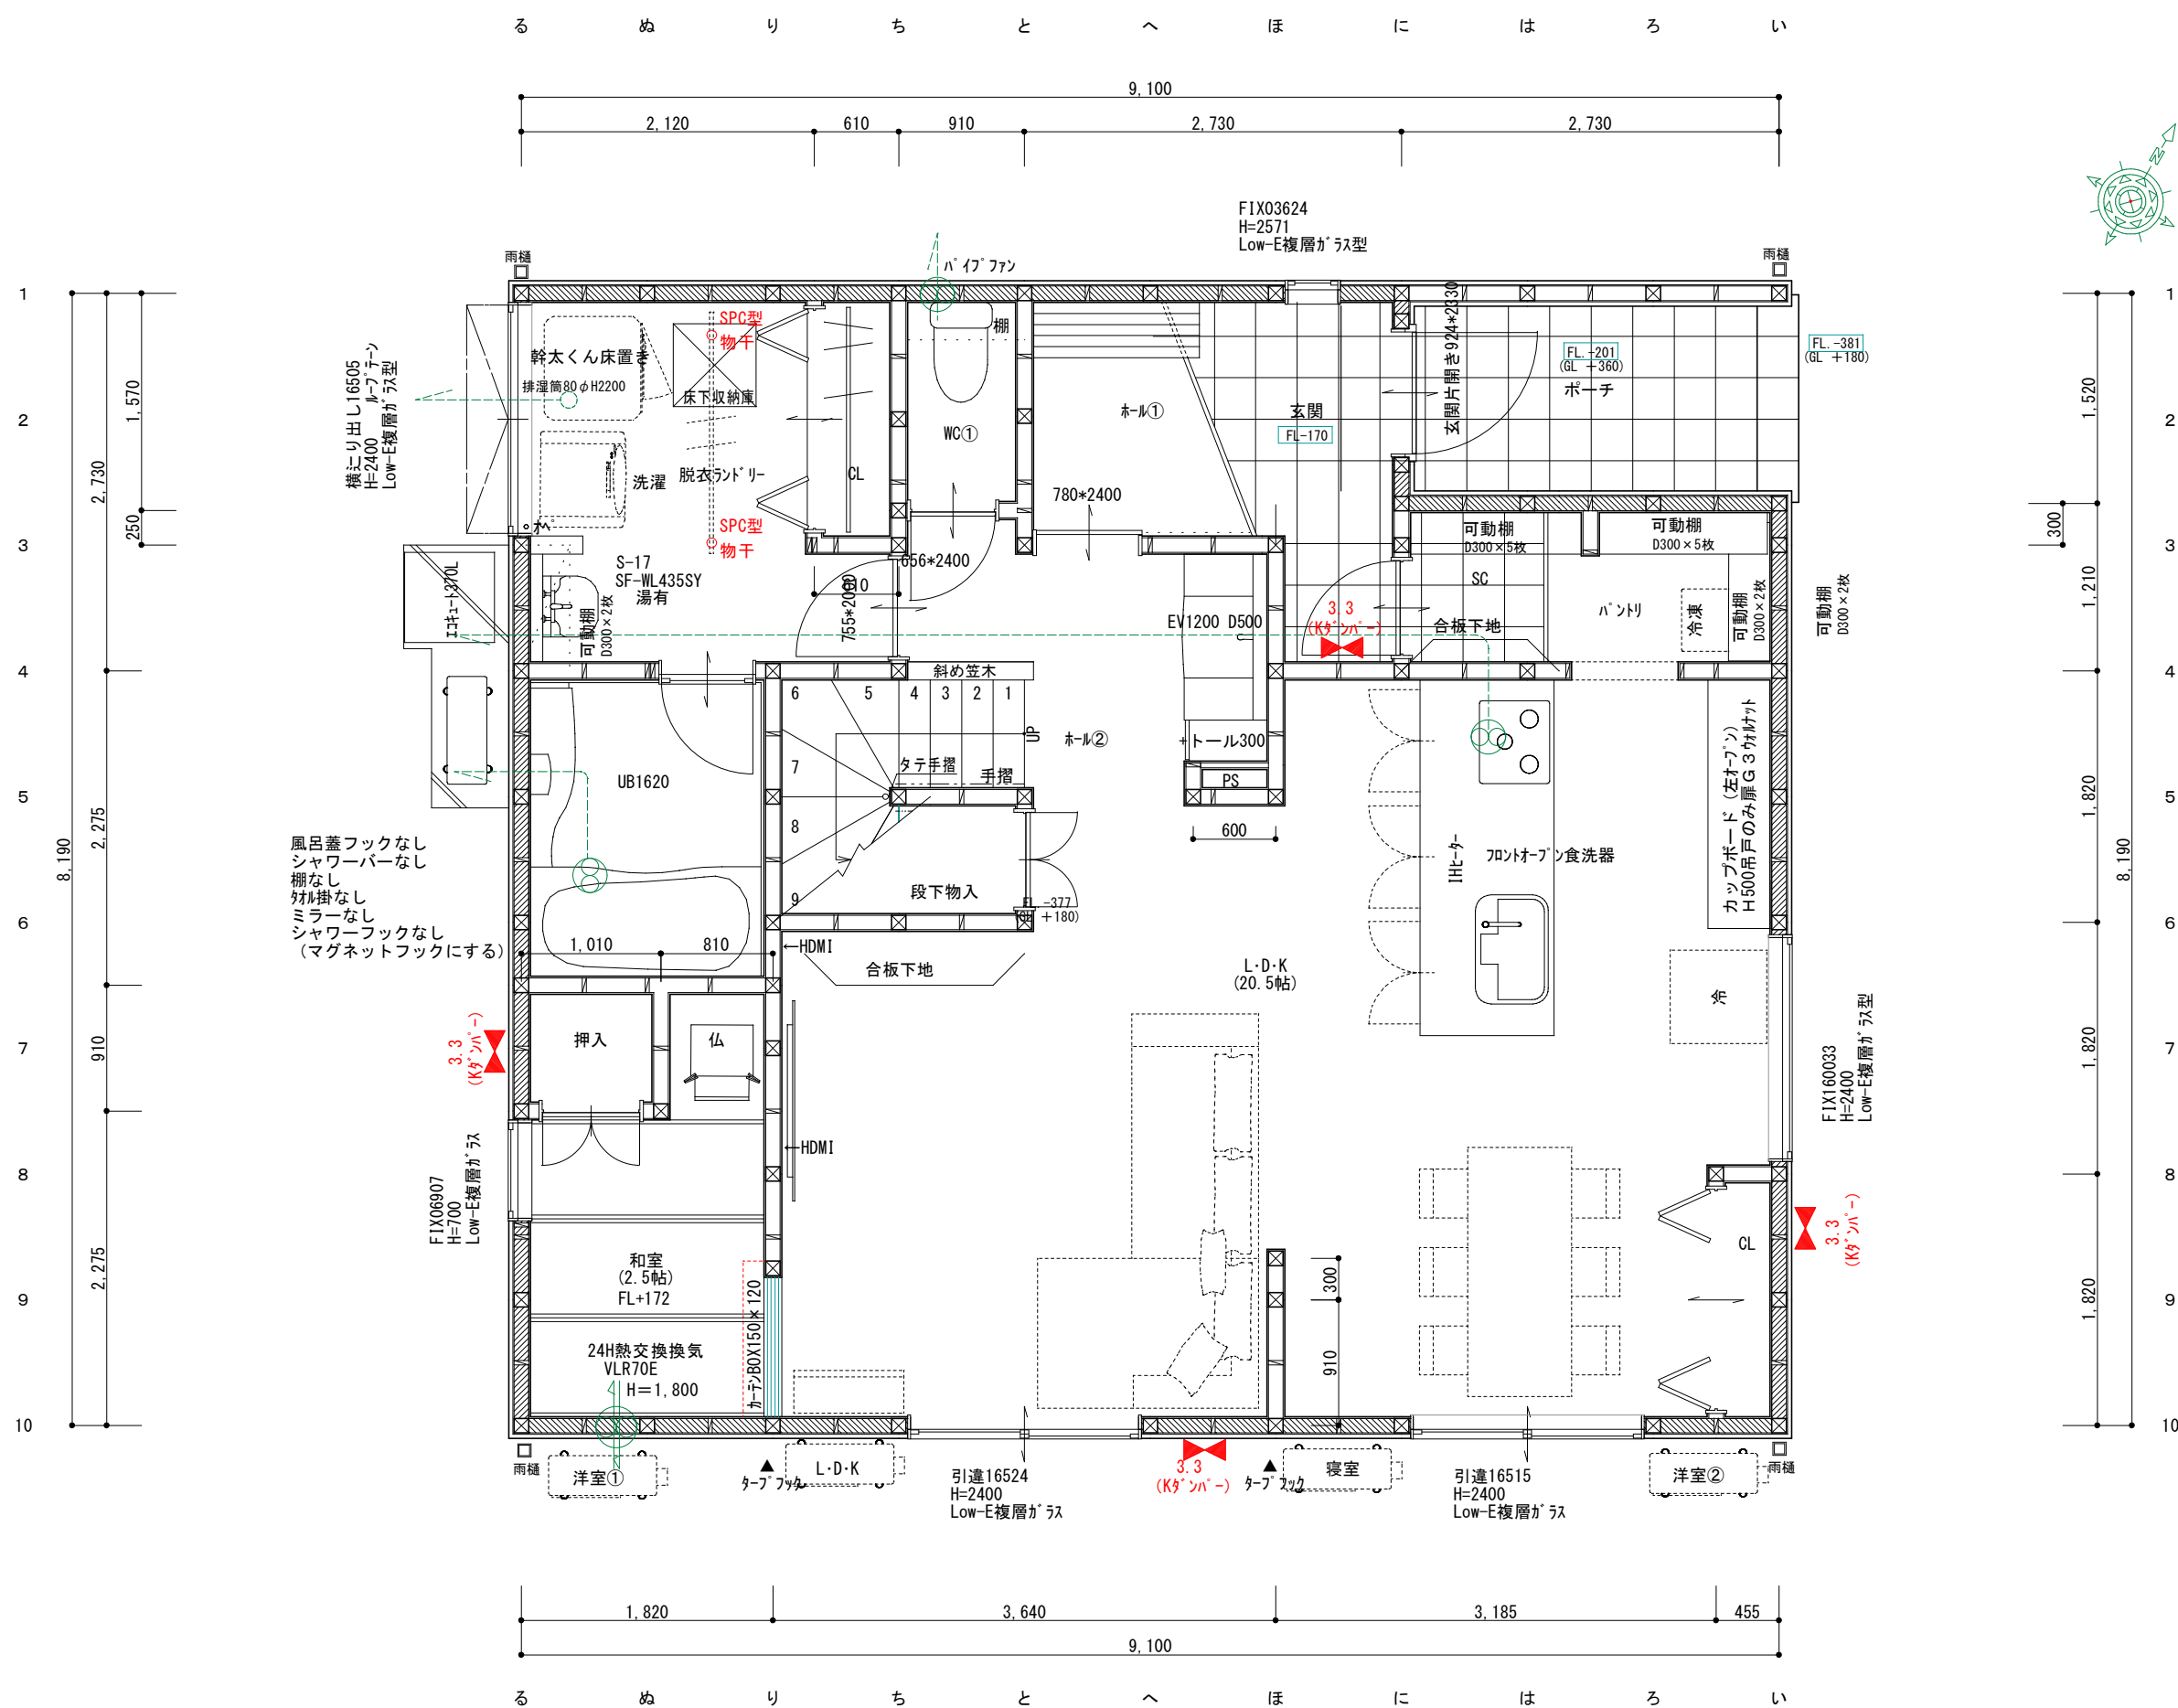

壁付付 住宅用火災報知器		数量
 熱感知	熱感知器	電池式(単独型)
		露出型
壁付付 住宅用火災報知器		数量
 煙感知	煙感知器	電池式(単独型)
		露出型

※ 煙感知器は壁・梁より600mm以上離す
壁に取付ける場合、
天井から150mm以上500mm以内離す
換気扇・エアコン吹出口から1500mm以上離す
※ 全室LED照明とする。
※ 標準天井高さ2,400

*** 凡例**

 管柱 (105 × 105)

 K $\frac{9}{10}$ ° $\frac{1}{2}$ ° -
(3.30倍 FRM-0641)

 片筋違い
(2.00倍 45 × 90)
(例 左:柱脚 右:柱頭)

 たすき掛筋違い
(4.00倍 45 × 90)

構造用合板 (2.50倍)
(t=9 $\frac{1}{2}$ イフト)

 床点検口

 天井点検口

 換気扇

 熱交換換気扇VLR-70

コスモワイド スクエア スマートデザイン (外部)	
凡例	
①	コンセント 1ヶ口
②	コンセント 2ヶ口
③	コンセント 3ヶ口
1 E T	コンセント1ヶ口接地ターミナル付
2 E T	コンセント2ヶ口接地ターミナル付
WP	防水型 エアコン用コンセント
	200V用コンセント
WP	防雨入換プレート
	スイッチ
●	3路スイッチ
●	4路スイッチ
⊗	直結電源
TV	テレビ取出し口
TEL	電話取出し口 (テレホンガイド)
LAN	LAN取出し口 (テレホンガイド)
	壁埋め
	リモコン (給湯関係・フルボ)
	メーター
	分電盤
	チャイム

※ACコンセント天井付け
※TVアンテナ工事
※スイッチはFL+1100、コンセントはFL+200

訂 正	浜 岡 一 級 総 合 設 計 事 務 所 一級建築士事務所 静岡県知事登録第 (10)2441 号 一級建築士 大臣登録第 365879 号 西原利昌	LIFEFUND PG HOUSE	株式会社 LIFEFUND InDesign office 一級建築士事務所 事務所登録 (2)第7595号 一級建築士登録 第179770号 鈴木 達男 〒432-8023 静岡県浜松市中央区鳴江3丁目70番23号	年 月 日	件 名 伊藤友章様邸 新築工事		設計	IC	工事	図 番
				2024. 10. 3						
							1/50	1階電気配線図		倉田

