



壁付け 住宅用火災報知器			数量
H 熱感知	電池式 (単独型)		
	露出型		
壁付け 住宅用火災報知器			数量
S 煙感知	電池式 (単独型)		
	露出型		


※ 煙感知器は壁・梁より600mm以上離す
壁に取付ける場合、
天井から150mm以上500mm以内離す
換気扇・エアコン吹出口から1500mm以上離す
※ 全室LED照明とする。
※ 標準天井高さ2,400

*** 凡例**


- 管柱 (105×105)
- Kダクト (3.30倍 FRM-0641)
- 片筋違い (2.00倍 45×90)
(例 左:柱脚 右:柱頭)
- たすき掛筋違い (4.00倍 45×90)
- 構造用合板 (2.50倍)
(t=9 タイタ)
- 床点検口
- 天井点検口
- 換気扇
- 熱交換換気扇VLR-70

コスモワイド スクエア スマートデザイン (外部)		
凡例	1	コンセント 1ヶロ
2	コンセント 2ヶロ	
3	コンセント 3ヶロ	
1ET	コンセント1ヶロ接地ターミナル付	
2ET	コンセント2ヶロ接地ターミナル付	
WP	コンセント 防水型	
	エアコン用コンセント	
	200V用コンセント	
WP	防雨入線プレート	
	スイッチ	
3	3路スイッチ	
4	4路スイッチ	
	直結電源	
TV	テレビ取出口	
TEL	電話取出口 (テレホンガイド)	
LAN	LAN取出口 (テレホンガイド)	
	壁照明	
	リモコン (給湯関係・ルフロ)	
	メーター	
	分電盤	
	チャイム	



※ACコンセント天井付け
※TVアンテナ工事
※スイッチはFL+1100、コンセントはFL+200

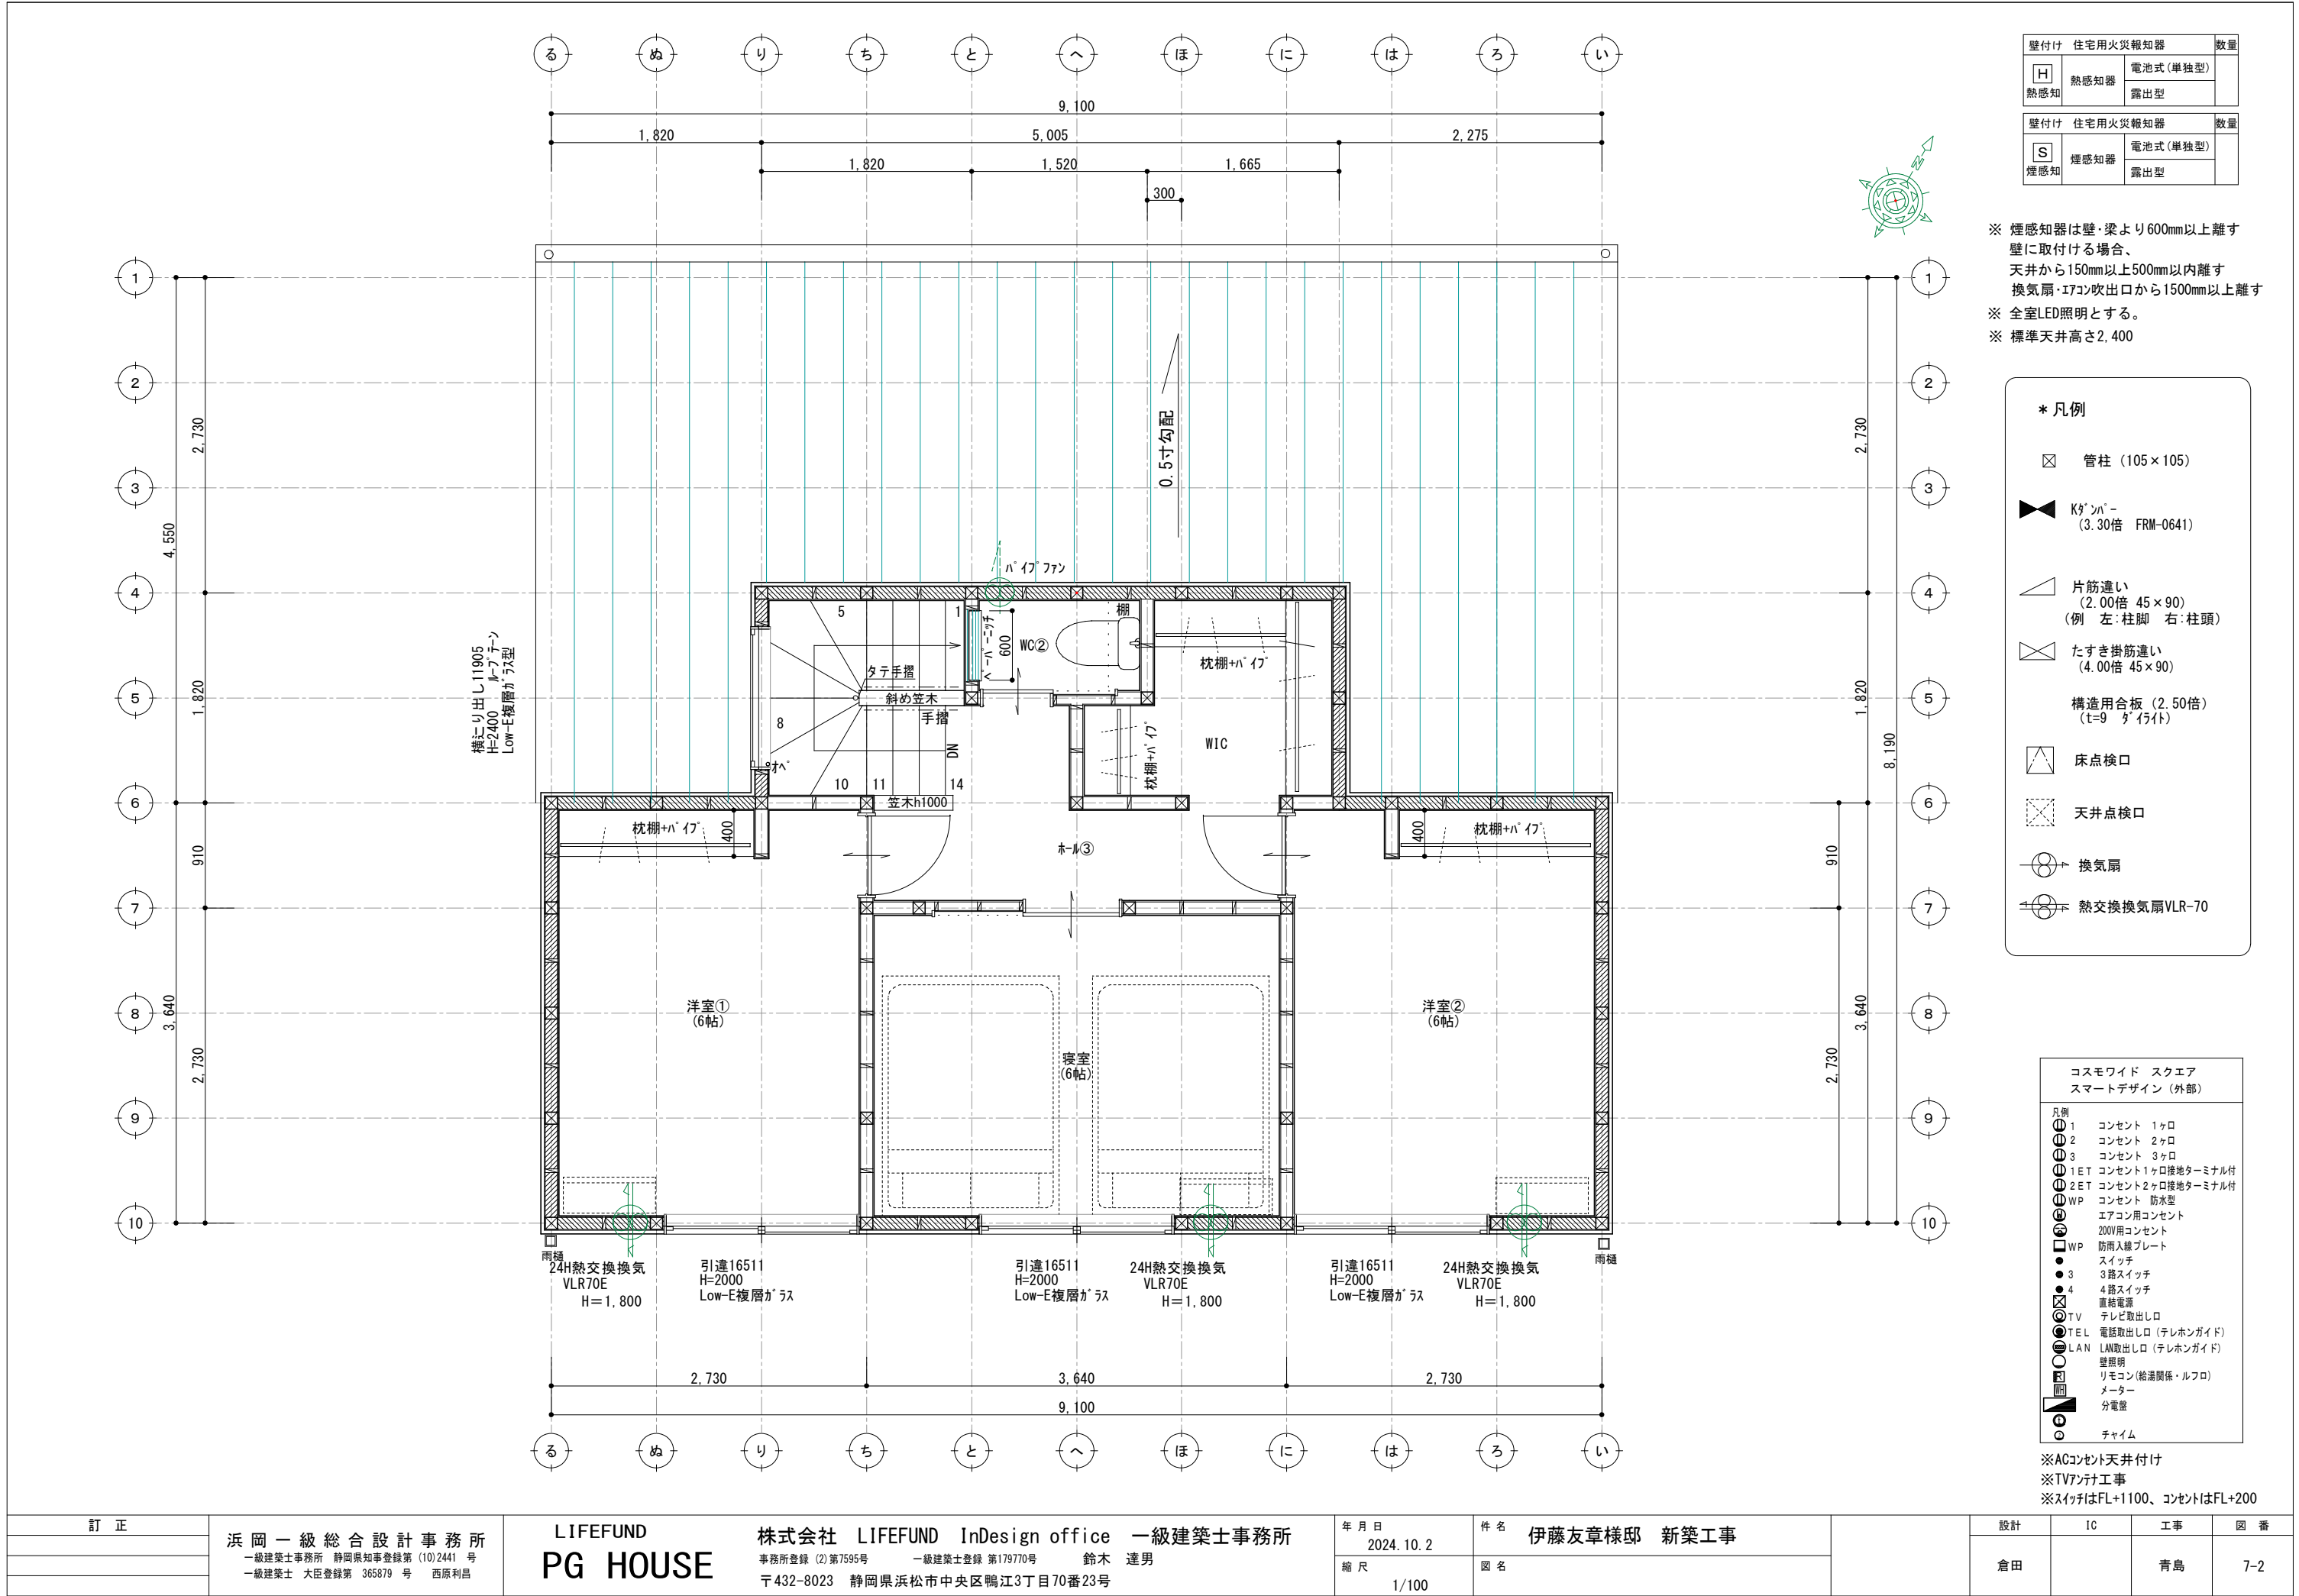

2階電気配線図

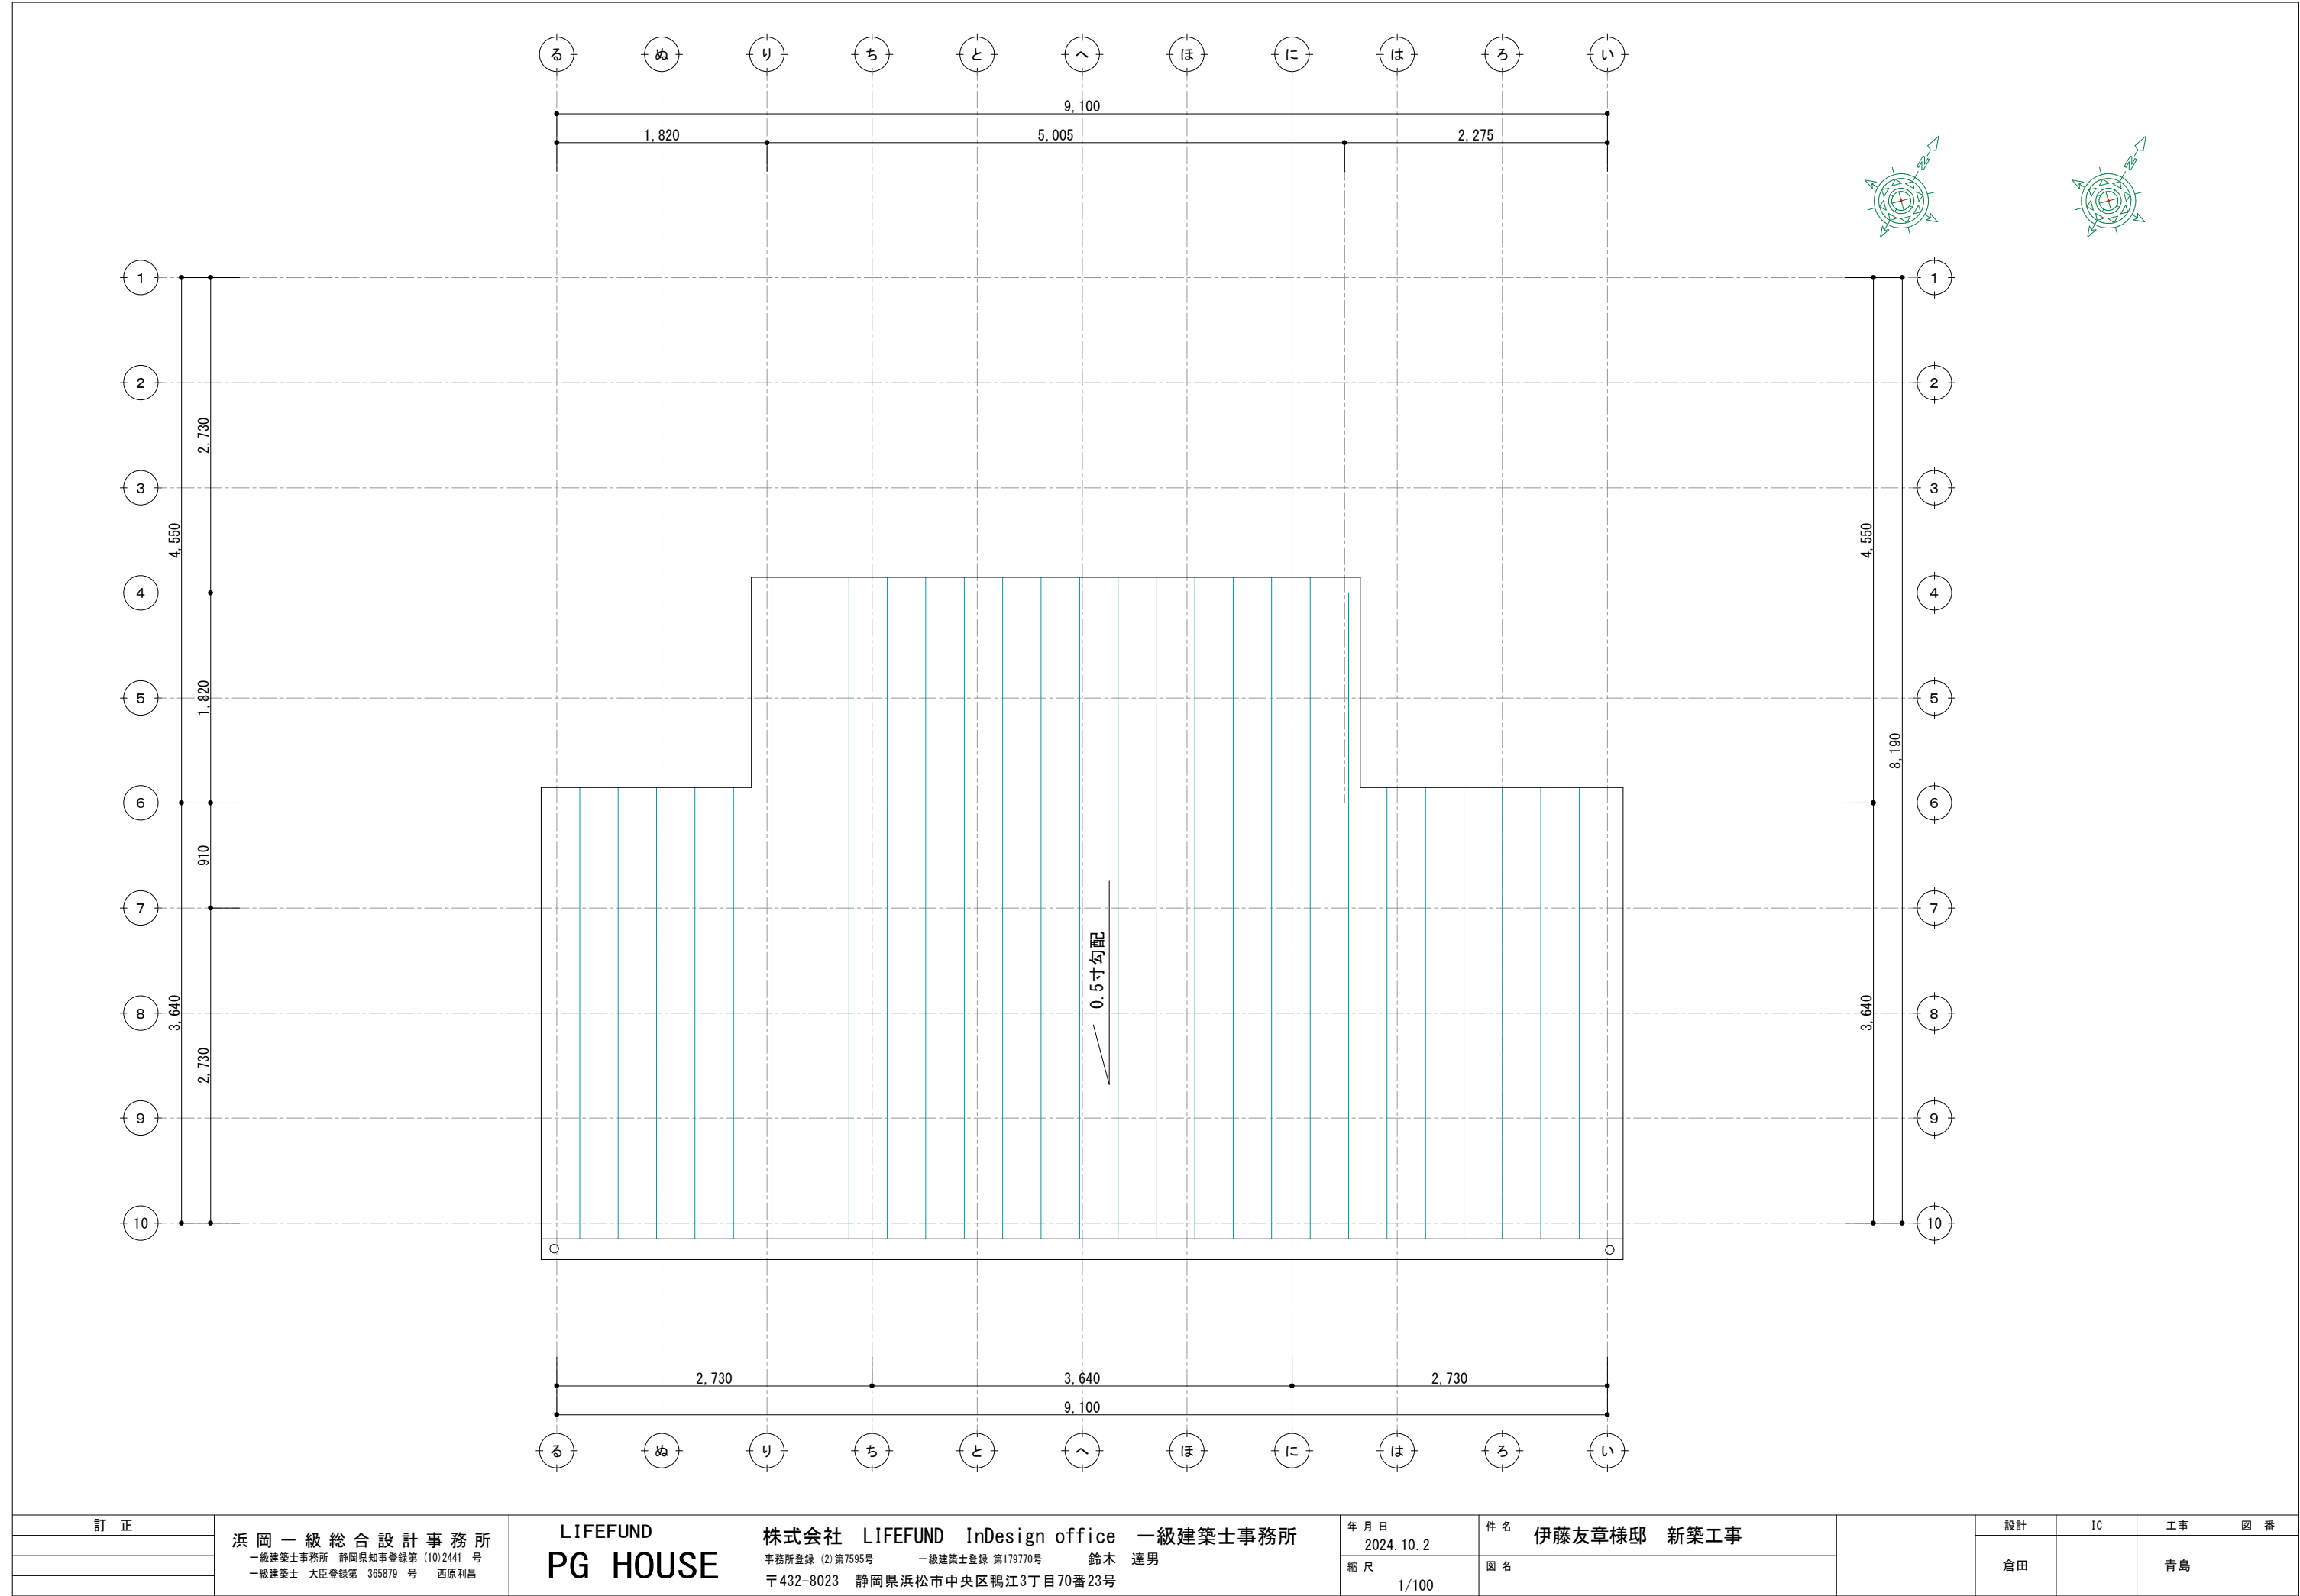

訂 正	浜 岡 一 級 総 合 設 計 事 務 所 一級建築士事務所 静岡県知事登録第 (10)2441 号 一級建築士 大臣登録第 365879 号 西原利昌	LIFEFUND PG HOUSE	株式会社 LIFEFUND InDesign office 一級建築士事務所 事務所登録 (2)第7595号 一級建築士登録 第179770号 鈴木 達男 〒432-8023 静岡県浜松市中央区鴨江3丁目70番23号	年月日 2024. 10. 2 縮 尺 1/100	件 名 伊藤友章様邸 新築工事 図 名		設計	IC	工事	図 番
							倉田		青島	

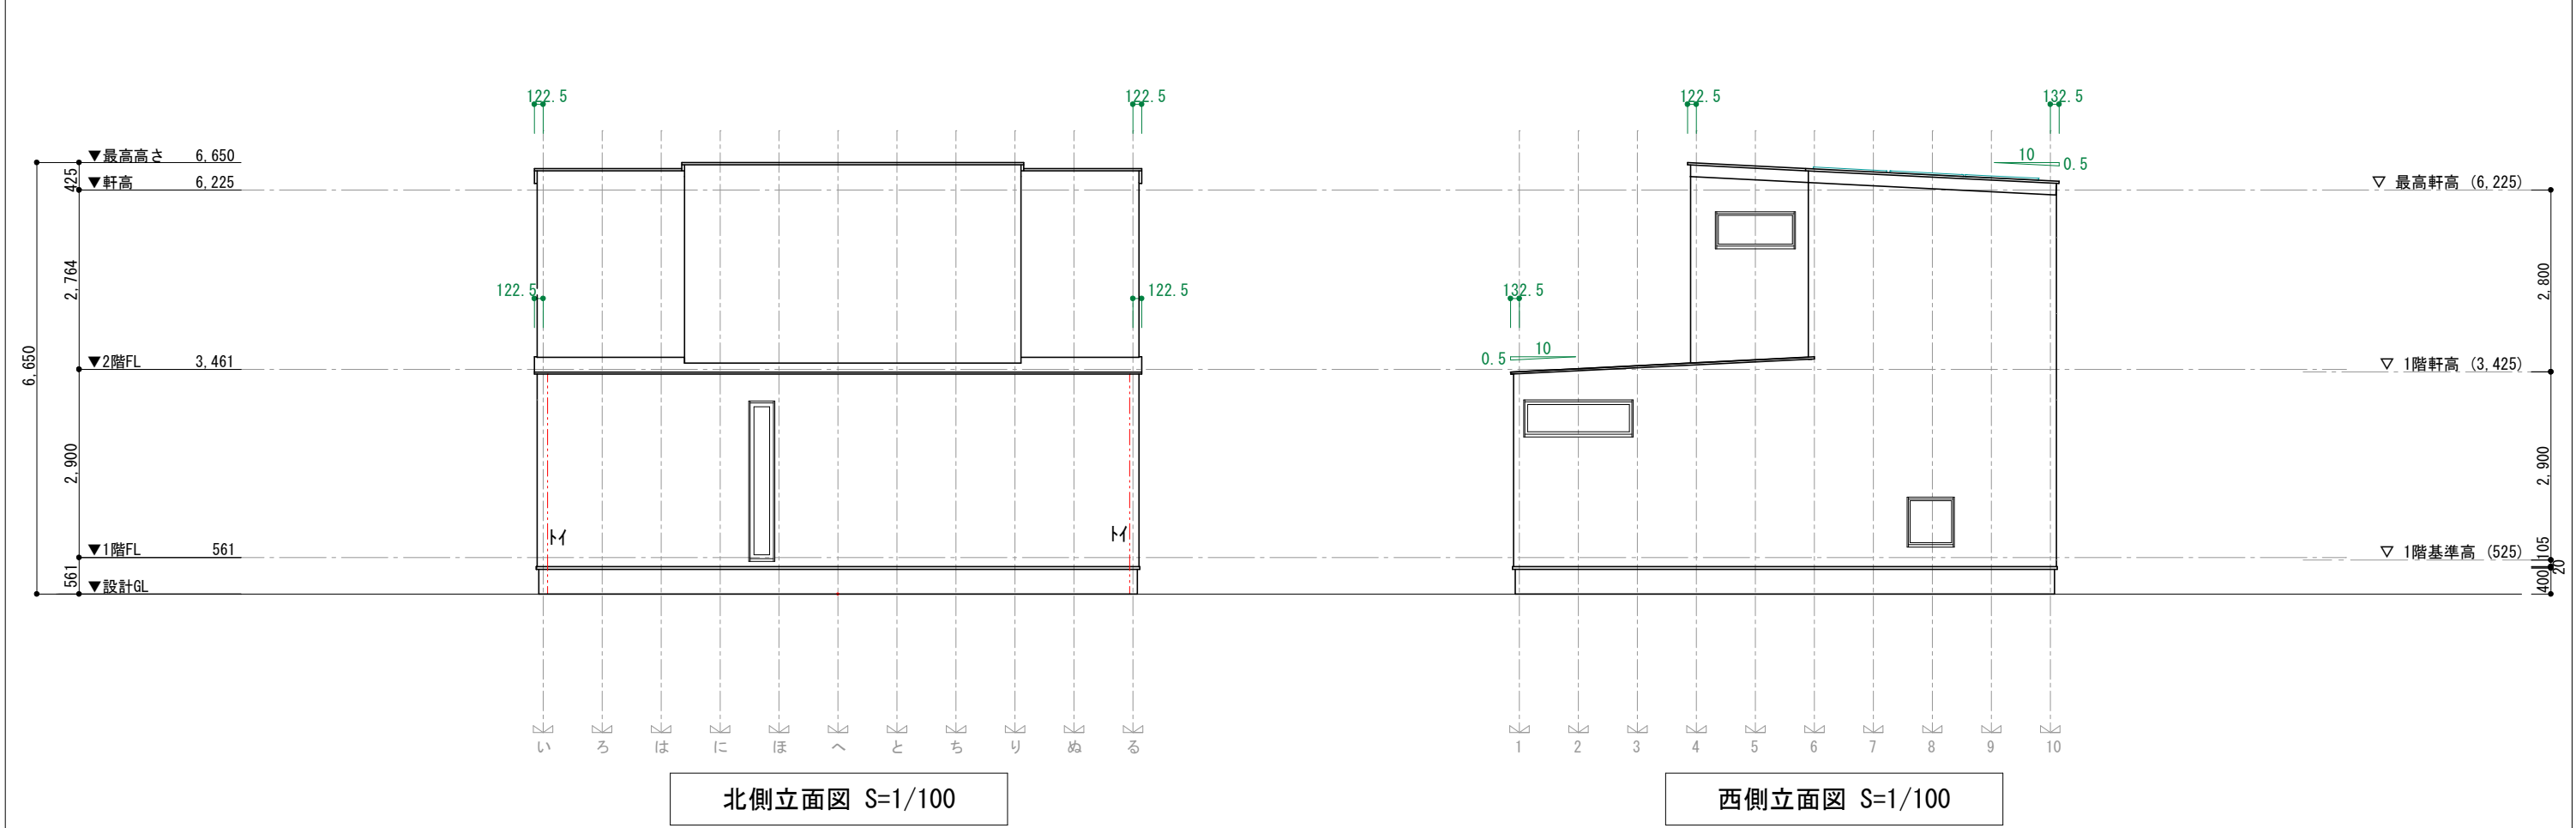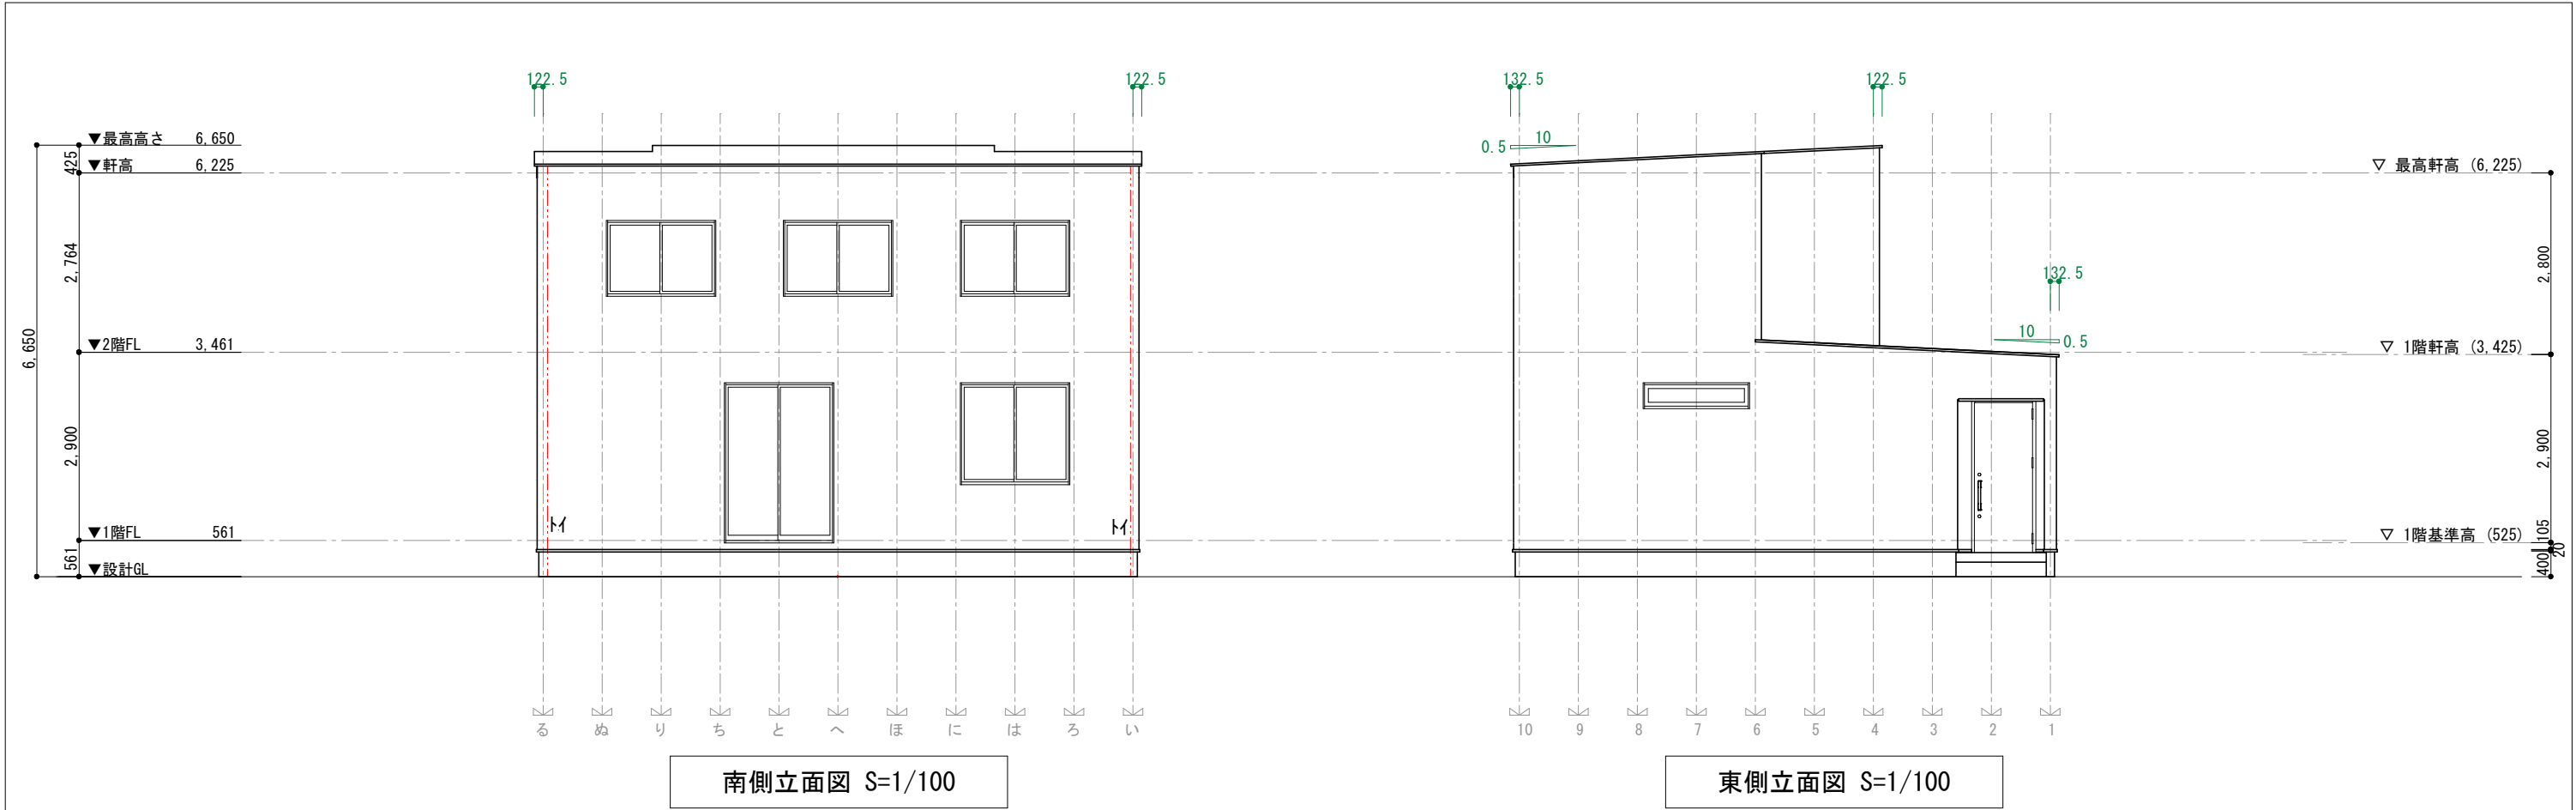

訂 正	浜 岡 一 級 総 合 設 計 事 務 所	LIFEFUND PG HOUSE	株式会社 LIFEFUND InDesign office 一級建築士事務所 事務所登録 (2) 第7595号 一級建築士登録 第179770号 鈴木 達男 〒432-8023 静岡県浜松市中央区鴨江3丁目70番23号	年 月 日	件 名		設計	IC	工事	図 番
	一級建築士事務所 静岡県知事登録第 (10)2441 号			2024. 10. 2	伊藤友章様邸 新築工事		倉田		青島	4
	一級建築士 大臣登録第 365879 号 西原利昌			縮 尺	図 名					