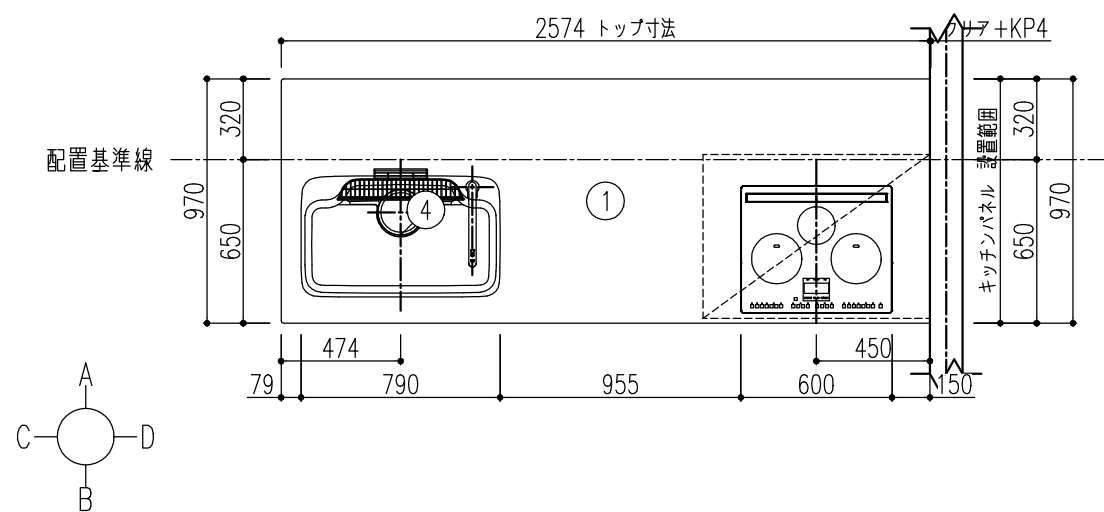



[illegible]

【 ご注意 】


- 記載のキャビネット寸法は扉前面までの呼び寸法です。キャビネット本体の寸法・扉厚み等は商品ガイドの巻末資料をご確認ください。
- 記載のワークトップ、カウンター、エンドパネル、サイドパネルの寸法は呼び寸法です。詳細寸法は商品ガイドの巻末資料をご確認ください。
- レンジフード電源プラグ仕様：3芯電源プラグ（アース工が必要です。）

特記事項 扉色 VK5:グレージュスタック 取手 [M]スリム取手 (ブラック) ワークトップカラー 【LE】シルフィングレー	物件名	伊藤友章 様邸【10/10ご来館】	案件No.	A2410DDDOE5RWP	図面名	レイアウト図	担当	栗野 友仁	図面	図番	株式会社 LIXIL
	仕様	ES21	見積No.	M24105290035-003-2	縮尺	1/30	日付		2024.10.10		


A面

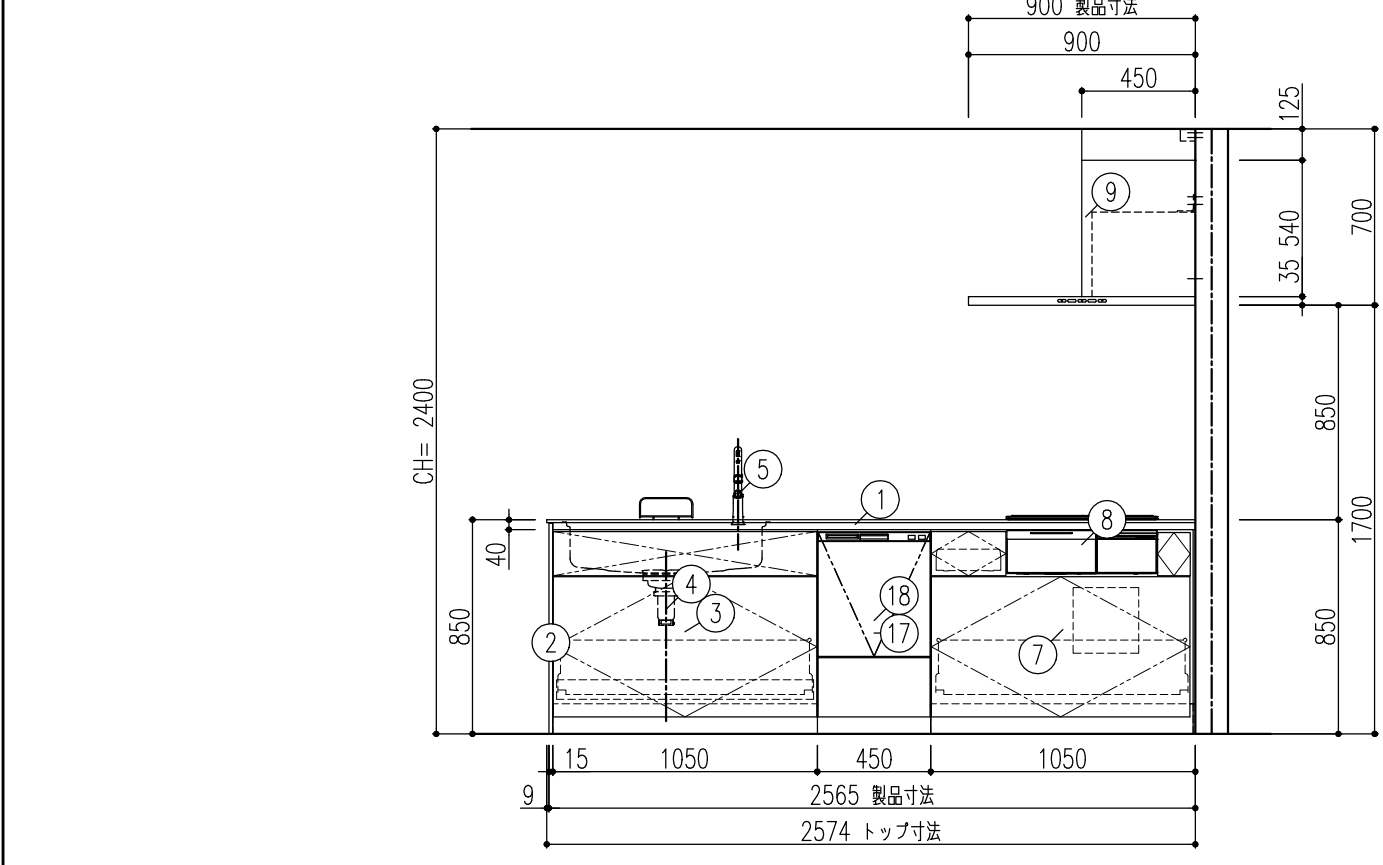


B面

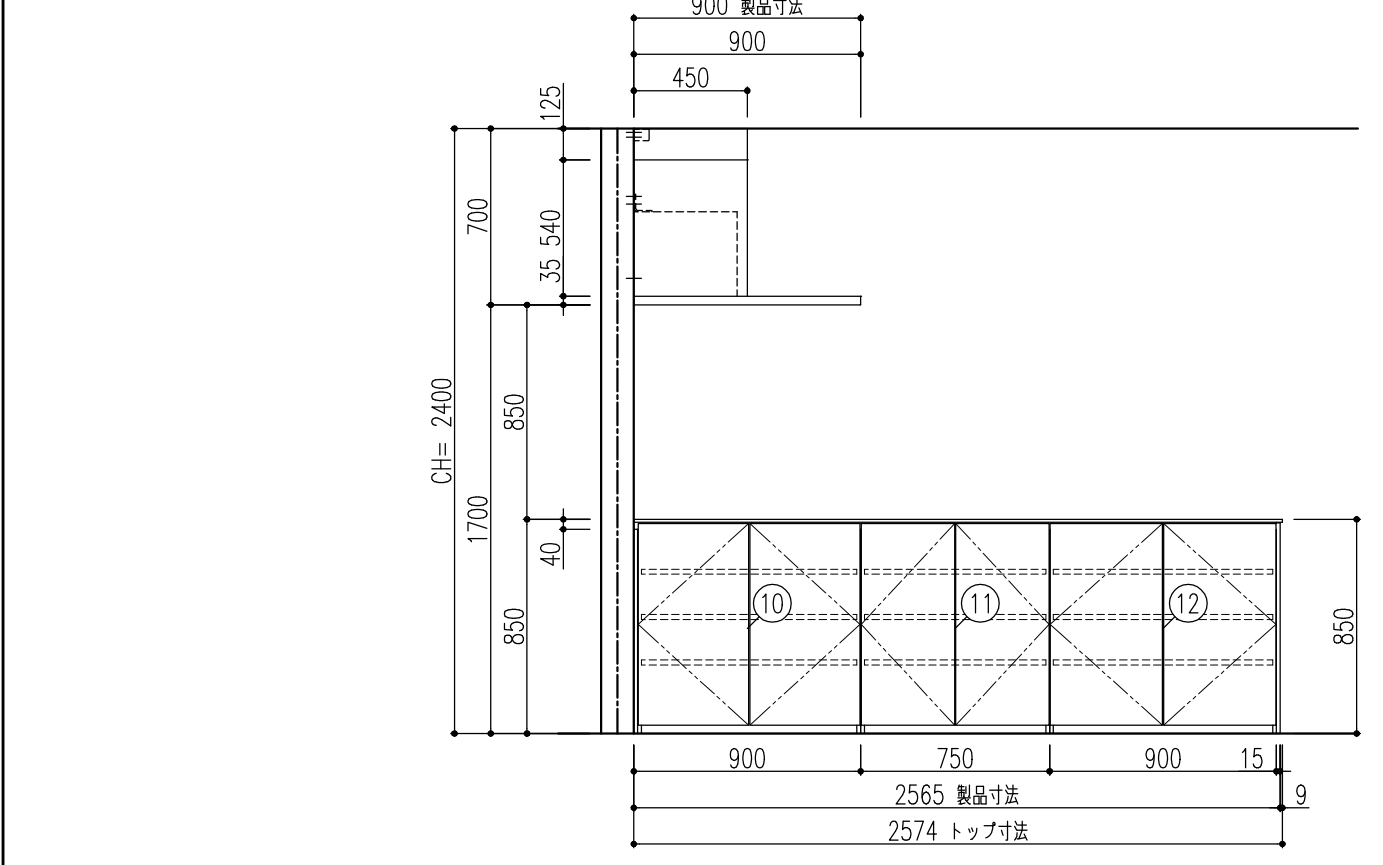

C面

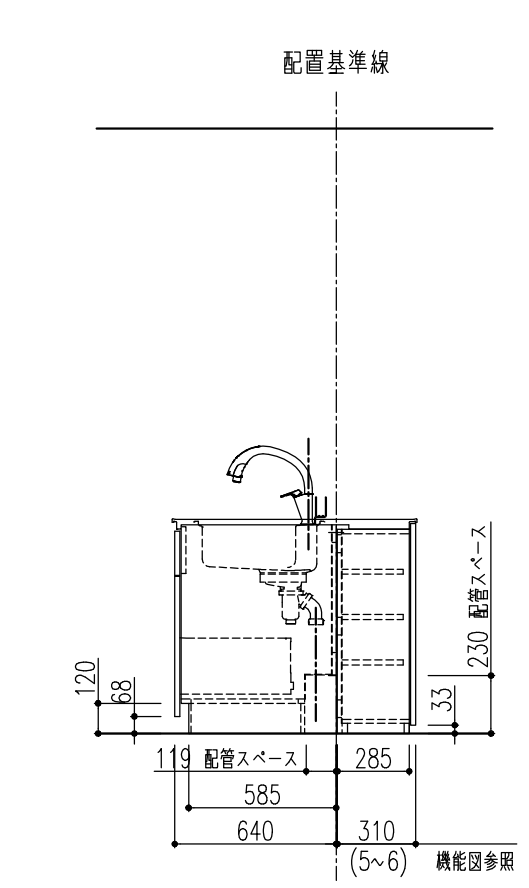

面


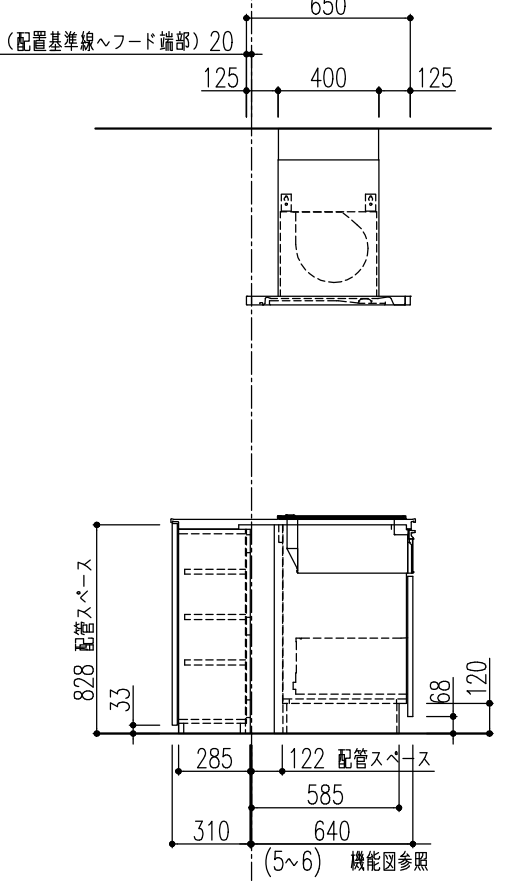


	特記事項 扉色 VK5:グレージュスタック 取手 [M]スリム取手(ブラック) ワークトップカラー 【LE】シルフィークレー	物件名	伊藤友章 様邸【10/10ご来館】	案件No.	図面名	担当	図面	図番 : 株式会社 LIXIL
				A2410DDDOE5RWP	レイアウト図	葉野 友仁		
		仕様	ES21	見積No.	縮尺	日付		
				M24105290035-003-2	1/30	2024.10.10		

A面


B面

- 注1) 125V・15A 2極接地極付アースターミナル付コンセント 【専用】
注2) 125V・15A 2極接地極付コンセント（側板取付）
注3) 250V・30A 2極接地極付コンセント（コンセントベース固定）【専用】

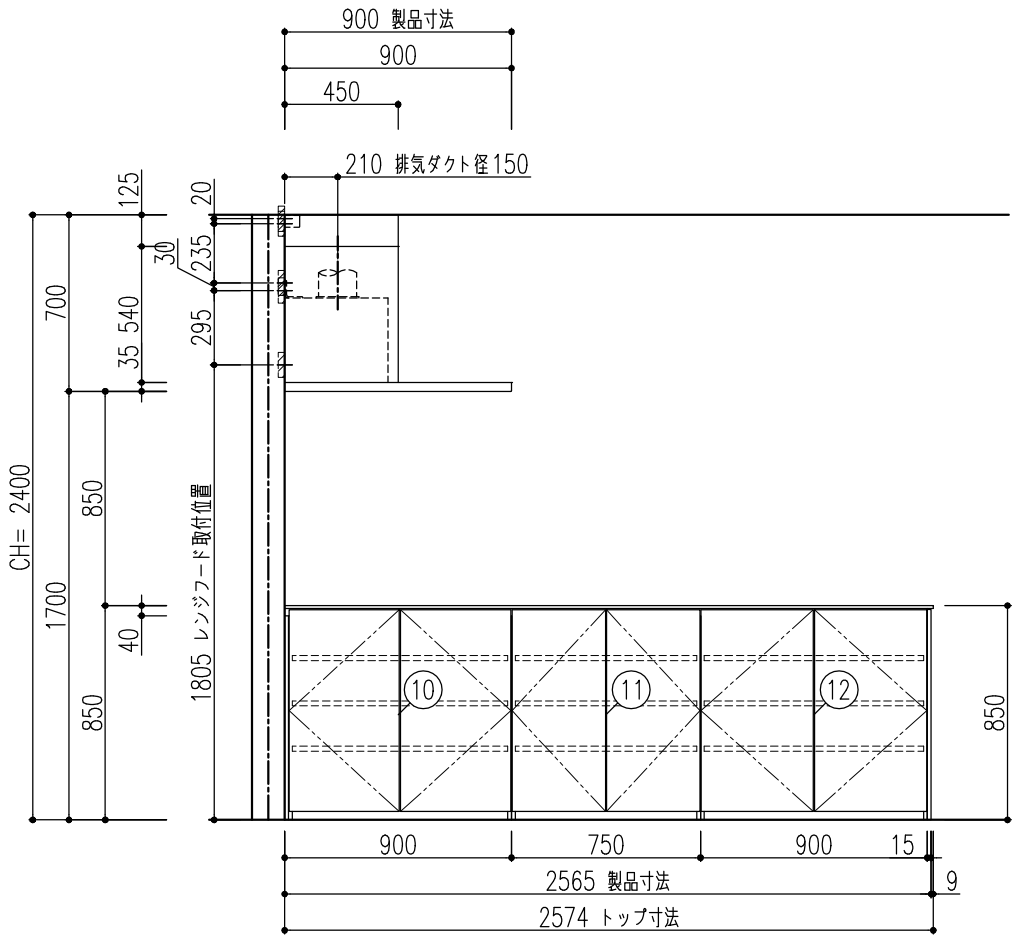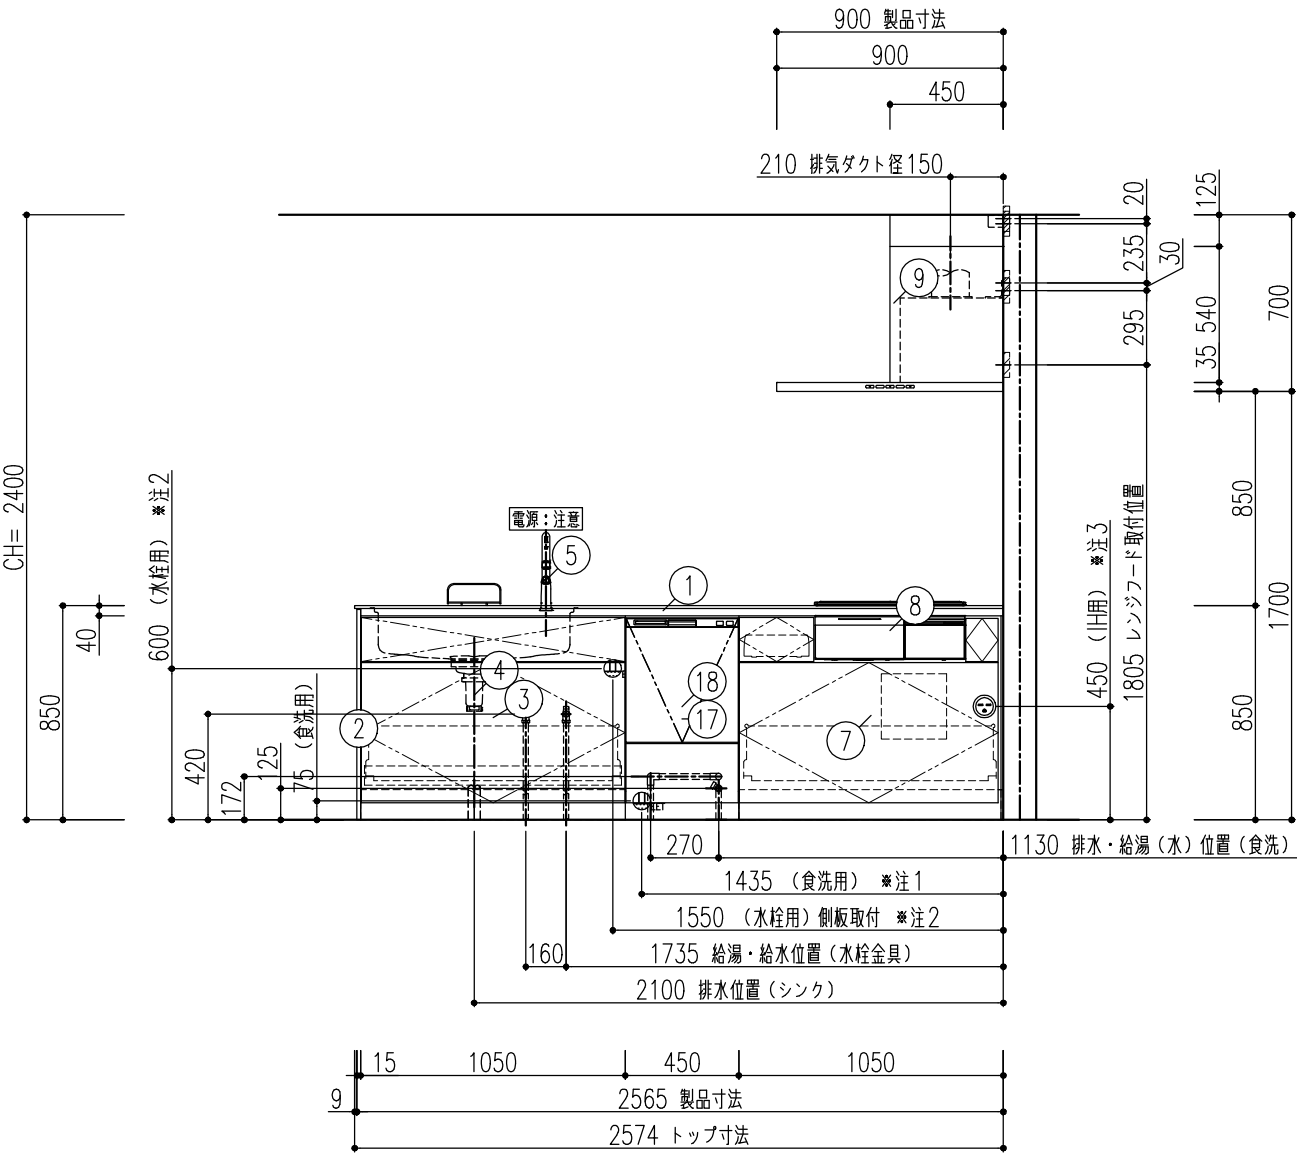


特記事項 扉色 VK5:グレージュスタック 取手 [M]スリム取手（ブラック） ワークトップカラー 【LE】シルフィィーグレー	物件名	伊藤友章 様邸【10/10ご来館】	案件No.	図面名	担当	図面	図番
	仕様	ES21	A2410DDDD0E5RWP	納まり図	栗野 友仁		株式会社 LIXIL
			見積No.	縮尺	日付		
			M24105290035-003-2	1/30	2024.10.10		

C面

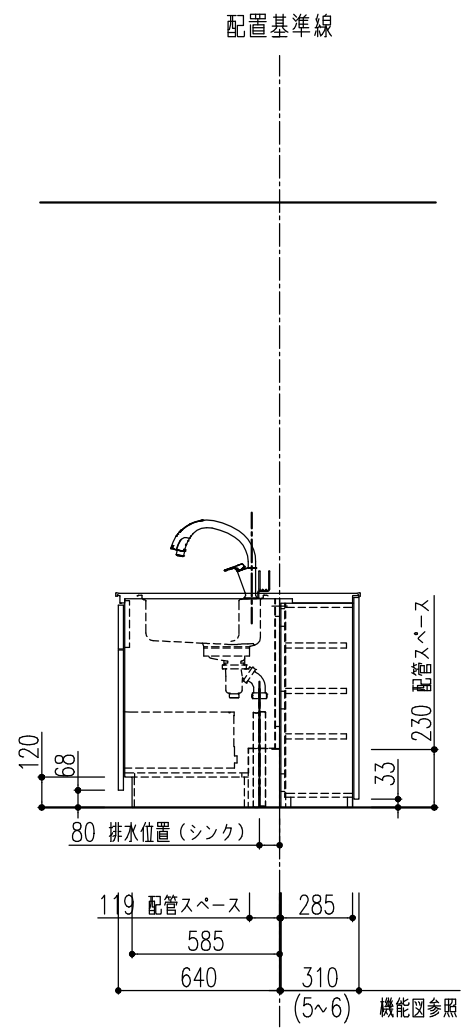


D面

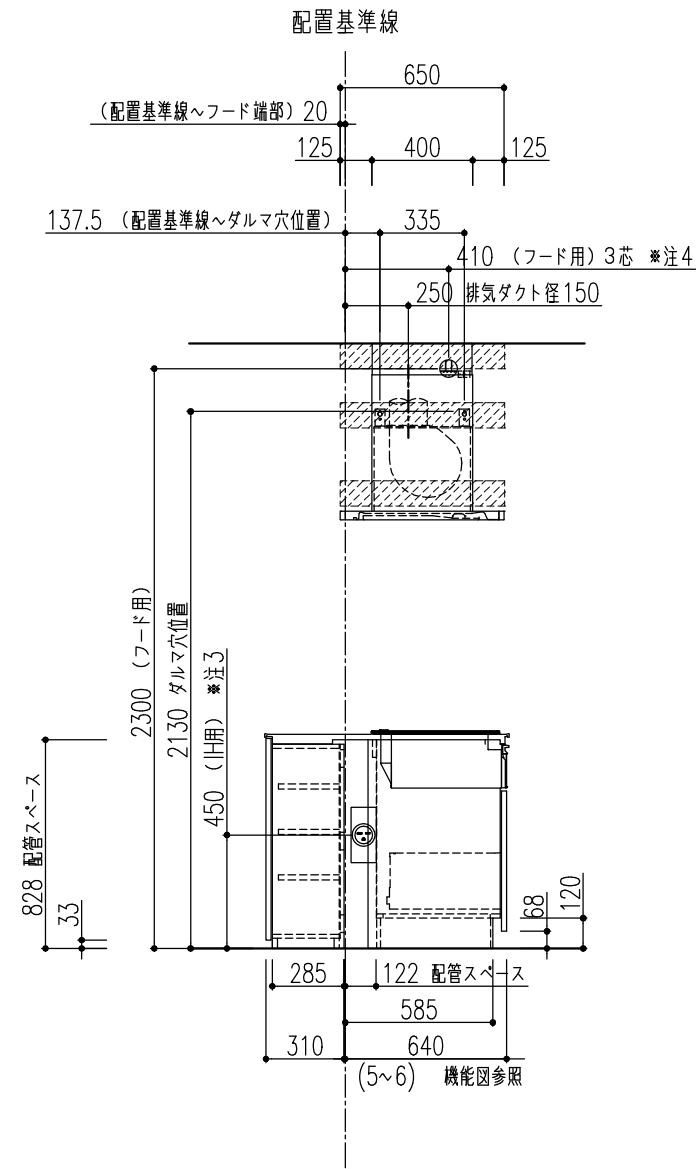

注3) 250V・30A 2極接地極付コンセント (コンセントベース固定) 【専用】
注4) 125V・15A 2極接地極付アースターミナル付コンセント 【専用】 (フード用)

特記事項 扉色 VK5:グレージュスタック 取手 [M]スリム取手 (ブラック) ワークトップカラー 【LE】シルフィークレー	物件名	伊藤友章 様邸【10/10ご来館】	案件No.	図面名	担当	図面	図番 : 株式会社 LIXIL
			A2410DDD0E5RWP	納まり図	栗野 友仁		
	仕様	ES21	見積No.	縮尺	日付		
			M24105290035-003-2	1/30	2024.10.10		




■ 床の不陸に関して

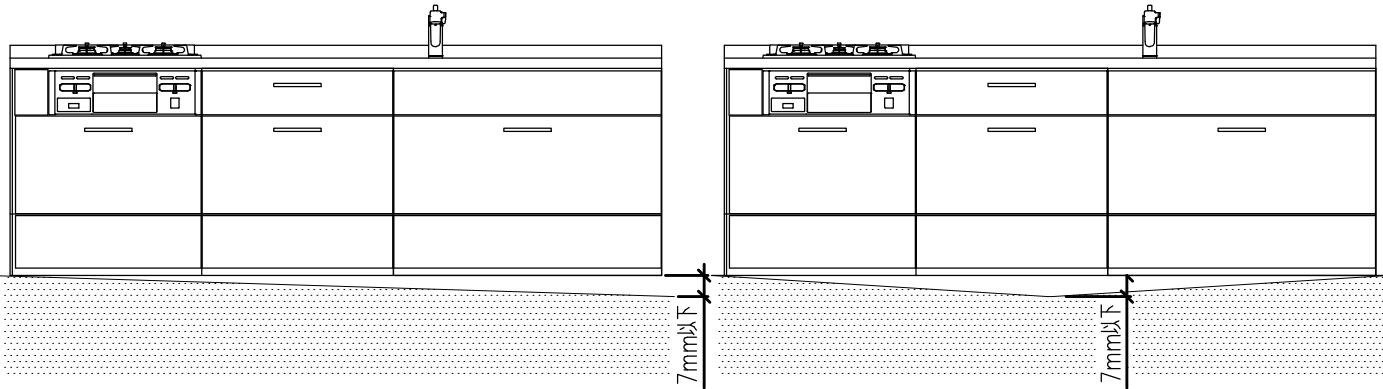

床の不陸は、7mm以下に抑えるようにしてください。不陸が大きい場合は、現場責任者に床の修正を依頼してください。
※キャビネット取付時には不陸調整スペーサー等で水平になるように設置してください。

■ 裏面キャビネット納まりについて

(キッチン側キャビネット背面) 配置基準▽

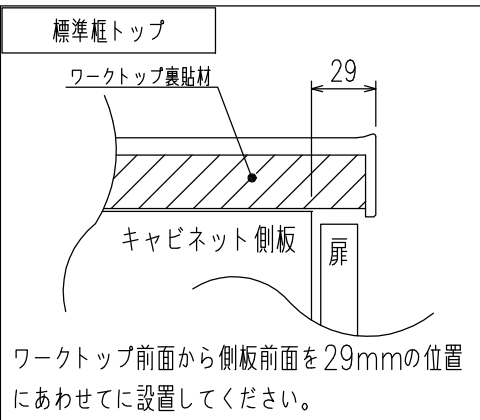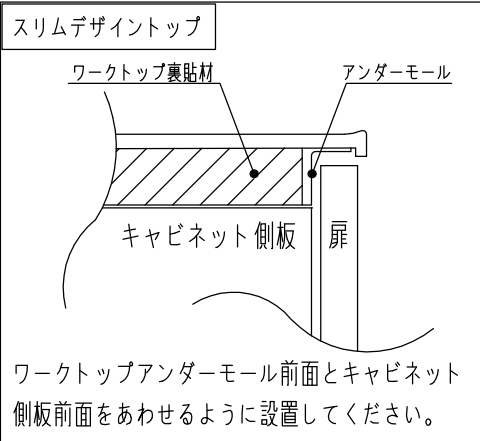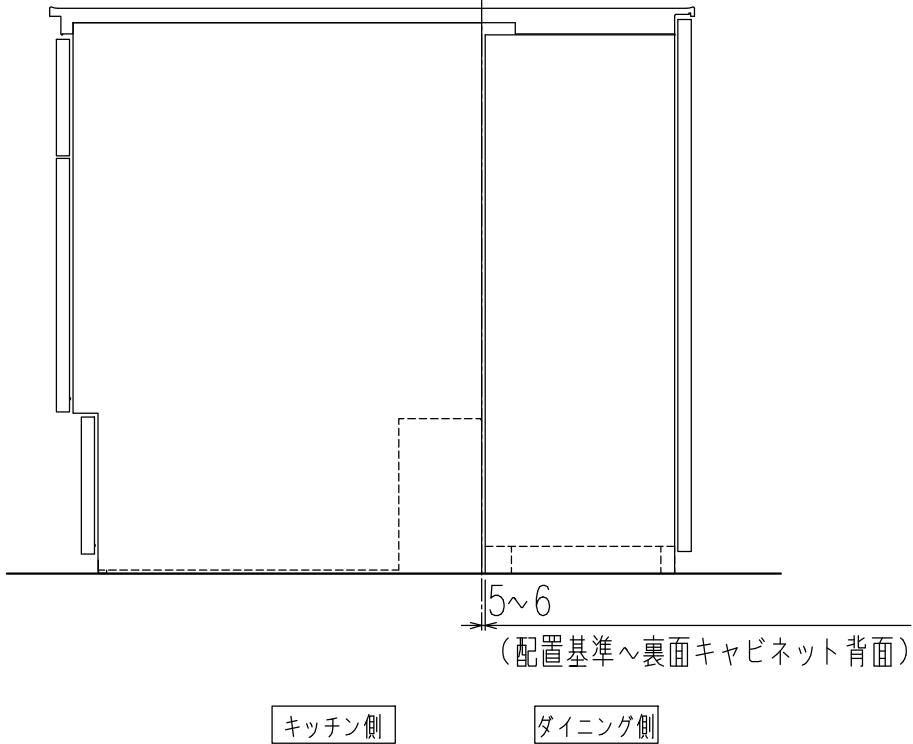

■ 食器洗い乾燥機内配管図 床立上げ配管例


※給水接続か給湯接続かお客様に確認したうえで施工願います。

給水 (給湯の場合は耐熱配管)

- ①アングル型止水栓 (ドライバー式)
- ②硬質塩化ビニルライニング鋼管相当品
- ③Rc1/2エルボ
- ④断熱材 (Φ48)

排水 (耐熱塩ビ使用のこと)

- ⑤排水パイプHT20相当品
- ⑥HT20エルボ

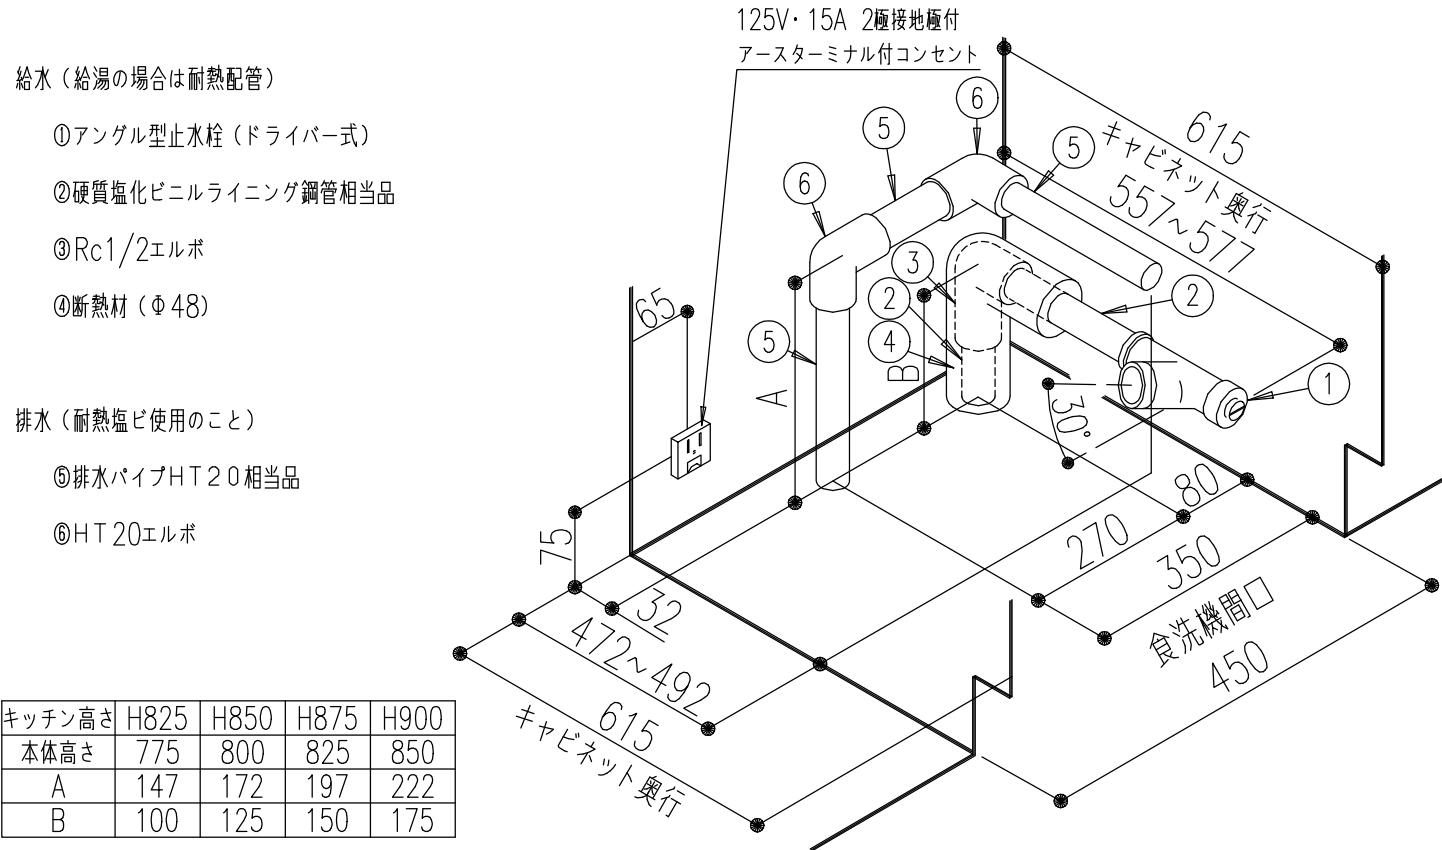


キッチン高さ	H825	H850	H875	H900
本体高さ	775	800	825	850
A	147	172	197	222
B	100	125	150	175

■ レンジフード取付注意事項 (壁面取付時)


レンジフードを取付ける場合は下地の材が厚み30mm以上、幅100mm以上、ビス固定位置が材の端部から25mm以上であることを確認してください。
また、壁強度などの詳細は「レンジフード設置説明書」を必ず事前に確認してください。

取付位置については、取付設置図を確認してください。


参考図_CLS. SER. NST. ASR. ADR. RVJ. GSR. BFRS. TARシリーズ
(※RVJ. GSRシリーズの場合はレンジフードパネルの取付下地は不要です。)

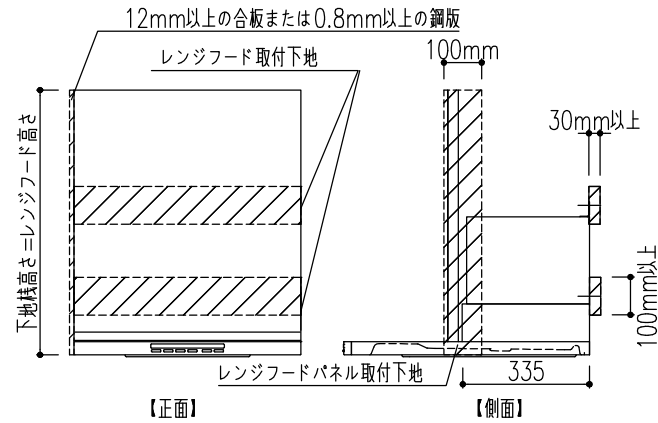

参考図_FED. HVR. NSDシリーズ (サイドマントルタイプ)

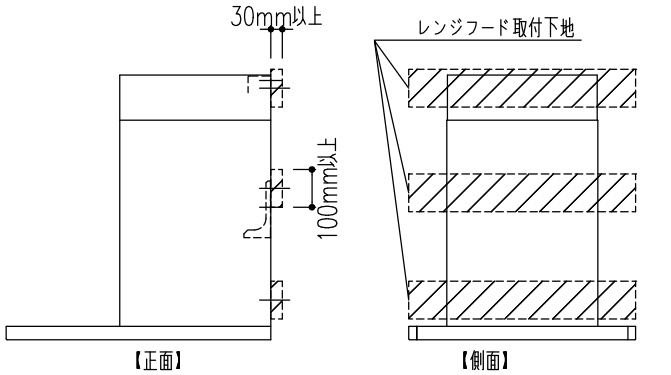

参考図_NBHシリーズ

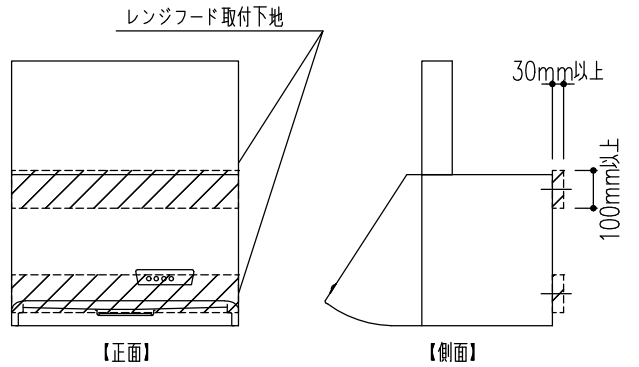

特記事項
扉色 VK5:グレージュスタック
取手 [M]スリム取手 (ブラック)
ワークトップカラー 【LE】シルフィィグレー

物件名 伊藤友章 様邸【10/10ご来館】


仕様 ES21

案件No.
A2410DDDOE5RWP
見積No.
M24105290035-003-2

図面名 機能図
縮尺 目付
2024.10.10

担当 栗野 友仁
図番 :
株式会社 LIXIL

■ SMHVRフード

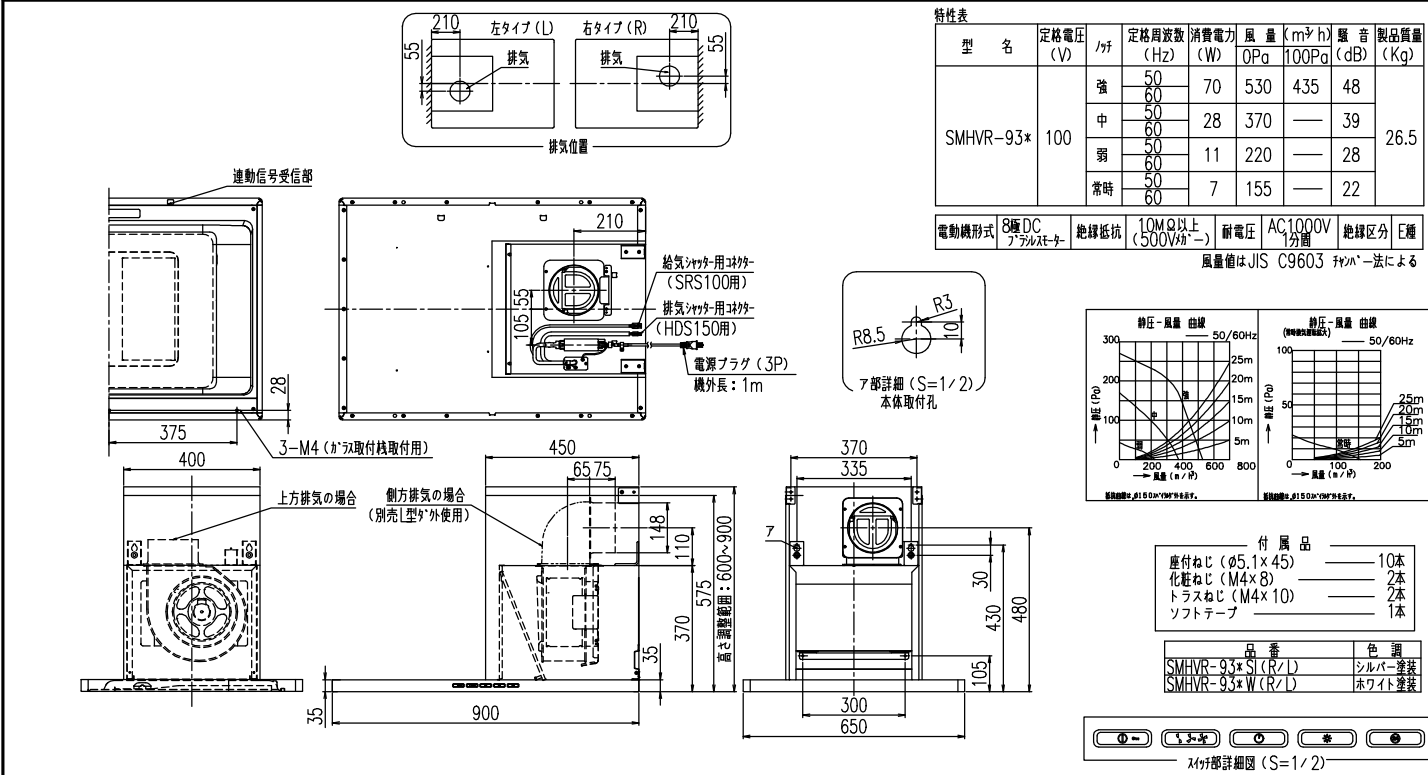


4. 製品名の末尾の () にはワザンリスによって記号が入る場合があります。
5. 電動シャッター (HDS150) (別売) を使用時は、中継コートを外して取り付けてください。
6. 赤外線連動型リモコンです。単独でも使用できます。
注) 1. 排気方向は側方 (L型) 外使用: 別売) と上方です。

■ IHヒーター用コンセント推奨位置図 / 側面設置の場合


※コンセントや電源プラグが、引き出しおよびIHヒーター用仕切板 (オプション) に接触しないように注意してください。
※木製キッチンの配管スペース付キャビネットは、キャビネット内にコンセントを取り付けるスペースがありませんので、別売のコンセントベース (W-SOCKET-B) などを使用して配管スペース内にコンセントを設置してください。

キッチン高さ	コンセント下端高さ	コンセントセンター高さ
800	355	400
850	405	450
900	455	500

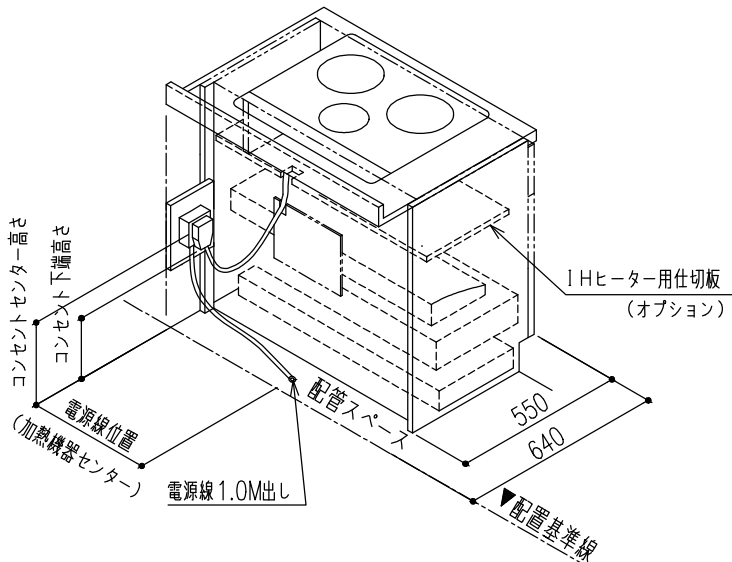


注意: 引き出しおよびIHヒーター用仕切板 (オプション) に接触しないように上記寸法を参照してください。

■ 止水栓図 (床立上げ)



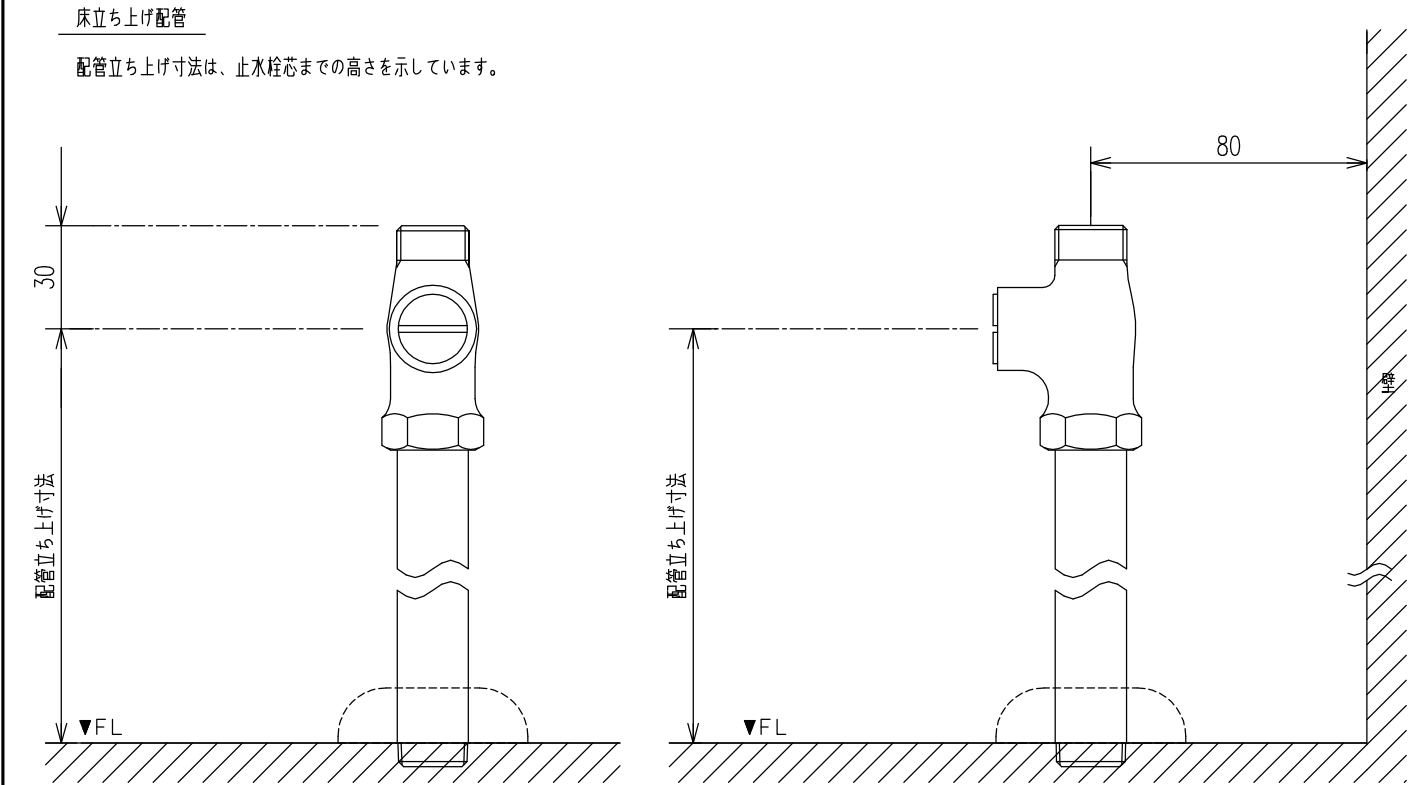


■ タッチレス水栓ナビッシュ 推奨電源位置図

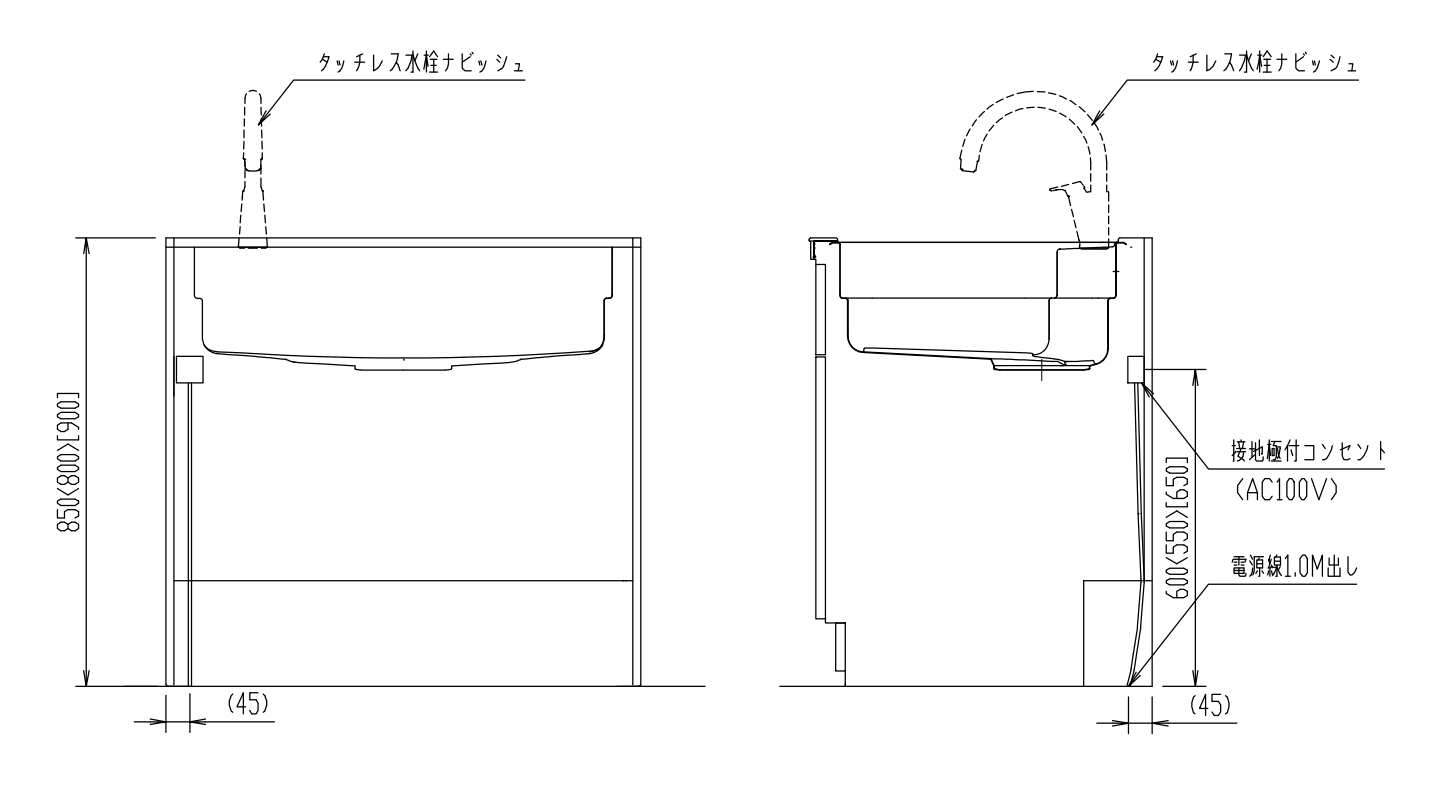




○水栓がシンク右側の場合、電源位置は左右対象の位置にしてください。
○< >内寸法はワークトップ高さ80cmの場合、[]内寸法はワークトップ高さ90cmの場合。

A3	特記事項 扉色 VK5:グレージュスタック 取手 [M]スリム取手 (ブラック) ワークトップカラー 【LE】シルフィィグレー	物件名 仕様	伊藤友章 様邸【10/10ご来館】 ES21	案件No.	図面名	担当	図面	図番
				A2410DDDOE5RWP	機能図	栗野 友仁		株式会社 LIXIL
				見積No.	縮尺	日付		
				M24105290035-003-2		2024.10.10		

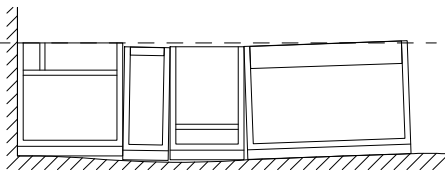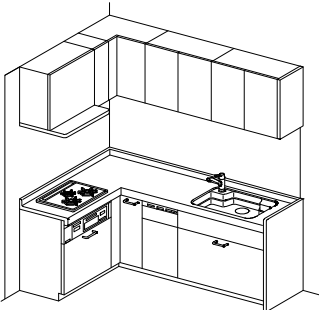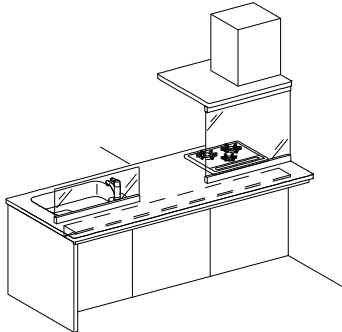■ キッチン取付者さま向け 動画コンテンツ ■ 商品取付けの注意点を2次元コードでご視聴いただけます。 取付日より前に、是非ご確認ください。										1 ページ目	
荷扱い・搬入 荷扱い・搬入 作成日：2024年10月01日			カウンター開梱搬入「養生ツール」 カウンター開梱搬入 「養生ツール」のご紹介 作成日：2024年10月01日			不陸の確認と調整  作成日：2024年02月07日			マグネットキッチンパネル マグネット キッチンパネル 「取付・設置」ポイント 作成日：2024年03月06日		
人造大理石カウンターL型キッチン  作成日：2024年02月07日			センターキッチン（ペニンシュラ型）  作成日：2024年02月07日								
		特記事項 扉色 VK5:グレージュスタック 取手 [M]スリム取手（ブラック） ワークトップカラー 【LE】シルフィークレー	物件名	伊藤友章 様邸【10/10ご来館】		案件No.		図面名	担当	図面	図番
						A2410DDD0E5RWP		機能図	栗野 友仁		株式会社 LIXIL
						見積No.		縮尺	日付		
						M24105290035-003-2			2024.10.10		
						仕様		ES21			

■ キッチン取付者さま向け 動画コンテンツ ■

商品取付けの注意点を2次元コードでご視聴いただけます。
取付日より前に、是非ご確認ください。

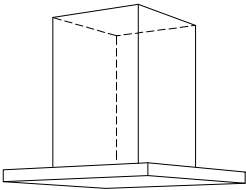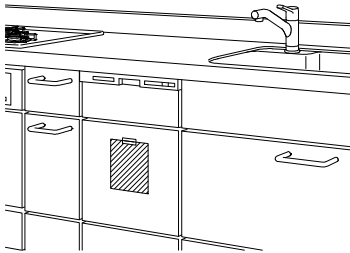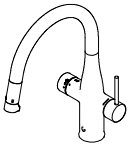センターフード型レンジフード (天吊りフード)  作成日：2024年06月03日 	I H加熱機器関連 I H加熱機器 仕切り板 作成日：2024年02月07日 	食器洗い乾燥機  作成日：2024年02月07日 	ミネラル浄水栓 Greentap  作成日：2024年06月03日 
---	--	--	---

--	--	--	--

--	--	--	--

特記事項 扉色 VK5:グレージュスタック 取手 [M]スリム取手 (ブラック) ワークトップカラー 【LE】シルフィーグレー	物件名	伊藤友章 様邸【10/10ご来館】	案件No.	図面名	担当	図面	図番
	仕様		A2410DDD0E5RWP	機能図	栗野 友仁		株式会社 LIXIL
			見積No.	縮尺	日付		
			M24105290035-003-2		2024.10.10		