





面

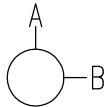

A面

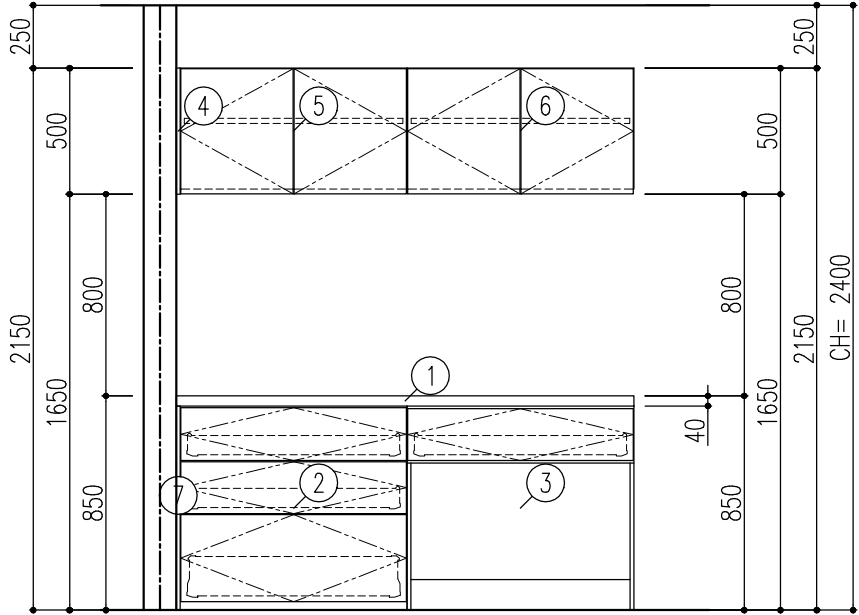


面

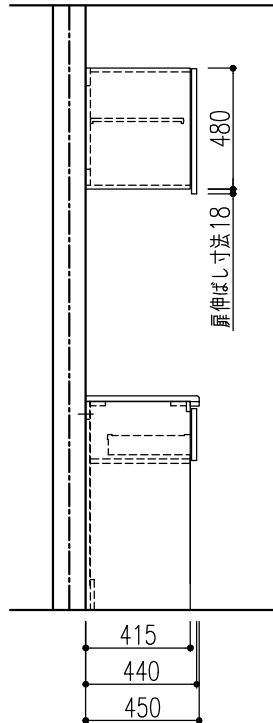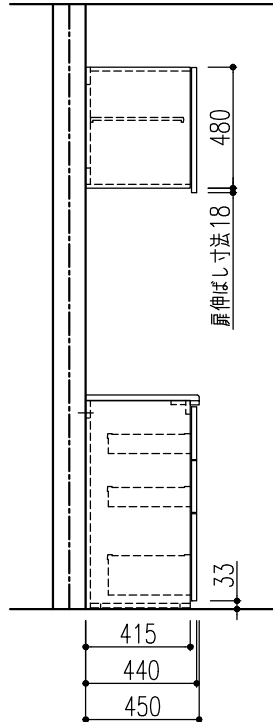[illegible]

【ご注意】

- 記載のキャビネット寸法は扉前面までの呼び寸法です。キャビネット本体の寸法・扉厚み等は商品ガイドの巻末資料をご確認ください。
- 記載のワークトップ、カウンター、エンドパネル、サイドパネルの寸法は呼び寸法です。詳細寸法は商品ガイドの巻末資料をご確認ください。

特記事項 扉色 VK5:グレイジュスタック 取手 [M]スリム取手(ブラック)	物件名	伊藤友章 様邸【10/10ご来館】	案件No.	図面名	担当	図面	図番 : 株式会社 LIXIL
			A2410DDD0E5RWP	レイアウト図	栗野 友仁		
	仕様	ES21	見積No.	縮尺	日付		
			M24105290035-003-6	1/30	2024.10.10		

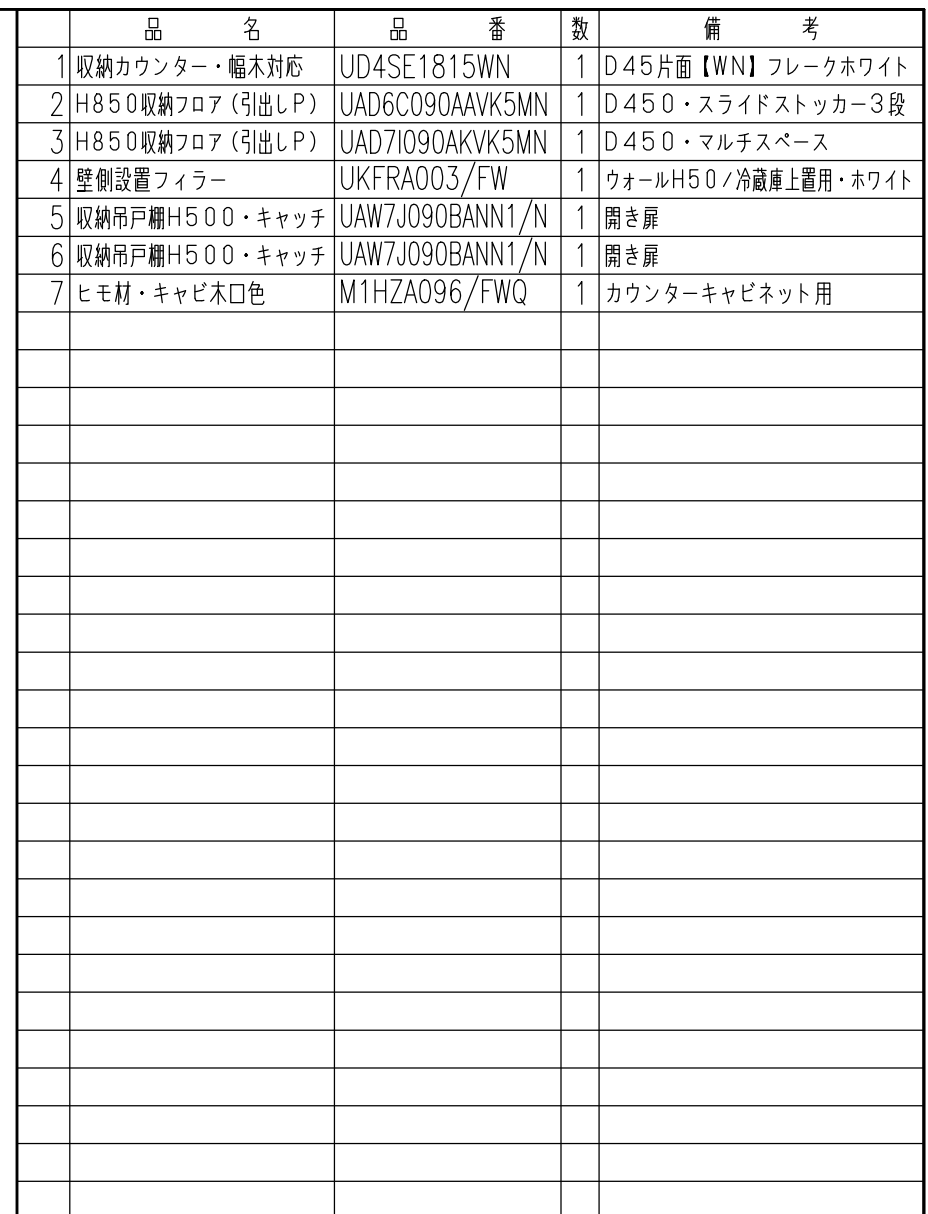

特記事項
扉色 VK5:グレイジュスタッコ
取手 [M]スリム取手(ブラック)


物件名	仕様
-----	----

伊藤友章 様邸【10/10ご来館】


ES21

案件No.	図面名	担当	図面	図番
10DDDOE5RWP	納まり図	栗野 友仁		株式会社 LIXIL
見積No.	縮尺	日付		
05290035-003-6	1/30	2024.10.10		

B面

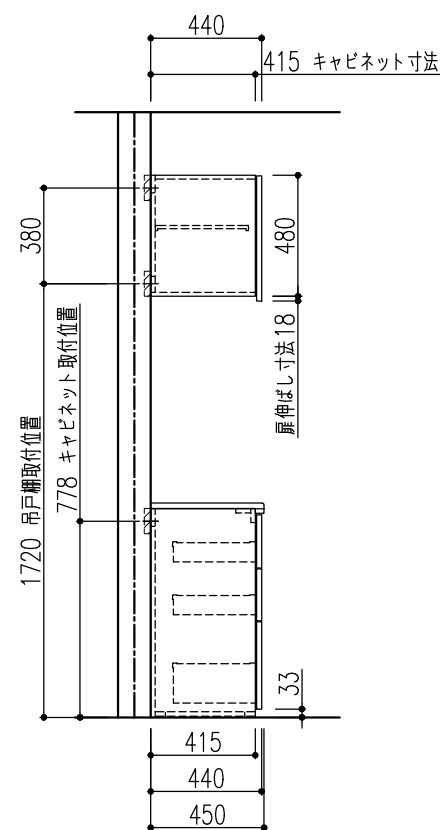

B面

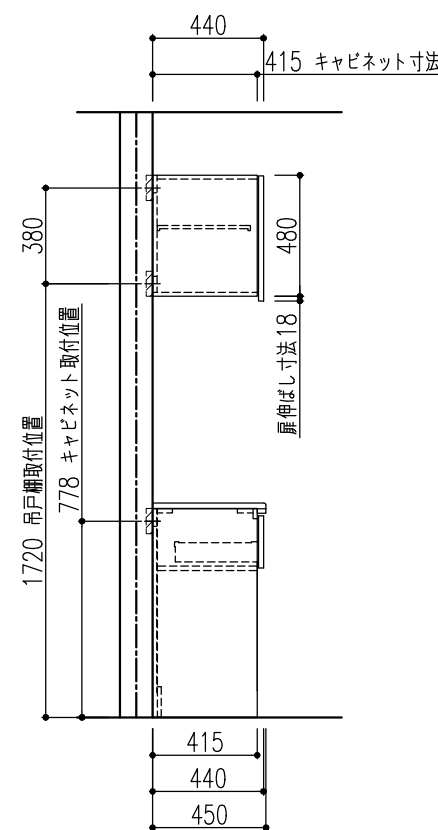


特記事項 扉色 VK5:グレージュスタック 取手 [M]スリム取手（ブラック）	物件名	伊藤友章 様邸【10/10ご来館】	案件No.	図面名	担当	図面	図番
	仕様		A2410DDDD0E5RWP	納まり図	栗野 友仁		株式会社 LIXIL
		ES 2 1	見積No.	縮尺	日付		
			M24105290035-003-6	1/30	2024.10.10		


■吊戸棚 取付注意事項

吊戸棚が落下する恐れがありますので、下記事項をお守りください。


- 本体重量と収納重量の荷重に対して、取付棧（下地）が落ちないだけの強度をもたせてください。
最大300kg/1キャビネット当たりの強度がもつように柱・間柱に確実に固定してください。
- キャビネットを取付・設置する壁面には、取付棧（下地）を取付けるか、埋め込みます。
- 取付棧（下地）は広葉樹、マツ・ツガ等の強度のある針葉樹いずれかの無垢材を使用します。
また、厚さ30mm以上、幅100mm以上が必要です。
- 合板を取付棧（下地）として使用する場合は、ラワン合板などの硬い材質の普通合板
（表面が平滑でフシがない、虫くいや、くされのないもの）を使用します。
また、必ず厚さ12mm以上のものを使用してください。
- せっこうボードで仕上げる壁面は、せっこうボードの内側に取付棧（下地）を取付けます。

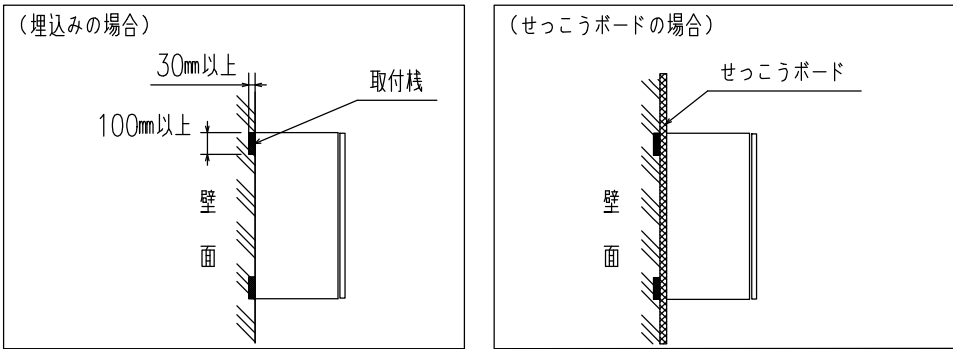

- 吊戸棚の取付けは、必ず商品同梱の専用ネジ（大皿タッピンねじ5.3X63）を使用し、取付棧（下地）に25mm以上かかるようにしてください。
- 合板下地の場合は、下地からのネジ貫通しを13mm以上としてください。
- 合板下地はネジ箇所だけではなく、全面下地（吊戸棚全体）を原則とします。

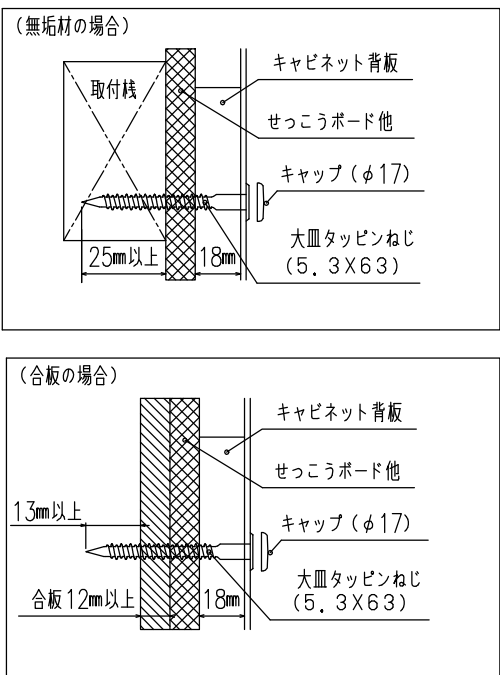


- 鋼板下地の場合 ・鋼板の変形を防ぐため必ずせっこうボード等で覆ってください。
・下地からのネジ貫通しを25mm以上としてください。
- 鋼板下地でせっこうボード2枚貼りの場合、その内側に下地を敷設する事は、
上記のネジ貫通しるが確保出来ないため設置できません。
- 鋼板の厚みは必ず0.8mm以上のものを使用してください。
- 軽量鉄骨躯体（LGS）の設置間隔は300mm以下を守ってください。

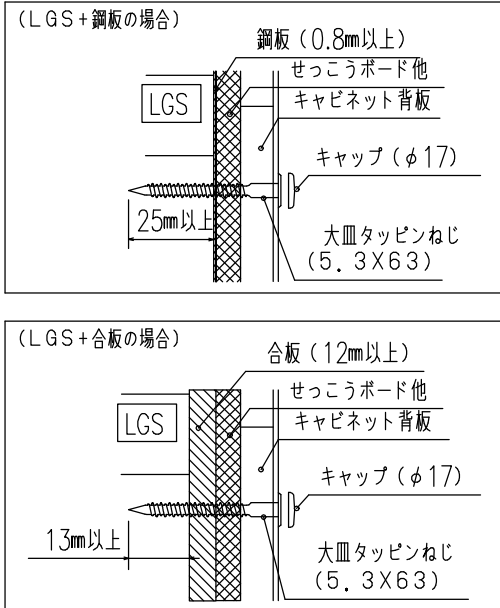


■アイレベルレール 取付注意事項

- ※ アイレベルレール設置の場合
- アイレベルレールの設置に関しては 下記要領で取付棧（下地）
を御用意願います。



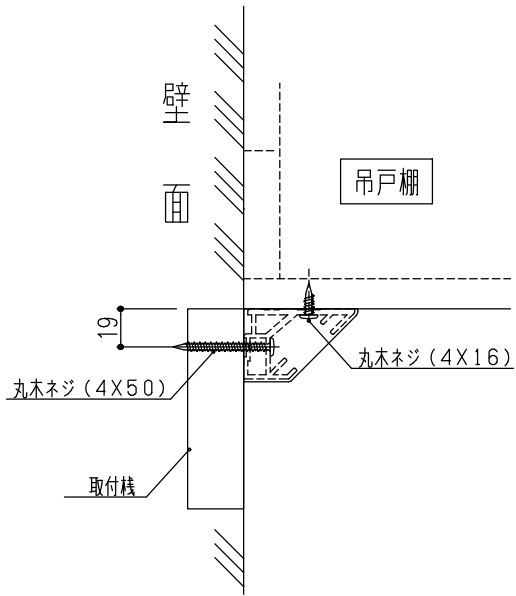


■ 床の不陸に関して

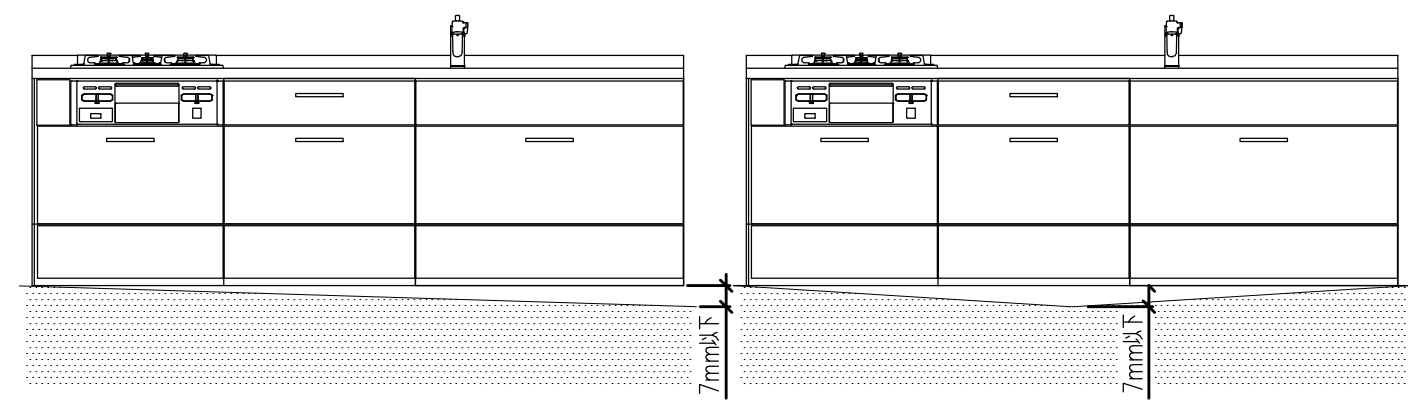




床の不陸は、7mm以下に抑えるようにしてください。不陸が大きい場合は、現場責任者に床の修正を依頼してください。
※キャビネット取付時には不陸調整スペーサー等で水平になるように設置してください。

	特記事項 扉色 VK5:グレイジュスタック 取手 [M]スリム取手（ブラック）	物件名	伊藤友章 様邸【10/10ご来館】	案件No.	図面名	担当	図面	図番 : <
--	---	-----	-------------------	-------	-----	----	----	---

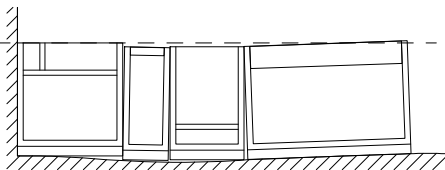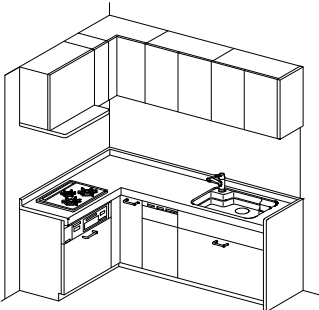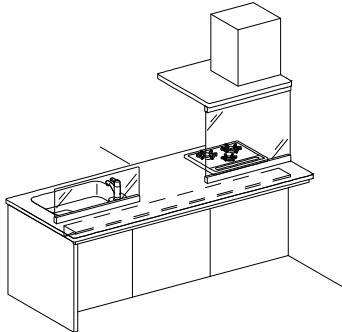■ キッチン取付者さま向け 動画コンテンツ ■ 商品取付けの注意点を2次元コードでご視聴いただけます。 取付日より前に、是非ご確認ください。											1 ページ目	
荷扱い・搬入 荷扱い・搬入 作成日：2024年10月01日			カウンター開梱搬入「養生ツール」 カウンター開梱搬入 「養生ツール」のご紹介 作成日：2024年10月01日			不陸の確認と調整  作成日：2024年02月07日			マグネットキッチンパネル マグネット キッチンパネル 「取付・設置」ポイント 作成日：2024年03月06日			
人造大理石カウンターL型キッチン  作成日：2024年02月07日			センターキッチン（ペニンシュラ型）  作成日：2024年02月07日									
		特記事項 扉色 VK5:グレージュスタック 取手 [M]スリム取手（ブラック）	物件名 仕様	伊藤友章 様邸【10/10ご来館】 ES21		案件No.		図面名	担当	図面	図番	
						A2410DDD0E5RWP		機能図	栗野 友仁		株式会社 LIXIL	
						見積No.		縮尺	日付			
						M24105290035-003-6			2024.10.10			

■ キッチン取付者さま向け 動画コンテンツ ■

商品取付けの注意点を2次元コードでご視聴いただけます。
取付日より前に、是非ご確認ください。

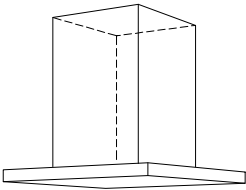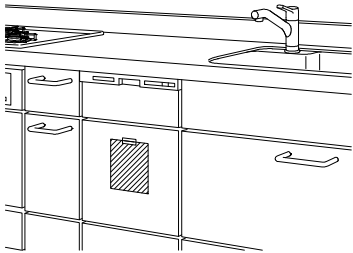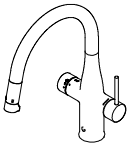センターフード型レンジフード (天吊りフード)  作成日：2024年06月03日 	I H加熱機器関連 I H加熱機器 仕切り板 作成日：2024年02月07日 	食器洗い乾燥機  作成日：2024年02月07日 	ミネラル浄水栓 Greentap  作成日：2024年06月03日 
---	--	--	---

--	--	--	--

--	--	--	--

特記事項 扉色 VK5:グレージュスタック 取手 [M]スリム取手（ブラック）	物件名	伊藤友章 様邸【10/10ご来館】	案件No.	図面名	担当	図面	図番 : 株式会社 LIXIL
			A2410DDD0E5RWP	機能図	栗野 友仁		
	仕様	ES21	見積No.	縮尺	日付		
			M24105290035-003-6		2024.10.10		