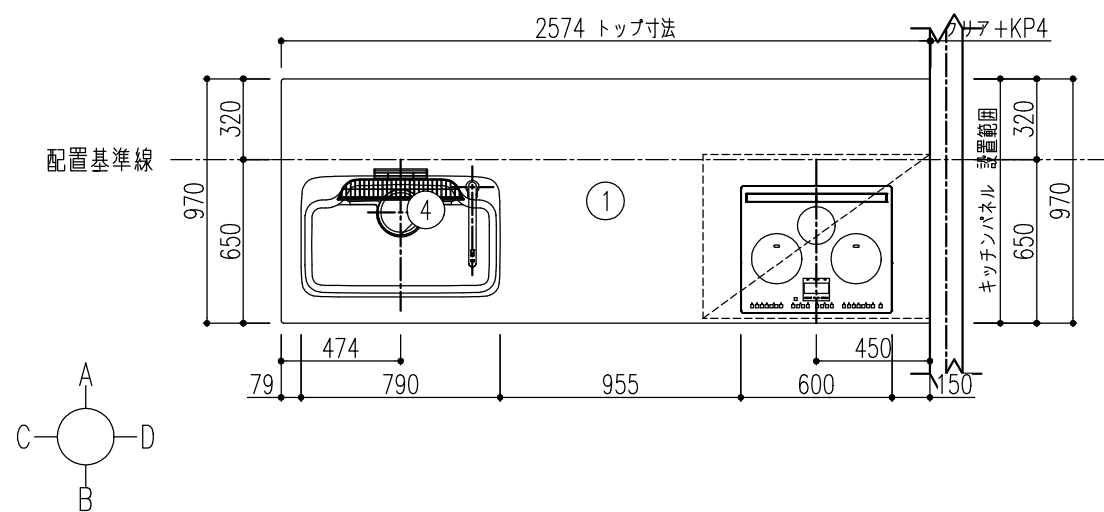



[illegible]

【 ご注意 】


- 記載のキャビネット寸法は扉前面までの呼び寸法です。キャビネット本体の寸法・扉厚み等は商品ガイドの巻末資料をご確認ください。
- 記載のワークトップ、カウンター、エンドパネル、サイドパネルの寸法は呼び寸法です。詳細寸法は商品ガイドの巻末資料をご確認ください。
- レンジフード電源プラグ仕様：3芯電源プラグ（アース工事がが必要です。）
- VVFケーブルの太さにつきましては、内線規程に準じてください。

特記事項 扉色 WK3:ソリッドホワイト 取手 [J]スリム取手（シルバー） ワークトップカラー 【DW】ソルティホワイト	物件名	伊藤友章 様邸【11/25ご依頼】	案件No.	図面名	担当	図面	図番 : 株式会社 LIXIL
			A2410DDDOE5RWP	レイアウト図	栗野 友仁		
	仕様	ES21	見積No.	縮尺	日付		
			M24105290035-011-2	1/30	2024.11.26		


A面

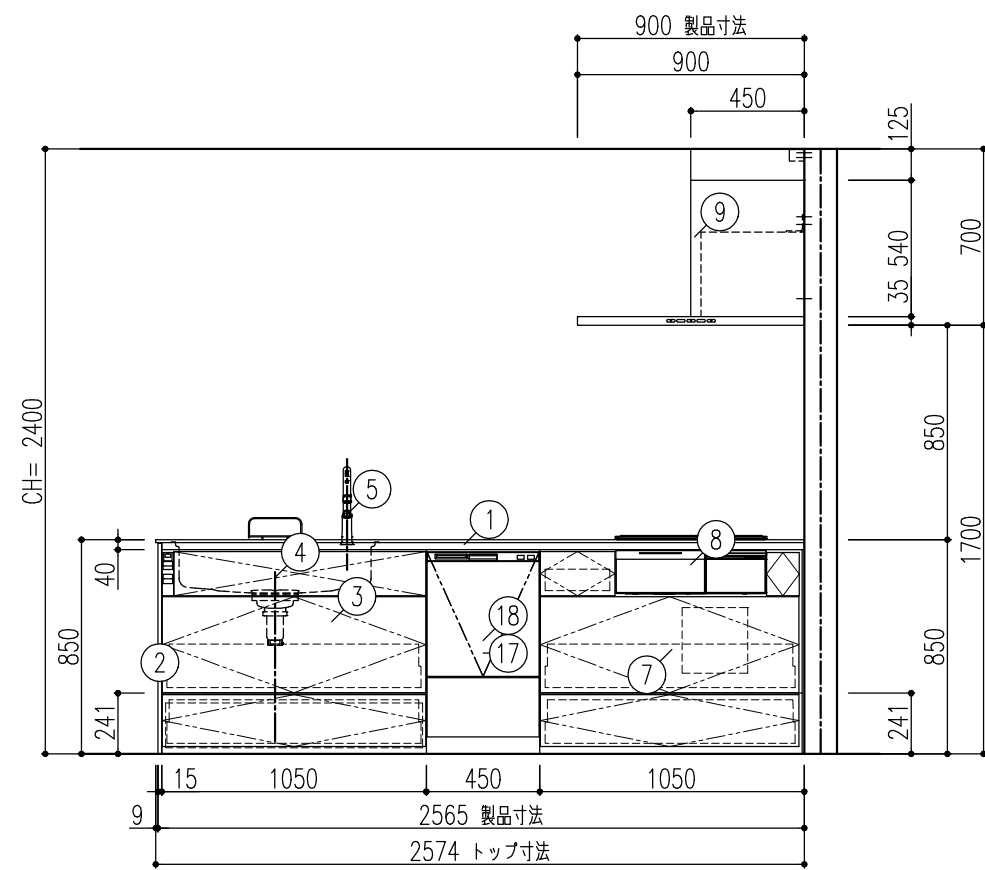


B面

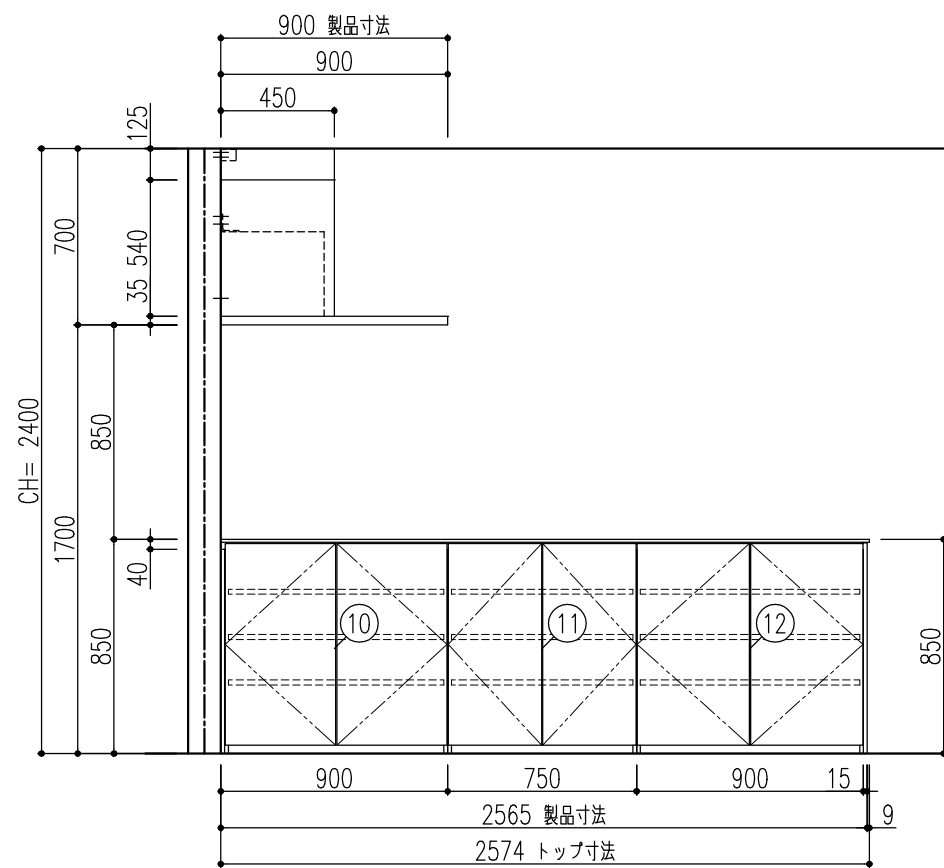


C面

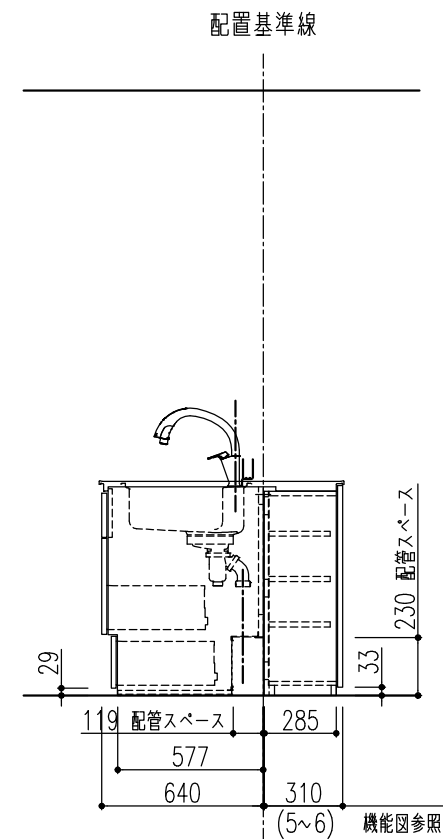

D面

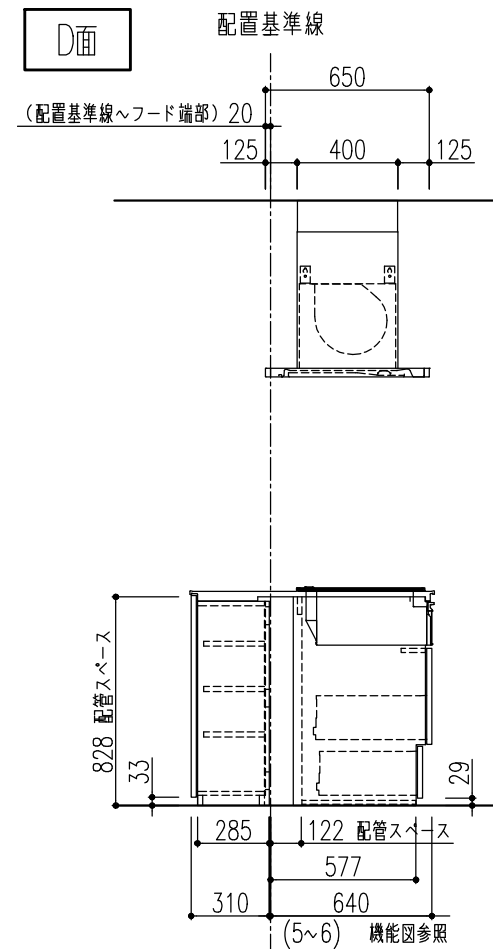

特記事項 扉色 WK3:ソリッドホワイト 取手 [J]スリム取手 (シルバー) ワークトップカラー 【DW】ソルティホワイト	物件名 仕様	伊藤友章 様邸【11/25ご依頼】 ES21	案件No.	図面名	担当	図面	図番
			A2410DDDOE5RWP	レイアウト図	栗野 友仁		株式会社 LIXIL
			見積No.	縮尺	日付		
			M24105290035-011-2	1/30	2024.11.26		

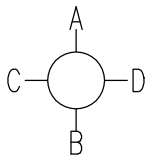

注1) 100V・15A 電源線取出し推奨位置(3.0M出し)【専用】※配管スペース内であれば他位置でも可
【ご注意】



- 記載のキャビネット寸法は扉前面までの呼び寸法です。キャビネット本体の寸法・扉厚等は商品ガイドの巻末資料をご確認ください。
- 記載のワークトップ、カウンター、エンドパネル、サイドパネルの寸法は呼び寸法です。詳細寸法は商品ガイドの巻末資料をご確認ください。
- 電気・ガス・給排水・換気等は法令・規定に従って有資格者が行ってください。
- 水道工事は排水配管工事となります。
- 取付・設置に際し、各製品の取付・設置説明書や図面の機能図を必ずお読み下さい。
- 内線規程上、各機器のプラグ仕様に問わず建築側には接地極付コンセントを推奨しています。
- レンジフード電源プラグ仕様：3芯電源プラグ（アース工が必要です。）
- 食洗機内配管の詳細については必ず別添の機能図をご確認ください。
- VVFケーブルの太さにつきましては、内線規程に準じてください。

A3 20241126N9UV-01

A面

B面

- 注2) 125V・15A 2極接地極付アースターミナル付コンセント 【専用】
注3) 125V・15A 2極接地極付コンセント（側板取付）
注4) 250V・30A 2極接地極付コンセント（コンセントベース固定）【専用】

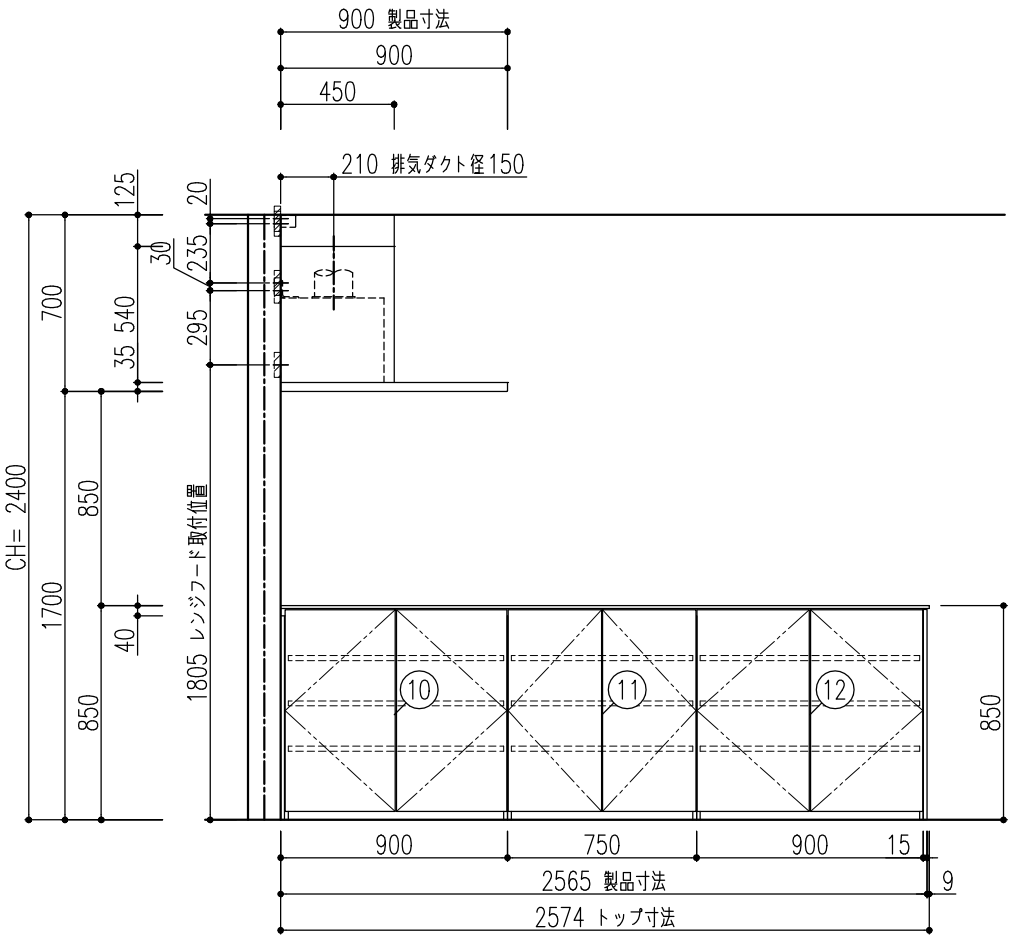
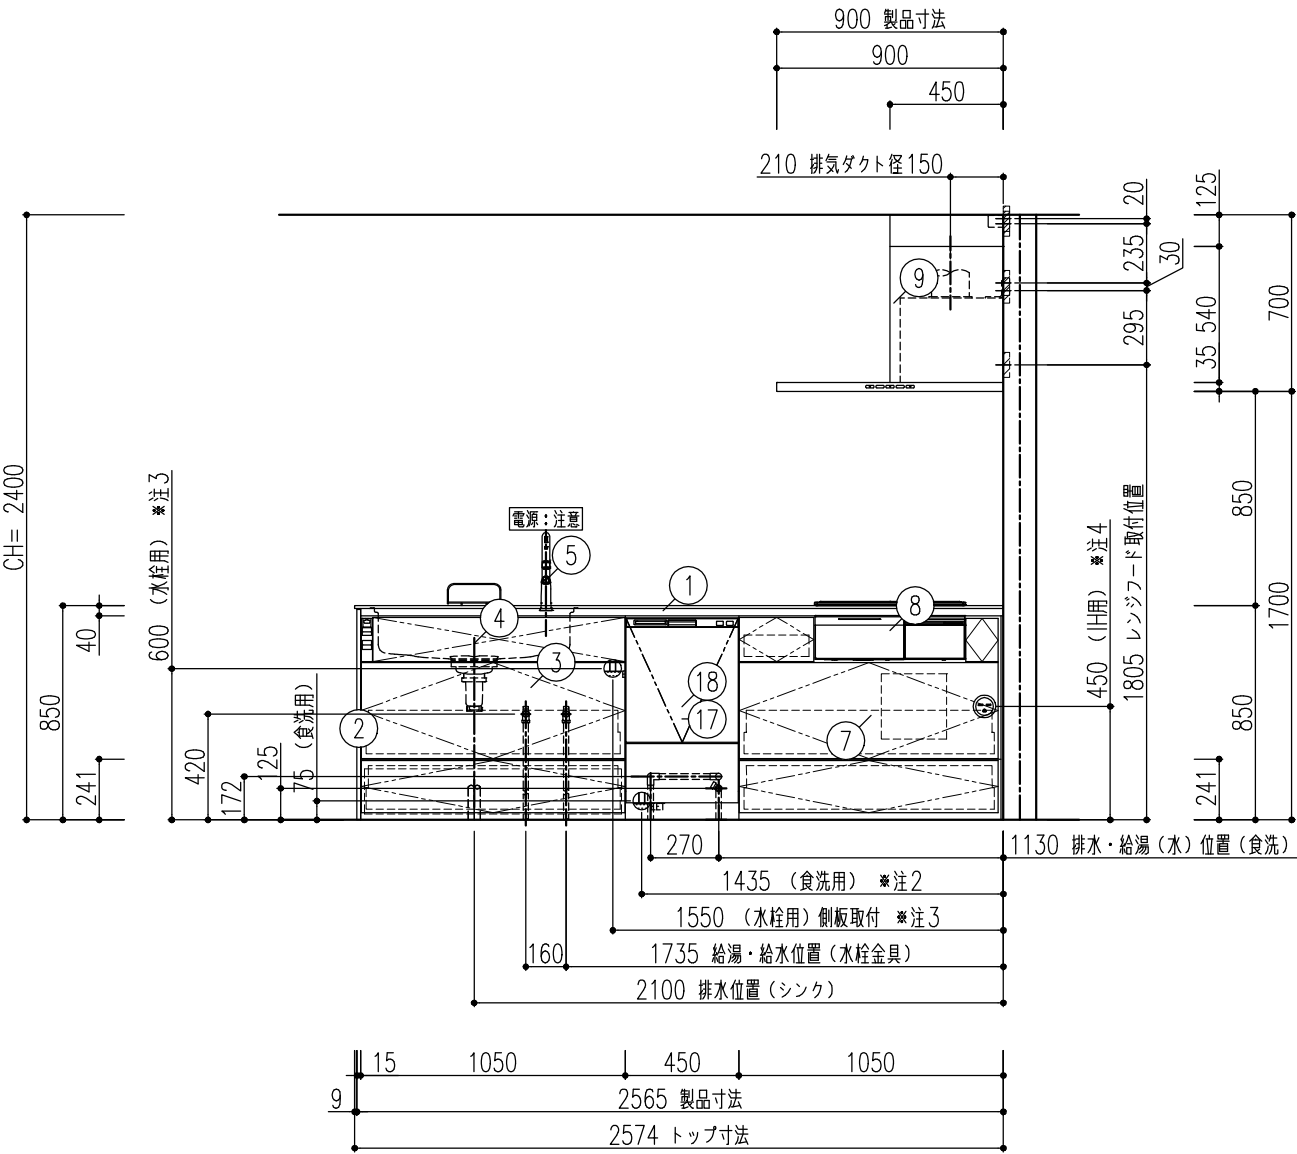


特記事項 扉色 WK3:ソリッドホワイト 取手 [J]スリム取手 (シルバー) ワークトップカラー 【DW】ソルティホワイト	物件名	伊藤友章 様邸【11/25ご依頼】	案件No.	図面名	担当	図面	図番
	仕様	ES21	A2410DDDD0E5RWP	納まり図	栗野 友仁		株式会社 LIXIL
			見積No.	縮尺	日付		
			M24105290035-011-2	1/30	2024.11.26		

C面


D面

注4) 250V・30A 2極接地極付コンセント（コンセントベース固定）【専用】
注5) 125V・15A 2極接地極付アースターミナル付コンセント 【専用】（フード用）

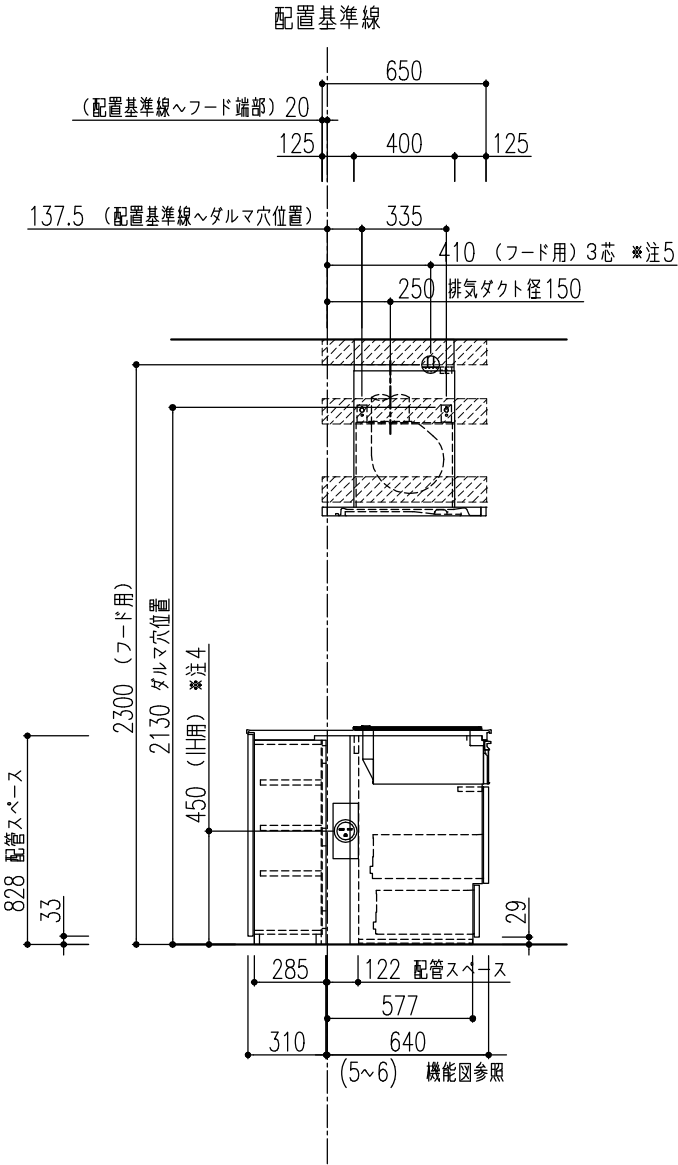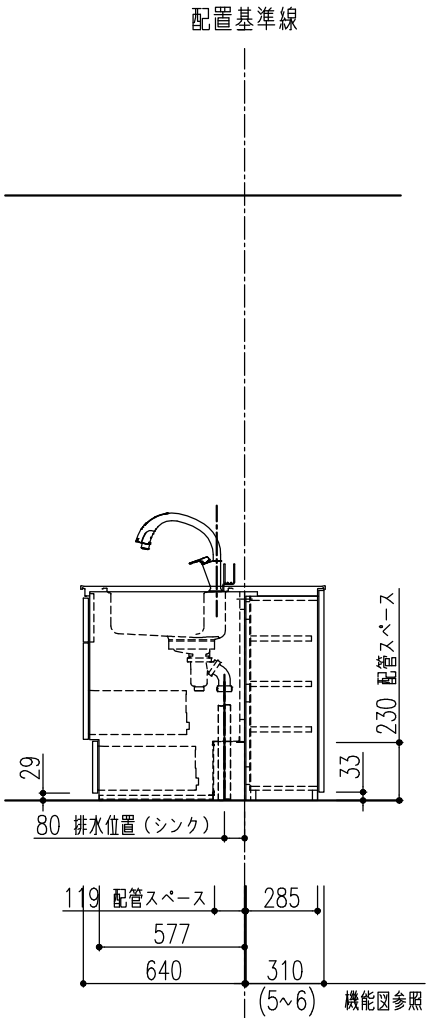

特記事項 扉色 WK3:ソリッドホワイト 取手 [J]スリム取手（シルバー） ワークトップカラー 【DW】ソルティホワイト	物件名	伊藤友章 様邸【11/25ご依頼】	案件No.	図面名	担当	図面	図番	株式会社 LIXIL
	仕様	ES21	A2410DDDD0E5RWP	納まり図	栗野 友仁			
			見積No.	縮尺	日付			
			M24105290035-011-2	1/30	2024.11.26			



■ 床の不陸に関して

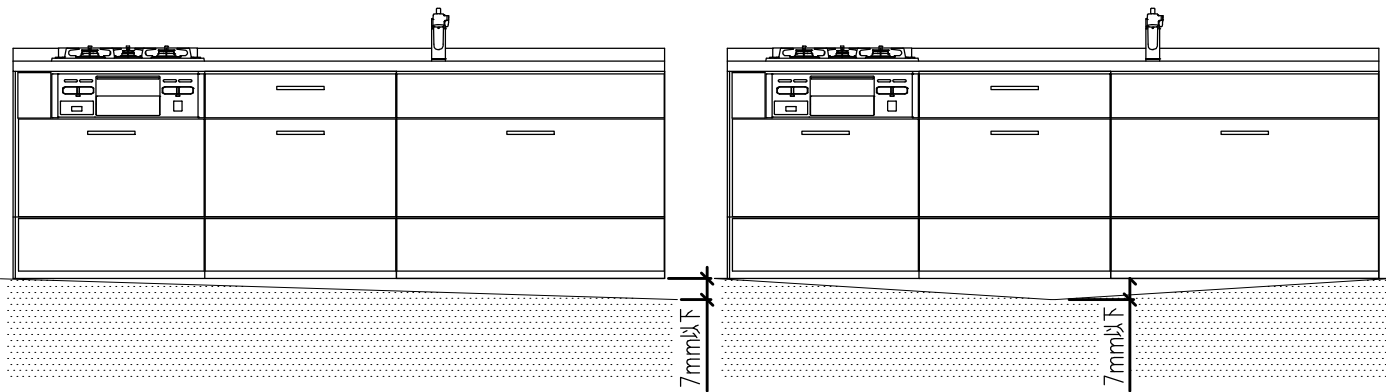

床の不陸は、7mm以下に抑えるようにしてください。不陸が大きい場合は、現場責任者に床の修正を依頼してください。
※キャビネット取付時には不陸調整スペーサー等で水平になるように設置してください。

■ 裏面キャビネット納まりについて

(キッチン側キャビネット背面) 配置基準▽

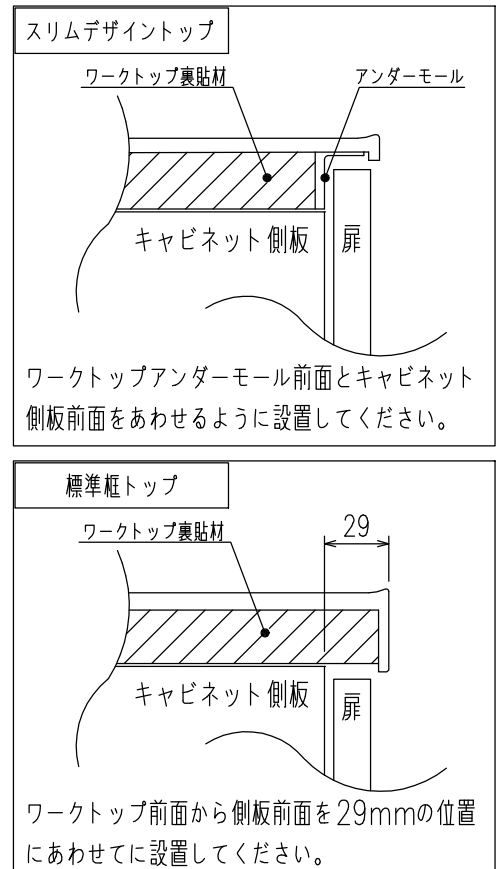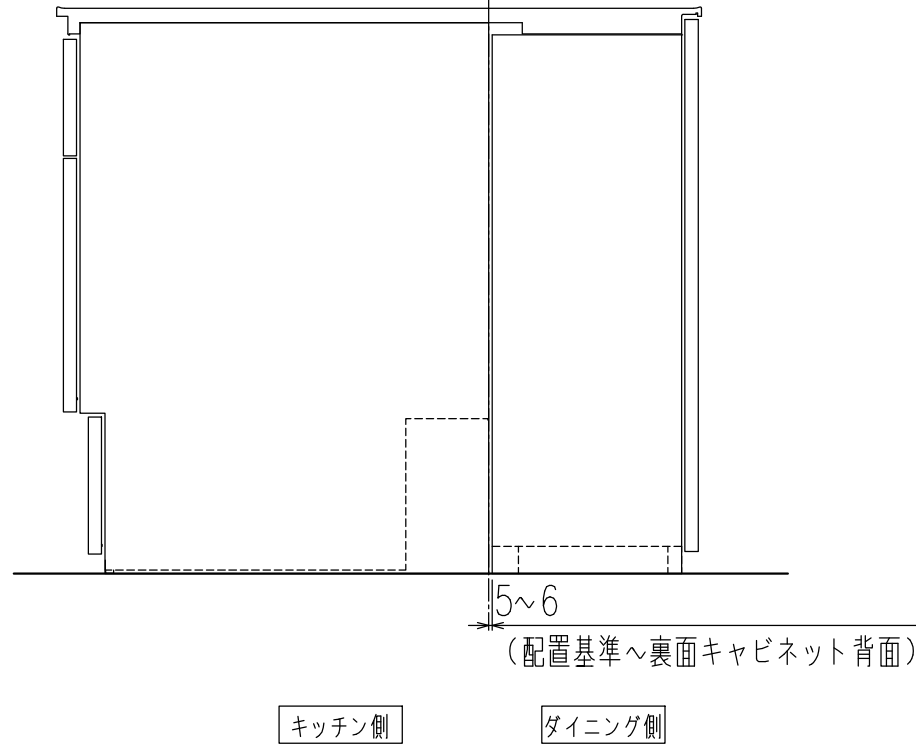

■ 食器洗い乾燥機内配管図 床立上げ配管例


※給水接続か給湯接続かお客様に確認したうえで施工願います。

給水 (給湯の場合は耐熱配管)

- ①アングル型止水栓 (ドライバー式)
- ②硬質塩化ビニルライニング鋼管相当品
- ③Rc1/2エルボ
- ④断熱材 (Φ48)

排水 (耐熱塩ビ使用のこと)

- ⑤排水パイプHT20相当品
- ⑥HT20エルボ

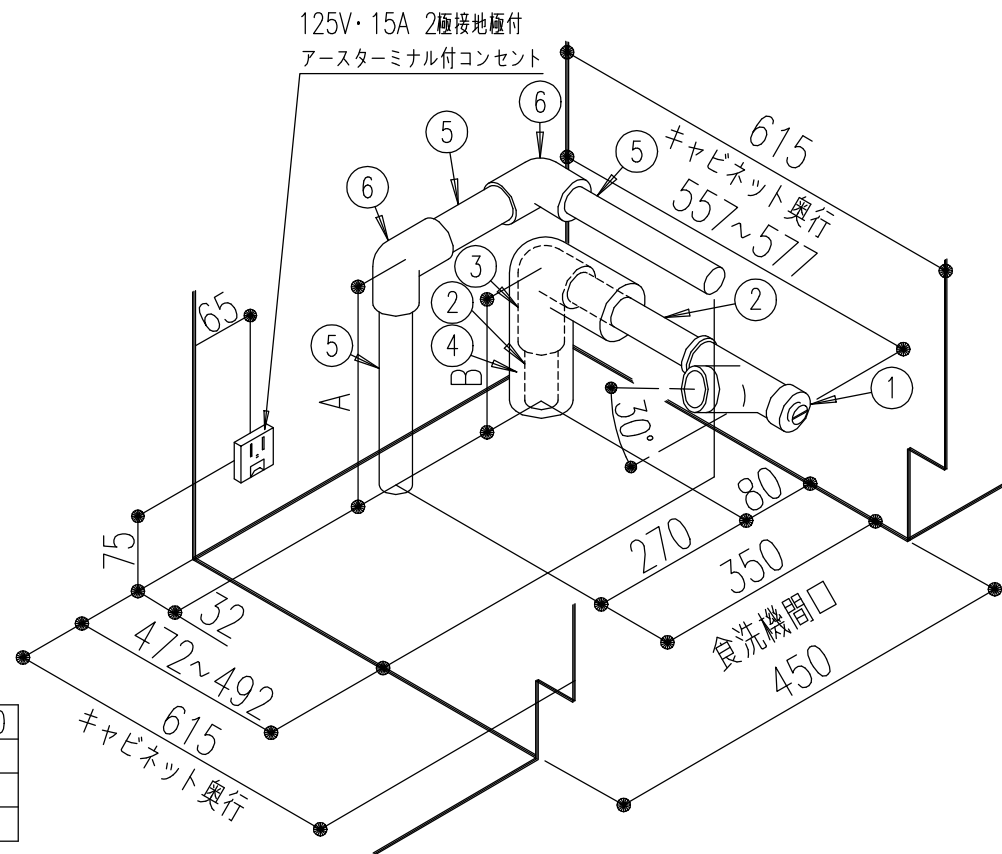


キッチン高さ	H825	H850	H875	H900
本体高さ	775	800	825	850
A	147	172	197	222
B	100	125	150	175

■ レンジフード取付注意事項 (壁面取付時)


レンジフードを取付ける場合は下地の材が厚み30mm以上、幅100mm以上、ビス固定位置が材の端部から25mm以上であることを確認してください。また、壁強度などの詳細は「レンジフード設置説明書」を必ず事前に確認してください。

取付位置については、取付設置図を確認してください。


参考図_CLS. SER. NST. ASR. ADR. RVJ. GSR. BFRS. TARシリーズ
(※RVJ. GSRシリーズの場合はレンジフードパネルの取付下地は不要です。)

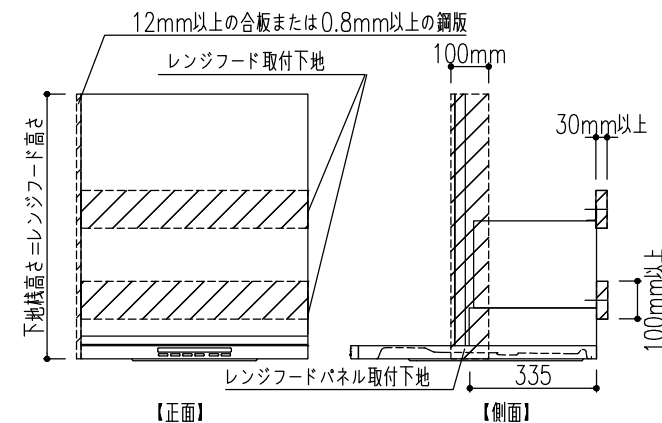

参考図_FED. HVR. NSDシリーズ (サイドマントルタイプ)

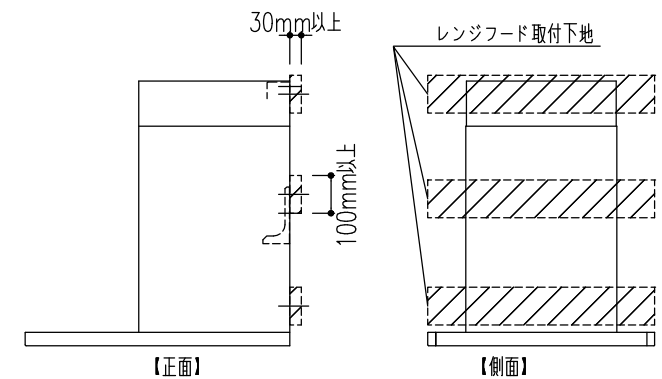

参考図_NBHシリーズ

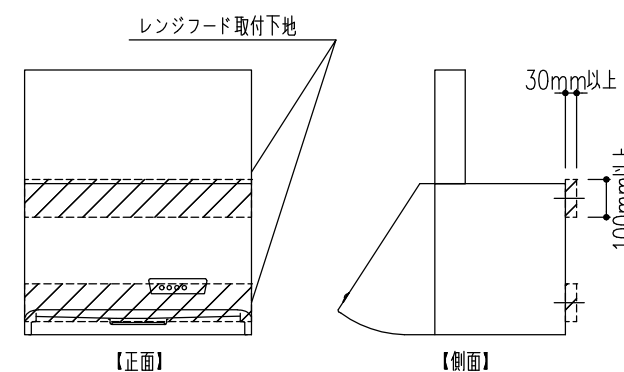

特記事項
扉色 WK3:ソリッドホワイト
取手 [J]スリム取手 (シルバー)
ワークトップカラー 【DW】ソルティホワイト

物件名 伊藤友章 様邸【11/25ご依頼】


仕様 ES21

案件No.
A2410DDDOE5RWP
見積No.
M24105290035-011-2

図面名 機能図
縮尺
図面 栗野 友仁
日付 2024.11.26

図番 :
株式会社 LIXIL


■ SMHVRフード

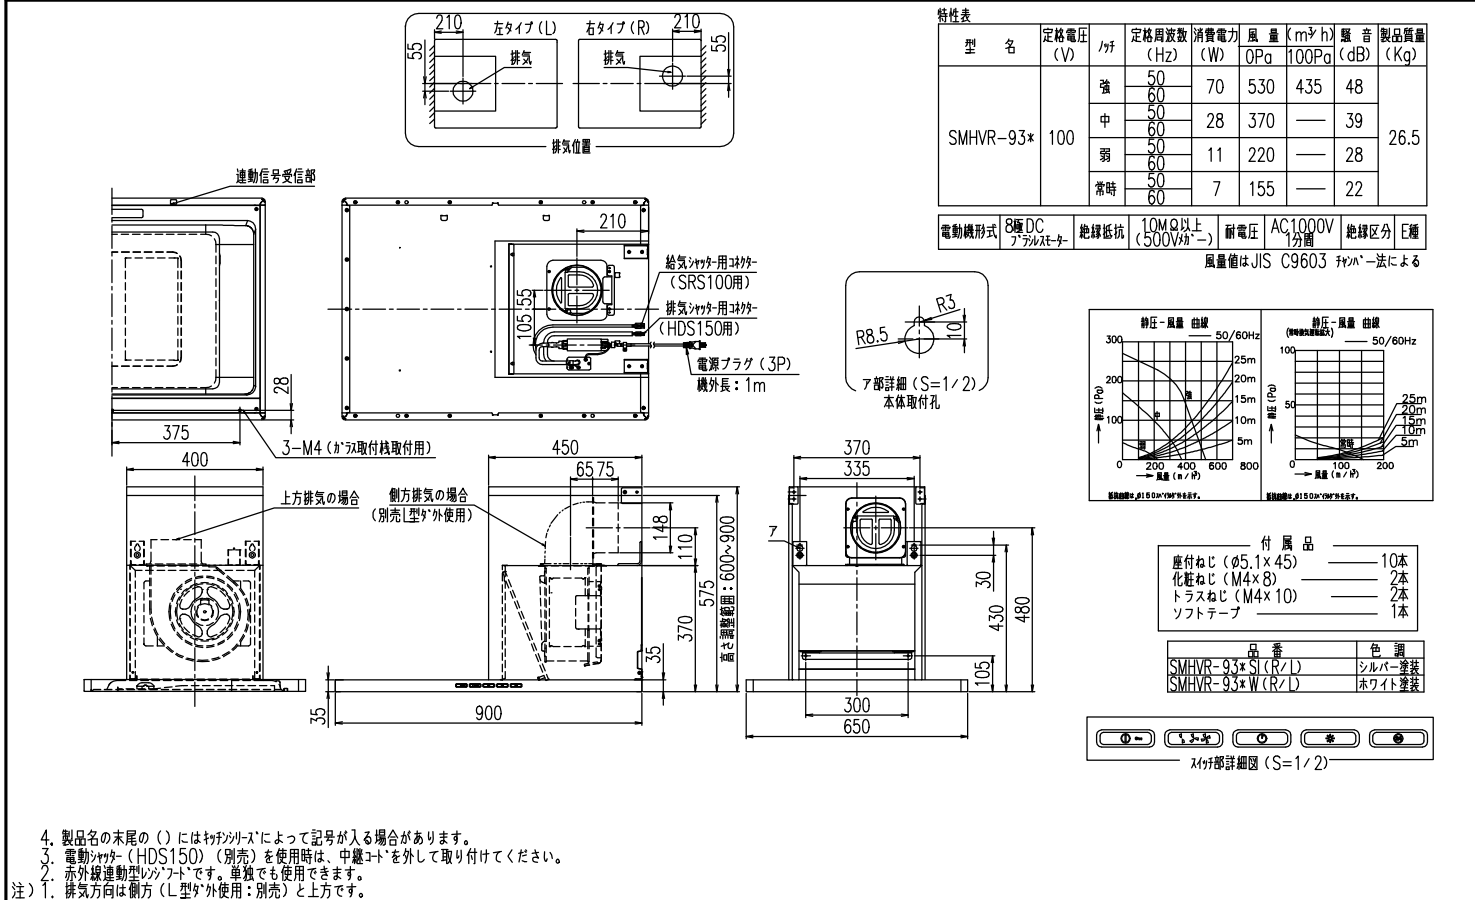

■ IHヒーター用コンセント推奨位置図 / 側面設置の場合

※コンセントや電源プラグが、引き出しおよびIHヒーター用仕切板（オプション）に接触しないように注意してください。					
※木製キッチンの配管スペース付キャビネットは、キャビネット内にコンセントを取り付けるスペースがありませんので、別売のコンセントベース（W-SOCKET-B）などを使用して配管スペース内にコンセントを設置してください。					

※コンセントや電源プラグが、引き出しおよびIHヒーター用仕切板（オプション）に接触しないように注意してください。					
※木製キッチンの配管スペース付キャビネットは、キャビネット内にコンセントを取り付けるスペースがありませんので、別売のコンセントベース（W-SOCKET-B）などを使用して配管スペース内にコンセントを設置してください。					

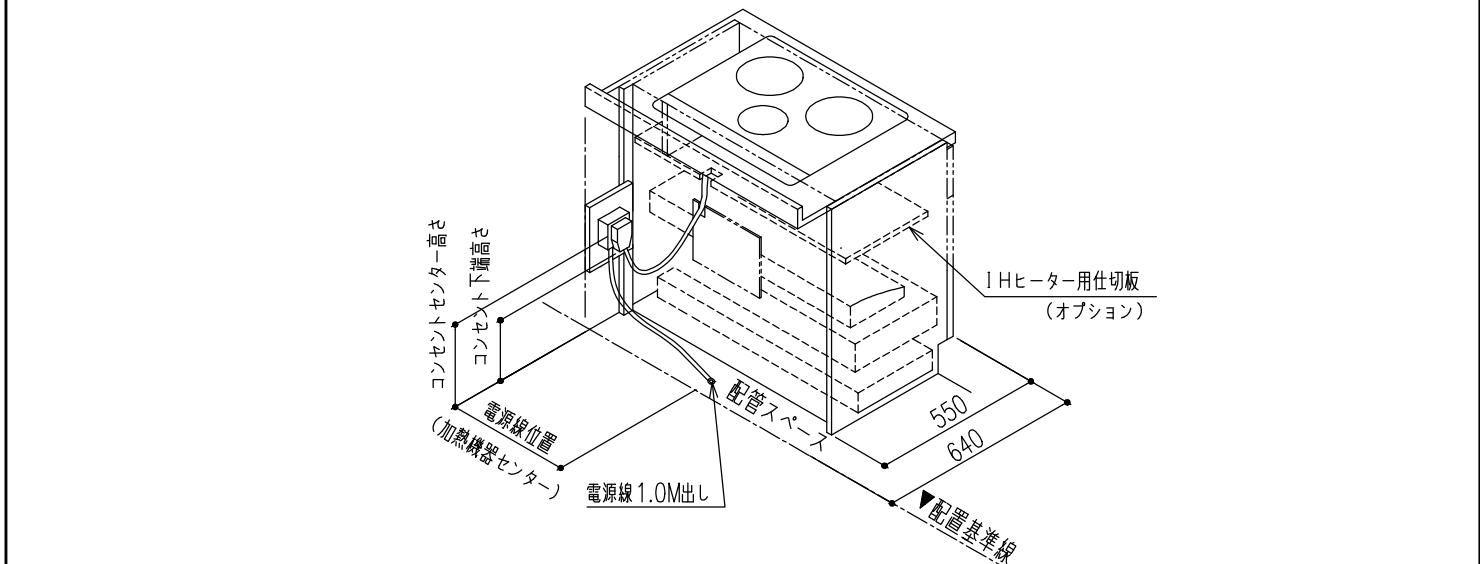


注意：引き出しおよびIHヒーター用仕切板（オプション）に接触しないように上記寸法を参照してください。


■ 止水栓図（床立上げ）

床立ち上げ配管

配管立ち上げ寸法は、止水栓芯までの高さを示しています。

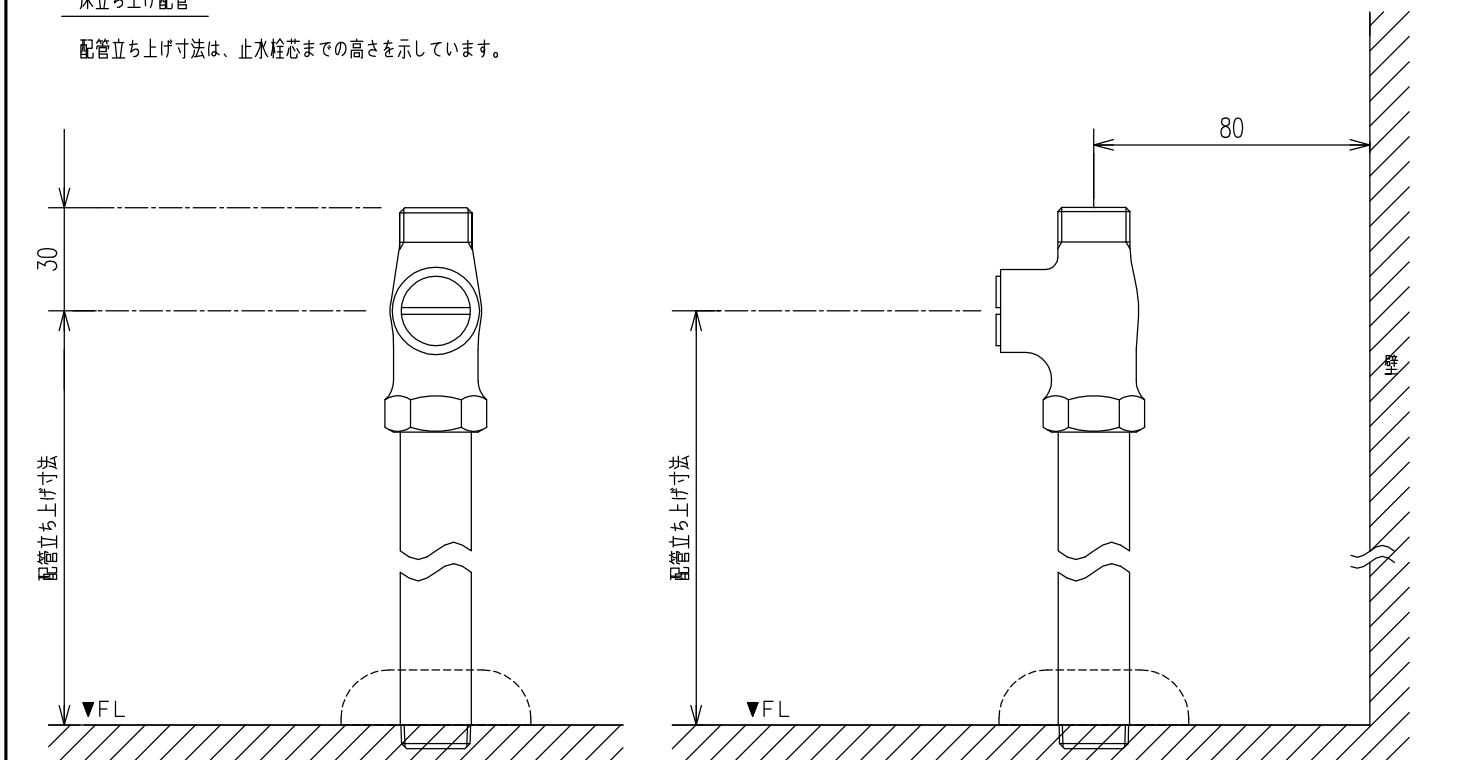

■ タッチレス水栓ナビッシュ 推奨電源位置図

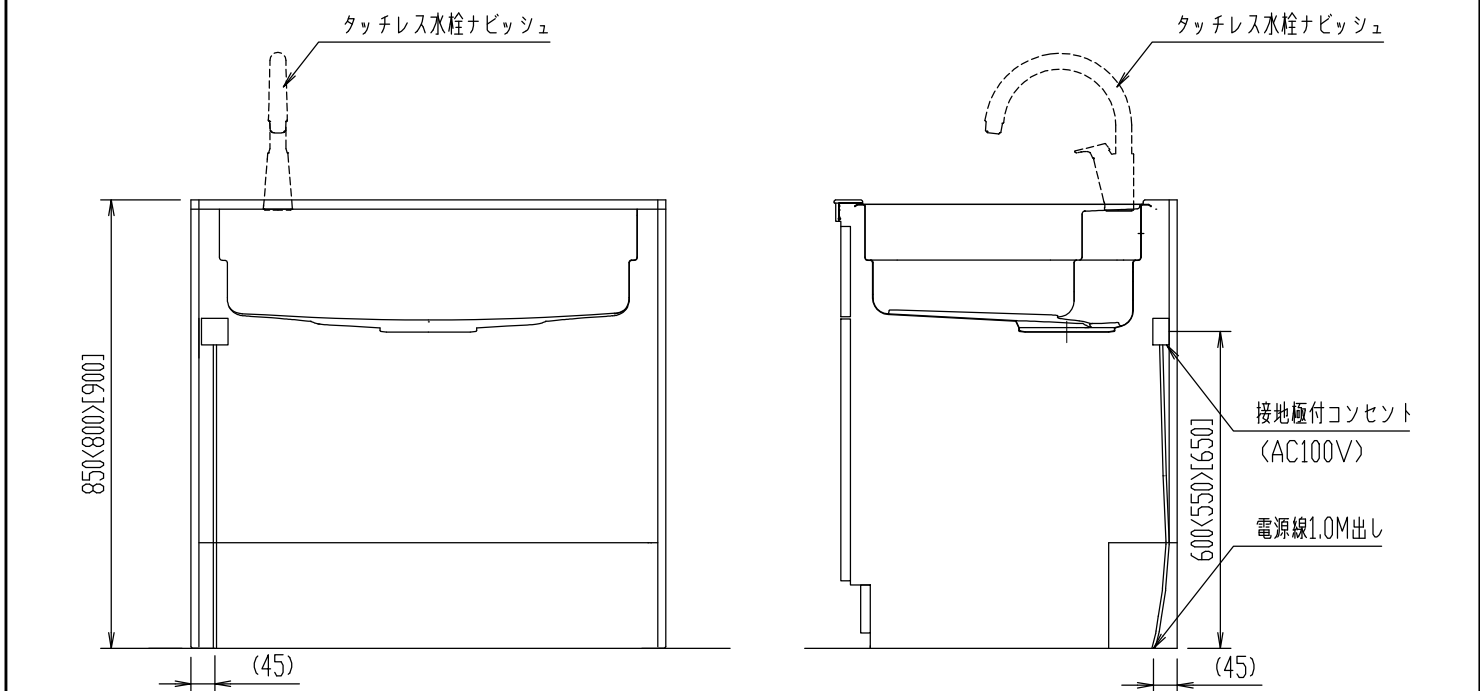




○水栓がシンク右側の場合、電源位置は左右対象の位置にしてください。
○ $\triangle$ 内寸法はワークトップ高さ80cmの場合、 $\square$ 内寸法はワークトップ高さ90cmの場合。

特記事項 扉色 WK3:ソリッドホワイト 取手 [J]スリム取手 (シルバー) ワークトップカラー 【DW】ソルティホワイト	物件名	伊藤友章 様邸【11/25ご依頼】	案件No.	図面名	担当	図面	図番 : 株式会社 LIXIL
	仕様		A2410DDDE5RWP	機能図	栗野 友仁		
			見積No.	縮尺	日付		
		ES21	M24105290035-011-2		2024.11.26		

■ キッチン取付者さま向け 動画コンテンツ ■

商品取付けの注意点を2次元コードでご視聴いただけます。
取付日より前に、是非ご確認ください。

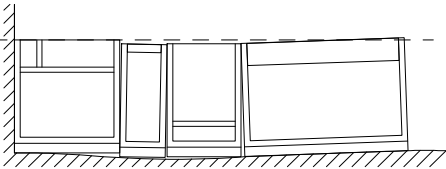荷扱い・搬入	カウンター開梱搬入「養生ツール」	不陸の確認と調整	マグネットキッチンパネル
荷扱い・搬入	カウンター開梱搬入「養生ツール」のご紹介		マグネット キッチンパネル「取付・設置」ポイント
作成日：2024年10月01日	作成日：2024年10月01日	作成日：2024年02月07日	作成日：2024年03月06日




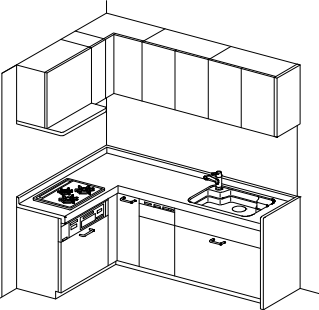
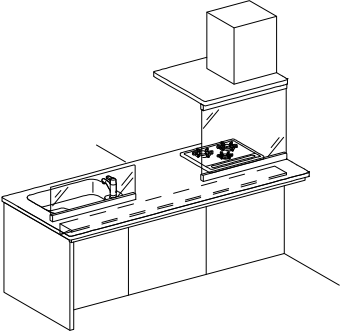
人造大理石カウンターL型キッチン	センターキッチン（ペニンシュラ型）		
			
作成日：2024年02月07日	作成日：2024年02月07日		

--	--	--	--

特記事項 扉色 WK3:ソリッドホワイト 取手 [J]スリム取手 (シルバー) ワークトップカラー 【DW】ソルティホワイト	物件名	伊藤友章 様邸【11/25ご依頼】	案件No.	図面名	担当	図面	図番
	仕様	ES21	A2410DDDD0E5RWP	機能図	栗野 友仁		株式会社 LIXIL
			見積No.	縮尺	日付		
			M24105290035-011-2		2024.11.26		

■ キッチン取付者さま向け 動画コンテンツ ■

商品取付けの注意点を2次元コードでご視聴いただけます。
取付日より前に、是非ご確認ください。

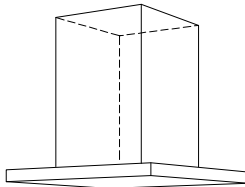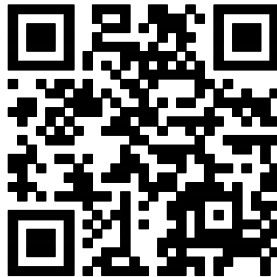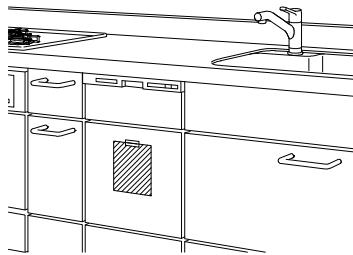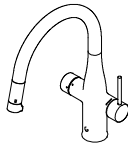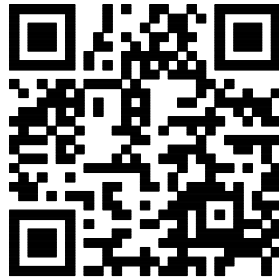センターフード型レンジフード (天吊りフード)  作成日：2024年06月03日 		I H加熱機器関連 I H加熱機器 仕切り板 作成日：2024年02月07日 		食器洗い乾燥機  作成日：2024年02月07日 		ミネラル浄水栓 Greentap  作成日：2024年06月03日 			
特記事項 扉色 WK3:ソリッドホワイト 取手 [J]スリム取手 (シルバー) ワークトップカラー 【DW】ソルティホワイト		物件名 伊藤友章 様邸【11/25ご依頼】 仕様 ES21		案件No.		図面名	担当	図面	図番
				A2410DDD0E5RWP		機能図	栗野 友仁		株式会社 LIXIL
				見積No.		縮尺	日付		
				M24105290035-011-2			2024.11.26		