


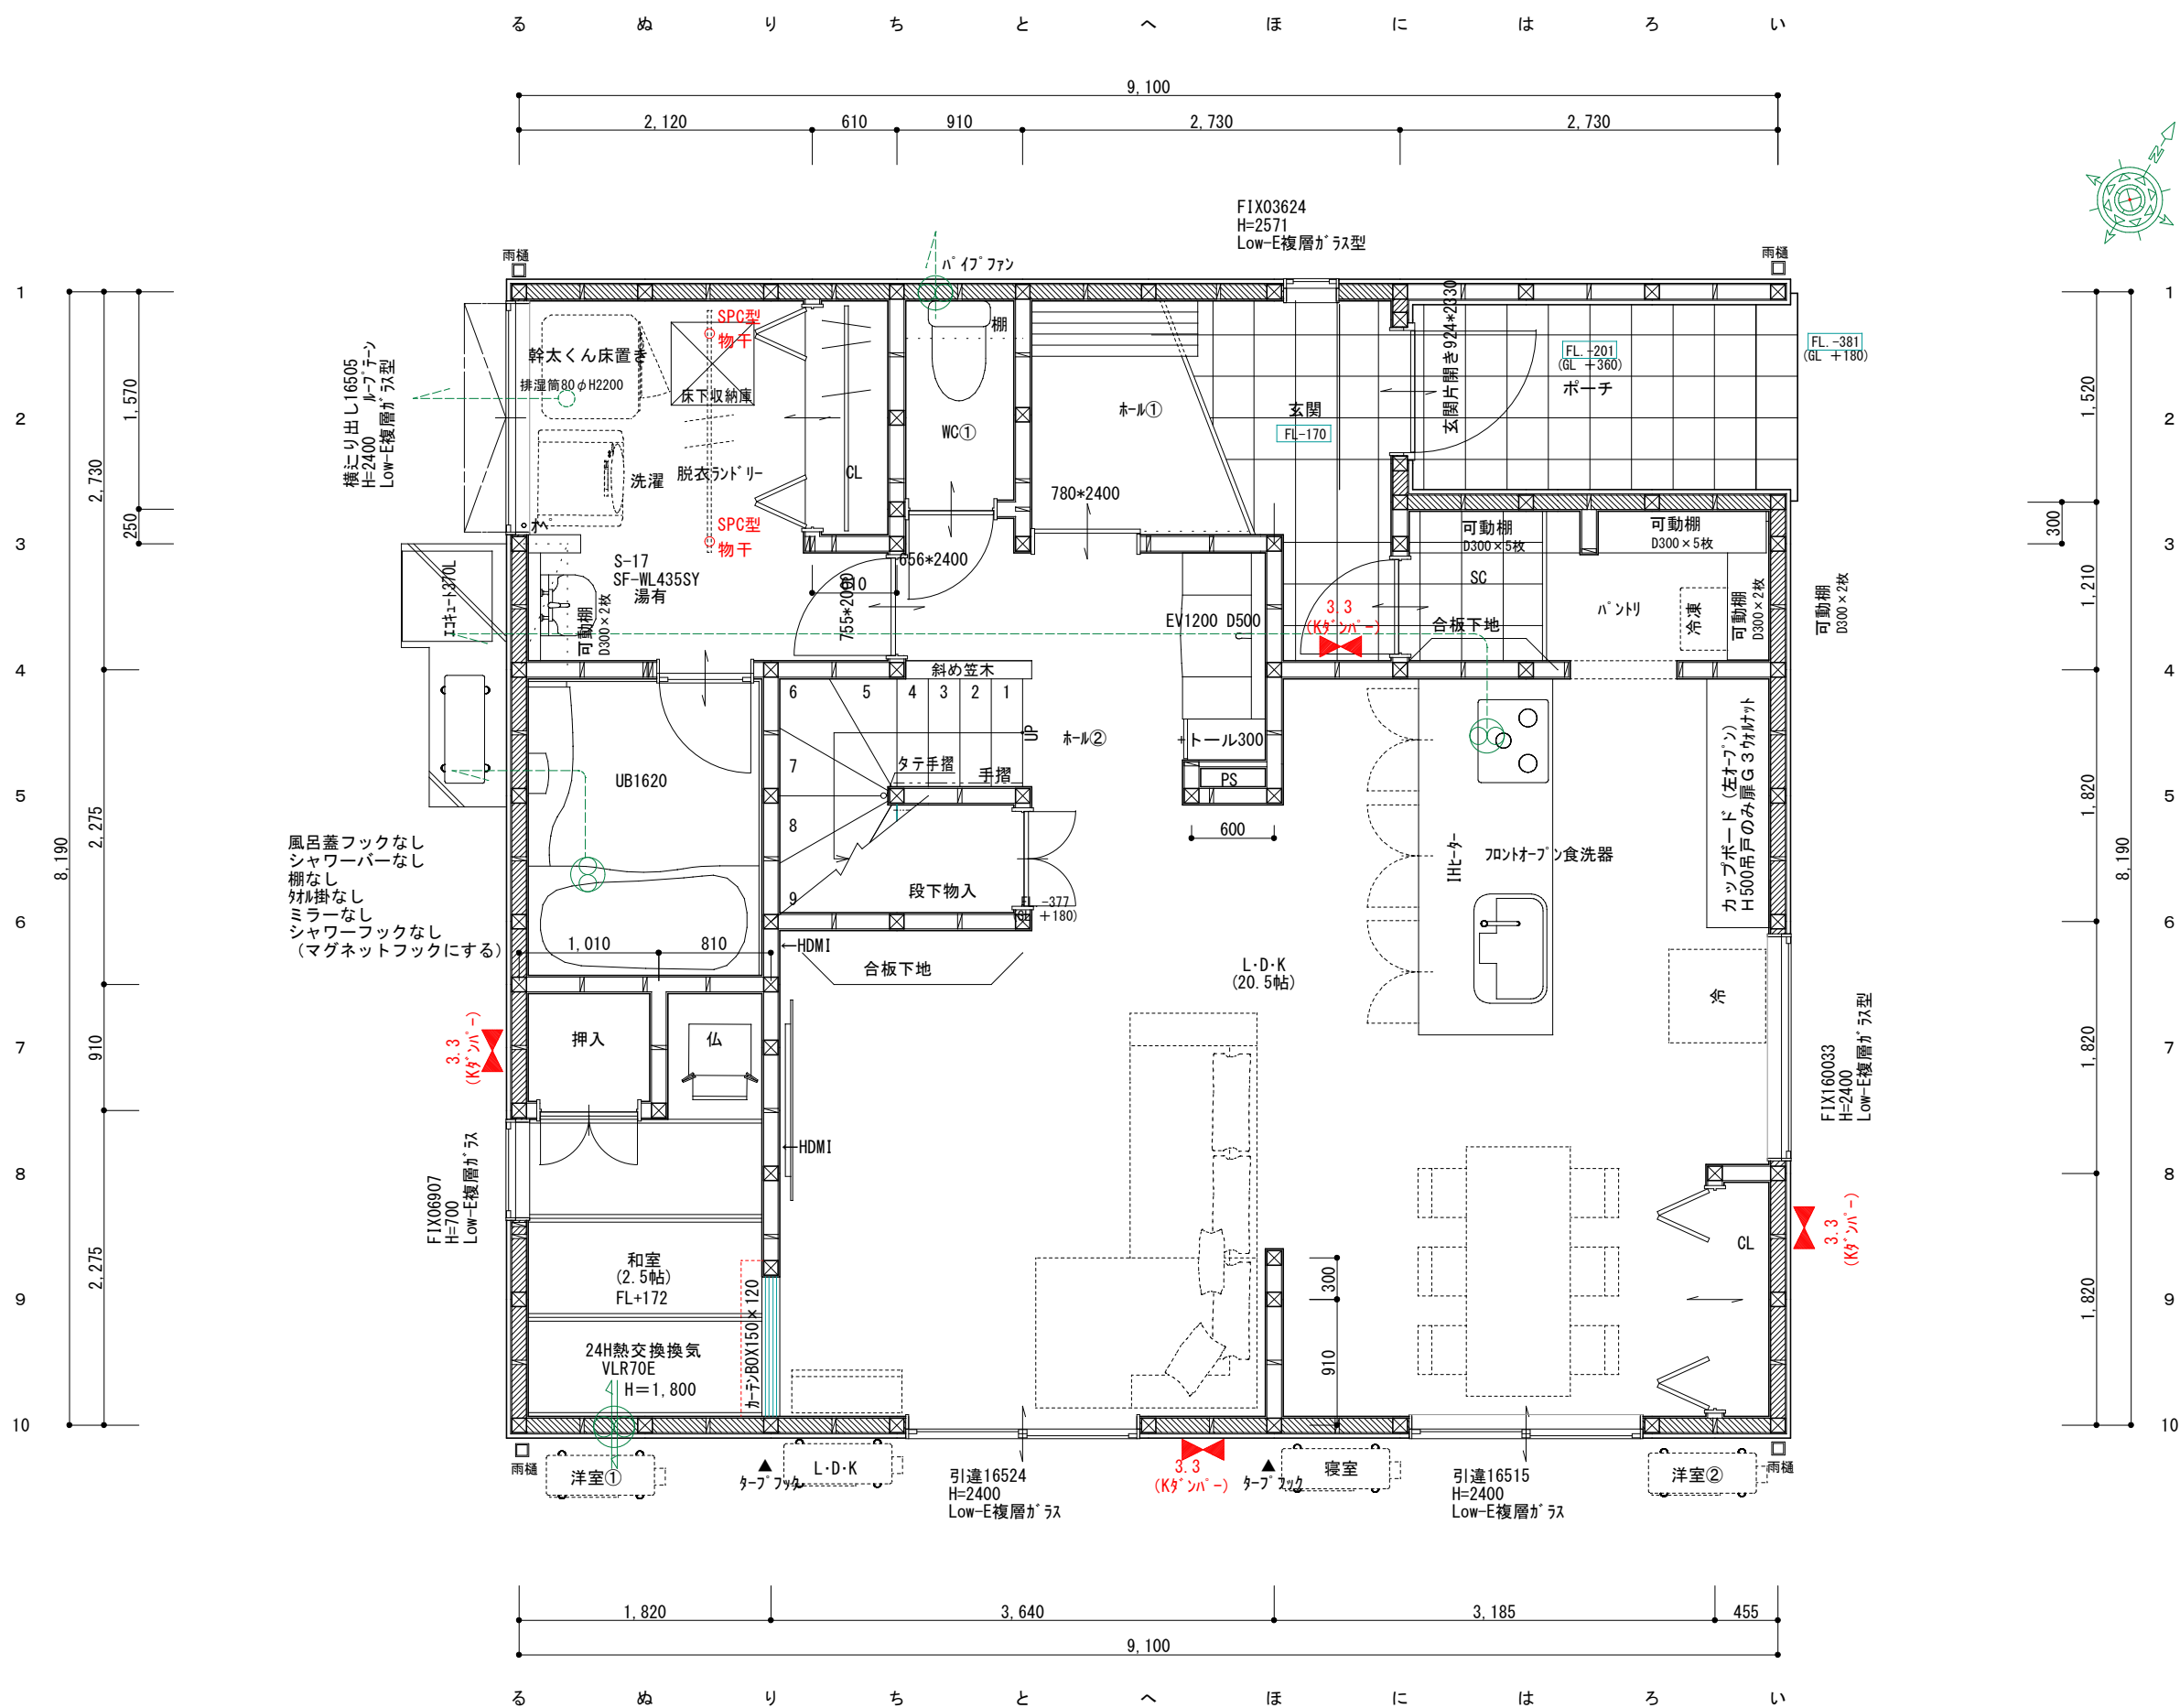

|                                                                                            |      |          |    |
|--------------------------------------------------------------------------------------------|------|----------|----|
| 壁付付                                                                                        |      | 住宅用火災報知器 | 数量 |
| <br>熱感知 | 熱感知器 | 電池式(单独型) |    |
|                                                                                            |      | 露出型      |    |
| 壁付付                                                                                        |      | 住宅用火災報知器 | 数量 |
| <br>煙感知 | 煙感知器 | 電池式(单独型) |    |
|                                                                                            |      | 露出型      |    |

- ※ 煙感知器は壁・梁より600mm以上離す  
壁に取付ける場合、  
天井から150mm以上500mm以内離す  
換気扇、エアコン吹出口から1500mm以上離す
- ※ 全室LED照明とする。
- ※ 標準天井高さ2,400

**\* 凡例**

 管柱 (105 × 105)

 K<sup>g</sup> ヲバ -  
(3.30倍 FRM-0641)

 片筋違い  
(2.00倍 45 × 90)  
(例 左:柱脚 右:柱頭)

 たすき掛筋違い  
(4.00倍 45 × 90)

構造用合板 (2.50倍)  
(t=9 45t)

 床点検口

 天井点検口

 換気扇

 熱交換換気扇VLR-70

| コスモワイド スクエア<br>スマートデザイン（外部） |                  |
|-----------------------------|------------------|
| 凡例                          |                  |
| ①                           | コンセント 1ヶ口        |
| ②                           | コンセント 2ヶ口        |
| ③                           | コンセント 3ヶ口        |
| ①ET                         | コンセント1ヶ口接地ターミナル付 |
| ②ET                         | コンセント2ヶ口接地ターミナル付 |
| WP                          | コンセント 防水型        |
|                             | エアコン用コンセント       |
|                             | 200V用コンセント       |
| WP                          | 防雨入線プレート         |
|                             | スイッチ             |
| ● 3                         | 3路スイッチ           |
| ● 4                         | 4路スイッチ           |
| ⊗                           | 直結電源             |
| TV                          | テレビ取出口           |
| TEL                         | 電話取出口（テレホンガイド）   |
| LAN                         | LAN取出口（テレホンガイド）  |
|                             | 壁照明              |
|                             | リモコン（給湯関係・ルーフ）   |
|                             | メーター             |
|                             | 分電盤              |
| ○                           | チャイム             |

※ACコンセント天井付け  
※TVアンテナ工事  
※スイッチはFL+1100、コンセントはFL+200