

■ 仕 様			■ HEAT20 G1		
断熱工事		■ 床:カネライトフォーム t65 ■ 土間床等の外周:スタイロフォームAT t25 ■ 壁:アクアフォームLITE吹付 t85 ■ 天井:アクファフォームLITE吹付 t170			
床下換気		■ 基礎パッキン JOTO (玄関・UB周り:気密基礎パッキン)			
防虫防蟻		■ 土壌処理・木部 ガントナーMC			
■ 外 部 仕 上 表			■ 22条地域		
部位		仕上・仕様・メーカー		色番・品番	
屋根		■ ガルバリウム鋼板(t0.35)UK立平 ニスクカラーPro GH 軒先通気金物 日本住環境株式会社【REV-15】		GHK01 Sブラック	
パラペット笠木		■ なし			
破風・鼻隠		■ なし			
雨樋	(軒樋)	■ Panasonic サーフেসケアFS-I型		ブラック	
	(縦樋)	■ Panasonic S30角樋		ブラック	
軒天	屋根軒	■ なし			
	ポーチ軒	■ 神島化学 t= 6mm 軒天ボード エンボス		Wチャコールブラック	
	バルコニー軒	■ なし			
オーバーハング水切り		■ ガルバリウム鋼板 ※外壁合わせ JOTO:HF-A3550		ブラック	
外壁 ※下地面材:タイガーEXハイパー 防火認定 PC030BE-4028	通気金物(15mm)	■メイン	ニチハ エモンエクセラード16 Vシリーズ リーガストーン調V	ランダムMGブラック	
		■アクセントA	なし		
		■アクセントB	なし		
玄関ポーチ		■ 床 玄関タイルに同じ		-	
基礎		■ 立上り巾木: モルタル刷毛引き		-	
基礎水切り金物		■ JOTO鋼板製 防鼠材付き水切り JOTO:WMF-N35		ブラック	
バルコニー	床・内壁	■ なし		-	
	笠木	■ なし			
外部建具		■ LIXIL EW(アルゴンガス高遮熱仕様LowE複層ガラスグリーン) ・SD、TSで記載がないものは、オペレーターハンドルとする ・オペレーター付サッシは固定網戸とする ・グレモンハンドル式サッシの選択箇所は可動網戸とする		外観 ブラック 内観 ホワイト ※樹脂パッキン・網戸付	
シャッター		■ なし			
玄関扉		■ LIXIL ジエスタ2 K2仕様 LIXILファミロック タグキー×3 (電池式)		ドア型: M17 型 ドア色: カームブラック ハンドル: S型ハンドル 色 ブラック	
外部物干し金物		■			
換気フード		■ 局所換気扇(トイレ 浴室 キッチンフード) 防火ダンパー無		外気フード: ブラック	
		■ ダクトレス熱交換換気システム (日本スティーベル株式会社) VLR-70E 防火ダンパー無		外気フード: B ブラック 室内パネル ホワイト	

■ 構 造 概 要					
基礎	■ RCベタ基礎コンクリート				
通し柱・管柱	■ 構造用集成材 105×105		間柱	■ 集成材	
土台	■ 桧 105×105	大引き	■ 桧 90*90	筋交い	■ 構造用製材 火打梁 ■ 鋼製火打(当社基準により米松あり)
桁・梁	■ 構造用製材及び集成材		制震装置	■ Kダンパー (株)アイ・エム・エー	
■ 設 備 装 着 品					
住宅設備	部位	メーカー	商品名 ※ 詳細は見積り、プレゼン参照	見積りNo.	(日付)
	キッチン	LIXIL	■ ES ペニンシュラ型 スライドストッカータイプ (扉 ソリッドホワイト)	見積り番号 : (日付)	A24105290035-006-2 2024.11.11
	バックカウンタ ※オプション	LIXIL	■ ES L1800(W900スライドストッカー+マルチスペース) 引き出しTレール仕様(扉 ソリッドホワイト) 吊戸棚H500(ライトグリーン)	見積り番号 : (日付)	A24105290035-006-3 2024.11.11
	浴室	LIXIL	■ AX1620 洗い場広タイプ ドア仕様	見積り番号 : (日付)	A24105290035-006-1 2024.11.11
	1Fトイレ	LIXIL	■ ベーシアシャワートイレ 白 ● タオル掛け: KF-AA70D(リング) タンク手洗 無し ● 紙巻き器: CF-AA22H /WA	見積り番号 : (日付)	A24105290035-006-5 2024.11.11
	2Fトイレ	LIXIL	■ ベーシアシャワートイレ 白 ● タオル掛け: KF-AA70D(リング) タンク手洗 有り ● 紙巻き器: CF-AA22H /WA	見積り番号 : (日付)	A24105290035-006-6 2024.11.11
	洗面台	LIXIL	■ EV W900(D500タイプ) 扉:グロスホワイト [引出しタイプ シングルハンドシャワー スタンダードLED三面鏡 その他 トールキャビネット300 ● タオル掛け: KF-AA71D(バー)	見積り番号 : (日付)	A24105290035-006-4 2024.11.11
	スロップシンク	LIXIL	■ S-17/BW1 シングルバー混合水栓SF-WM435SY(170)	A24105290035-006-7 2024.11.11	
給排水設備	給湯器	■ エコキュート370L Panasonic NSシリーズ スタンダードモデル 追い焚きフルオート			
	排水	■ 合併浄化槽 5人槽 ポンプアップ無			
	外水栓	■ 1 カ所 (平面図参照)	■ 外部立栓柱: PVC製 水栓柱12型グリーンシリーズ【前澤化成工業】		
	外部ガーデンパン	■ 無し			
	その他	■ 洗濯機用単水栓: 緊急止水弁付		■ 洗濯機用排水: トラップ金物(標準)	
	■ 排水さや管(長期優良住宅仕様)				
ガス配管設備	■ あり(LPG) (配置図・平面図参照 ※乾太くん用)				
電気設備	インターホン	■ パナソニック VL-SZ30KL			
	TVアンテナ	■ UHF + BS・110度CS／CSアンテナ [2K・4K・8K対応] ■ブラック ※電波状況によりホワイトになる可能性あり			
	エアコン	■ 設置場所:			
	ソーラー ※標準搭載	■ あり(Qセルズ)	12 枚	5.28 KW	Re.RISE-G3 440 (1722×1134×30)
	■ 屋外パワコン 西面				
その他					


	浜 岡 一 級 総 合 設 計 事 務 所 一級建築士事務所 静岡県知事登録第 (10)2441 号 一級建築士 大臣登録第 365879 号 西原利昌	 PG HOUSE	株式会社 LIFEFUND InDesign office 一級建築士事務所 事務所登録 (2)第7595号 一級建築士登録 第179770号 鈴木 達男 〒432-8023 静岡県浜松市中央区鴨江3丁目70番23号	年 月 日	件名		設計	IC	工務	図 番
				2024.11.23	伊藤友章 様邸 新築工事					
				縮尺	図面		倉田		青島	1-1
					仕上表 1					


内 部 仕 上 表 （壁下地:石膏ボード12.5mm/天井下地:9.5mm）※脱衣室:床合板特類 下地									
階		床	巾木	壁	品番	廻 縁	天 井	品番	特記事項
1F	ポーチ	LIXILパセオ300/PSO-FIO 4							
	玄関	LIXILパセオ300/PSO-FIO 4	ライン巾木(W)	ビニルクロス	SLP-251	突付	ビニルクロス	SLP-251	
	SC	LIXILパセオ300/PSO-FIO 4	ライン巾木(W)	ビニルクロス	SLP-251	突付	ビニルクロス	SLP-251	
	パントリー	イタ銘木フロアースティックt12 ナラ桜3P	ライン巾木(W)	ビニルクロス	SLP-251	突付	ビニルクロス	SLP-251	
	ホール①								
	ホール②/洗面	イタ銘木フロアースティックt12 ナラ桜3P	ライン巾木(W)	ビニルクロス	SLP-251	突付	ビニルクロス	SLP-251	
	WC①	フロアタイルt2.3 サンゲツIS-2071	H40ソフト巾木W97	ビニルクロス	SLP-251	突付	ビニルクロス	SLP-251	ペーパーニッチ/床ニッチ
	脱衣ランドリー	フロアタイルt2.3 サンゲツIS-2071	H40ソフト巾木W97	ビニルクロス	SLP-251	突付	ビニルクロス	SLP-251	SPC型物干 乾太くん台
	ダイニングキッチン	イタ銘木フロアースティックt12 ナラ桜3P	ライン巾木(W)	ビニルクロス	SLP-251	突付	ビニルクロス	SLP-251	
	リビング	イタ銘木フロアースティックt12 ナラ桜3P	ライン巾木(W)	ビニルクロス	SLP-251	突付	ビニルクロス	SLP-251	
	和室	1畳縁ありスタイロ畳 t55	畳寄せ	ビニルクロス	SLP-251	突付	ビニルクロス	SLP-251	畳縁:高田織物 浮No.13
	仏間	イタ銘木フロアースティックt12 ナラ桜3P	雑巾摺	ビニルクロス	SLP-251	突付	ビニルクロス	SLP-251	
2F	ホール③	イタ銘木フロアースティックt12 ナラ桜3P	ライン巾木(W)	ビニルクロス	SLP-251	突付	ビニルクロス	SLP-251	
	寝室	イタ銘木フロアースティックt12 ナラ桜3P	ライン巾木(W)	ビニルクロス	SLP-251	突付	ビニルクロス	SLP-251	
	洋室①	イタ銘木フロアースティックt12 ナラ桜3P	ライン巾木(W)	ビニルクロス	SLP-251	突付	ビニルクロス	SLP-251	アクセントクロス BB 8690(BEST)
	洋室②	イタ銘木フロアースティックt12 ナラ桜3P	ライン巾木(W)	ビニルクロス	SLP-251	突付	ビニルクロス	SLP-251	アクセントクロス BB 8680(BEST)
	WIC	イタ銘木フロアースティックt12 ナラ桜3P	ライン巾木(W)	ビニルクロス	SLP-251	突付	ビニルクロス	SLP-251	
	WC②	フロアタイルt2.3 サンゲツIS-2071	H40ソフト巾木W97	ビニルクロス	SLP-251	突付	ビニルクロス	SLP-251	ペーパーニッチ
物入・収納・CL etc		※接続する部屋と同仕様とする							

上 框 ※	■ LIXILラシッサS 付框30×150 色: クリエペール		
階 段	■ LIXIL KA 階段	ササラ:	プレシャスホワイト
KA階段で対応できない場合、オプション	段板: クリエペール	蹴込板:	プレシャスホワイト
ラウンド手摺	ラウンド手摺: プレシャスホワイト	手摺金物	プレシャスホワイト
にてラシッサS階段	上段框: クリエペール	長尺笠木:	LIXIL プレシャスホワイト
窓 枠	■ LIXIL スマート10	色	プレシャスホワイト
	※浴室ドア枠 フクビ3方枠 ホワイト		
天井点検口	■ 天井アルミ点検口枠 450角 TAN45BW	フクビ化学工業 ミルキーホワイト	
床下収納庫	■ 高気密型床下点検口断熱型 SPF-R6060 城東テクノ	収納付	
		(脱衣室)	ライトグレー(LG)
トイレ棚	■ 2階トイレ D250	アートランバー棚(シェルホワイト)	
室内物干し金物	■ 川口技研SPC型1セット		
LDK-カウンター	■ なし	色	
下足入 プッシュタイプ	■ LIXILラシッサS	色	リエペール
	サイズ: W1200 D400	形状:	二の字型

支給品	■ 無し
備考	可動棚アートランバー色 パントリーのみアッシュウォールナット その他はシェルホワイトとする。 受金物類は全てホワイト ※付框は30×150 プレシャスホワイト

内 部 建 具 表							
LIXIL		建具色：プレシャスホワイト		枠色 ： 扉同色		※その他、下記特記による	
ラフィス		把手 ： スクエアL（シャインニッケル） 丁番 固定枠（156） 外付戸当り ガイドピン床色合せ 引戸のみ上吊W77フモーション					
階	No	室名	形式	枠外W サイズ	デザイン	枠色	特記事項
				枠外H サイズ	建具色	把手	
1	1	脱衣ランドリー	片開き戸	—	RAA	—	明り窓・表示錠
	WD			2400	—	—	
	2	WC①	片開き戸	—	RAA	—	明り窓・表示錠
	WD			2400	—	—	
	3	ホール①	アウトセット片引	—	RAA	—	
	WD			2400	—	—	
	4	SC	片開き戸	—	RAA	—	
	WD			2400	—	—	
	5	階段下収納	観音開	—	RAA	—	
	WD			2400	—	—	
	6	ダイニングCL	折れ戸		RAA		
	WD			2400			
	7	押入	観音開	—	RAA	—	
	WD			2200	—	—	H200mm切詰
	8	WC②	片引き戸	—	RAA	—	明り窓・表示錠
	WD			2400	—	—	
	9	洋室②	片開き戸	—	RAA	—	
	WD			2400	—	—	
	10	寝室	片引き戸	—	RAA	—	
	WD			2400	—	—	
	11	洋室①	片開き戸	2400	RAA	—	
	WD				—	—	

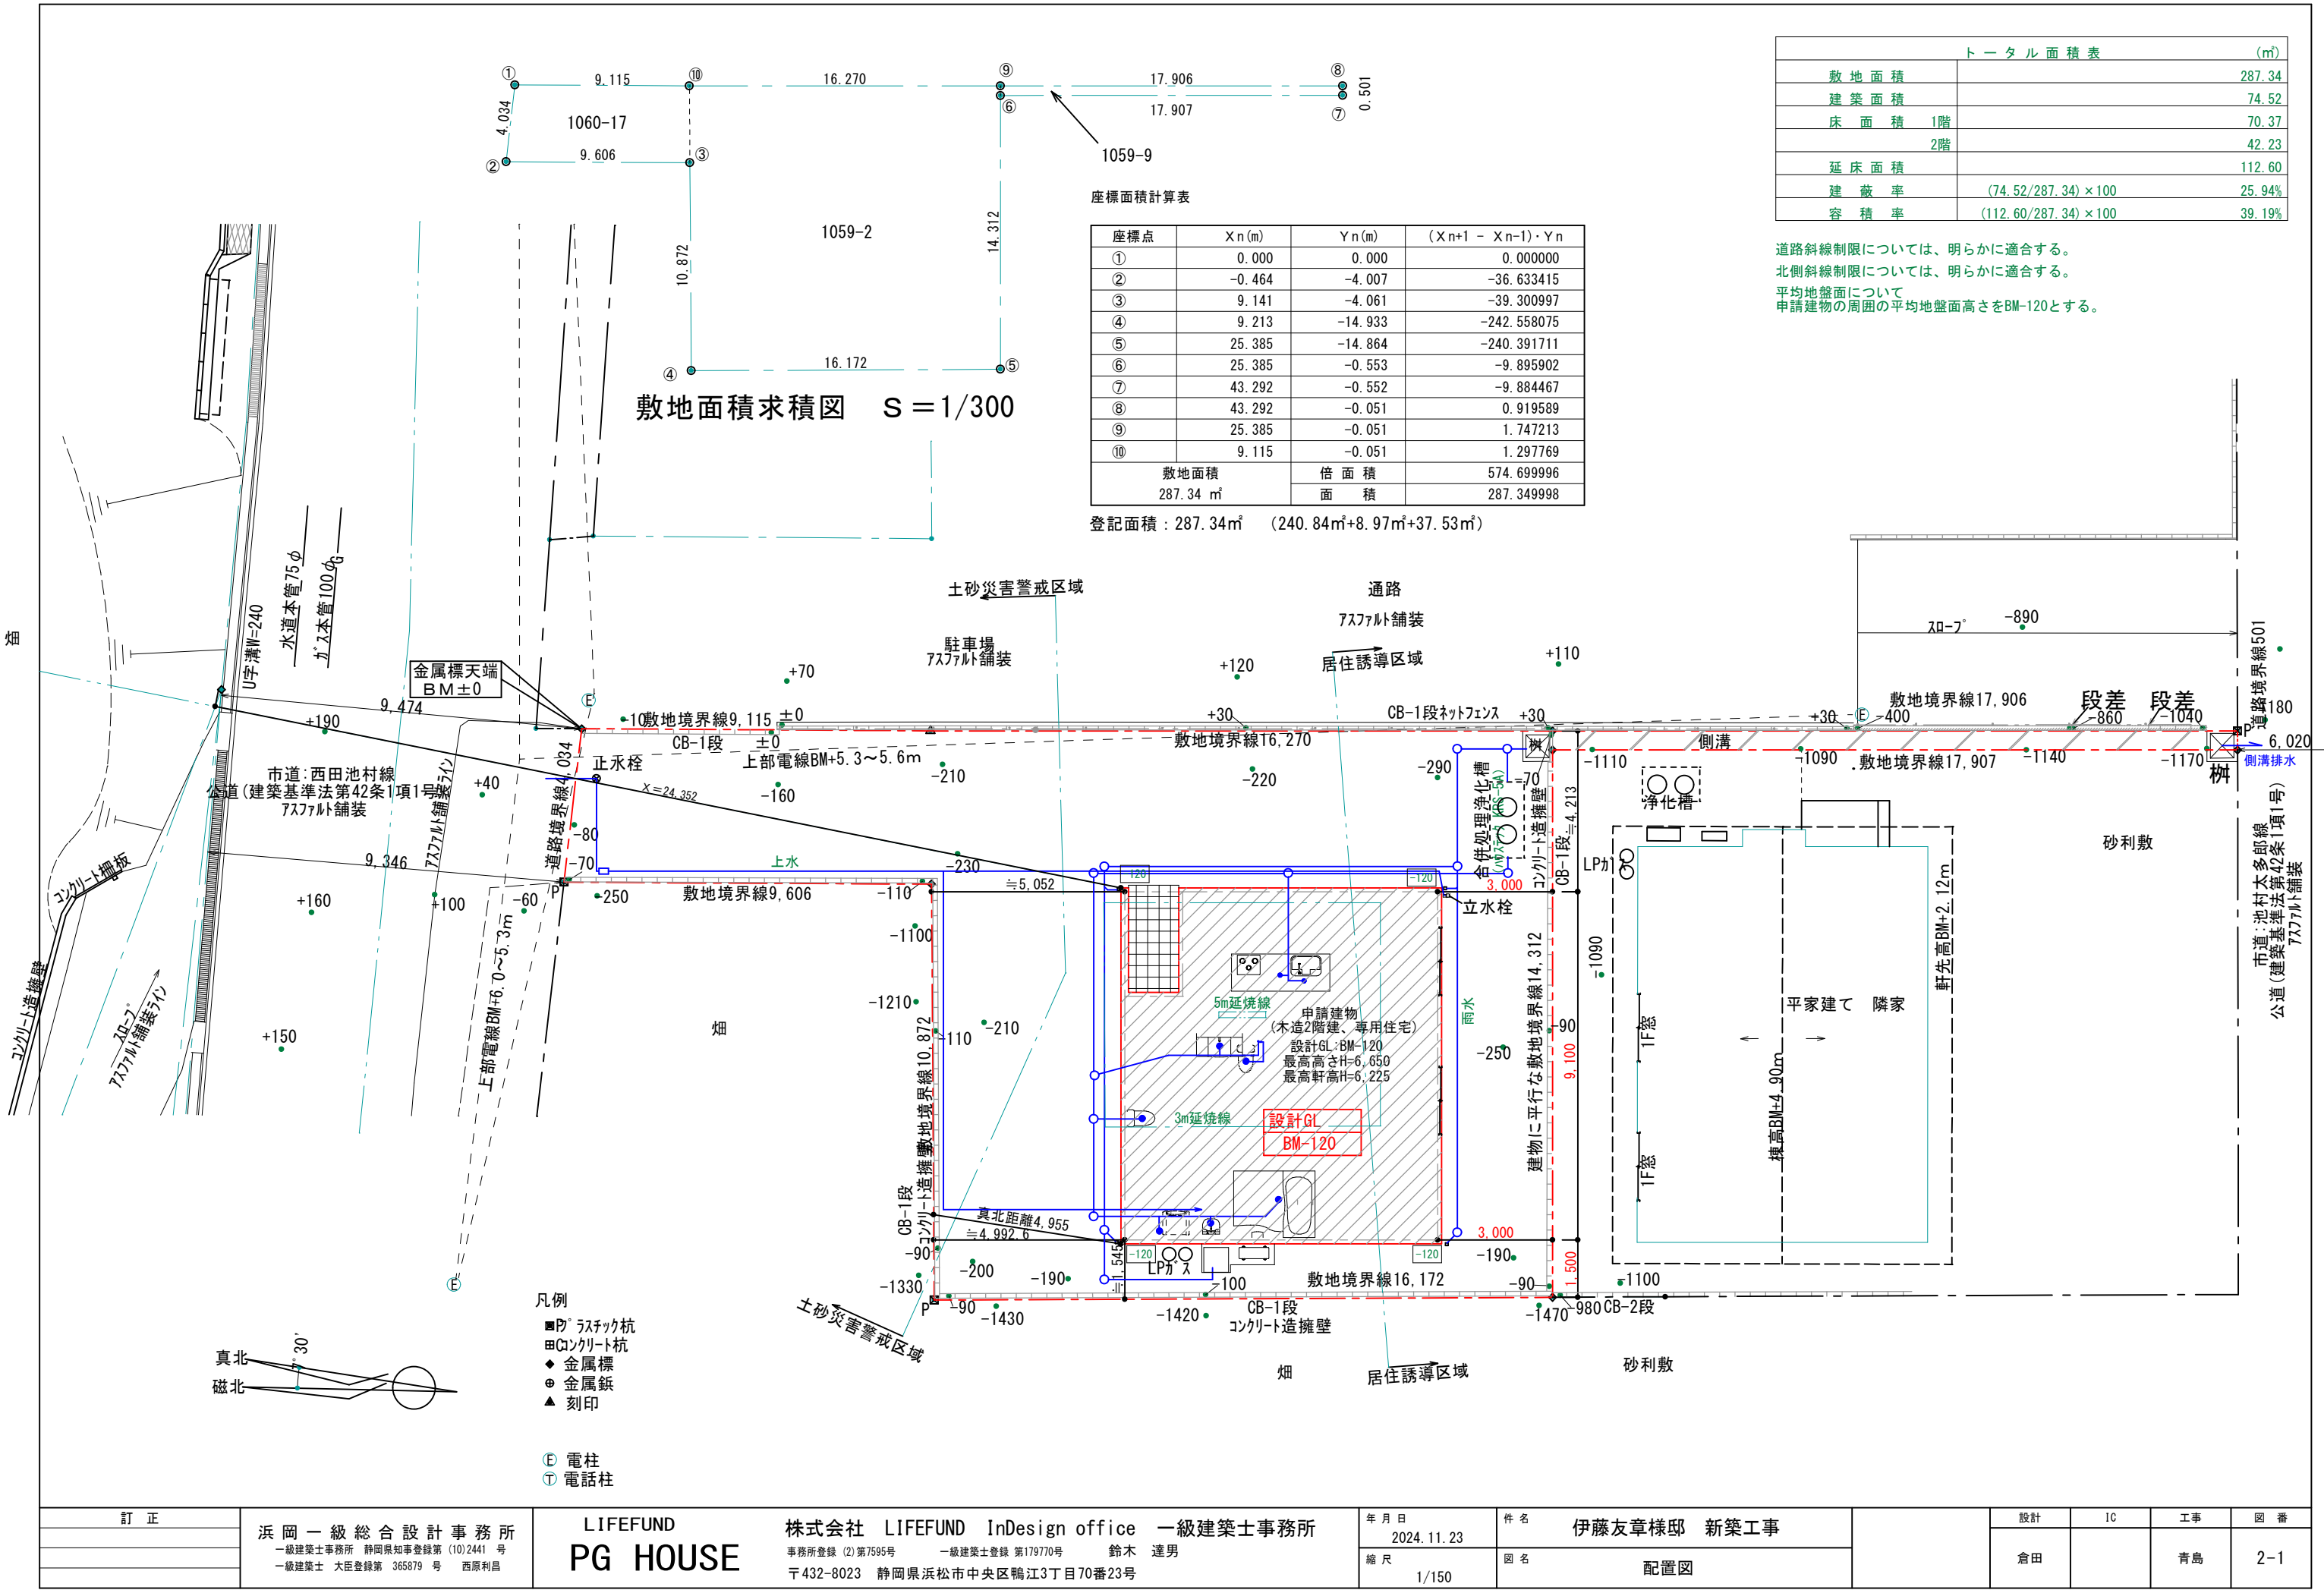

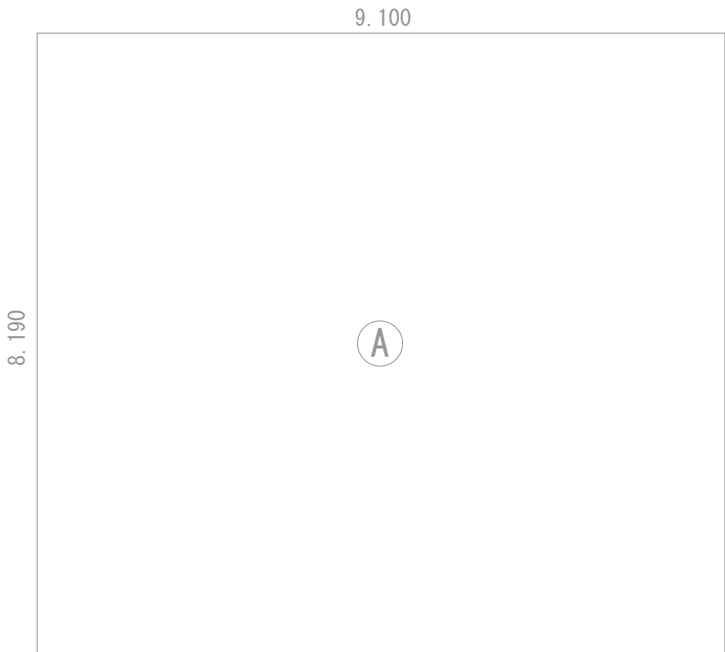


建築面積求積図 S=1/100

建築面積求積表

番号	計算式	(m)	面積 (㎡)
A	9.100 × 8.190		74.529
合計			74.529 74.52

(22.5坪)

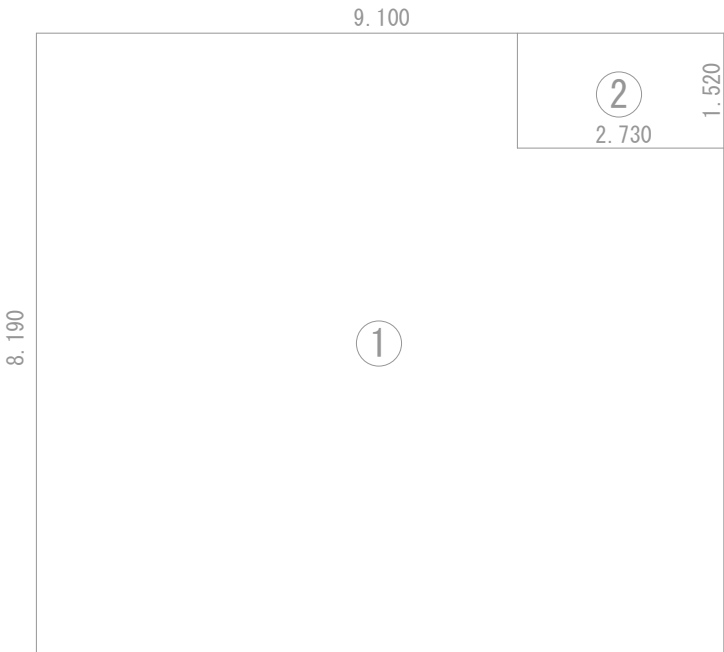


1階床面積図 S=1/100

1階床面積求積表

番号	計算式	(m)	面積 (㎡)
1	9.100 × 8.190		74.529
2	1.520 × 2.730		-4.1496
合計			70.3794 70.37

(21.2坪)

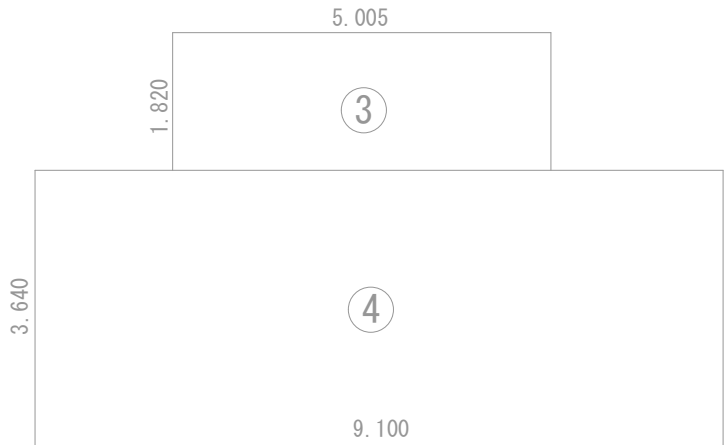

2階床面積図 S=1/100

2階床面積求積表


番号	計算式	(m)	面積 (㎡)
3	5.005 × 1.820		9.1091
4	3.640 × 3.640		33.124
合計			42.2331 42.23


(12.7坪)


延べ床面積表

	番号	(m)	面積 (㎡)
1階床面積	1 - 2		70.37
2階床面積	3 + 4		42.23
合計			112.60

(34.0坪)

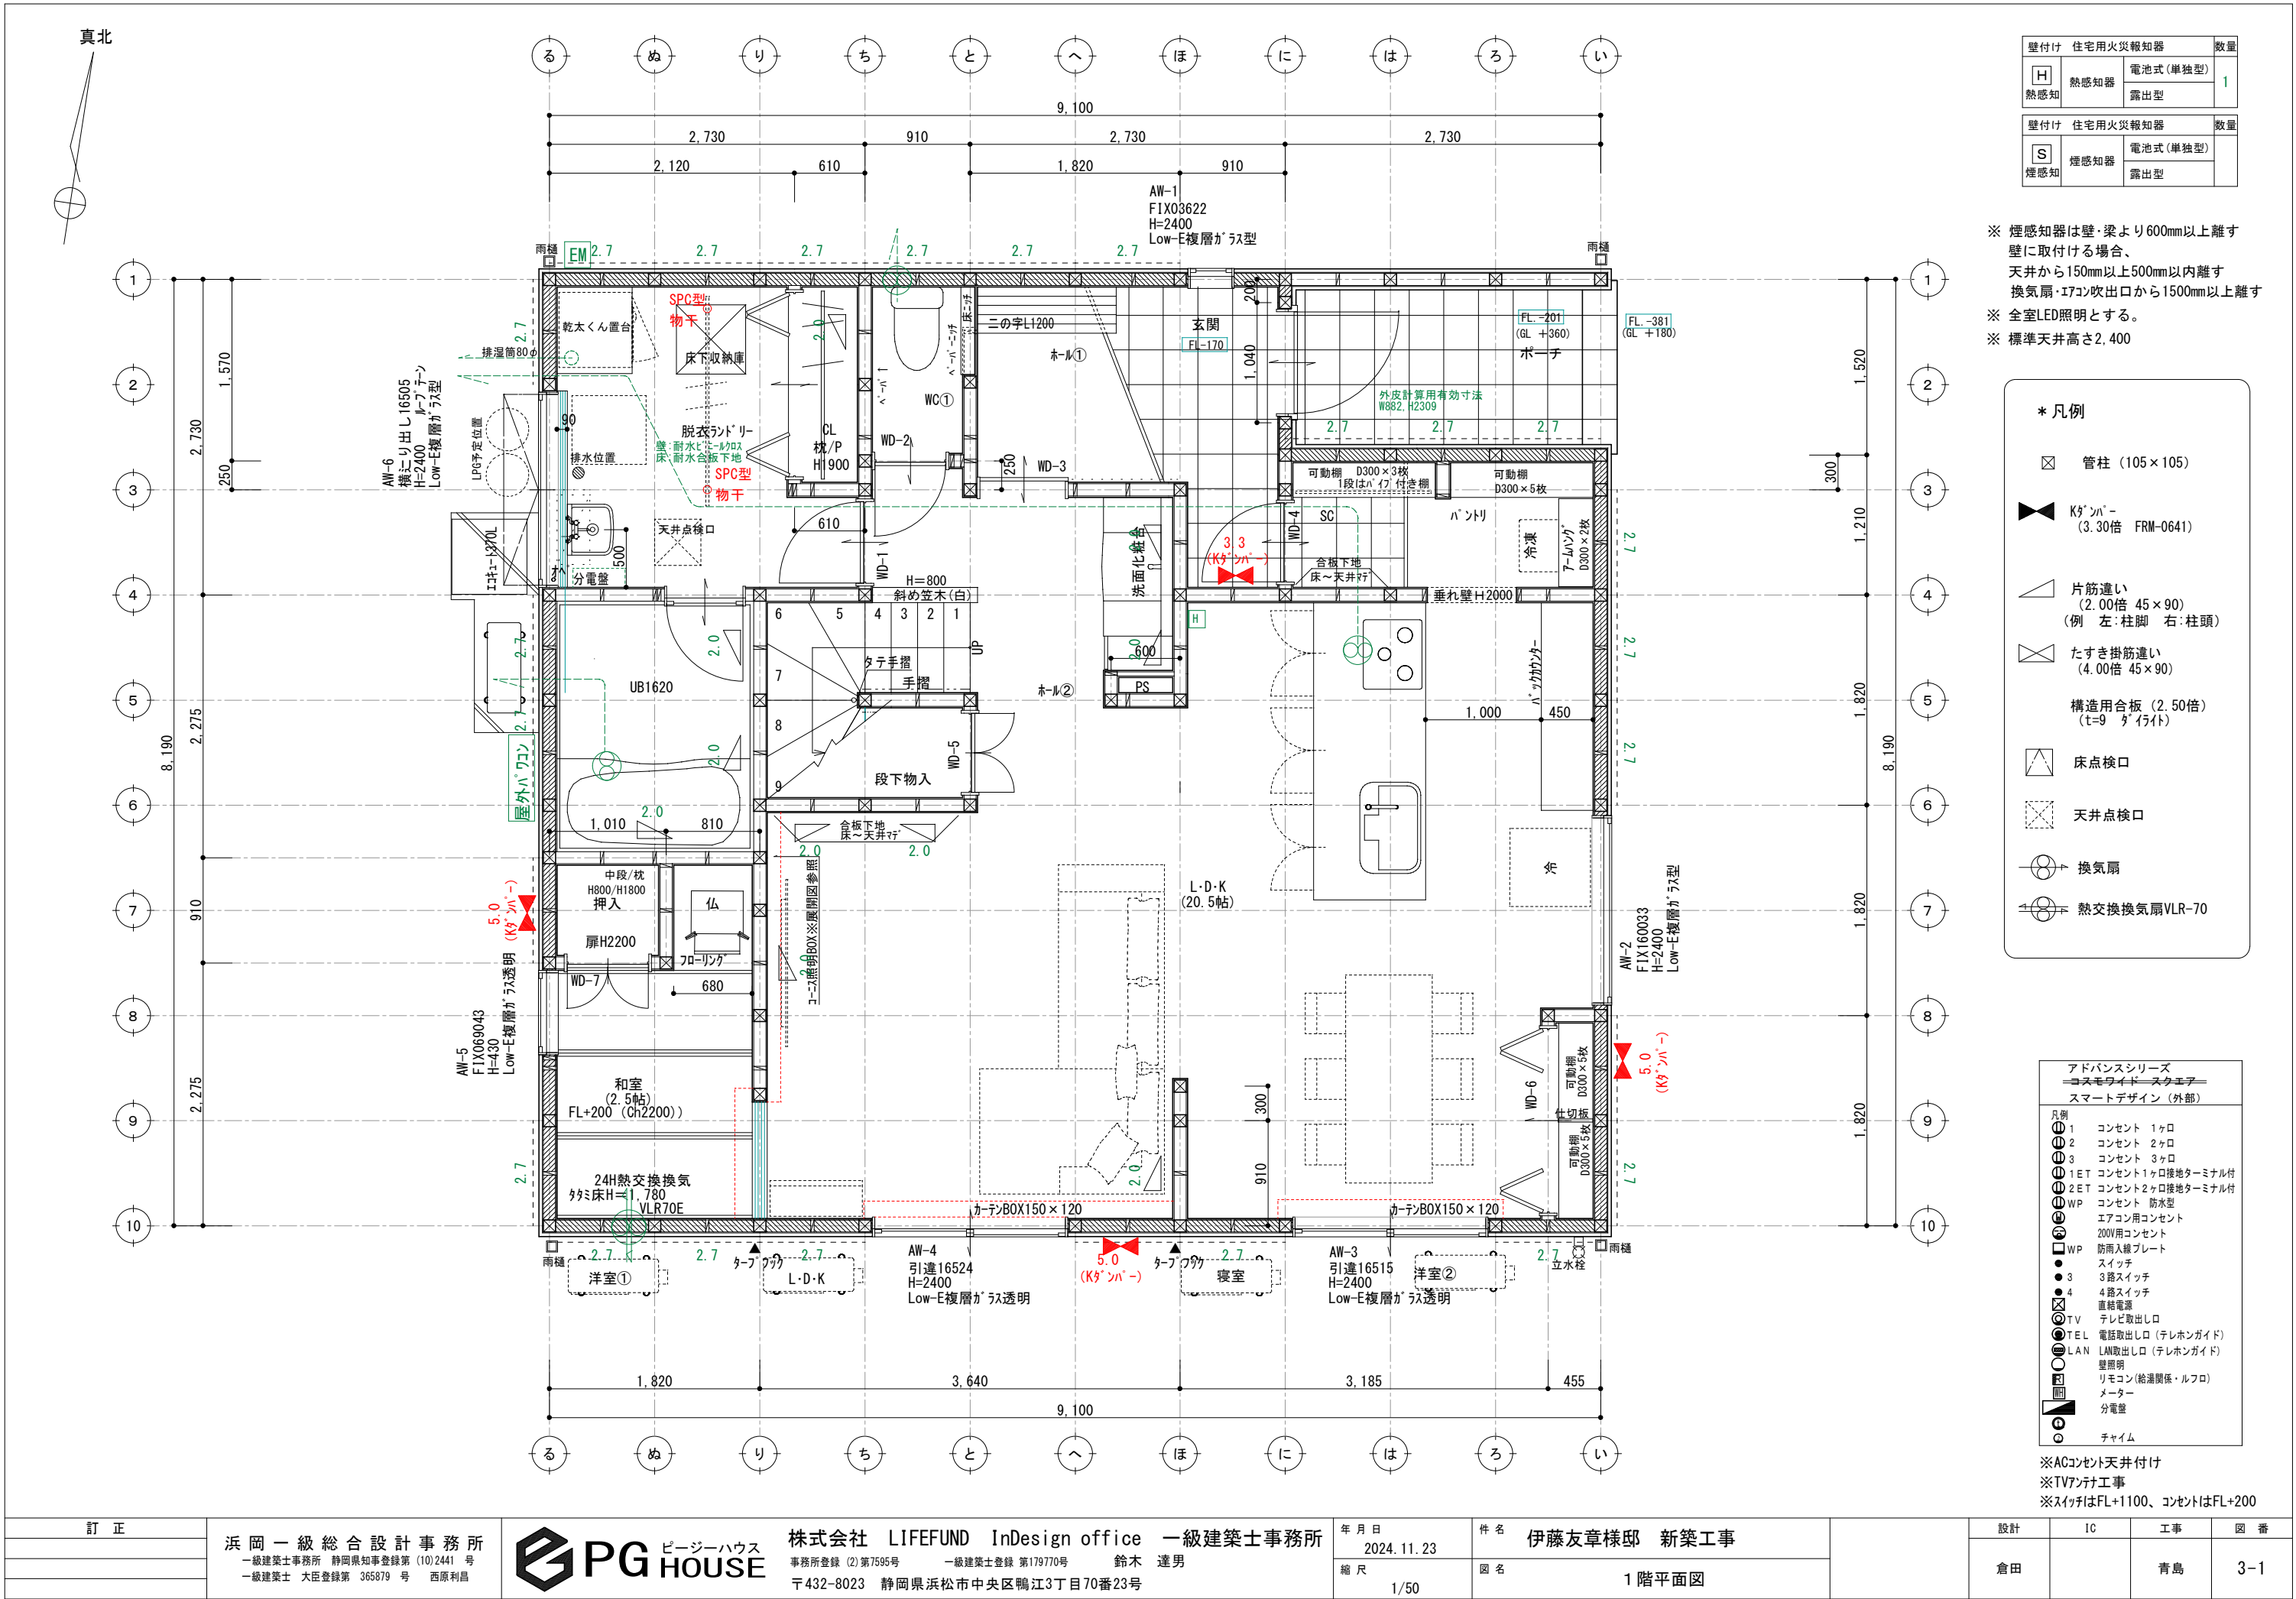


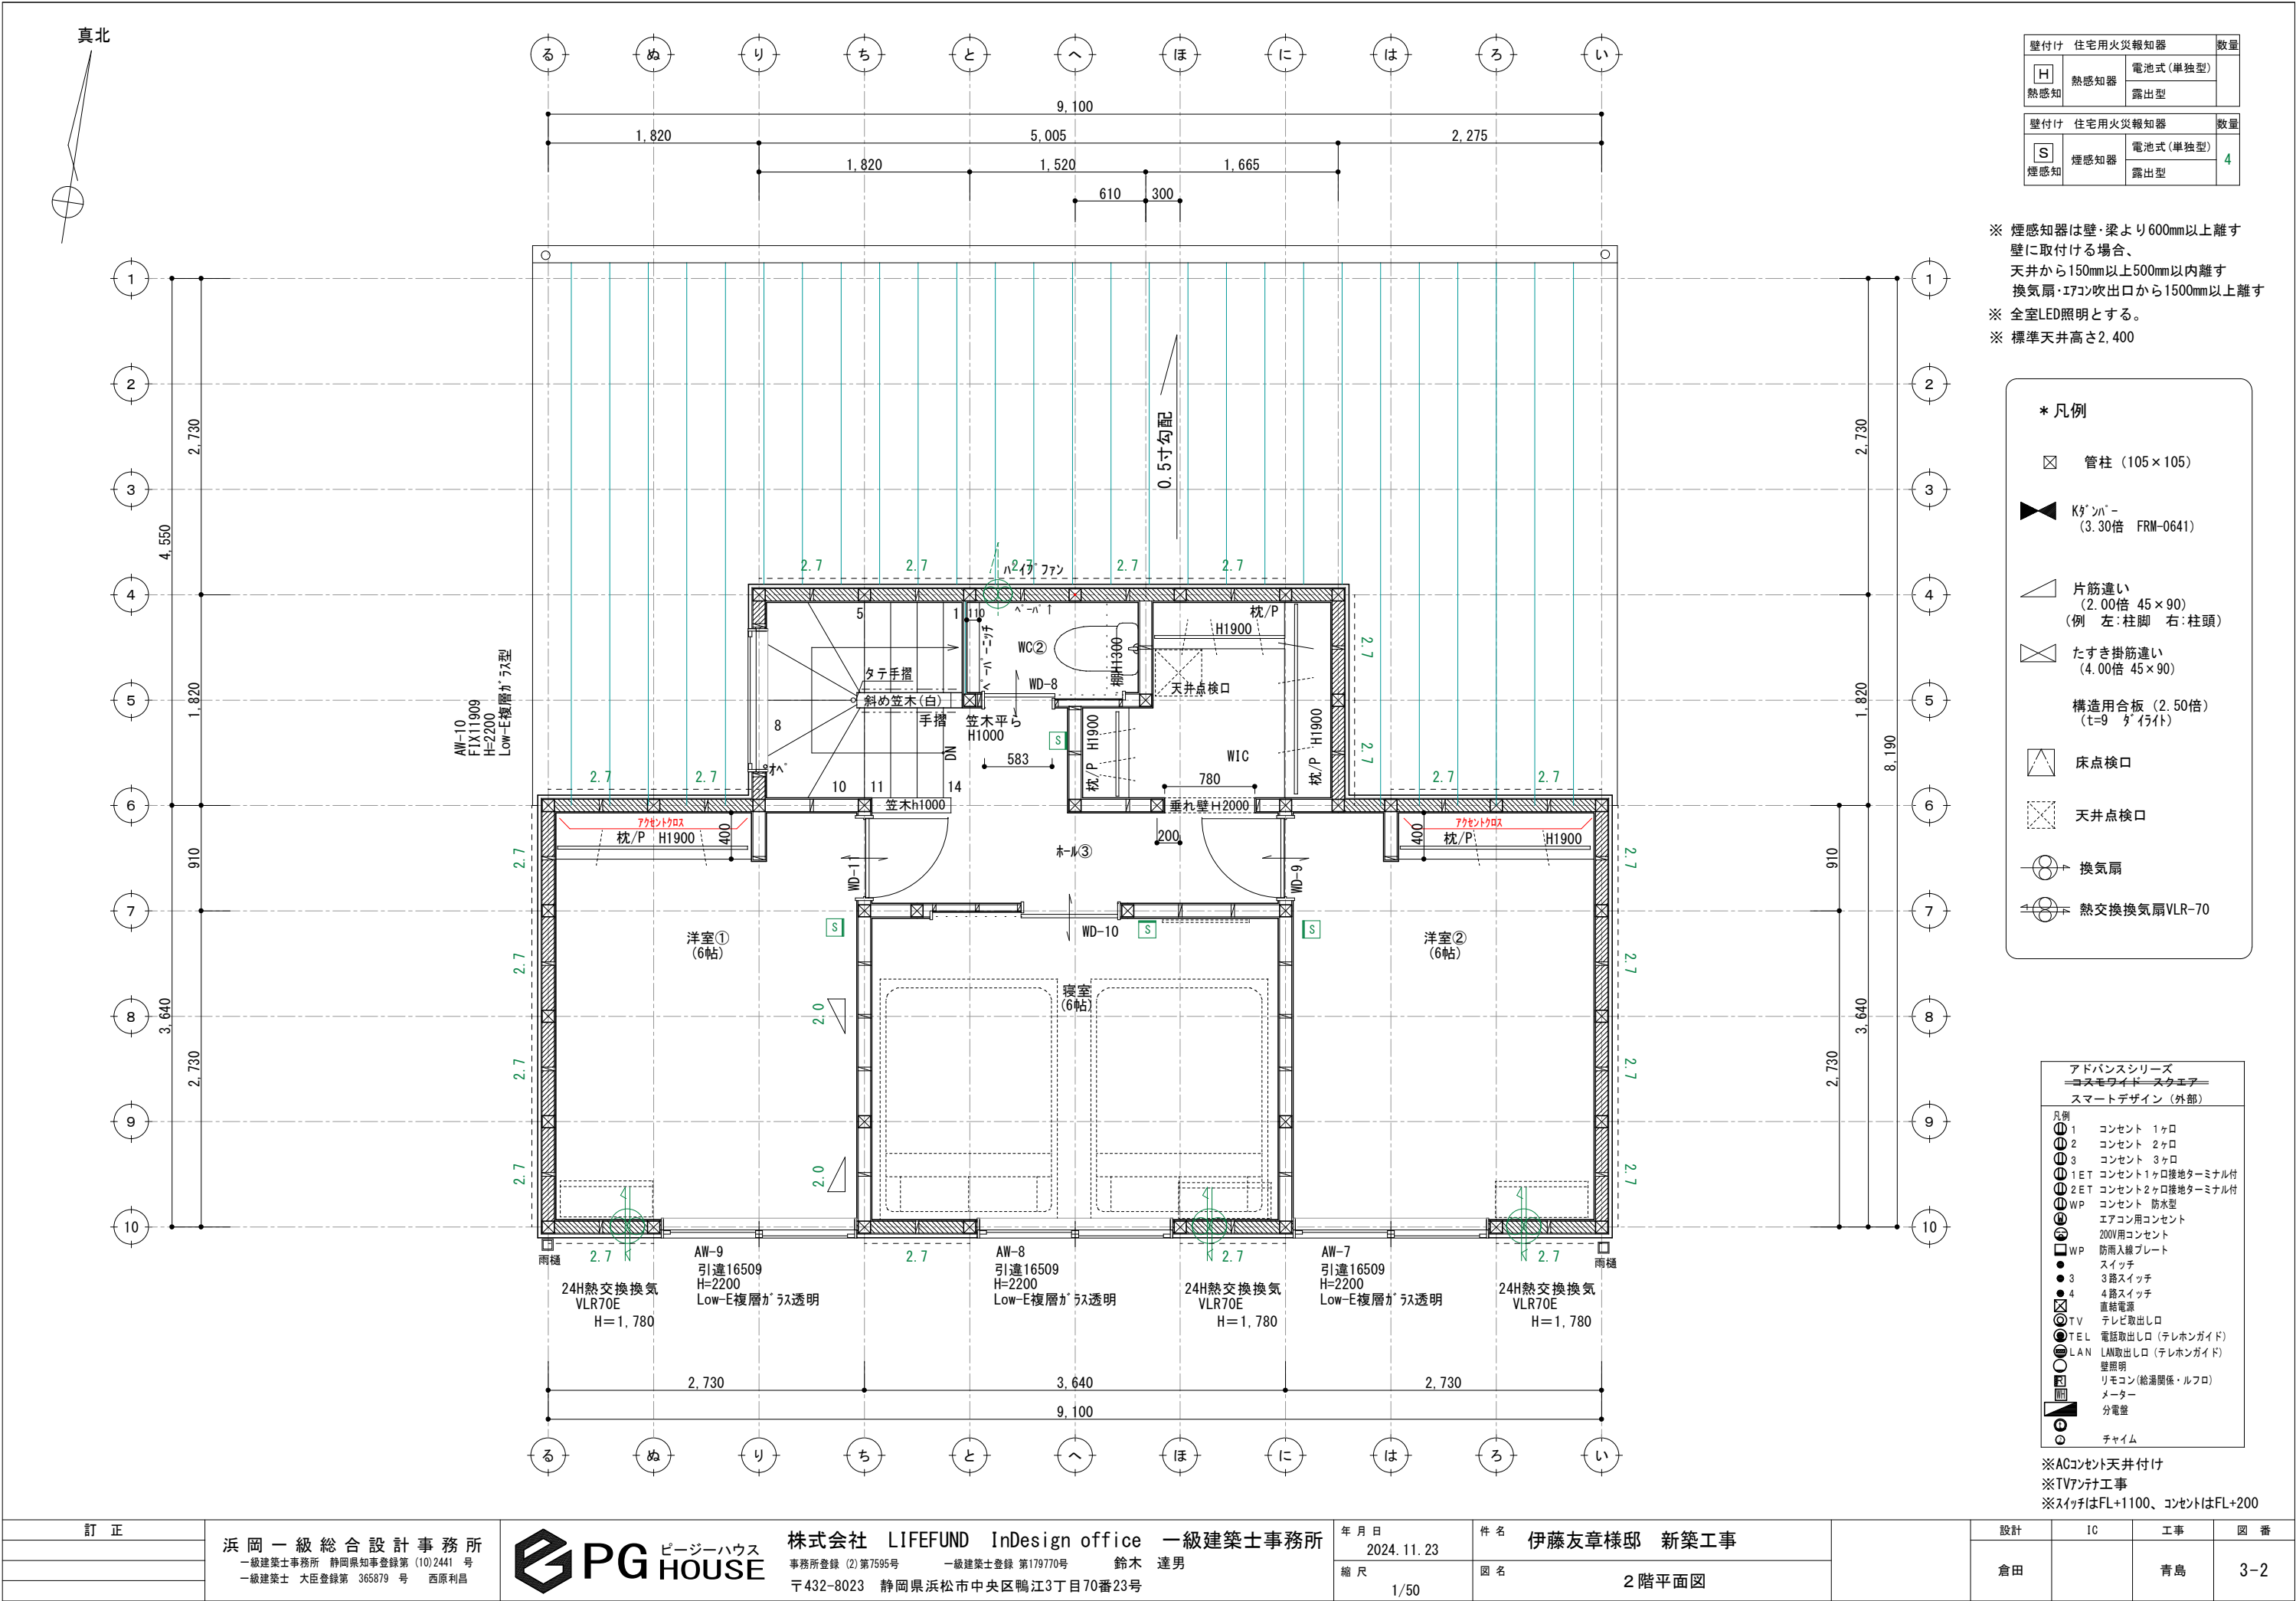


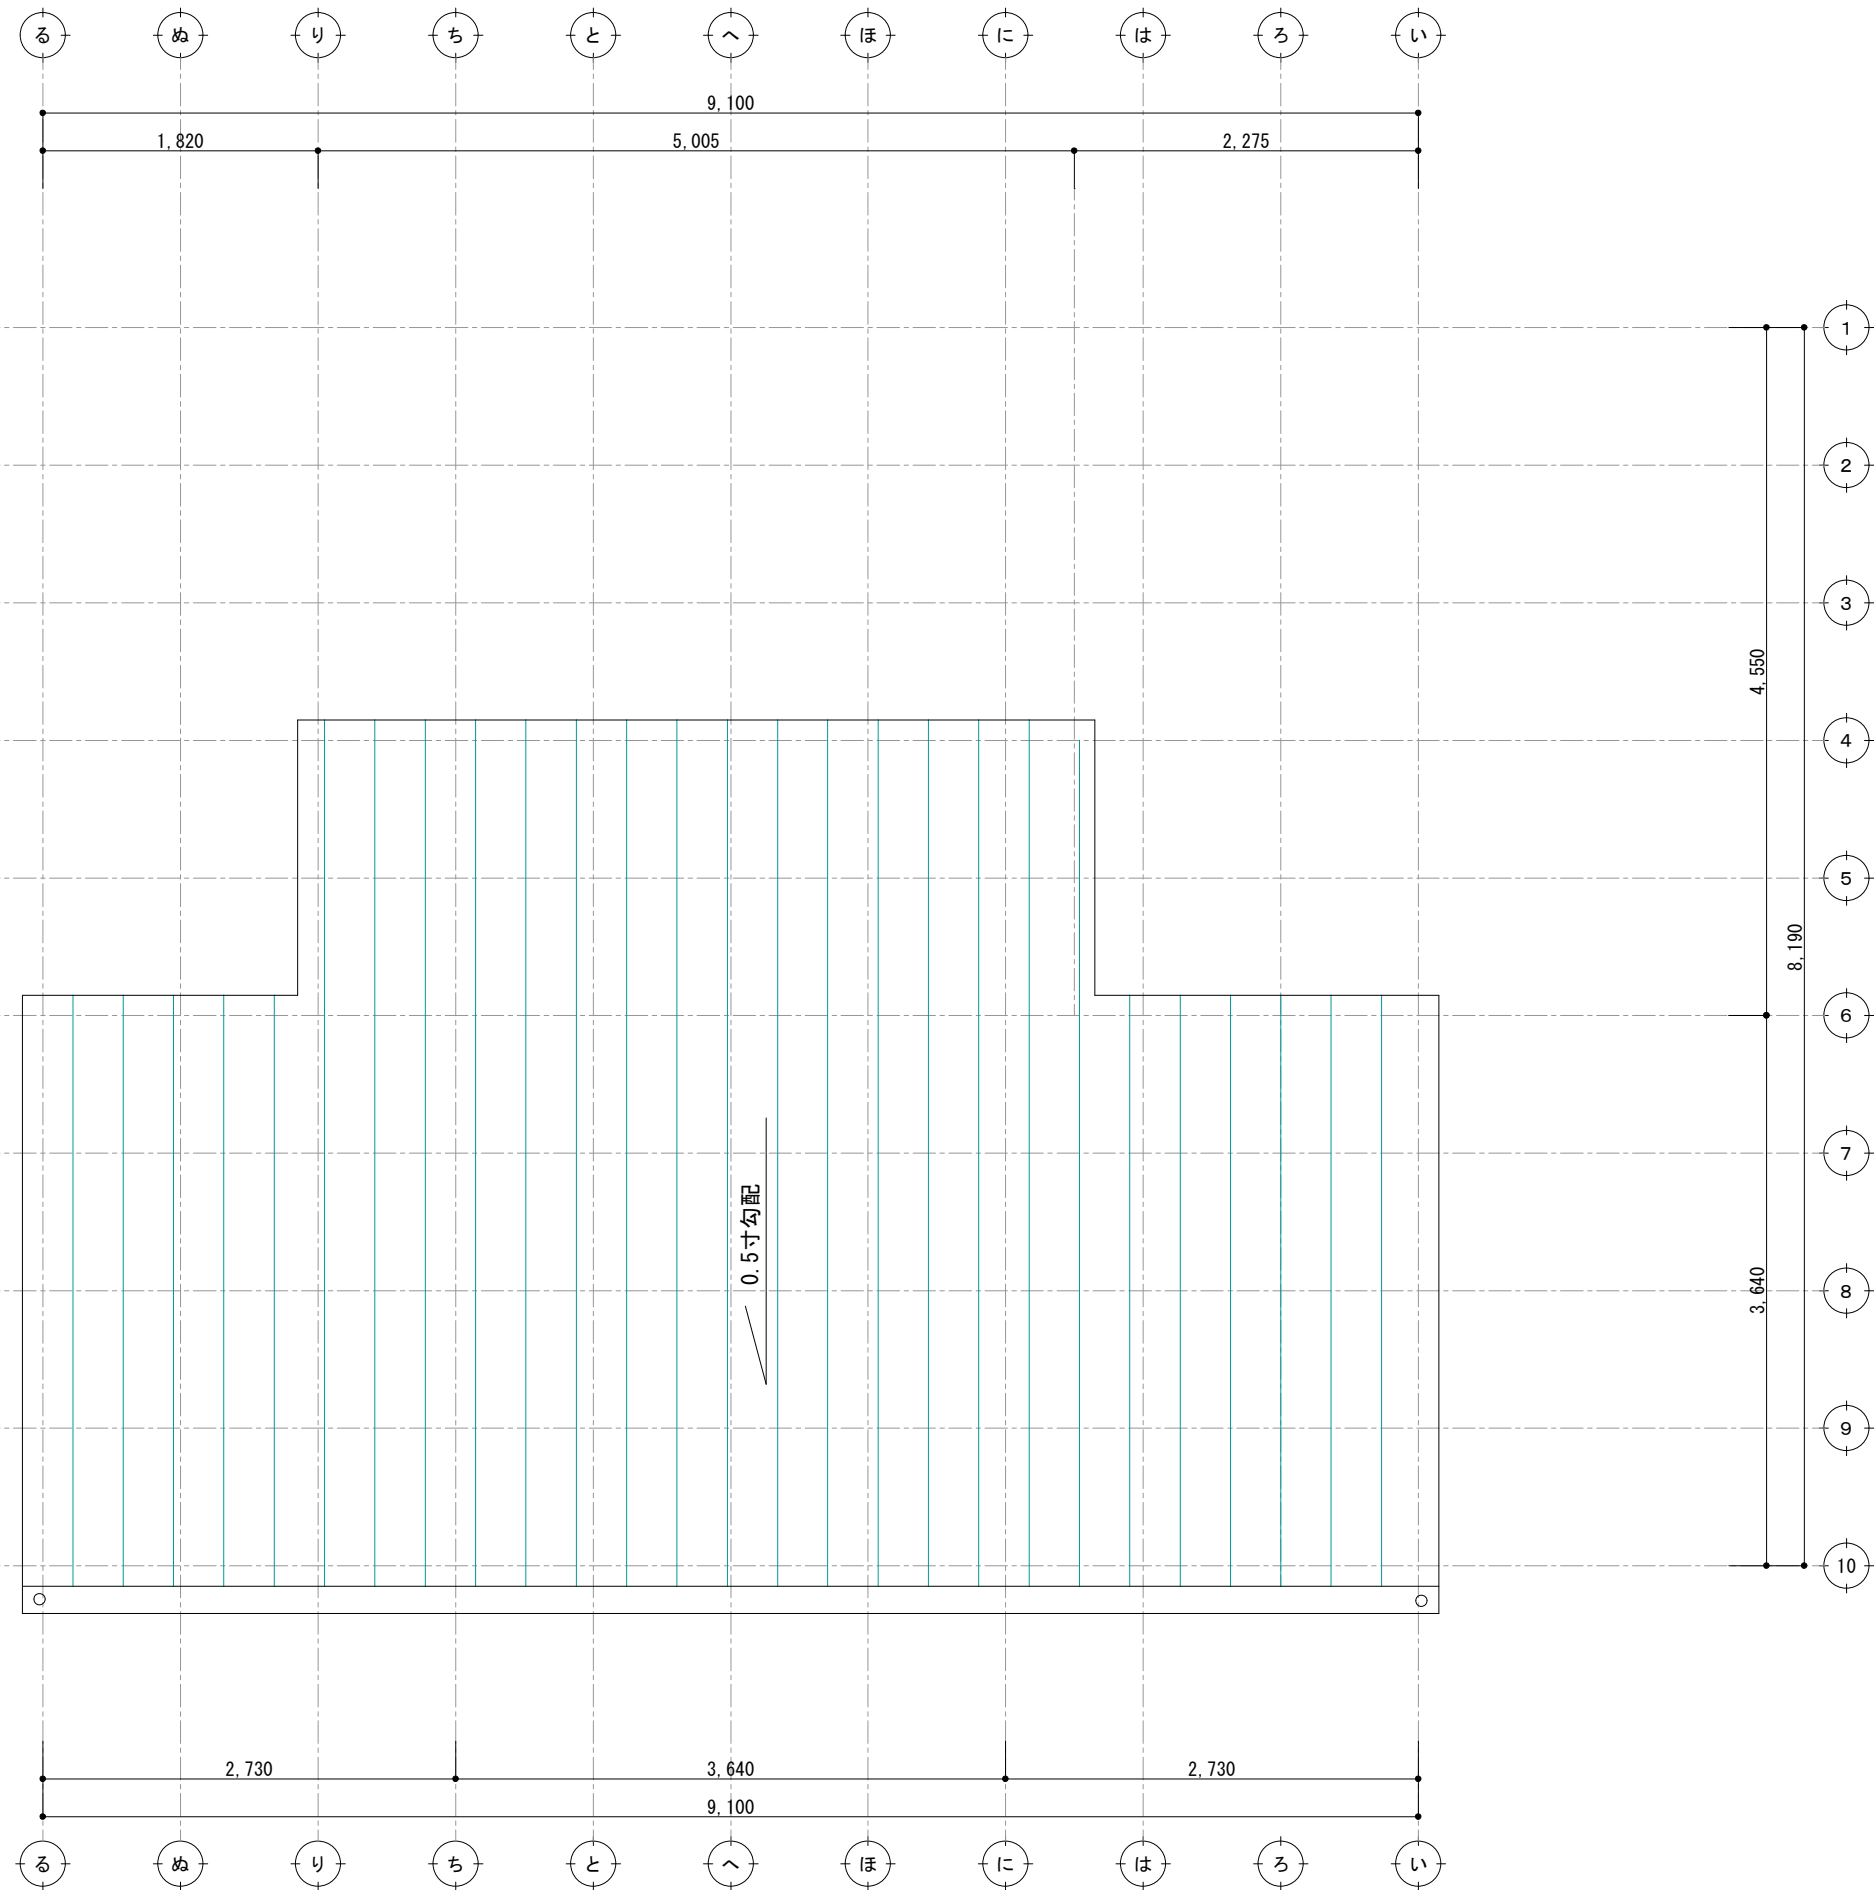


訂 正	浜 岡 一 級 総 合 設 計 事 務 所 一級建築士事務所 静岡県知事登録第 (10)2441 号 一級建築士 大臣登録第 365879 号 西原利昌		株式会社 LIFEFUND InDesign office 一級建築士事務所 事務所登録 (2) 第7595号 一級建築士登録 第179770号 鈴木 達男 〒432-8023 静岡県浜松市中央区鴨江3丁目70番23号	年 月 日	件 名	設計	IC	工事	図 番
				2024. 11. 23	伊藤友章様邸 新築工事				
				縮 尺	図 名				
				1/100	屋根伏図	倉田		青島	3-3




株式会社 LIFEFUND InDesign office 一級建築士事務所
事務所登録 (2) 第7595号 一級建築士登録 第179770号 鈴木 達男
〒432-8023 静岡県浜松市中央区鴨江3丁目70番23号

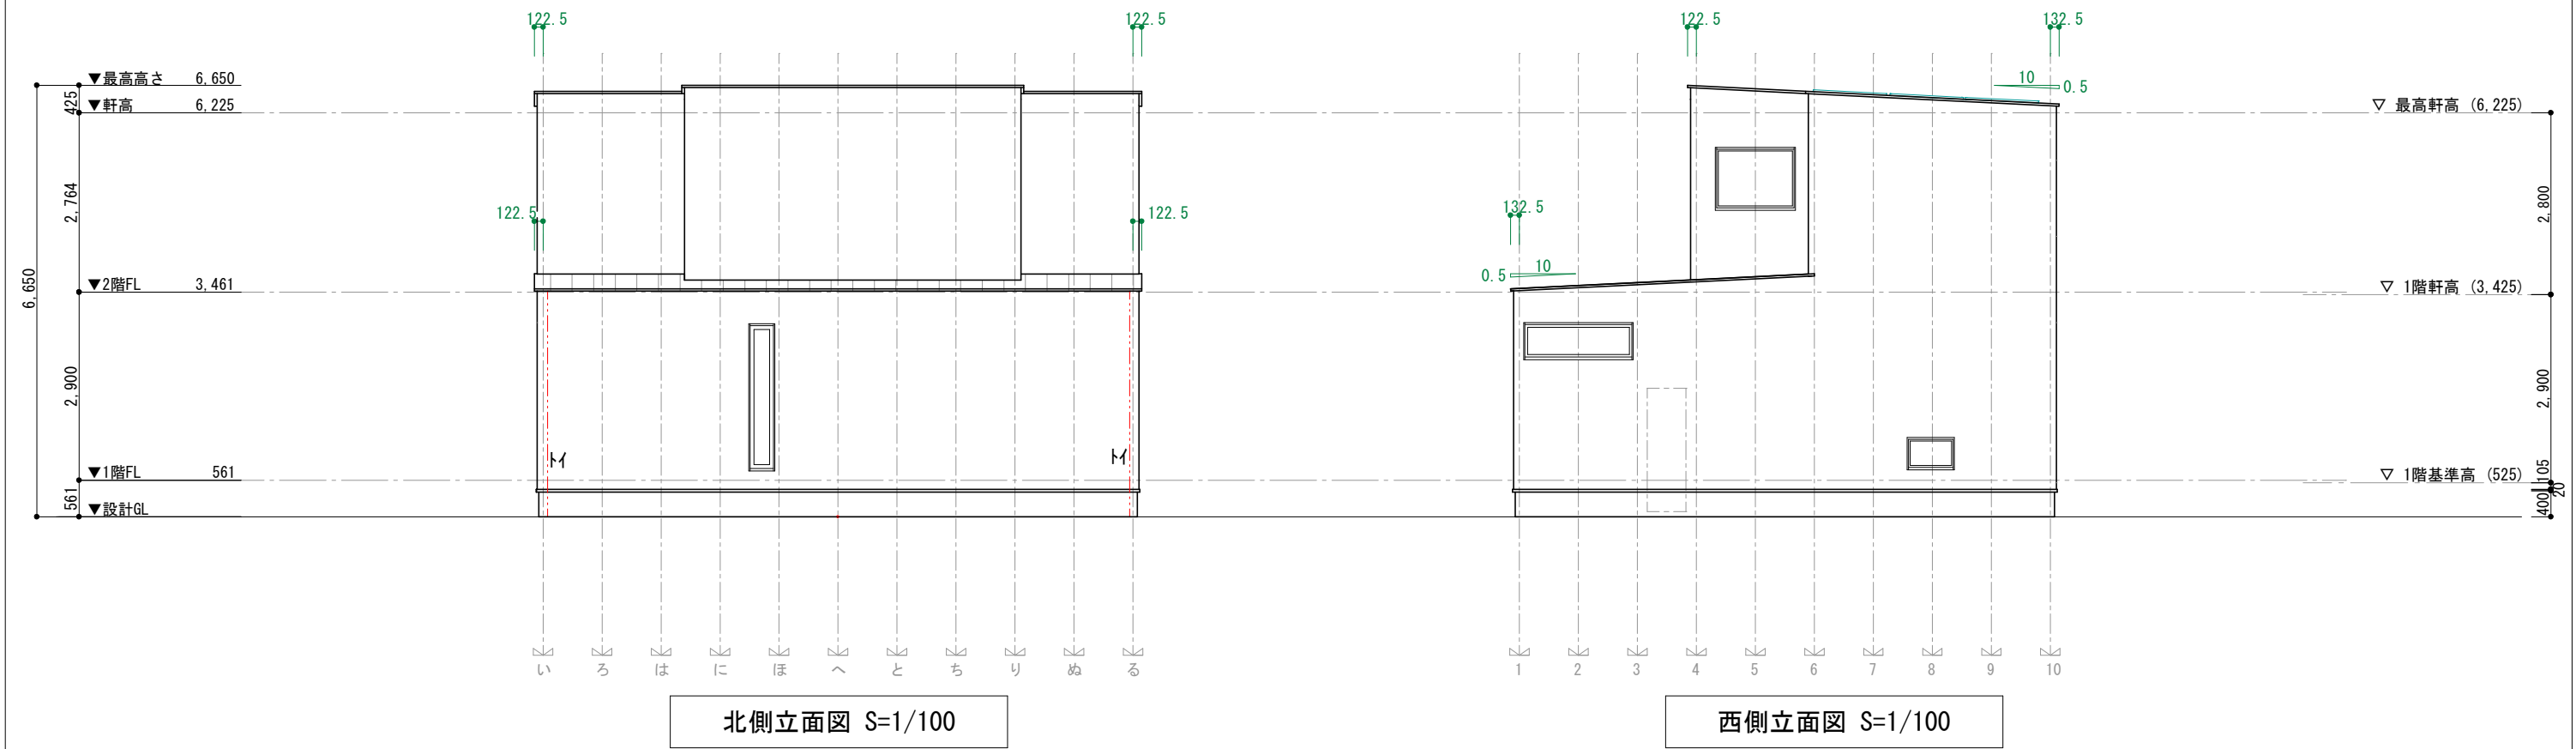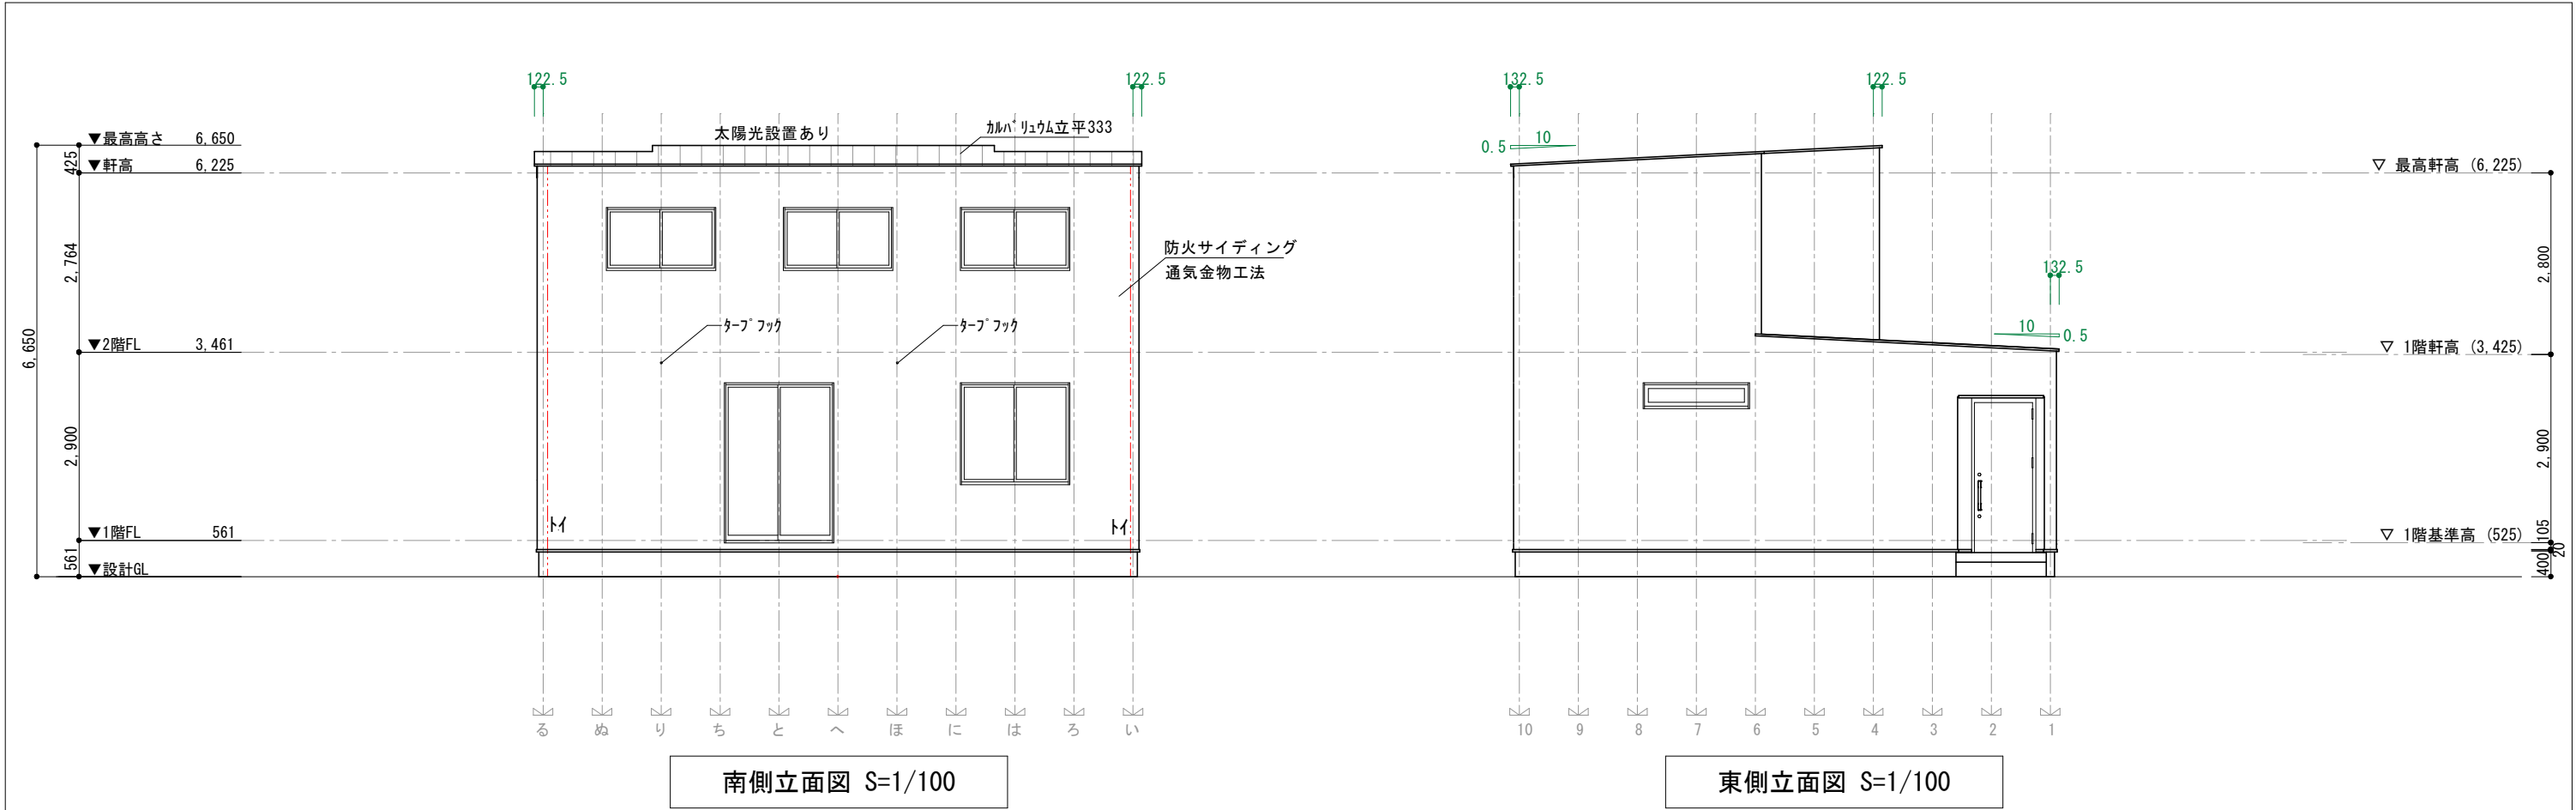


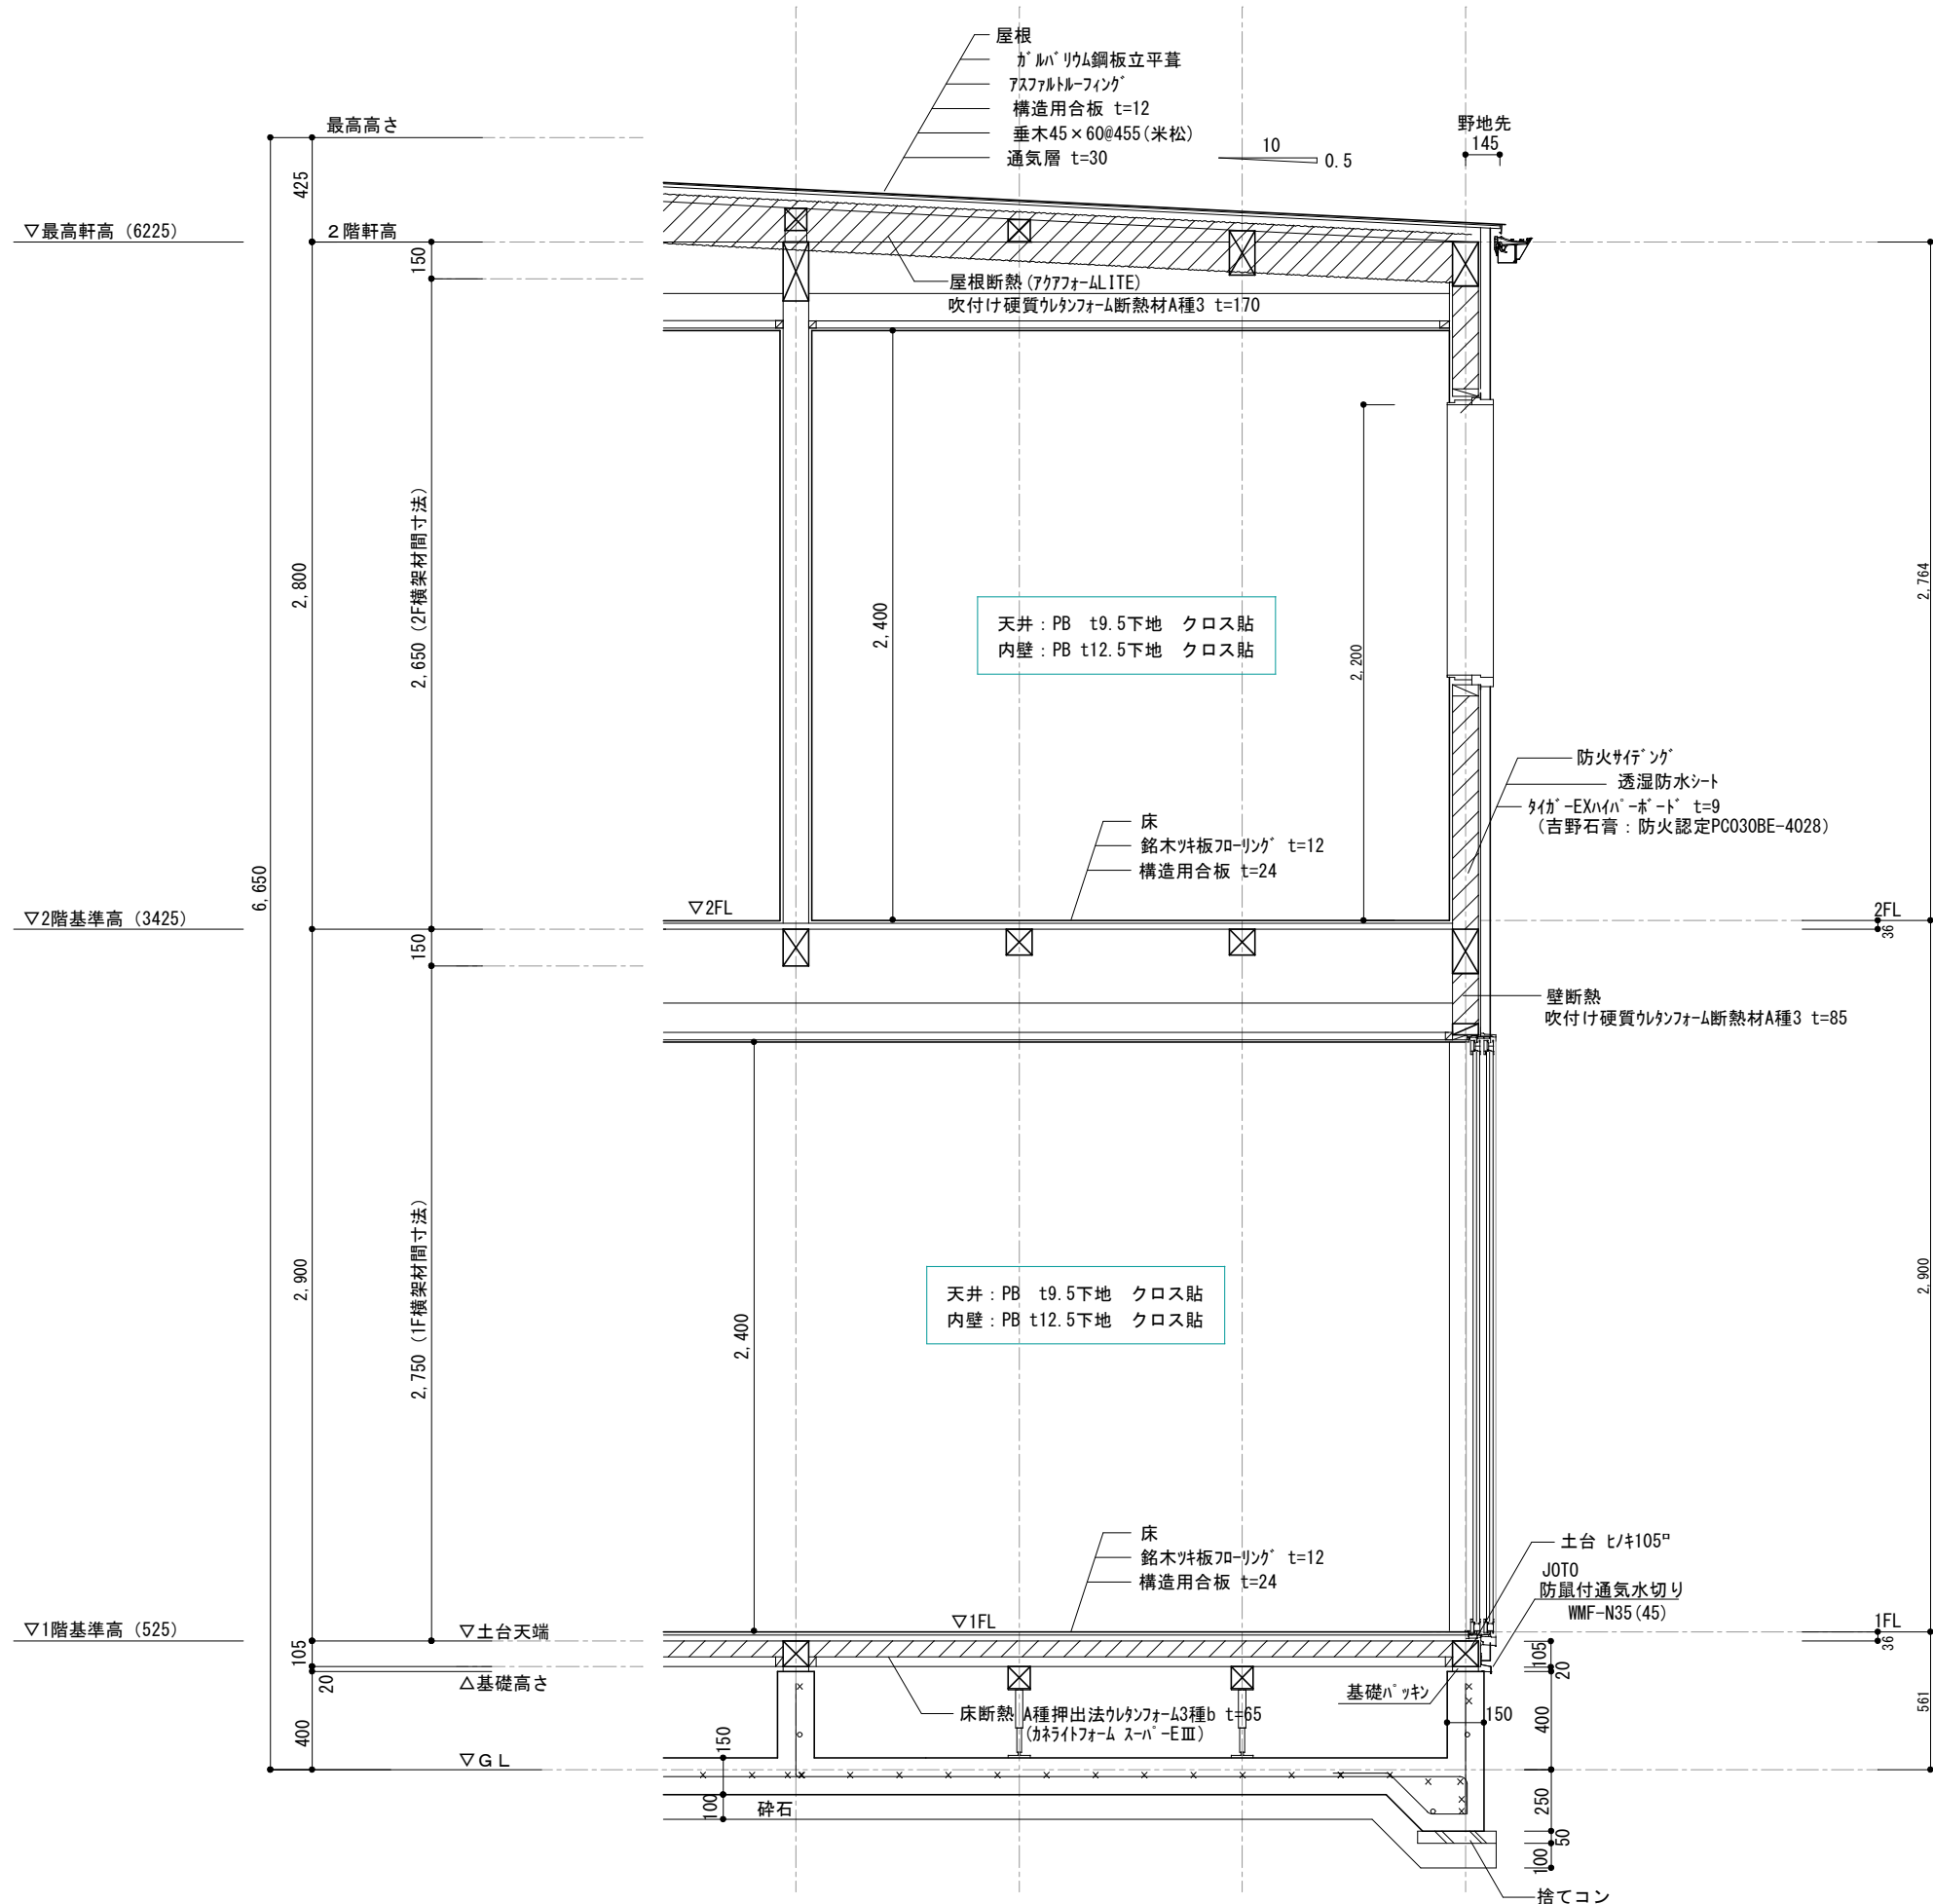


訂正	浜岡一級総合設計事務所 一級建築士事務所 静岡県知事登録第(10)2441号 一級建築士 大臣登録第 365879号 西原利昌		株式会社 LIFEFUND InDesign office 一級建築士事務所 事務所登録(2)第7595号 一級建築士登録 第179770号 鈴木 達男 〒432-8023 静岡県浜松市中央区鶴江3丁目70番23号	年月日	件名		設計	IC	工事	図番
				2024.11.23	伊藤友章様邸 新築工事		倉田		青島	A-5
				縮尺	図名					
				1/100	矩計図					

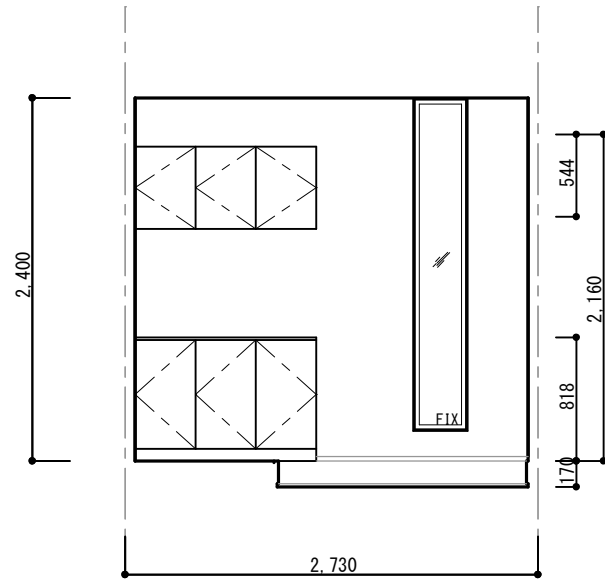


玄関 北面

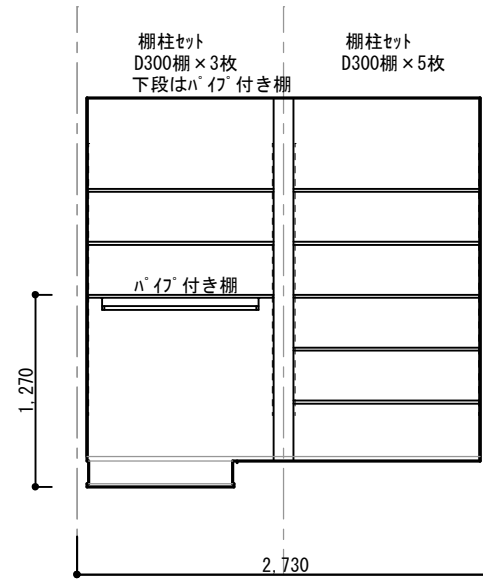


パントリー 北面

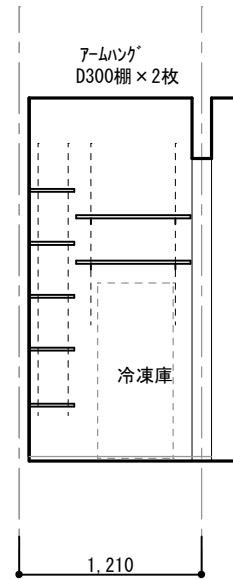


パントリー 東面

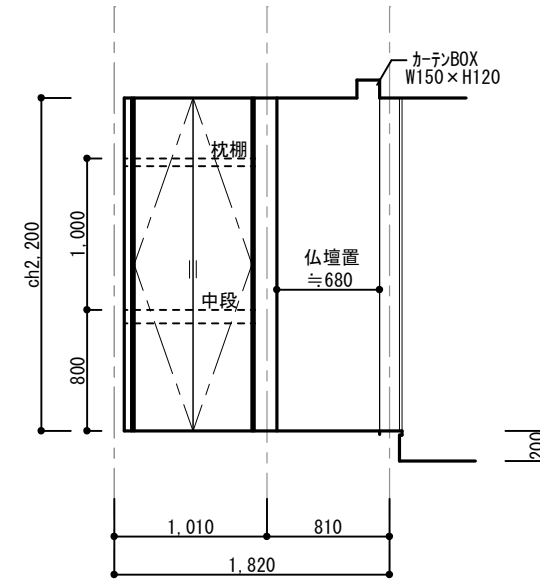


パントリー 東面

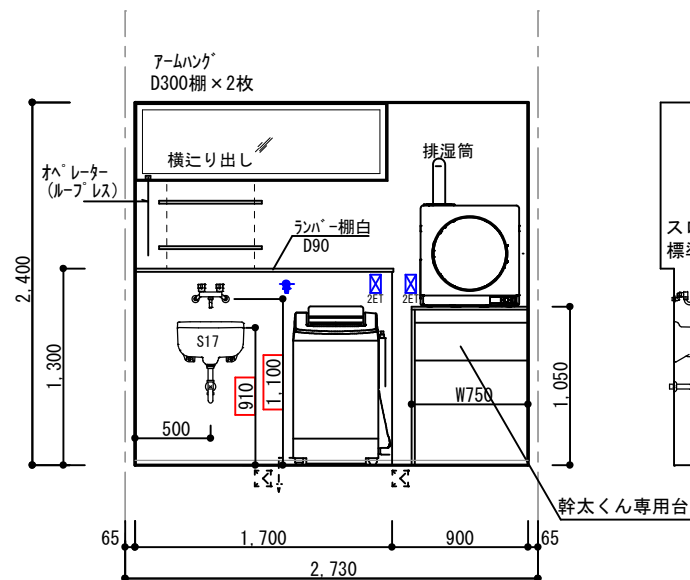


脱衣ランドリー 西面

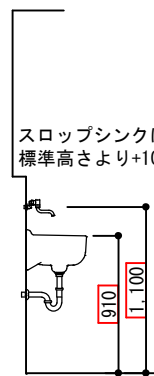


スロップシンクは標準高さより+100mm

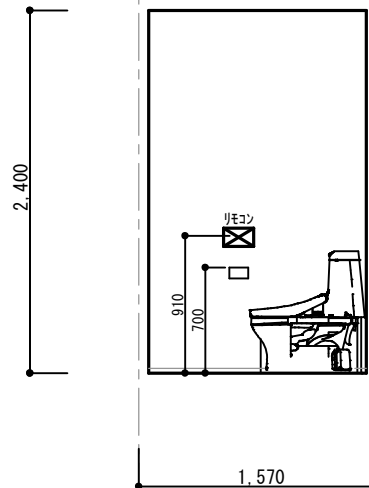


WC① 西側

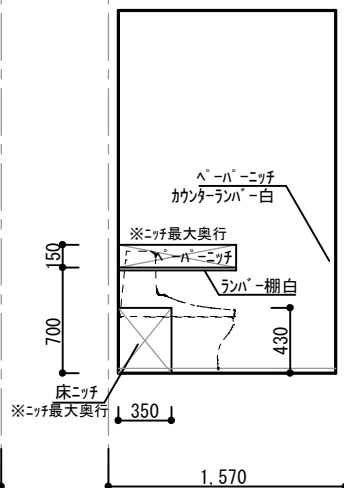


WC① 東側

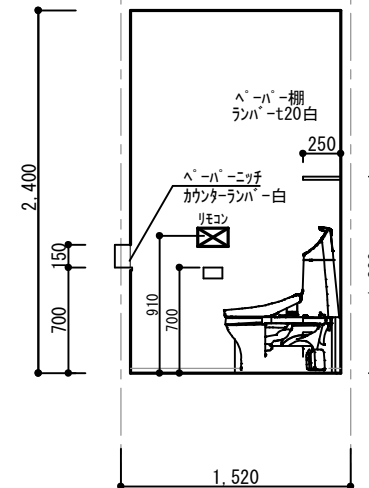


WC② 北面

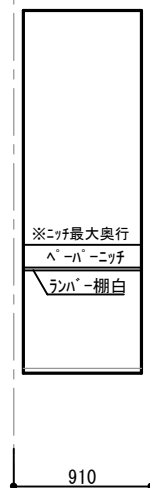


WC② 西面

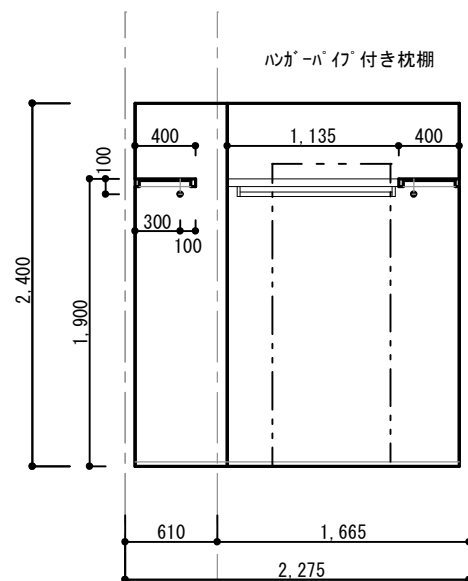

WIC 北面

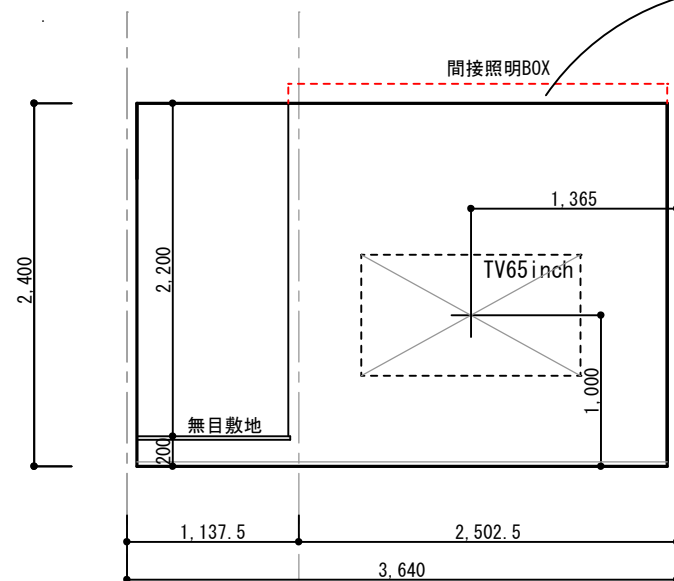


LDK 西面

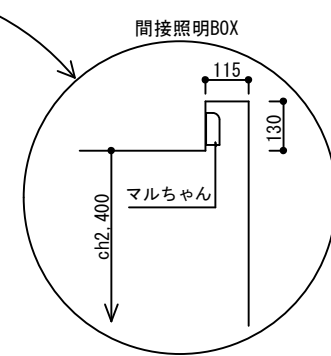


間接照明BOX


マルちゃん

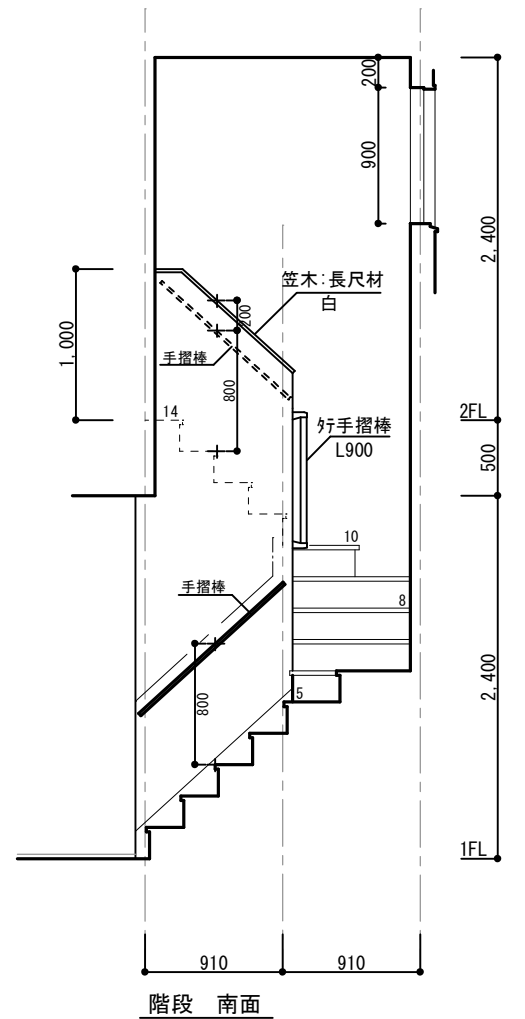


階段 南面


訂正	浜岡一級総合設計事務所 一級建築士事務所 静岡県知事登録第 (10)2441 号 一級建築士 大臣登録第 365879 号 西原利昌	LIFEFUND PG HOUSE	株式会社 LIFEFUND InDesign office 一級建築士事務所 事務所登録 (2)第7595号 一級建築士登録 第179770号 鈴木 達男 〒432-8023 静岡県浜松市中央区鴨江3丁目70番23号	年月日 2024.11.23 縮尺 1/50	件名 伊藤友章様邸 新築工事 図名 展開図		設計 倉田	IC	工事 青島	図番 6-1
----	--	----------------------	--	---------------------------------	--------------------------------	--	----------	----	----------	-----------

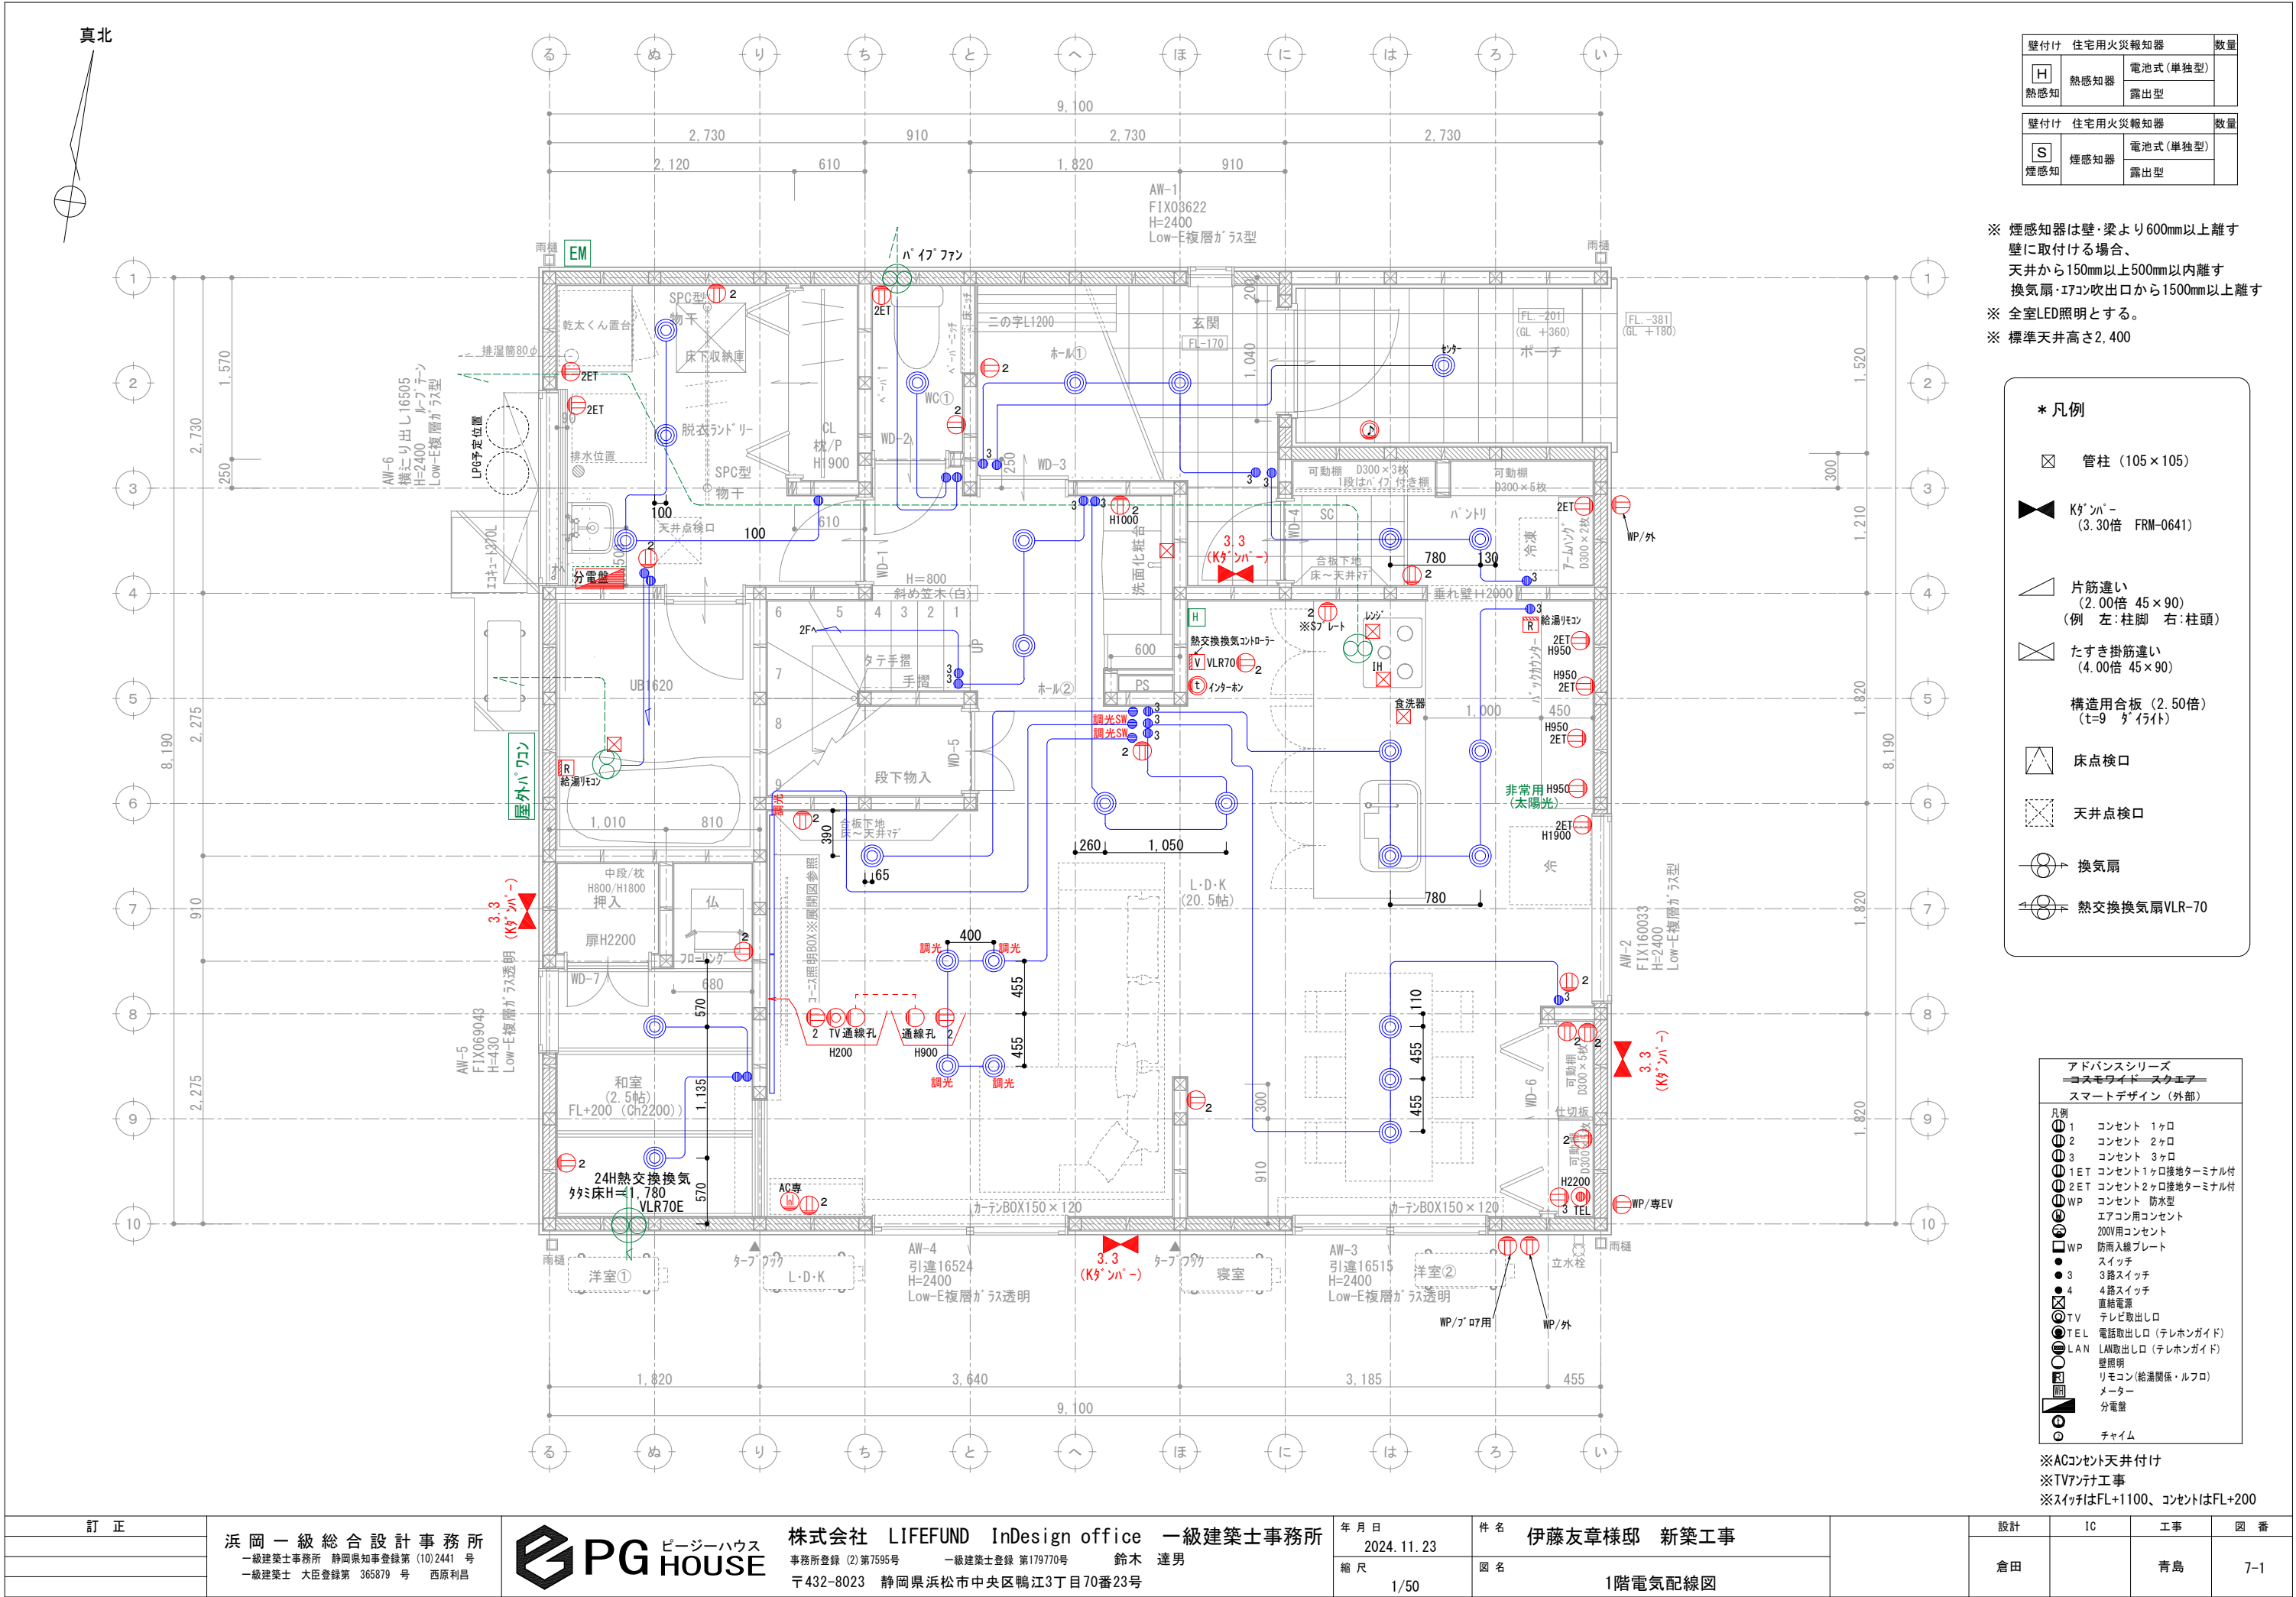

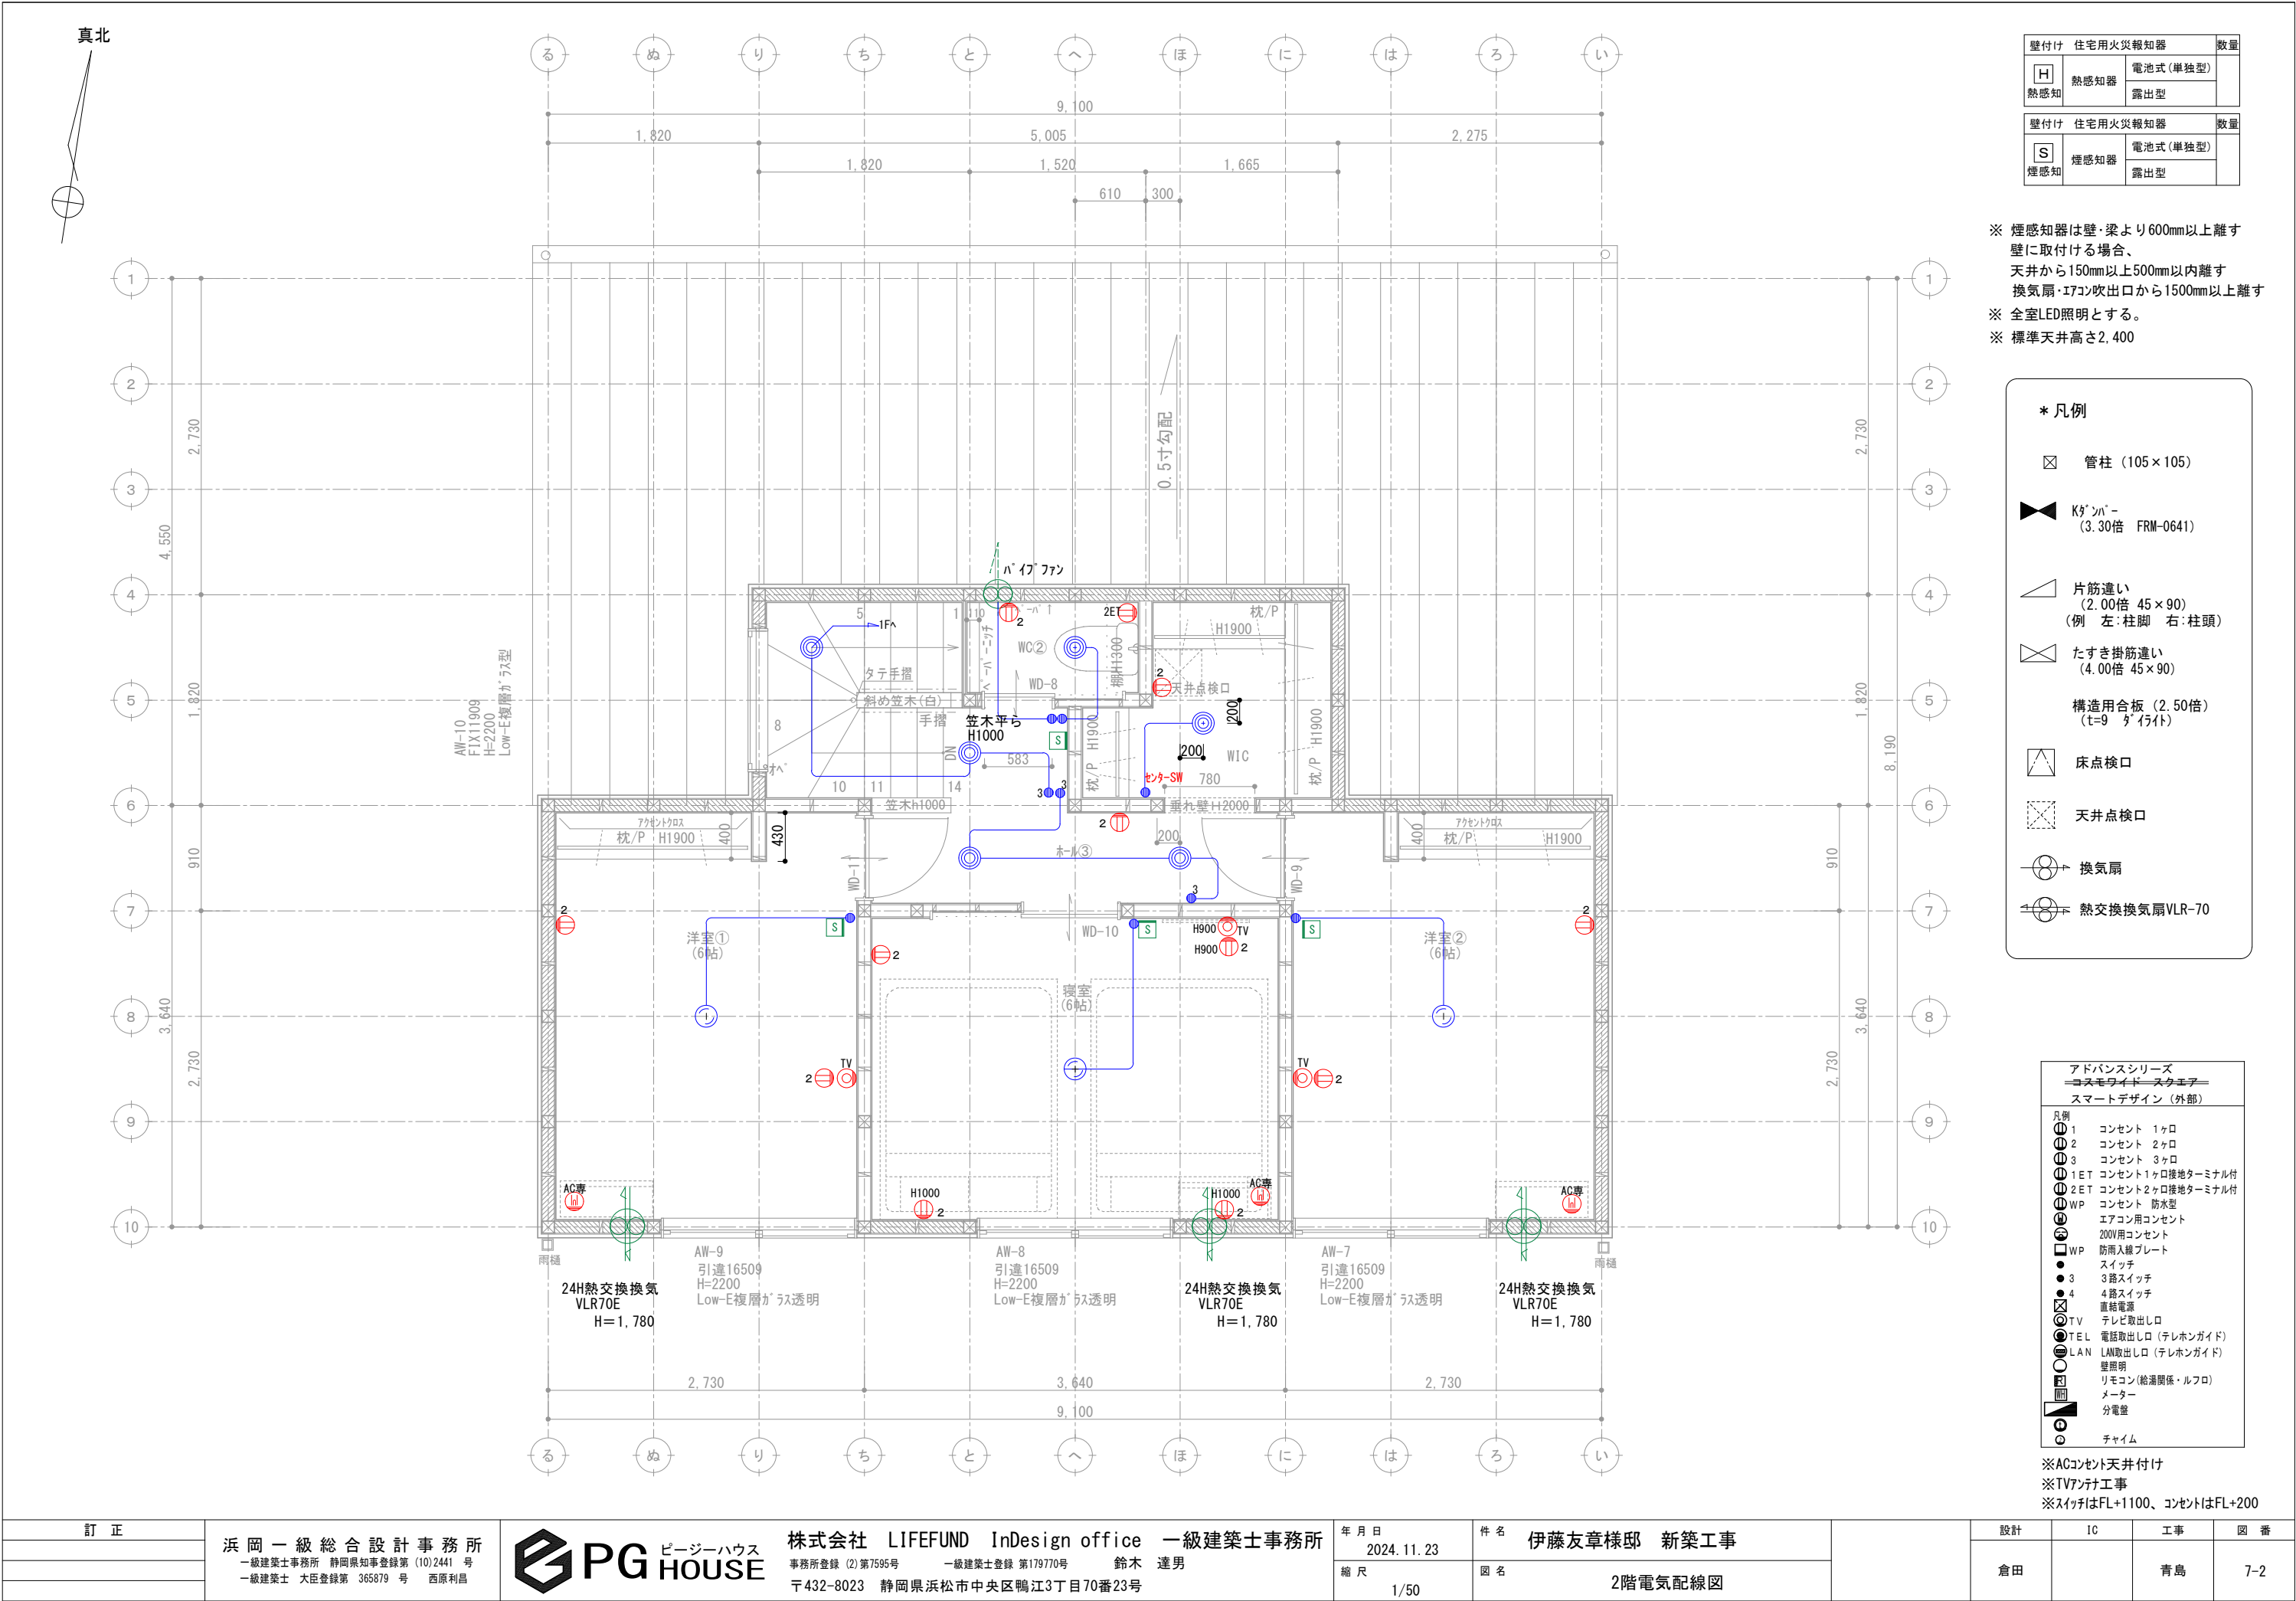

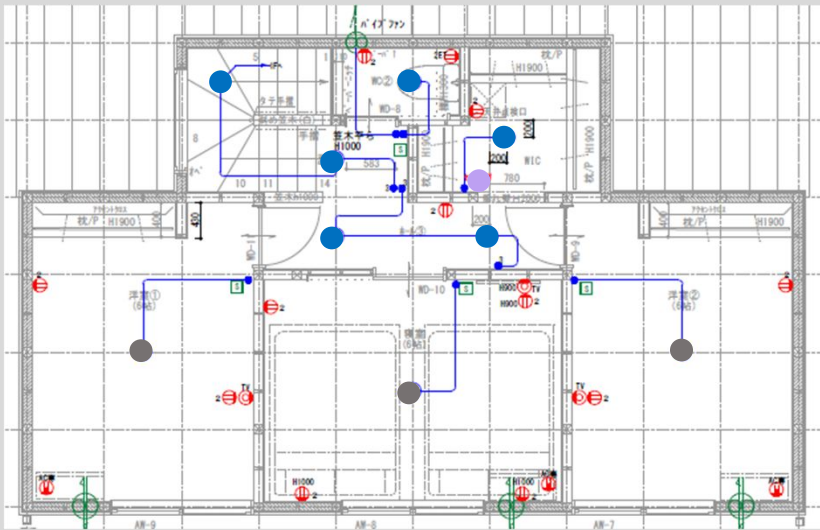

2階

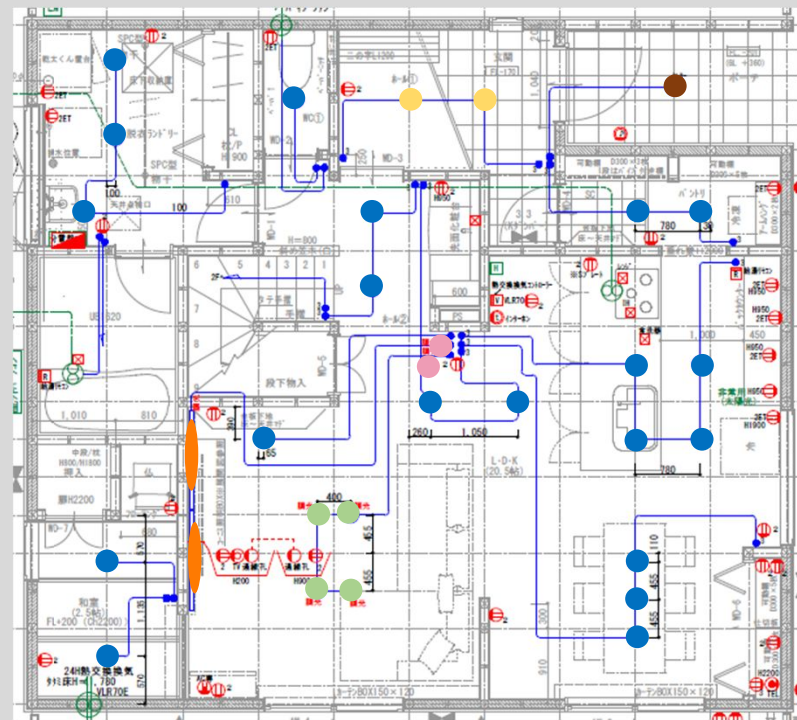

1階

ドアホン：VL-SZ30KL
(Panasonic)



外部：スマートサインシリーズ



間接照明
● × 2
DSY-4393 AWG



L=1200mm

DSY-4393 AWG
温白色 / 3500K・Ra83

定格光束 3410lm	消費電力 29W	固有エネルギー消費効率 117.5lm/W
----------------	-------------	--------------------------

¥29,800-(税抜) (LED内蔵)

LED LED 29W 電源内蔵

- アルミ型材 白アルマイト
- アクリル 乳白(マット)
- 巾85 長1200 高35mm 1.5kg
- 29VA
- AC100V
- 連結最大15台まで
- 調光可能(1%~100%)
- シーンコントローラー別売
- 調光にはLED専用調光器(別売)をご使用ください。
- オプション取付金具別売(DP-40543)
- 光源寿命40,000時間

天井壁(横向)・床付兼用

調光

傾斜天井
可能
(横向)


LED交換
不可

人感センサSW
● × 1

WTA1811WK



コンセント：WTA1811WK
プレート：WTA8101W

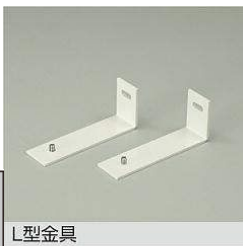

L型金具

DP-40543

¥2,200-(税抜) (2個)

- 銅板 白塗装
- 巾25 長110 高35mm 0.01kg
- 注)器具1台につき2個ずつご使用ください。

調光SW
● × 2

WTA57583WK



WTA57583WK

希望小売価格 11,900円(税抜)

※掲載の価格には消費税は含まれていません。

LED 埋込逆位相調光スイッチC(はたはスイッチC)

(適合LED専用3.2A) (ロータリー式)

(下線調光設定機能付)(マットホワイト)

WTA7101WK

希望小売価格 320円(税抜)

※掲載の価格には消費税は含まれていません。

居室シーリング
● × 3

DCL40507



タイマー付リモコン・ブルレス | 調色調光タイプ

DCL-40507

星白色 / 6500K・Ra83 ~ 電球色 / 2700K・Ra83

LED LED 29.5W 定格光束 3699lm 消費電力 29.5W 固有エネルギー消費効率 125.3lm/W

¥22,000-(税抜) (LED内蔵)

●アクリル 乳白(マット)

●径φ510 高128mm 1.6kg

●ブルレススイッチ付(全灯・※点灯・常夜灯)

※消灯前の調色調光状態

●調色機能付(6500K~2700K)

●調光機能付(5%~100%)

●常夜灯6段階調光

●AC100V

●光源寿命40,000時間

●消費効率星白色時

●調光器併用不可

●シーンコントローラーは使用できません。

クイック取付式

カバー回転式

傾斜天井 55°

別売取付パーツ DP-40091

手続天井 可能

別売取付パーツ DP-40638

ポーチ灯

● × 1

DDL-4496YB



高気密Se形 | 人感センサー | 連動マルチタイプ

DDL-4496 YB

電球色 / 2700K・Ra83

定格光束 消費電力 固有エネルギー消費効率

425lm 7.7W 55.1lm/W

¥18,800-(税抜) (LED内蔵)

LED LED 7.7W

白熱灯60W相当

- アルミダイキャスト 黒塗装
- アクリル 乳白(マット)
- 径φ111 埋込穴φ100
- 埋込深80mm 0.5kg
- 14VA
- 点灯照度調節機能付(暗・明切)
- 点灯保持時間(1分)
- 拡散パネル付
- AC100V
- 光源寿命50,000時間
- 取付可能天井厚5~25mm
- 調光器併用不可
- 【連動器具について】
- LED調光タイプ60VAまで
- LED非調光タイプ不可 蛍光灯不可
- 白熱灯60Wまで

強制 ON

非調光

ソフト

スタート

フェード

アウト

埋込穴

100

埋込

必要高

80

LED交換

不可

防雨形


温度保護

機能付

基本照明ダ ウナイト

● × 26 (20+6)

DDL6102AW

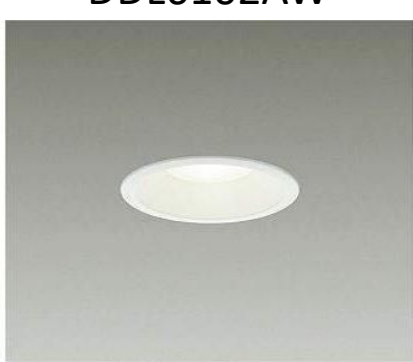

COBタイプ | 高気密Se形

DDL-6102 AW

温白色 / 3500K・Ra83

定格光束 消費電力 固有エネルギー消費効率

470lm 4.6W 102.1lm/W

¥3,600-(税抜) (LED内蔵)

LED LED 4.6W

白熱灯60W相当

- 銅板 白塗装
- アクリル 乳白(マット)
- 径φ116 埋込穴φ100 埋込深70mm 0.3kg
- 8VA
- 拡散パネル付
- AC100V
- 光源寿命60,000時間
- 取付可能天井厚5~25mm
- 調光器併用不可

LED交換

不可

非調光

防雨形

60°

温度保護

機能付

埋込穴

100

埋込

必要高

70


傾斜天井

55°

準耐火

● × 2

DDL6102YW

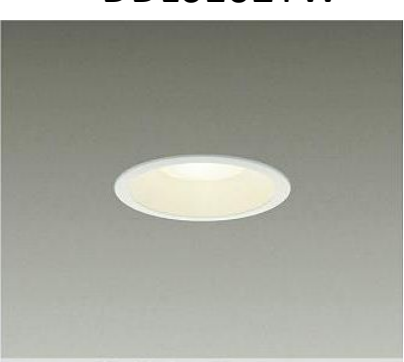

COBタイプ | 高気密Se形

DDL-6102 YW

電球色 / 2700K・Ra83

定格光束 消費電力 固有エネルギー消費効率

440lm 4.6W 95.6lm/W

¥3,600-(税抜) (LED内蔵)

LED LED 4.6W

白熱灯60W相当

- 銅板 白塗装
- アクリル 乳白(マット)
- 径φ116 埋込穴φ100 埋込深70mm 0.3kg
- 8VA
- 拡散パネル付
- AC100V
- 光源寿命60,000時間
- 取付可能天井厚5~25mm
- 調光器併用不可

LED交換

不可

非調光

防雨形

60°

温度保護

機能付

埋込穴

100

埋込

必要高

70

傾斜天井

55°

準耐火

● × 4

DDL6002AWG



COBタイプ | 高気密Se形

DDL-6002 AWG

温白色 / 3500K・Ra83

定格光束 消費電力 固有エネルギー消費効率

470lm 5.8W 81.0lm/W

¥4,600-(税抜) (LED内蔵)

LED LED 5.8W

白熱灯60W相当

- 銅板 白塗装
- アクリル 乳白(マット)
- 径φ116 埋込穴φ100 埋込深71mm 0.3kg
- 7VA
- 拡散パネル付
- AC100V
- 調光可能(1%~100%)
- 調光にはLED専用調光器(別売)をご使用ください。
- 光源寿命60,000時間
- 取付可能天井厚5~25mm

LED交換

不可

調光

防雨形

60°

温度保護

機能付

埋込穴

100

埋込

必要高

80

傾斜天井

55°

準耐火

準耐火

2024.11.08.





PG House

伊藤友章様邸

新築工事

Lighting

Plan (図番 7-3)

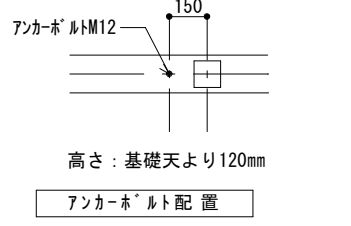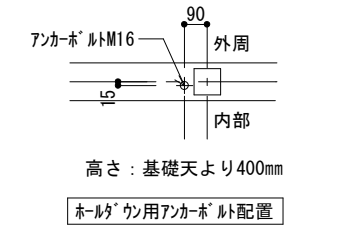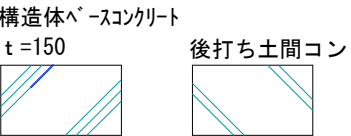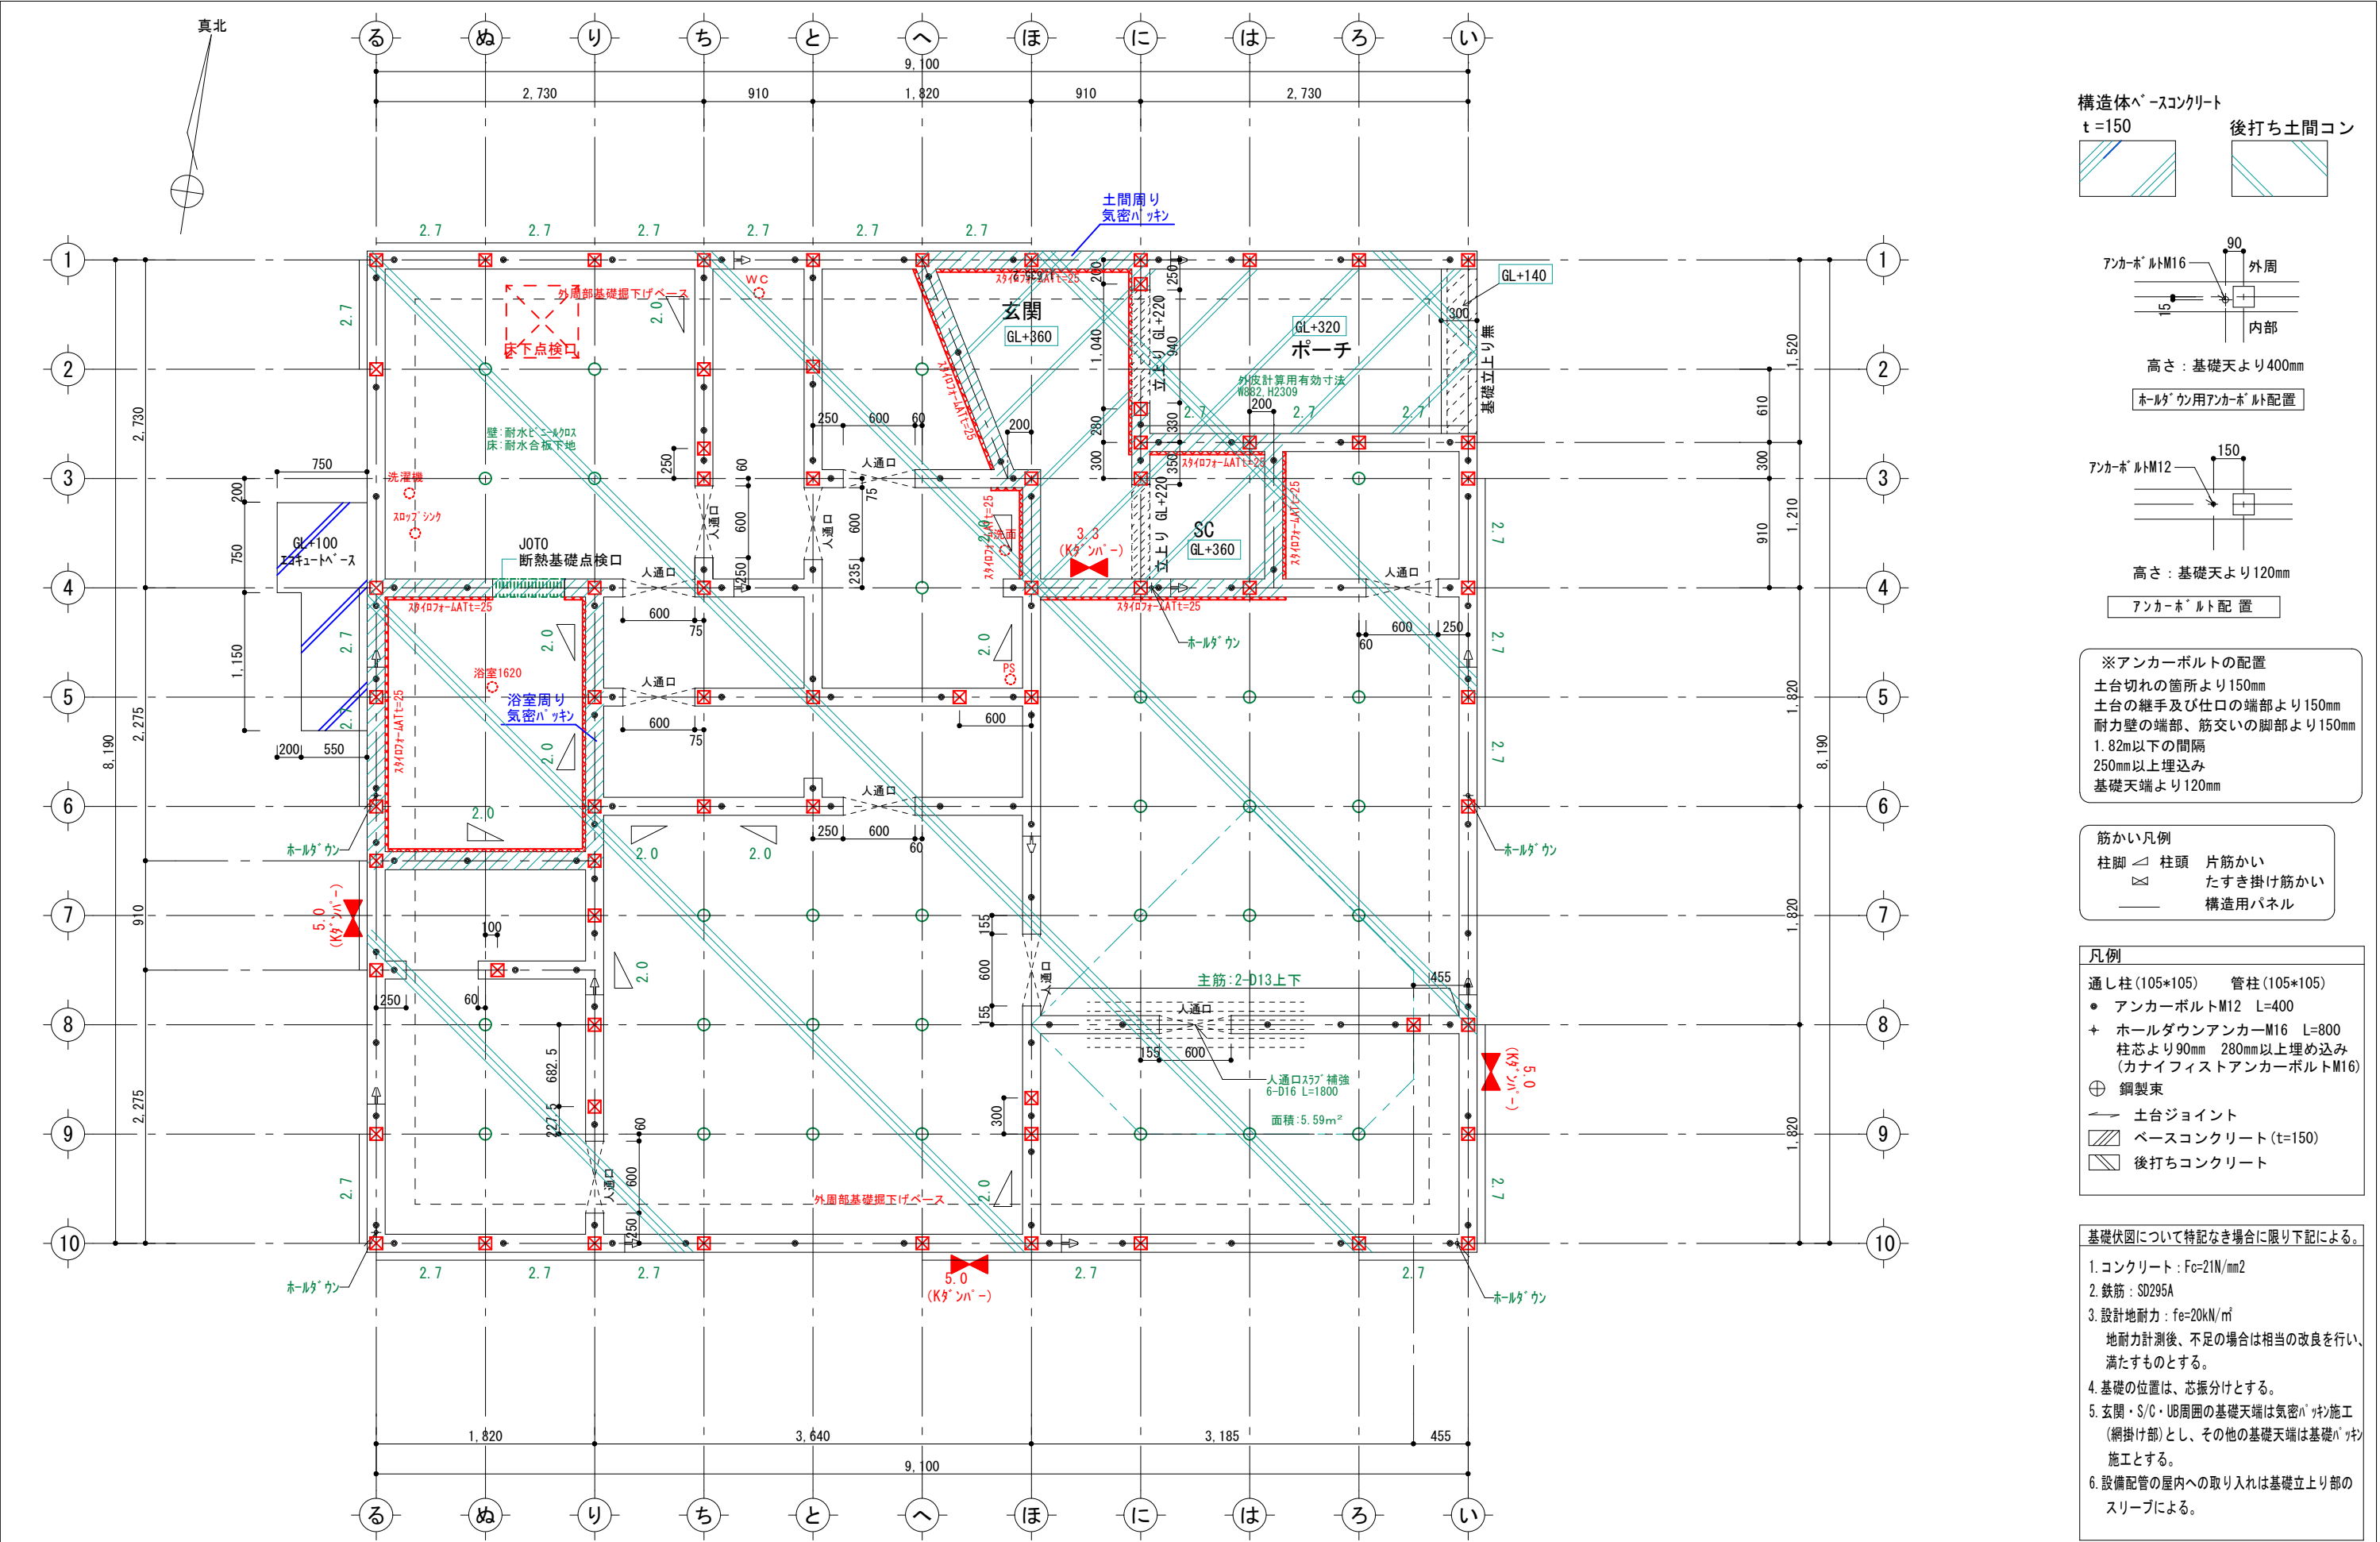


※アンカーボルトの配置
土台切れの箇所より150mm
土台の継手及び仕口の端部より150mm
耐力壁の端部、筋交いの脚部より150mm
1.82m以下の間隔
250mm以上埋込み
基礎天端より120mm

筋かい凡例
柱脚 柱頭 筋かい
たすき掛け筋かい
構造用パネル


凡例
通し柱(105*105) 管柱(105*105)
● アンカーボルトM12 L=400
+ ホールダウンアンカーM16 L=800
柱芯より90mm 280mm以上埋め込み
(カナイフィーストアンカーボルトM16)
⊕ 鋼製束
土台ジョイント
ベースコンクリート (t=150)
後打ちコンクリート

基礎伏図について特記なき場合に限り下記による。


- コンクリート：Fc=21N/mm2
- 鉄筋：SD295A
- 設計地耐力：fe=20kN/m²
地耐力計測後、不足の場合は相当の改良を行い、満たすものとする。
- 基礎の位置は、芯振分けとする。
- 玄関・S/C・UB周囲の基礎天端は気密パッキン施工（網掛け部）とし、その他の基礎天端は基礎パッキン施工とする。
- 設備配管の屋内への取り入れは基礎立上り部のスリーブによる。

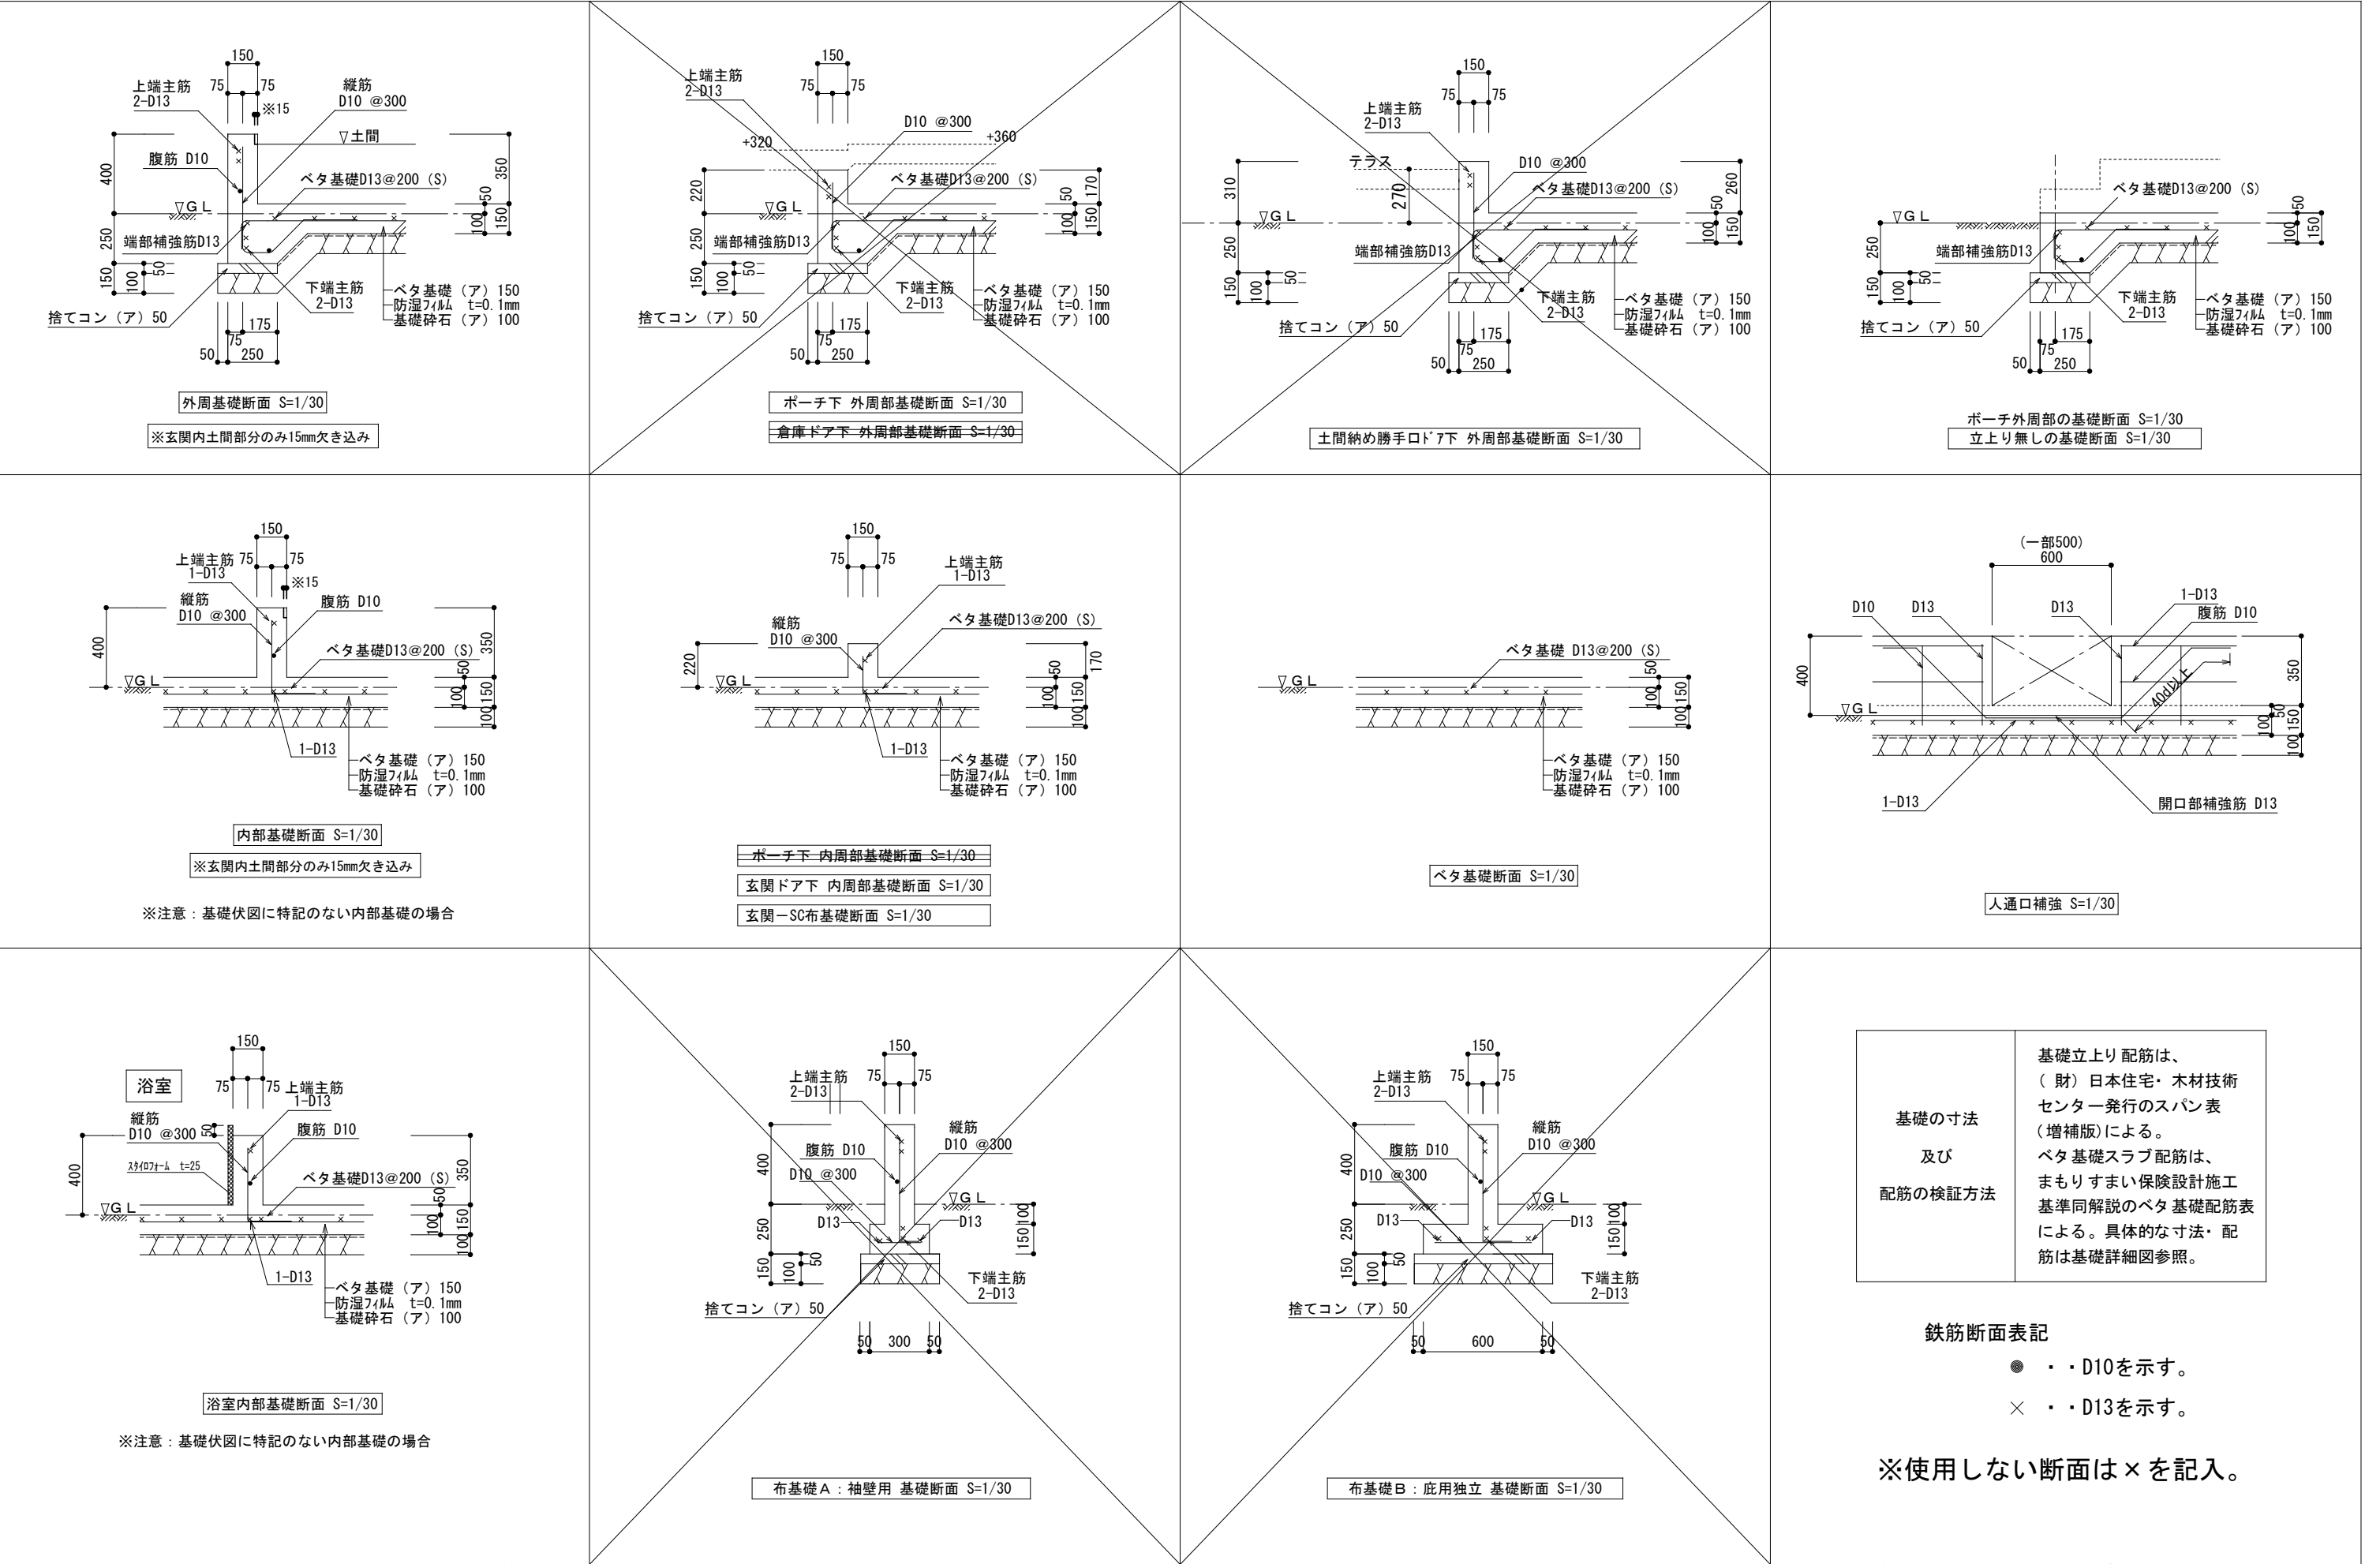

訂 正	浜 岡 一 級 総 合 設 計 事 務 所 一級建築士事務所 静岡県知事登録第 (10)2441 号 一級建築士 大臣登録第 365879 号 西原利昌		株式会社 LIFE FUND InDesign office 一級建築士事務所 事務所登録 (2) 第7595号 一級建築士登録 第179770号 鈴木 達男 〒432-8023 静岡県浜松市中央区鴨江3丁目70番23号	年 月 日 2024. 11. 23	件 名 伊藤友章様邸 新築工事		設計	I C	工務	図 番
				縮 尺 1/30	図 名 基礎断面リスト		倉田	青島	B-2	

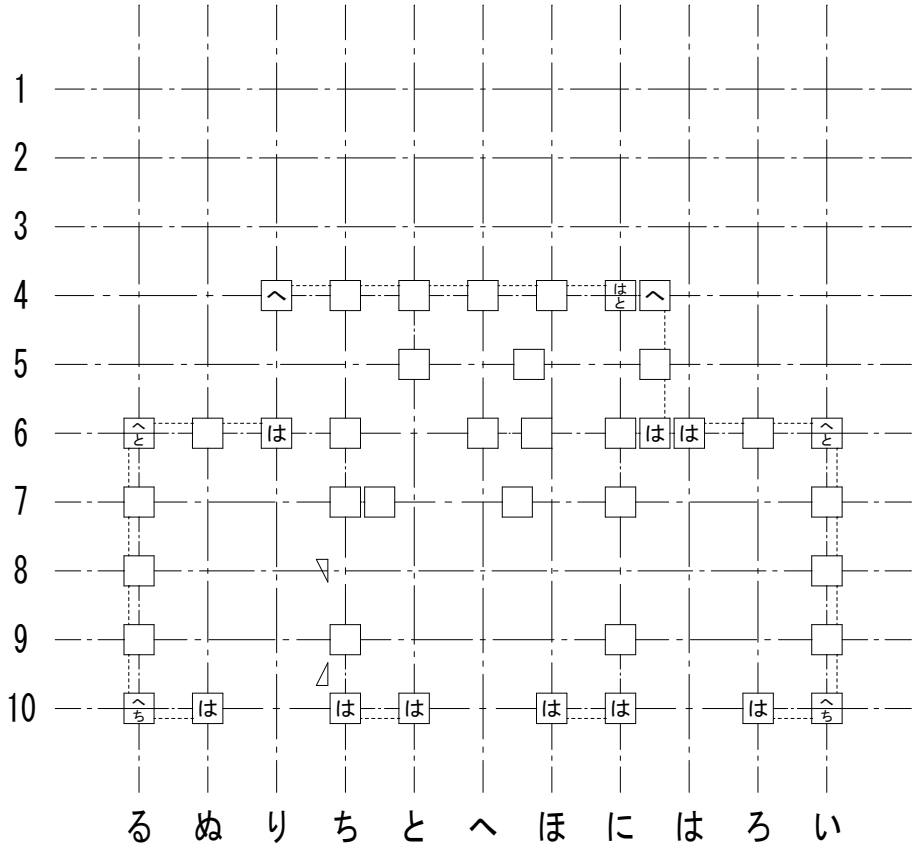

2階柱壁伏図

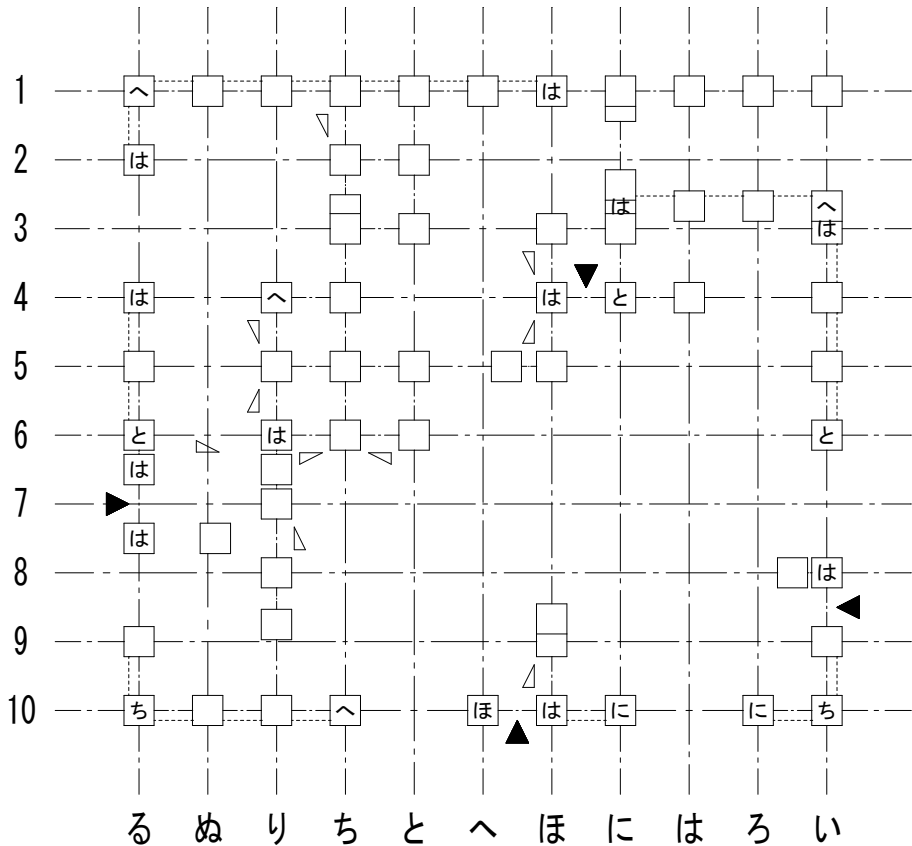

1階柱壁伏図

接合部凡例				*接合部凡例はユーザ設定されたものです。	
記号	仕様（カナイ金物）		N	倍率	
SBCP	スリムビルドコーナー75		0.00	1.00	
SBCP	スリムビルドコーナー75		0.65	1.00	
SBCP	は	スリムビルドコーナー75	1.00	1.00	
ARCG	に	アレントコーナー合板用	1.40	2.20	
ARCG	ほ	アレントコーナー合板用	1.60	2.20	
ARCG	へ	アレントコーナー合板用	1.80	2.20	
HD15	と	ブレイブホールダウン B-HD15	2.80	3.60	
HD20	ち	ブレイブホールダウン B-HD20	3.70	4.70	
HD25	り	ブレイブホールダウン B-HD25	4.70	4.80	
HD30	ぬ	ブレイブホールダウン B-HD30	5.60	7.20	
J1	る	腰掛け蟻若しくは大入れ蟻掛け+羽子板*ルト、短冊金物		1.90	梁継手・仕口用
J2	を	腰掛け蟻若しくは大入れ蟻掛け+羽子板*ルト、短冊金物×2		3.00	梁継手・仕口用

※表示なき金物は「は」とする。

接合部凡例				*接合部凡例はユーザ設定されたものです。	
記号	仕様（タナカ金物）		N	倍率	
FCP	フックコーナー		0.00	1.00	
FCP	フックコーナー		0.65	1.00	
FCP	は	フックコーナー	1.00	1.00	
CCP	に	シナコーナー	1.40	2.20	
CCP	ほ	シナコーナー	1.60	2.20	
CCP	へ	シナコーナー	1.80	2.20	
HD15	と	ビス止めホールダウンU HD15	2.80	3.60	
HD20	ち	ビス止めホールダウンU HD20	3.70	4.70	
HD25	り	ビス止めホールダウンU HD25	4.70	4.80	
HD30	ぬ	ビス止めホールダウンU HD15×2（HD35）	5.60	7.20	
J1	る	腰掛け蟻若しくは大入れ蟻掛け+羽子板*ルト、短冊金物		1.90	梁継手・仕口用
J2	を	腰掛け蟻若しくは大入れ蟻掛け+羽子板*ルト、短冊金物×2		3.00	梁継手・仕口用

※表示なき金物は「は」とする。

筋かいの種類に応じた筋かいの端部の接合部の仕様		
	筋かいの種類	接合部の仕様（構造方法）
イ	鉄筋φ9	柱又は横架材を貫通し、三角座金を介してナット締め、又は鋼板添え板を用い鋼板を柱及び横架材にCN90, 8本平打ち
ロ	筋かい:15×90	柱・横架材を欠き込み、柱・横架材双方に対してN65, 5本平打ち
ハ	筋かい:30×90	鋼板添え板t=1.6mmを筋かいに対してボルトφ12及びCN65, 3本平打ち、柱に対してCN65, 3本平打ち、横架材に対してCN65, 4本平打ち。筋かいプレートBP同等品
ニ	筋かい:45×90	鋼板添え板t=2.3mmを筋かいに対してボルトφ12及びスクリュー釘φ4.5L50, 7本平打ち、柱及び横架材に対してスクリュー釘φ4.5L50, 5本平打ち。筋かいプレートBP-2同等品
ホ	筋かい:90×90	柱又は横架材にボルトφ12mmを用いて一面剪断接合

胴差と通し柱の接合部の仕様		
	胴差と通し柱の条件	仕口
T1	通し柱の片側に胴差が来る場合	胴差を柱にかたぎ大入れ短ほぞ差しの上、羽子板ボルト、かね折り金物又は同等以上の仕口
T2	通し柱の両側に胴差が来る場合	胴差を柱にかたぎ大入れ短ほぞ差しの上、短冊金物又は、同等以上の仕口で胴差相互を緊結
T3	通し柱と胴差の接合部の近くに90×90以上の筋かいが来る場合（通し柱が建物の出隅にあるか、筋かい壁が外壁と直交して接する場合）	胴差を通し柱に、15KN用引き寄せ金物を水平に用いて緊結