


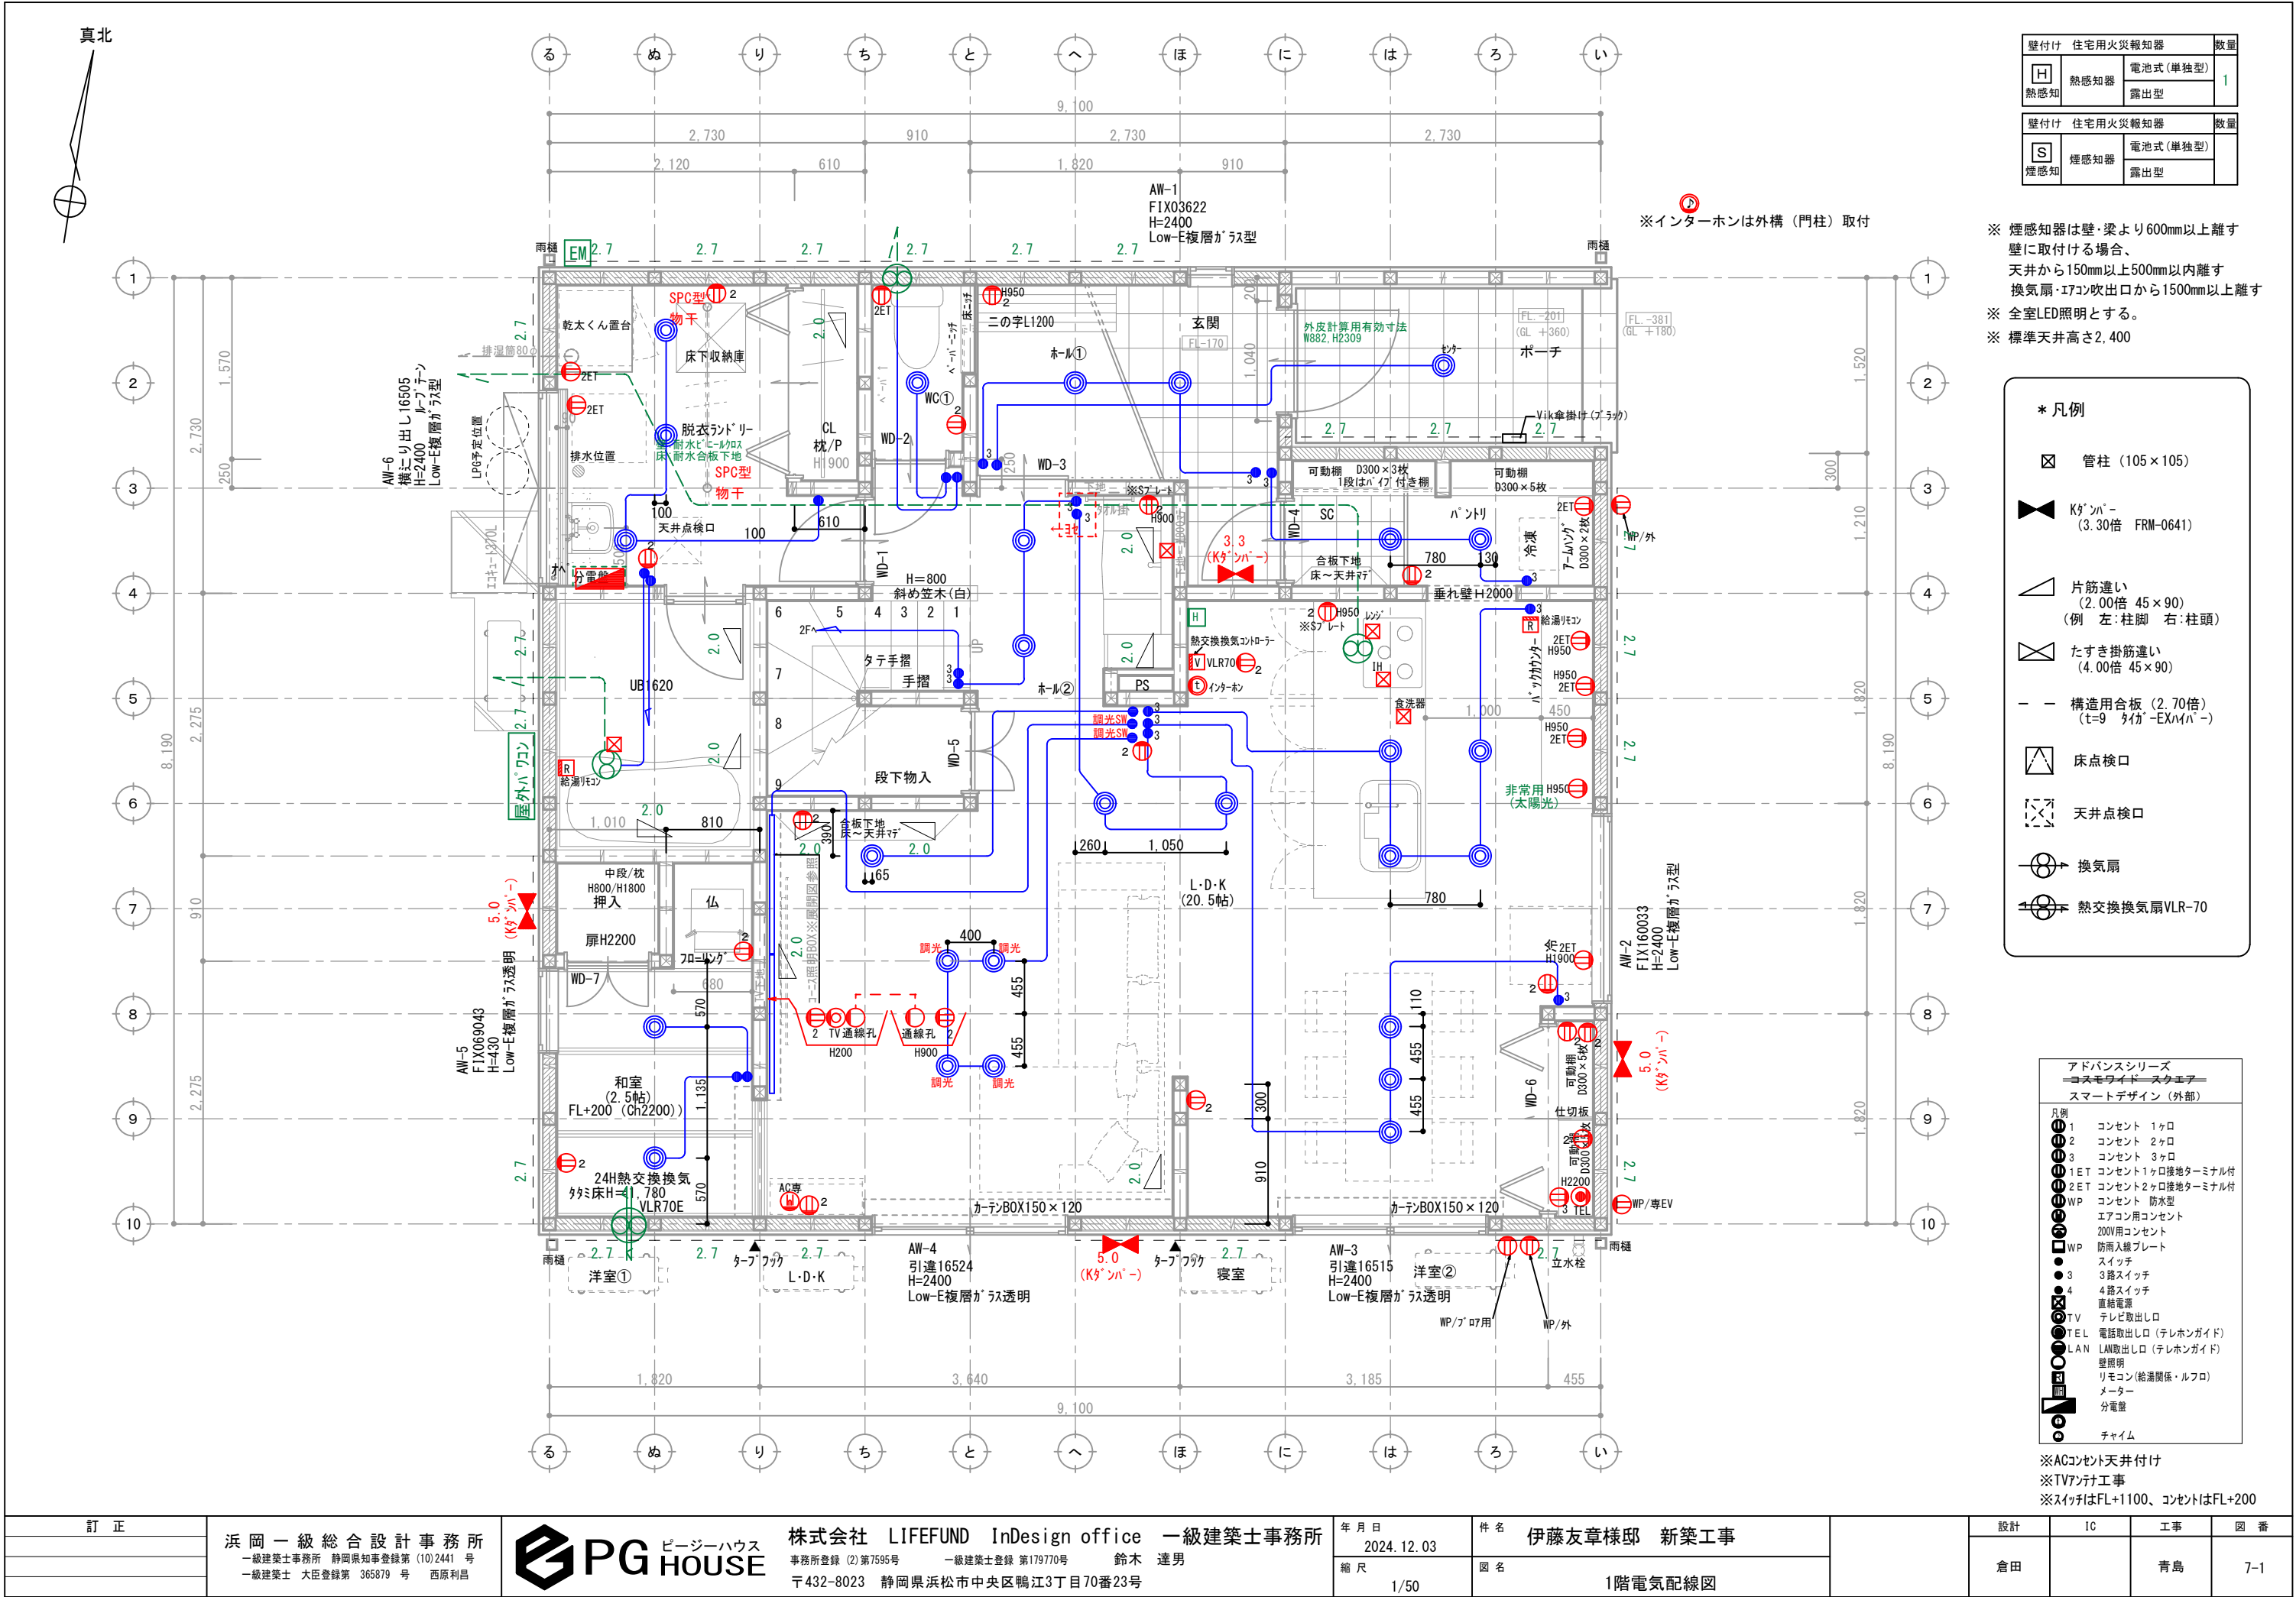

壁付け 住宅用火災報知器			数量
熱感知	H	電池式 (単独型)	1
		露出型	
壁付け 住宅用火災報知器			数量
煙感知	S	電池式 (単独型)	
		露出型	

※ 煙感知器は壁・梁より600mm以上離す
壁に取付ける場合、
天井から150mm以上500mm以内離す
換気扇・エアコン吹出口から1500mm以上離す
※ 全室LED照明とする。
※ 標準天井高さ2,400

* 凡例

- 管柱 (105×105)
- Kタンパー (3.30倍 FRM-0641)
- 片筋違い (2.00倍 45×90)
(例 左:柱脚 右:柱頭)
- たすき掛筋違い (4.00倍 45×90)
- 構造用合板 (2.70倍)
(t=9 材種-EXハイバー)
- 床点検口
- 天井点検口
- 換気扇
- 熱交換換気扇VLR-70

アドバンスシリーズ コネクター・スイッチ・ターミナル スマートデザイン (外部)		
凡例	1	コンセント 1ヶ所
	2	コンセント 2ヶ所
	3	コンセント 3ヶ所
	1ET	コンセント1ヶ所接地ターミナル付
	2ET	コンセント2ヶ所接地ターミナル付
	WP	コンセント 防水型
		エアコン用コンセント
		200V用コンセント
	WP	防雨入線プレート
		スイッチ
	3	3路スイッチ
	4	4路スイッチ
		直結電源
	TV	テレビ取出口
	TEL	電話取出口 (テレホンガイド)
	LAN	LAN取出口 (テレホンガイド)
		壁照明
		リモコン (給湯関係・ルフロ)
		メーター
		分電盤
		チャイム

※ACコンセント天井付け
※TVアンテナ工事
※スイッチはFL+1100、コンセントはFL+200