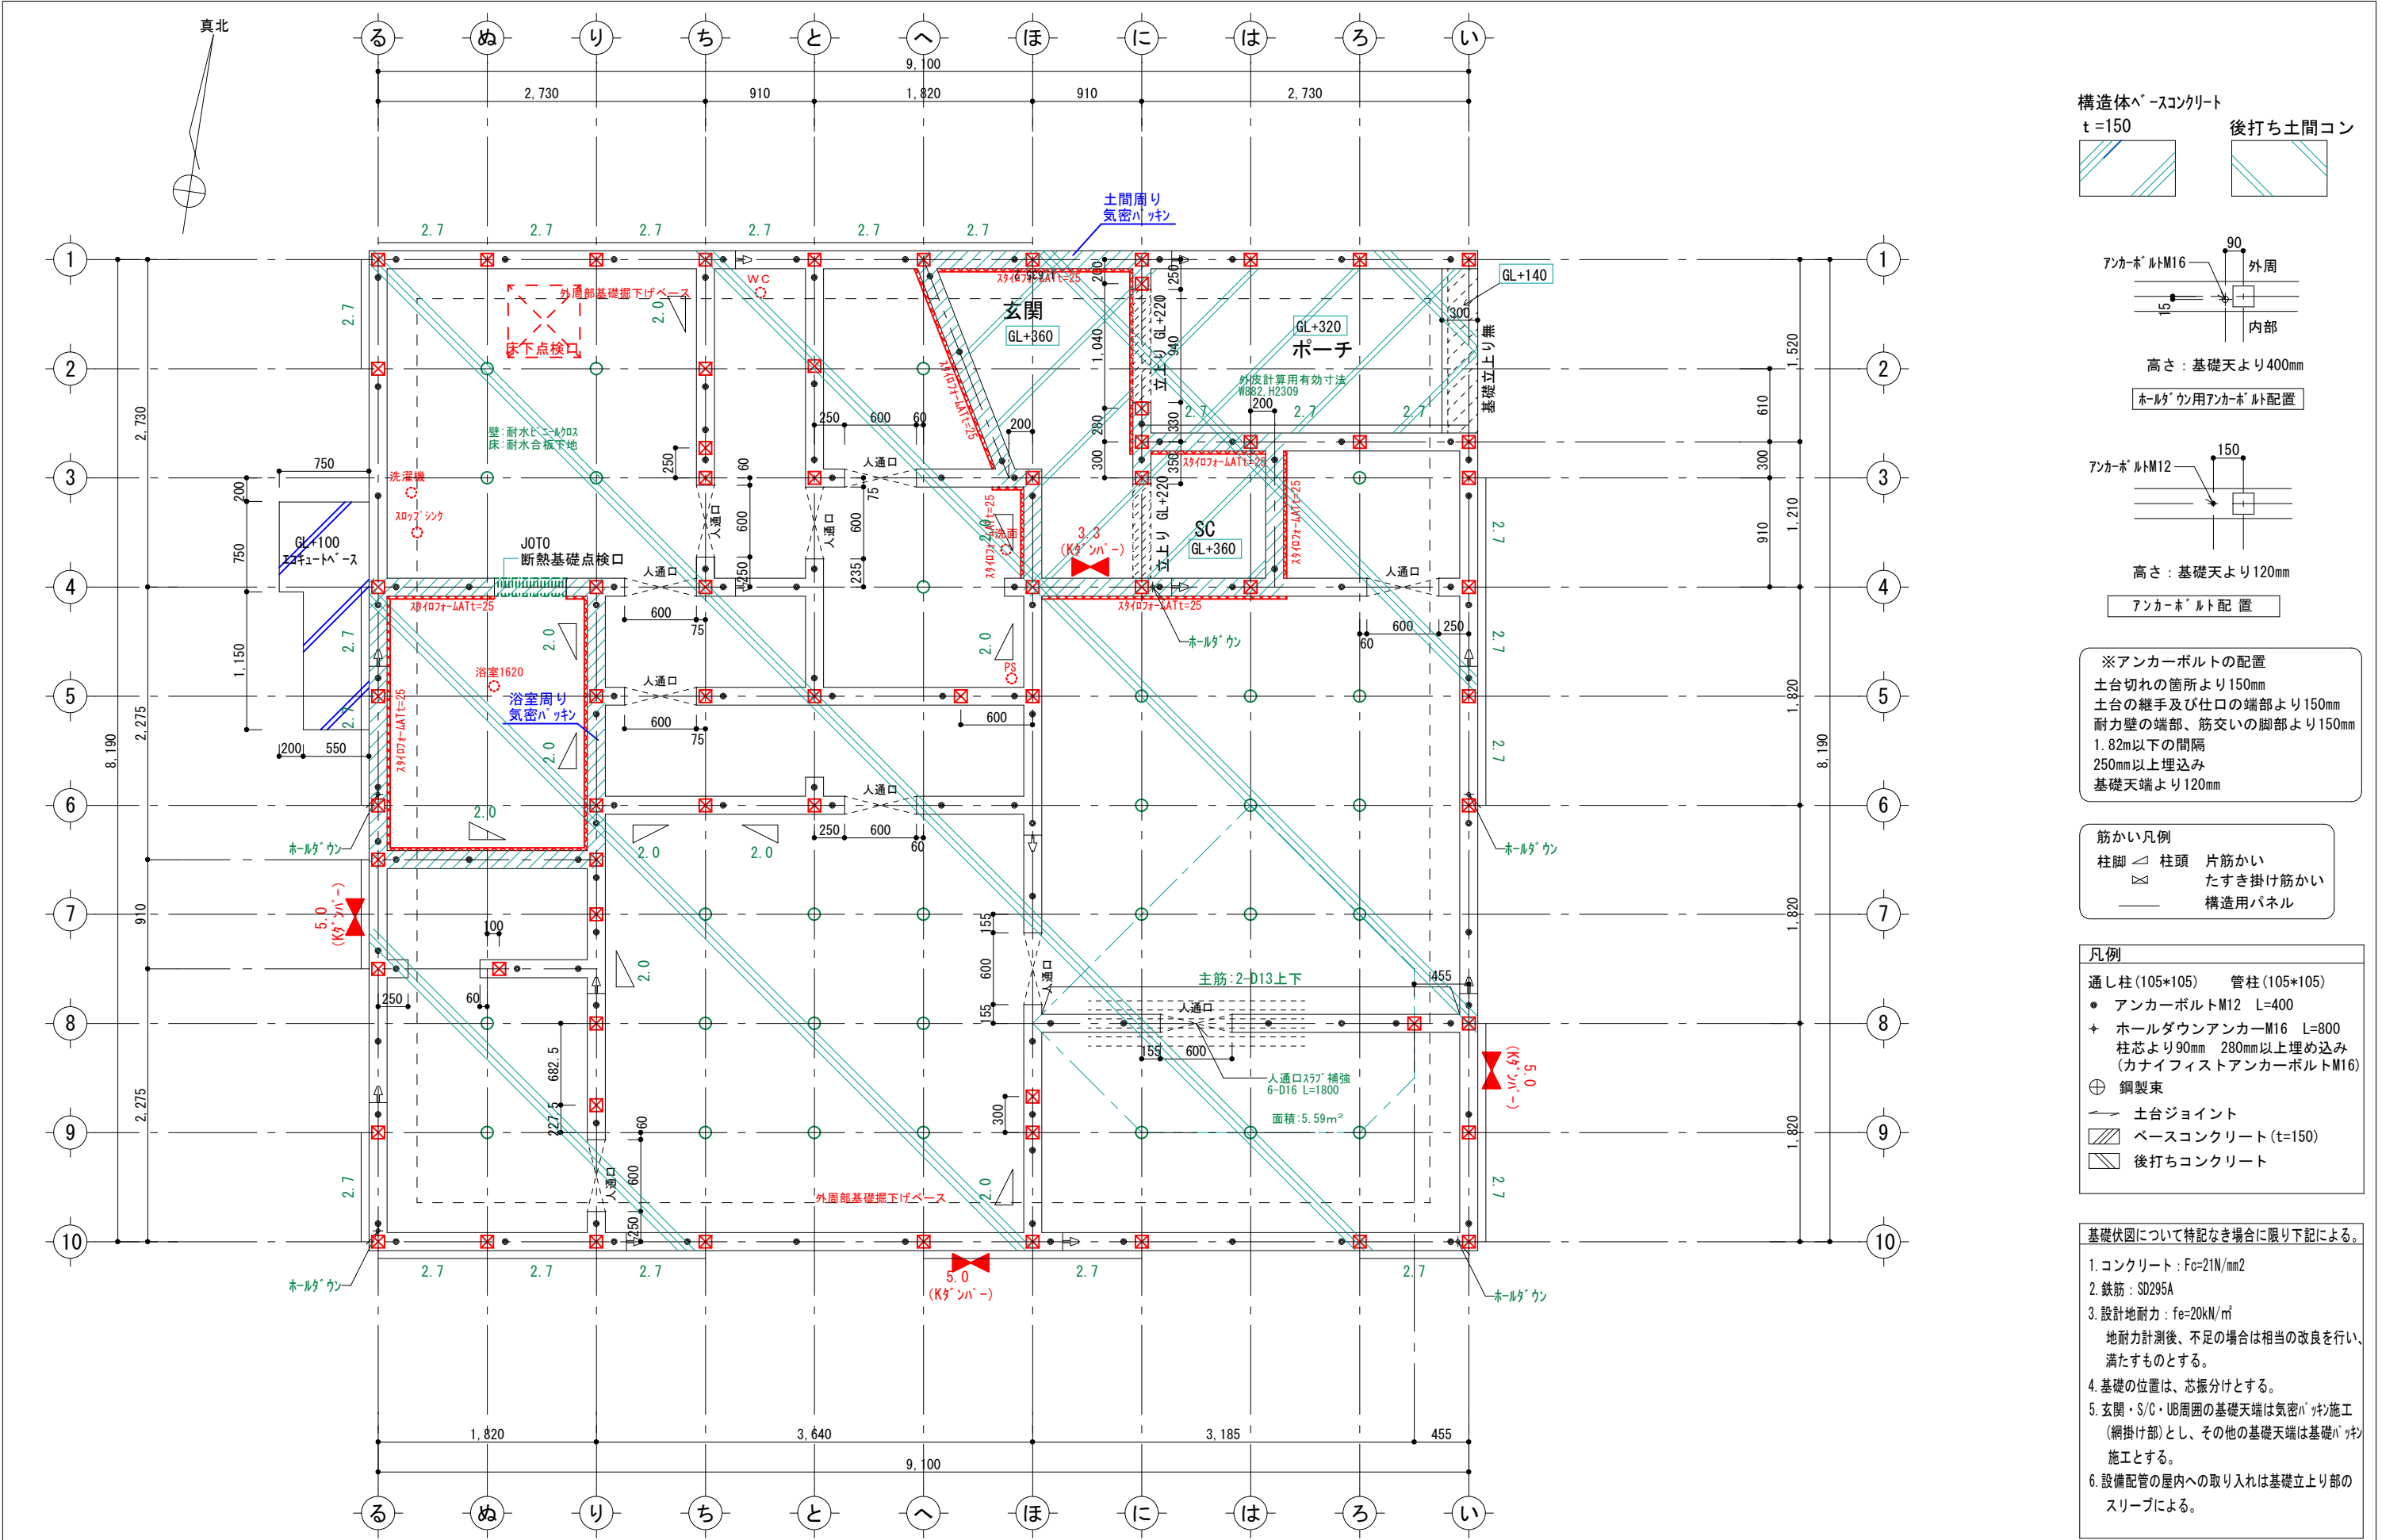


※アンカーボルトの配置
土台切れの箇所より150mm
土台の継手及び仕口の端部より150mm
耐力壁の端部、筋交いの脚部より150mm
1.82m以下の間隔
250mm以上埋込み
基礎天端より120mm

筋かい凡例
柱脚 柱頭 筋かい
たすき掛け筋かい
構造用パネル

凡例
通し柱 (105*105) 管柱 (105*105)
● アンカーボルトM12 L=400
+ ホールダウンアンカーM16 L=800
柱芯より90mm 280mm以上埋め込み
(カナイフィーストアンカーボルトM16)
⊕ 鋼製束
土台ジョイント
ベースコンクリート (t=150)
後打ちコンクリート

基礎伏図について特記なき場合に限り下記による。

- コンクリート: $F_c=21N/mm^2$
- 鉄筋: SD295A
- 設計地耐力: $f_e=20kN/m^2$
地耐力計測後、不足の場合は相当の改良を行い、満たすものとする。
- 基礎の位置は、芯振分けとする。
- 玄関・S/C・UB周囲の基礎天端は気密パッキン施工 (網掛け部) とし、その他の基礎天端は基礎パッキン施工とする。
- 設備配管の屋内への取り入れは基礎立上り部のスリーブによる。