

■ 仕 様			■ HEAT20 G1		
断熱工事		■ 床:カネライトフォーム t65 ■ 土間床等の外周:スタイロフォームAT t25 ■ 壁:アクアフォームLITE吹付 t85 ■ 天井:アクアフォームLITE吹付 t170			
床下換気		■ 基礎パッキン JOTO (玄関・UB周り:気密基礎パッキン)			
防虫防蟻		■ 土壌処理・木部 ガントナーMC			
■ 外 部 仕 上 表			■ 22条地域		
部位		仕上・仕様・メーカー		色番・品番	
屋根		■ ガルバリウム鋼板(t0.35)UK立平 ニスクカラーPro GH 軒先通気金物 日本住環境株式会社【REV-15】		GHK01 Sブラック	
パラペット笠木		■ なし			
破風・鼻隠		■ なし			
雨樋		(軒樋) ■ Panasonic サーフェスケアFS-I型		ブラック	
		(縦樋) ■ Panasonic S30角樋		ブラック	
軒天	屋根軒	■ なし			
	ポーチ軒	■ 神島化学 t= 6mm 軒天ボード エンボス		Wチャコールブラック	
	バルコニー軒	■ なし			
オーバーハング水切り		■ ガルバリウム鋼板 ※外壁合わせ JOTO:HF-A3550		ブラック	
外壁 ※下地面材:タイガーEXハイパー 防火認定 PC030BE-4028	通気金物(15mm)	■メイン	ニチハ エモンエクセラード16 Vシリーズ リーガストーン調V	ランダムMGブラック	
		■アクセントA	なし		
		■アクセントB	なし		
玄関ポーチ		■ 床 玄関タイルに同じ		-	
基礎		■ 立上り巾木: モルタル刷毛引き		-	
基礎水切り金物		■ JOTO鋼板製 防鼠材付き水切り JOTO:WMF-N35		ブラック	
バルコニー	床・内壁	■ なし		-	
	笠木	■ なし			
外部建具		■ LIXIL EW(アルゴンガス高遮熱仕様LowE複層ガラス グリーン) ・SD、TSで記載がないものは、オペレーターハンドルとする ・オペレーター付サッシは固定網戸とする ・グレモンハンドル式サッシの選択箇所は可動網戸とする		外観 ブラック 内観 ホワイト ※樹脂パッキン・網戸付	
シャッター		■ なし			
玄関扉		■ LIXIL ジエスタ2 K2仕様 LIXILファミロック タグキー×3 (電池式)		ドア型: M17 型 ドア色: カムブラック ハンドル: S型ハンドル 色 ブラック	
外部物干し金物		■			
換気フード		■ 局所換気扇(トイレ 浴室 キッチンフード) 防火ダンパー無		外気フード: ブラック	
		■ ダクトレス熱交換換気システム (日本スティーベル株式会社) VLR-70E 防火ダンパー無		外気フード: B ブラック	

■ 構 造 概 要					
基礎	■ RCベタ基礎コンクリート				
通し柱・管柱	■ 構造用集成材 105×105		間柱	■ 集成材	
土台	■ 桧 105×105	大引き	■ 桧 90*90	筋交い	■ 構造用製材 火打梁 ■ 鋼製火打(当社基準により米松あり)
桁・梁	■ 構造用製材及び集成材			制震装置	■ Kダンパー (株)アイ・エム・エー
■ 設 備 装 着 品					
住宅設備	部位	メーカー	商品名 ※ 詳細は見積り、プレゼン参照	見積りNo.	(日付)
	キッチン	LIXIL	■ ES ペニンシュラ型 スライドストッカー (扉 3色の内未決)	見積り番号 : A24105290035-004-3	(日付) 2024.10.11
	バックカウンタ ※オプション	LIXIL	■ ES L1800(W900スライドストッカー+マルチスペース) 引き出しTレール仕様 吊戸棚H500(フレンチオーク(ライトグレン))	見積り番号 : A24105290035-004-(5,7)	(日付) 2024.10.11
	浴室	LIXIL	■ AX1620 洗い場広タイプ ドア仕様	見積り番号 : A24105290035-004-1	(日付) 2024.10.11
	1Fトイレ	LIXIL	■ ベーシアシャワートイレ 白 ● タオル掛け: KF-AA70D(リンク) タンク手洗 無し ● 紙巻き器: CF-AA22H /WA	見積り番号 : A24105290035-004-9	(日付) 2024.10.11
	2Fトイレ	LIXIL	■ ベーシアシャワートイレ 白 ● タオル掛け: KF-AA70D(リンク) タンク手洗 有り ● 紙巻き器: CF-AA22H /WA	見積り番号 : A24105290035-004-10	(日付) 2024.10.11
	洗面台	LIXIL	■ EV W900(D500タイプ) 扉:グロスホワイト [引出しタイプ シングルハンドシャワー スタンダードLED三面鏡 その他 トールキャビネット300 ● タオル掛け: KF-AA71D(バー)	見積り番号 : A24105290035-004-8	(日付) 2024.10.11
	スロップシンク	LIXIL	■ S-17/BW1 シングルバー混合水栓SF-WM435SY(170)	A24105290035-004-11	2024.10.11
給排水設備	給湯器	■ エコキュート370L Panasonic NSシリーズ スタンダードモデル 追い焚きフルオート			
	排水	■ 合併浄化槽 5人槽 ポンプアップ無			
	外水栓	■ 1 カ所 (平面図参照)	■ 外部立栓柱: PVC製 水栓柱12型【前澤化成工業】		
	外部ガーデンパン	■ 無し			
	その他	■ 洗濯機用単水栓: 緊急止水弁付		■ 洗濯機用排水: トラップ金物(標準)	
		■ 排水さや管(長期優良住宅仕様)			
ガス配管設備		■ あり(LPG) (配置図・平面図参照 ※乾太くん用)			
電気設備	インターホン	■ パナソニック VL-SZ30KL			
	TVアンテナ	■ UHF + BS・110度CS/CSアンテナ [2K・4K・8K対応] ■ブラック ※電波状況によりホワイトになる可能性あり			
	エアコン	■ 設置場所:			
	ソーラー	■ あり(Qセルズ) 12 枚 5.28 KW		Re.RISE-G3 440 (1722×1134×30)	
	※標準搭載	※メーカーのモデルチェンジ等で後継品に変更される可能性あり			
		■ 屋外パワコン 西面			
その他					

浜 岡 一 級 総 合 設 計 事 務 所		株式会社 LIFEFUND InDesign office 一級建築士事務所		年 月 日	件 名	設計 IC 工務 図 番			
一級建築士事務所 静岡県知事登録第 (10)2441 号 一級建築士 大臣登録第 365879 号 西原利昌		PG HOUSE 事務所登録 (2)第7595号 一級建築士登録 第179770号 鈴木 達男 〒432-8023 静岡県浜松市中央区鴨江3丁目70番23号		2024.11.8 縮尺	伊藤友章 様邸 新築工事 図面 仕上表 1				
						倉田	青島	1-1	


内 部 仕 上 表（壁下地:石膏ボード12.5mm/天井下地:9.5mm）※脱衣室:床合板特類 下地									
階		床	巾木	壁	品番	廻 縁	天 井	品番	特記事項
1F	ポーチ	LIXILパセオ300/PSO-FIO 4							
	玄関	LIXILパセオ300/PSO-FIO 4	ライン巾木(W)	ビニルクロス	SLP-251	突付	ビニルクロス	SLP-251	
	SC	LIXILパセオ300/PSO-FIO 4	ライン巾木(W)	ビニルクロス	SLP-251	突付	ビニルクロス	SLP-251	
	パントリー	イタ銘木フローラスティックt12 ナラ桎3P	ライン巾木(W)	ビニルクロス	SLP-251	突付	ビニルクロス	SLP-251	
	ホール①								
	ホール②/洗面	イタ銘木フローラスティックt12 ナラ桎3P	ライン巾木(W)	ビニルクロス	SLP-251	突付	ビニルクロス	SLP-251	
	WC①	フロアタイルt2.3 サンゲツIS-2071	H40ソフト巾木W97	ビニルクロス	SLP-251	突付	ビニルクロス	SLP-251	ペーパーニッチ/床ニッチ
	脱衣ラントリー	フロアタイルt2.3 サンゲツIS-2071	H40ソフト巾木W97	ビニルクロス	SLP-251	突付	ビニルクロス	SLP-251	SPC型物干 乾太くん台
	ダイニングキッチン	イタ銘木フローラスティックt12 ナラ桎3P	ライン巾木(W)	ビニルクロス	SLP-251	突付	ビニルクロス	SLP-251	
	リビング	イタ銘木フローラスティックt12 ナラ桎3P	ライン巾木(W)	ビニルクロス	SLP-251	突付	ビニルクロス	SLP-251	
	和室	1畳縁ありスタイロ置 t55	畳寄せ	ビニルクロス	SLP-251	突付	ビニルクロス	SLP-251	畳縁:高田織物 浮No.13
	仏間	イタ銘木フローラスティックt12 ナラ桎3P	雑巾摺	ビニルクロス	SLP-251	突付	ビニルクロス	SLP-251	
2F	ホール③	イタ銘木フローラスティックt12 ナラ桎3P	ライン巾木(W)	ビニルクロス	SLP-251	突付	ビニルクロス	SLP-251	
	洋室①	イタ銘木フローラスティックt12 ナラ桎3P	ライン巾木(W)	ビニルクロス	SLP-251	突付	ビニルクロス	SLP-251	アタリ
	洋室②①	イタ銘木フローラスティックt12 ナラ桎3P	ライン巾木(W)	ビニルクロス	SLP-251	突付	ビニルクロス	SLP-251	マロン202 BB 8690
	洋室③②	イタ銘木フローラスティックt12 ナラ桎3P	ライン巾木(W)	ビニルクロス	SLP-251	突付	ビニルクロス	SLP-251	〃 B 8680
	WIC	イタ銘木フローラスティックt12 ナラ桎3P	ライン巾木(W)	ビニルクロス	SLP-251	突付	ビニルクロス	SLP-251	
	WC②	フロアタイルt2.3 サンゲツIS-2071	H40ソフト巾木W97	ビニルクロス	SLP-251	突付	ビニルクロス	SLP-251	ペーパーニッチ
物入・収納・CL etc		※接続する部屋と同仕様とする							

上框&付框	■ LIXILラシッサS 付框30×150(全周廻し) 色: クリエペール
階段	■ LIXIL KA 階段 ササラ: プレシャスホワイト
KA階段で対応できない場合、オプションにてラシッサS階段	段板: クリエペール 蹴込板: プレシャスホワイト ラウンド手摺: プレシャスホワイト 手摺金物: プレシャスホワイト 上段框: クリエペール 長尺笠木: LIXIL プレシャスホワイト
窓枠	■ LIXIL スマート10 色: プレシャスホワイト ※浴室ドア枠 フクビ3方枠 []
キッチン笠木	■ なし 色:
カウンター	形状: t=
天井点検口	■ 天井アルミ点検口枠 450角 TAN45BW フクビ化学工業 ミルキーホワイト
床下収納庫	■ 高気密型床下点検口断熱型 SPF-R6060 城東テクノ 収納付 (脱衣室) ライトグレー(LG)
トイレ棚	■ 2階トイレ D250 アートランパー棚(シェルホワイト)
室内物干し金物	■ 川口技研SPC型1セット
LDK-カウンター	■ なし 色:
下足入 パッシュタイプ	■ LIXILラシッサS 色: クリエペール サイズ: W1200 D400 形状: 二の字型

支給品	■ 無し
備考	可動棚はパントリーのみ アタリ外 他は、シェルホワイト 受金物はすべてホワイト

内 部 建 具 表							
LIXIL ラフィス		建具色: プレシャスホワイト 枠色: 扉同色 ※その他、下記特記による 把手: スクエアL(シャインニッケル) 丁番 固定枠(156) 外付戸当り ガイドピン床色合せ 引戸のみ上吊ワイヤモーション					
階	No	室名	形式	枠外W サイズ 枠外H サイズ	デザイン 建具色	枠色 把手	特記事項
1	1	脱衣ラントリー	片開き戸	—	RAA	—	明り窓・表示錠
	WD			2400	—	—	
	2	WC①	片開き戸	—	RAA	—	明り窓・表示錠
	WD			2400	—	—	
	3	ホール①	アウトセット片引	—	RAA	—	
	WD			2400	—	—	
	4	SC	片開き戸	—	RAA	—	
	WD			2400	—	—	
	5	階段下収納	観音開	—	RAA	—	
	WD			2400	—	—	
	6	ダイニングCL	折れ戸		RAA		
	WD			2400			
	7	押入	観音開	—	RAA	—	
	WD			2200	—	—	H200mm切詰
	8	WC②	片引き戸	—	RAA	—	明り窓・表示錠
	WD			2400	—	—	
	9	洋室②	片開き戸	—	RAA	—	
	WD			2400	—	—	
	10	寝室	片引き戸	—	RAA	—	
	WD			2400	—	—	
	11	洋室①	片開き戸	2400	RAA	—	
	WD				—	—	

浜 岡 一 級 総 合 設 計 事 務 所		株式会社 LIFE FUND InDesign office 一級建築士事務所		年 月 日	件 名	設計 IC 工務 図 番	
一級建築士事務所 静岡県知事登録第 (10)2441 号 一級建築士 大臣登録第 365879 号 西原利昌		PG HOUSE 事務所登録 (2)第1696号 一級建築士登録 第17973号 鈴木 達男 〒432-8023 静岡県浜松市中央区鶴江3丁目70番23号		2024.11.8	伊藤友章 様邸 新築工事		
				縮尺	図面	倉田 0 青島 1-2	
				仕上表 2			

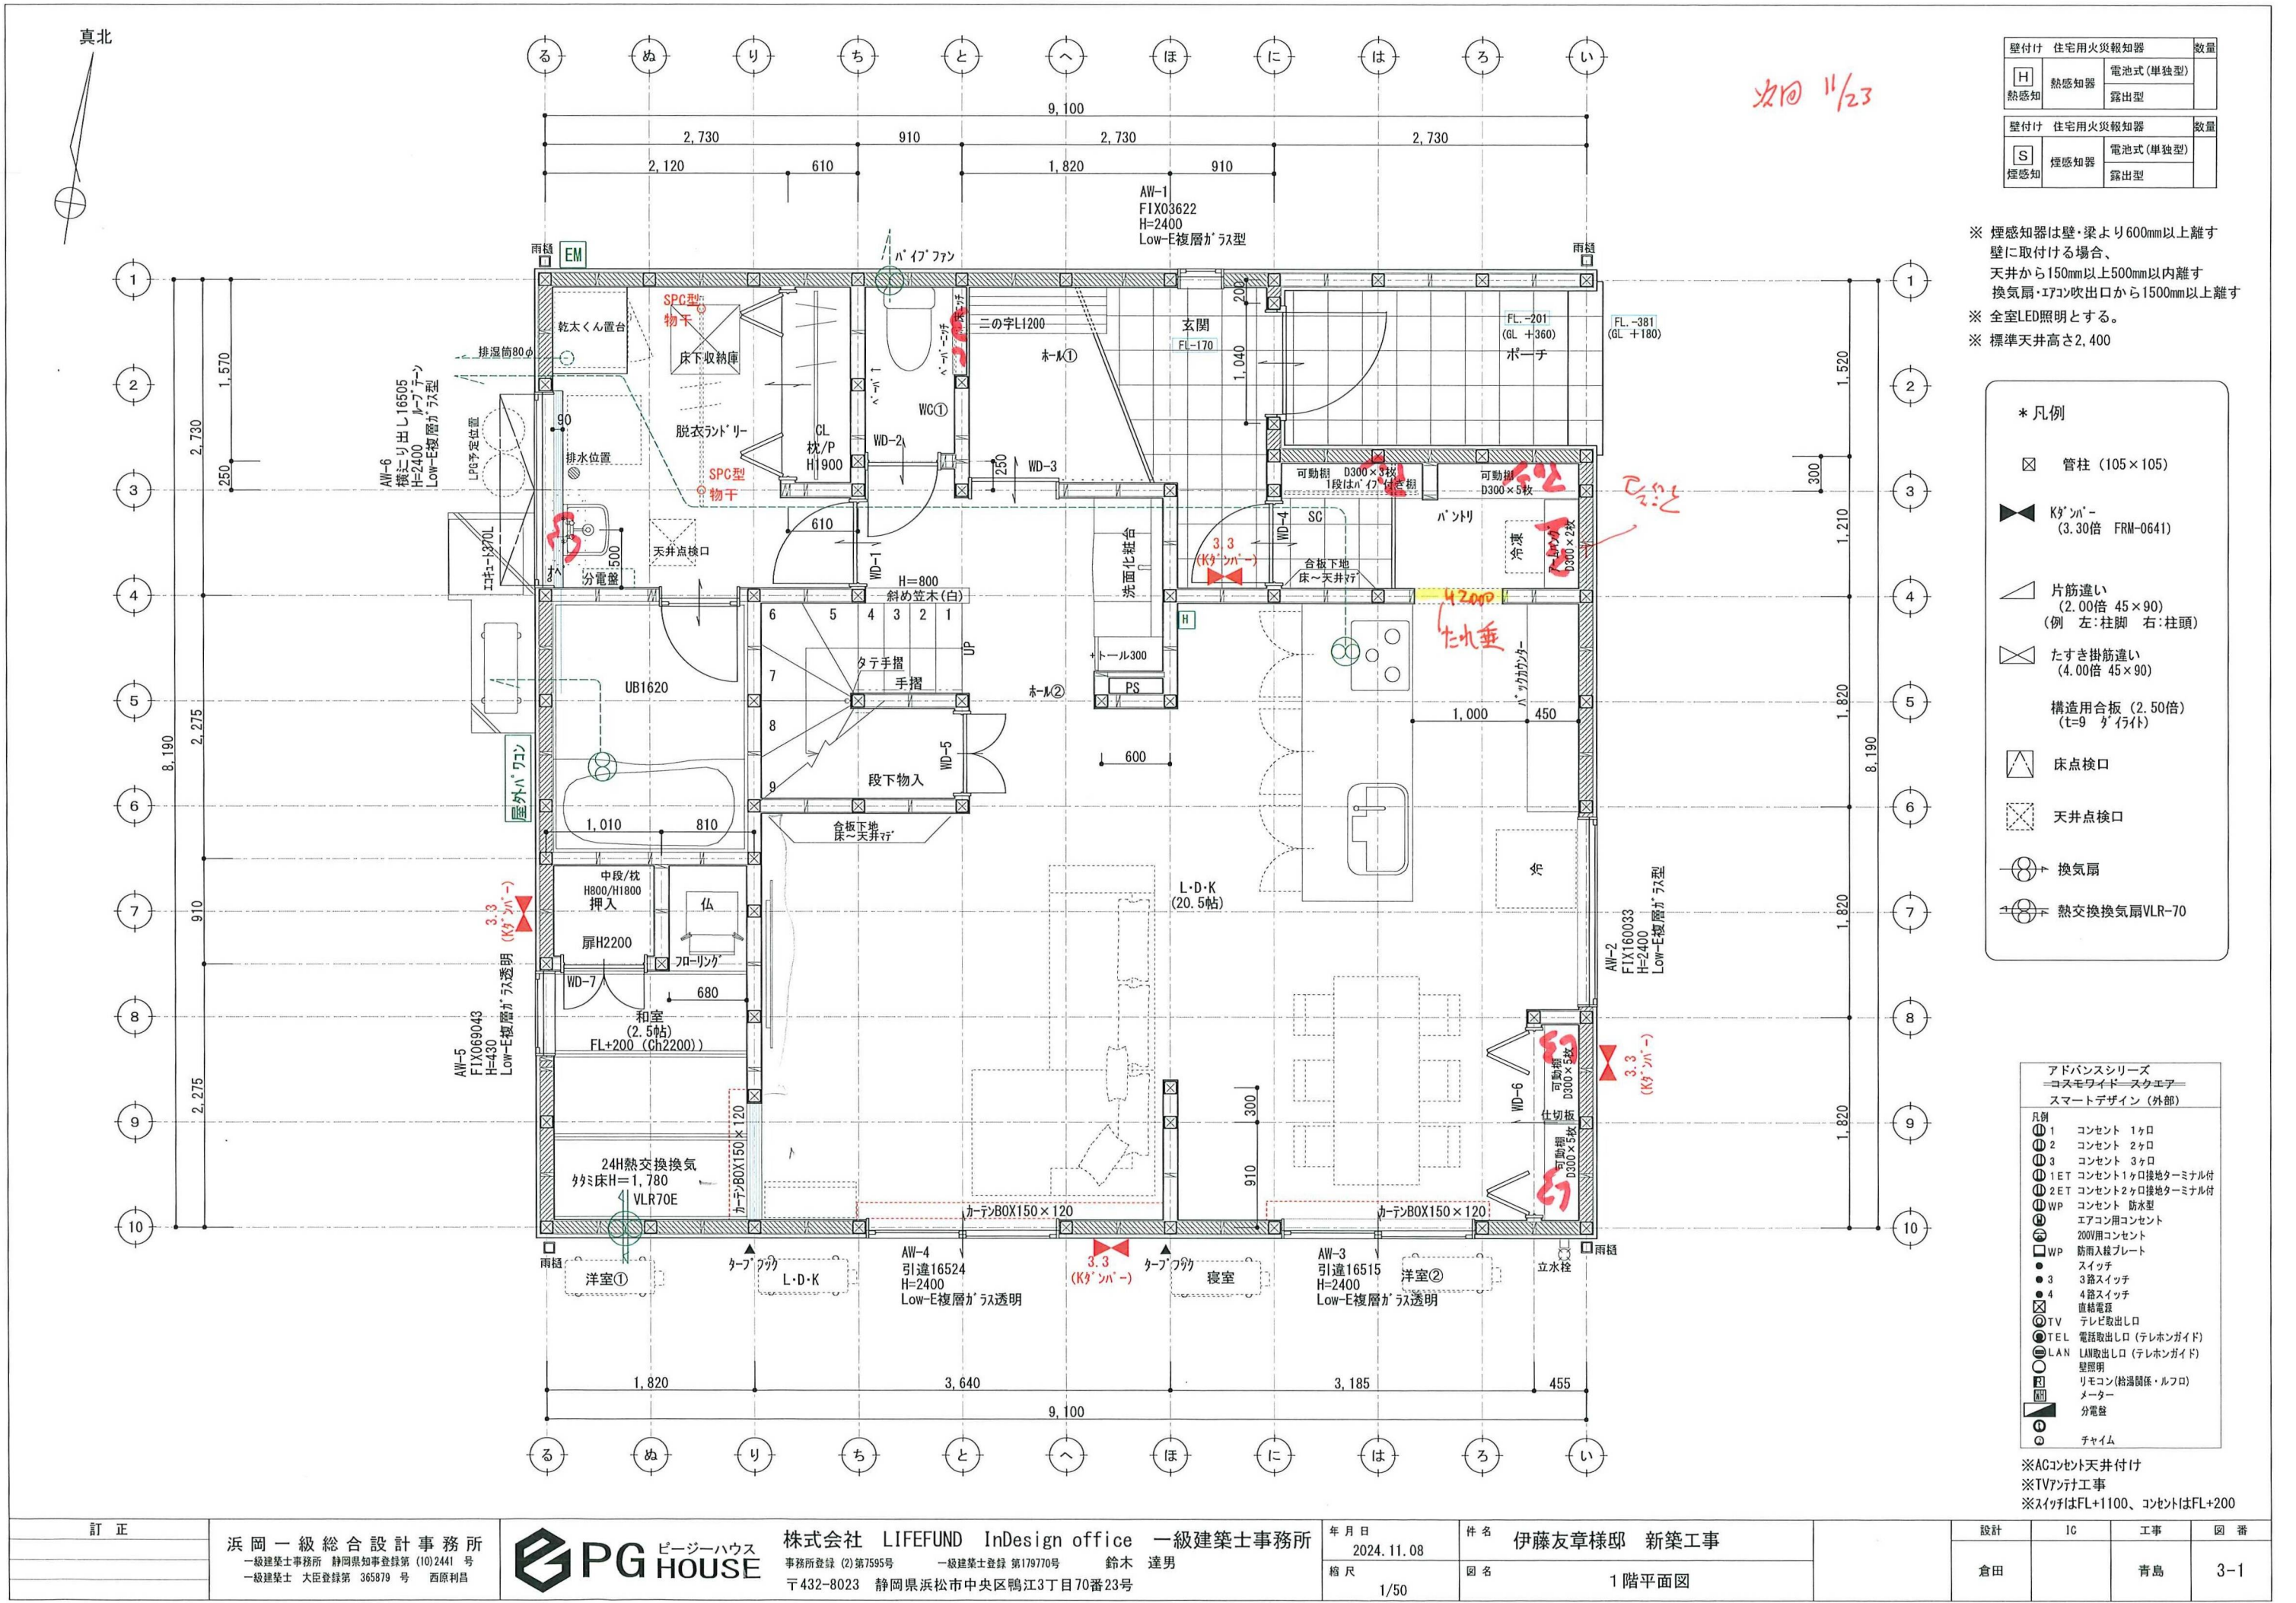

壁付け 住宅用火災報知器			数量
[H] 熱感知	熱感知器	電池式(単独型)	
	熱感知器	露出型	
壁付け 住宅用火災報知器			数量
[S] 煙感知	煙感知器	電池式(単独型)	
	煙感知器	露出型	

※ 煙感知器は壁・梁より600mm以上離す
壁に取付ける場合、
天井から150mm以上500mm以内離す
換気扇・エアコン吹出口から1500mm以上離す
※ 全室LED照明とする。
※ 標準天井高さ2,400

- * 凡例
- ☒ 管柱 (105×105)
 - ⚡ Kダクト (3.30倍 FRM-0641)
 - △ 片筋違い (2.00倍 45×90)
(例 左:柱脚 右:柱頭)
 - ⊠ たすき掛筋違い (4.00倍 45×90)
 - 構造用合板 (2.50倍)
(t=9 釘15t)
 - ⬆ 床点検口
 - ⬆ 天井点検口
 - ⊕ 換気扇
 - ⊕ 熱交換換気扇VLR-70

アドバンスシリーズ =コスモサイド=スクエア スマートデザイン (外部)		
凡例	1	コンセント 1ヶ所
2	コンセント 2ヶ所	
3	コンセント 3ヶ所	
1ET	コンセント1ヶ所接地ターミナル付	
2ET	コンセント2ヶ所接地ターミナル付	
WP	コンセント 防水型	
WP	エアコン用コンセント 200V用コンセント	
WP	防雨入線プレート	
3	スイッチ 3路スイッチ	
4	スイッチ 4路スイッチ	
⊗	直結電圧	
TV	テレビ取出口	
TEL	電話取出口 (テレホンガイド)	
LAN	LAN取出口 (テレホンガイド)	
⊕	照明	
リモコン	リモコン (給湯関係・ルフロ)	
メーター	メーター	
分電盤	分電盤	
チャイム	チャイム	

※ACコンセント天井付け
※TVアンテナ工事
※スイッチはFL+1100、コンセントはFL+200



壁付け 住宅用火災報知器			数量
H	熱感知器	電池式(単独型)	
	煙感知器	露出型	
壁付け 住宅用火災報知器			数量
S	煙感知器	電池式(単独型)	
	熱感知器	露出型	













※ 煙感知器は壁・梁より600mm以上離す
壁に取付ける場合、
天井から150mm以上500mm以内離す
換気扇・エアコン吹出口から1500mm以上離す
※ 全室LED照明とする。
※ 標準天井高さ2,400

*** 凡例**

- ☒ 管柱 (105×105)
- ◀▶ Kダクト (3.30倍 FRM-0641)
- △ 片筋違い (2.00倍 45×90)
(例 左:柱頭 右:柱頭)
- ⊠ たすき掛筋違い (4.00倍 45×90)
- ▤ 構造用合板 (2.50倍)
(t=9 ダイヤ)
- ⊞ 床点検口
- ⊞ 天井点検口
- ⊞ 換気扇
- ⊞ 熱交換換気扇VLR-70

アドバンスシリーズ =コスモライズ=ステア スマートデザイン (外部)	
凡例	
①	コンセント 1ヶ口
②	コンセント 2ヶ口
③	コンセント 3ヶ口
①ET	コンセント1ヶ口接地ターミナル付
②ET	コンセント2ヶ口接地ターミナル付
①WP	コンセント 防水型
①	エアコン用コンセント 200V用コンセント
WP	防雨入線プレート
●	スイッチ
●3	3路スイッチ
●4	4路スイッチ
⊞	直結電線
⊞TV	テレビ取出口
⊞TEL	電話取出口 (テレホンガイド)
⊞LAN	LAN取出口 (テレホンガイド)
⊞	壁照明
⊞	リモコン (給湯関係・ルフロ)
⊞	メーター
⊞	分電盤
⊞	チャイム


※ACコンセント天井付け
※TVアンテナ工事
※スイッチはFL+1100、コンセントはFL+200

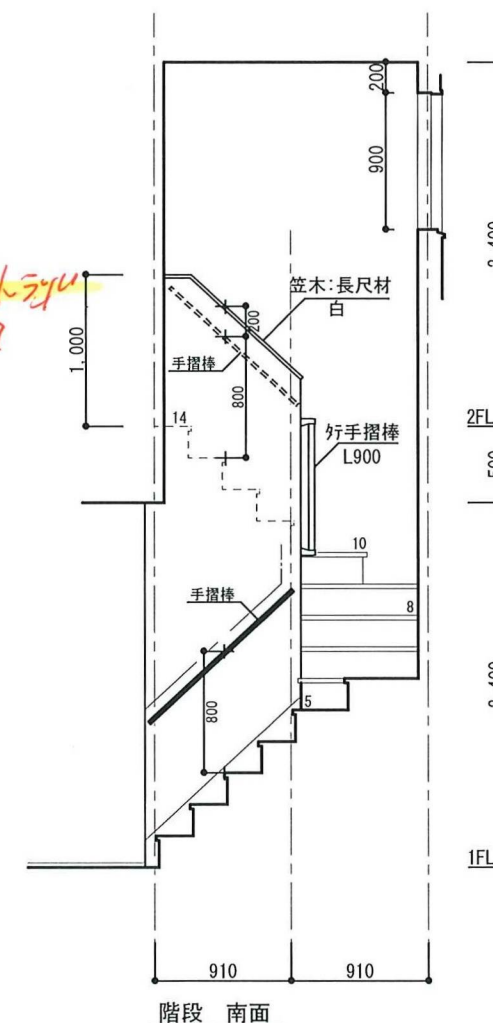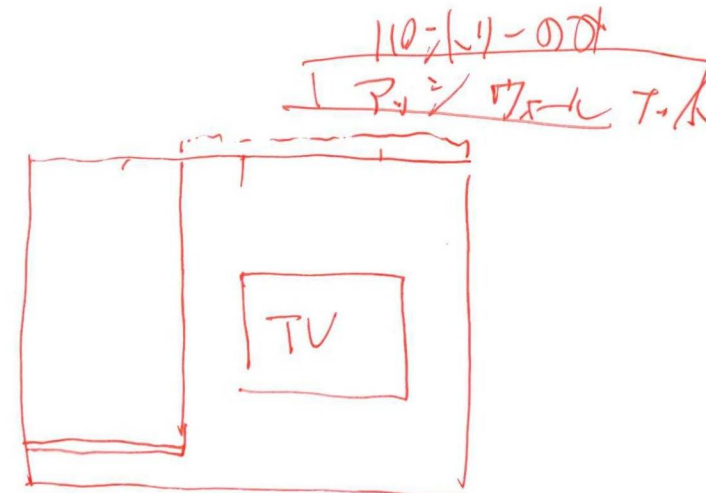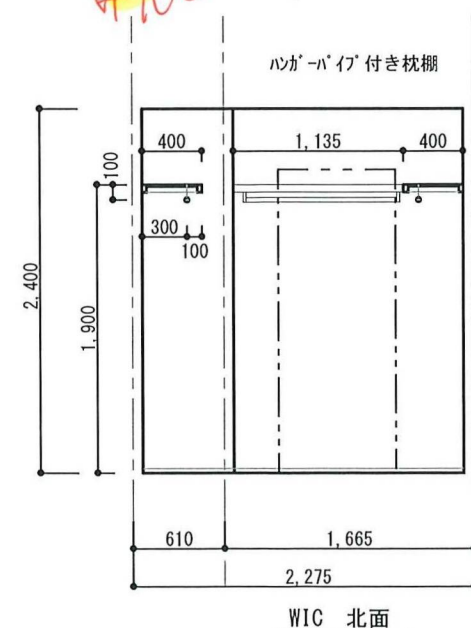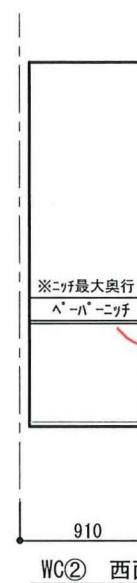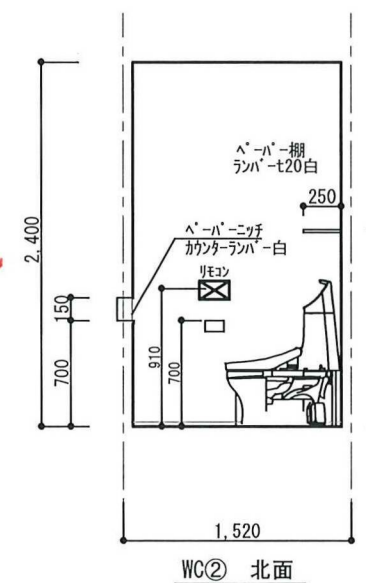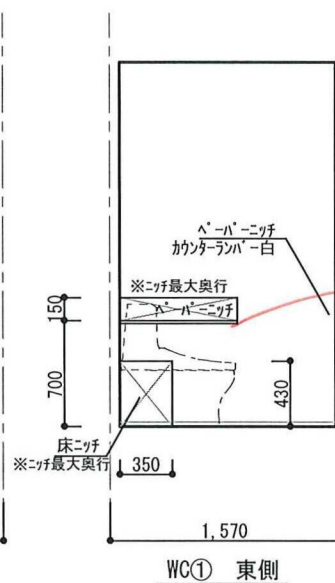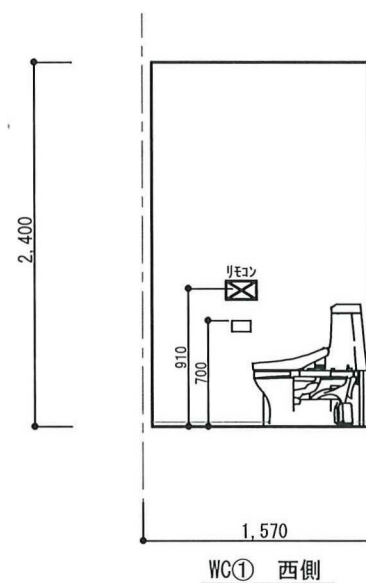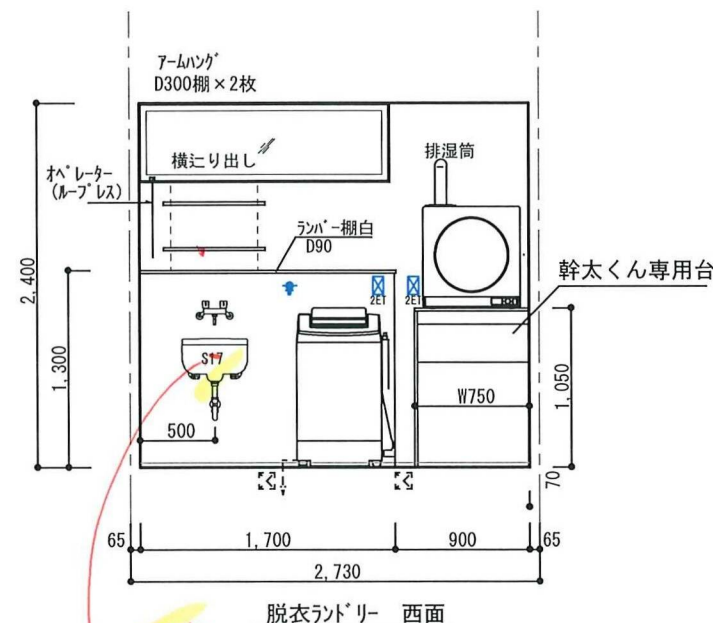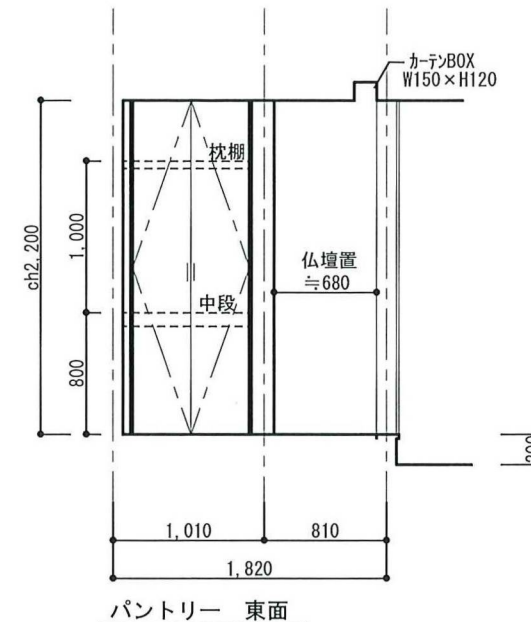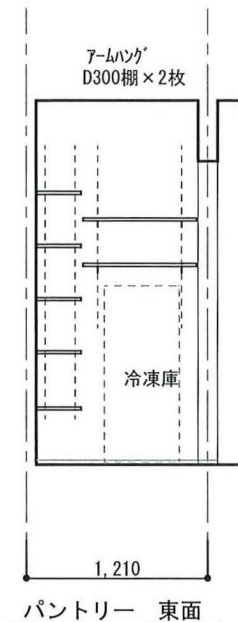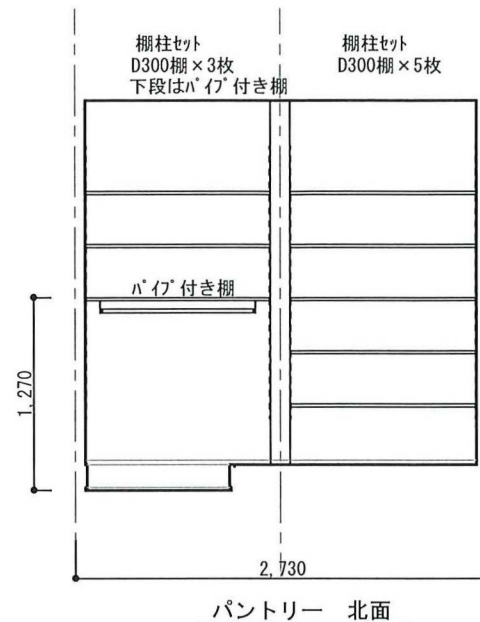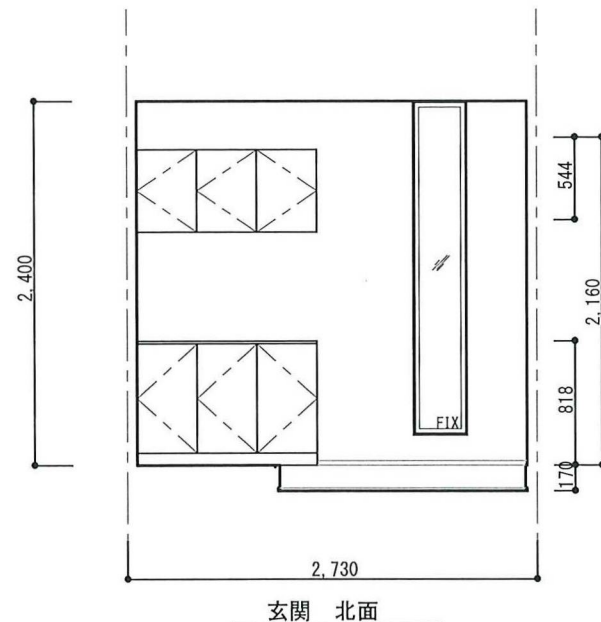

I-TD90SA

訂正	浜岡一級総合設計事務所 一級建築士事務所 静岡県知事登録第 (10)2441 号 一級建築士 大臣登録第 365879 号 西原利昌	LIFEFUND PG HOUSE	株式会社 LIFEFUND InDesign office 一級建築士事務所 事務所登録 (2)第7595号 一級建築士登録 第179770号 鈴木 達男 〒432-8023 静岡県浜松市中央区鶴江3丁目70番23号	年月日 2024.11.08 縮尺 1/50	件名 伊藤友章様邸 新築工事 図名 展開図	設計 倉田	IC	工事 青島	図番 6-1
----	--	----------------------	--	---------------------------------	--------------------------------	----------	----	----------	-----------

真北

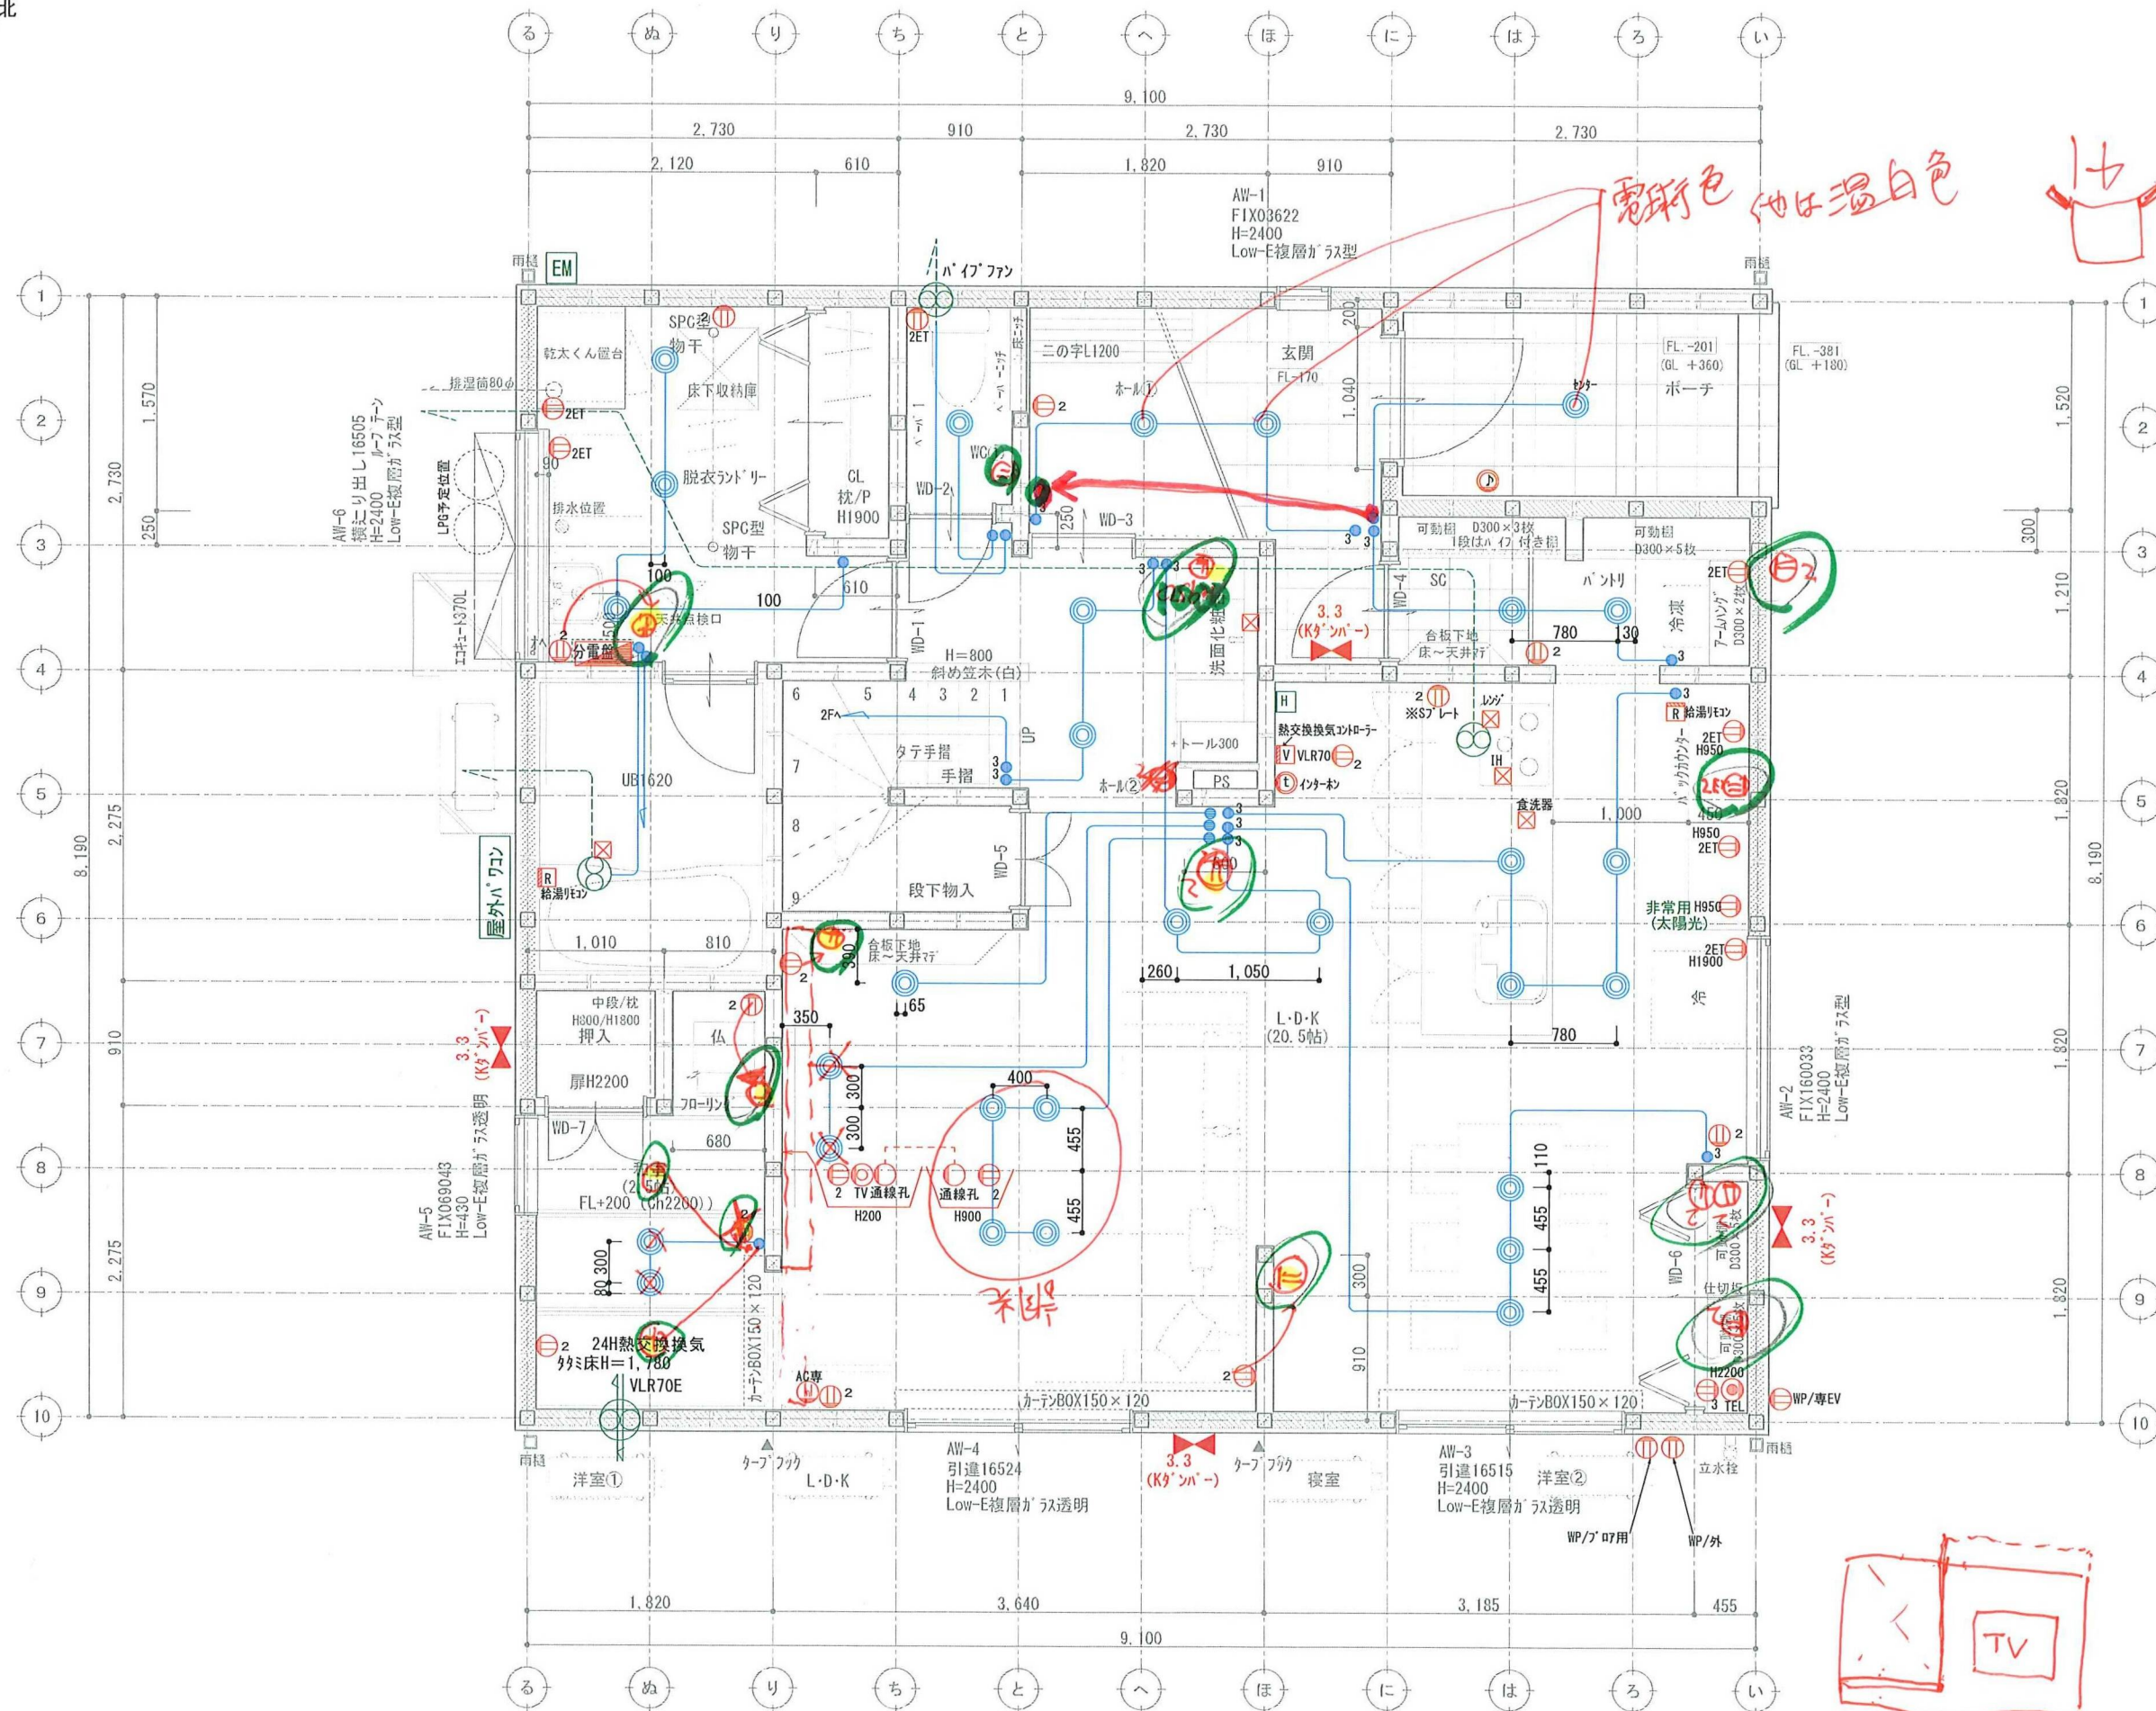

壁付け 住宅用火災報知器			数量
H	熱感知器	電池式(単独型)	
	熱感知器	露出型	
壁付け 住宅用火災報知器			数量
S	煙感知器	電池式(単独型)	
	煙感知器	露出型	

※ 煙感知器は壁・梁より600mm以上離す
壁に取付ける場合、
天井から150mm以上500mm以内離す
換気扇・エアコン吹出口から1500mm以上離す
※ 全室LED照明とする。
※ 標準天井高さ2,400

* 凡例

☒ 管柱 (105×105)

◀▶ Kダクト (3.30倍 FRM-0641)

△ 片筋違い (2.00倍 45×90)
(例 左:柱脚 右:柱頭)

◻ たすき掛筋違い (4.00倍 45×90)

構造用合板 (2.50倍)
(t=9 ダイヤ付)

◻ 床点検口

◻ 天井点検口

⊕ 換気扇

⊕ 熱交換換気扇VLR-70

アドバンスシリーズ =スマートデザイン=			スマートデザイン (外部)
凡例	1	コンセント 1ヶ所	
	2	コンセント 2ヶ所	
	3	コンセント 3ヶ所	
	1ET	コンセント1ヶ所接地ターミナル付	
	2ET	コンセント2ヶ所接地ターミナル付	
	WP	コンセント 防水型	
		エアコンコンセント	
		200V用コンセント	
	WP	防雨入換プレート	
		スイッチ	
	3	3路スイッチ	
	4	4路スイッチ	
	⊕	直結電線	
	TV	テレビ取出口	
	TEL	電話取出口 (テレホンガイド)	
	LAN	LAN取出口 (テレホンガイド)	
	⊕	壁照明	
	リモコン	リモコン (給湯関係・ルフロ)	
	メーター	メーター	
	分電盤	分電盤	
	チャイム	チャイム	

※ACコンセント天井付け
※TVアンテナ工事
※スイッチはFL+1100、コンセントはFL+200

訂正

浜岡一級総合設計事務所
一級建築士事務所 静岡県知事登録第 (10)2441号
一級建築士 大臣登録第 365879号 西原利昌

PG HOUSE
ピージーハウス

株式会社 LIFEFUND InDesign office 一級建築士事務所
事務所登録 (2)第7595号 一級建築士登録 第179770号 鈴木 達男
〒432-8023 静岡県浜松市中央区鶴江3丁目70番23号

年月日
2024.11.08
縮尺
1/50

件名
伊藤友章様邸 新築工事
図名
1階電気配線図

設計	IC	工事	図番
倉田		青島	7-1

真北

センサ SW WTA 1811 wk
272 sw
WTA 57583 wk

壁付け 住宅用火災報知器			数量
H	熱感知器	電池式(単独型)	
	熱感知器	露出型	
壁付け 住宅用火災報知器			数量
S	煙感知器	電池式(単独型)	
	煙感知器	露出型	


※ 煙感知器は壁・梁より600mm以上離す
壁に取付ける場合、
天井から150mm以上500mm以内離す
換気扇・エアコン吹出口から1500mm以上離す
※ 全室LED照明とする。
※ 標準天井高さ2,400

* 凡例

- ☒ 管柱 (105×105)
- ◀▶ Kダクト (3.30倍 FRM-0641)
- △ 片筋違い (2.00倍 45×90)
(例 左:柱脚 右:柱頭)
- ⊠ たすき掛筋違い (4.00倍 45×90)
- 構造用合板 (2.50倍)
(t=9 3イロ)
- △ 床点検口
- ⊠ 天井点検口
- ⊕ 換気扇
- ⊕ 熱交換換気扇VLR-70

アドバンスシリーズ =コネモワイド=システム スマートデザイン (外部)		
凡例	1	コンセント 1ヶ口
2	コンセント 2ヶ口	
3	コンセント 3ヶ口	
1ET	コンセント1ヶ口接地ターミナル付	
2ET	コンセント2ヶ口接地ターミナル付	
WP	コンセント 防水型	
WP	エアコンコンセント	
WP	200V用コンセント	
WP	防雨入換プレート	
3	スイッチ	
4	3路スイッチ	
4	4路スイッチ	
⊕	直結電線	
TV	テレビ取出口	
TEL	電話取出口 (テレホンガイド)	
LAN	LAN取出口 (テレホンガイド)	
照明	照明 (給湯関係・ルフロ)	
リモコン	リモコン (給湯関係・ルフロ)	
メーター	メーター	
分電盤	分電盤	
チャイム	チャイム	

※ACコンセント天井付け
※TVアンテナ工事
※スイッチはFL+1100、コンセントはFL+200

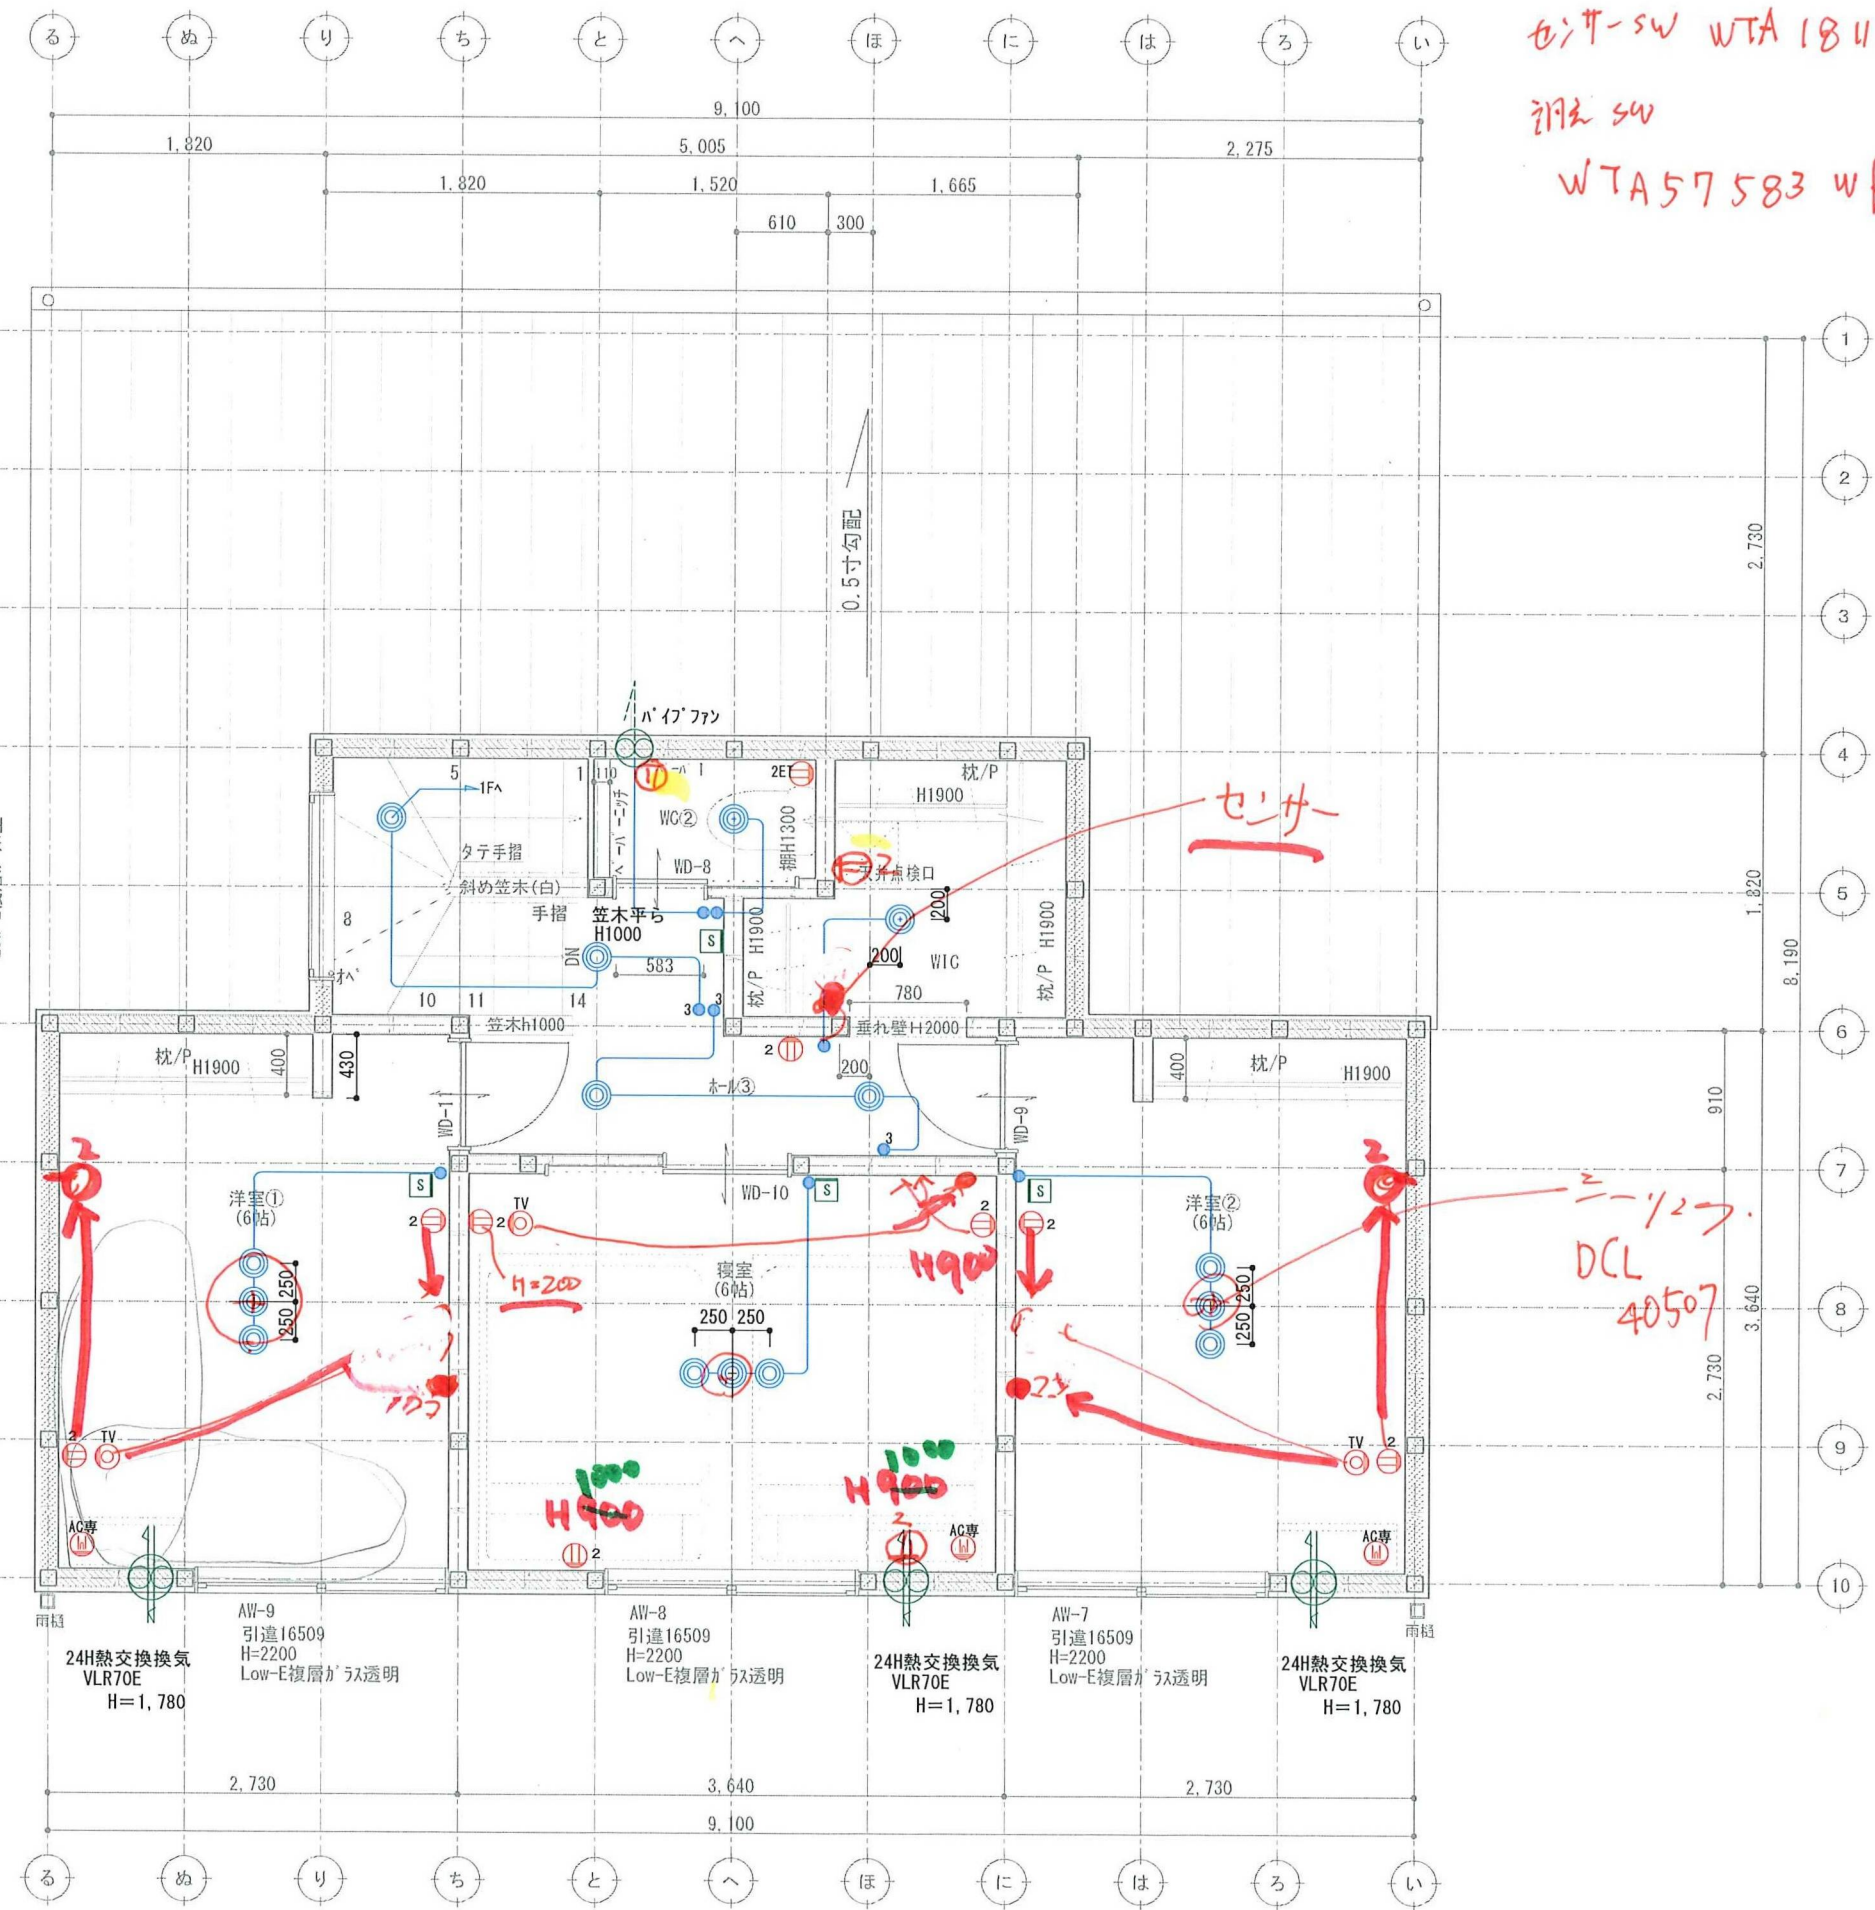

訂正

浜岡 一級総合設計事務所
一級建築士事務所 静岡県知事登録第 (10)2441 号
一級建築士 大臣登録第 365879 号 西原利晶




株式会社 LIFEFUND InDesign office 一級建築士事務所
事務所登録 (2)第7595号 一級建築士登録 第179770号 鈴木 達男
〒432-8023 静岡県浜松市中央区鶴江3丁目70番23号


年月日
2024.11.08
縮尺
1/50

件名
伊藤友章様邸 新築工事
図名
2階電気配線図

設計	IC	工事	図番
倉田		青島	7-2

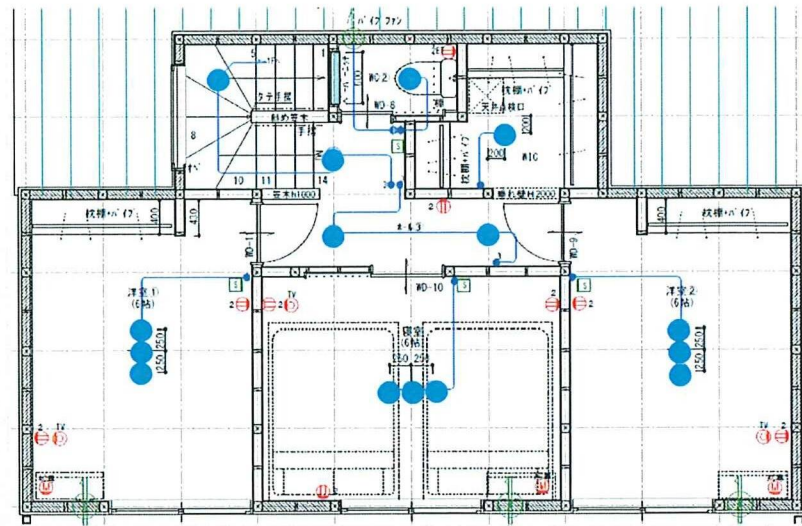

2階

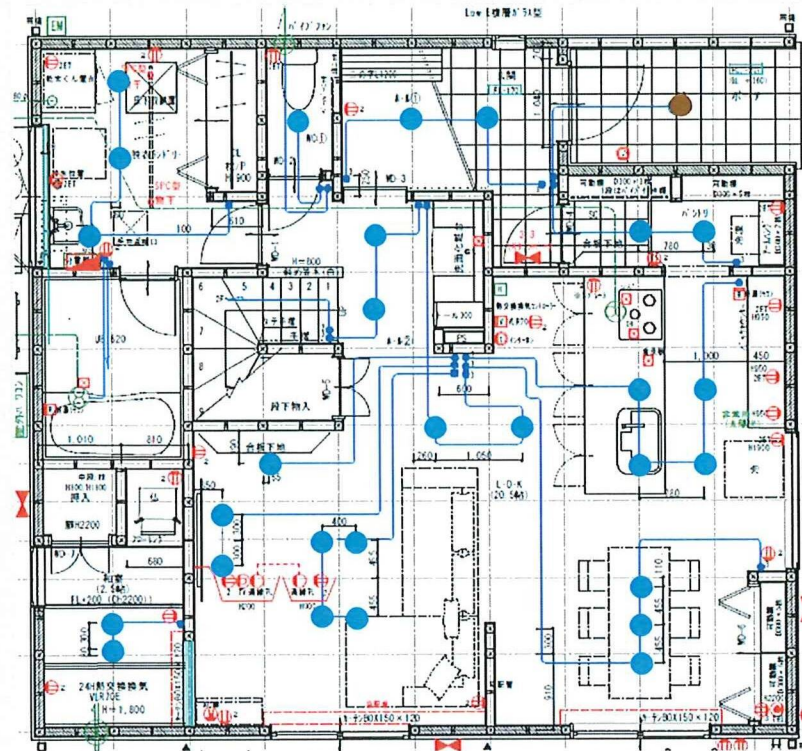


1階

★オプション

内部：アドバンス(Panasonic)




ドアホン：VL-SZ30KL
(Panasonic)

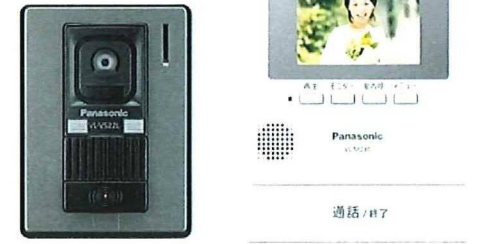


外部：スマートデザインシリーズ (Panasonic)

表情豊かな住まいをつくり出すスマートデザインシリーズ。

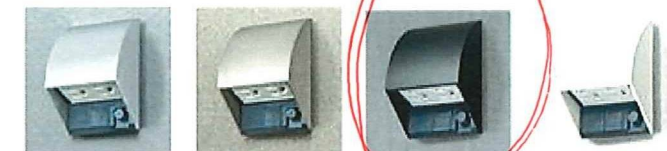


外壁色に合わせ。

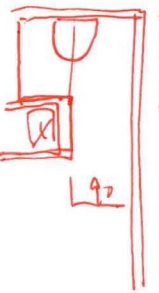

ポーチ灯

● × 1

DDL-4496YB

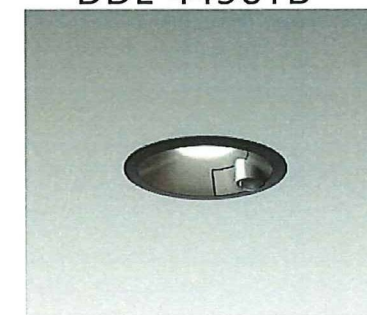

高気密Se形 | 人感センサー | 連動マルチタイプ

DDL-4496 YB

電球色 / 2700K・Ra83

定格光束 消費電力 省エネルギー削減率
425lm 7.7W 55.1lm/W

¥18,800-(税抜) (LED内蔵)

- LED LED 7.7W 白熱灯60W相当
- アルミダイカスト 黒塗装
- アクリル 乳白(マット)
- 径φ111 埋込穴φ100 埋込深80mm 0.5kg
- 14VA
- 点灯照度調節機能付(暗・明・切)
- 点灯保持時間(1分)
- 拡散パネル付
- AC100V
- 光源寿命50,000時間
- 取付可能天井厚5~25mm
- 調光器併用不可


【連動器具について】
LED調光タイプ60VAまで
LED非調光タイプ不可 蛍光灯不可
白熱灯60Wまで

- 強制ON
- 非調光
- ソフトスタート
- 60°
- フェードアウト
- 0.1m
- 遮光型
- 100
- 80
- LED交換不可
- 防雨形
- 温度保護機能付

基本照明ダウンライト

● × 43 (23+15)

DDL6102YW

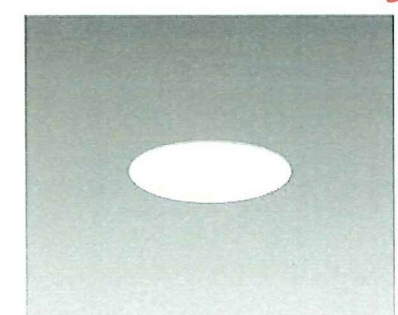

COBタイプ | 高気密Se形

DDL-6102 YW

電球色 / 2700K・Ra83

定格光束 消費電力 省エネルギー削減率
440lm 4.6W 95.6lm/W

¥3,600-(税抜) (LED内蔵)

- LED LED 4.6W 白熱灯60W相当
- 鋼板 白塗装
- アクリル 乳白(マット)
- 径φ116 埋込穴φ100 埋込深70mm 0.3kg
- 8VA
- 拡散パネル付
- AC100V
- 光源寿命60,000時間
- 取付可能天井厚5~25mm
- 調光器併用不可

- LED交換不可
- 非調光
- 防雨形
- 60°
- 温度保護機能付
- 0.1m
- 遮光型
- 100
- 70
- LED交換不可
- 防雨形
- 温度保護機能付

選白

2024.11.08.