

■ 仕 様		■ HEAT20 G1
断熱工事	■ 床:カネライトフォーム t65 ■ 土間床等の外周:スタイロフォームAT t25 ■ 壁:アクアフォームLITE吹付 t85 ■ 天井:アクファフォームLITE吹付 t170	
床下換気	■ 基礎パッキン JOTO (玄関・UB周り:気密基礎パッキン)	
防虫防蟻	■ 土壌処理・木部 ガントナーMC	

■ 外 部 仕 上 表			■ 22条地域
部位		仕上・仕様・メーカー	色番・品番
屋根		■ ガルバリウム鋼板(t0.35)UK立平 ニスクカラーPro GH 軒先通気金物 日本住環境株式会社【REV-15】	GHK01 Sブラック
パラペット笠木		■ なし	
破風・鼻隠		■ なし	
雨樋	(軒樋)	■ Panasonic サーフেসケアFS-I型	ブラック
	(縦樋)	■ Panasonic S30角樋	ブラック
軒天	屋根軒	■ なし	
	ポーチ軒	■ 神島化学 t= 6mm 軒天ボード エンボス	Wチャコールブラック
	バルコニー軒	■ なし	
オーバーハング水切り		■ ガルバリウム鋼板 ※外壁合わせ JOTO:HF-A3550	ブラック
外壁	通気金物(15mm)	■メイン ニチハ エモンエクセラード16 Vシリーズ リーガストーン調V	ランダムMGブラック
	※下地面材:タイガーEXハイパー	■アクセントA なし	
	防火認定 PC030BE-4028	■アクセントB なし	
玄関ポーチ		■ 床 玄関タイルに同じ	-
基礎		■ 立上り巾木: モルタル刷毛引き	-
基礎水切り金物		■ JOTO鋼板製 防鼠材付き水切り JOTO:WMF-N35	ブラック
バルコニー	床・内壁	■ なし	-
	笠木	■ なし	
外部建具		■ LIXIL EW(アルゴンガス高遮熱仕様LowE複層ガラス グリーン) ・SD、TSで記載がないものは、オペレーターハンドルとする ・オペレーター付サッシは固定網戸とする ・グレモンハンドル式サッシの選択箇所は可動網戸とする	外観 ブラック 内観 ホワイト ※樹脂パッキン・網戸付
シャッター		■ なし	
玄関扉		■ LIXIL ジエスタ2 K2仕様 LIXILファミロック タグキー×3 (電池式)	ドア型: M17 型 ドア色: カームブラック ハンドル: S型ハンドル 色 ブラック
外部物干し金物		■	
換気フード		■ 局所換気扇(トイレ 浴室 キッチンフード) 防火ダンパー無 ■ ダクトレス熱交換換気システム (日本スティーベル株式会社) VLR-70E 防火ダンパー無	外気フード: ブラック 外気フード: B ブラック

■ 構 造 概 要			
基礎	■ RCベタ基礎コンクリート		
通し柱・管柱	■ 構造用集成材 105×105		間柱 ■ 集成材
土台	■ 桧 105×105	大引き ■ 桧 90*90	筋交い ■ 構造用製材 火打梁 ■ 鋼製火打(当社基準により米松あり)
桁・梁	■ 構造用製材及び集成材		制震装置 ■ Kダンパー (株)アイ・エム・エー

■ 設 備 装 着 品				
住宅設備	部位	メーカー	商品名 ※ 詳細は見積り、プレゼン参照	見積りNo. (日付)
	キッチン	LIXIL	■ ES ペニンシュラ型 スライドストッカー (扉 3色の内未決)	見積り番号 : A24105290035-004-3 (日付) 2024.10.11
	バックカウンタ ※オプション	LIXIL	■ ES L1800(W900スライドストッカー+マルチスペース) 引き出しTレール仕様 吊戸棚H500(フレーションorライトグレン)	見積り番号 : A24105290035-004-(5,7) (日付) 2024.10.11
	浴室	LIXIL	■ AX1620 洗い場広タイプ ドア仕様	見積り番号 : A24105290035-004-1 (日付) 2024.10.11
	1Fトイレ	LIXIL	■ ベーシアシャワートイレ 白 ● タオル掛け: KF-AA70D(リング) タンク手洗 無し ● 紙巻き器: CF-AA22H /WA	見積り番号 : A24105290035-004-9 (日付) 2024.10.11
	2Fトイレ	LIXIL	■ ベーシアシャワートイレ 白 ● タオル掛け: KF-AA70D(リング) タンク手洗 有り ● 紙巻き器: CF-AA22H /WA	見積り番号 : A24105290035-004-10 (日付) 2024.10.11
	洗面台	LIXIL	■ EV W900(D500タイプ) 扉:グロスホワイト [引出しタイプ シングルハンドシャワー スタンダードLED三面鏡 その他 トールキャビネット300 ● タオル掛け: KF-AA71D(バー)	見積り番号 : A24105290035-004-8 (日付) 2024.10.11
	スロップシンク	LIXIL	■ S-17/BW1 シングルバー混合水栓SF-WM435SY(170)	A24105290035-004-11 2024.10.11
給排水設備	給湯器		■ エコキュート370L Panasonic NSシリーズ スタンダードモデル 追い焚きフルオート	
	排水		■ 合併浄化槽 5人槽 ポンプアップ無	
	外水栓		■ 1 カ所 (平面図参照) ■ 外部立栓柱: PVC製 水栓柱12型【前澤化成工業】	
	外部ガーデンパン		■ 無し	
	その他		■ 洗濯機用単水栓: 緊急止水弁付 ■ 洗濯機用排水: トラップ金物(標準)	
ガス配管設備			■ あり(LPG) (配置図・平面図参照 ※乾太くん用	
電気設備	インターホン		■ パナソニック VL-SZ30KL	
	TVアンテナ		■ UHF + BS・110度CS／CSアンテナ [2K・4K・8K対応] ■ブラック ※電波状況によりホワイトになる可能性あり	
	エアコン		■ 設置場所:	
	ソーラー		■ あり(Qセルズ) 12 枚 5.28 KW Re.RISE-G3 440 (1722×1134×30)	
	※標準搭載		※メーカーのモデルチェンジ等で後継品に変更される可能性あり ■ 屋外パワコン 西面	
その他				


	浜 岡 一 級 総 合 設 計 事 務 所 一級建築士事務所 静岡県知事登録第 (10)2441 号 一級建築士 大臣登録第 365879 号 西原利昌	 株式会社 LIFEFUND InDesign office 一級建築士事務所 事務所登録 (2)第7595号 一級建築士登録 第179770号 鈴木 達男 〒432-8023 静岡県浜松市中央区鴨江3丁目70番23号	年 月 日	2024.11.8	件名	伊藤友章 様邸 新築工事		設計	IC	工務	図 番
			縮尺		図面	仕上表 1		倉田		青島	1-1


内 部 仕 上 表 （壁下地:石膏ボード12.5mm/天井下地:9.5mm）※脱衣室:床合板特類 下地									
階		床	巾木	壁	品番	廻 縁	天 井	品番	特記事項
1F	ポーチ	LIXILパセオ300/PSO-FIO 4							
	玄関	LIXILパセオ300/PSO-FIO 4	ライン巾木(W)	ビニルクロス	SLP-251	突付	ビニルクロス	SLP-251	
	SC	LIXILパセオ300/PSO-FIO 4	ライン巾木(W)	ビニルクロス	SLP-251	突付	ビニルクロス	SLP-251	
	パントリー	イタ銘木フロアースティックt12 ナラ桜3P	ライン巾木(W)	ビニルクロス	SLP-251	突付	ビニルクロス	SLP-251	
	ホール①								
	ホール②/洗面	イタ銘木フロアースティックt12 ナラ桜3P	ライン巾木(W)	ビニルクロス	SLP-251	突付	ビニルクロス	SLP-251	
	WC①	フロアタイルt2.3 サンゲツIS-2071	H40ソフト巾木W97	ビニルクロス	SLP-251	突付	ビニルクロス	SLP-251	ペーパーニッチ/床ニッチ
	脱衣ランドリー	フロアタイルt2.3 サンゲツIS-2071	H40ソフト巾木W97	ビニルクロス	SLP-251	突付	ビニルクロス	SLP-251	SPC型物干 乾太くん台
	ダイニングキッチン	イタ銘木フロアースティックt12 ナラ桜3P	ライン巾木(W)	ビニルクロス	SLP-251	突付	ビニルクロス	SLP-251	
	リビング	イタ銘木フロアースティックt12 ナラ桜3P	ライン巾木(W)	ビニルクロス	SLP-251	突付	ビニルクロス	SLP-251	
	和室	1畳縁ありスタイロ畳 t55	畳寄せ	ビニルクロス	SLP-251	突付	ビニルクロス	SLP-251	畳縁:高田織物 浮No.13
	仏間	イタ銘木フロアースティックt12 ナラ桜3P	雑巾摺	ビニルクロス	SLP-251	突付	ビニルクロス	SLP-251	
2F	ホール③	イタ銘木フロアースティックt12 ナラ桜3P	ライン巾木(W)	ビニルクロス	SLP-251	突付	ビニルクロス	SLP-251	
	洋室①	イタ銘木フロアースティックt12 ナラ桜3P	ライン巾木(W)	ビニルクロス	SLP-251	突付	ビニルクロス	SLP-251	
	洋室②	イタ銘木フロアースティックt12 ナラ桜3P	ライン巾木(W)	ビニルクロス	SLP-251	突付	ビニルクロス	SLP-251	
	洋室③	イタ銘木フロアースティックt12 ナラ桜3P	ライン巾木(W)	ビニルクロス	SLP-251	突付	ビニルクロス	SLP-251	
	WIC	イタ銘木フロアースティックt12 ナラ桜3P	ライン巾木(W)	ビニルクロス	SLP-251	突付	ビニルクロス	SLP-251	
	WC②	フロアタイルt2.3 サンゲツIS-2071	H40ソフト巾木W97	ビニルクロス	SLP-251	突付	ビニルクロス	SLP-251	ペーパーニッチ
物入・収納・CL etc		※接続する部屋と同仕様とする							

上框&付框	■ LIXILラシッサS 付框30×150(全周廻し) 色: クリエペール		
階段	■ LIXIL KA 階段	ササラ:	プレシャスホワイト
KA階段で対応できない場合、オプション	段板: クリエペール	蹴込板:	プレシャスホワイト
ラウンド手摺	ラウンド手摺: プレシャスホワイト	手摺金物	プレシャスホワイト
にてラシッサS階段	上段框: クリエペール	長尺笠木:	LIXIL プレシャスホワイト
窓枠	■ LIXIL スマート10	色	プレシャスホワイト
	※浴室ドア枠 フクビ3方枠 []		
キッチン笠木	■ なし	色	
カウンター	形状		t=
天井点検口	■ 天井アルミ点検口枠 450角 TAN45BW	フクビ化学工業 ミルキーホワイト	
床下収納庫	■ 高気密型床下点検口断熱型 SPF-R6060 城東テクノ	収納付 (脱衣室) ライトグレー(LG)	
トイレ棚	■ 2階トイレ D250	アートランバー棚(シェルホワイト)	
室内物干し金物	■ 川口技研SPC型1セット		
LDK-カウンター	■ なし	色	
下足入	■ LIXILラシッサS	色	リエペール
プッシュタイプ	サイズ: W1200 D400	形状:	二の字型

支給品	■ 無し
備考	

内 部 建 具 表							
LIXIL		建具色：プレシャスホワイト		枠色 ： 扉同色		※その他、下記特記による	
ラフィス		把手 ： スクエアL（シャインニッケル） 丁番 固定枠（156） 外付戸当り ガイドピン床色合せ 引戸のみ上吊W77フモーション					
階	No	室名	形式	枠外W サイズ	デザイン	枠色	特記事項
				枠外H サイズ	建具色	把手	
1	1	脱衣ランドリー	片開き戸	—	RAA	—	明り窓・表示錠
	WD			2400	—	—	
	2	WC①	片開き戸	—	RAA	—	明り窓・表示錠
	WD			2400	—	—	
	3	ホール①	アウトセット片引	—	RAA	—	
	WD			2400	—	—	
	4	SC	片開き戸	—	RAA	—	
	WD			2400	—	—	
	5	階段下収納	観音開	—	RAA	—	
	WD			2400	—	—	
	6	ダイニングCL	折れ戸		RAA		
	WD			2400			
	7	押入	観音開	—	RAA	—	
	WD			2200	—	—	H200mm切詰
	8	WC②	片引き戸	—	RAA	—	明り窓・表示錠
	WD			2400	—	—	
	9	洋室②	片開き戸	—	RAA	—	
	WD			2400	—	—	
	10	寝室	片引き戸	—	RAA	—	
	WD			2400	—	—	
	11	洋室①	片開き戸	2400	RAA	—	
	WD				—	—	

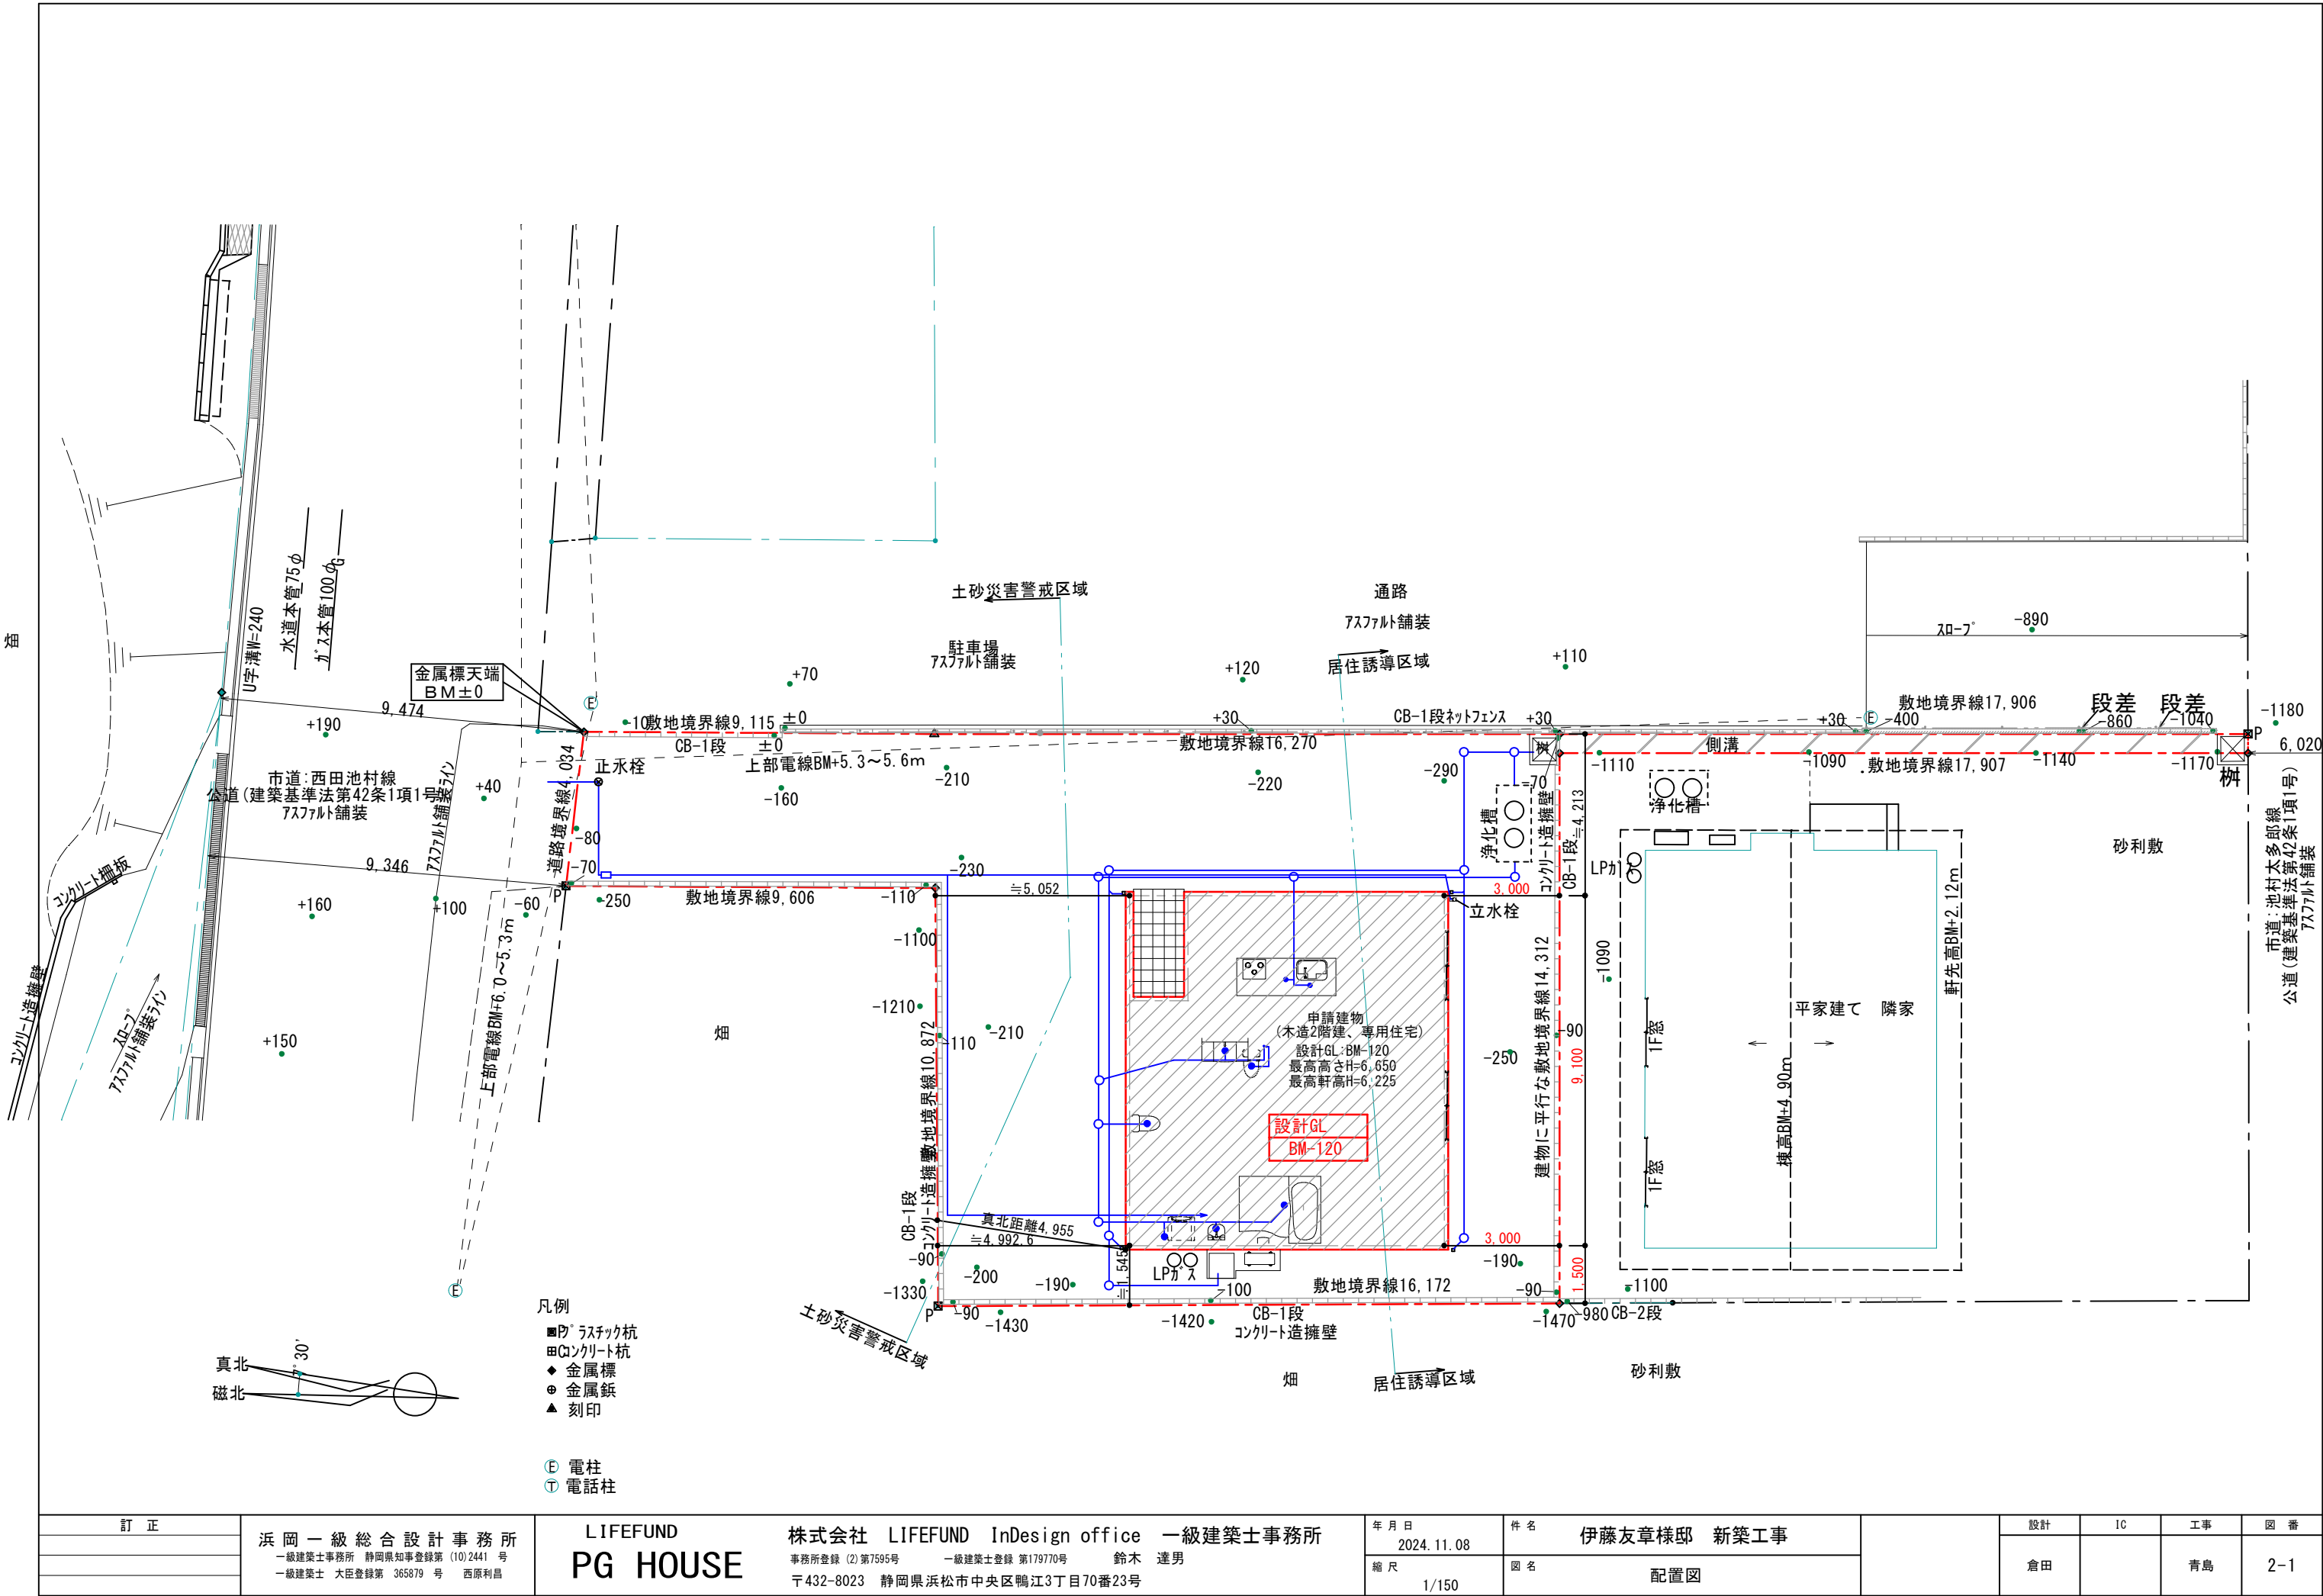

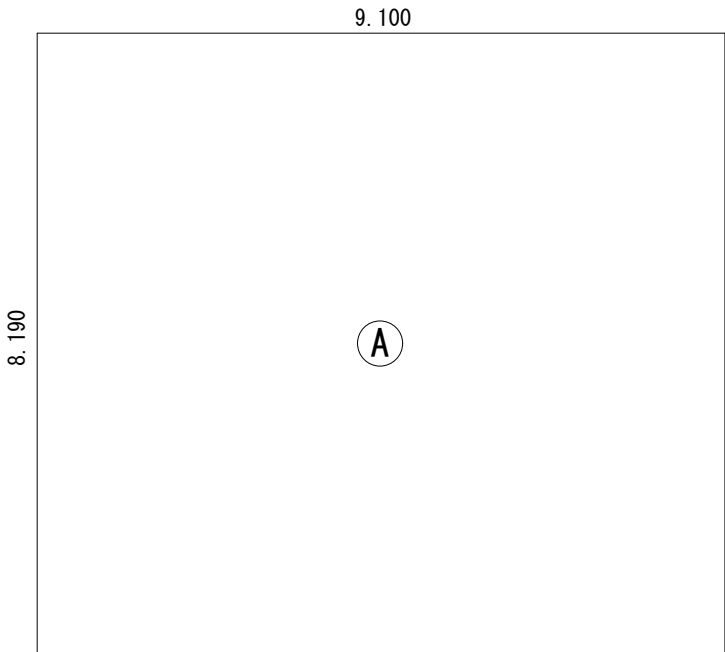


建築面積求積図 S=1/100

建築面積求積表

番号	計算式	(m)	面積 (㎡)
Ⓐ	9.100 × 8.190		74.529
合計			74.529 74.52

(22.5坪)

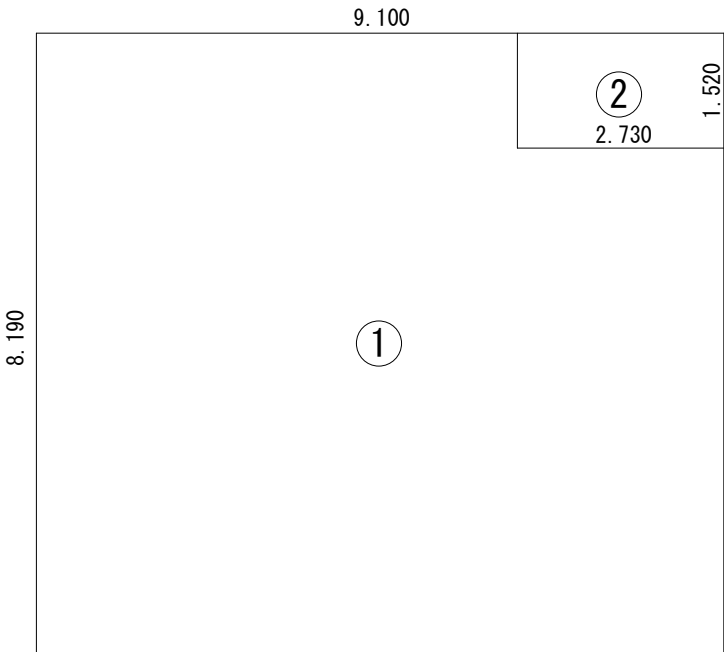


1階床面積図 S=1/100

1階床面積求積表

番号	計算式	(m)	面積 (㎡)
①	9.100 × 8.190		74.529
②	1.520 × 2.730		-4.1496
合計			70.3794 70.37

(21.2坪)

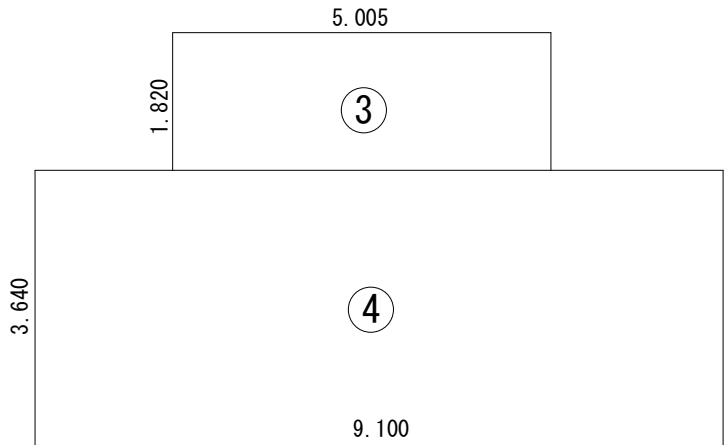

2階床面積図 S=1/100

2階床面積求積表


番号	計算式	(m)	面積 (㎡)
③	5.005 × 1.820		9.1091
④	3.640 × 3.640		33.124
合計			42.2331 42.23


(12.7坪)



延べ床面積表


	番号	(m)	面積 (㎡)
1階床面積	① - ②		70.37
2階床面積	③ + ④		42.23
合計			112.60

(34.0坪)

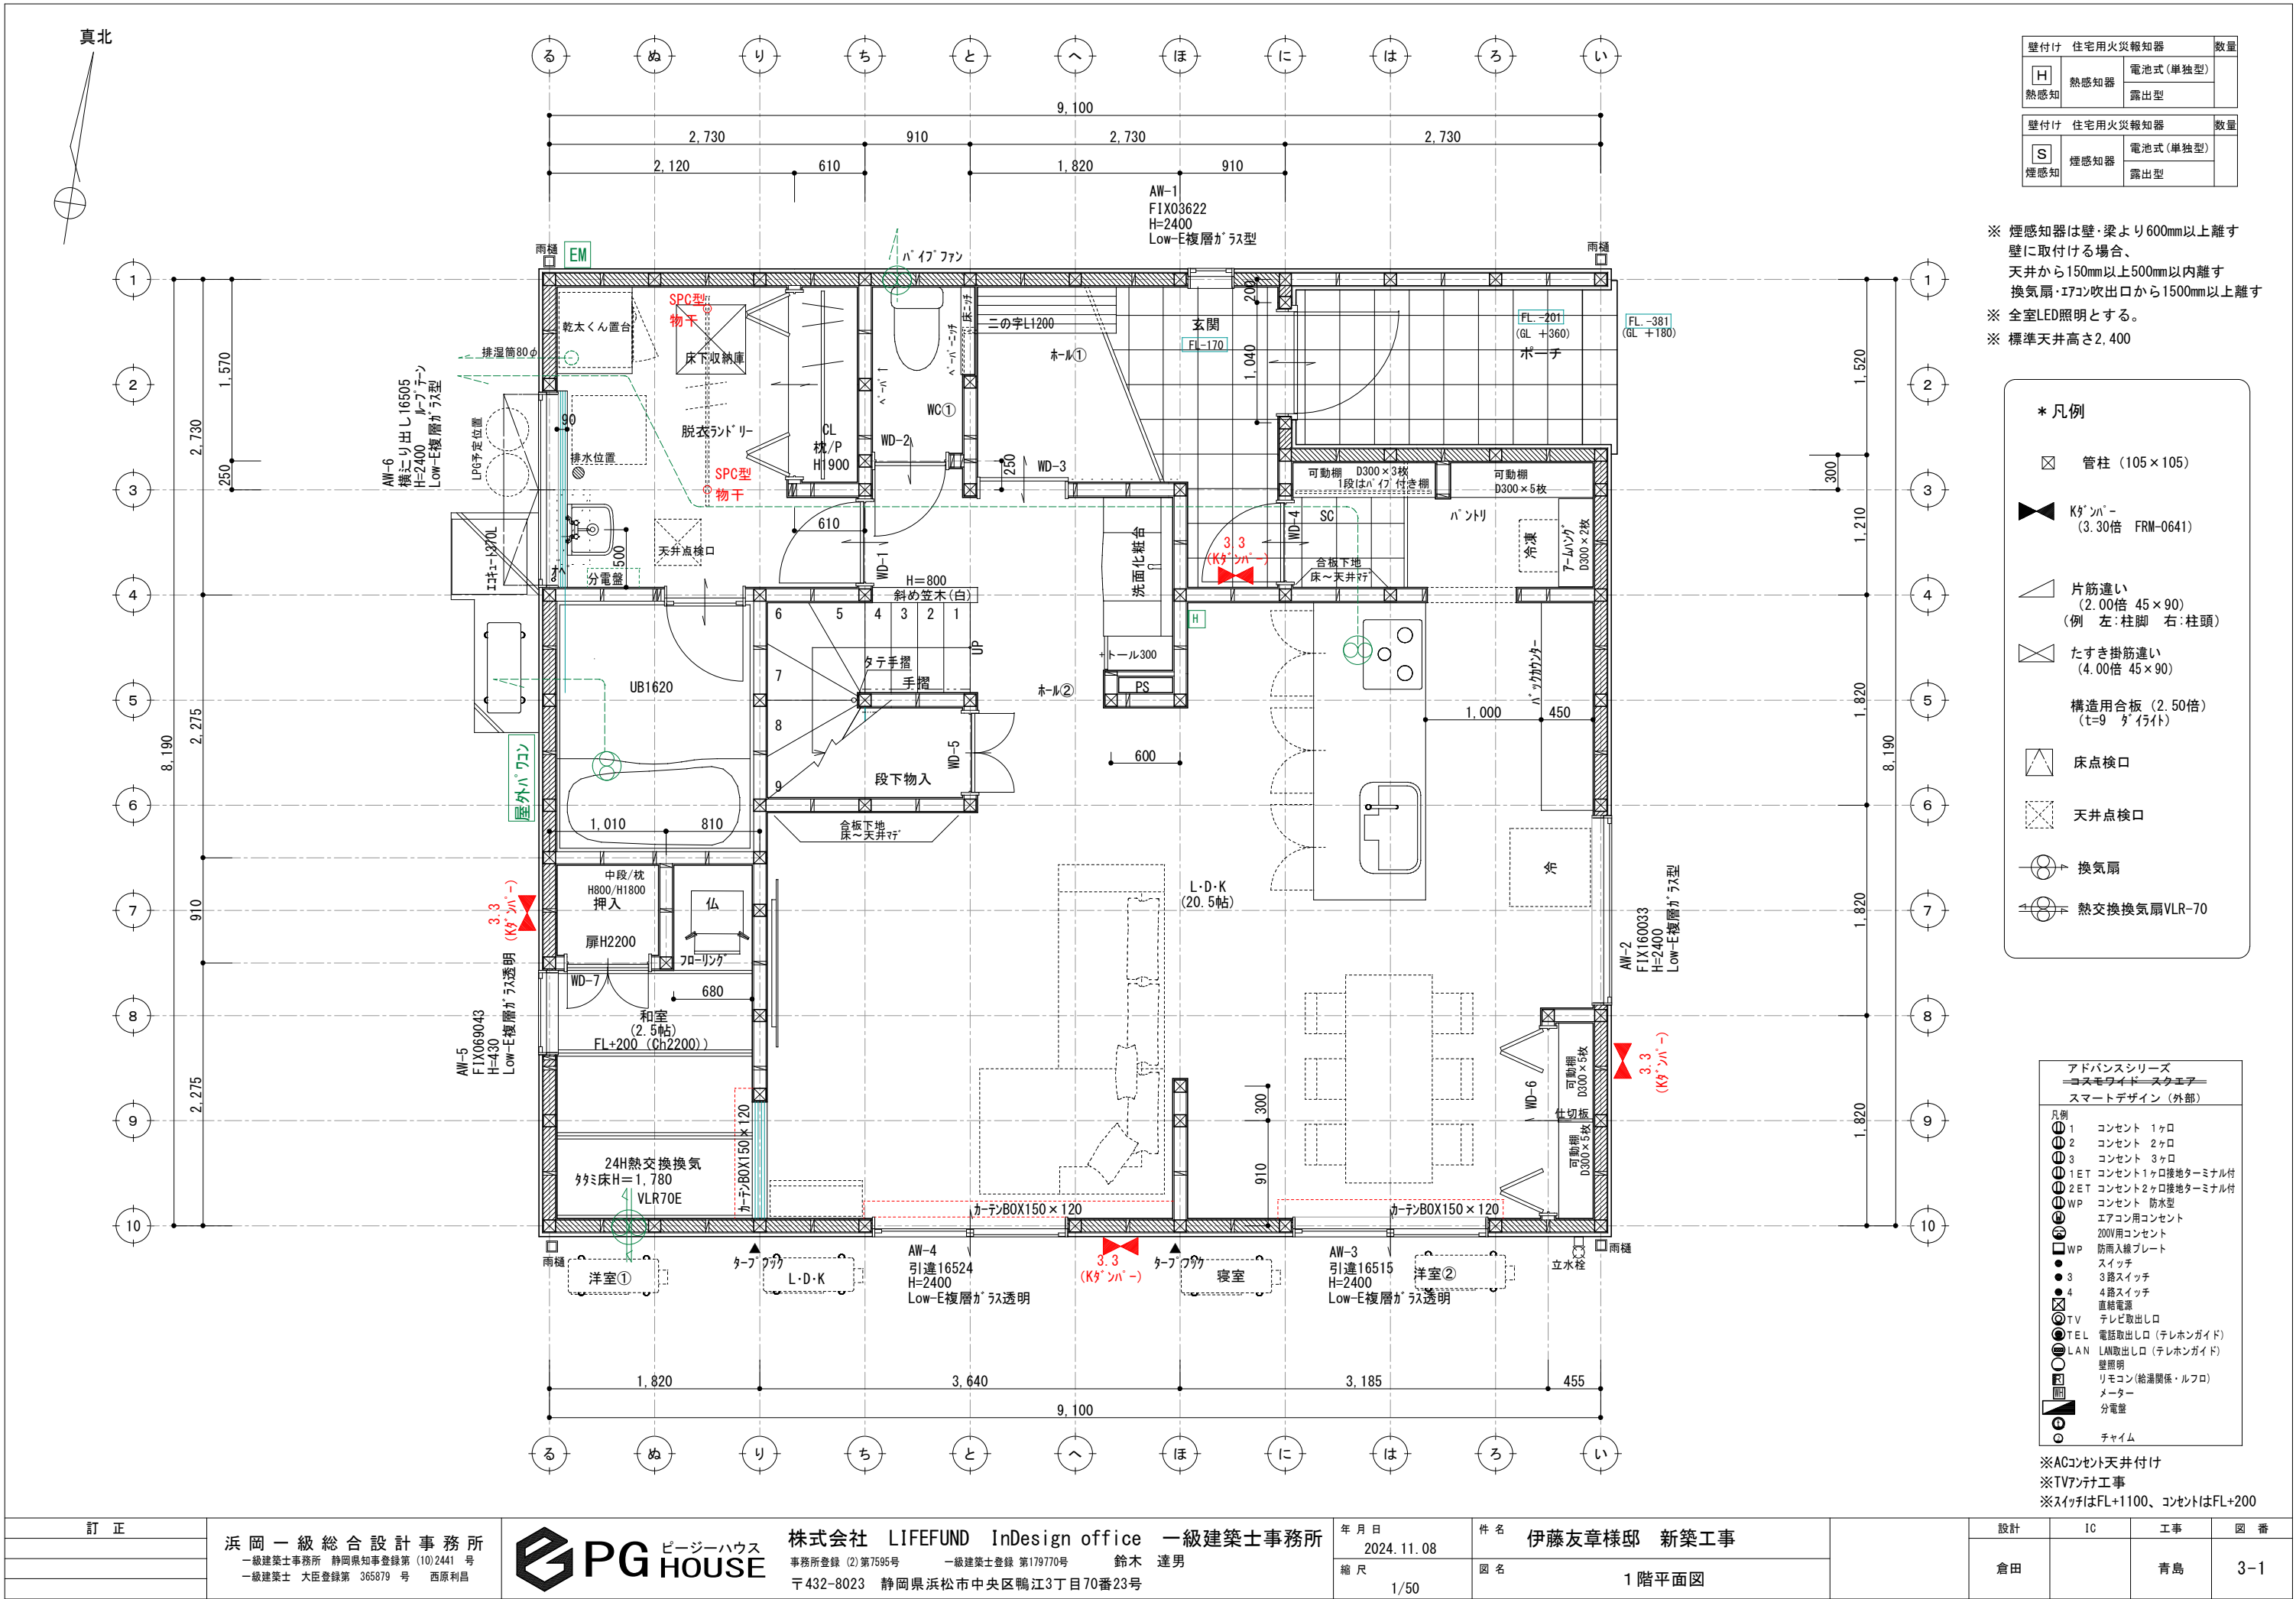


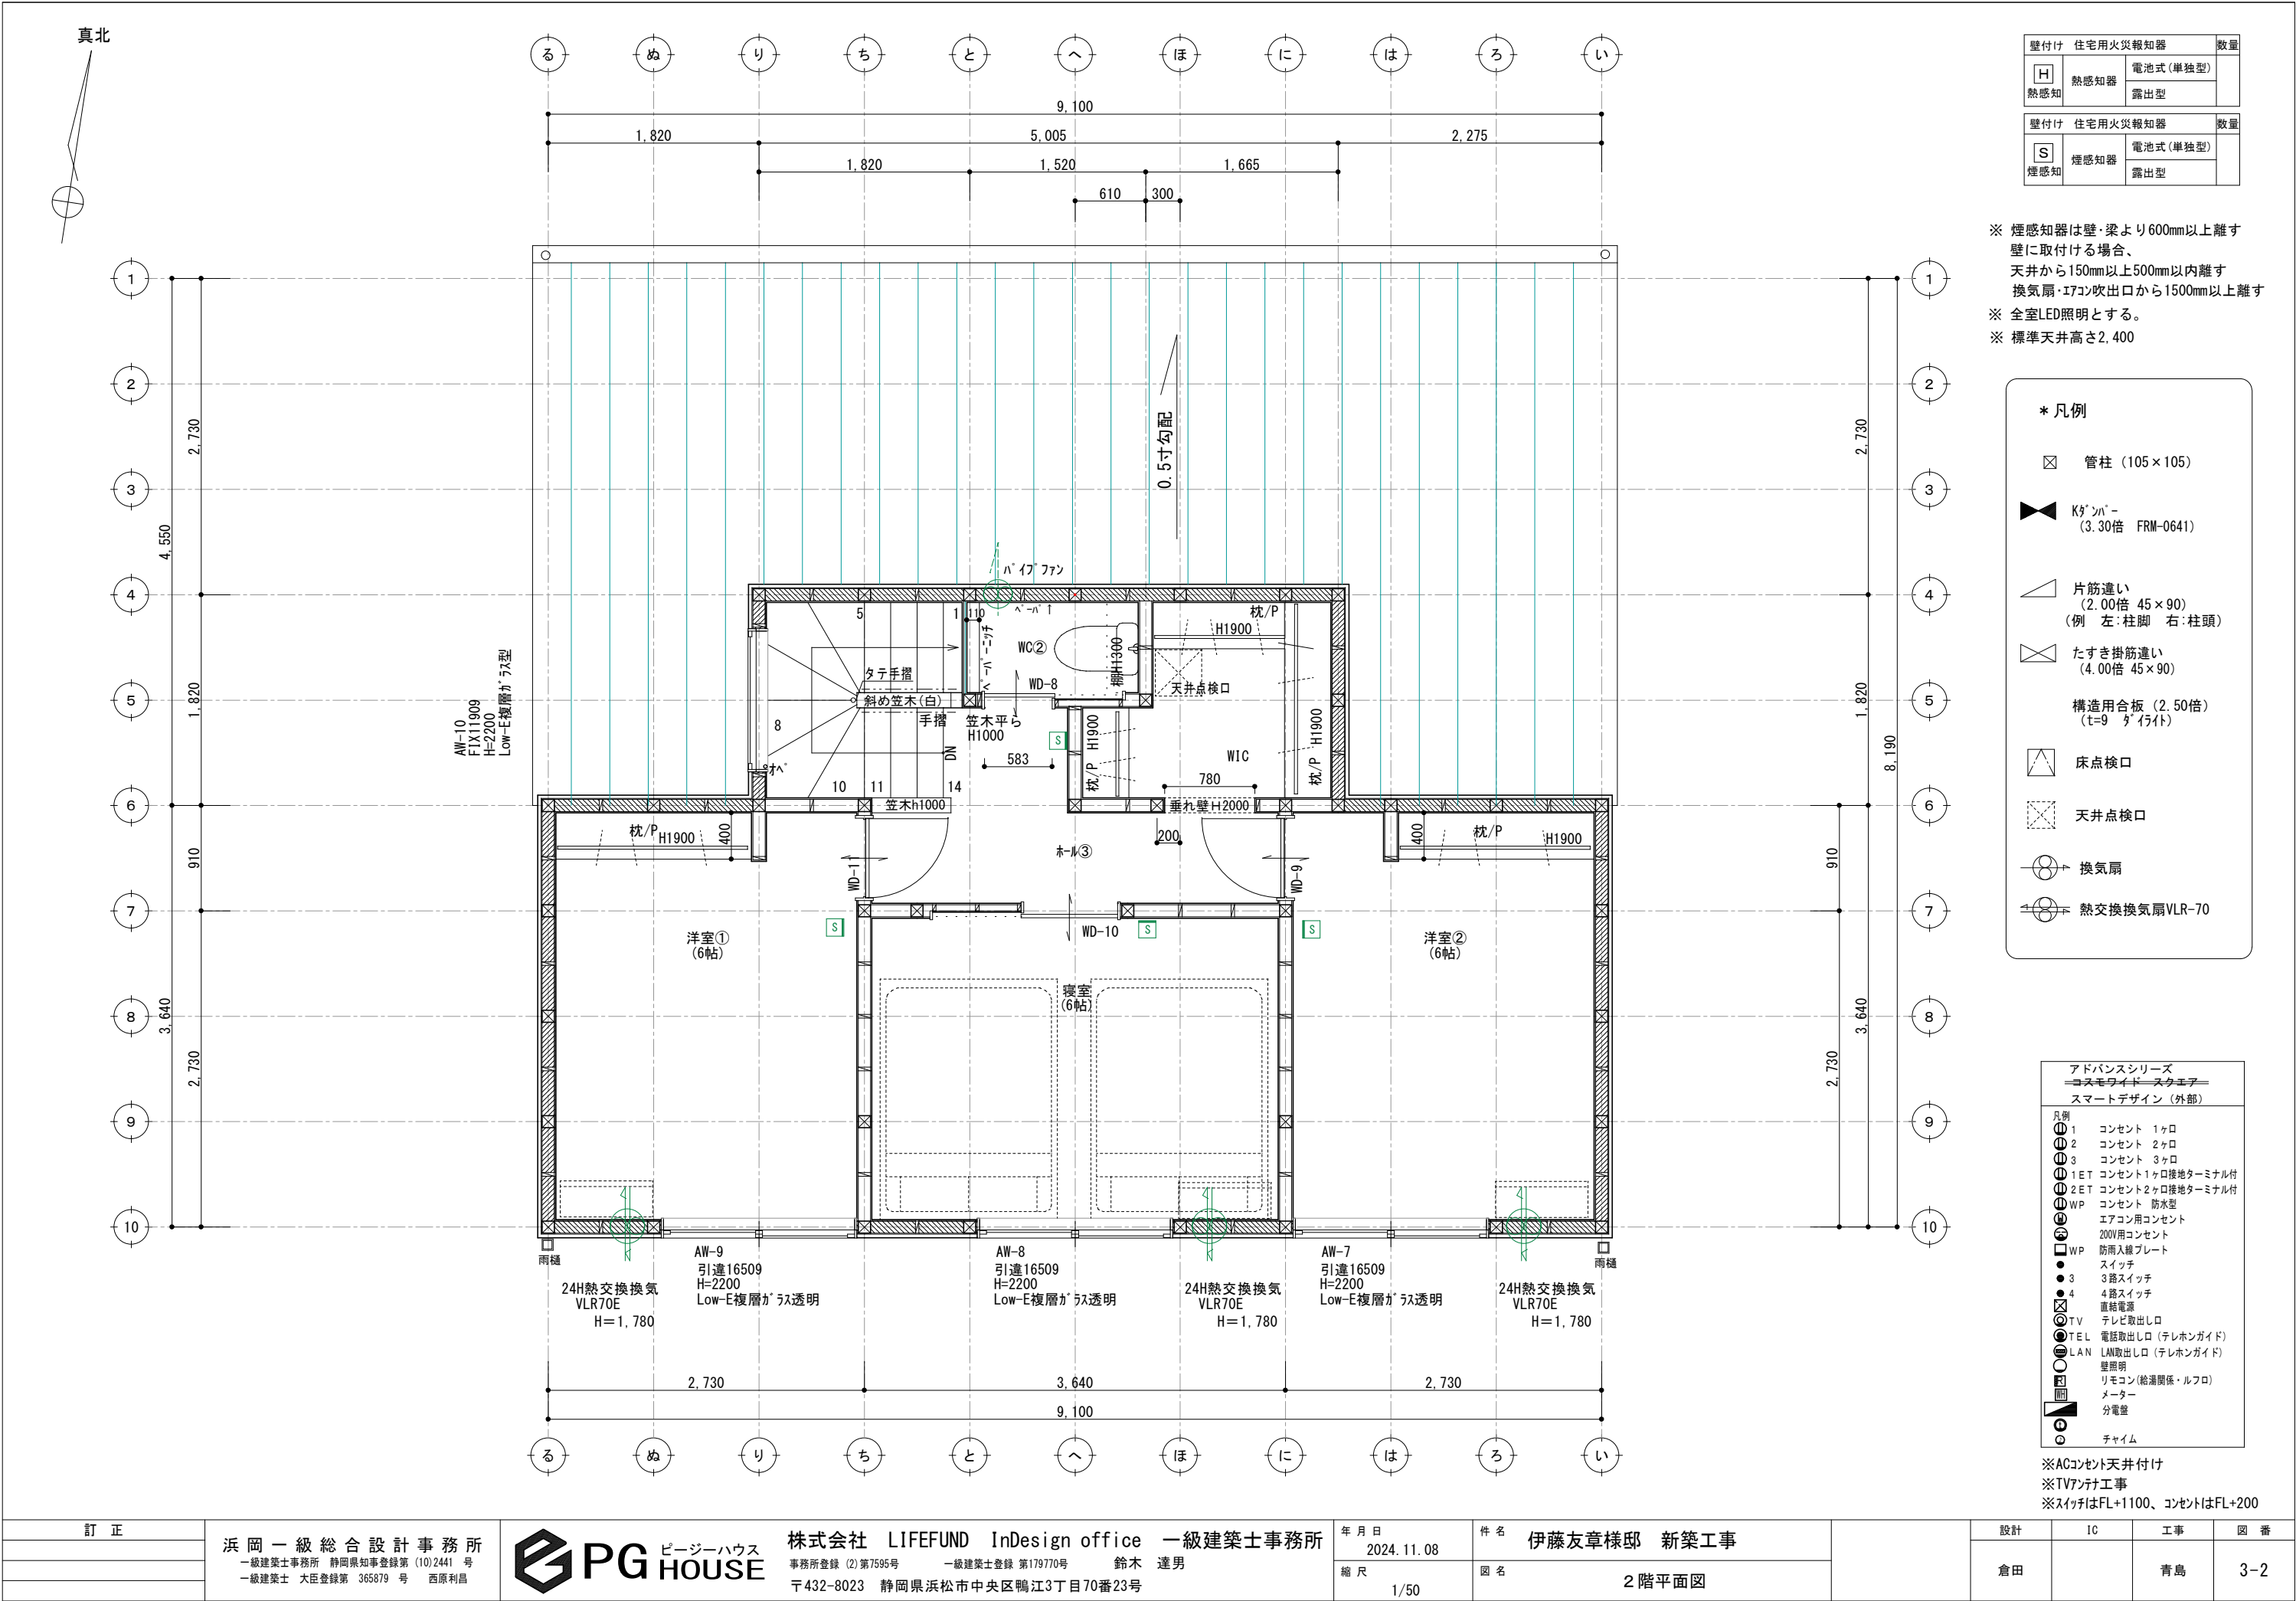

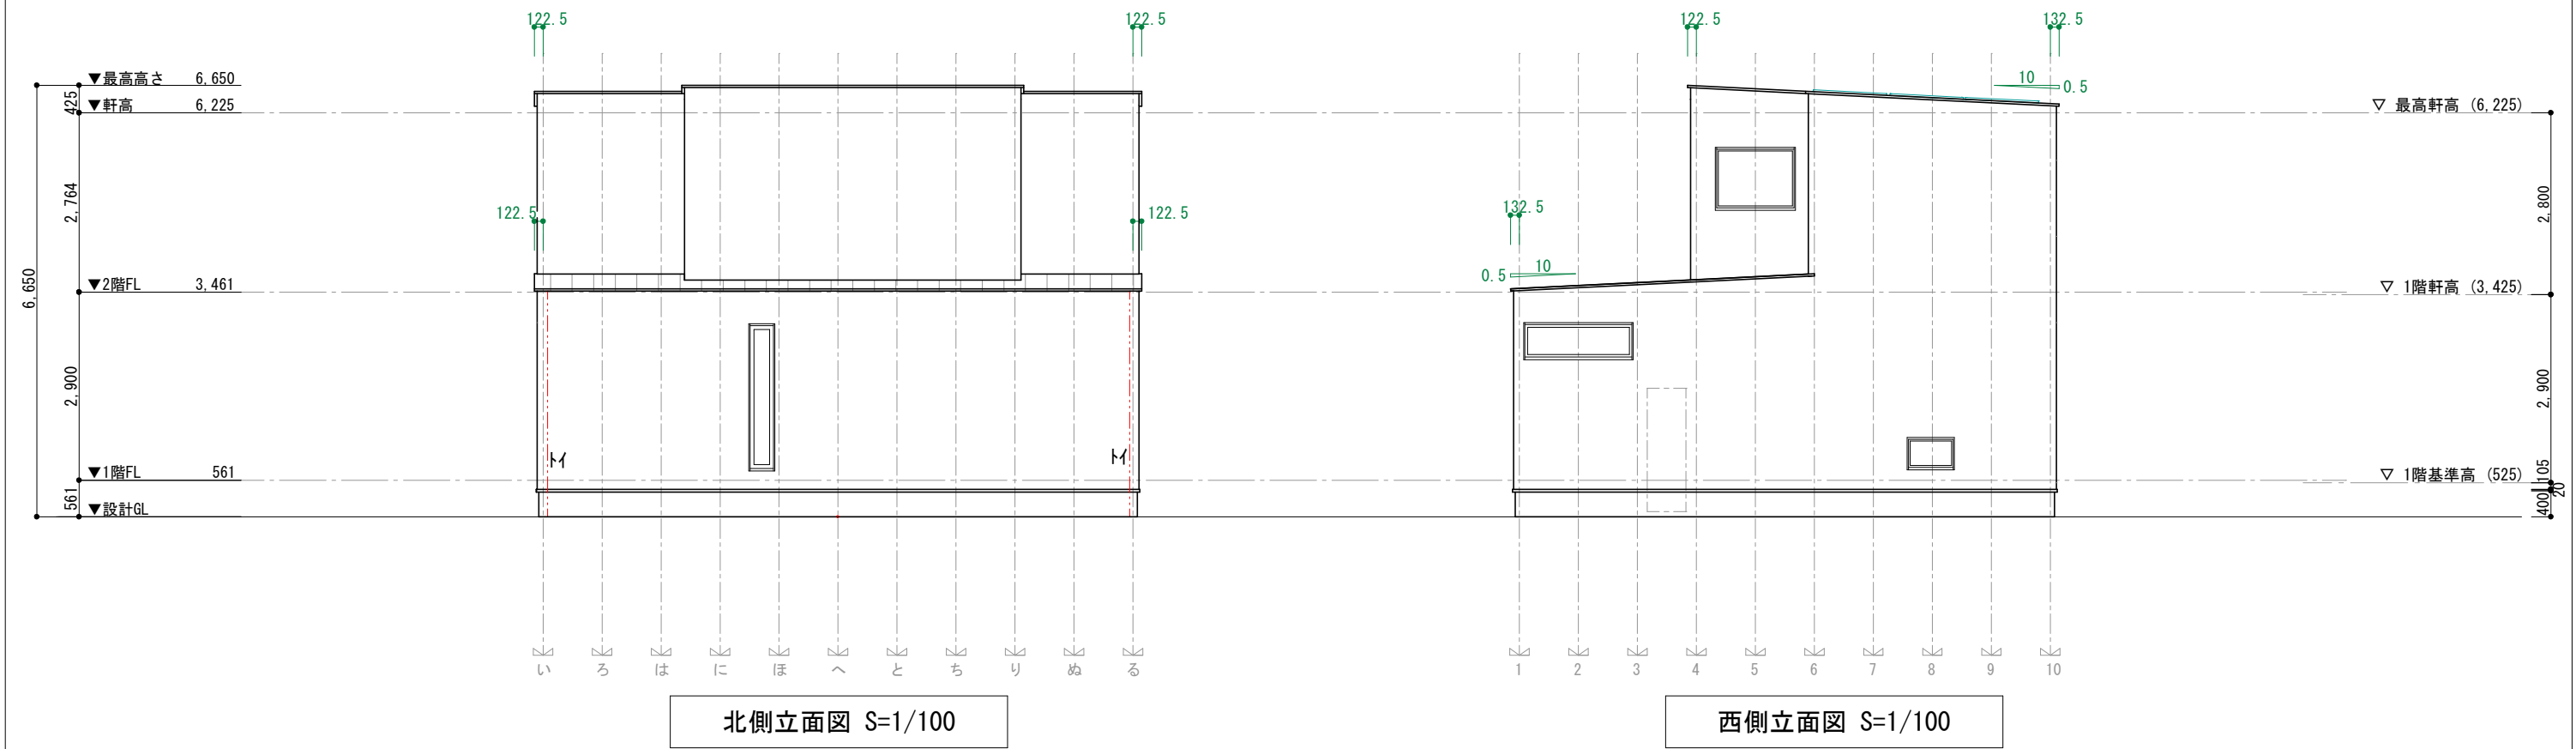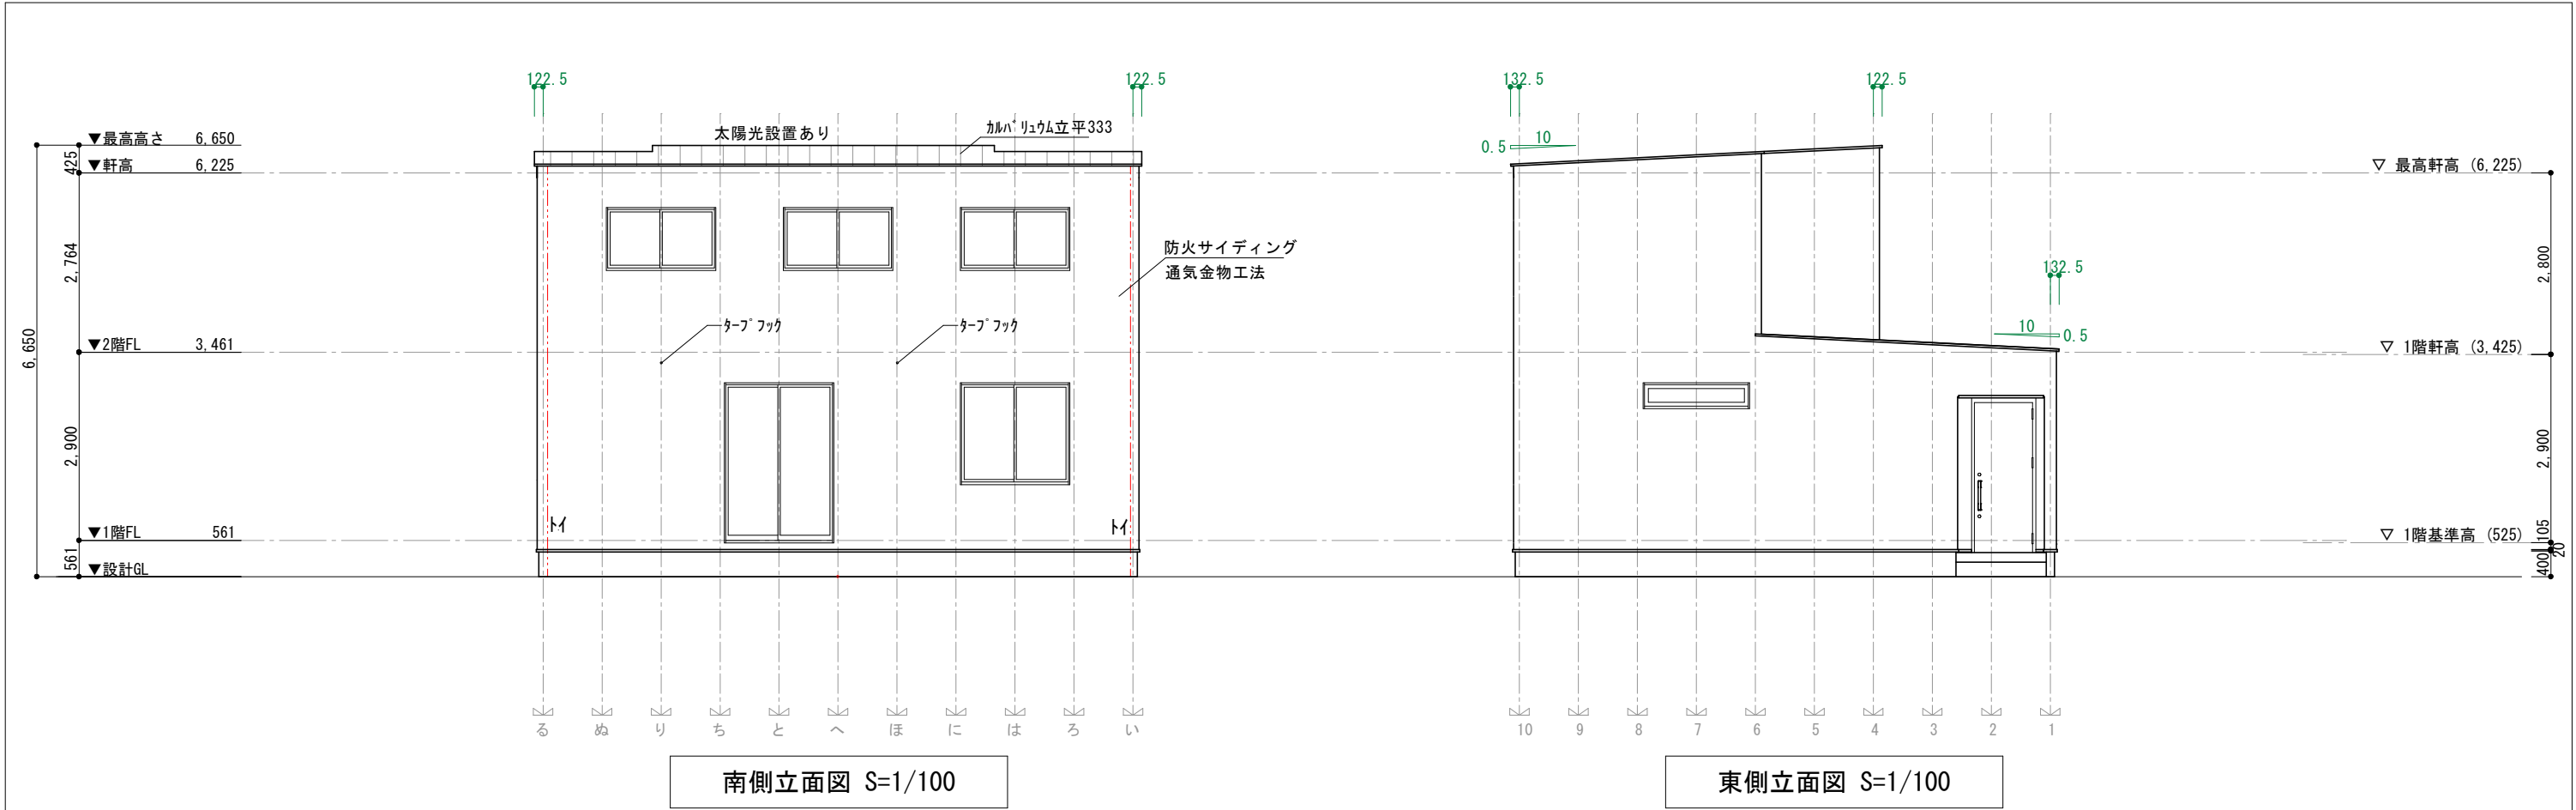


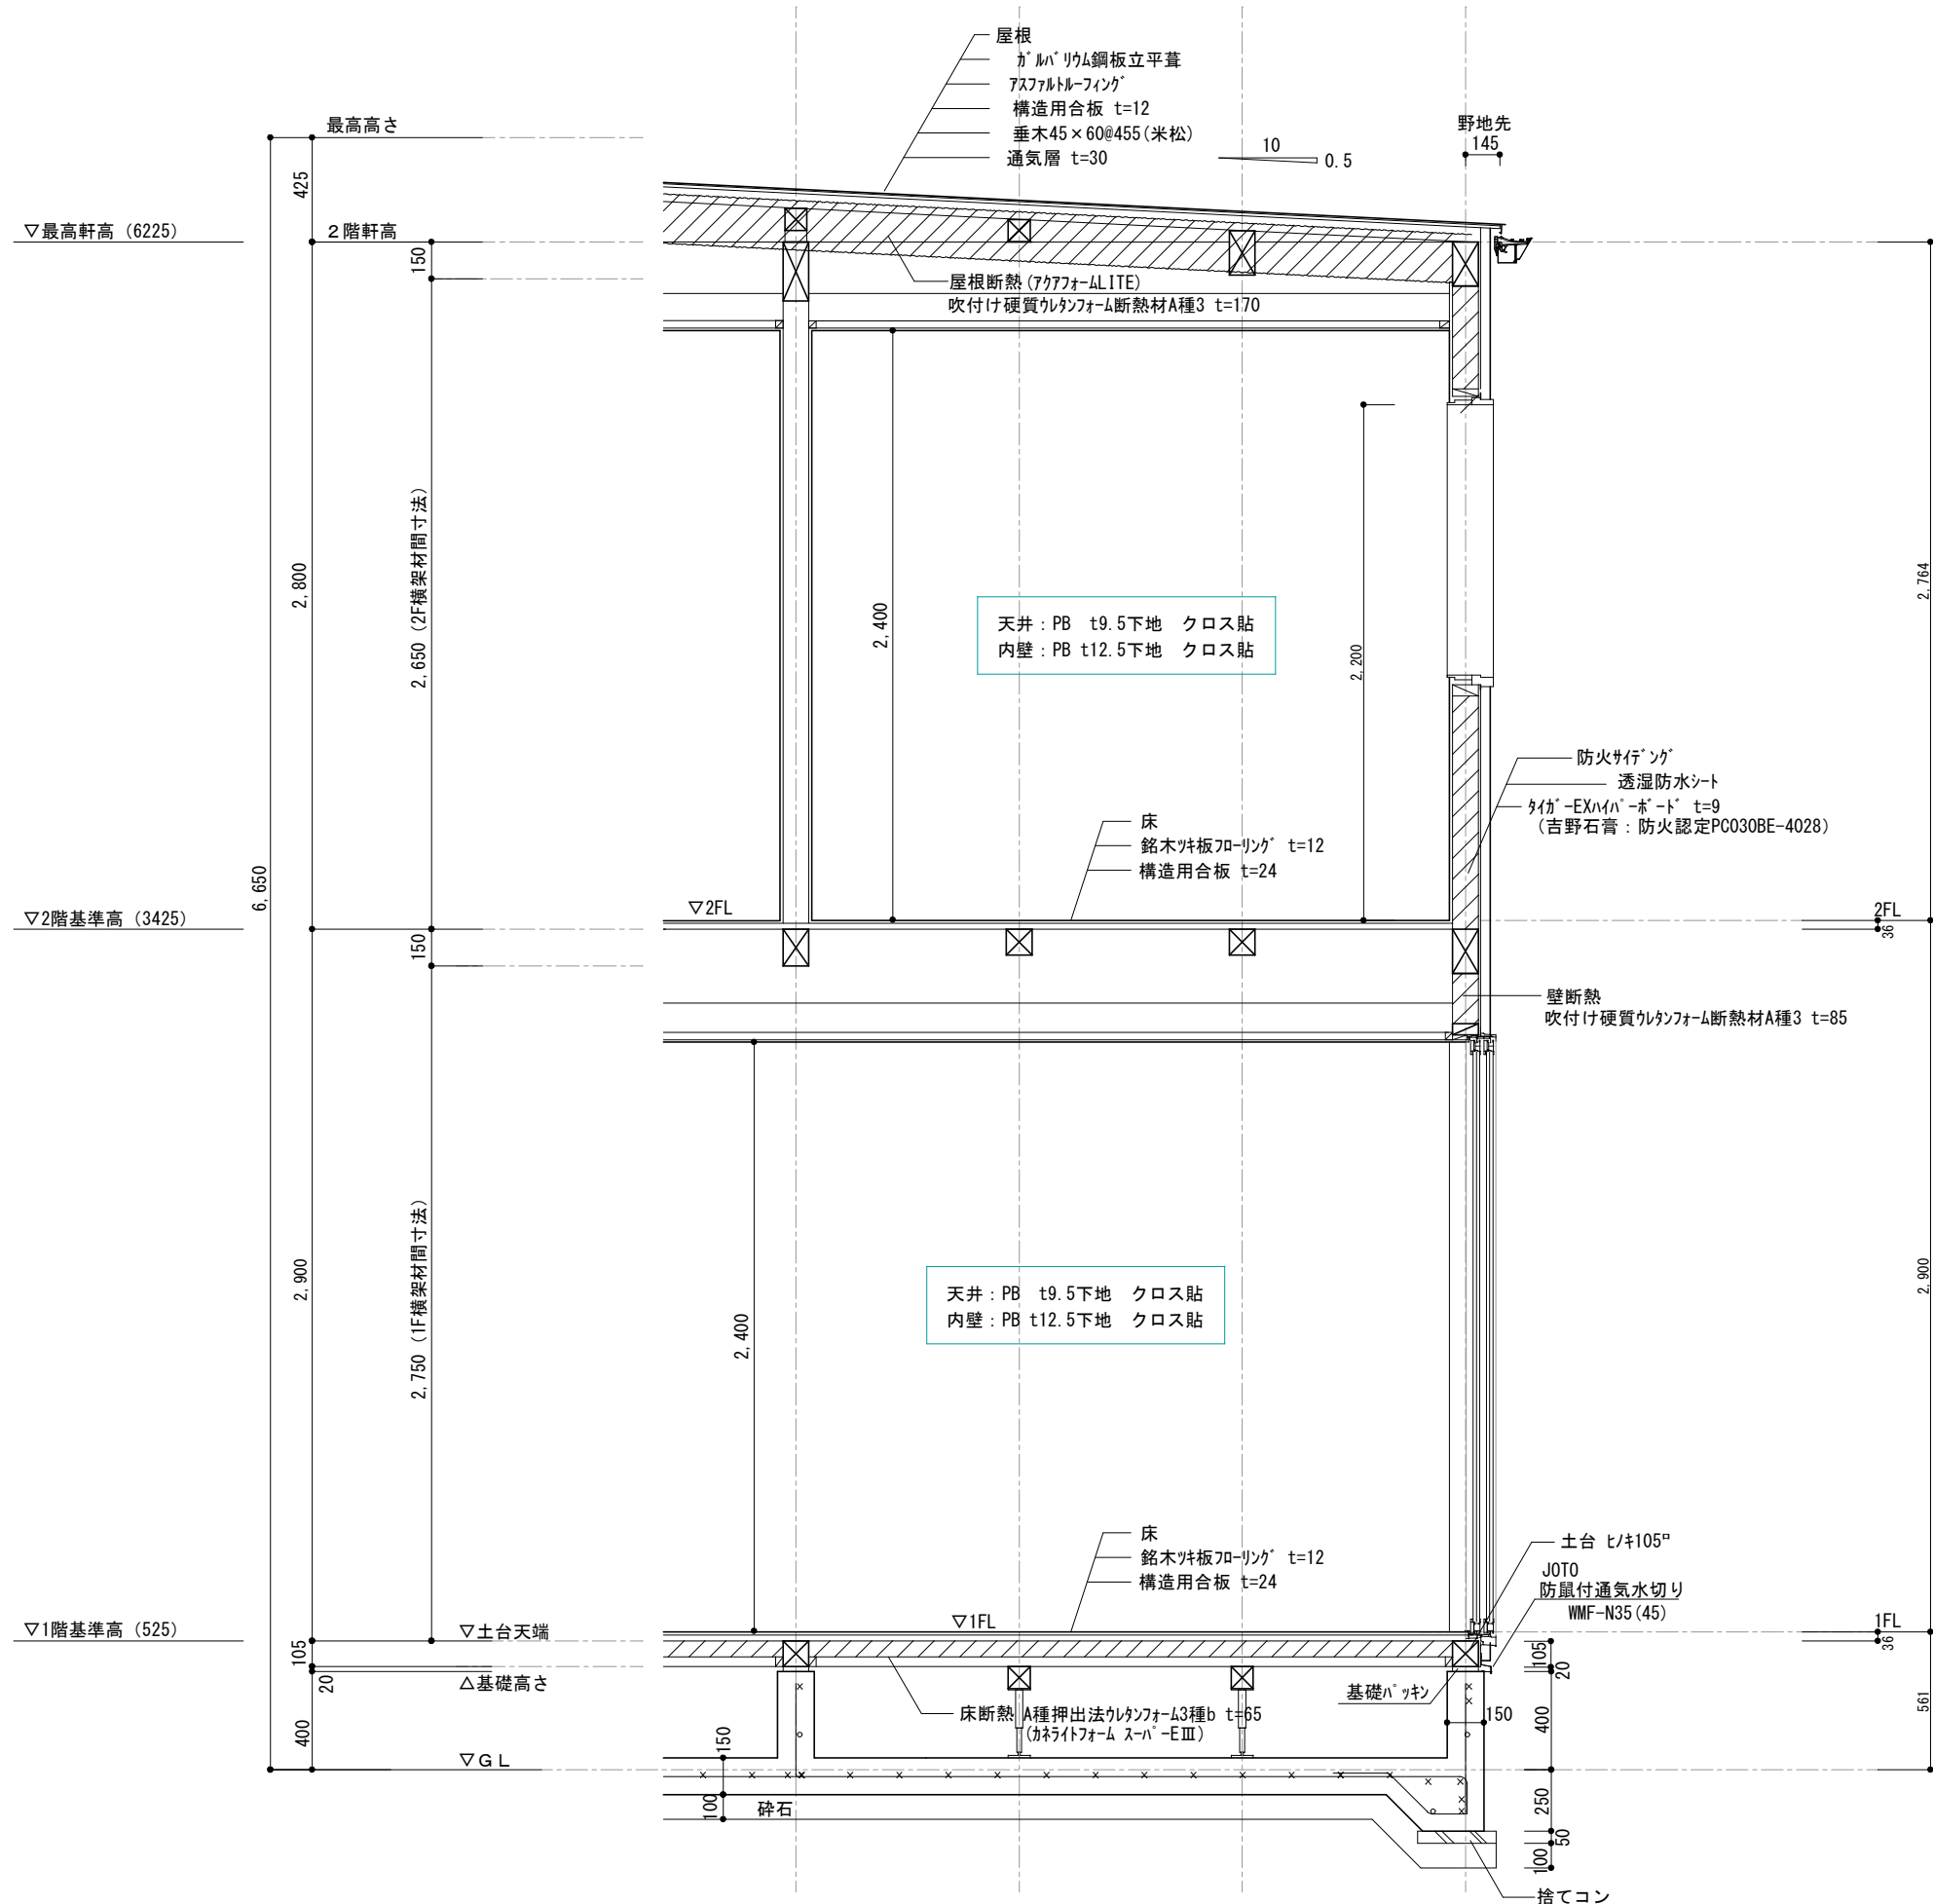


訂正	浜岡一級総合設計事務所 一級建築士事務所 静岡県知事登録第 (10)2441 号 一級建築士 大臣登録第 365879 号 西原利昌		株式会社 LIFEFUND InDesign office 一級建築士事務所 事務所登録 (2) 第7595号 一級建築士登録 第179770号 鈴木 達男 〒432-8023 静岡県浜松市中央区鶴江3丁目70番23号	年月日 2024.11.08	件名 伊藤友章様邸 新築工事		設計	IC	工事	図番
				縮尺 1/100	図名 矩計図		倉田		青島	A-5

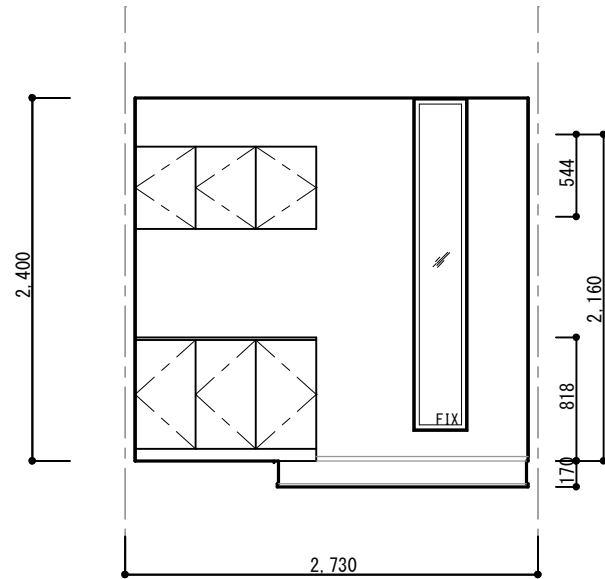


玄関 北面

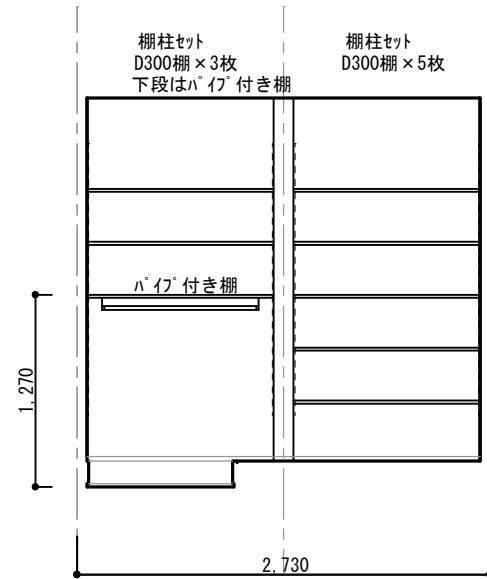


パントリー 北面

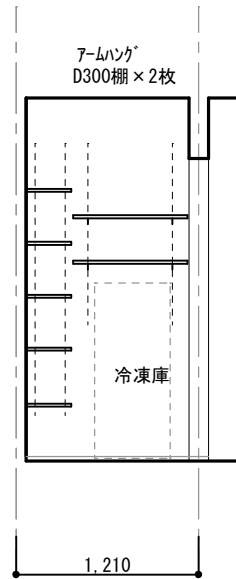


パントリー 東面

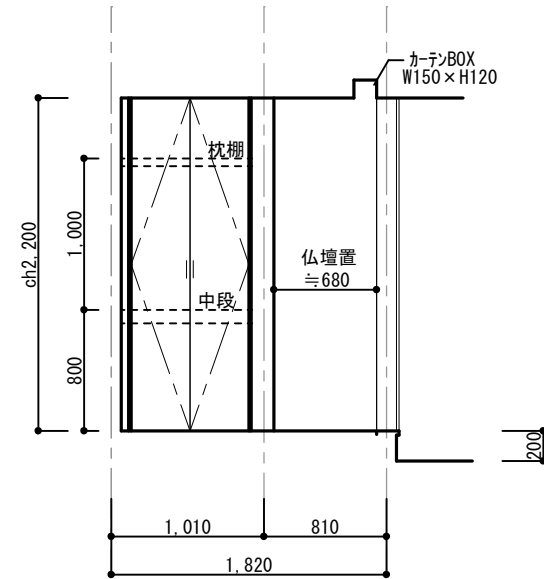


パントリー 東面

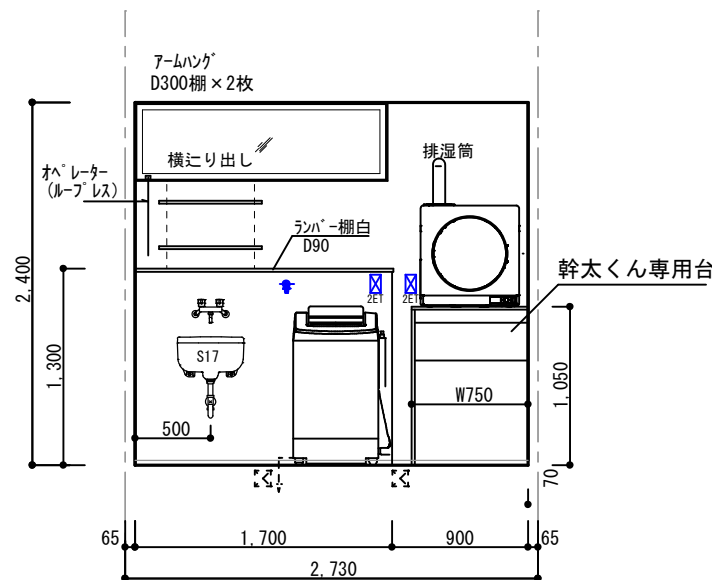


脱衣ランドリー 西面

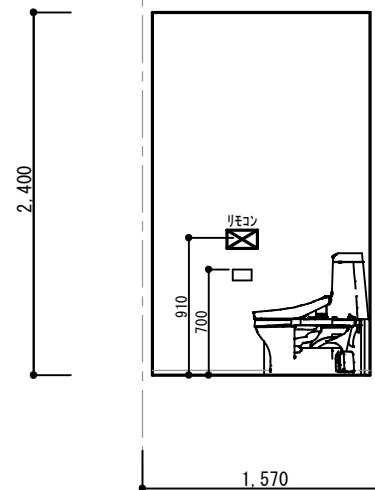


WC① 西側

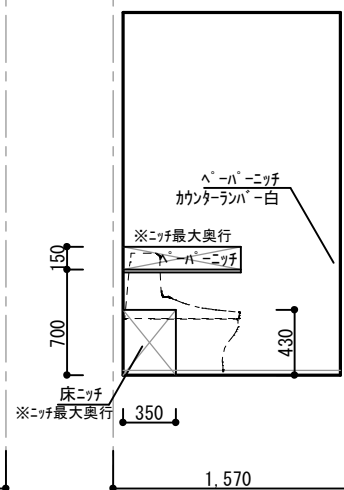


WC① 東側

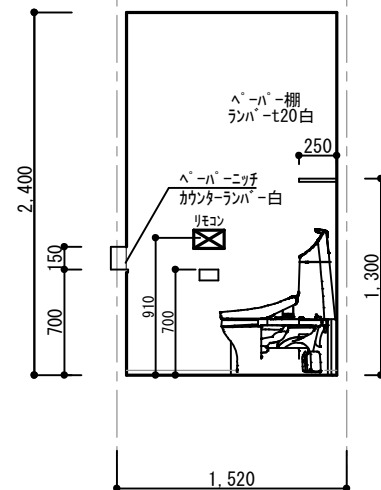


WC② 北面

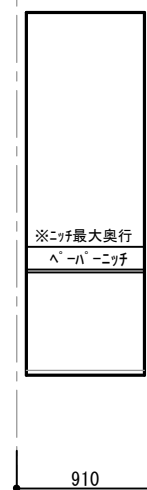

WC② 西面

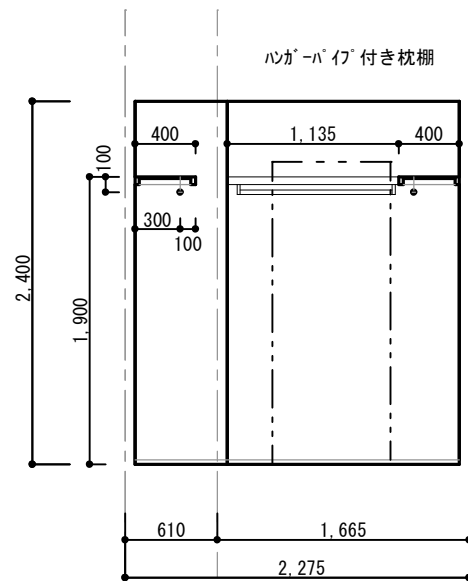


WIC 北面

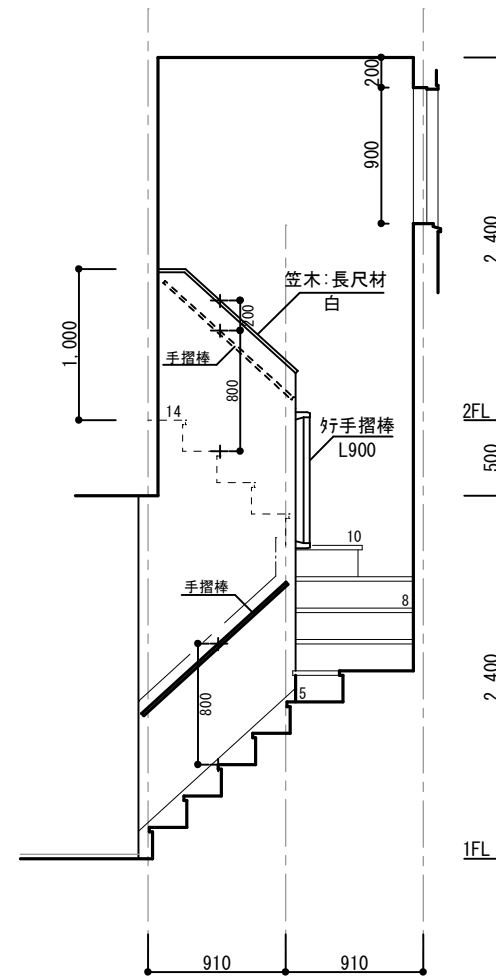



階段 南面

JW-TD90SA


訂正	浜岡一級総合設計事務所 一級建築士事務所 静岡県知事登録第 (10)2441 号 一級建築士 大臣登録第 365879 号 西原利昌	LIFEFUND PG HOUSE	株式会社 LIFEFUND InDesign office 一級建築士事務所 事務所登録 (2) 第7595号 一級建築士登録 第179770号 鈴木 達男 〒432-8023 静岡県浜松市中央区鴨江3丁目70番23号	年月日 2024.11.08 縮尺 1/50	件名 伊藤友章様邸 新築工事 図名 展開図		設計 倉田	IC	工事 青島	図番 6-1
----	--	----------------------	---	---------------------------------	--------------------------------	--	----------	----	----------	-----------

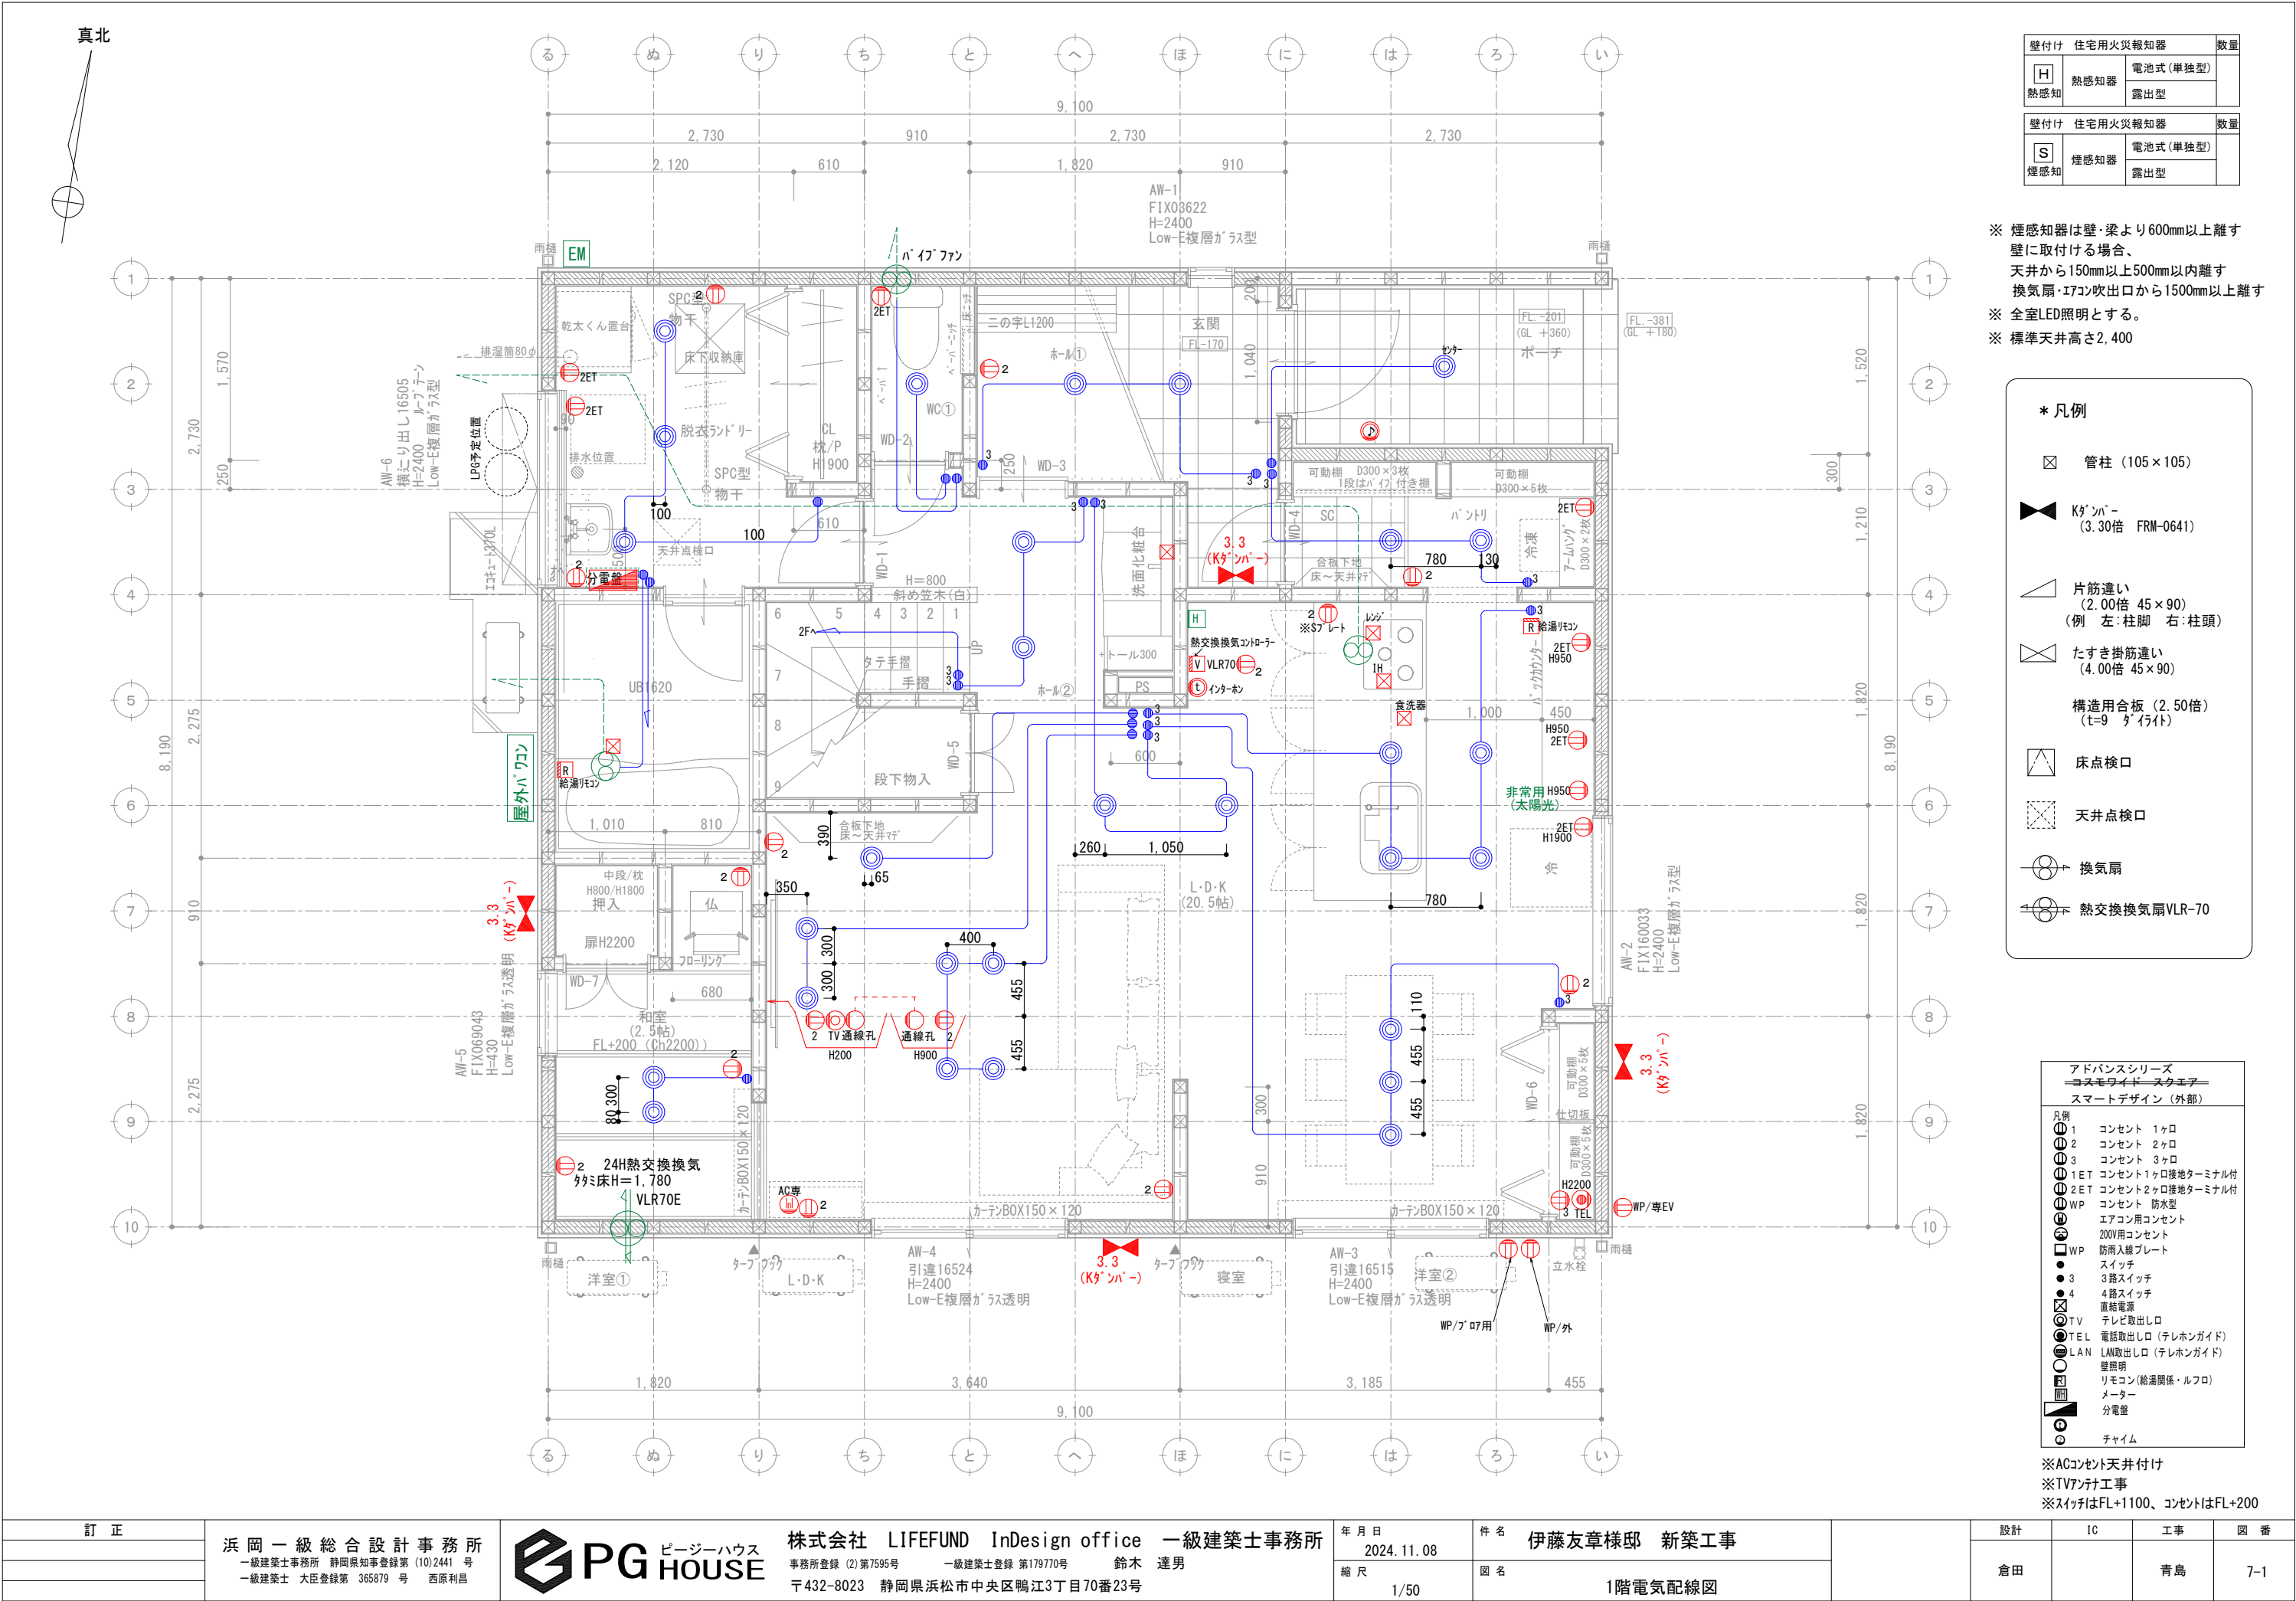

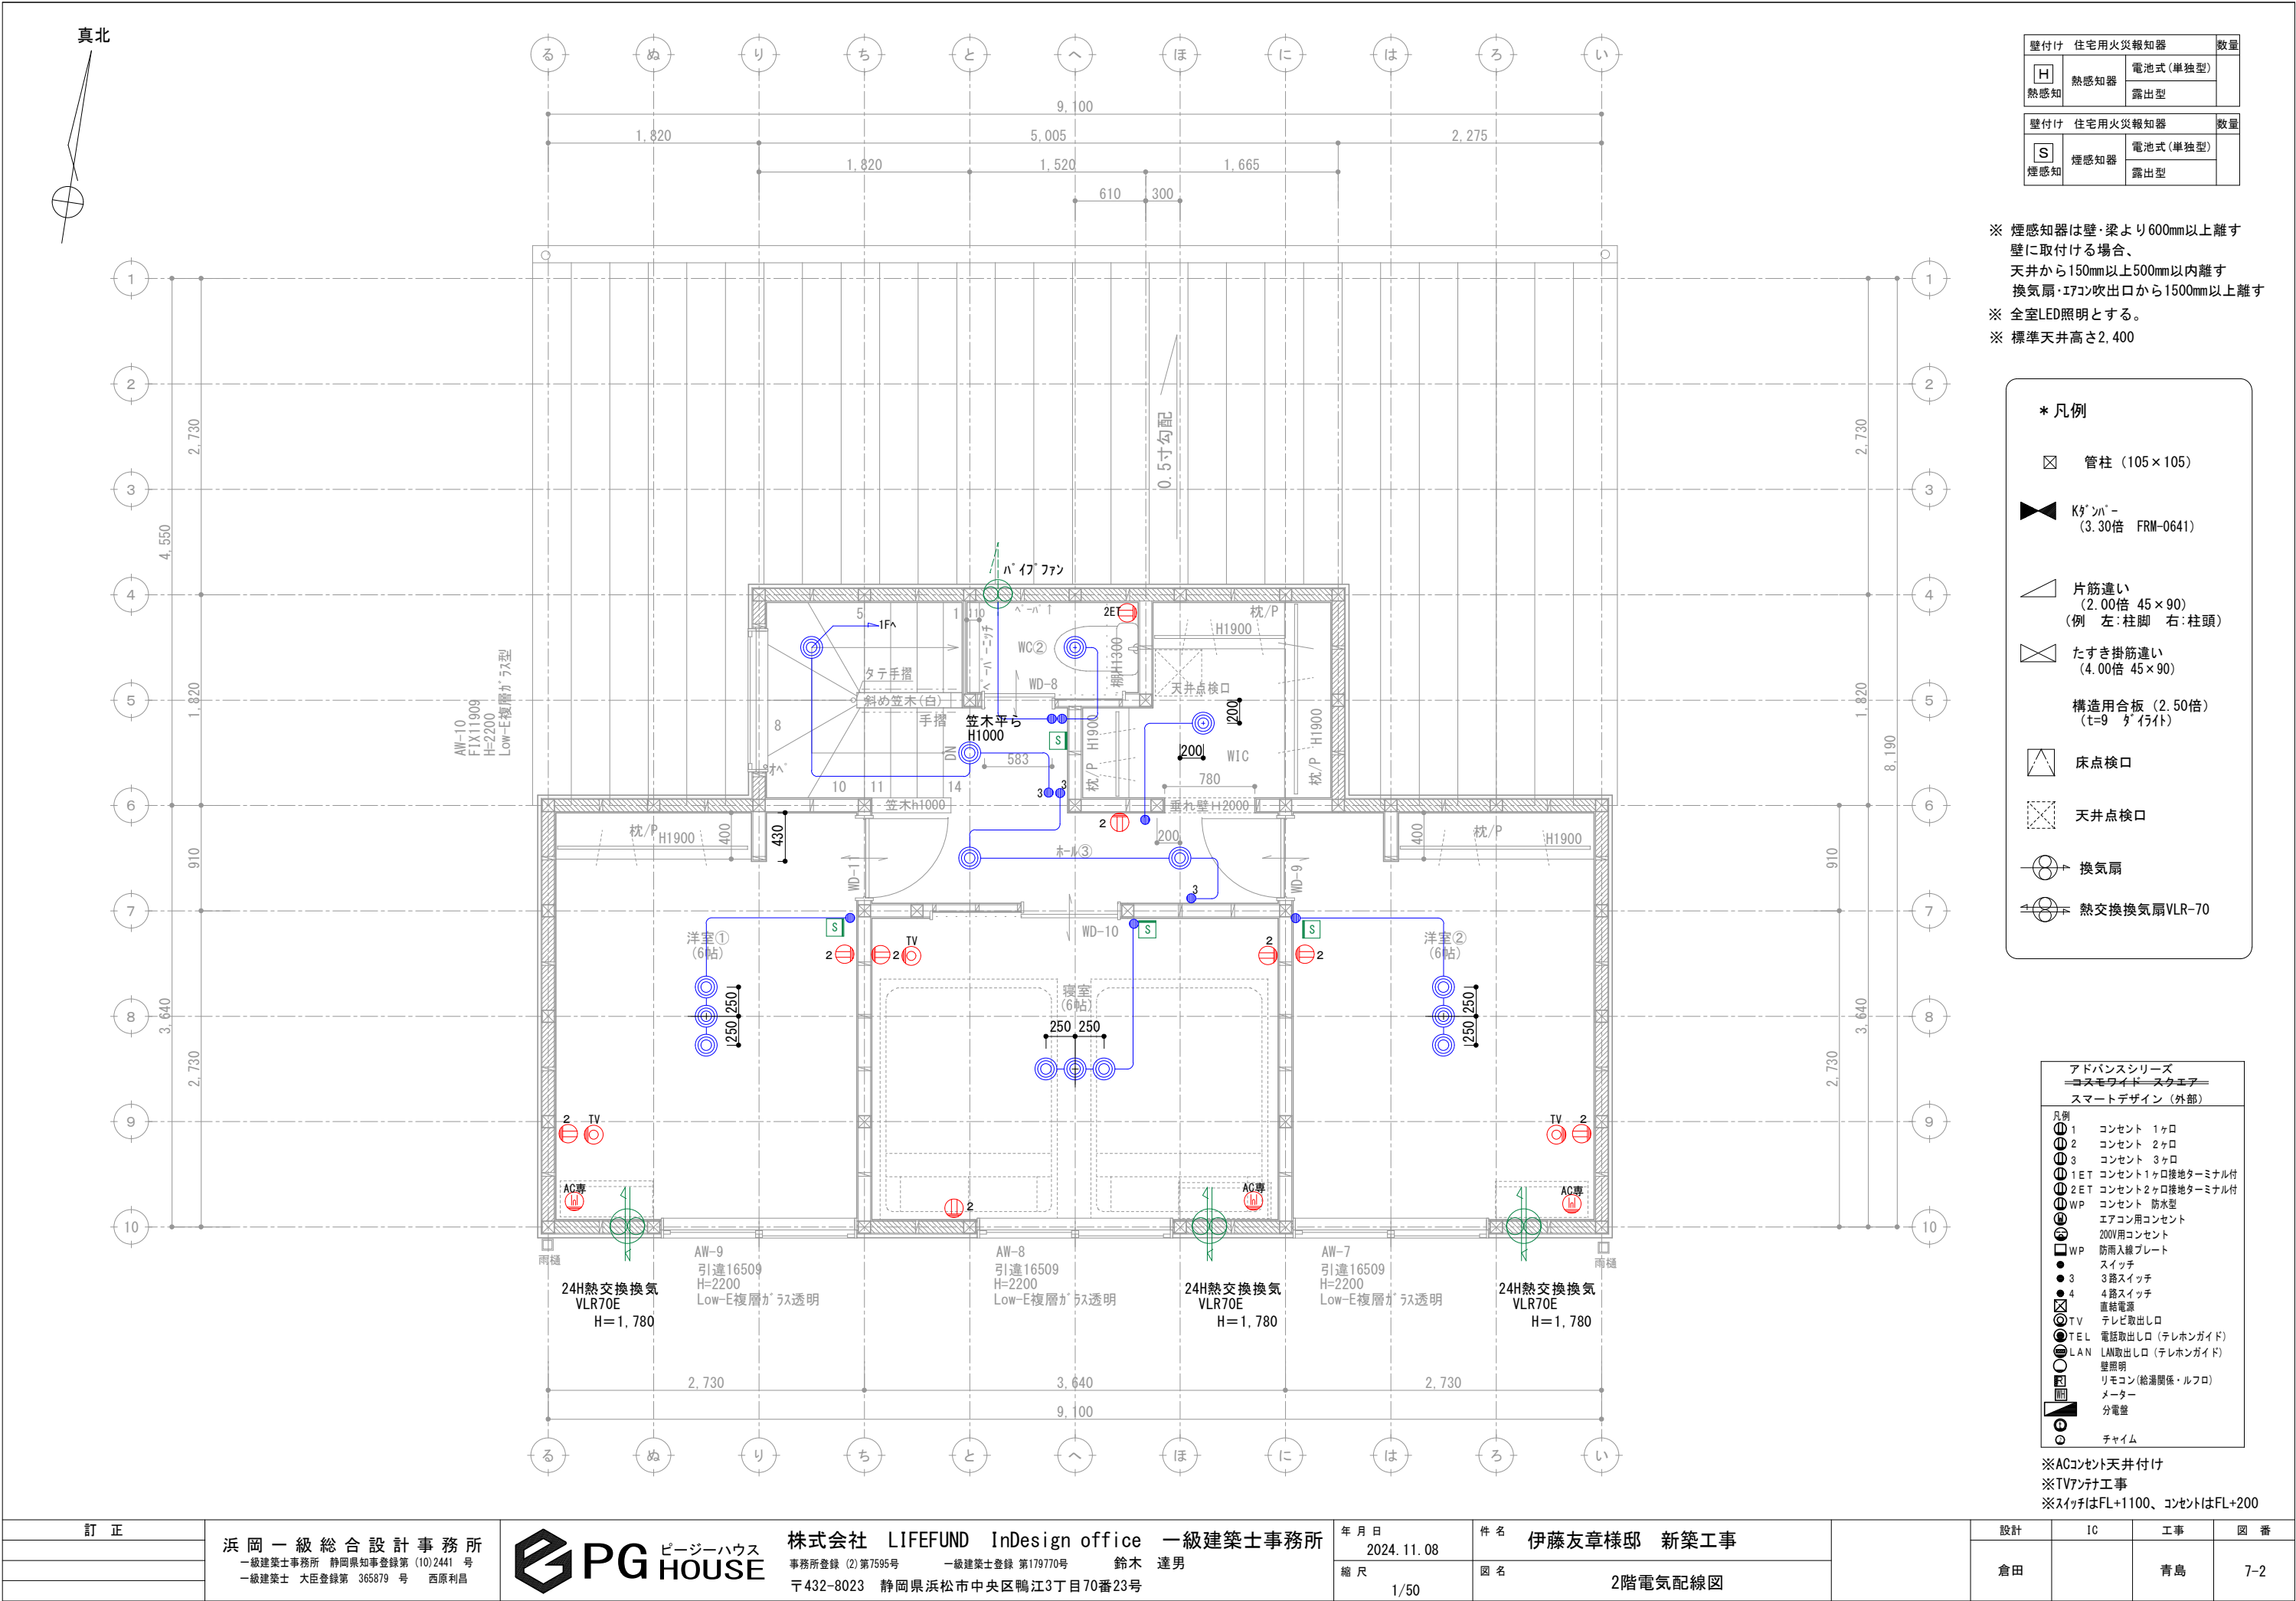

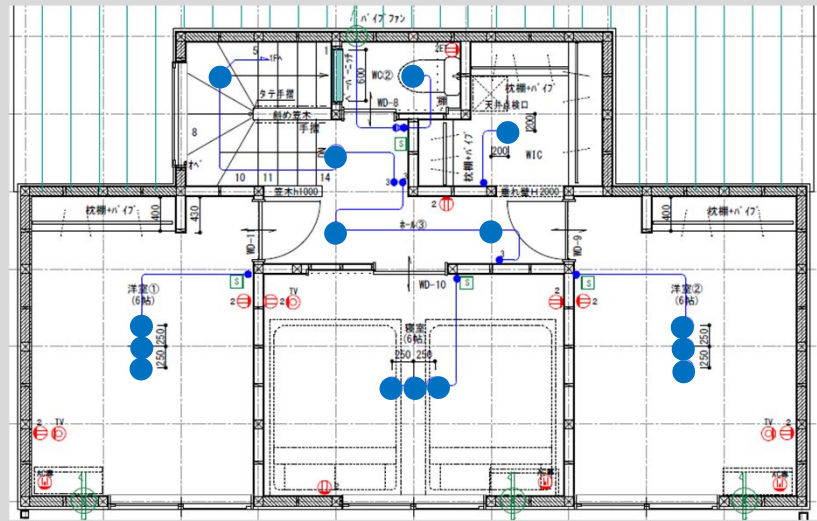


2 階

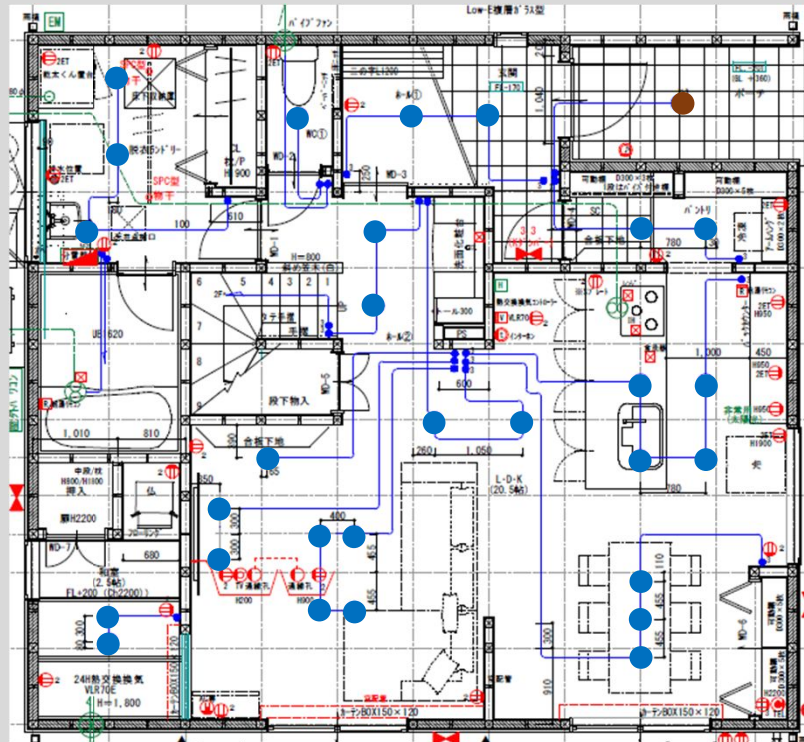

1 階

★オプション

内部：アドバンス(Panasonic)

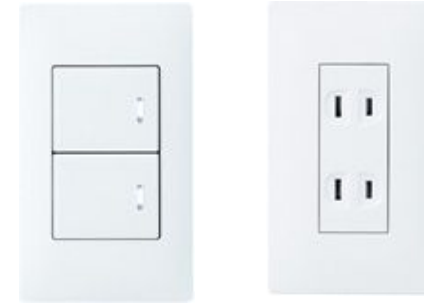

ドアホン：VL-SZ30KL
(Panasonic)



外部：スマートデザインシリーズ (Panasonic)

表情豊かな住まいをつくり出すスマートデザインシリーズ。



外壁色に合わせ。

ポーチ灯

● × 1

DDL-4496YB



高気密Se形 | 人感センサー | 連動マルチタイプ

DDL-4496 YB

電球色 / 2700K・Ra83

定格光束 消費電力 固有エネルギー消費効率
425lm 7.7W 55.1lm/W

¥18,800-(税抜) (LED内蔵)

- LED LED 7.7W 白熱灯60W相当
- アルミダイカスト 黒塗装
- アクリル 乳白(マット)
- 径φ111 埋込穴φ100
- 埋込深80mm 0.5kg
- 14VA
- 点灯照度調節機能付(暗・明・切)
- 点灯保持時間(1分)
- 拡散パネル付
- AC100V
- 光源寿命50,000時間
- 取付可能天井厚5~25mm
- 調光器併用不可

【連動器具について】
LED調光タイプ60VAまで
LED非調光タイプ不可 蛍光灯不可
白熱灯60Wまで

基本照明ダウンライト

● × 43 (23+15)

DDL6102YW



COBタイプ | 高気密Se形

DDL-6102 YW

電球色 / 2700K・Ra83





定格光束 消費電力 固有エネルギー消費効率
440lm 4.6W 95.6lm/W

¥3,600-(税抜) (LED内蔵)

- LED LED 4.6W 白熱灯60W相当
- 銅板 白塗装
- アクリル 乳白(マット)
- 径φ116 埋込穴φ100 埋込深70mm 0.3kg
- 8VA
- 拡散パネル付
- AC100V
- 光源寿命60,000時間
- 取付可能天井厚5~25mm
- 調光器併用不可

LED交換不可	非調光
防雨形	60°
温度保護機能付	0.1m 近接検出
埋込穴 100	埋込必要高 70
	傾斜天井 55°
	準耐火

2024.11.08.

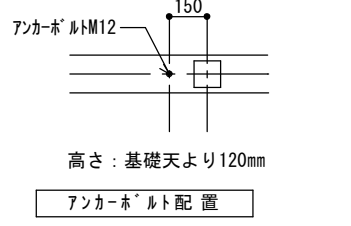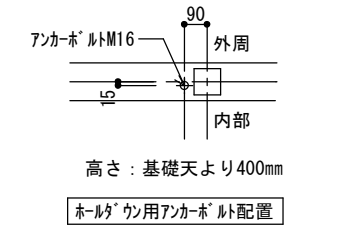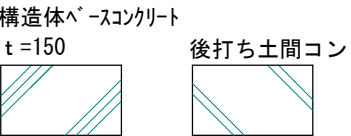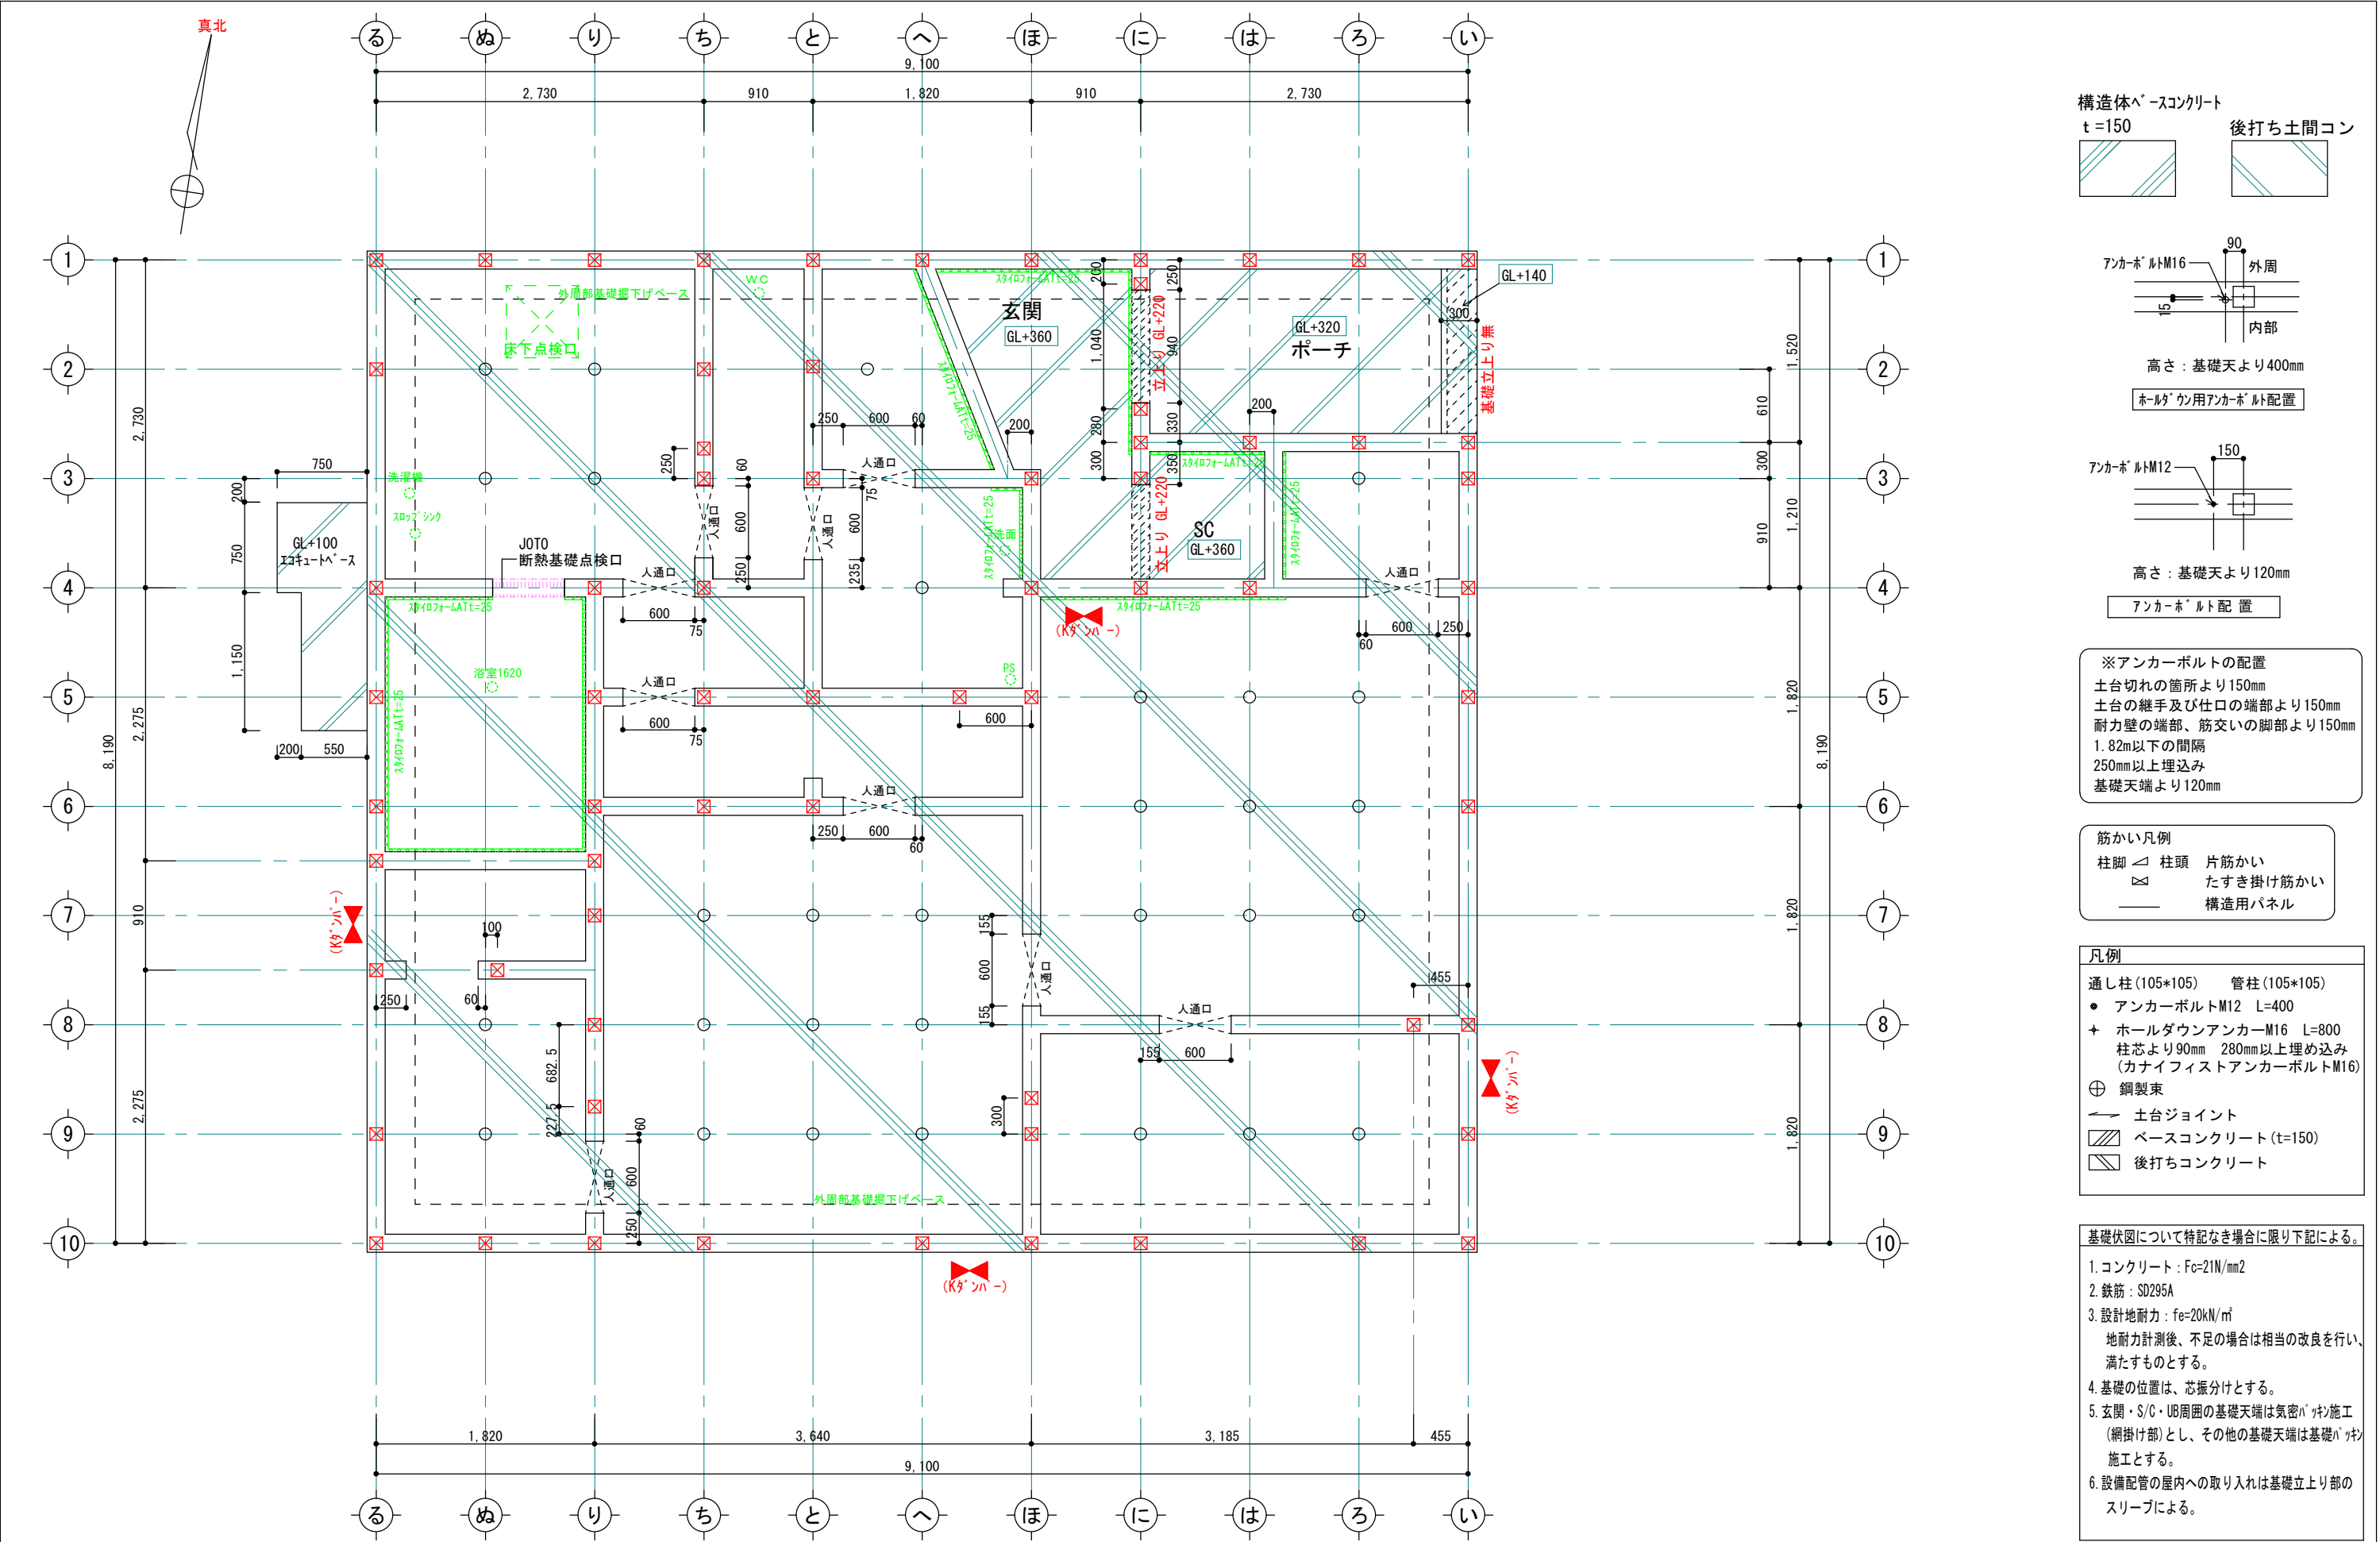


※アンカーボルトの配置
土台切れの箇所より150mm
土台の継手及び仕口の端部より150mm
耐力壁の端部、筋交いの脚部より150mm
1.82m以下の間隔
250mm以上埋込み
基礎天端より120mm

筋かい凡例
柱脚 柱頭 筋かい
たすき掛け筋かい
構造用パネル

凡例
通し柱 (105*105) 管柱 (105*105)
● アンカーボルトM12 L=400
+ ホールダウンアンカーM16 L=800
柱芯より90mm 280mm以上埋め込み
(カナイフイストアンカーボルトM16)
⊕ 鋼製束
土台ジョイント
ベースコンクリート (t=150)
後打ちコンクリート

基礎伏図について特記なき場合に限り下記による。

1. コンクリート : $F_c=21N/mm^2$
2. 鉄筋 : SD295A
3. 設計地耐力 : $f_e=20kN/m^2$
地耐力計測後、不足の場合は相当の改良を行い、満たすものとする。
4. 基礎の位置は、芯振分けとする。
5. 玄関・S/C・UB周囲の基礎天端は気密パッキン施工 (網掛け部)とし、その他の基礎天端は基礎パッキン施工とする。
6. 設備配管の屋内への取り入れは基礎立上り部のスリーブによる。

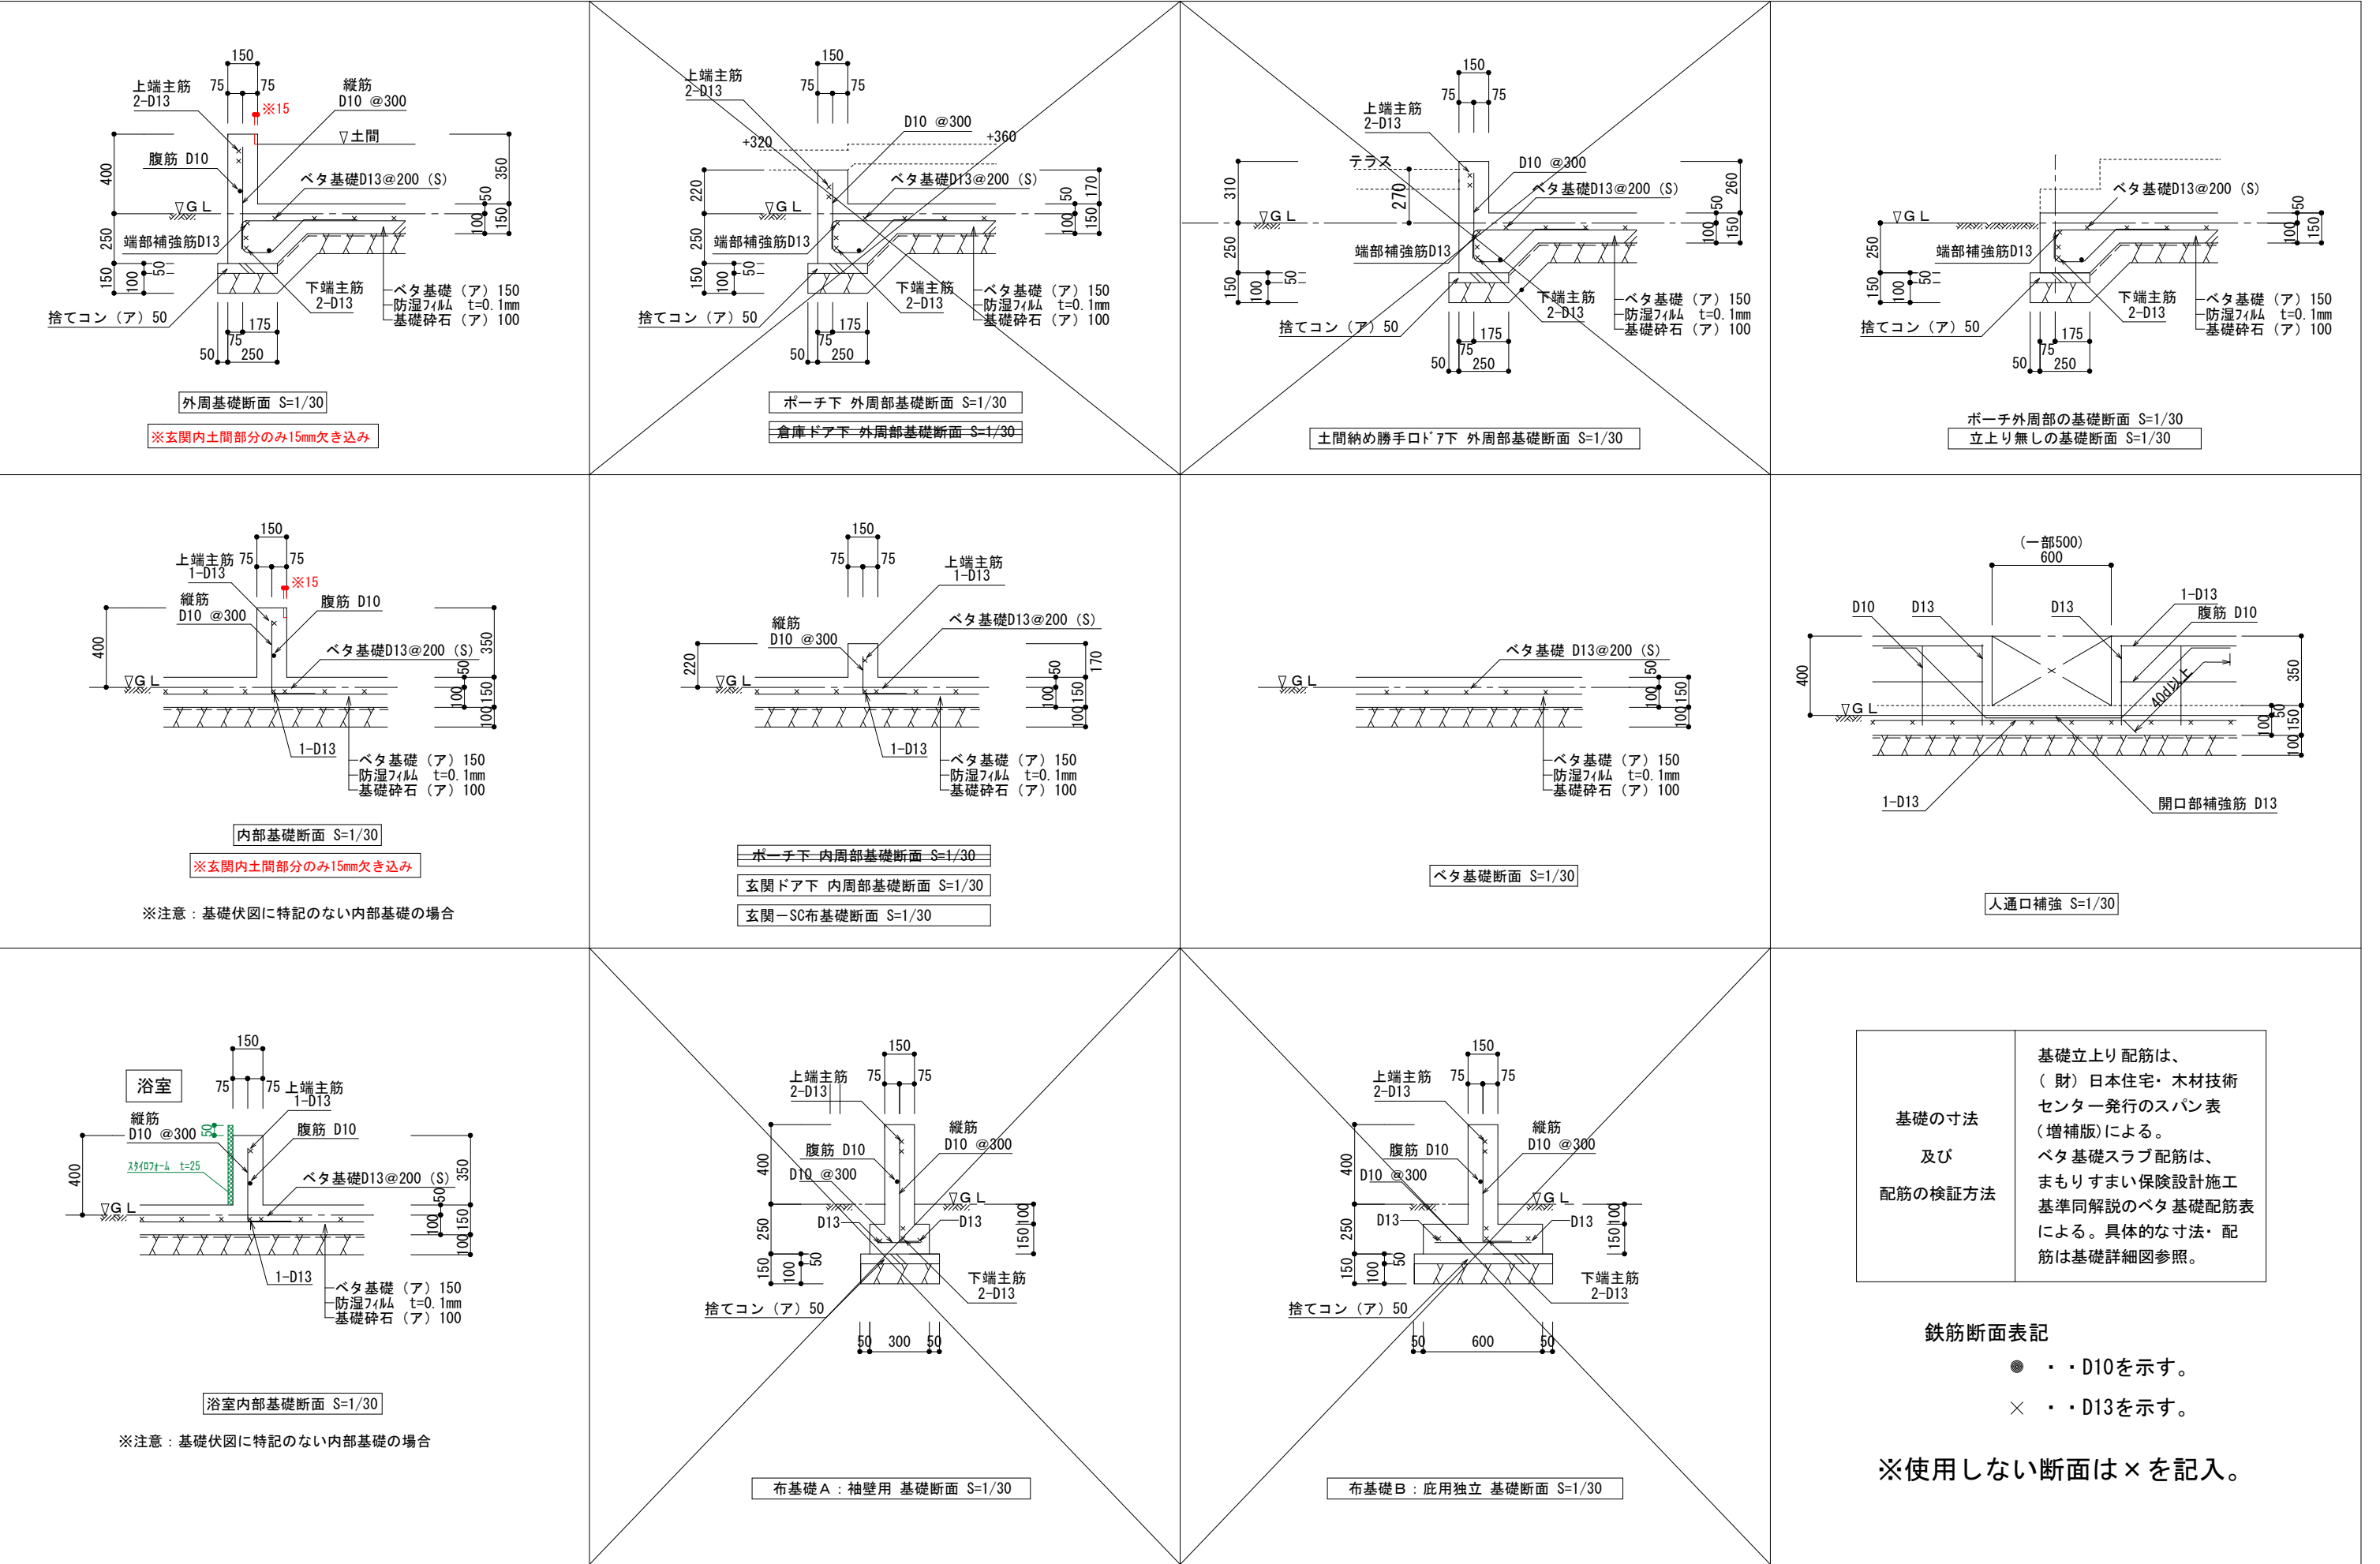

基礎の寸法
及び
配筋の検証方法

基礎立上り配筋は、
(財)日本住宅・木材技術
センター発行のスパン表
(増補版)による。
ベタ基礎スラブ配筋は、
まもりすまい保険設計施工
基準同解説のベタ基礎配筋表
による。具体的な寸法・配
筋は基礎詳細図参照。

鉄筋断面表記

●・・・D10を示す。
×・・・D13を示す。

※使用しない断面は×を記入。