


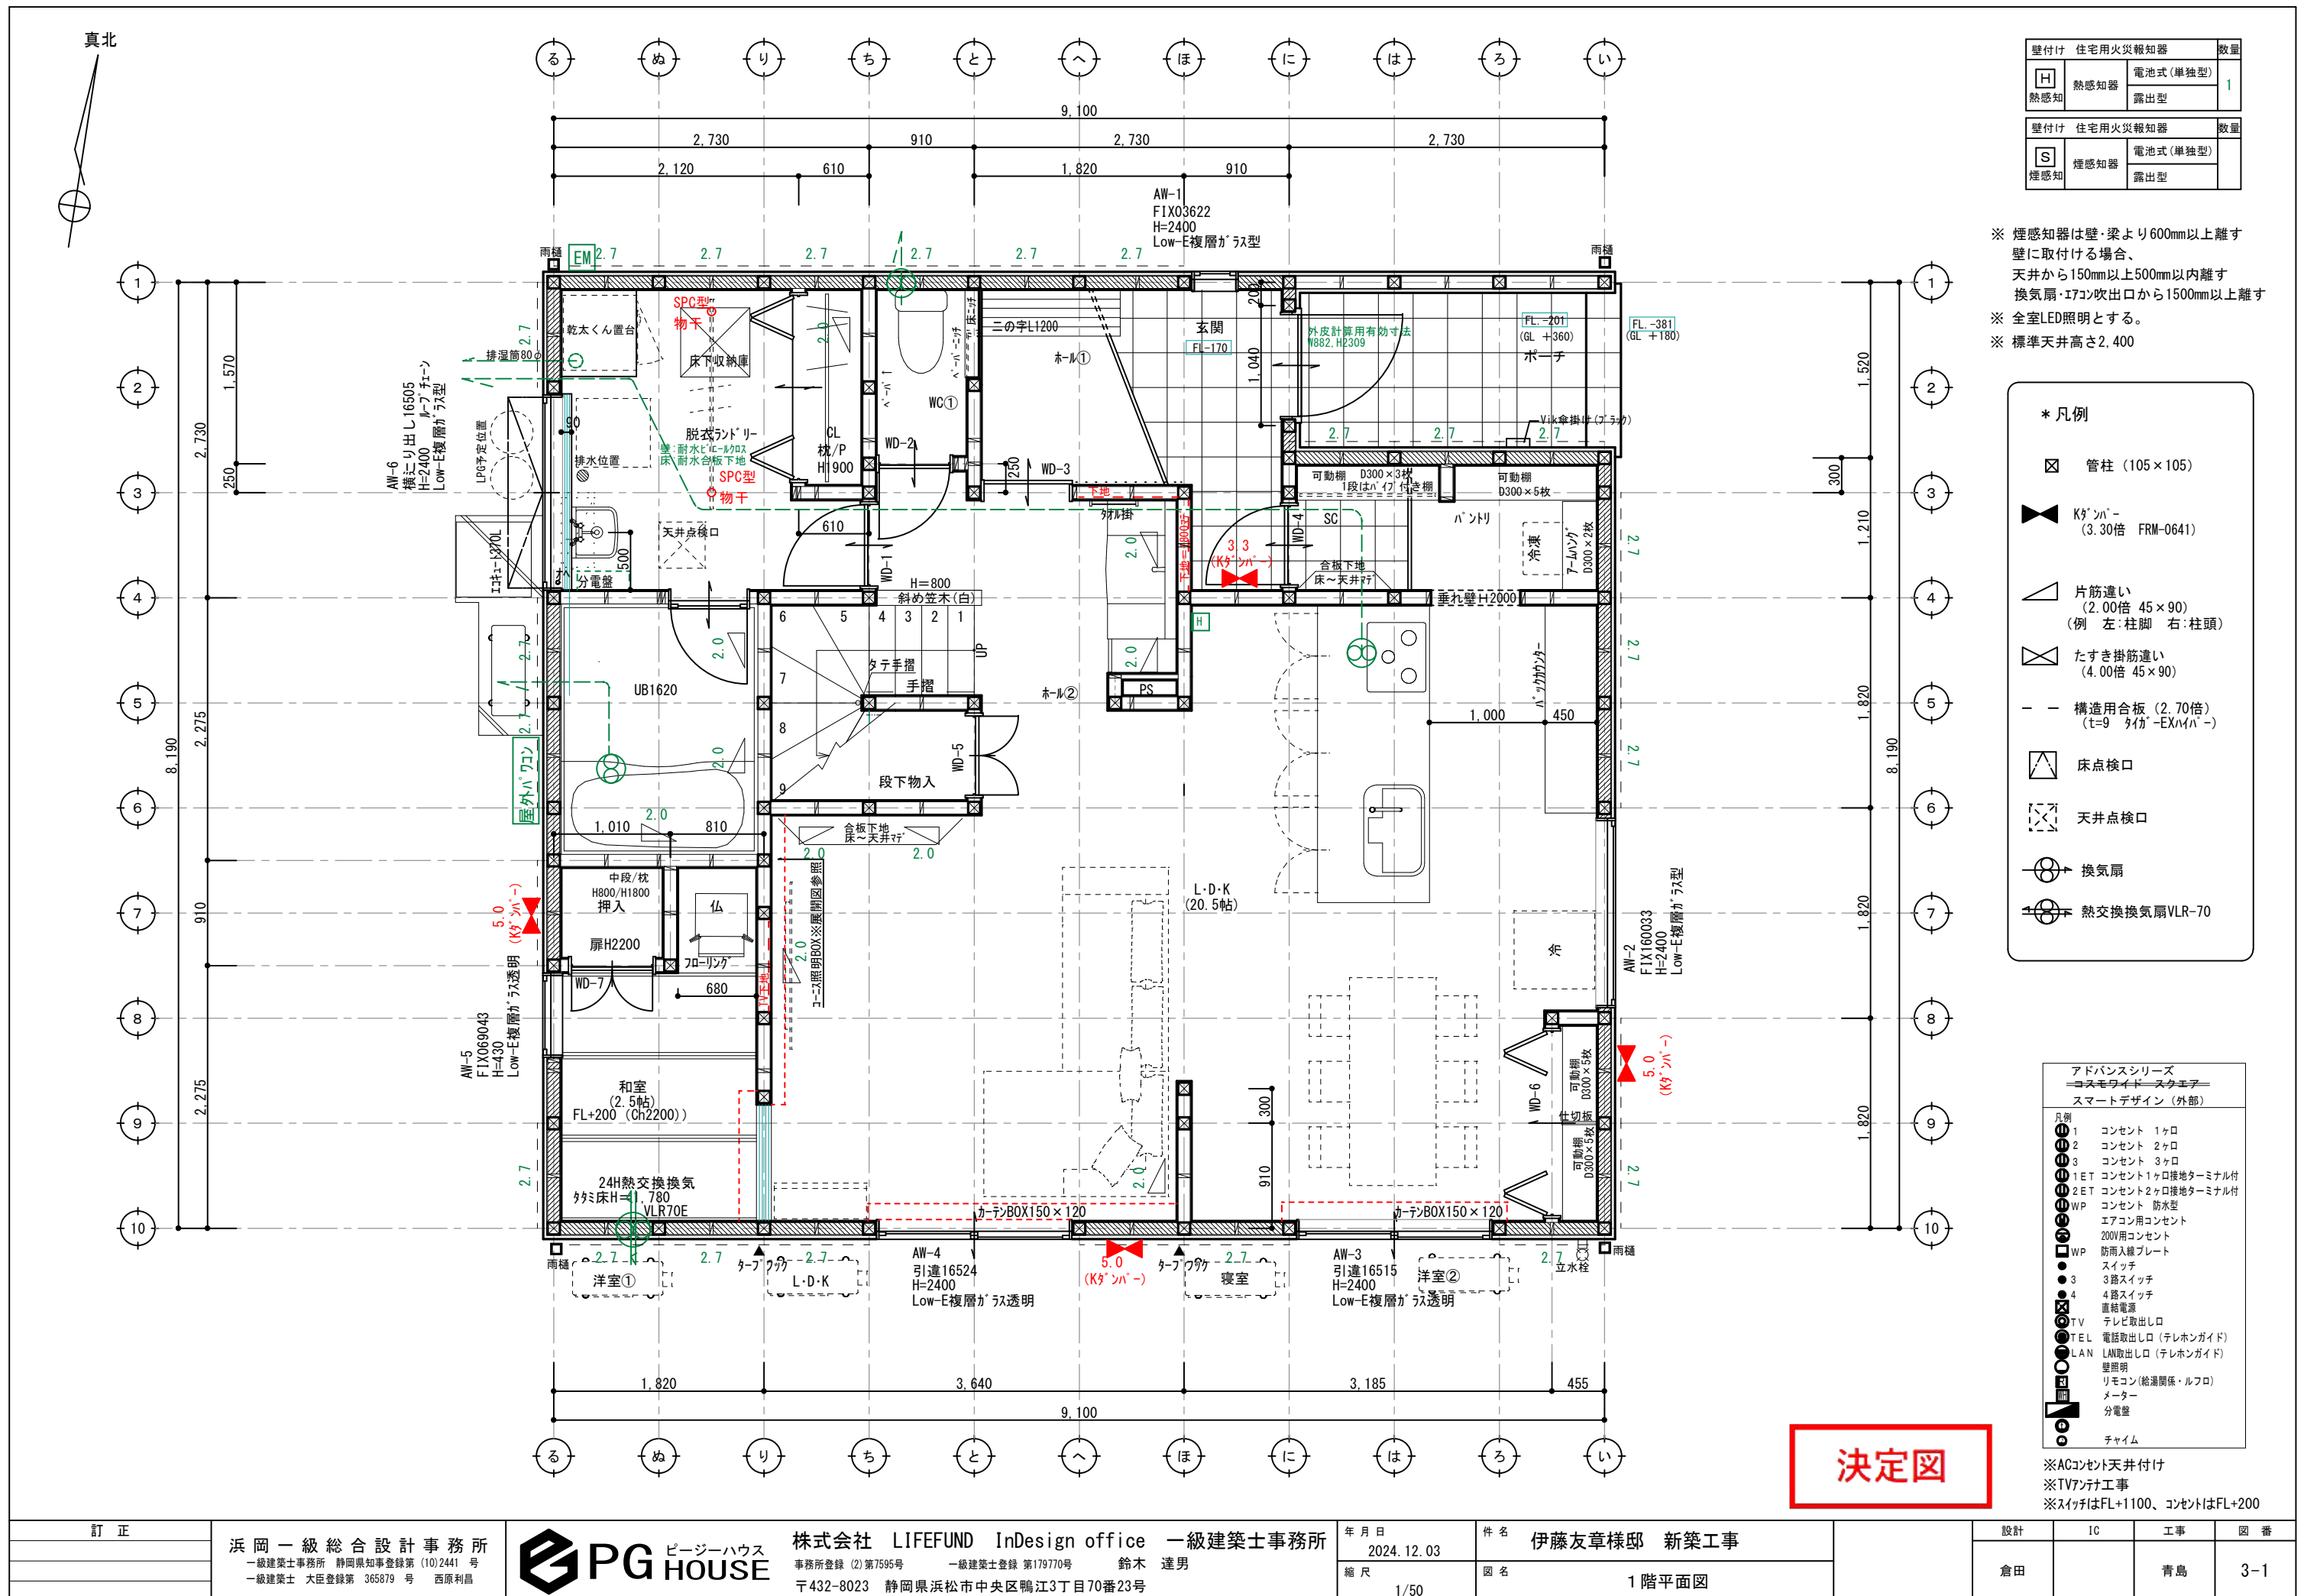

壁付け 住宅用火災報知器			数量
H	熱感知器	電池式(単独型)	1
	露出型		
壁付け 住宅用火災報知器			数量
S	煙感知器	電池式(単独型)	
	露出型		

※ 煙感知器は壁・梁より600mm以上離す
壁に取付ける場合、
天井から150mm以上500mm以内離す
換気扇・エアコン吹出口から1500mm以上離す
※ 全室LED照明とする。
※ 標準天井高さ2,400

* 凡例

管柱 (105×105)

Kダクト (3.30倍 FRM-0641)

片筋違い (2.00倍 45×90)
(例 左:柱脚 右:柱頭)

たすき掛筋違い (4.00倍 45×90)

構造用合板 (2.70倍)
(t=9 材種-EXハイバ-)

床点検口

天井点検口

換気扇

熱交換換気扇VLR-70

アドバンスシリーズ コネクトワイヤードライバースタンド スマートデザイン (外部)			
凡例	1	コンセント 1ヶ所	
	2	コンセント 2ヶ所	
	3	コンセント 3ヶ所	
	1ET	コンセント1ヶ所接地ターミナル付	
	2ET	コンセント2ヶ所接地ターミナル付	
	WP	コンセント 防水型	
		エアコン用コンセント	
		200V用コンセント	
	WP	防雨入線プレート	
		スイッチ	
	3	3路スイッチ	
	4	4路スイッチ	
		直結電源	
	TV	テレビ取出口	
	TEL	電話取出口 (テレホンガイド)	
	LAN	LAN取出口 (テレホンガイド)	
		壁照明	
		リモコン (給湯関係・ルフロ)	
		メーター	
		分電盤	
		チャイム	

※ACコンセント天井付け
※TVアンテナ工事
※スイッチはFL+1100、コンセントはFL+200

決定図