




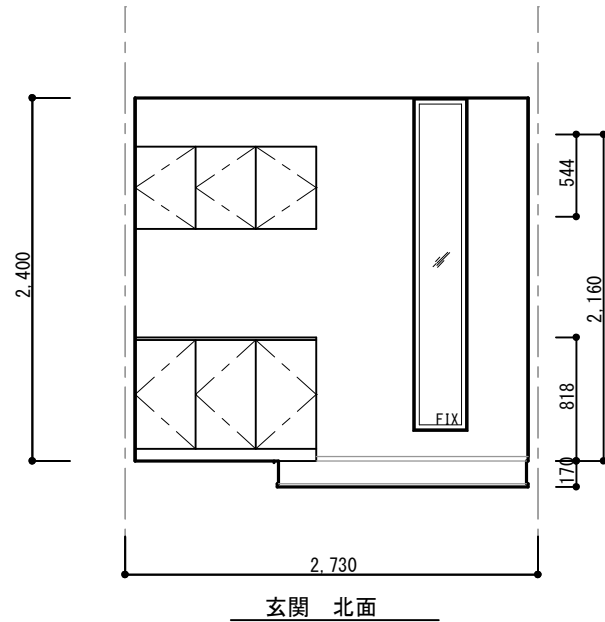


玄関 北面

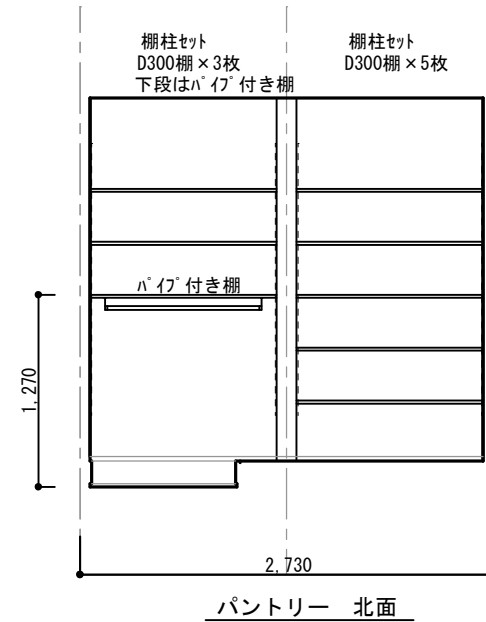


パントリー 北面

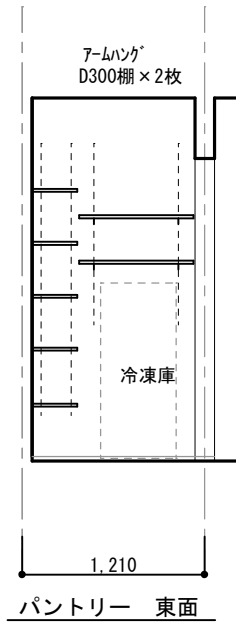



パントリー 東面

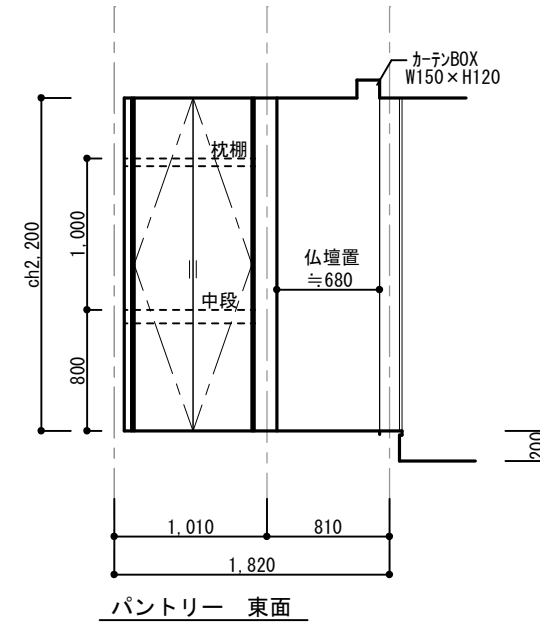


パントリー 東面

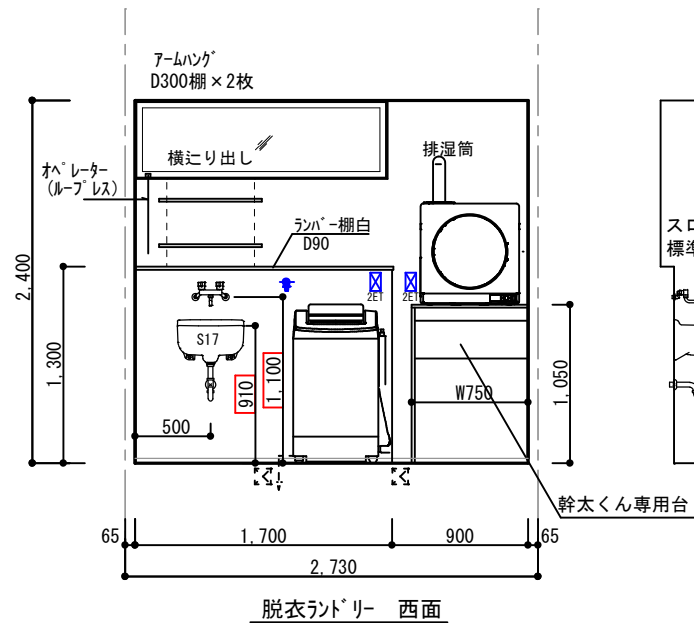


脱衣ランドリー 西面

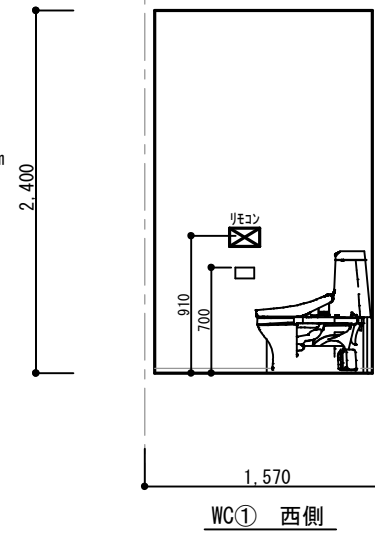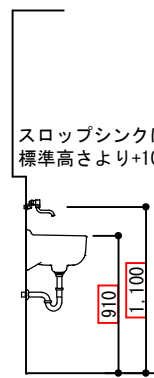


WC① 西側

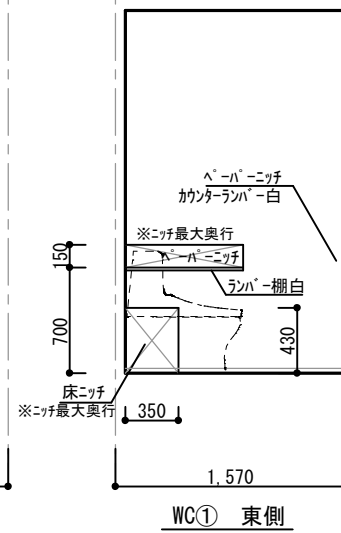


WC① 東側

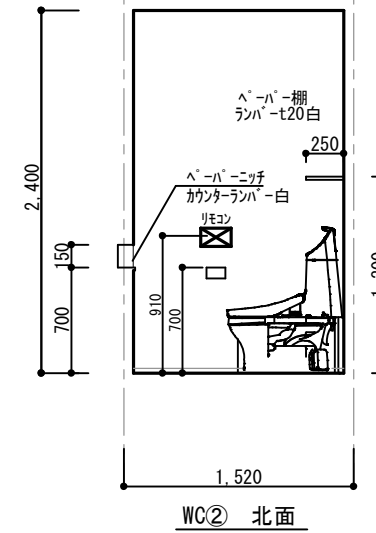


WC② 北面

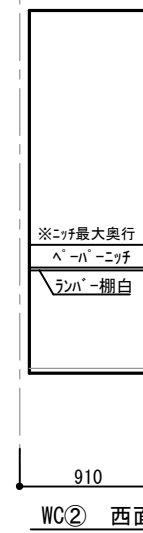


WC② 西面

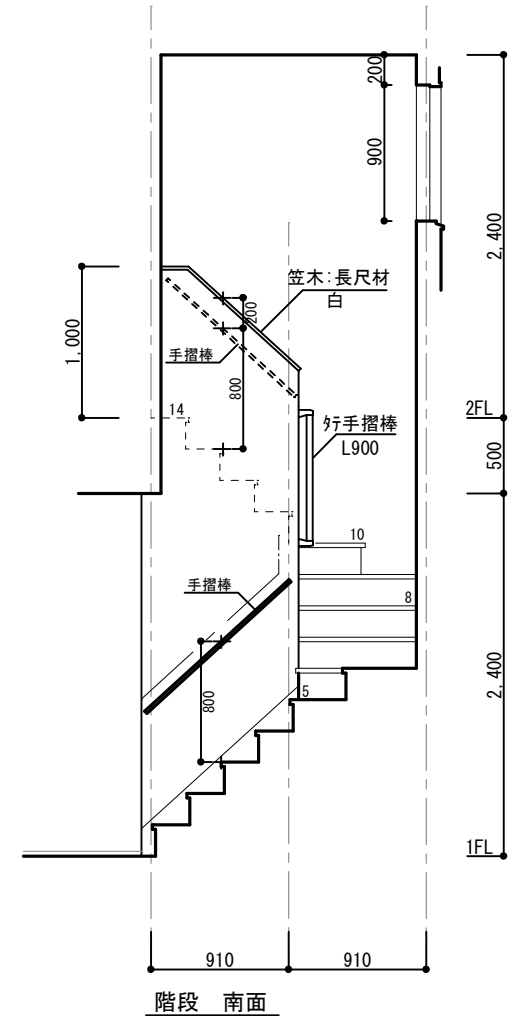


階段 南面

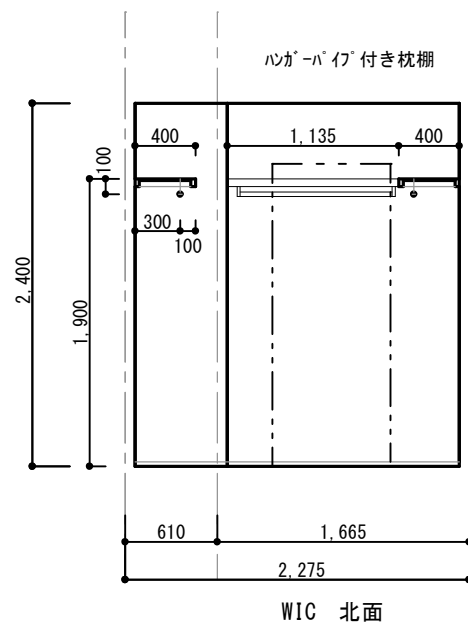


LDK 北面

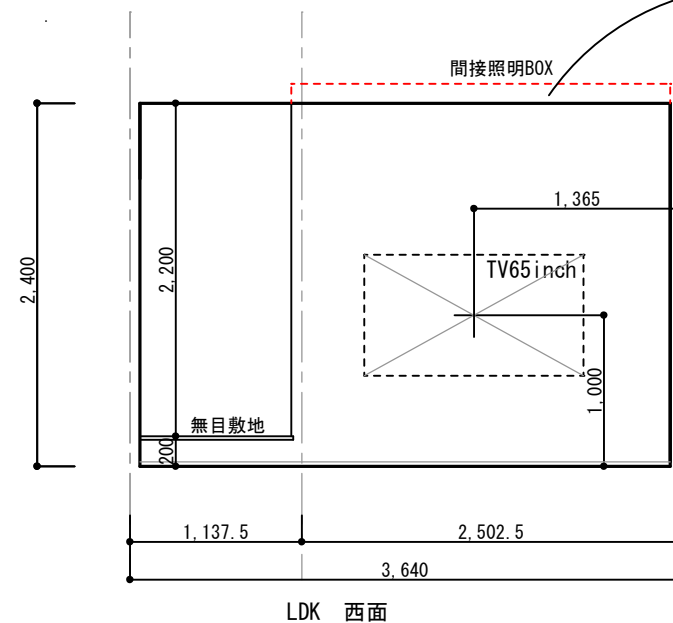

LDK 西面

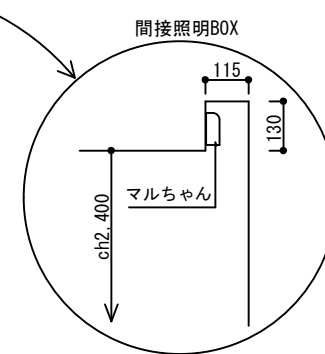

タオル掛け 紙巻器は支給のため下地要す。(WC① ② 洗面)

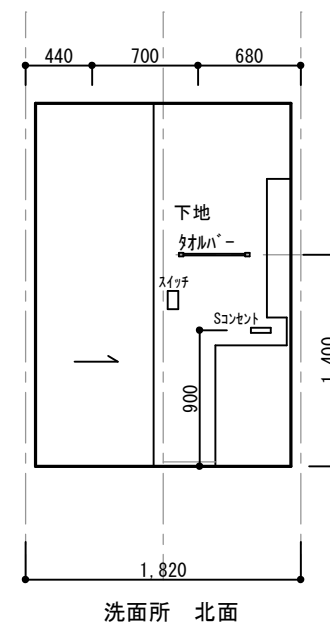

洗面所 北面

決定図

訂正	浜岡一級総合設計事務所 一級建築士事務所 静岡県知事登録第 (10)2441 号 一級建築士 大臣登録第 365879 号 西原利昌	LIFEFUND PG HOUSE	株式会社 LIFEFUND InDesign office 一級建築士事務所 事務所登録 (2) 第7595号 一級建築士登録 第179770号 鈴木 達男 〒432-8023 静岡県浜松市中央区鴨江3丁目70番23号	年月日 2024. 11. 25 縮尺 1/50	件名 伊藤友章様邸 新築工事 図名 展開図		設計 倉田	IC	工事 青島	図番 6-1
----	--	----------------------	---	-----------------------------------	--------------------------------	--	----------	----	----------	-----------