



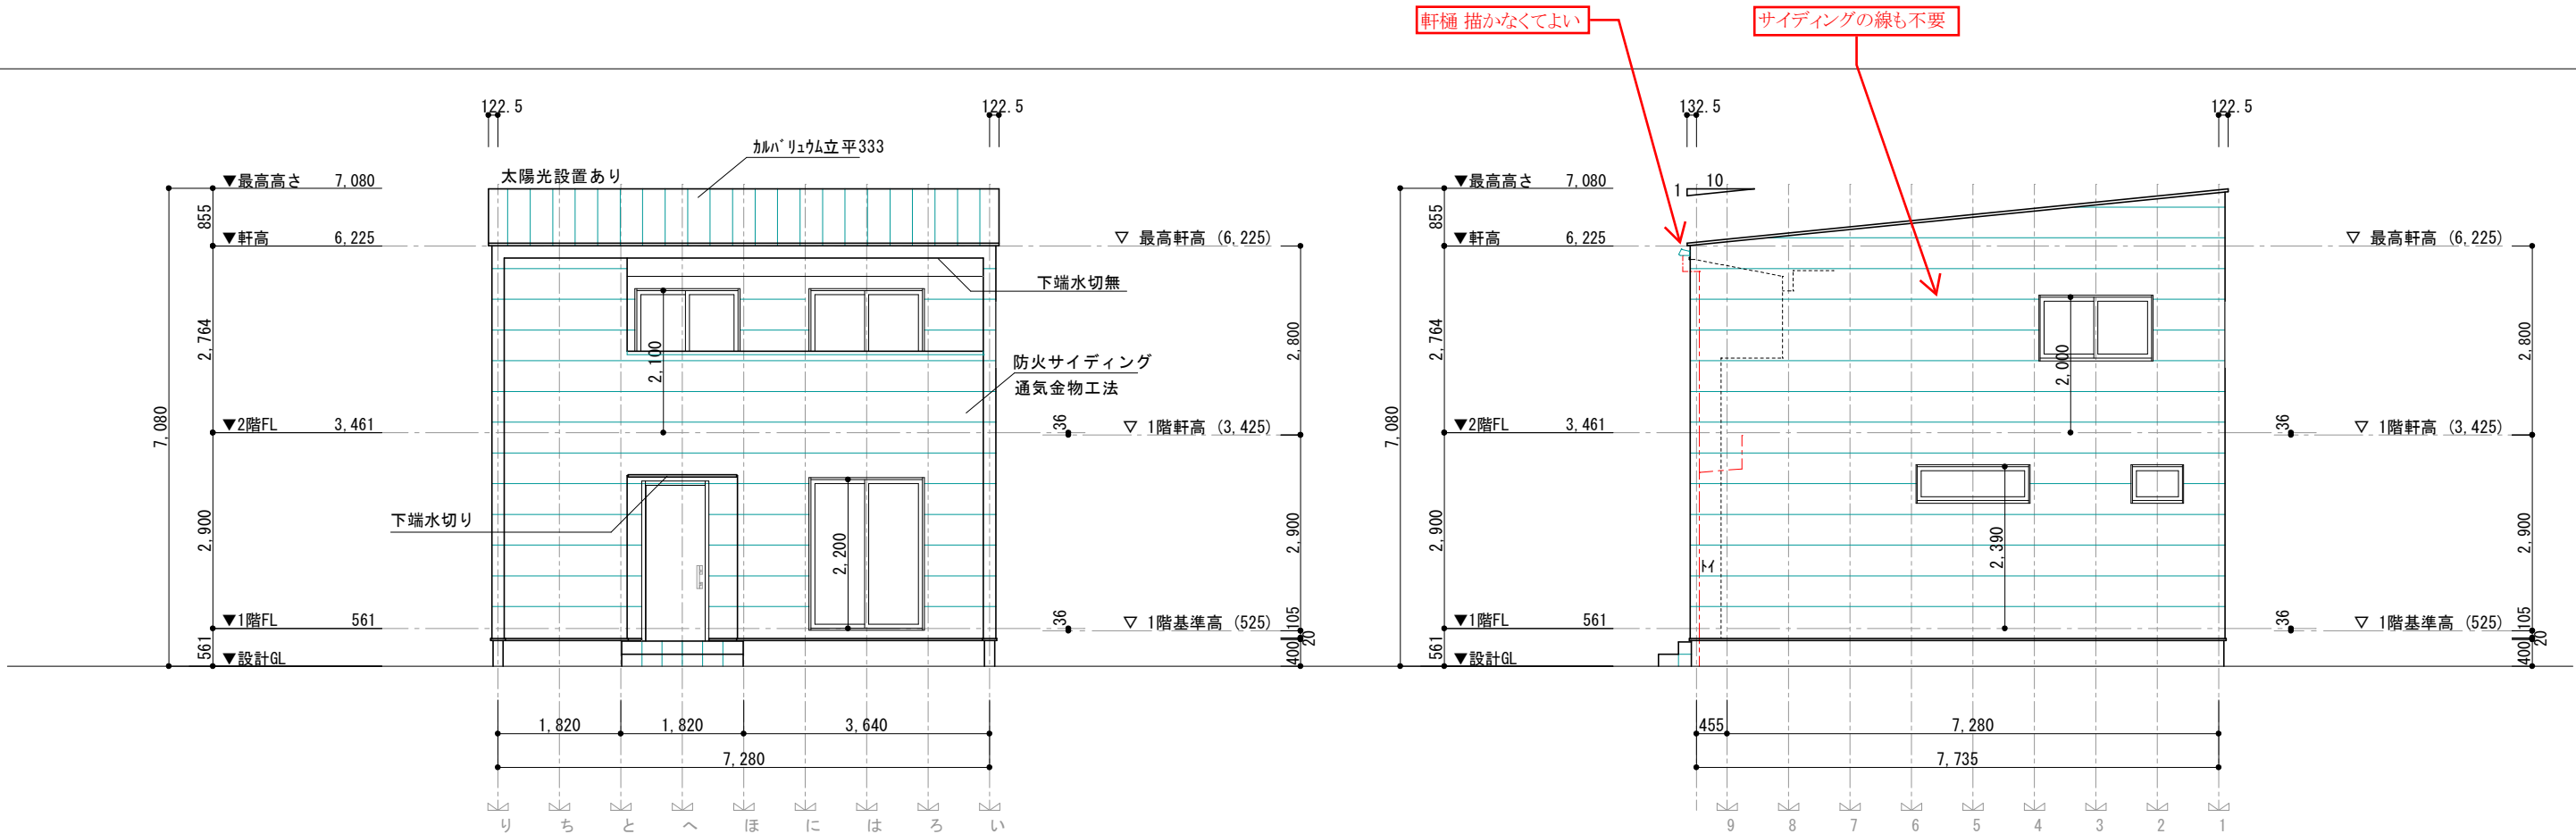


南側立面図 S=1/100

東側立面図 S=1/100

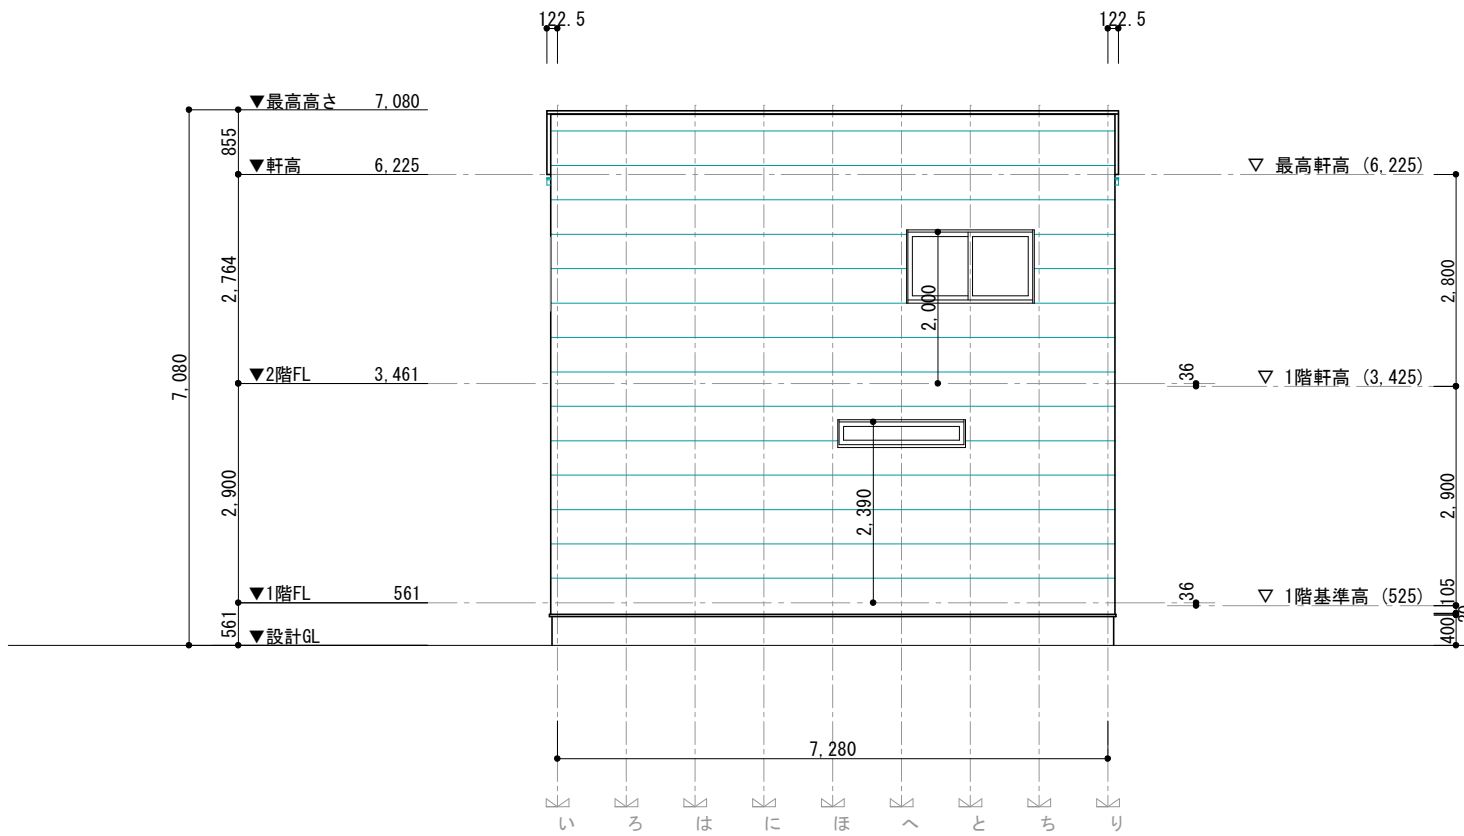

北側立面図 S=1/100

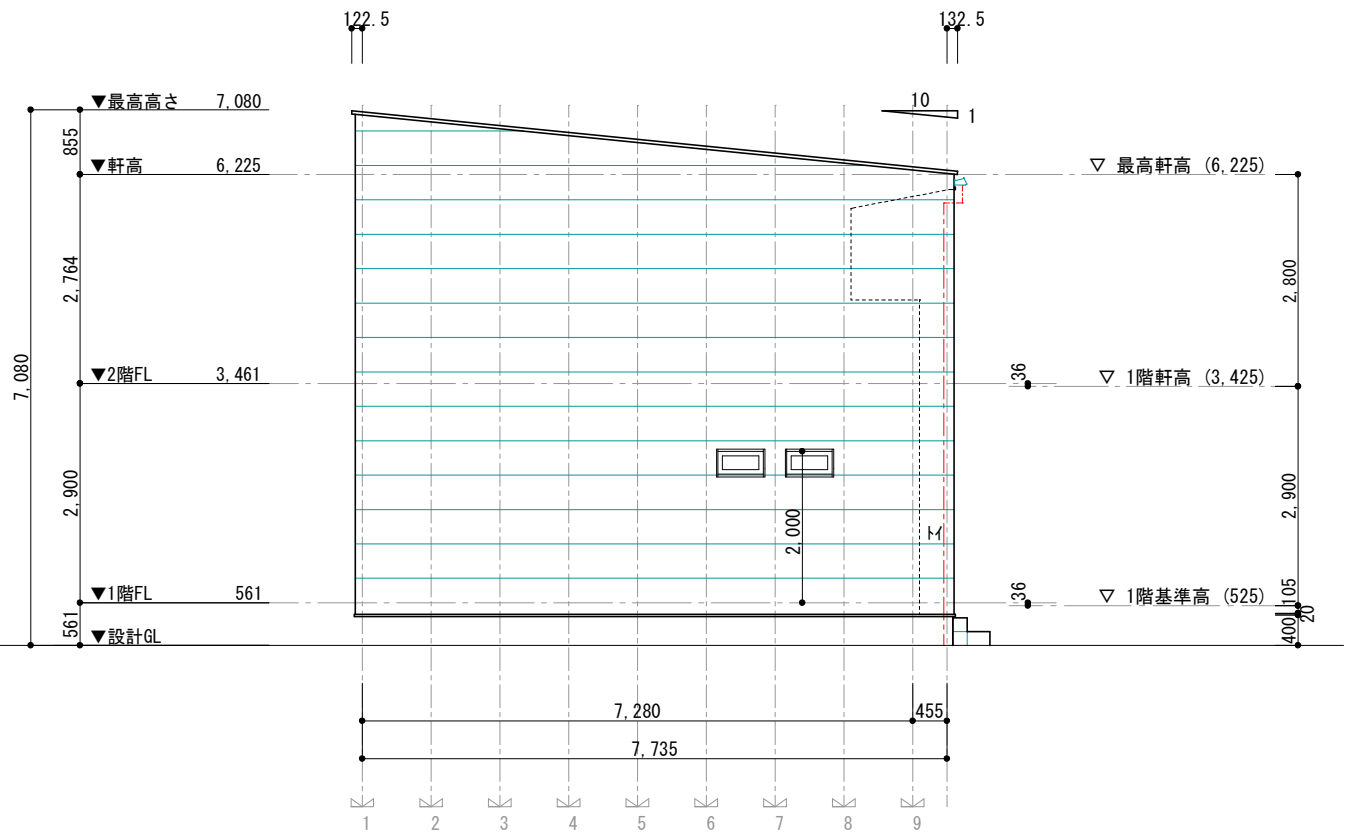

西側立面図 S=1/100

訂 正	浜 岡 一 級 総 合 設 計 事 務 所 一級建築士事務所 静岡県知事登録第 (10)2441 号 一級建築士 大臣登録第 365879 号 西原利昌	LIFEFUND PG HOUSE	株式会社 LIFEFUND InDesign office 一級建築士事務所 事務所登録 (2)第7595号 一級建築士登録 第179770号 鈴木 達男 〒432-8023 静岡県浜松市中央区鴨江3丁目70番23号	年 月 日	件 名		設計	IC	工事	図 番
				2024. 8. 22	PG有玉西分譲 新築工事		倉田	青島	4	
				縮 尺	図 名					
				1/100	立面図					