
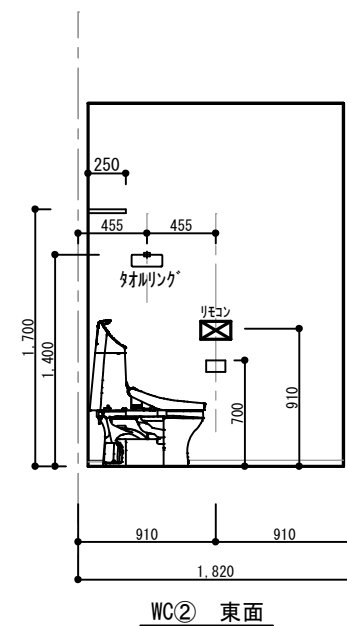
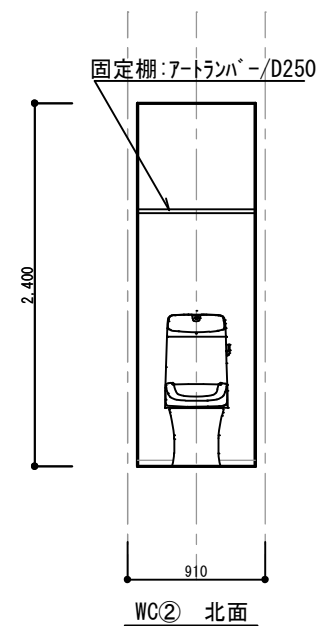
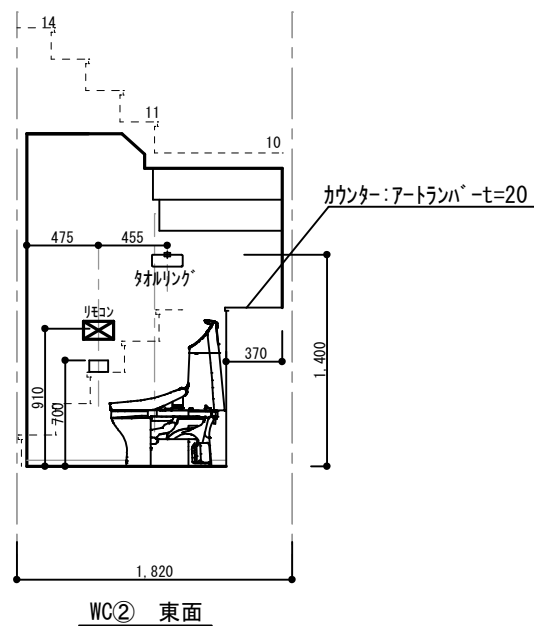
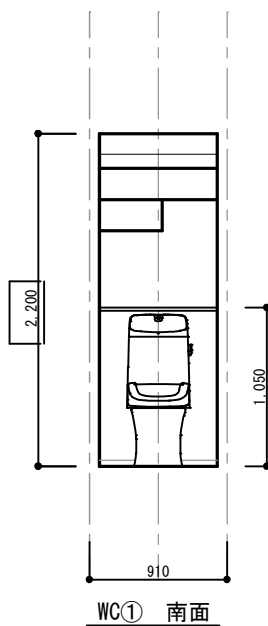
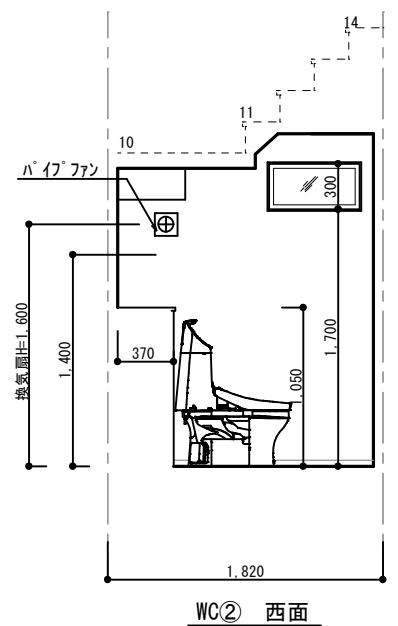
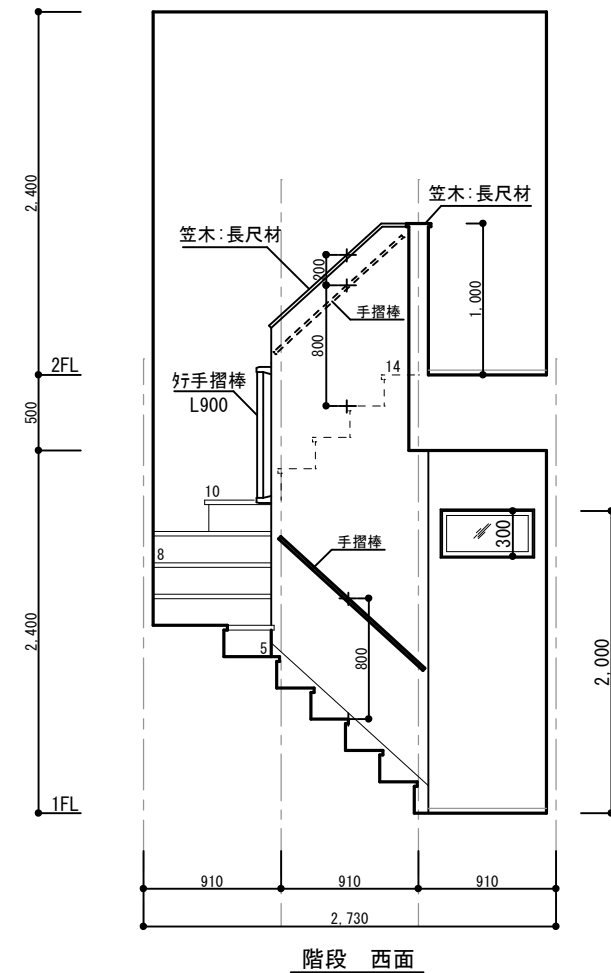
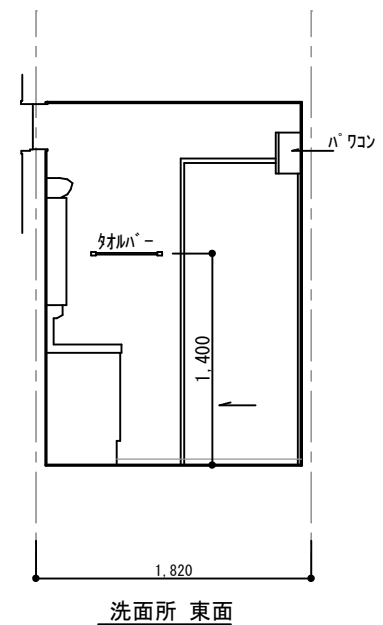
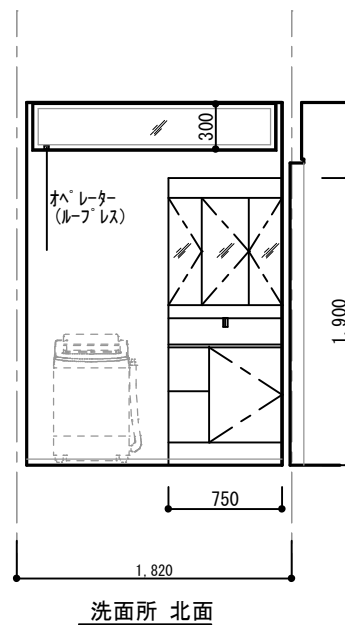
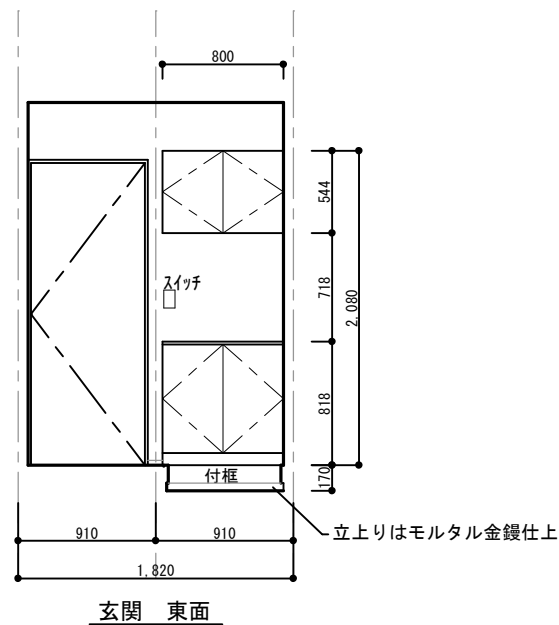
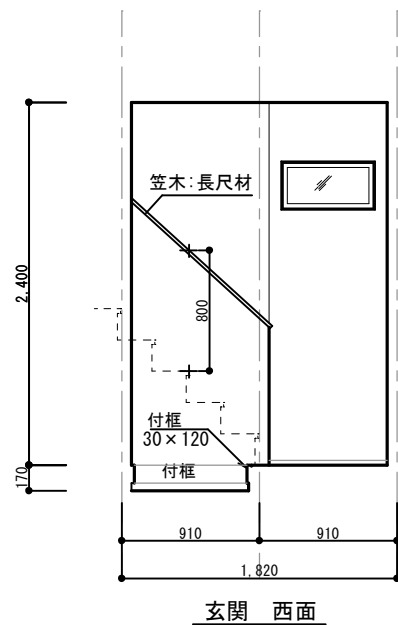


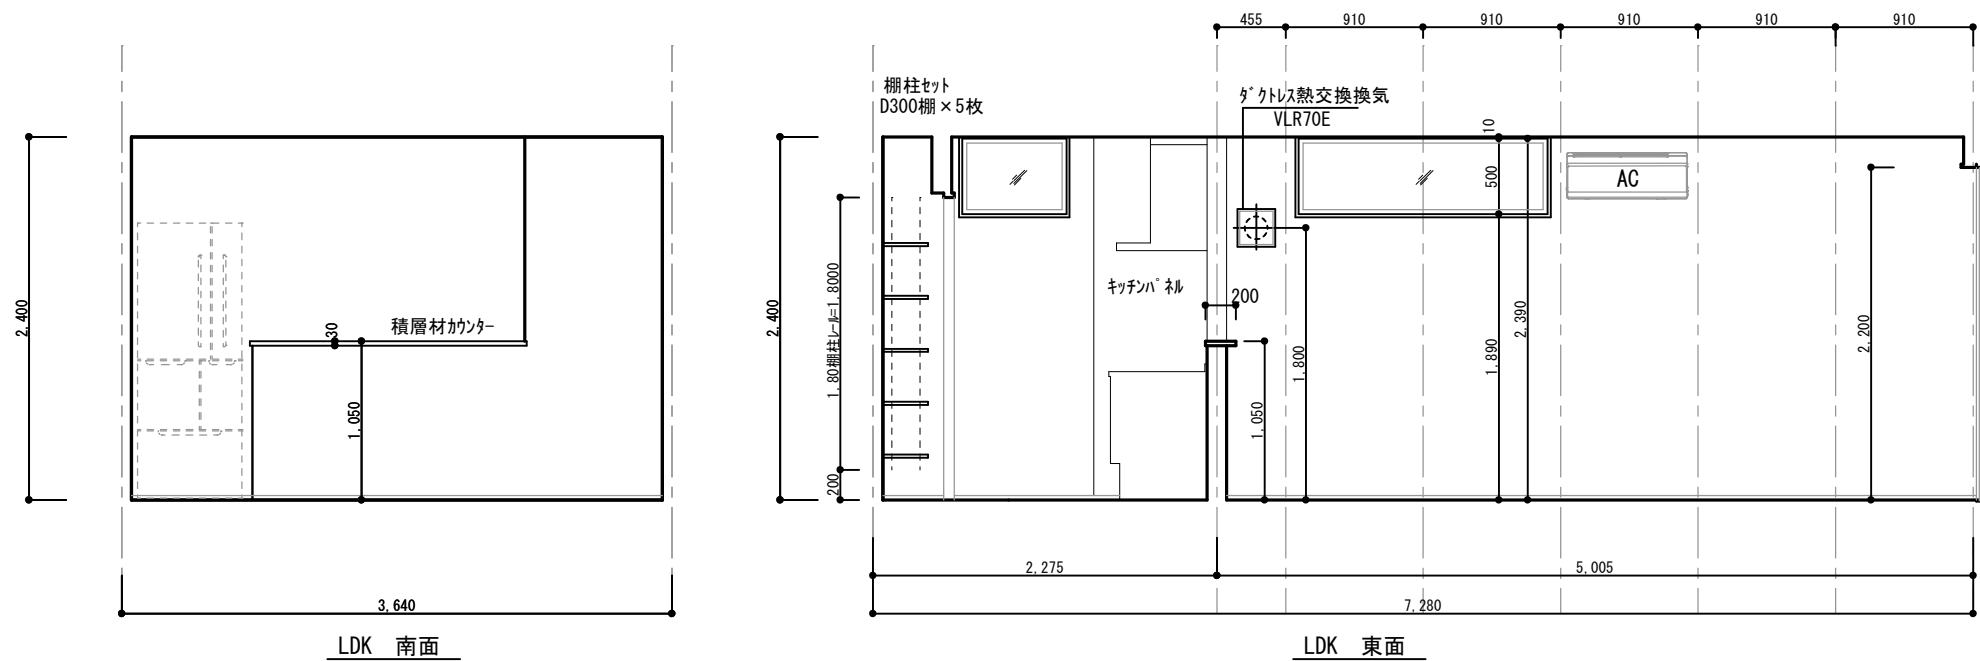

|    |                                                                           |                      |   |                                  |                                 |  |                                             |
|----|---------------------------------------------------------------------------|----------------------|---|----------------------------------|---------------------------------|--|---------------------------------------------|
| 訂正 | 浜岡 一級総合設計事務所<br>一級建築士事務所 静岡県知事登録第 (10)2441 号<br>一級建築士 大臣登録第 365879 号 西原利昌 | LIFEFUND<br>PG HOUSE | 株式会社 LIFEFUND InDesign office 一級建築士事務所<br>事務所登録 (2) 第7595号 一級建築士登録 第179770号 鈴木 達男<br>〒432-8023 静岡県浜松市中央区鴨江3丁目70番23号 | 年月日<br>2024. 8. 22<br>縮尺<br>1/30 | 件名<br>PG有玉西分譲 新築工事<br>図名<br>展開図 |  | 設計<br>倉田<br>IC<br><br>工事<br>青島<br>図番<br>6-1 |
|----|---------------------------------------------------------------------------|----------------------|---|----------------------------------|---------------------------------|--|---------------------------------------------|