


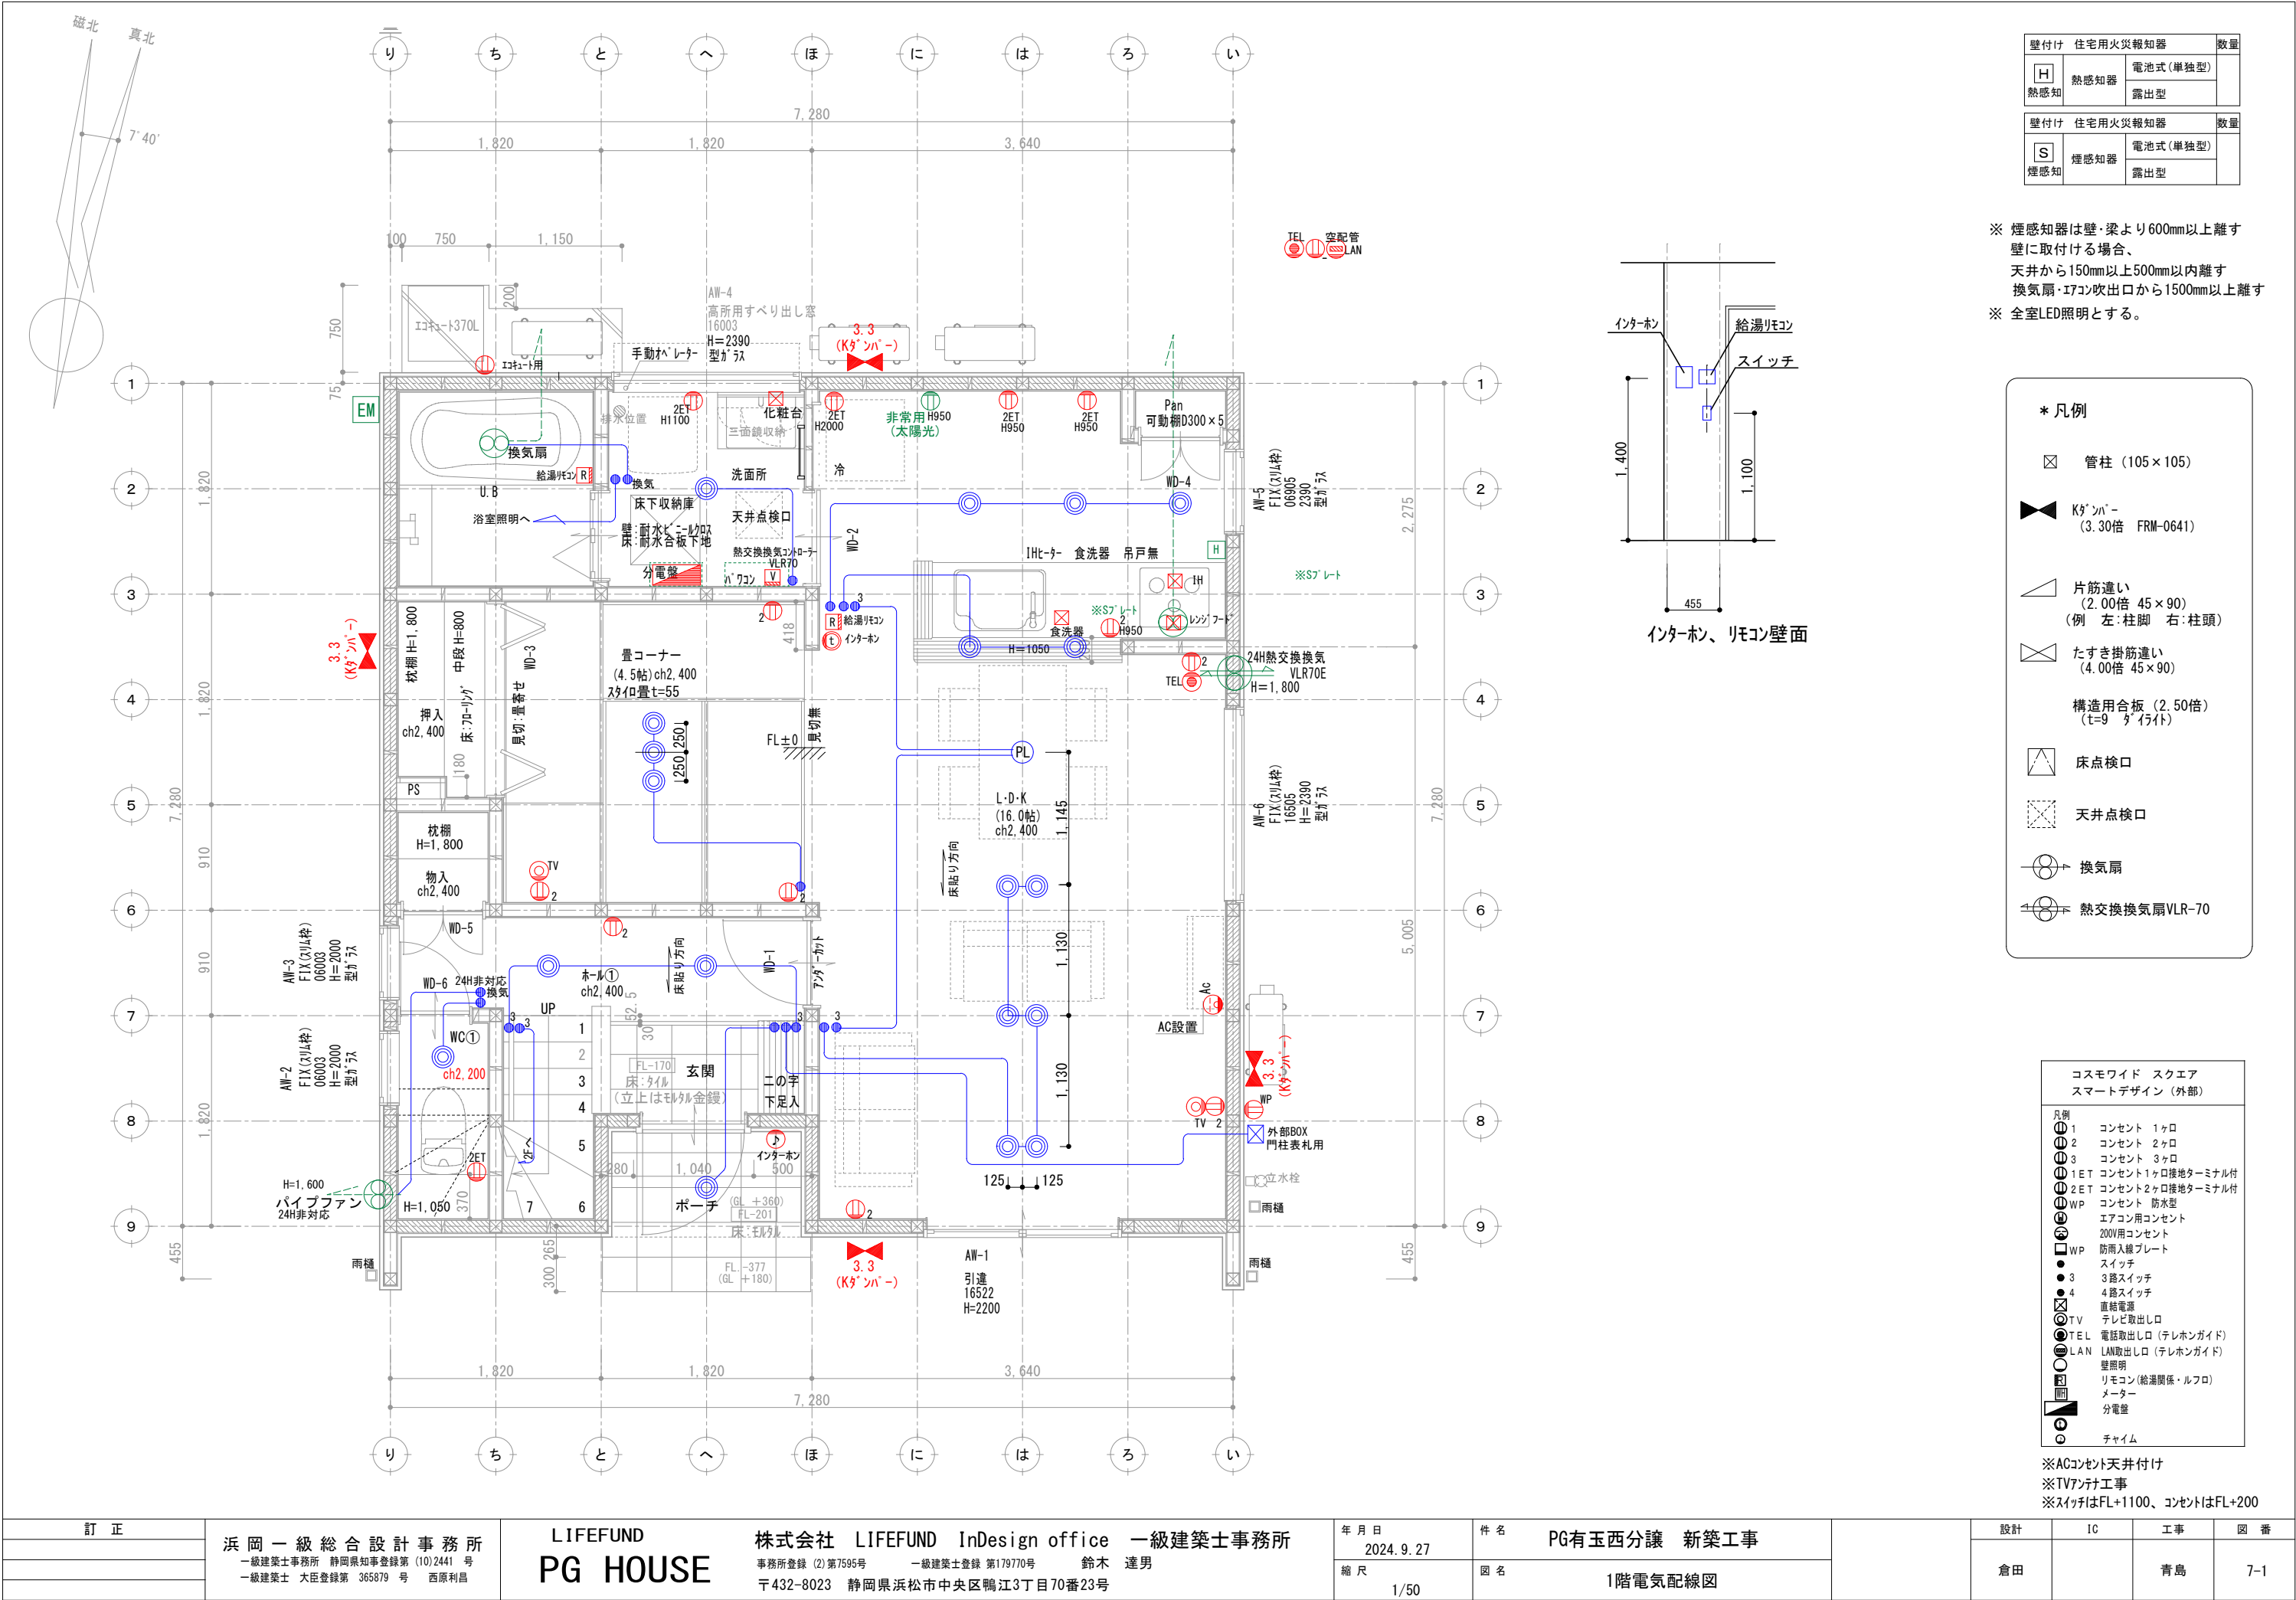


壁付け 住宅用火災報知器			数量
H	熱感知器	電池式(単独型)	
		露出型	

壁付け 住宅用火災報知器			数量
S	煙感知器	電池式(単独型)	
		露出型	

※ 煙感知器は壁・梁より600mm以上離す壁に取付ける場合、天井から150mm以上500mm以内離す換気扇・エアコン吹出口から1500mm以上離す

※ 全室LED照明とする。

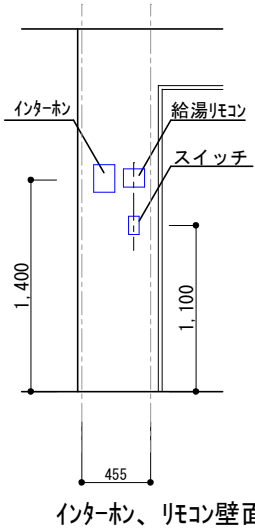

* 凡例	
管柱 (105×105)	
K ³ ンバー (3.30倍 FRM-0641)	
片筋違い (2.00倍 45×90) (例 左:柱脚 右:柱頭)	
たすき掛筋違い (4.00倍 45×90)	
構造用合板 (2.50倍) (t=9 タイラト)	
床点検口	
天井点検口	
換気扇	
熱交換換気扇VLR-70	

コスモワイド スクエア スマートデザイン (外部)	
凡例	
1	コンセント 1ヶロ
2	コンセント 2ヶロ
3	コンセント 3ヶロ
1ET	コンセント1ヶロ接地ターミナル付
2ET	コンセント2ヶロ接地ターミナル付
WP	コンセント 防水型
WP	エアコン用コンセント 200V用コンセント
WP	防雨入線プレート
WP	スイッチ
3	3路スイッチ
4	4路スイッチ
TV	直接電源 テレビ取出口
TEL	電話取出口 (テレホンガイド)
LAN	LAN取出口 (テレホンガイド)
壁照明	壁照明
リモコン	リモコン (給湯関係・ルフロ)
メーター	メーター
分電盤	分電盤
チャイム	チャイム

※ACコンセント天井付け

※TVアンテナ工事

※スイッチはFL+1100、コンセントはFL+200