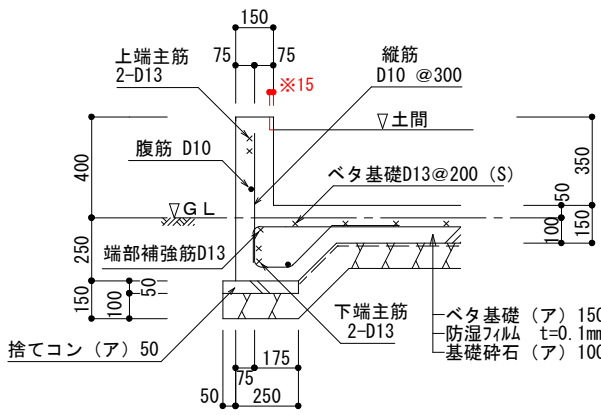
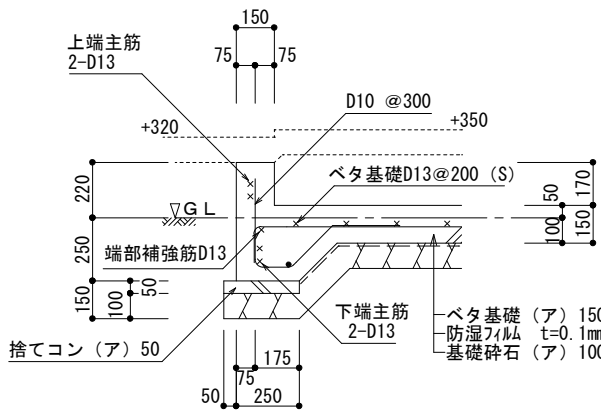
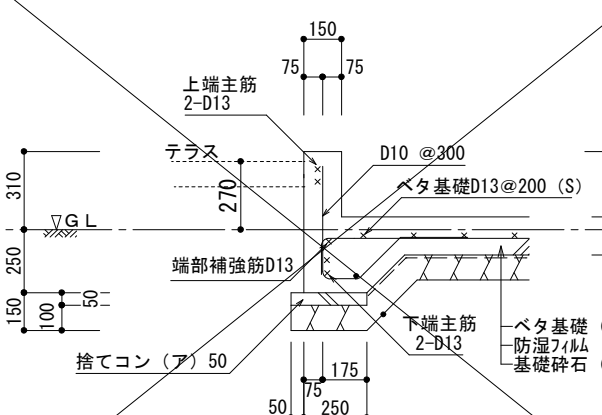
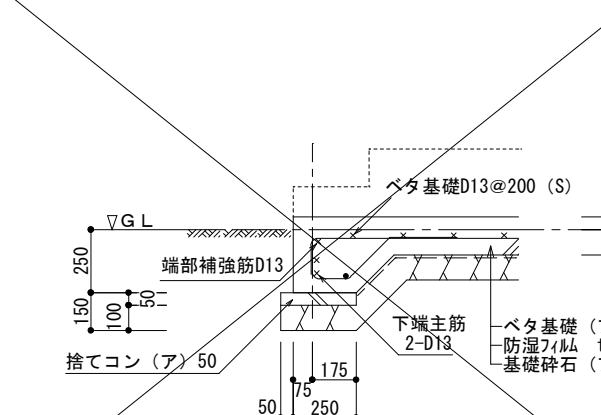
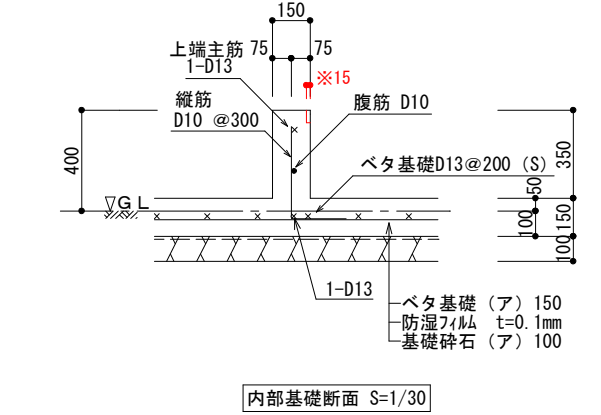
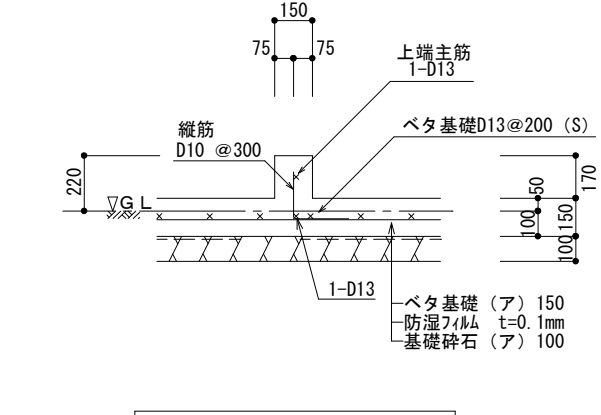
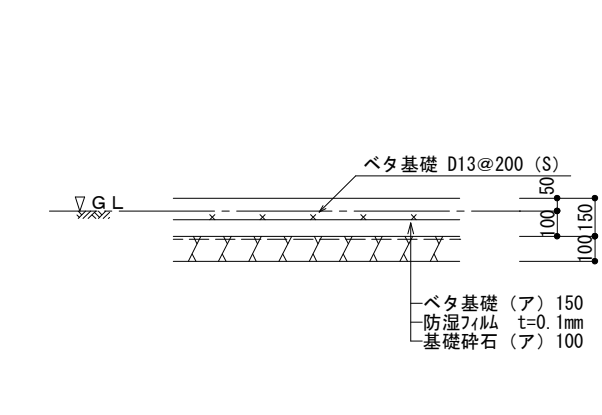
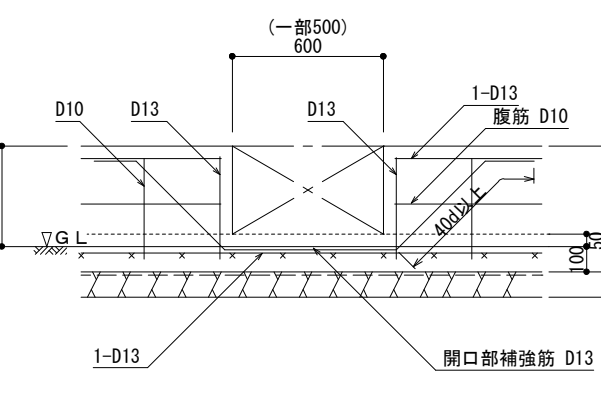
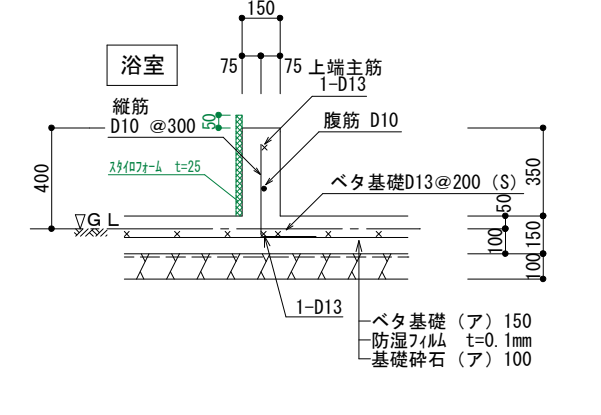
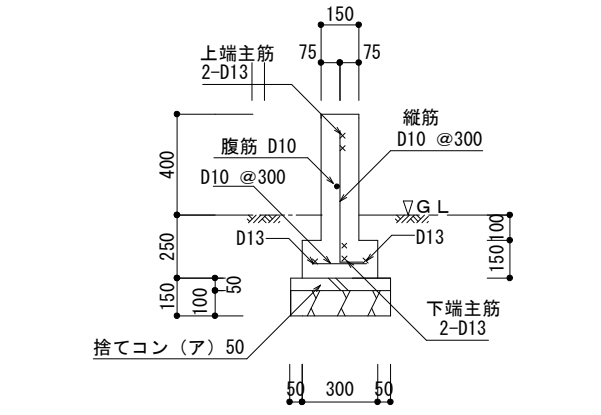
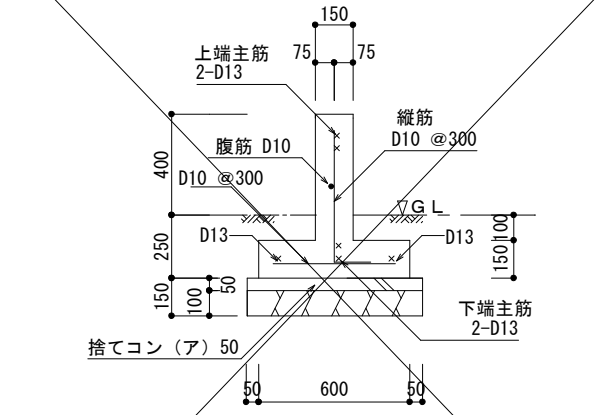


|   |   |   |   |                                |   |  |                                              |
|---|---|---|---|--------------------------------|---|--|----------------------------------------------|
|  <p>外周基礎断面 S=1/30</p> <p>※玄関内土間部分のみ15mm欠き込み</p>                               |  <p>ポーチ下 外周部基礎断面 S=1/30</p> <p>倉庫ドア下 外周部基礎断面 S=1/30</p>                          |  <p>土間納め勝手口ドア下 外周部基礎断面 S=1/30</p> |  <p>立上り無しの基礎断面 S=1/30</p>   |                                |   |  |                                              |
|  <p>内部基礎断面 S=1/30</p> <p>※玄関内土間部分のみ15mm欠き込み</p> <p>※注意：基礎伏図に特記のない内部基礎の場合</p> |  <p>ポーチ下 内周部基礎断面 S=1/30</p> <p>玄関ドア下 内周部基礎断面 S=1/30</p> <p>玄関内横断基礎断面 S=1/30</p> |  <p>ベタ基礎断面 S=1/30</p>            |  <p>人通口補強 S=1/30</p>   |                                |   |  |                                              |
|  <p>浴室内部基礎断面 S=1/30</p> <p>※注意：基礎伏図に特記のない内部基礎の場合</p>                        |  <p>布基礎A：袖壁用 基礎断面 S=1/30</p>                                                   |  <p>布基礎B：底用独立 基礎断面 S=1/30</p>   | <table><tr><td>基礎の寸法<br/>及び<br/>配筋の検証方法</td><td>基礎立上り配筋は、<br/>(財)日本住宅・木材技術<br/>センター発行のスパン表<br/>(増補版)による。<br/>ベタ基礎スラブ配筋は、<br/>まもりすまい保険設計施工<br/>基準同解説のベタ基礎配筋表<br/>による。具体的な寸法・配<br/>筋は基礎詳細図参照。</td></tr></table> <p>鉄筋断面表記</p> <p>●・・・D10を示す。<br/>×・・・D13を示す。</p> <p>※使用しない断面は×を記入。</p> | 基礎の寸法<br>及び<br>配筋の検証方法         | 基礎立上り配筋は、<br>(財)日本住宅・木材技術<br>センター発行のスパン表<br>(増補版)による。<br>ベタ基礎スラブ配筋は、<br>まもりすまい保険設計施工<br>基準同解説のベタ基礎配筋表<br>による。具体的な寸法・配<br>筋は基礎詳細図参照。 |  |                                              |
| 基礎の寸法<br>及び<br>配筋の検証方法   | 基礎立上り配筋は、<br>(財)日本住宅・木材技術<br>センター発行のスパン表<br>(増補版)による。<br>ベタ基礎スラブ配筋は、<br>まもりすまい保険設計施工<br>基準同解説のベタ基礎配筋表<br>による。具体的な寸法・配<br>筋は基礎詳細図参照。                                |   |   |                                |   |  |                                              |
| 訂正   | 浜岡一級総合設計事務所<br>一級建築士事務所 静岡県知事登録第(10)2441号<br>一級建築士 大臣登録第365879号 西原利昌                                                                                               | LIFEFUND<br>PG HOUSE                                                                                                 | 株式会社LIFEFUND InDesign office 一級建築士事務所<br>事務所登録 (2)第7595号 一級建築士登録 第179770号 鈴木 達男<br>〒432-8023 静岡県浜松市中央区鴨江3丁目70番23号   | 年月日<br>2024.8.22<br>縮尺<br>1/30 | 件名<br>PG有玉西分譲 新築工事<br>図名<br>基礎断面リスト                                                                                                 |  | 設計<br>倉田<br>I C<br><br>工務<br>青島<br>図番<br>B-2 |