


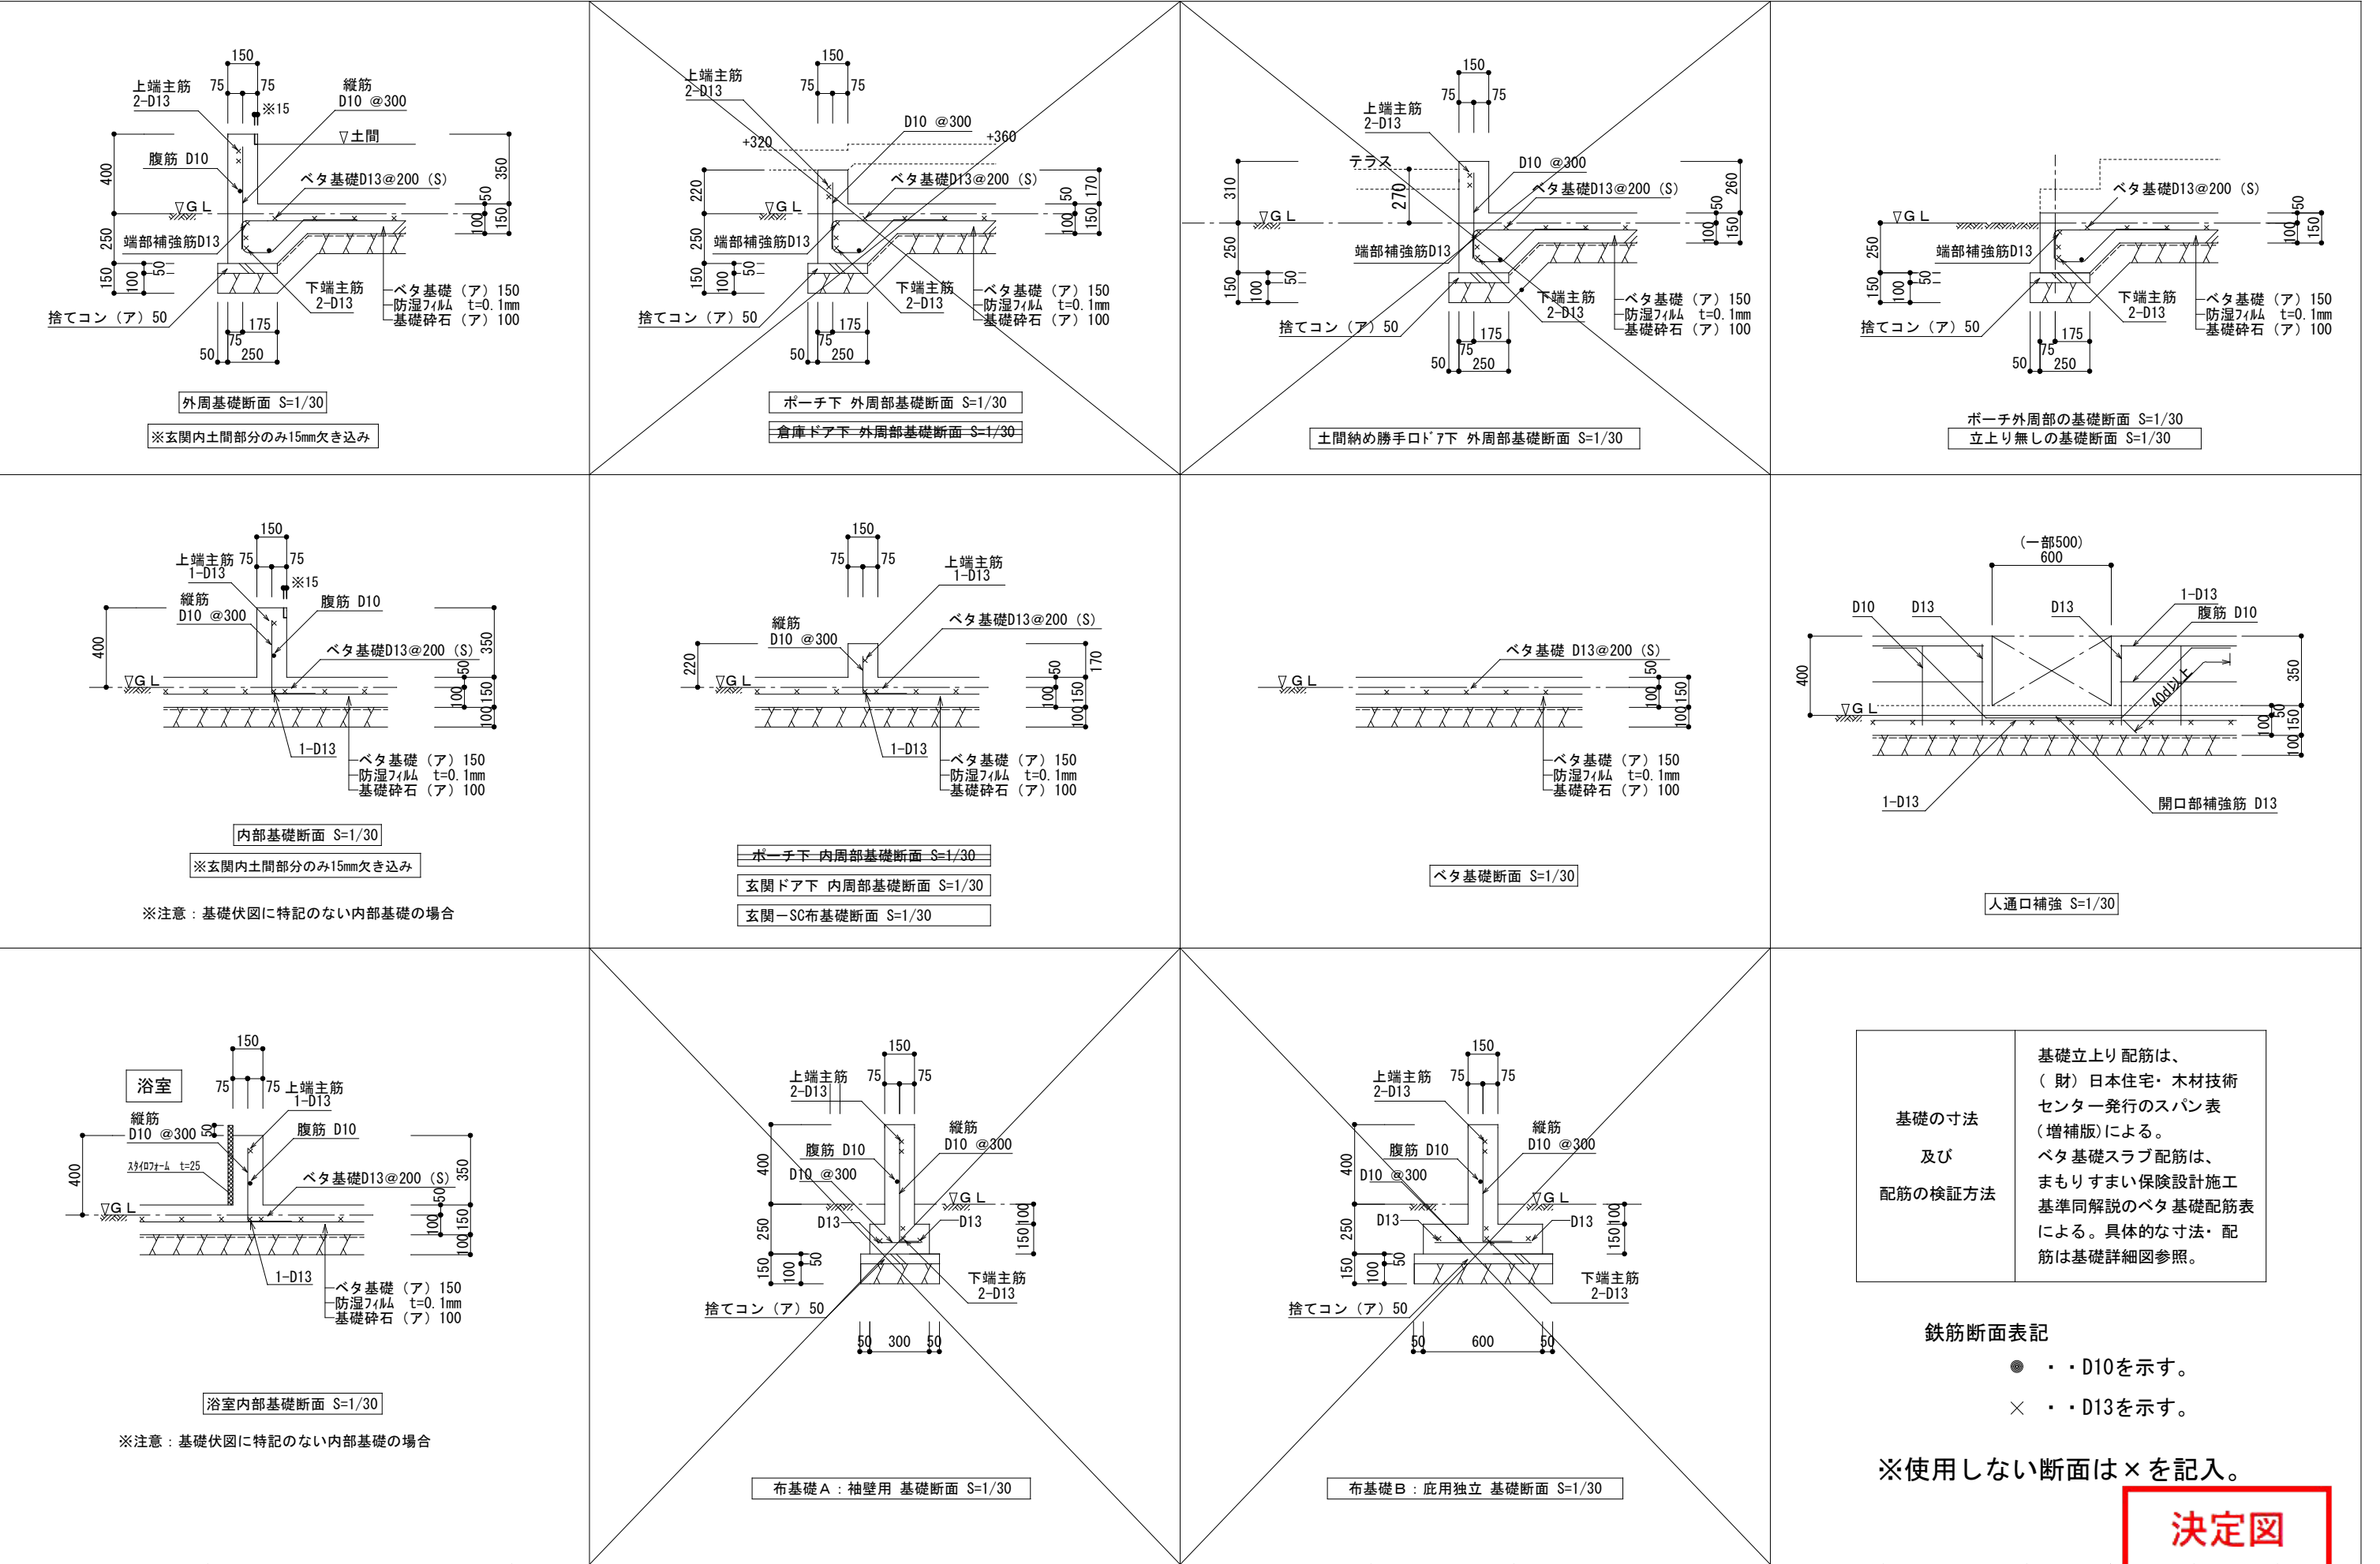

決定図

訂正	浜岡 一級総合設計事務所		株式会社 LIFEFUND InDesign office 一級建築士事務所	年月日	件名	設計	施工	図番
	一級建築士事務所 静岡県知事登録第 (10)2441 号			2024. 11. 23	伊藤友章様邸 新築工事			
	一級建築士 大臣登録第 365879 号 西原利昌			縮尺	図名			
				1/30	基礎断面リスト	倉田	青島	B-2