

| ■ 仕 様                                                     |         |   |  | ■ HEAT20 G1                                          |  |
|-----------------------------------------------------------|---------|---|--|------------------------------------------------------|--|
| 断熱工事                                                      |         | ■ 床:カネライトフォーム t65                      ■ 土間床等の外周:スタイロフォームAT t25<br>■ 壁:アクアフォームLITE吹付 t85              ■ 天井:アクファフォームLITE吹付 t170 |  |                                                      |  |
| 床下換気                                                      |         | ■ 基礎パッキン                      JOTO              (玄関・UB周り:気密基礎パッキン)                                                             |  |                                                      |  |
| 防虫防蟻                                                      |         | ■ 土壌処理・木部                      ガントナーMC                                                                                         |  |                                                      |  |
| ■ 外 部 仕 上 表                                               |         |   |  | ■ 22条地域                                              |  |
| 部位                                                        |         | 仕上・仕様・メーカー   |  | 色番・品番                                                |  |
| 屋根                                                        |         | ■ ガルバリウム鋼板(t0.35)UK立平 ニスクカラーPro GH<br>軒先通気金物 日本住環境株式会社【REV-15】                                                                 |  | GHK01 Sブラック                                          |  |
| パラペット笠木                                                   |         | ■ なし   |  |                                                      |  |
| 破風・鼻隠                                                     |         | ■ なし   |  |                                                      |  |
| 雨樋                                                        | (軒樋)    | ■ Panasonic サーフেসケアFS-I型   |  | ブラック                                                 |  |
|                                                           | (縦樋)    | ■ Panasonic S30角樋   |  | ブラック                                                 |  |
| 軒天                                                        | 屋根軒     | ■ なし   |  |                                                      |  |
|                                                           | ポーチ軒    | ■ 神島化学 t= 6mm 軒天ボード エンボス   |  | Wチャコールブラック                                           |  |
|                                                           | バルコニー軒  | ■ なし   |  |                                                      |  |
| オーバーハング水切り                                                |         | ■ ガルバリウム鋼板 ※外壁合わせ JOTO:HF-A3550                                                                                                |  | ブラック                                                 |  |
| 外壁<br>通気金物(15mm)<br>※下地面材:タイガーEXハイパー<br>防火認定 PC030BE-4028 | ■メイン    | ニチハ エモンエクセラード16 Vシリーズ リーガストーン調V                                                                                                |  | ランダムMGブラック                                           |  |
|                                                           | ■アクセントA | なし   |  |                                                      |  |
|                                                           | ■アクセントB | なし   |  |                                                      |  |
| 玄関ポーチ                                                     |         | ■ 床 玄関タイルに同じ   |  | -                                                    |  |
| 基礎                                                        |         | ■ 立上り巾木: モルタル刷毛引き   |  | -                                                    |  |
| 基礎水切り金物                                                   |         | ■ JOTO鋼板製 防鼠材付き水切り JOTO:WMF-N35                                                                                                |  | ブラック                                                 |  |
| バルコニー                                                     | 床・内壁    | ■ なし   |  | -                                                    |  |
|                                                           | 笠木      | ■ なし   |  |                                                      |  |
| 外部建具                                                      |         | ■ LIXIL EW(アルゴンガス高遮熱仕様LowE複層ガラス グリーン)<br>・SD、TSで記載がないものは、オペレーターハンドルとする<br>・オペレーター付サッシは固定網戸とする<br>・グレモンハンドル式サッシの選択箇所は可動網戸とする    |  | 外観 ブラック<br>内観 ホワイト<br>※樹脂パッキン・網戸付                    |  |
| シャッター                                                     |         | ■ なし   |  |                                                      |  |
|                                                           |         |   |  |                                                      |  |
| 玄関扉                                                       |         | ■ LIXIL ジエスタ2 K2仕様<br>LIXILファミロック タグキー×3 (電池式)                                                                                 |  | ドア型: M17 型<br>ドア色: カームブラック<br>ハンドル: S型ハンドル<br>色 ブラック |  |
|                                                           |         |   |  |                                                      |  |
| 外部物干し棟                                                    |         | ■   |  |                                                      |  |
| 外部フック棟                                                    |         | ■ ポーチ:傘フック(Vik) 南面:タープフック   |  |                                                      |  |
|                                                           |         |   |  |                                                      |  |
| 換気フード                                                     |         | ■ 局所換気扇(トイレ 浴室 キッチンフード)<br>防火ダンパー無                                                                                             |  | 外気フード: ブラック                                          |  |
|                                                           |         | ■ ダクトレス熱交換換気システム (日本スティーベル株式会社)<br>VLR-70E                                                                                     |  | 外気フード: B ブラック<br>室内パネル ホワイト                          |  |
|                                                           |         | 防火ダンパー無   |  |                                                      |  |


| ■ 構 造 概 要   |                  |                                                                      |   |                                               |
|-------------|------------------|----------------------------------------------------------------------|---|-----------------------------------------------|
| 基礎          | ■ RCベタ基礎コンクリート   |                                                                      |   |                                               |
| 通し柱・管柱      | ■ 構造用集成材 105×105 |                                                                      | 間柱   | ■ 集成材                                         |
| 土台          | ■ 桧 105×105      | 大引き ■ 桧 90*90                                                        | 筋交い   | ■ 構造用製材 火打梁 ■ 鋼製火打(当社基準により米松あり)               |
| 桁・梁         | ■ 構造用製材及び集成材     |                                                                      | 制震装置   | ■ Kダンパー (株)アイ・エム・エー                           |
| ■ 設 備 装 着 品 |                  |                                                                      |   |                                               |
| 住宅設備        | 部位               | メーカー                                                                 | 商品名 ※ 詳細は見積り、プレゼン参照                                                                                      | 見積りNo. (日付)                                   |
|             | キッチン             | LIXIL                                                                | ■ ES ペニンシュラ型                                                                                             | 見積り番号 : A24105290035-012-2<br>(日付) 2024.11.27 |
|             | バックカウンタ          | LIXIL                                                                | ■ ES L1800(W900スライドストッカー×2)<br>引き出しTレール仕様(扉 ソリッドホワイト) 吊戸棚H500(ライトグレン)                                    | 見積り番号 : A24105290035-012-3<br>(日付) 2024.11.27 |
|             | 浴室               | LIXIL                                                                | ■ AX1620 洗い場広タイプ ドア仕様                                                                                    | 見積り番号 : A24105290035-012-1<br>(日付) 2024.11.27 |
|             | 1Fトイレ            | LIXIL                                                                | ■ ベーシアシャワートイレ 白 ● タオル掛け: なし<br>タンク手洗 無し ● 紙巻き器: なし(支給品取付)                                                | 見積り番号 : A24105290035-012-5<br>(日付) 2024.11.27 |
|             | 2Fトイレ            | LIXIL                                                                | ■ ベーシアシャワートイレ 白 ● タオル掛け: なし(支給品取付)<br>タンク手洗 有り ● 紙巻き器: なし(支給品取付)                                         | 見積り番号 : A24105290035-012-6<br>(日付) 2024.11.27 |
|             | 洗面台              | LIXIL                                                                | ■ EV W900(D500タイプ) 扉:グロスホワイト<br>[ 引出しタイプ シングルハンドシャワー スタンダードLED三面鏡<br>その他 トールキャビネット300 ● タオル掛け: なし(支給品取付) | 見積り番号 : A24105290035-012-4<br>(日付) 2024.11.27 |
|             | スロップシンク          | LIXIL                                                                | ■ S-17/BW1 シングルバー混合水栓SF-WM435SY(170)                                                                     | A24105290035-012-7<br>2024.11.27              |
|             |                  |                                                                      |   |                                               |
| 給排水設備       | 給湯器              | ■ エコキュート370L Panasonic NSシリーズ スタンダードモデル 追い焚きフルオート                    |   |                                               |
|             | 排水               | ■ 合併浄化槽 5人槽 ポンプアップ無                                                  |   |                                               |
|             | 外水栓              | ■ 1 カ所 (平面図参照)                                                       | ■ 外部立栓柱: PVC製 水栓柱12型グレーシリーズ【前澤化成工業】                                                                      |                                               |
|             | 外部ガーデンパン         | ■ 無し                                                                 |   |                                               |
|             | その他              | ■ 洗濯機用単水栓: 緊急止水弁付 ■ 洗濯機用排水: トラップ金物(標準)<br>■ 排水さや管(長期優良住宅仕様)          |   |                                               |
| ガス配管設備      |                  | ■ あり(LPG) (配置図・平面図参照 ※乾太くん用)                                         |   |                                               |
| 電気設備        | インターホン           | ■ パナソニック VL-SZ30KL                                                   |   |                                               |
|             | TVアンテナ           | ■ UHF + BS・110度CS/CSアンテナ [2K・4K・8K対応] ■ブラック ※電波状況によりホワイトになる可能性あり     |   |                                               |
|             | エアコン             | ■ 設置場所:                                                              |   |                                               |
|             | ソーラー<br>※標準搭載    | ■ あり(Qセルズ) 12 枚 5.28 KW Re.RISE-G3 440 (1722×1134×30)<br>■ 屋外パワコン 西面 |   |                                               |
| その他         |                  |                                                                      |   |                                               |


決定図

決定図

|  |  |                              |  |   |  |            |              |  |  |    |    |    |     |
|--|--|------------------------------|--|---|--|------------|--------------|--|--|----|----|----|-----|
|  |  | 浜 岡 一 級 総 合 設 計 事 務 所        |  |  株式会社 LIFEFUND InDesign office 一級建築士事務所 |  | 年 月 日      | 件 名          |  |  | 設計 | IC | 工務 | 図 番 |
|  |  | 一級建築士事務所 静岡県知事登録第 (10)2441 号 |  | 事務所登録 (2)第7595号 一級建築士登録 第179770号 鈴木 達男                                                                                       |  | 2024.11.29 | 伊藤友章 様邸 新築工事 |  |  | 倉田 |    | 青島 | 1-1 |
|  |  | 一級建築士 大臣登録第 365879 号 西原利昌    |  | 〒432-8023 静岡県浜松市中央区鴨江3丁目70番23号                                                                                               |  | 縮尺         | 図面           |  |  |    |    |    |     |
|  |  |                              |  |   |  |            | 仕上表 1        |  |  |    |    |    |     |



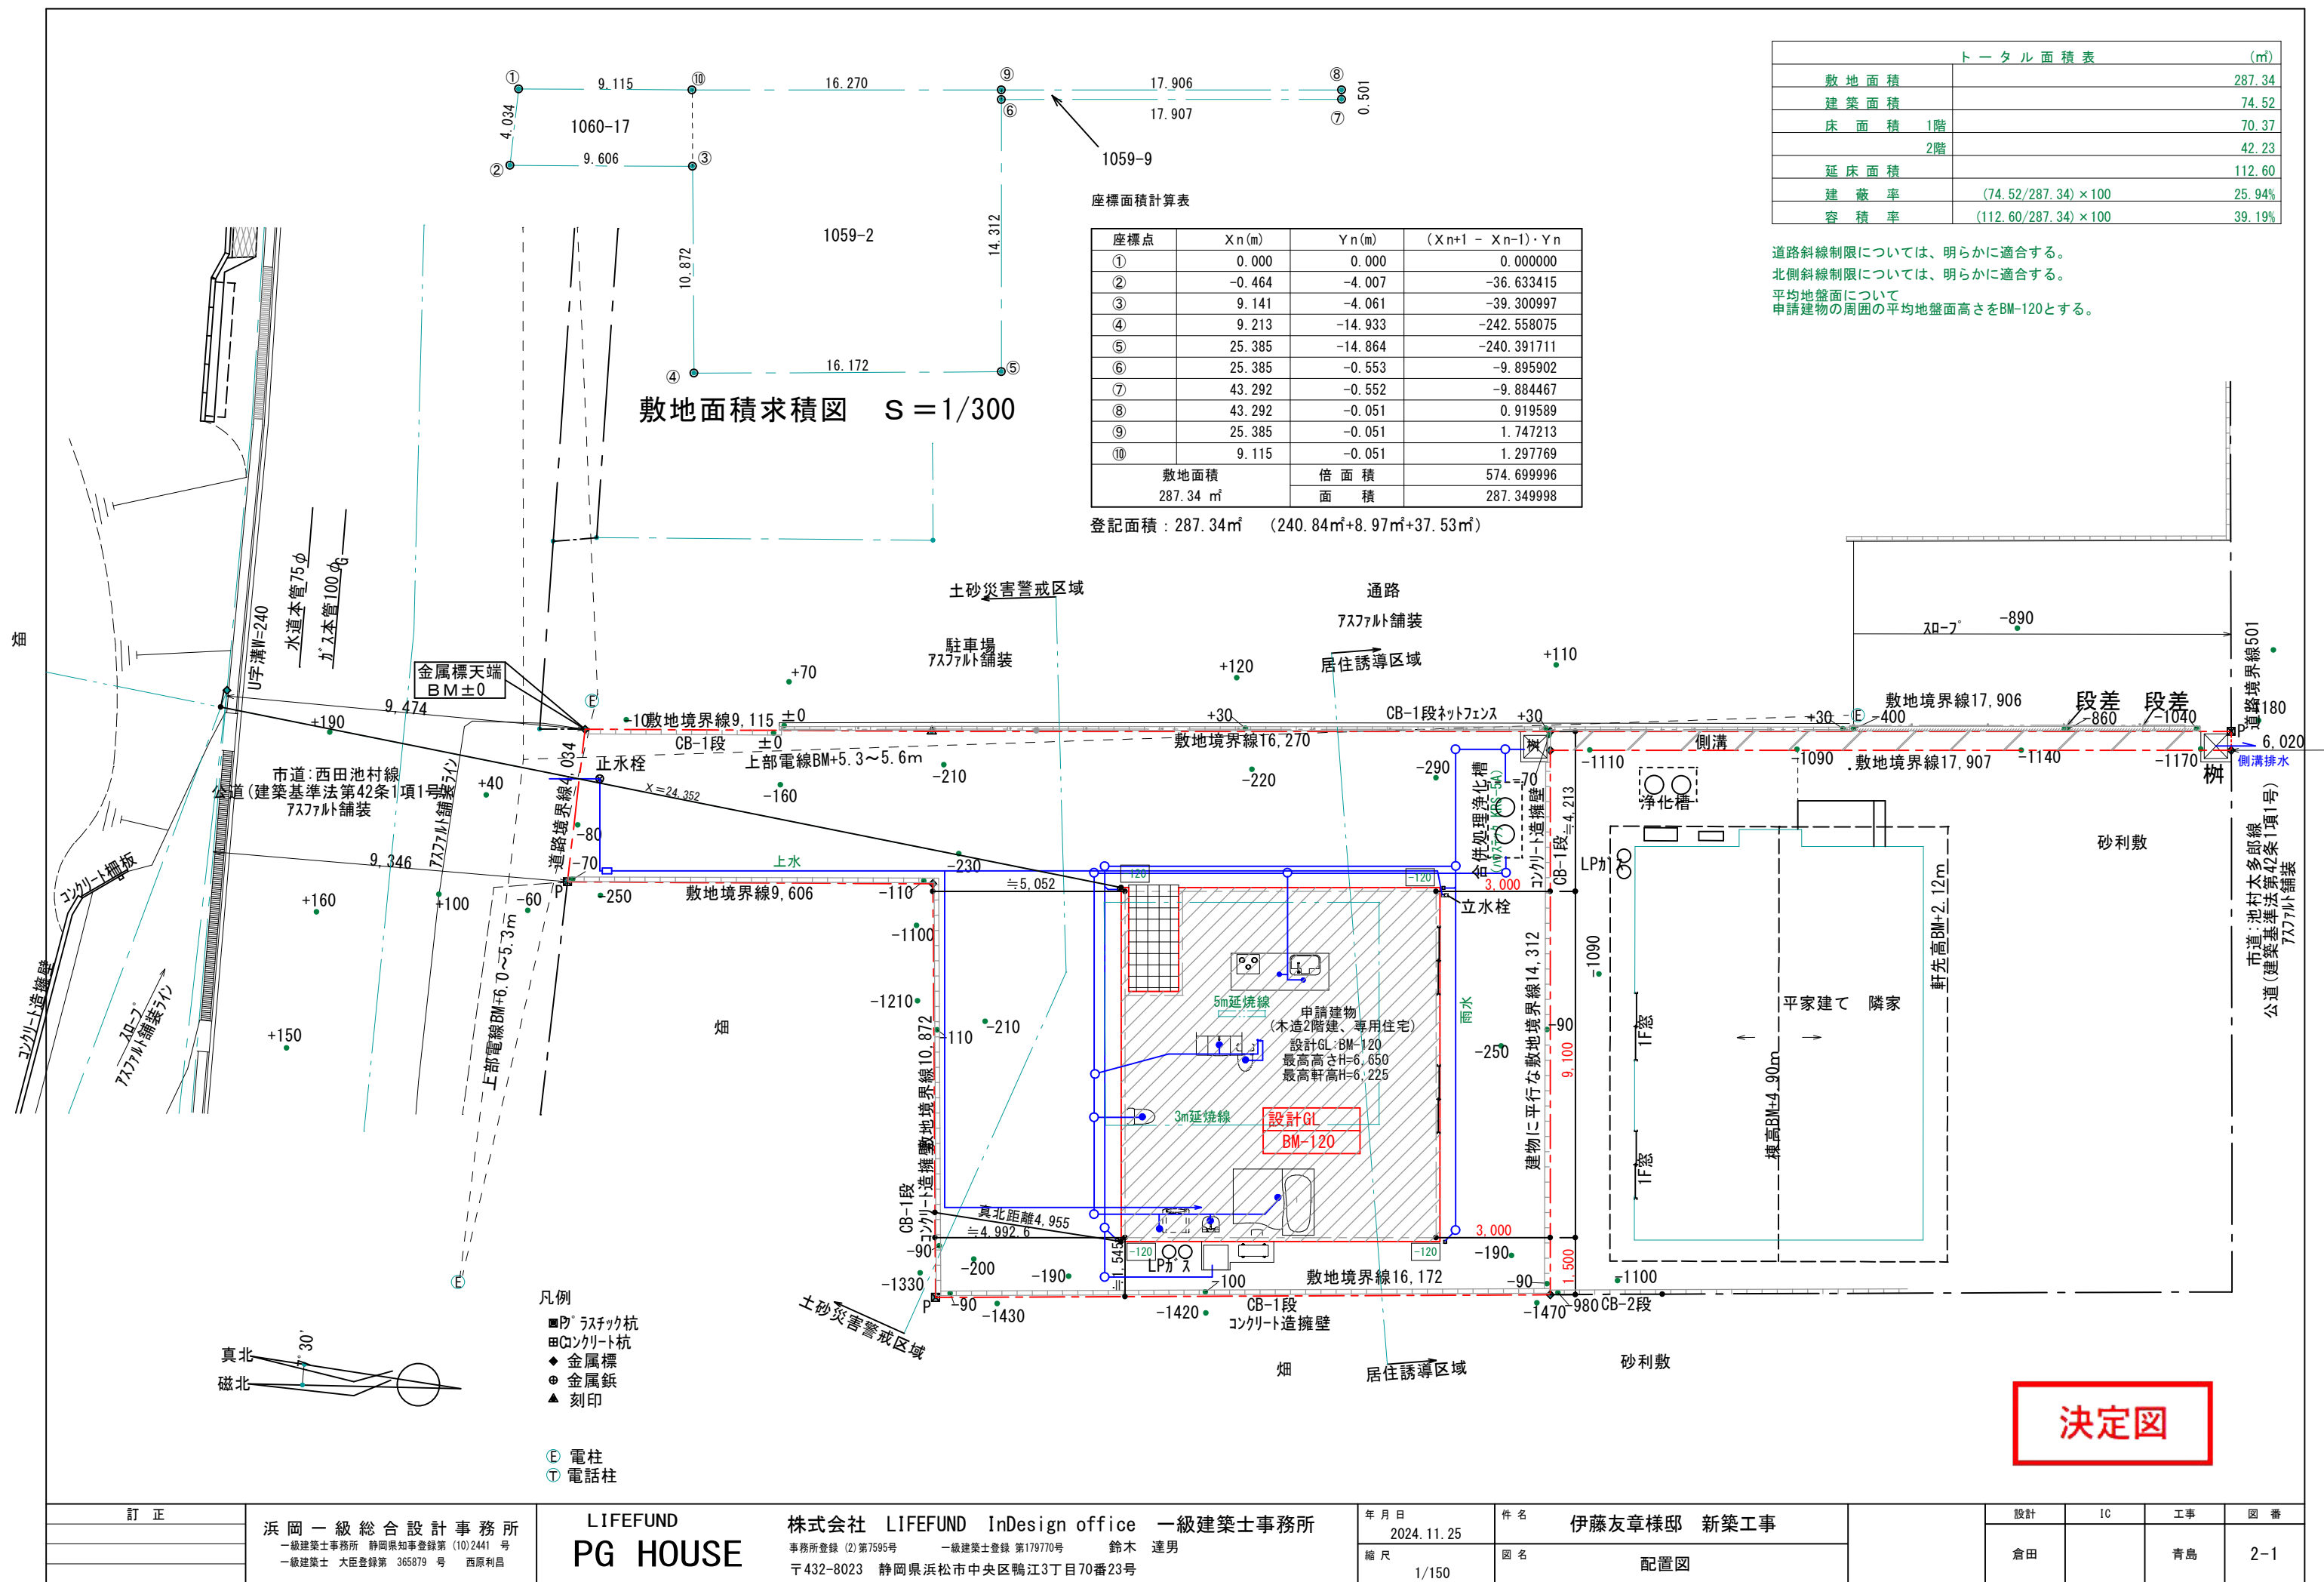

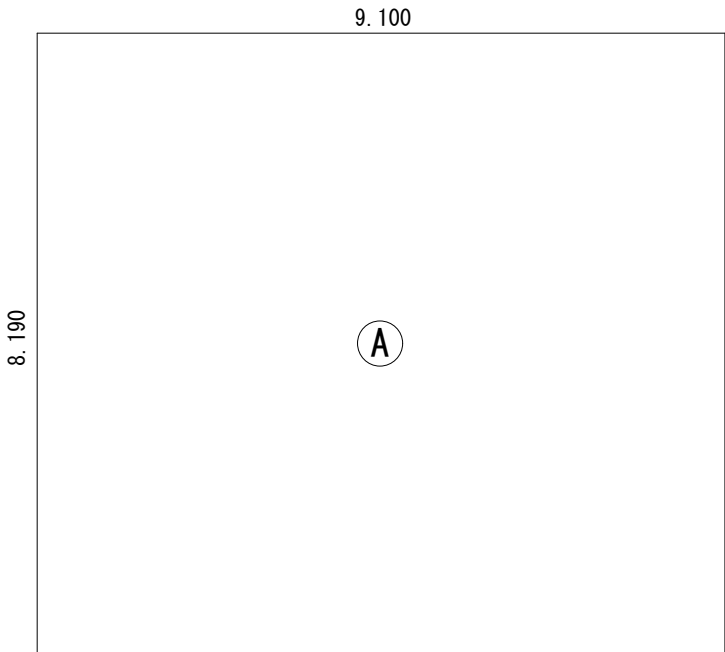


建築面積求積図 S=1/100

建築面積求積表

| 番号 | 計算式           | (m) | 面積 (㎡)          |
|----|---------------|-----|-----------------|
| A  | 9.100 × 8.190 |     | 74.529          |
|    |               |     |                 |
|    |               |     |                 |
| 合計 |               |     | 74.529<br>74.52 |

(22.5坪)

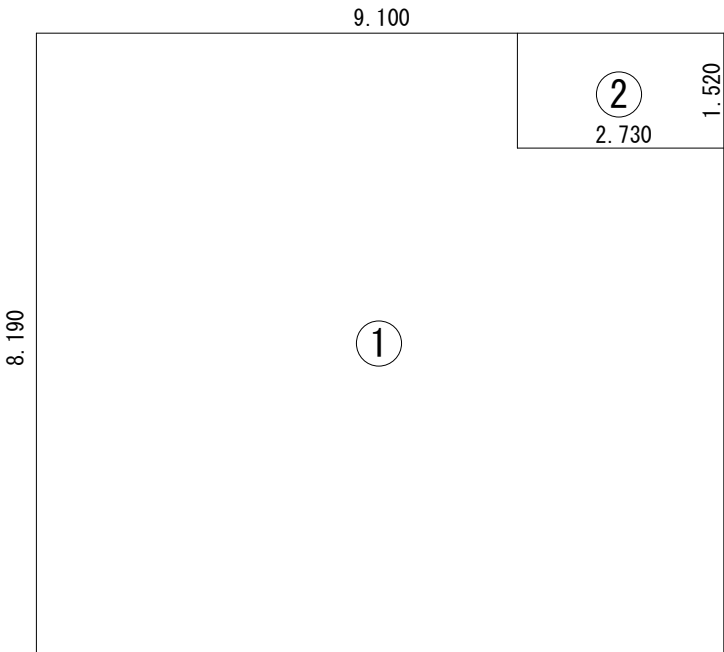


1階床面積図 S=1/100

1階床面積求積表

| 番号 | 計算式           | (m) | 面積 (㎡)           |
|----|---------------|-----|------------------|
| 1  | 9.100 × 8.190 |     | 74.529           |
| 2  | 1.520 × 2.730 |     | -4.1496          |
|    |               |     |                  |
| 合計 |               |     | 70.3794<br>70.37 |

(21.2坪)

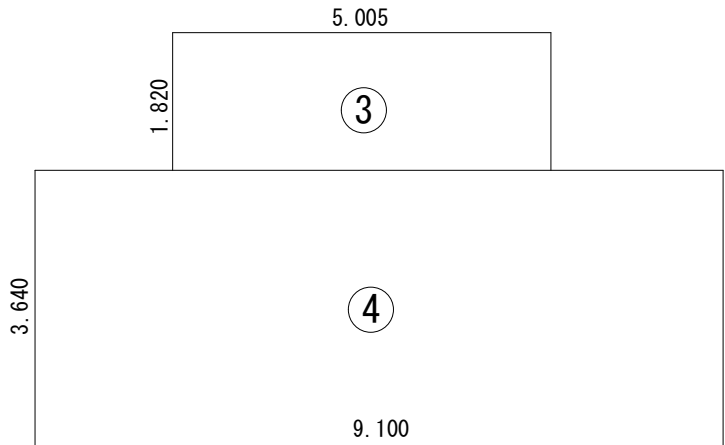

2階床面積図 S=1/100

2階床面積求積表

| 番号 | 計算式           | (m) | 面積 (㎡)           |
|----|---------------|-----|------------------|
| 3  | 5.005 × 1.820 |     | 9.1091           |
| 4  | 3.640 × 3.640 |     | 33.124           |
|    |               |     |                  |
| 合計 |               |     | 42.2331<br>42.23 |

(12.7坪)


延べ床面積表

|       | 番号    | (m) | 面積 (㎡) |
|-------|-------|-----|--------|
| 1階床面積 | 1 - 2 |     | 70.37  |
| 2階床面積 | 3 + 4 |     | 42.23  |
| 合計    |       |     | 112.60 |

(34.0坪)

決定図



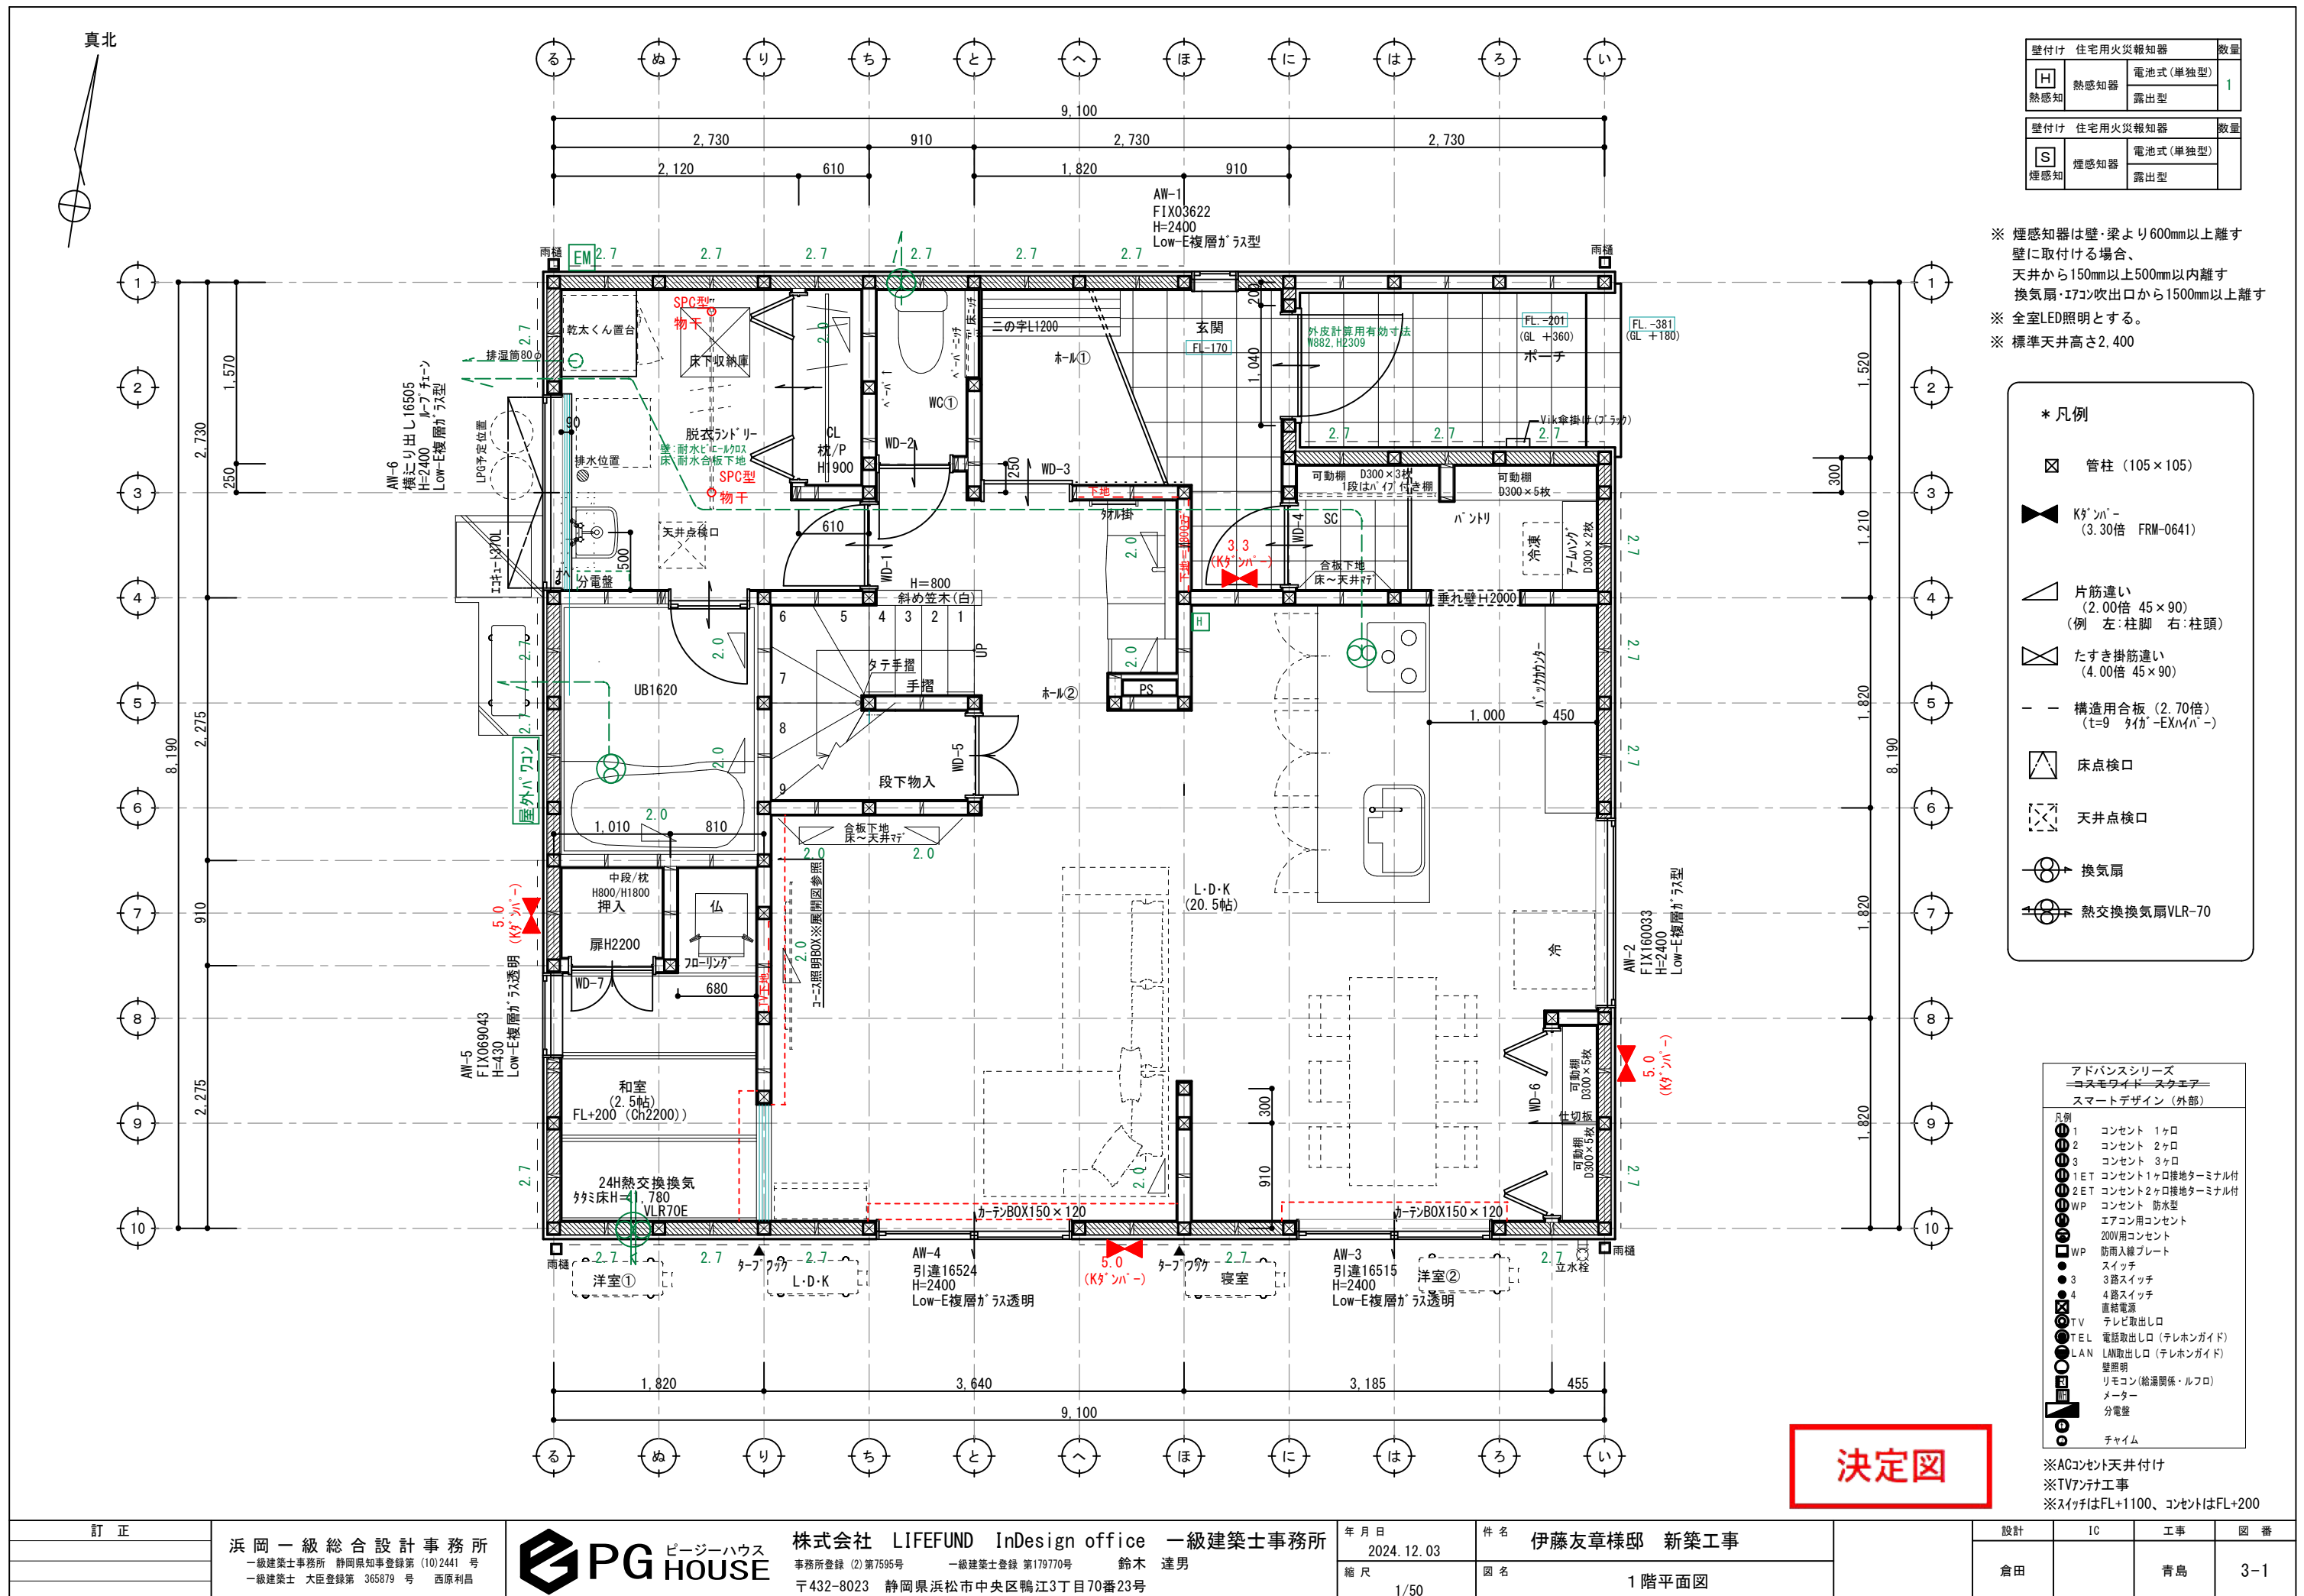

| 壁付け 住宅用火災報知器 |      |          | 数量 |
|--------------|------|----------|----|
| [H]          | 熱感知器 | 電池式(単独型) | 1  |
|              | 露出型  |          |    |
| 壁付け 住宅用火災報知器 |      |          | 数量 |
| [S]          | 煙感知器 | 電池式(単独型) |    |
|              | 露出型  |          |    |

※ 煙感知器は壁・梁より600mm以上離す  
壁に取付ける場合、  
天井から150mm以上500mm以内離す  
換気扇・エアコン吹出口から1500mm以上離す  
※ 全室LED照明とする。  
※ 標準天井高さ2,400


**\* 凡例**


- 管柱 (105×105)
- K&Sバルコニー (3.30倍 FRM-0641)
- 片筋違い (2.00倍 45×90)  
(例 左:柱脚 右:柱頭)
- たすき掛筋違い (4.00倍 45×90)
- 構造用合板 (2.70倍)  
(t=9 9材 EXハイパー)
- 床点検口
- 天井点検口
- 換気扇
- 熱交換換気扇VLR-70

| アドバンスシリーズ<br>コネクトワイヤードシステム<br>スマートデザイン (外部) |     |                  |  |
|---------------------------------------------|-----|------------------|--|
| 凡例                                          | 1   | コンセント 1ヶ所        |  |
|                                             | 2   | コンセント 2ヶ所        |  |
|                                             | 3   | コンセント 3ヶ所        |  |
|                                             | 1ET | コンセント1ヶ所接地ターミナル付 |  |
|                                             | 2ET | コンセント2ヶ所接地ターミナル付 |  |
|                                             | WP  | コンセント 防水型        |  |
|                                             |     | エアコン用コンセント       |  |
|                                             |     | 200V用コンセント       |  |
|                                             | WP  | 防雨入線プレート         |  |
|                                             |     | スイッチ             |  |
|                                             | 3   | 3路スイッチ           |  |
|                                             | 4   | 4路スイッチ           |  |
|                                             |     | 直結電源             |  |
|                                             | TV  | テレビ取出口           |  |
|                                             | TEL | 電話取出口 (テレホンガイド)  |  |
|                                             | LAN | LAN取出口 (テレホンガイド) |  |
|                                             |     | 壁照明              |  |
|                                             |     | リモコン (給湯関係・ルフロ)  |  |
|                                             |     | メーター             |  |
|                                             |     | 分電盤              |  |
|                                             |     | チャイム             |  |

※ACコンセント天井付け  
※TVアンテナ工事  
※スイッチはFL+1100、コンセントはFL+200


**決定図**

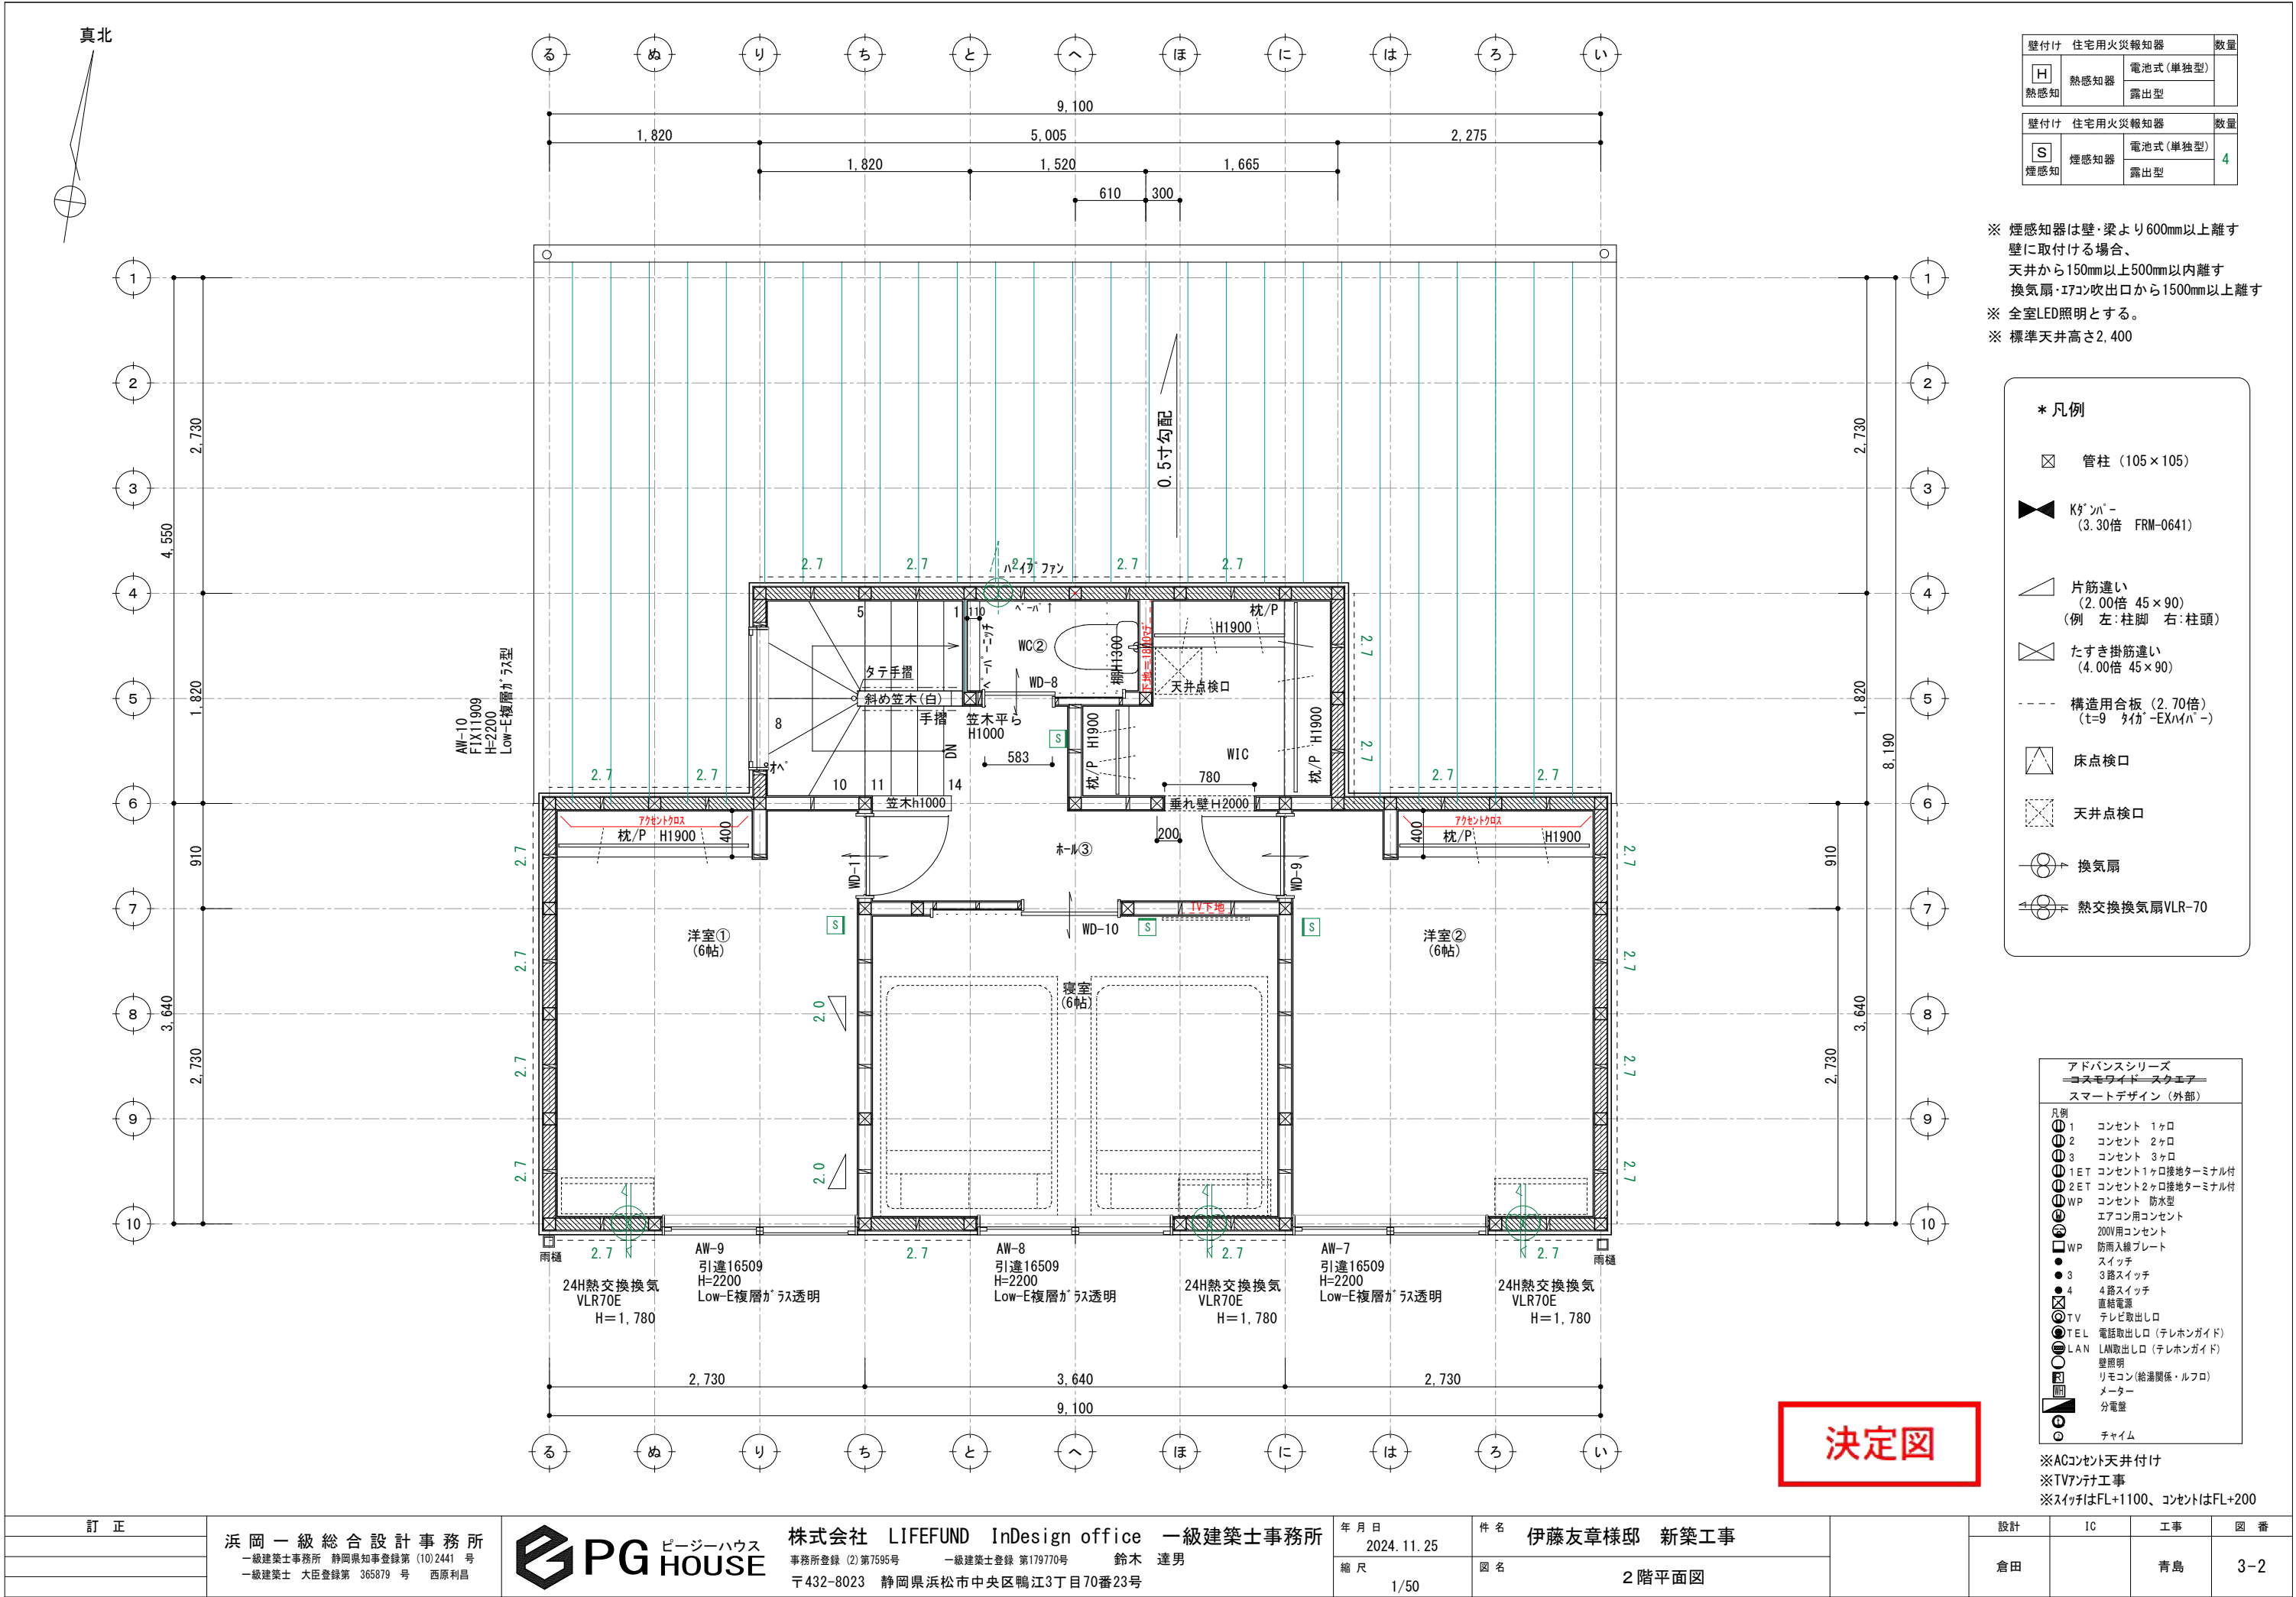

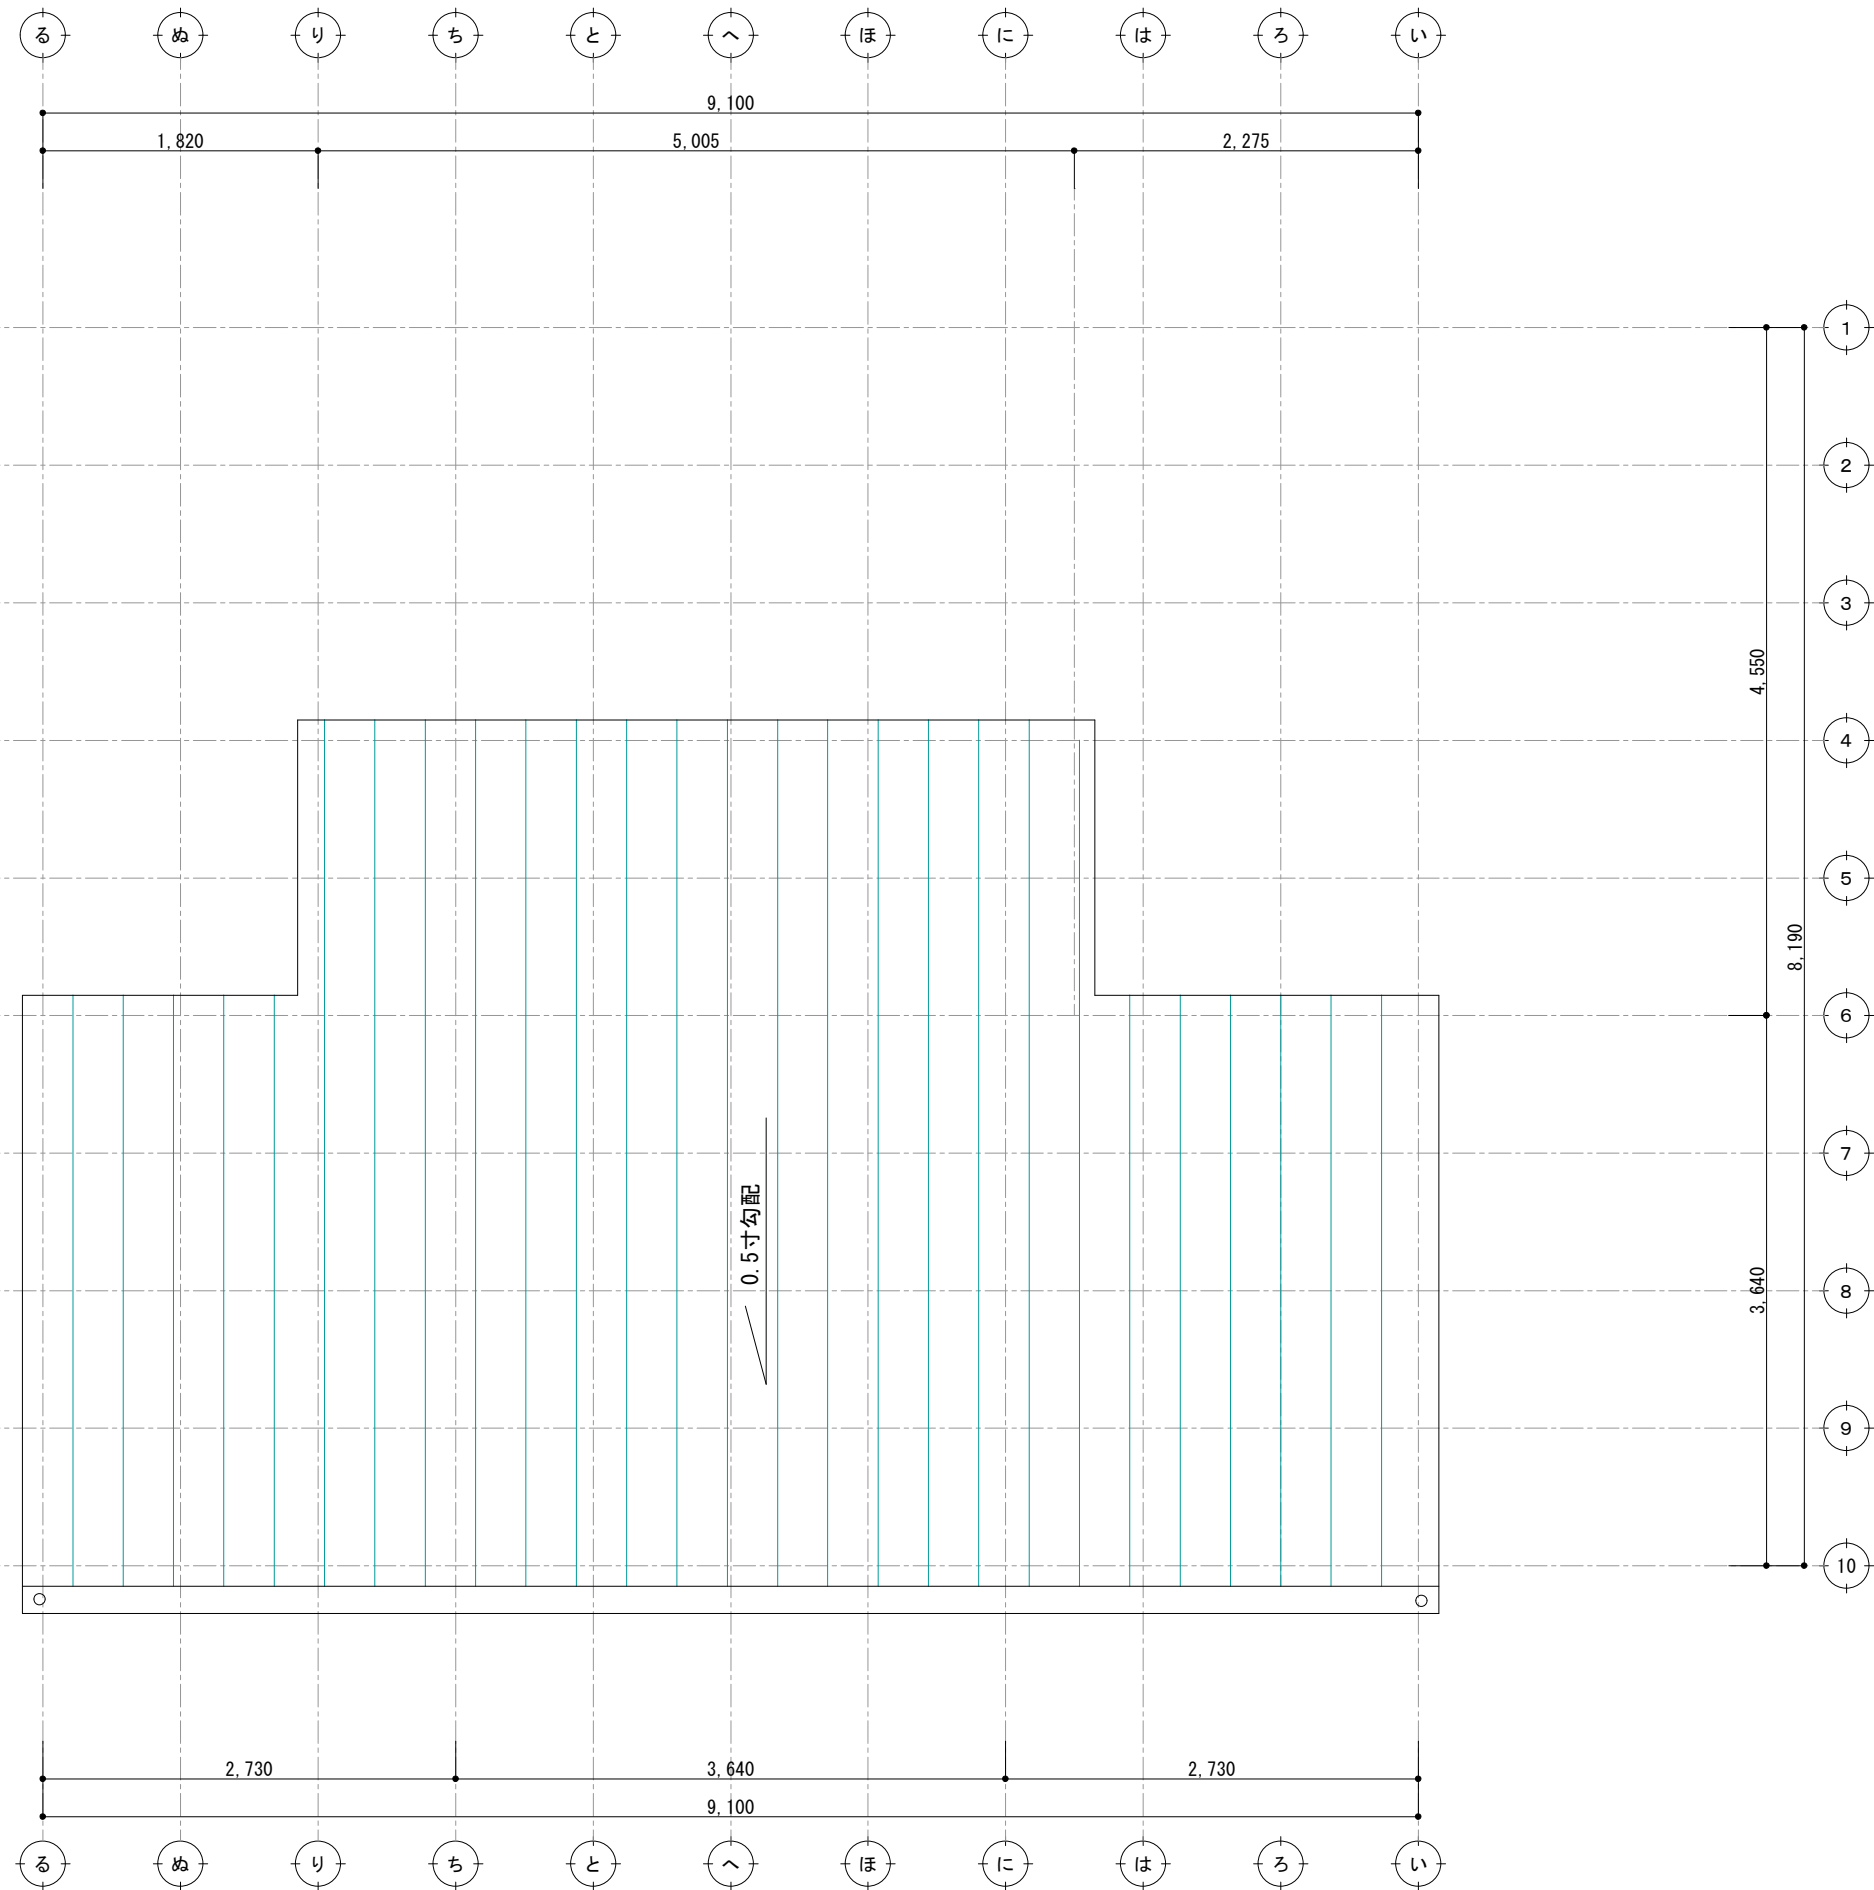


決定図

|     |                                                                                    |                                                                                      |   |              |             |  |    |    |    |     |
|-----|------------------------------------------------------------------------------------|--------------------------------------------------------------------------------------|---|--------------|-------------|--|----|----|----|-----|
| 訂 正 | 浜 岡 一 級 総 合 設 計 事 務 所<br>一級建築士事務所 静岡県知事登録第 (10)2441 号<br>一級建築士 大臣登録第 365879 号 西原利昌 |  | 株式会社 LIFEFUND InDesign office 一級建築士事務所<br>事務所登録 (2) 第7595号 一級建築士登録 第179770号 鈴木 達男<br>〒432-8023 静岡県浜松市中央区鴨江3丁目70番23号 | 年 月 日        | 件 名         |  | 設計 | IC | 工事 | 図 番 |
|     |                                                                                    |                                                                                      |   | 2024. 11. 23 | 伊藤友章様邸 新築工事 |  |    |    |    |     |
|     |                                                                                    |                                                                                      |   | 縮 尺          | 図 名         |  |    |    |    |     |
|     |                                                                                    |                                                                                      |   | 1/100        | 屋根伏図        |  | 倉田 |    | 青島 | 3-3 |

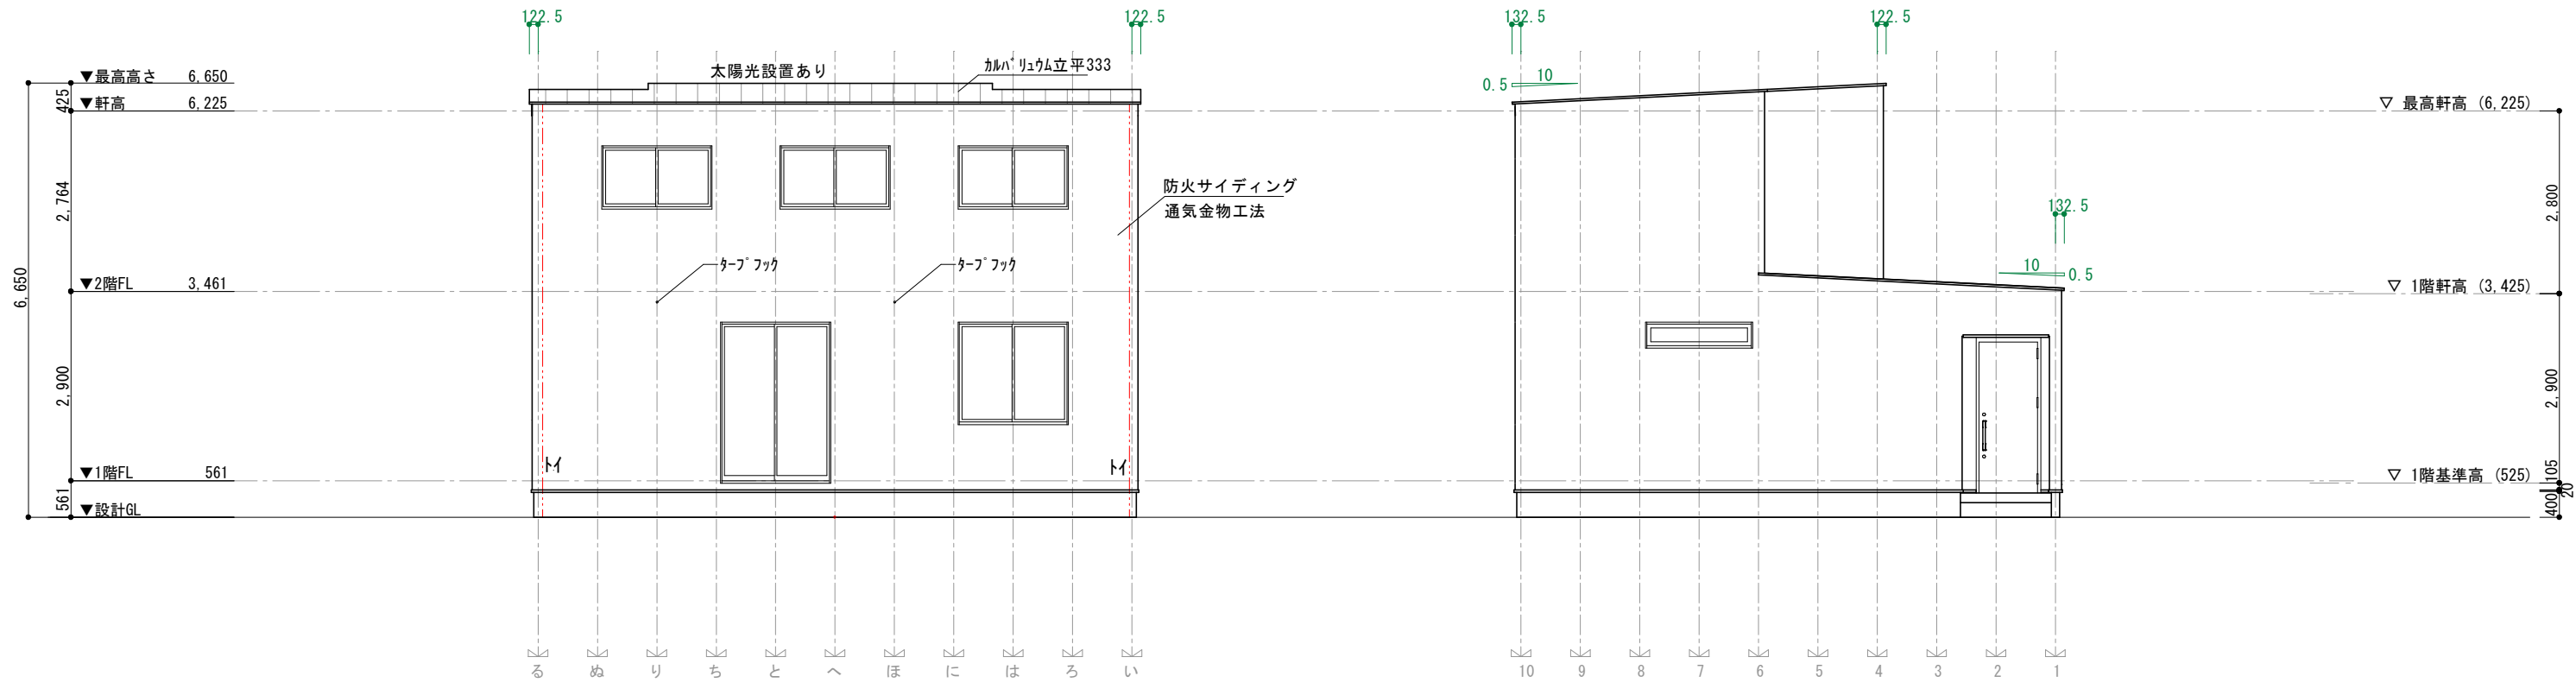

南側立面図 S=1/100

東側立面図 S=1/100

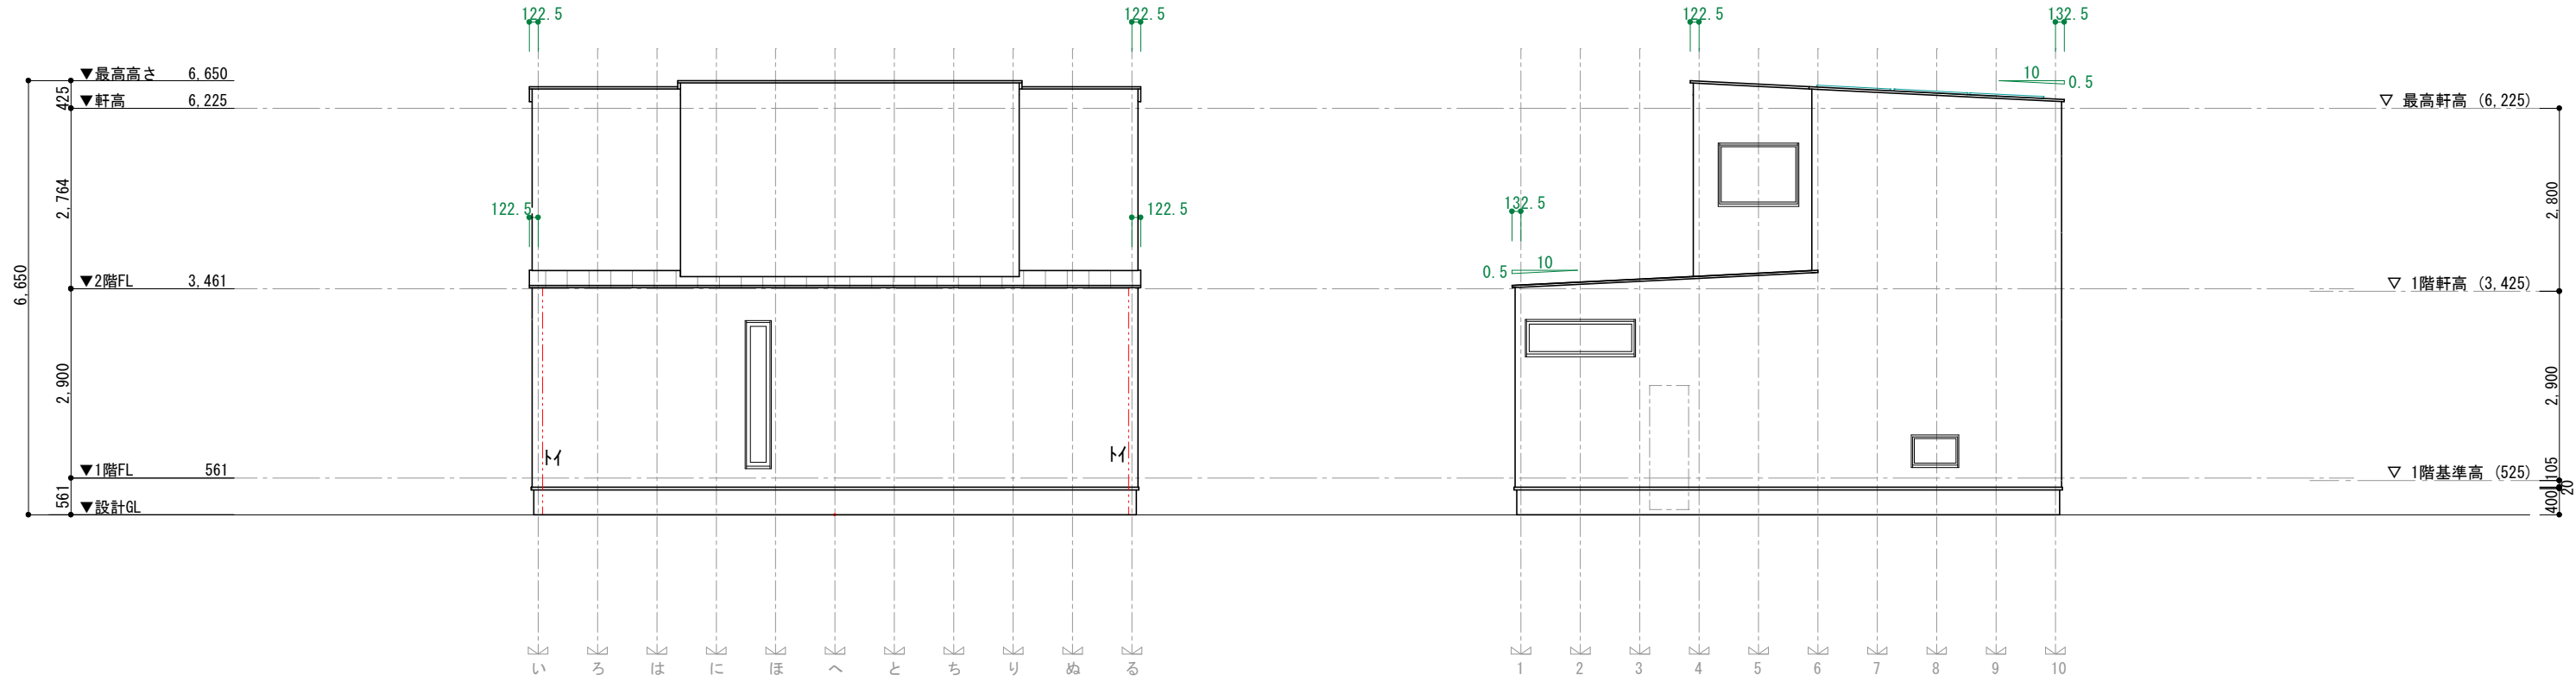


北側立面図 S=1/100

西側立面図 S=1/100

決定図


|    |                                                                          |                                                                                      |   |                   |                   |  |    |    |    |    |
|----|--------------------------------------------------------------------------|--------------------------------------------------------------------------------------|---|-------------------|-------------------|--|----|----|----|----|
| 訂正 | 浜岡一級総合設計事務所<br>一級建築士事務所 静岡県知事登録第 (10)2441 号<br>一級建築士 大臣登録第 365879 号 西原利昌 |  | 株式会社 LIFEFUND InDesign office 一級建築士事務所<br>事務所登録 (2) 第7595号 一級建築士登録 第179770号 鈴木 達男<br>〒432-8023 静岡県浜松市中央区鴨江3丁目70番23号 | 年月日<br>2024.11.23 | 件名<br>伊藤友章様邸 新築工事 |  | 設計 | IC | 工事 | 図番 |
|    |                                                                          |                                                                                      |   | 縮尺<br>1/100       | 図名<br>立面図         |  | 倉田 |    | 青島 | 4  |
|    |                                                                          |                                                                                      |   |                   |                   |  |    |    |    |    |



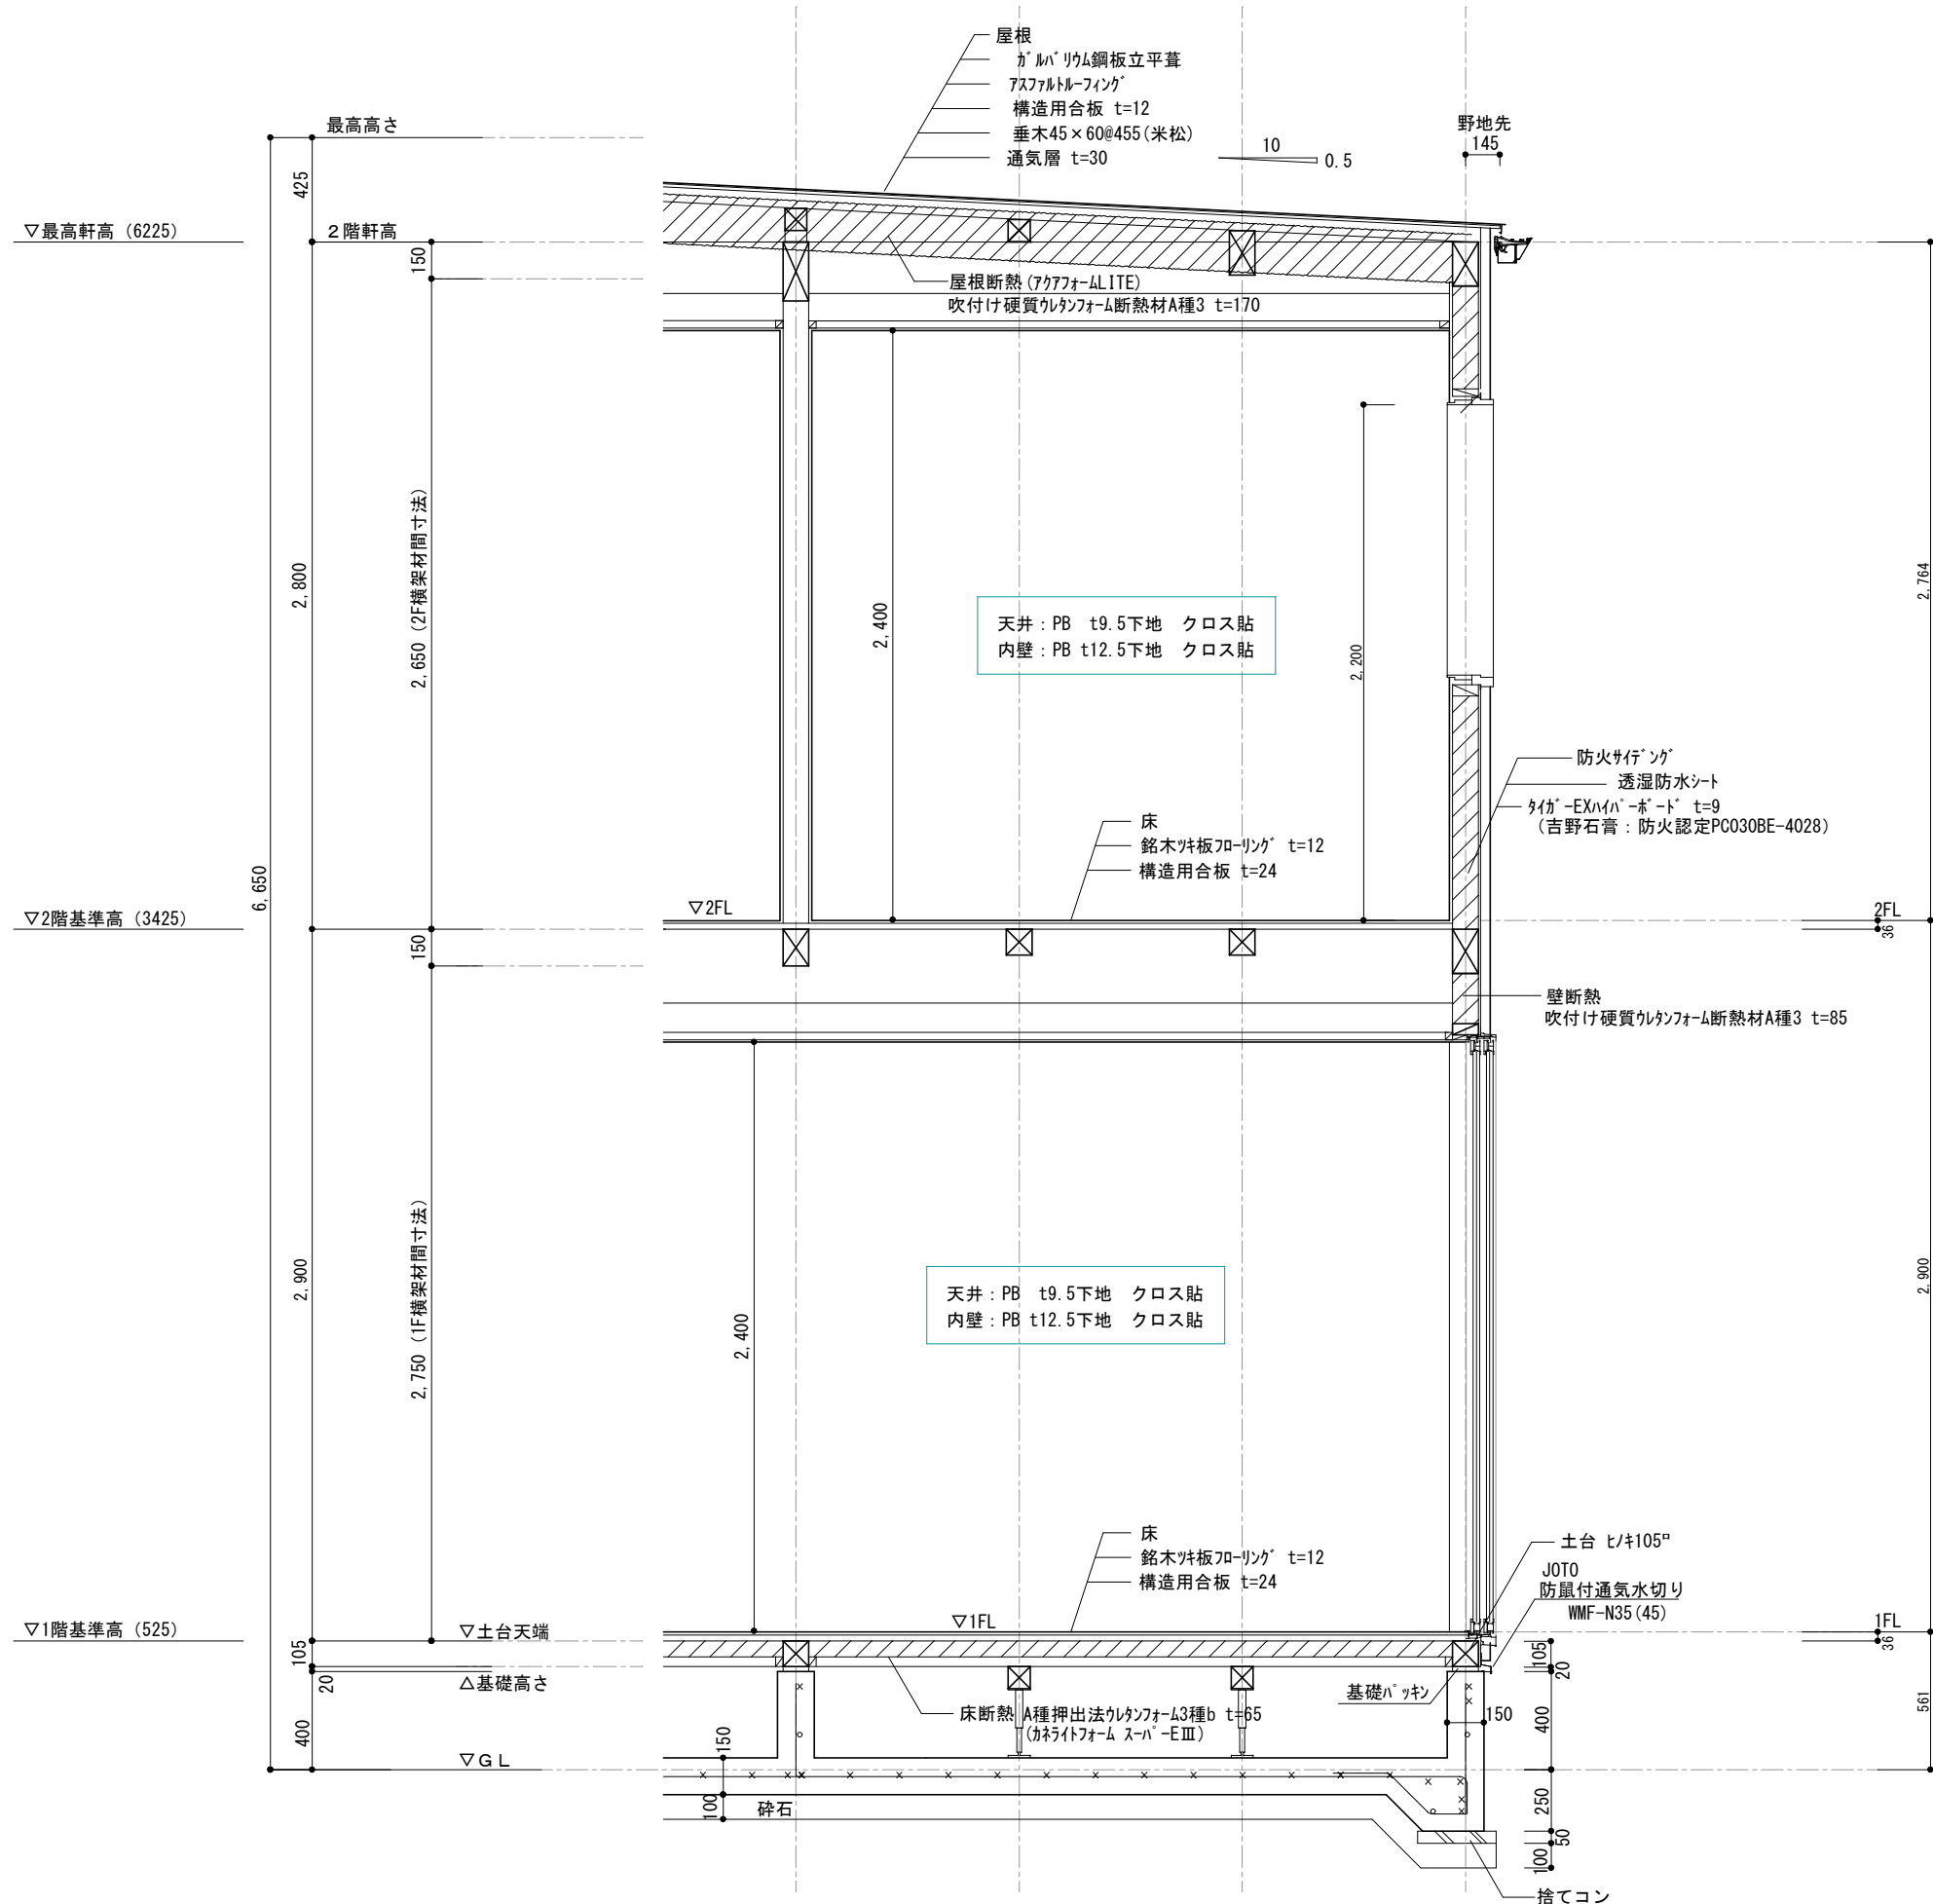


決定図


|    |                                                                       |                                                                                      |   |                                  |                                |  |    |    |    |     |
|----|-----------------------------------------------------------------------|--------------------------------------------------------------------------------------|---|----------------------------------|--------------------------------|--|----|----|----|-----|
| 訂正 | 浜岡一級総合設計事務所<br>一級建築士事務所 静岡県知事登録第(10)2441号<br>一級建築士 大臣登録第 365879号 西原利昌 |  | 株式会社 LIFEFUND InDesign office 一級建築士事務所<br>事務所登録(2)第7595号 一級建築士登録 第179770号 鈴木 達男<br>〒432-8023 静岡県浜松市中央区鶴江3丁目70番23号 | 年月日<br>2024.11.25<br>縮尺<br>1/100 | 件名<br>伊藤友章様邸 新築工事<br>図名<br>矩計図 |  | 設計 | IC | 工事 | 図番  |
|    |                                                                       |                                                                                      |   |                                  |                                |  | 倉田 |    | 青島 | A-5 |

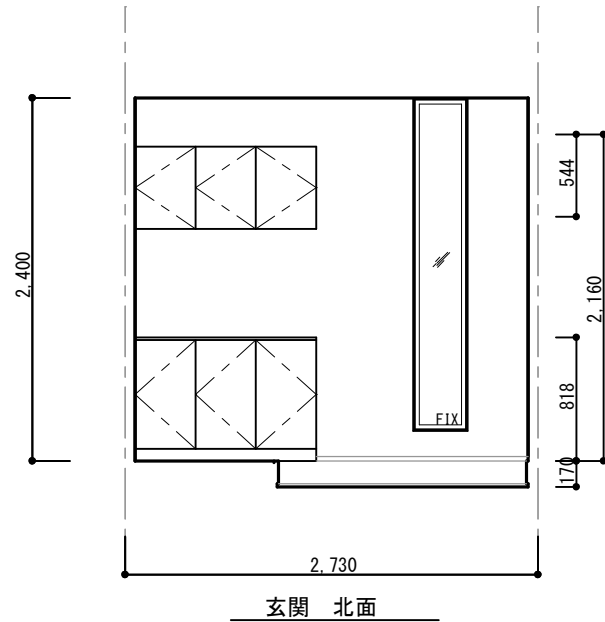


玄関 北面

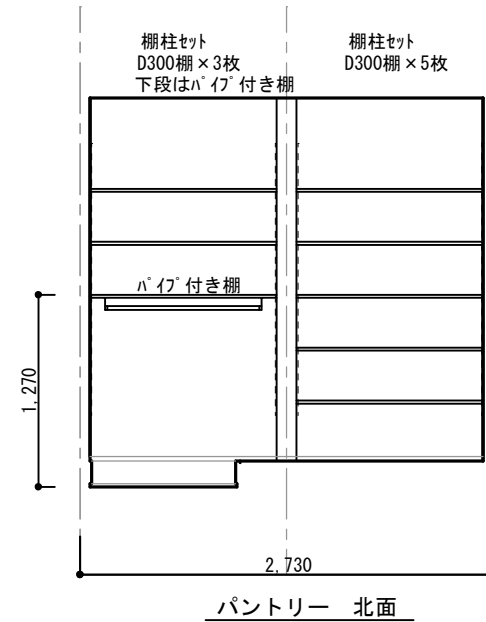


パントリー 北面

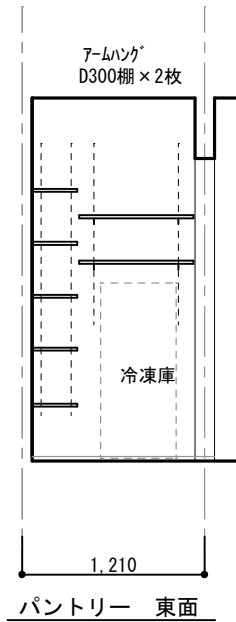



パントリー 東面

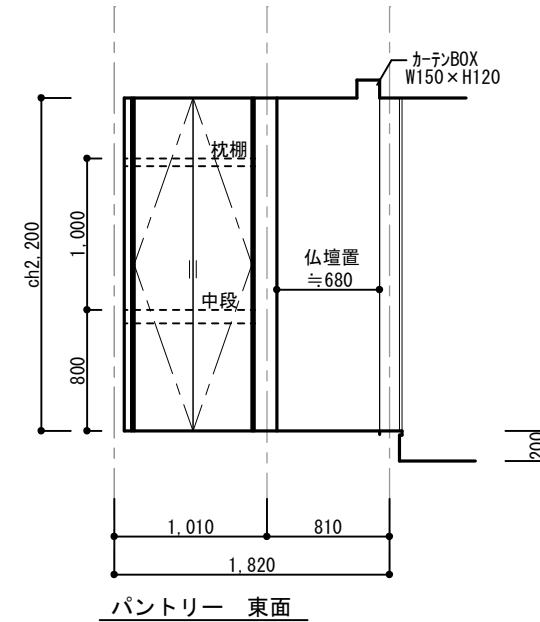


パントリー 東面

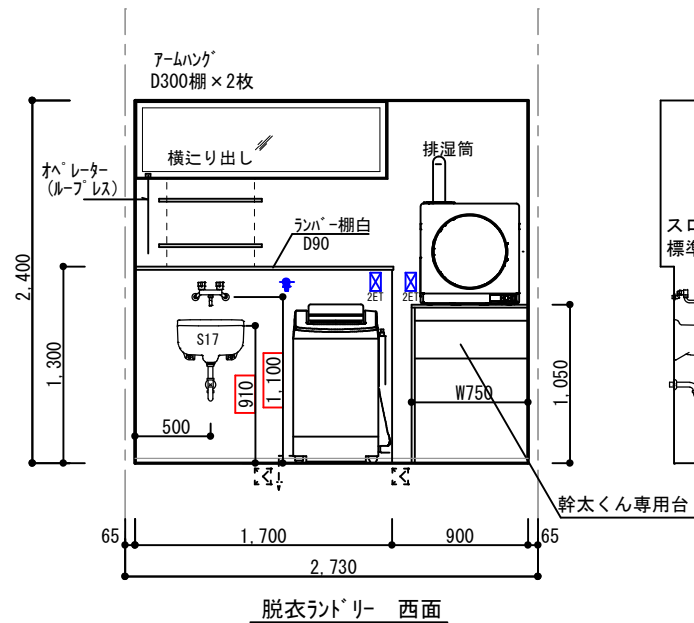


脱衣ランドリー 西面

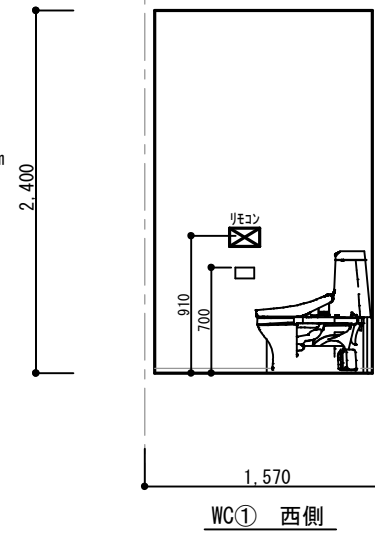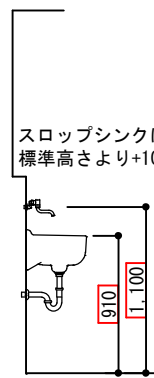


WC① 西側

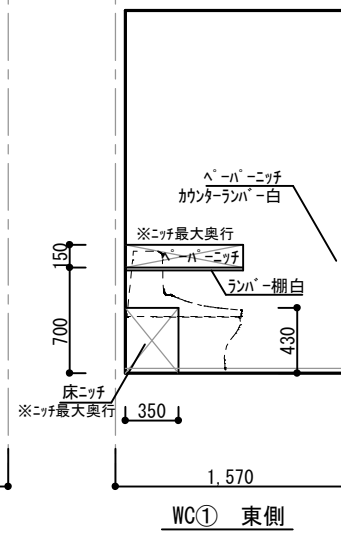


WC① 東側

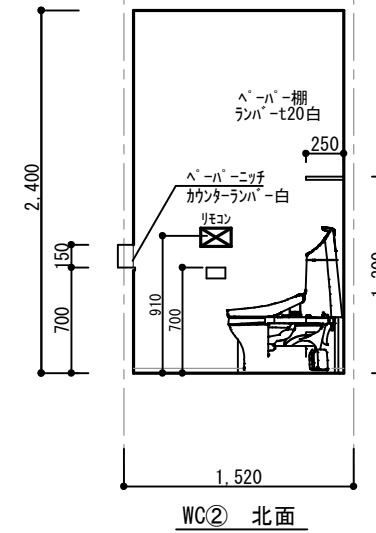


WC② 北面

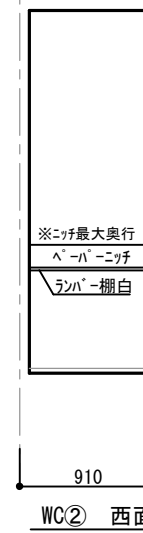


WC② 西面

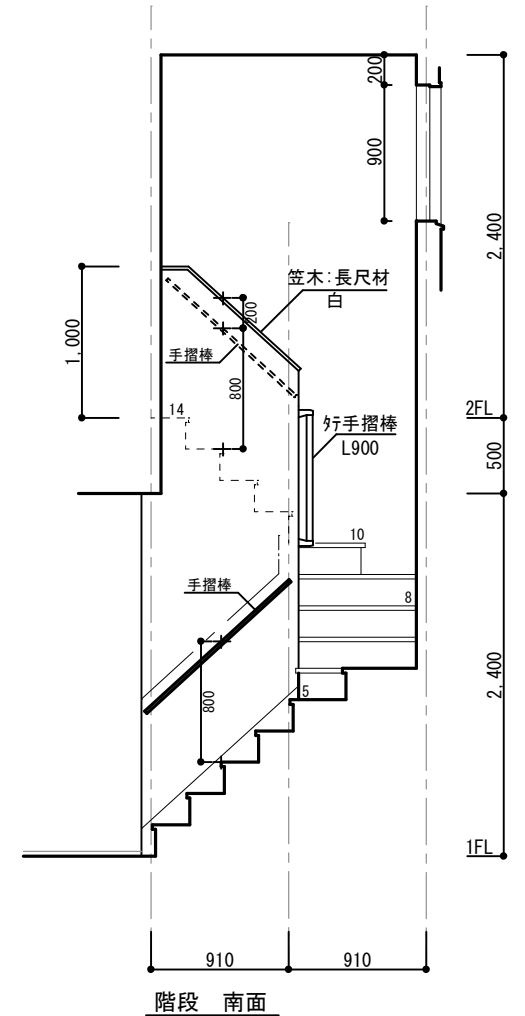


階段 南面

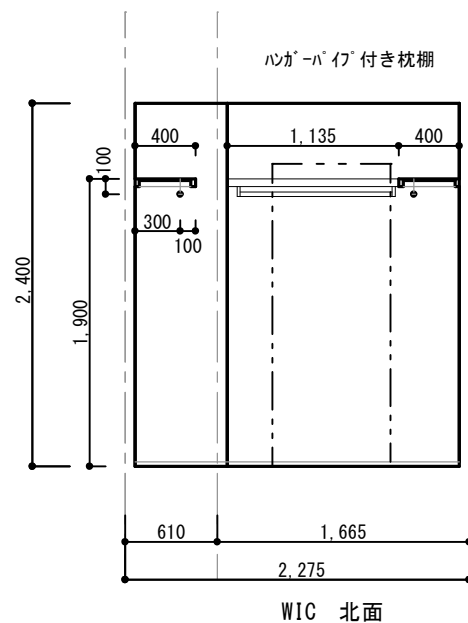


LDK 北面

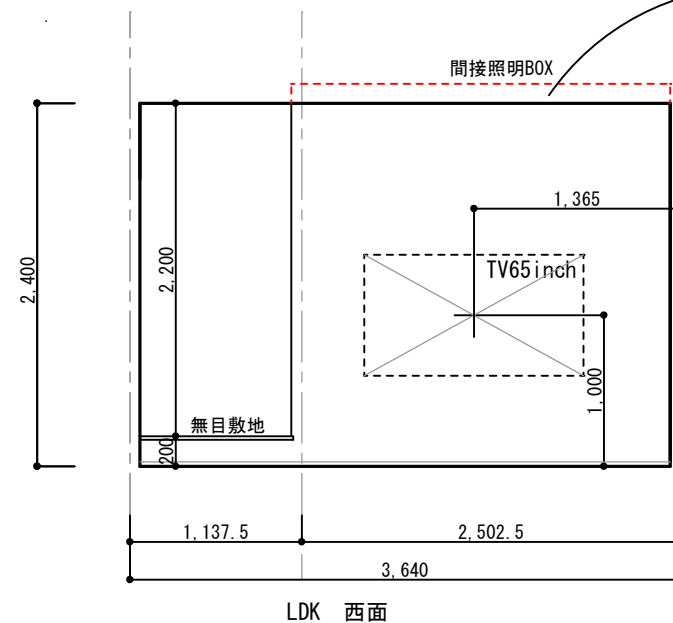

LDK 西面

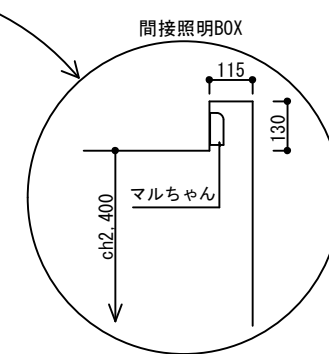


タオル掛け 紙巻器は支給のため下地要す。(WC① ② 洗面)

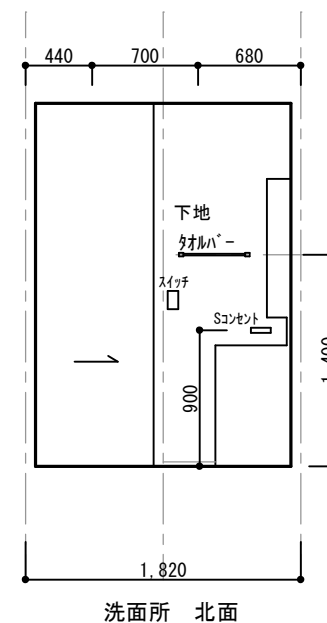


洗面所 北面


決定図

|    |                                                                          |                      |   |                                   |                                |  |          |    |          |           |
|----|--------------------------------------------------------------------------|----------------------|---|-----------------------------------|--------------------------------|--|----------|----|----------|-----------|
| 訂正 | 浜岡一級総合設計事務所<br>一級建築士事務所 静岡県知事登録第 (10)2441 号<br>一級建築士 大臣登録第 365879 号 西原利昌 | LIFEFUND<br>PG HOUSE | 株式会社 LIFEFUND InDesign office 一級建築士事務所<br>事務所登録 (2) 第7595号 一級建築士登録 第179770号 鈴木 達男<br>〒432-8023 静岡県浜松市中央区鴨江3丁目70番23号 | 年月日<br>2024. 11. 25<br>縮尺<br>1/50 | 件名<br>伊藤友章様邸 新築工事<br>図名<br>展開図 |  | 設計<br>倉田 | IC | 工事<br>青島 | 図番<br>6-1 |
|----|--------------------------------------------------------------------------|----------------------|---|-----------------------------------|--------------------------------|--|----------|----|----------|-----------|

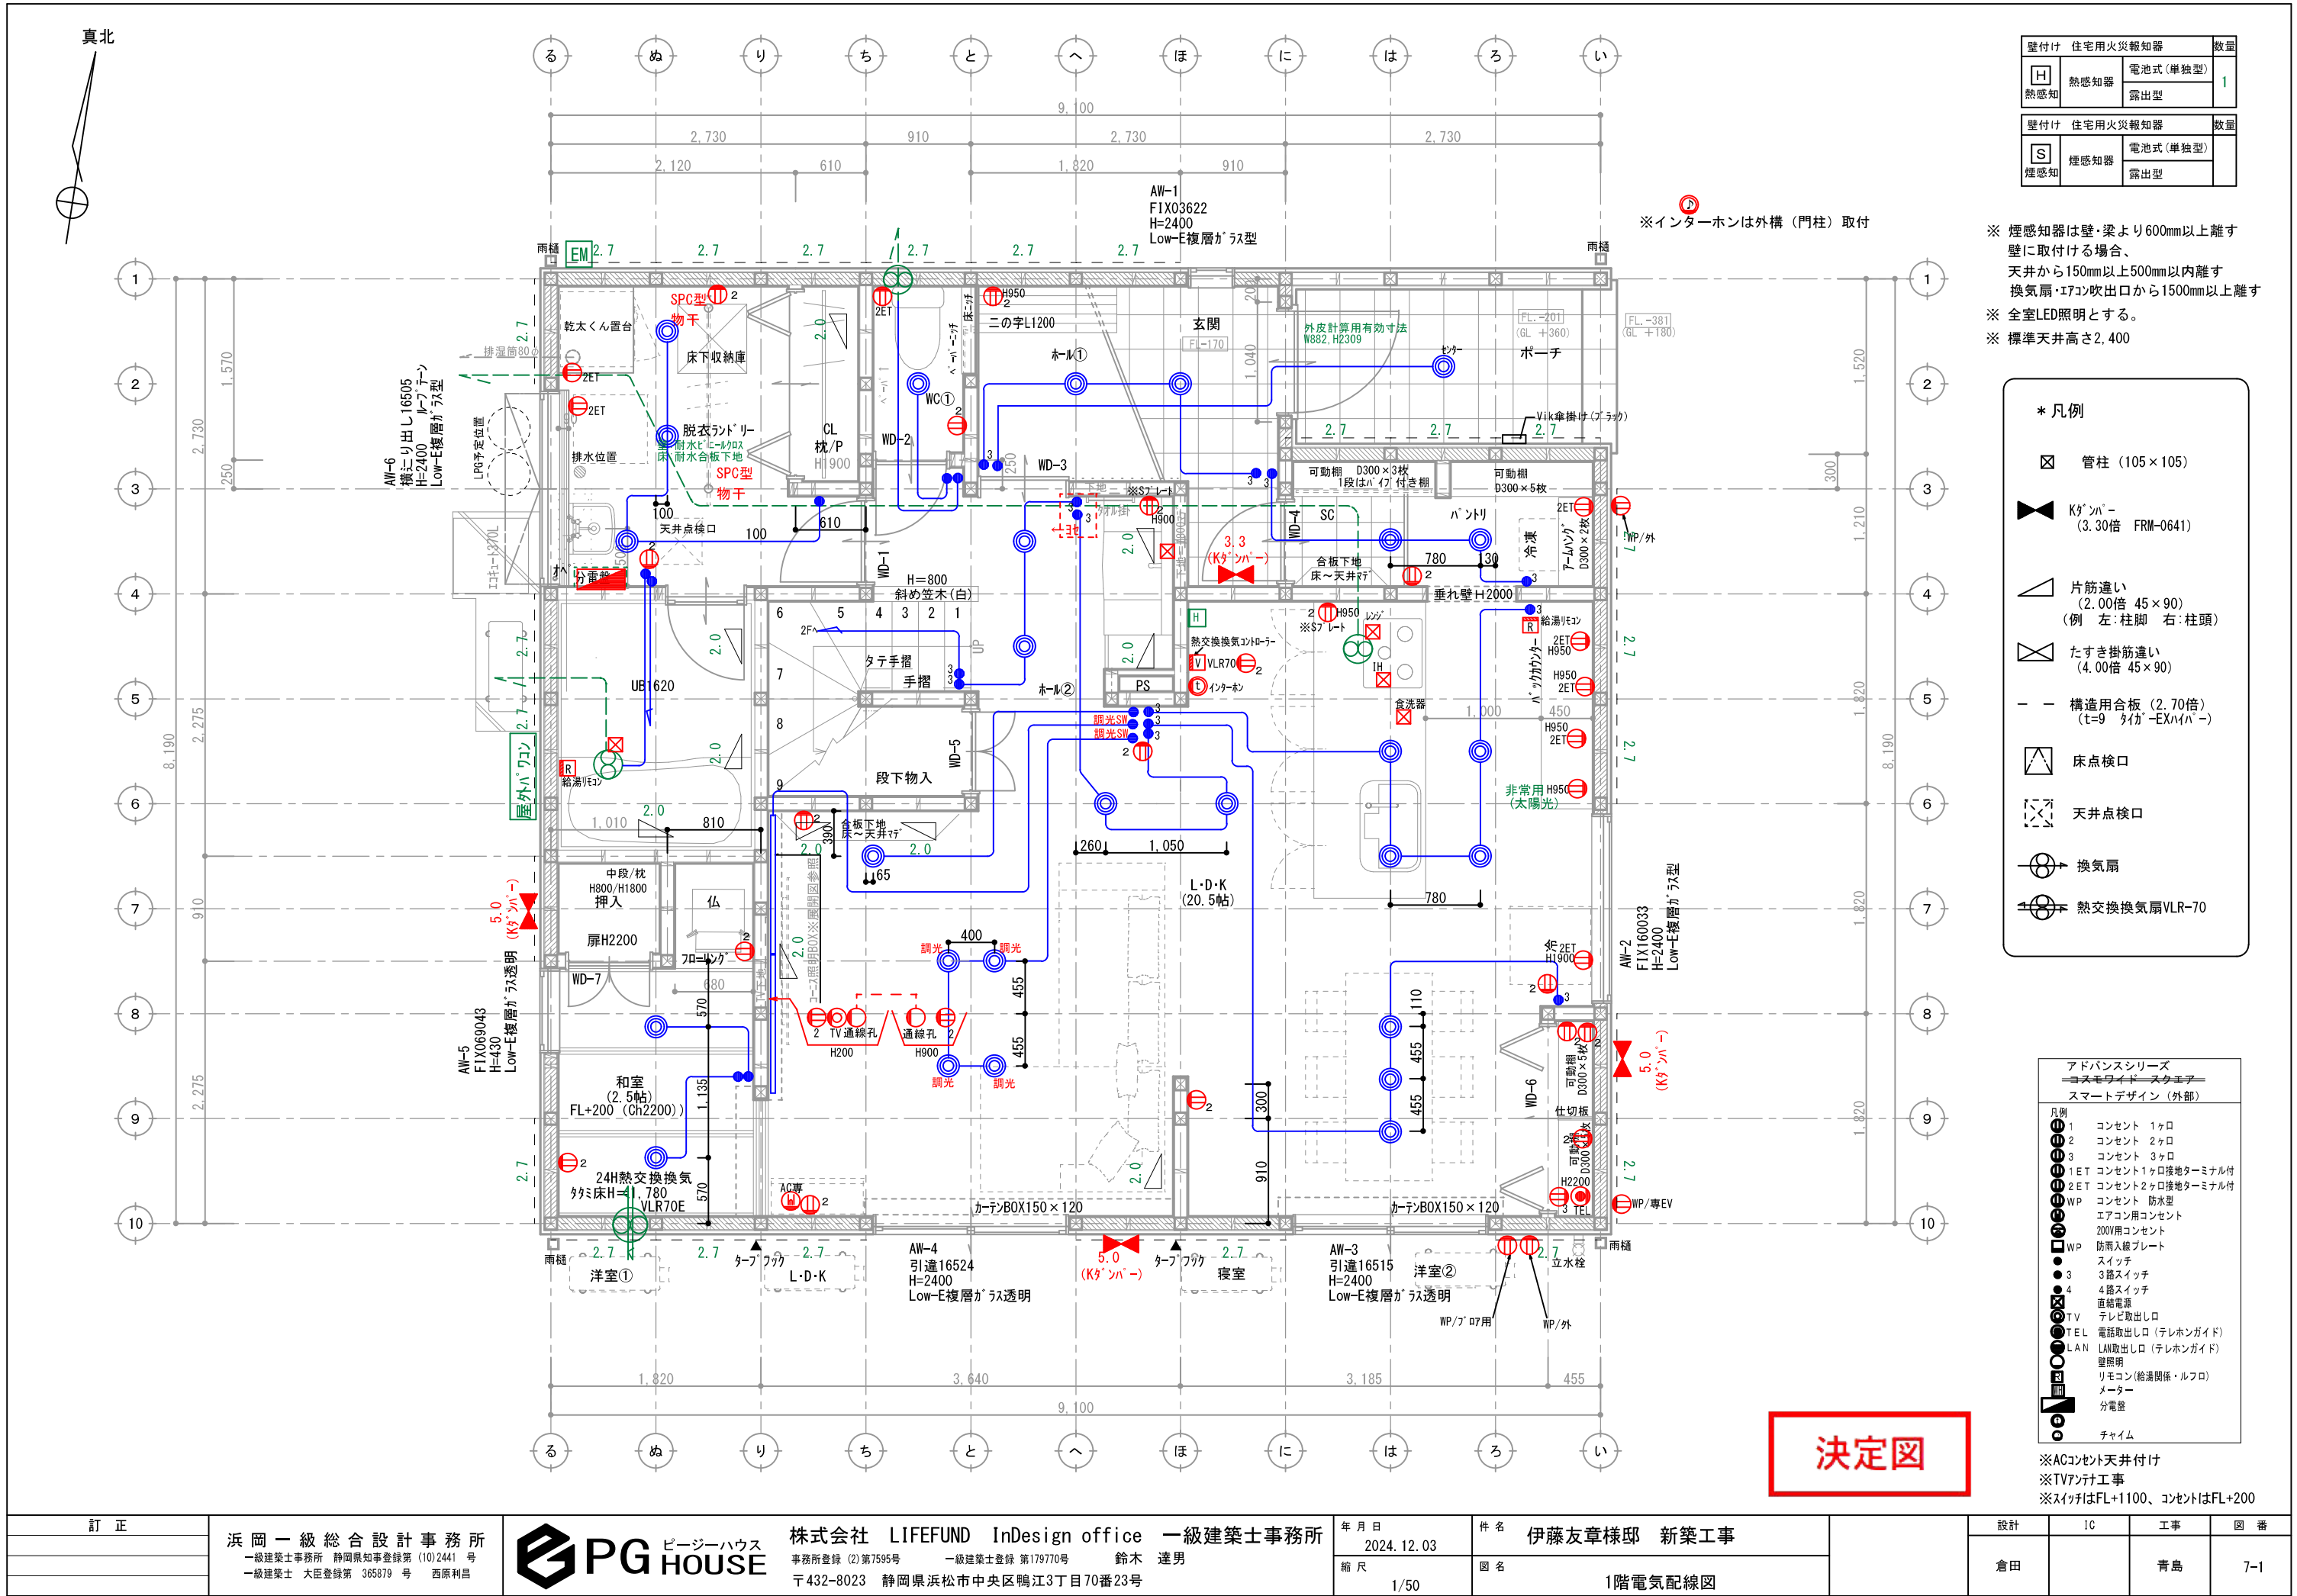


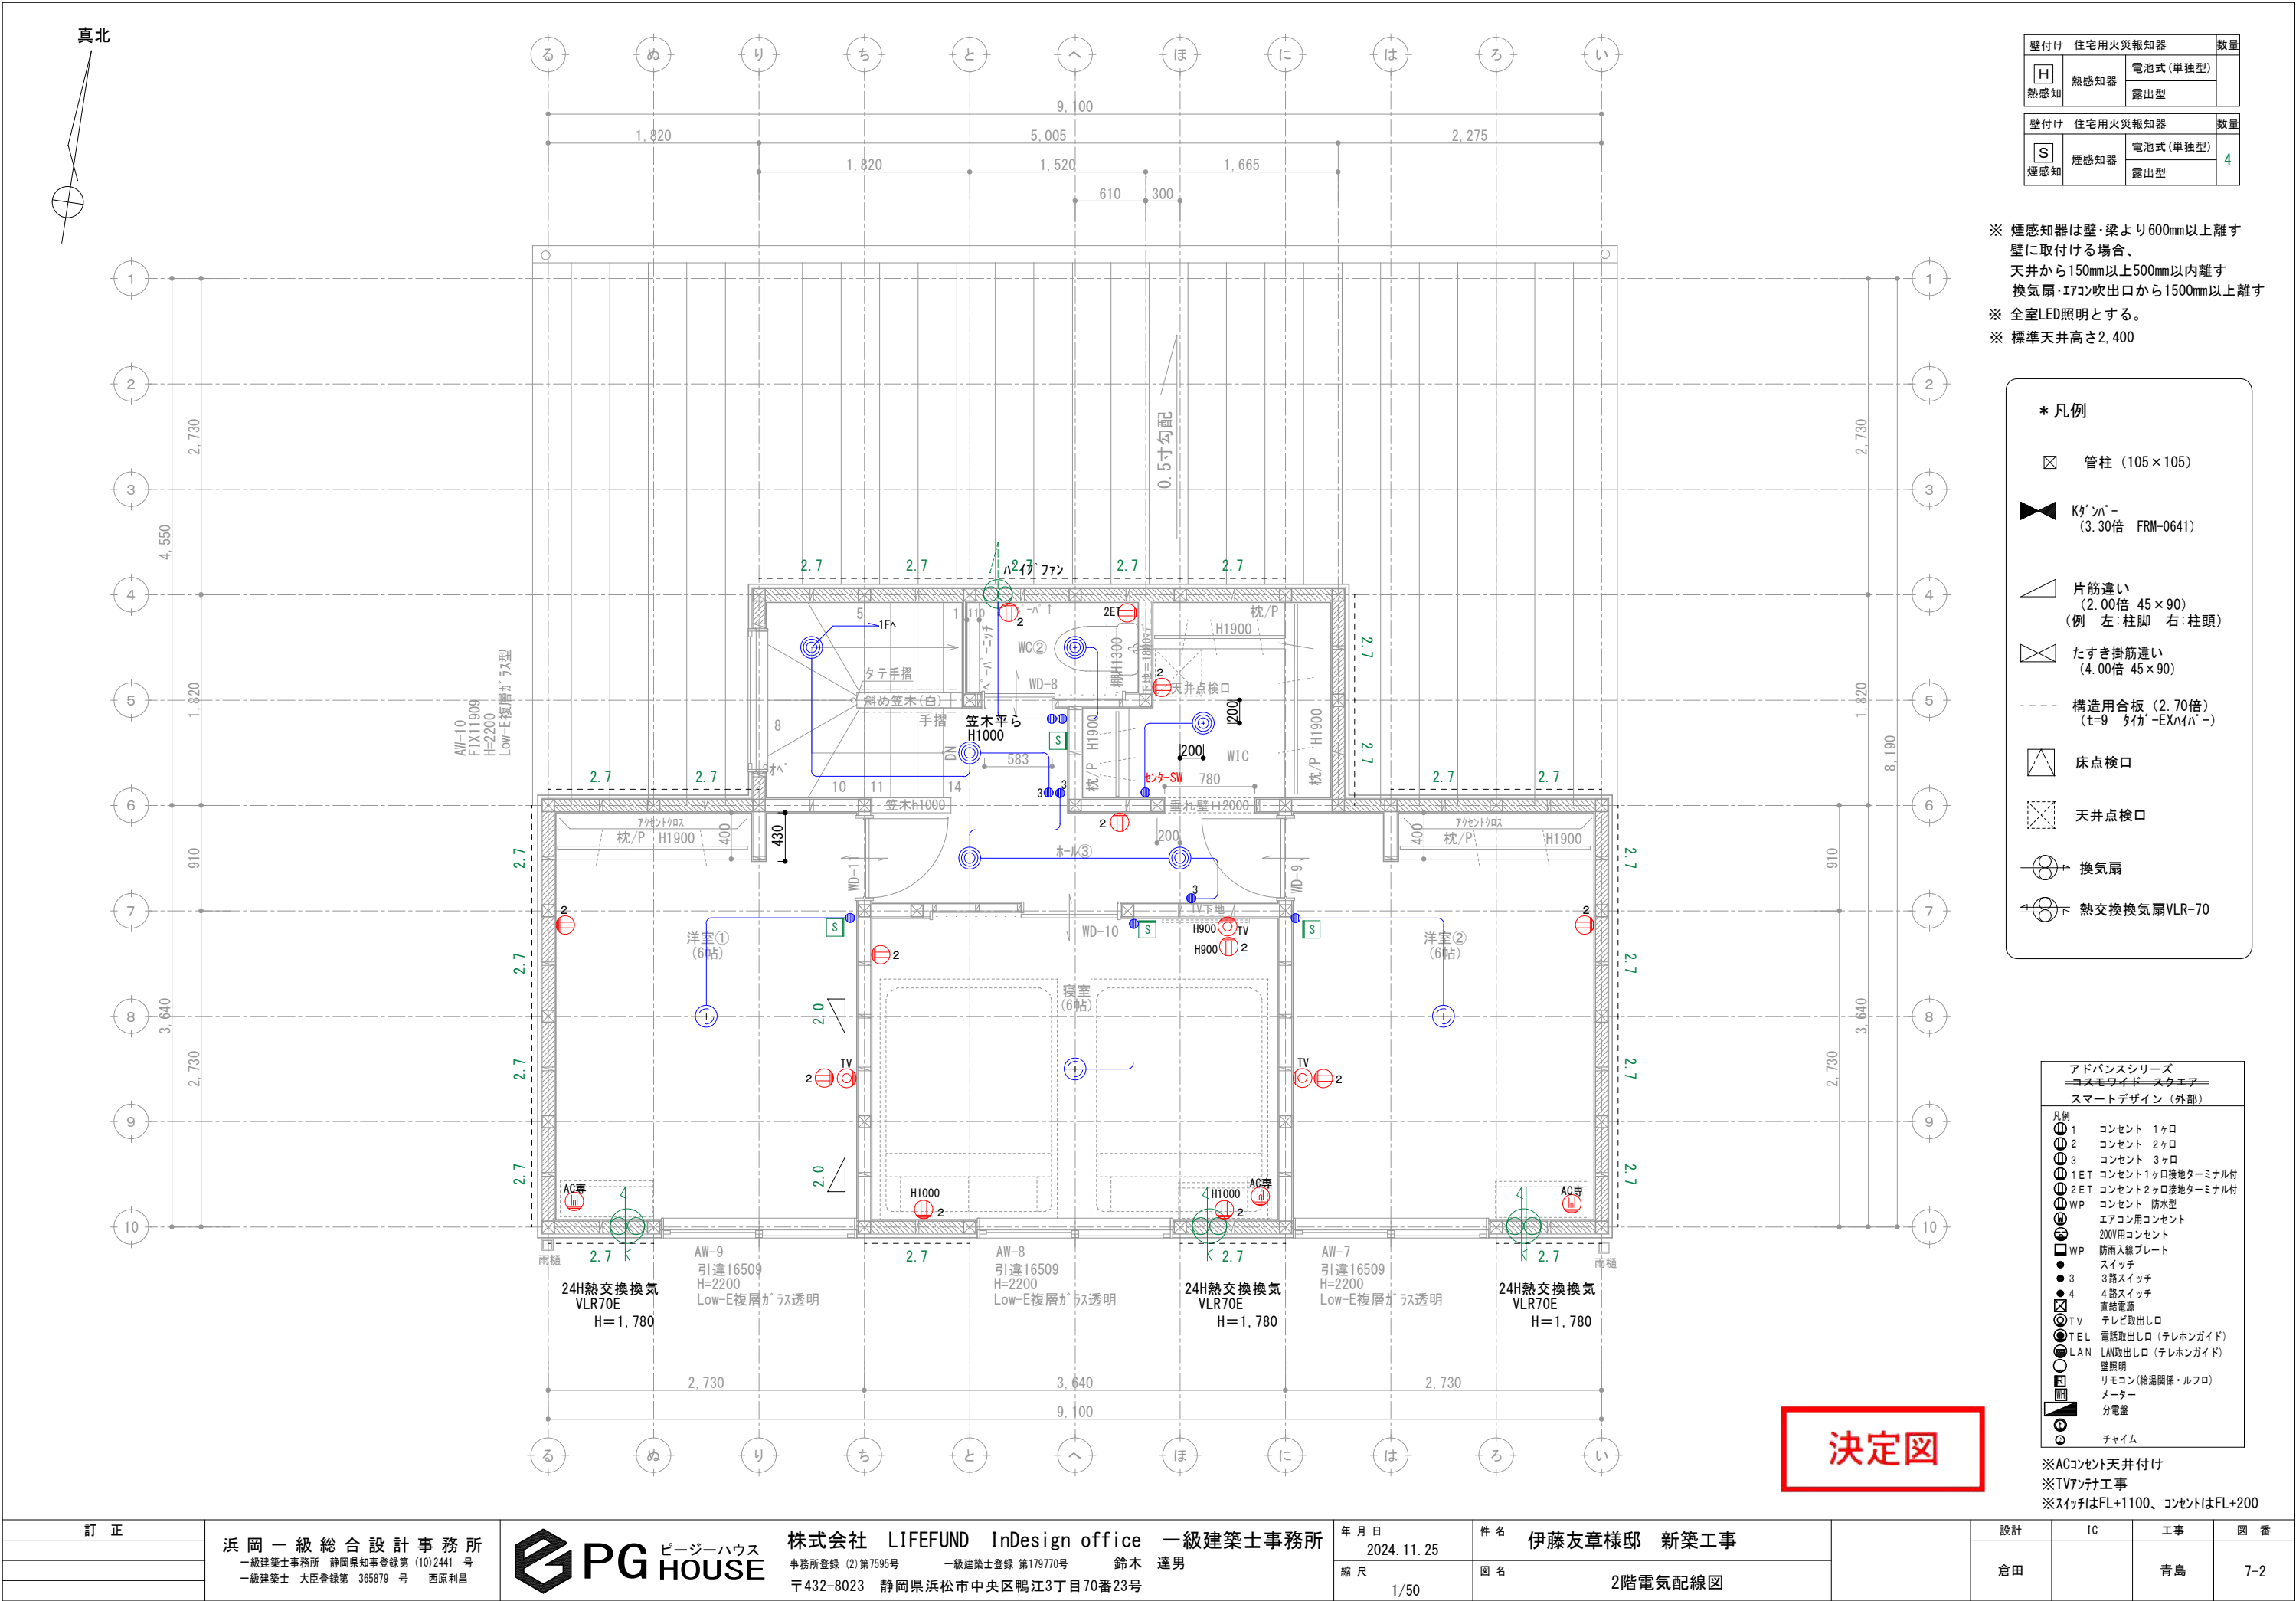



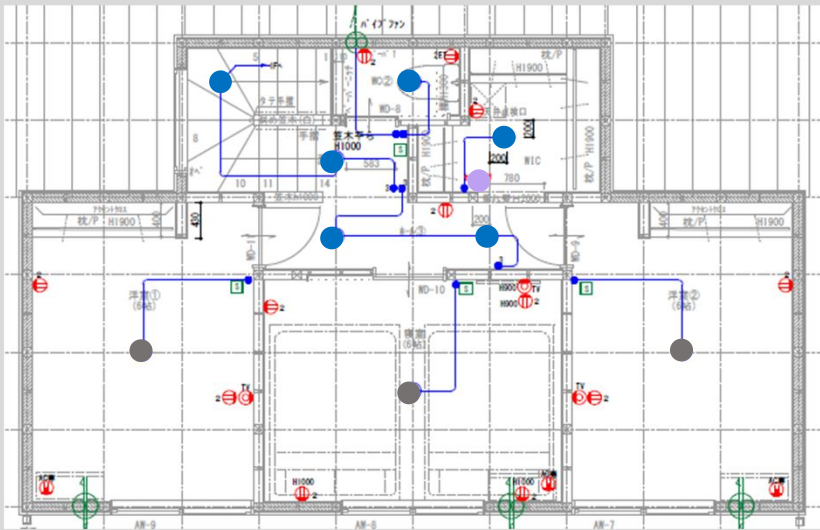

2階

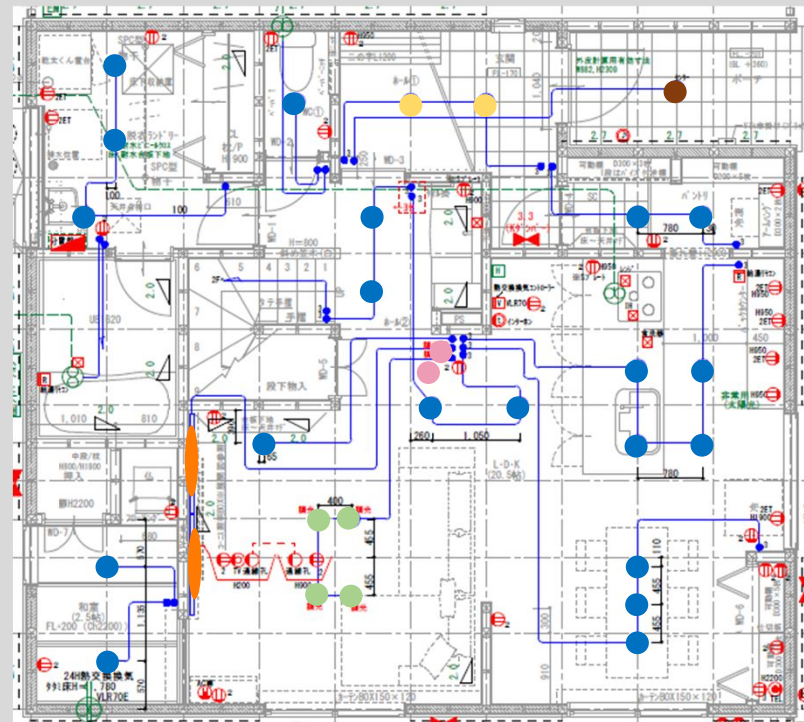

1階

ドアホン：VL-SZ30KL  
(Panasonic)



外部：スマートサインシリーズ



間接照明  
● × 2  
DSY-4393 AWG



L=1200mm

DSY-4393 AWG  
温白色 / 3500K・Ra83

|                |             |                          |
|----------------|-------------|--------------------------|
| 定格光束<br>3410lm | 消費電力<br>29W | 固有エネルギー消費効率<br>117.5lm/W |
|----------------|-------------|--------------------------|

¥29,800-(税抜) (LED内蔵)

LED LED 29W 電源内蔵

- アルミ型材 白アルマイト
- アクリル 乳白(マット)
- 巾85 長1200 高35mm 1.5kg
- 29VA
- AC100V
- 連結最大15台まで
- 調光可能(1%~100%)
- シーンコントローラー別売
- 調光にはLED専用調光器(別売)をご使用ください。
- オプション取付金具別売(DP-40543)
- 光源寿命40,000時間

天井・壁(横向)・床付兼用

調光

傾斜天井  
可能  
(横向)

LED交換  
不可

人感センサSW  
● × 1

WTA1811WK



コンセント：WTA1811WK  
プレート：WTA8101W

調光SW  
● × 2

WTA57583WK



WTA57583WK

希望小売価格 11,900円(税抜)  
※掲載の価格には消費税は含まれていません。  
LED 埋込逆位相調光スイッチC(はたはスイッチC)  
(適合LED専用3.2A) (ロータリー式)  
(下照角度設定機能付)(マットホワイト)

WTA7101WK

希望小売価格 320円(税抜)  
※掲載の価格には消費税は含まれていません。

居室シーリング  
● × 3

DCL40507



タイマー付リモコン・ブルレス | 調色調光タイプ

DCL-40507  
星白色 / 6500K・Ra83 ~ 電球色 / 2700K・Ra83

|     |                     |                |               |                          |
|-----|---------------------|----------------|---------------|--------------------------|
| LED | LED 29.5W<br>● 30VA | 定格光束<br>3699lm | 消費電力<br>29.5W | 固有エネルギー消費効率<br>125.3lm/W |
|-----|---------------------|----------------|---------------|--------------------------|

¥22,000-(税抜) (LED内蔵)

- アクリル 乳白(マット)
- 径φ510 高128mm 1.6kg
- ブルレススイッチ付(全灯・※点灯・常夜灯)
- ※消灯前の調色調光段階
- 調色機能付(6500K~2700K)
- 調光機能付(5%~100%)
- 常夜灯6段階調光
- AC100V
- 光源寿命40,000時間
- 消費効率星白色時
- 調光器併用不可
- シーンコントローラーは使用できません。

クイック取付式  
カバー回転式

傾斜天井 55° 傾斜天井 55° DP-40091 傾斜天井 55° DP-40638

決定図

ポーチ灯

● × 1

DDL-4496YB



高気密Se形 | 人感センサー | 連動マルチタイプ

DDL-4496 YB  
電球色 / 2700K・Ra83

|               |              |                         |
|---------------|--------------|-------------------------|
| 定格光束<br>425lm | 消費電力<br>7.7W | 固有エネルギー消費効率<br>55.1lm/W |
|---------------|--------------|-------------------------|

¥18,800-(税抜) (LED内蔵)

LED LED 7.7W  
白熱灯60W相当

- アルミダイカスト 黒塗装
- アクリル 乳白(マット)
- 径φ111 埋込穴φ100
- 埋込深80mm 0.5kg
- 14VA
- 点灯照度調節機能付(暗・明・切)
- 点灯保持時間(1分)
- 拡散バネル付
- AC100V
- 光源寿命50,000時間
- 取付可能天井厚5~25mm
- 調光器併用不可
- 【調光器具について】  
LED調光タイプ60VAまで  
LED非調光タイプ不可 蛍光灯不可  
白熱灯60Wまで

強制  
ON

非調光

ソフト  
スタート

フェード  
アウト

埋込穴  
100

埋込  
必要高  
80

LED交換  
不可


防雨形

温度保護  
機能付

基本照明ダウナイト

● × 26 (20+6)

DDL6102AW

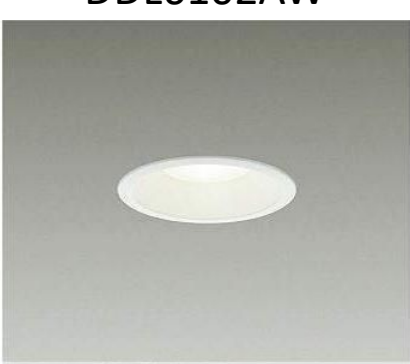

COBタイプ | 高気密Se形

DDL-6102 AW  
温白色 / 3500K・Ra83

|               |              |                          |
|---------------|--------------|--------------------------|
| 定格光束<br>470lm | 消費電力<br>4.6W | 固有エネルギー消費効率<br>102.1lm/W |
|---------------|--------------|--------------------------|

¥3,600-(税抜) (LED内蔵)

LED LED 4.6W  
白熱灯60W相当

- 銅板 白塗装
- アクリル 乳白(マット)
- 径φ116 埋込穴φ100 埋込深70mm 0.3kg
- 8VA
- 拡散バネル付
- AC100V
- 光源寿命60,000時間
- 取付可能天井厚5~25mm
- 調光器併用不可

LED交換  
不可

非調光

防雨形

60°

温度保護  
機能付

埋込穴  
100


埋込  
必要高  
70

傾斜天井  
55°

準耐火

● × 2

DDL6102YW

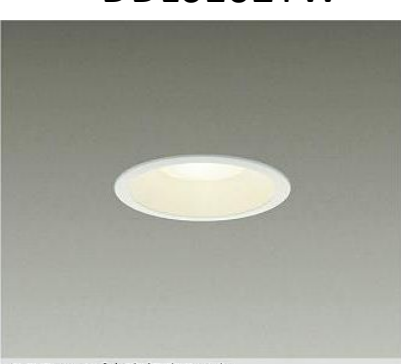

COBタイプ | 高気密Se形

DDL-6102 YW  
電球色 / 2700K・Ra83

|               |              |                         |
|---------------|--------------|-------------------------|
| 定格光束<br>440lm | 消費電力<br>4.6W | 固有エネルギー消費効率<br>95.6lm/W |
|---------------|--------------|-------------------------|

¥3,600-(税抜) (LED内蔵)

LED LED 4.6W  
白熱灯60W相当

- 銅板 白塗装
- アクリル 乳白(マット)
- 径φ116 埋込穴φ100 埋込深70mm 0.3kg
- 8VA
- 拡散バネル付
- AC100V
- 光源寿命60,000時間
- 取付可能天井厚5~25mm
- 調光器併用不可

LED交換  
不可

非調光

防雨形

60°

温度保護  
機能付

埋込穴  
100

埋込  
必要高  
70

傾斜天井  
55°

準耐火

● × 4

DDL6002AWG



COBタイプ | 高気密Se形

DDL-6002 AWG  
温白色 / 3500K・Ra83

|               |              |                         |
|---------------|--------------|-------------------------|
| 定格光束<br>470lm | 消費電力<br>5.8W | 固有エネルギー消費効率<br>81.0lm/W |
|---------------|--------------|-------------------------|

¥4,600-(税抜) (LED内蔵)

LED LED 5.8W  
白熱灯60W相当

- 銅板 白塗装
- アクリル 乳白(マット)
- 径φ116 埋込穴φ100 埋込深71mm 0.3kg
- 7VA
- 拡散バネル付
- AC100V
- 調光可能(1%~100%)
- 調光にはLED専用調光器(別売)をご使用ください。
- 光源寿命60,000時間
- 取付可能天井厚5~25mm

LED交換  
不可

調光

防雨形

60°

温度保護  
機能付

埋込穴  
100

埋込  
必要高  
80

傾斜天井  
55°

準耐火

PG House

伊藤友章様邸





新築工事

Lighting

Plan (図番 7-3)

2024. 12.1



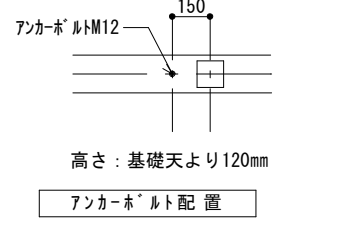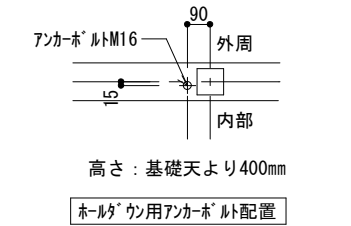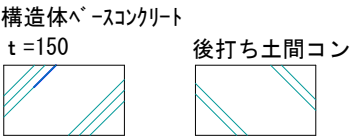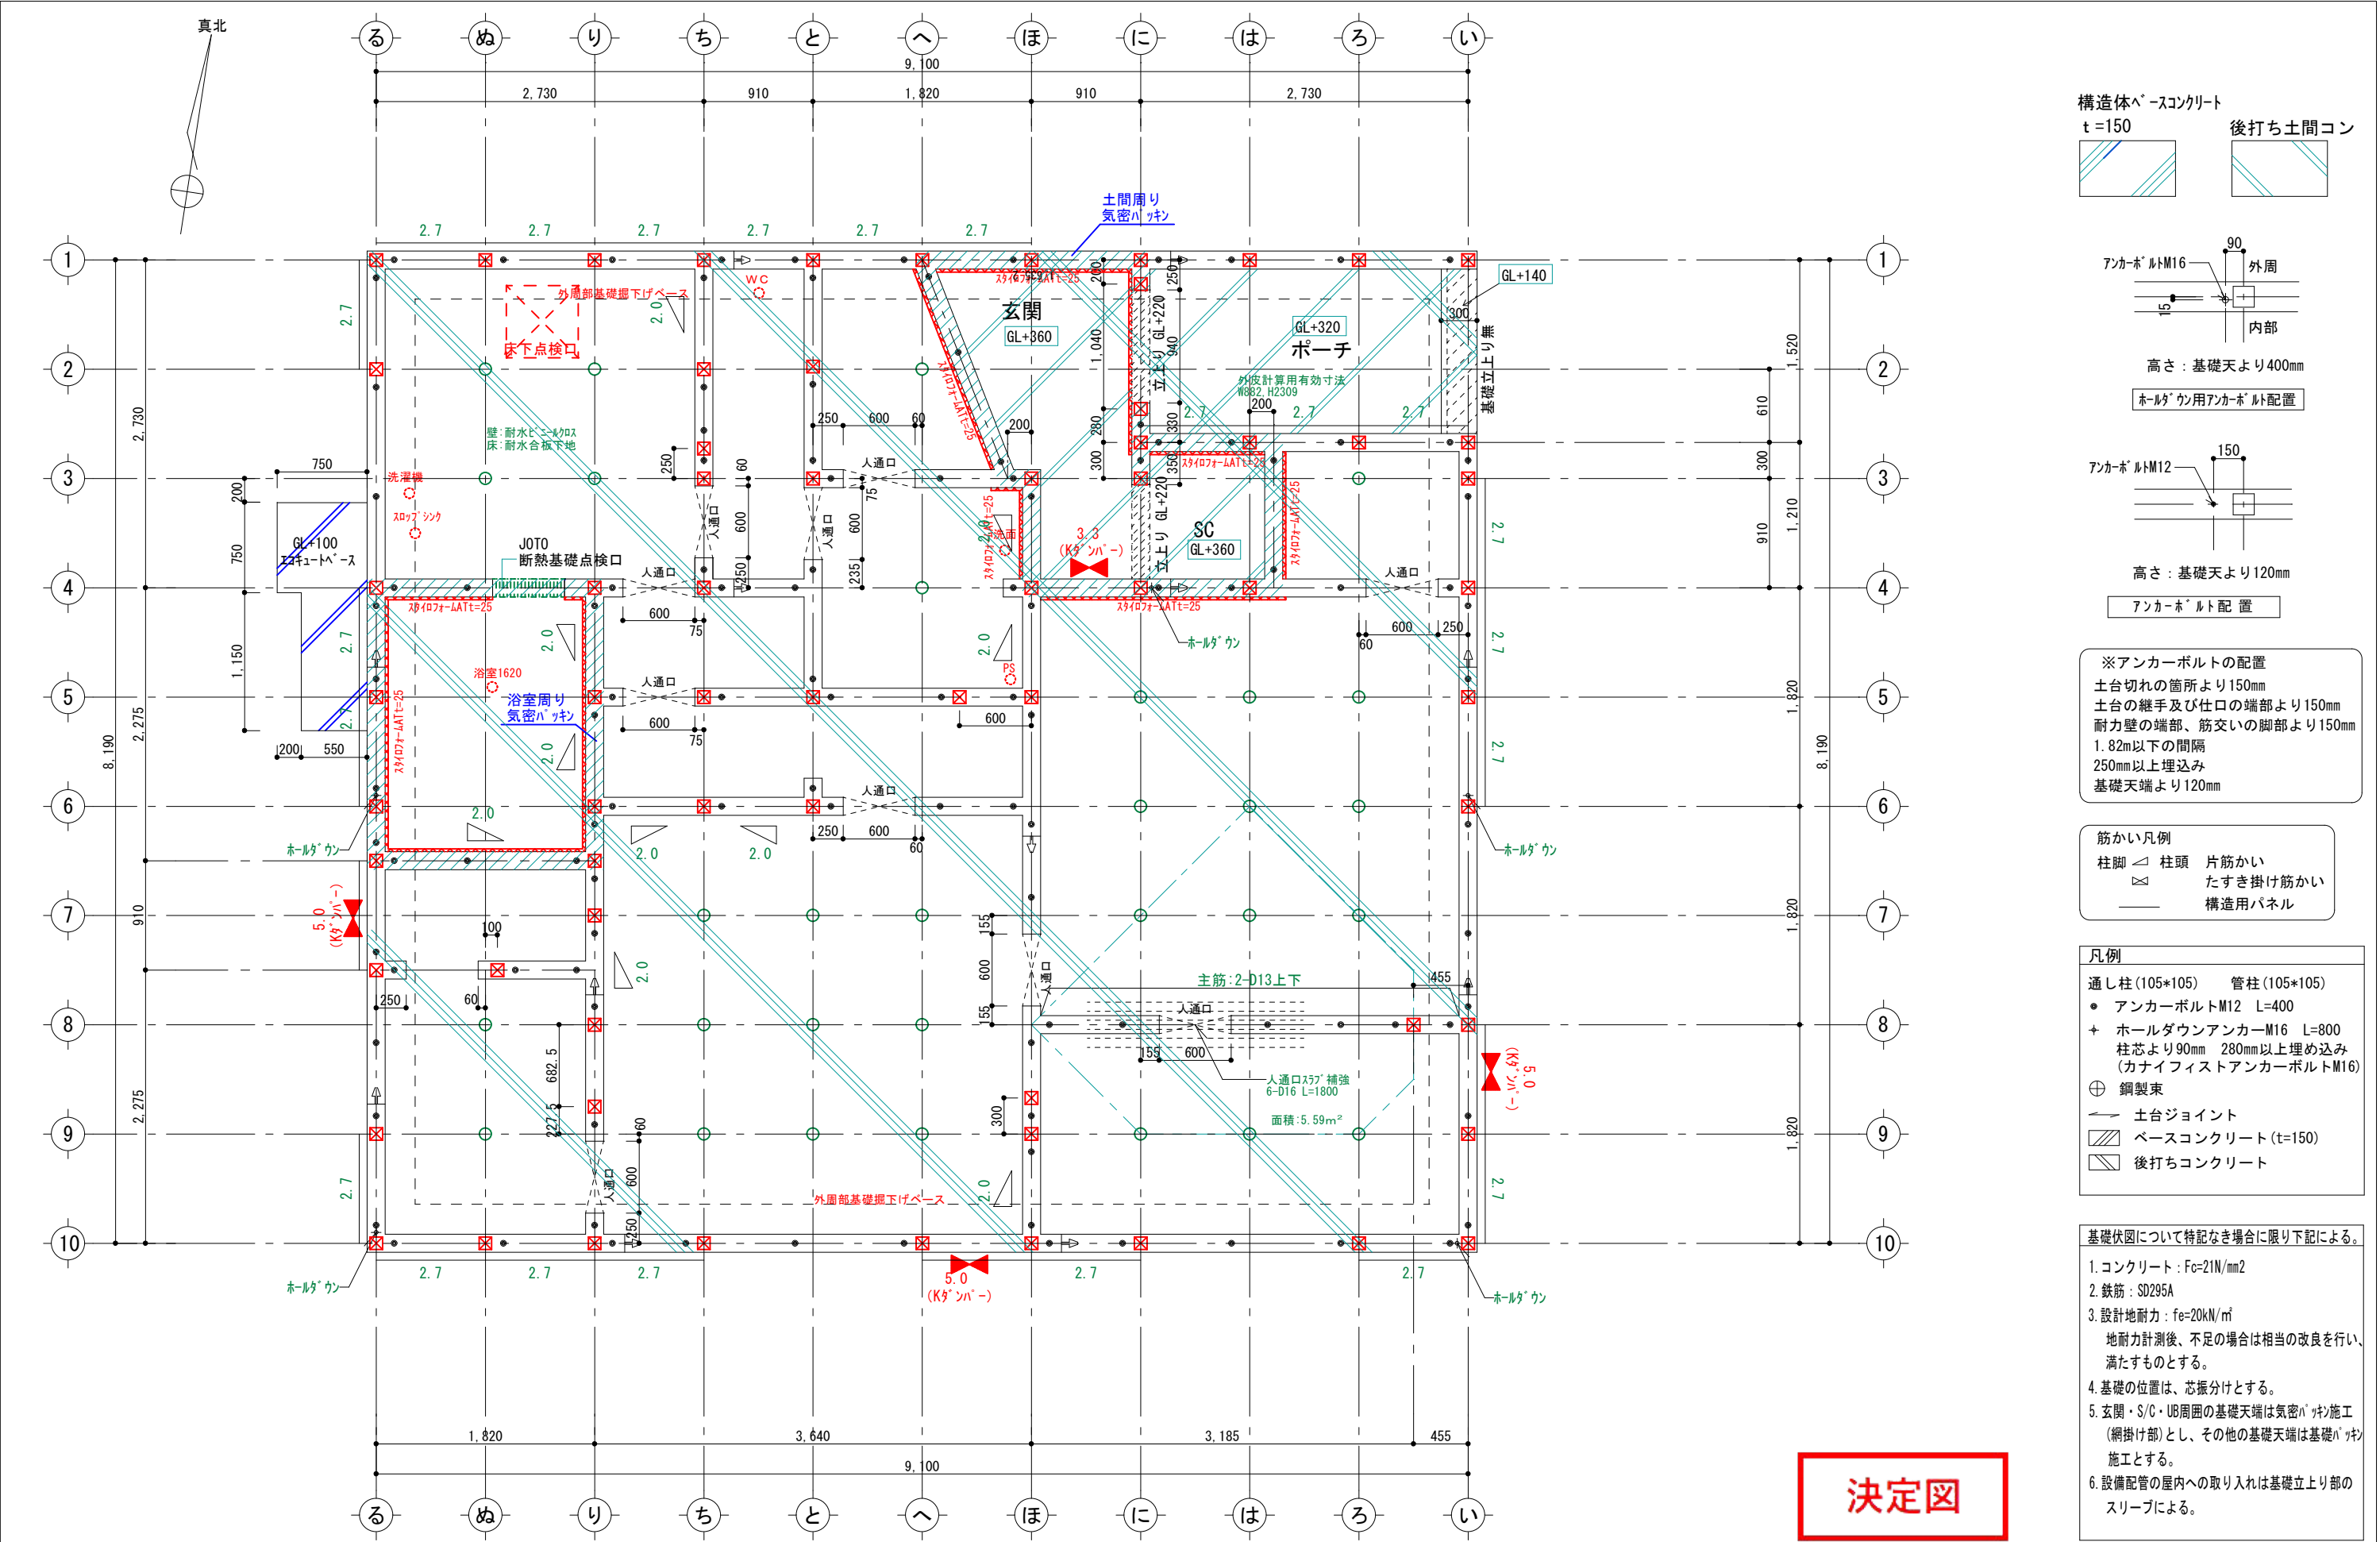


※アンカーボルトの配置  
土台切れの箇所より150mm  
土台の継手及び仕口の端部より150mm  
耐力壁の端部、筋交いの脚部より150mm  
1.82m以下の間隔  
250mm以上埋込み  
基礎天端より120mm

筋かい凡例  
柱脚 柱頭 筋かい  
たすき掛け筋かい  
構造用パネル

凡例  
通し柱(105\*105) 管柱(105\*105)  
● アンカーボルトM12 L=400  
+ ホールダウンアンカーM16 L=800  
柱芯より90mm 280mm以上埋め込み  
(カナイフリストアンカーボルトM16)  
⊕ 鋼製束  
土台ジョイント  
ベースコンクリート (t=150)  
後打ちコンクリート

基礎伏図について特記なき場合に限り下記による。

- コンクリート：Fc=21N/mm2
- 鉄筋：SD295A
- 設計地耐力：fe=20kN/m<sup>2</sup>  
地耐力計測後、不足の場合は相当の改良を行い、満たすものとする。
- 基礎の位置は、芯振分けとする。
- 玄関・S/C・UB周囲の基礎天端は気密パ'ン施工（網掛け部）とし、その他の基礎天端は基礎パ'ン施工とする。
- 設備配管の屋内への取り入れは基礎立上り部のスリーブによる。

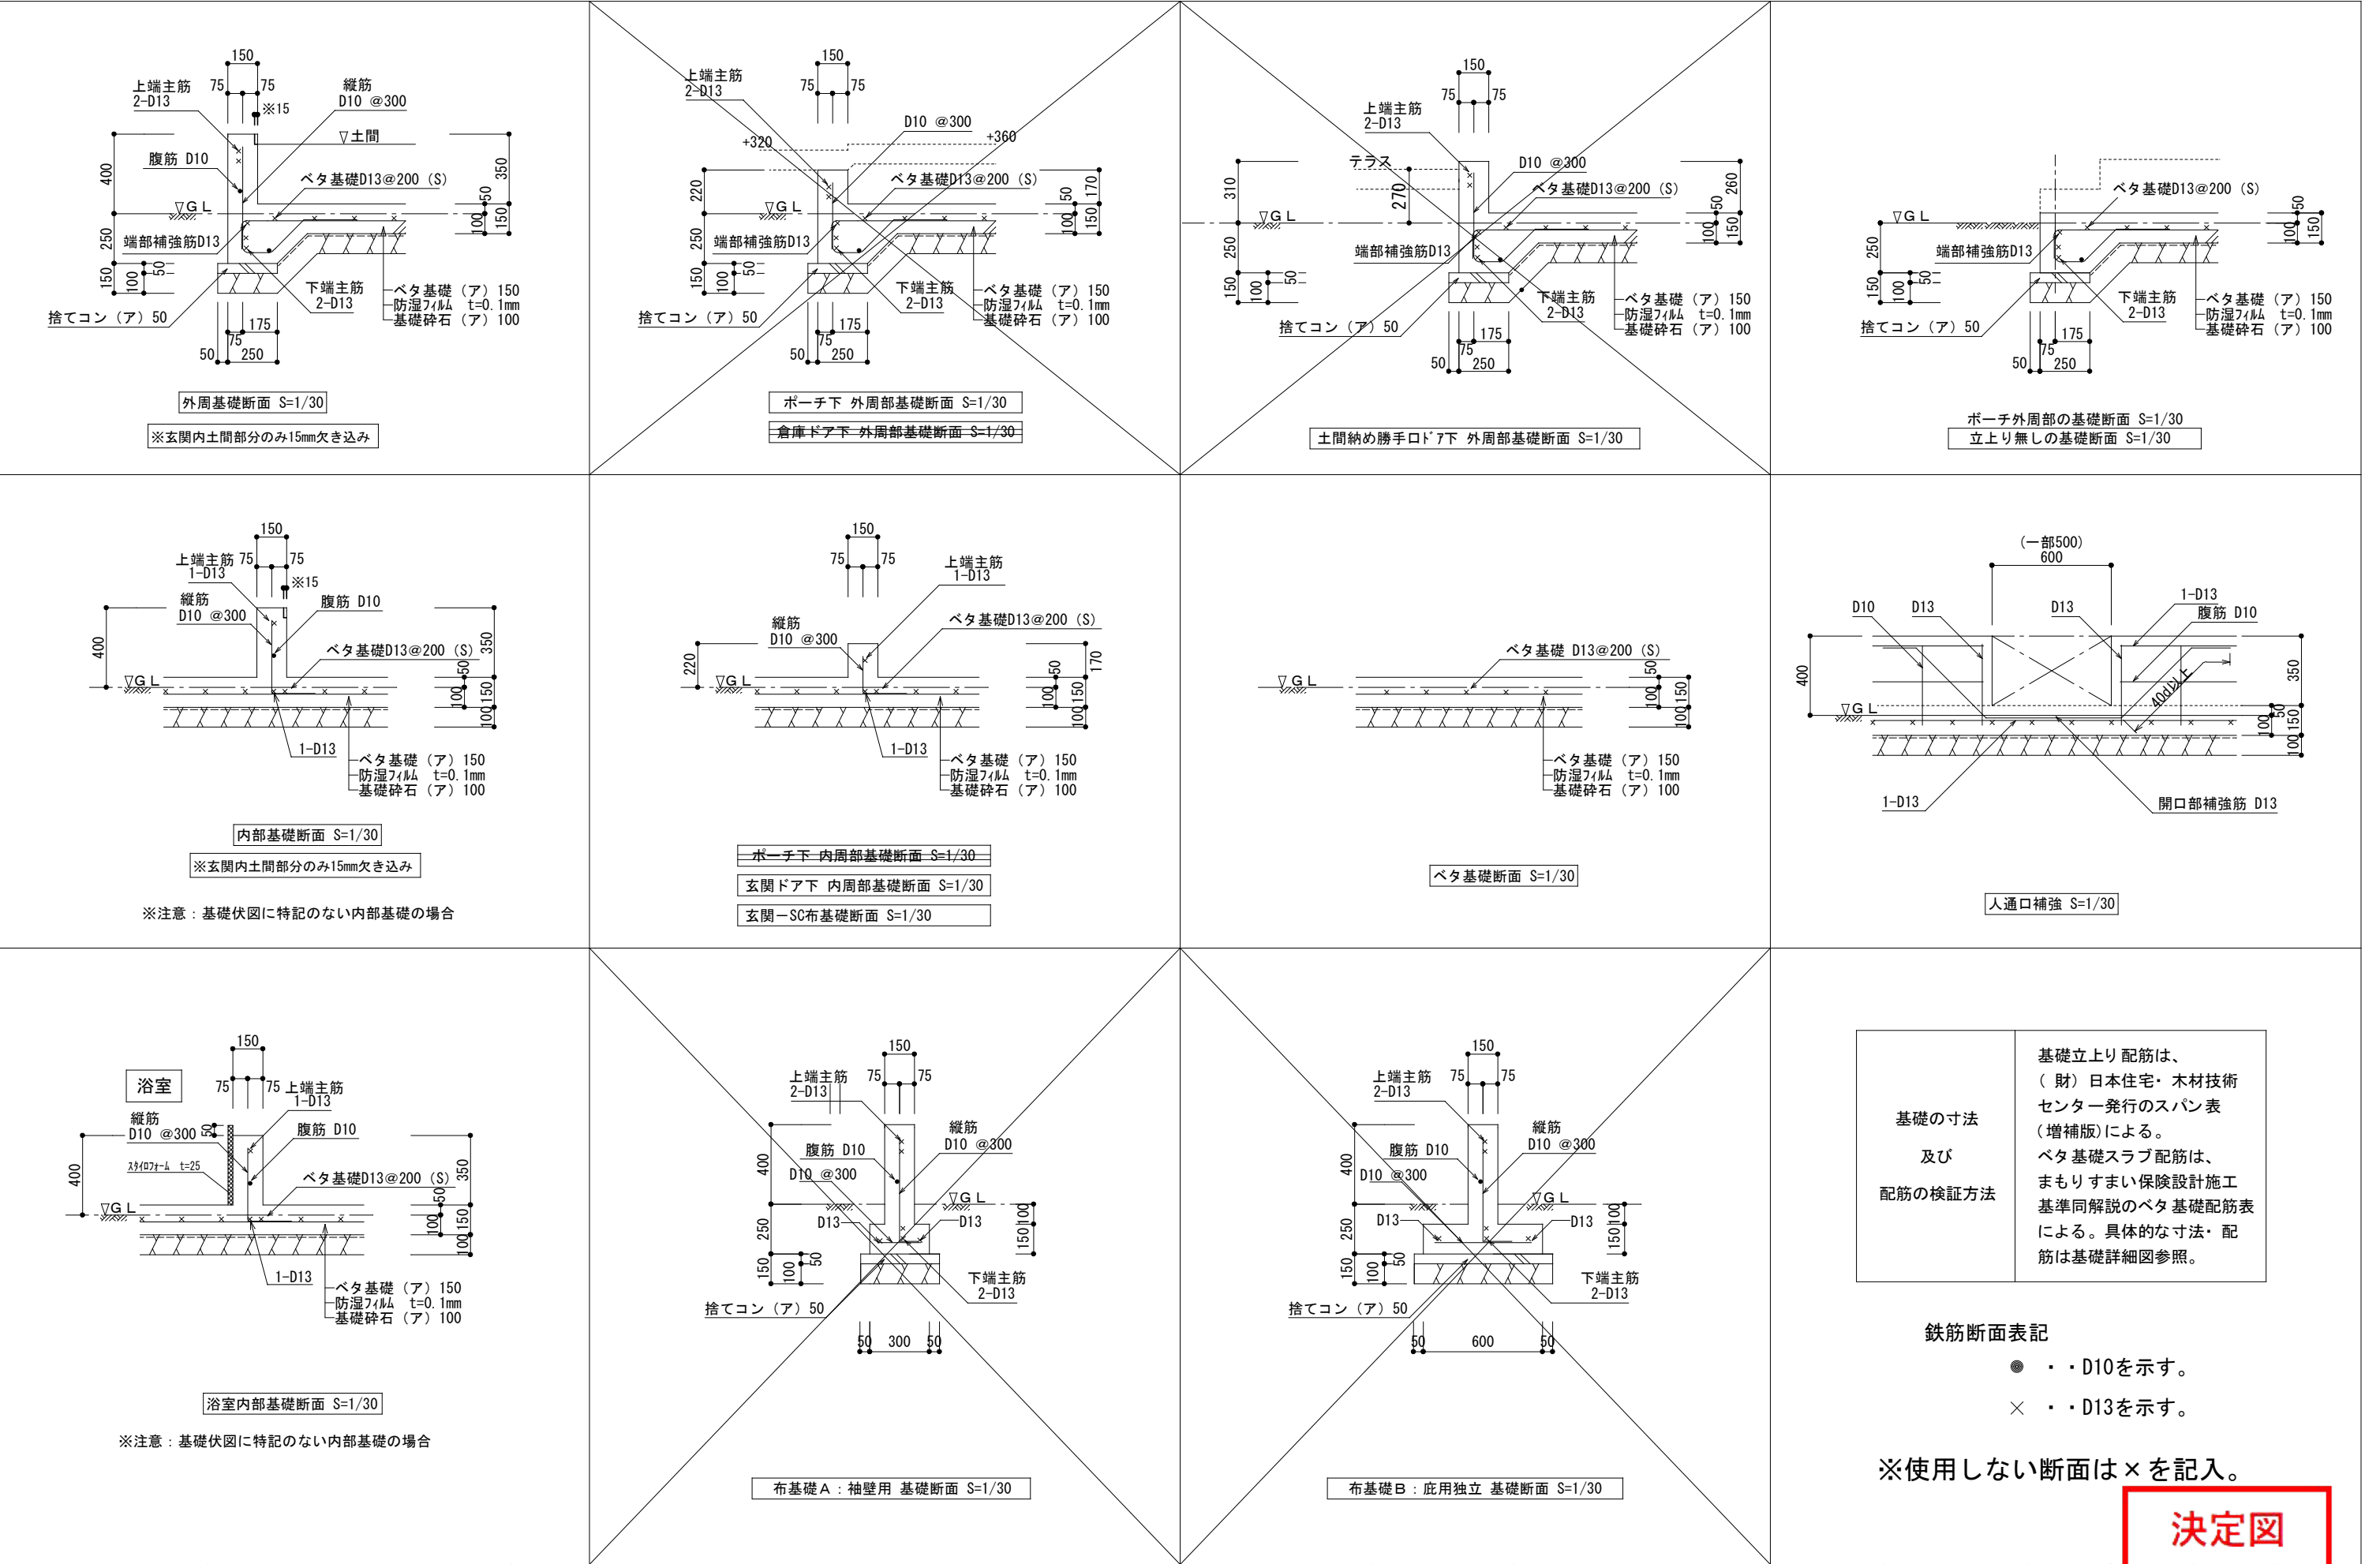

基礎の寸法  
及び  
配筋の検証方法


基礎立上り配筋は、  
(財)日本住宅・木材技術  
センター発行のスパン表  
(増補版)による。  
ベタ基礎スラブ配筋は、  
まもりすまい保険設計施工  
基準同解説のベタ基礎配筋表  
による。具体的な寸法・配  
筋は基礎詳細図参照。

鉄筋断面表記


●・・・D10を示す。  
×・・・D13を示す。

※使用しない断面は×を記入。

決定図

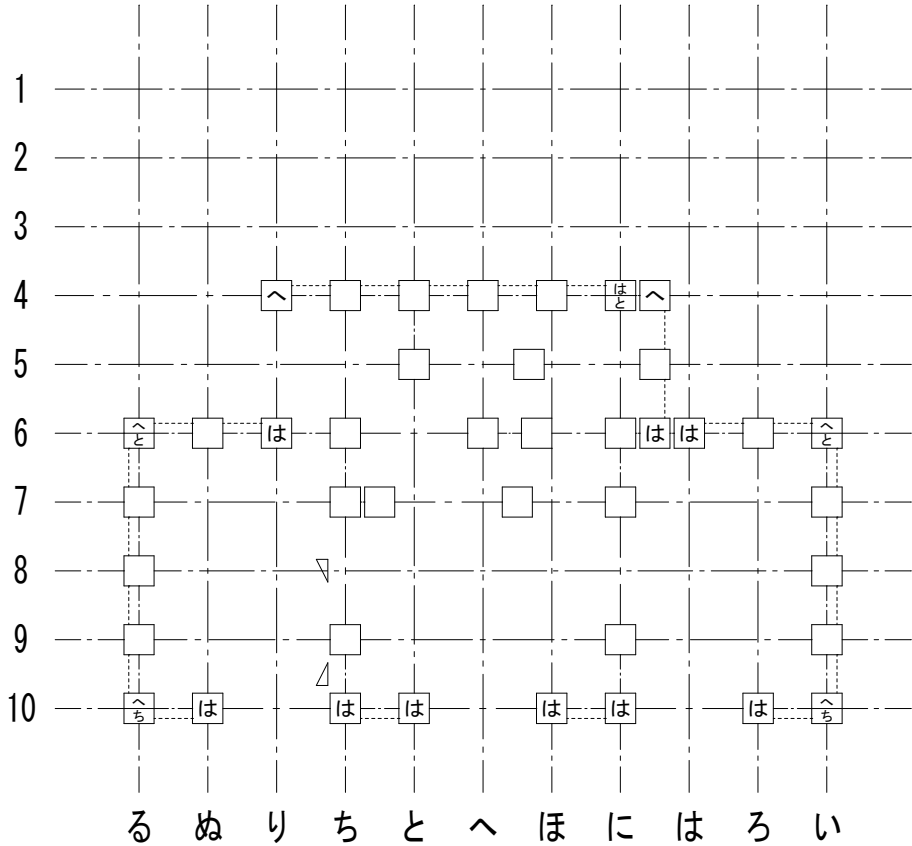

2階柱壁伏図

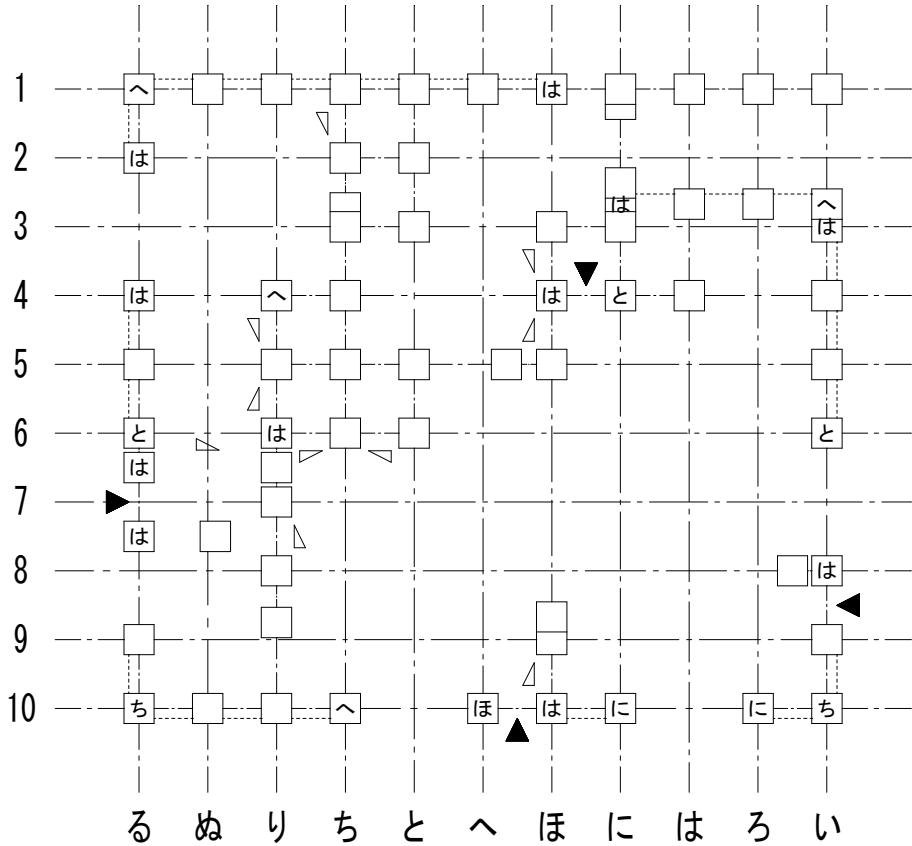

1階柱壁伏図

| 接合部凡例 |              |                              |      | *接合部凡例はユーザ設定されたものです。 |         |
|-------|--------------|------------------------------|------|----------------------|---------|
| 記号    | 仕様（カナイ金物）    |                              | N    | 倍率                   |         |
| SBCP  | スリムビルドコーナー75 |                              | 0.00 | 1.00                 |         |
| SBCP  | スリムビルドコーナー75 |                              | 0.65 | 1.00                 |         |
| SBCP  | は            | スリムビルドコーナー75                 | 1.00 | 1.00                 |         |
| ARCG  | に            | アレントコーナー合板用                  | 1.40 | 2.20                 |         |
| ARCG  | ほ            | アレントコーナー合板用                  | 1.60 | 2.20                 |         |
| ARCG  | へ            | アレントコーナー合板用                  | 1.80 | 2.20                 |         |
| HD15  | と            | ブレイブホールダウン B-HD15            | 2.80 | 3.60                 |         |
| HD20  | ち            | ブレイブホールダウン B-HD20            | 3.70 | 4.70                 |         |
| HD25  | り            | ブレイブホールダウン B-HD25            | 4.70 | 4.80                 |         |
| HD30  | ぬ            | ブレイブホールダウン B-HD30            | 5.60 | 7.20                 |         |
| J1    | る            | 腰掛け蟻若しくは大入れ蟻掛け+羽子板*ルト、短冊金物   |      | 1.90                 | 梁継手・仕口用 |
| J2    | を            | 腰掛け蟻若しくは大入れ蟻掛け+羽子板*ルト、短冊金物×2 |      | 3.00                 | 梁継手・仕口用 |

※表示なき金物は「は」とする。

| 接合部凡例 |           |                              |      | *接合部凡例はユーザ設定されたものです。 |         |
|-------|-----------|------------------------------|------|----------------------|---------|
| 記号    | 仕様（タナカ金物） |                              | N    | 倍率                   |         |
| FCP   | フックコーナー   |                              | 0.00 | 1.00                 |         |
| FCP   | フックコーナー   |                              | 0.65 | 1.00                 |         |
| FCP   | は         | フックコーナー                      | 1.00 | 1.00                 |         |
| CCP   | に         | シナコーナー                       | 1.40 | 2.20                 |         |
| CCP   | ほ         | シナコーナー                       | 1.60 | 2.20                 |         |
| CCP   | へ         | シナコーナー                       | 1.80 | 2.20                 |         |
| HD15  | と         | ビス止めホールダウンU HD15             | 2.80 | 3.60                 |         |
| HD20  | ち         | ビス止めホールダウンU HD20             | 3.70 | 4.70                 |         |
| HD25  | り         | ビス止めホールダウンU HD25             | 4.70 | 4.80                 |         |
| HD30  | ぬ         | ビス止めホールダウンU HD15×2（HD35）     | 5.60 | 7.20                 |         |
| J1    | る         | 腰掛け蟻若しくは大入れ蟻掛け+羽子板*ルト、短冊金物   |      | 1.90                 | 梁継手・仕口用 |
| J2    | を         | 腰掛け蟻若しくは大入れ蟻掛け+羽子板*ルト、短冊金物×2 |      | 3.00                 | 梁継手・仕口用 |

※表示なき金物は「は」とする。

| 筋かいの種類に応じた筋かいの端部の接合部の仕様 |           |                                                                                                |
|-------------------------|-----------|------------------------------------------------------------------------------------------------|
|                         | 筋かいの種類    | 接合部の仕様（構造方法）                                                                                   |
| イ                       | 鉄筋φ9      | 柱又は横架材を貫通し、三角座金を介してナット締め、又は鋼板添え板を用い鋼板を柱及び横架材にCN90, 8本平打ち                                       |
| ロ                       | 筋かい:15×90 | 柱・横架材を欠き込み、柱・横架材双方に対してN65, 5本平打ち                                                               |
| ハ                       | 筋かい:30×90 | 鋼板添え板t=1.6mmを筋かいに対してボルトφ12及びCN65, 3本平打ち、柱に対してCN65, 3本平打ち、横架材に対してCN65, 4本平打ち。筋かいプレートBP同等品       |
| ニ                       | 筋かい:45×90 | 鋼板添え板t=2.3mmを筋かいに対してボルトφ12及びスクリュー釘φ4.5L50, 7本平打ち、柱及び横架材に対してスクリュー釘φ4.5L50, 5本平打ち。筋かいプレートBP-2同等品 |
| ホ                       | 筋かい:90×90 | 柱又は横架材にボルトφ12mmを用いて一面剪断接合                                                                      |

| 胴差と通し柱の接合部の仕様 |                                                                 |                                           |
|---------------|-----------------------------------------------------------------|-------------------------------------------|
|               | 胴差と通し柱の条件                                                       | 仕口                                        |
| T1            | 通し柱の片側に胴差が来る場合                                                  | 胴差を柱にかたぎ大入れ短ほぞ差しの上、羽子板ボルト、かね折り金物又は同等以上の仕口 |
| T2            | 通し柱の両側に胴差が来る場合                                                  | 胴差を柱にかたぎ大入れ短ほぞ差しの上、短冊金物又は、同等以上の仕口で胴差相互を緊結 |
| T3            | 通し柱と胴差の接合部の近くに90×90以上の筋かいが来る場合（通し柱が建物の出隅にあるか、筋かい壁が外壁と直交して接する場合） | 胴差を通し柱に、15KN用引き寄せ金物を水平に用いて緊結              |

決定図