
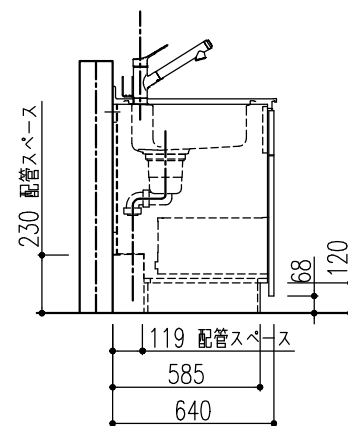
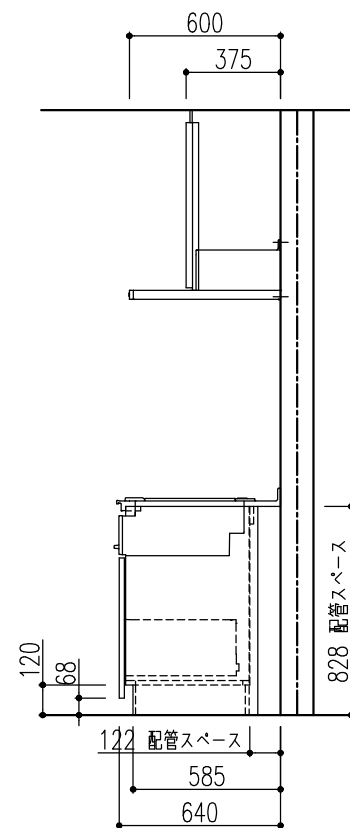
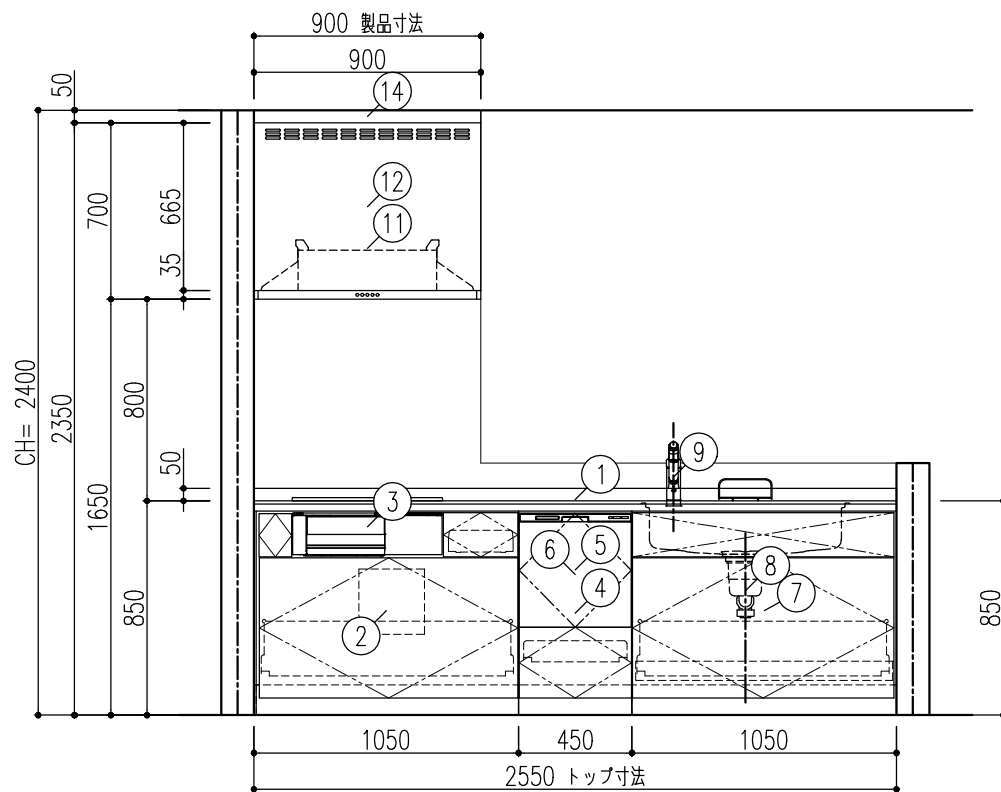
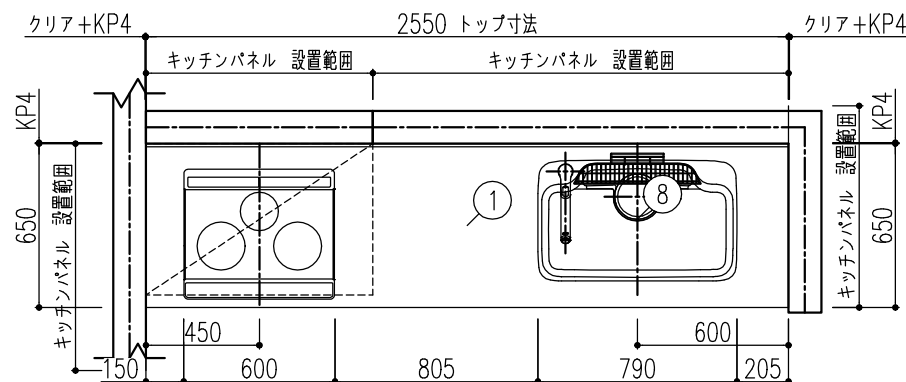
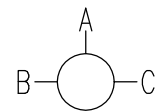


[illegible]

【ご注意】

- 壁面仕上材（キッチンパネル・タイルなど）の貼付下端位置が変わります。〔機能図参照〕
- 記載のキャビネット寸法は扉前面までの呼び寸法です。キャビネット本体の寸法・扉厚み等は商品ガイドの巻末資料をご確認ください。
- 記載のワークトップ、カウンター、エンドパネル、サイドパネルの寸法は呼び寸法です。詳細寸法は商品ガイドの巻末資料をご確認ください。
- レンジフード電源プラグ仕様：2芯電源プラグ（アース工事が必要です。）

特記事項 扉色 VK5:グレージュスタック 取手 [M]スリム取手 (ブラック) ワークトップカラー 【DW】ソルティホワイト	物件名	PG有玉西町分譲住宅 様	案件No.	図面名	担当	図面	図番 : 株式会社 LIXIL
			A2407DDD0E066X	レイアウト図	栗野 友仁		
	仕様	ES21	見積No.	縮尺	日付		
			M24074457351-002	1/30	2024.07.25		

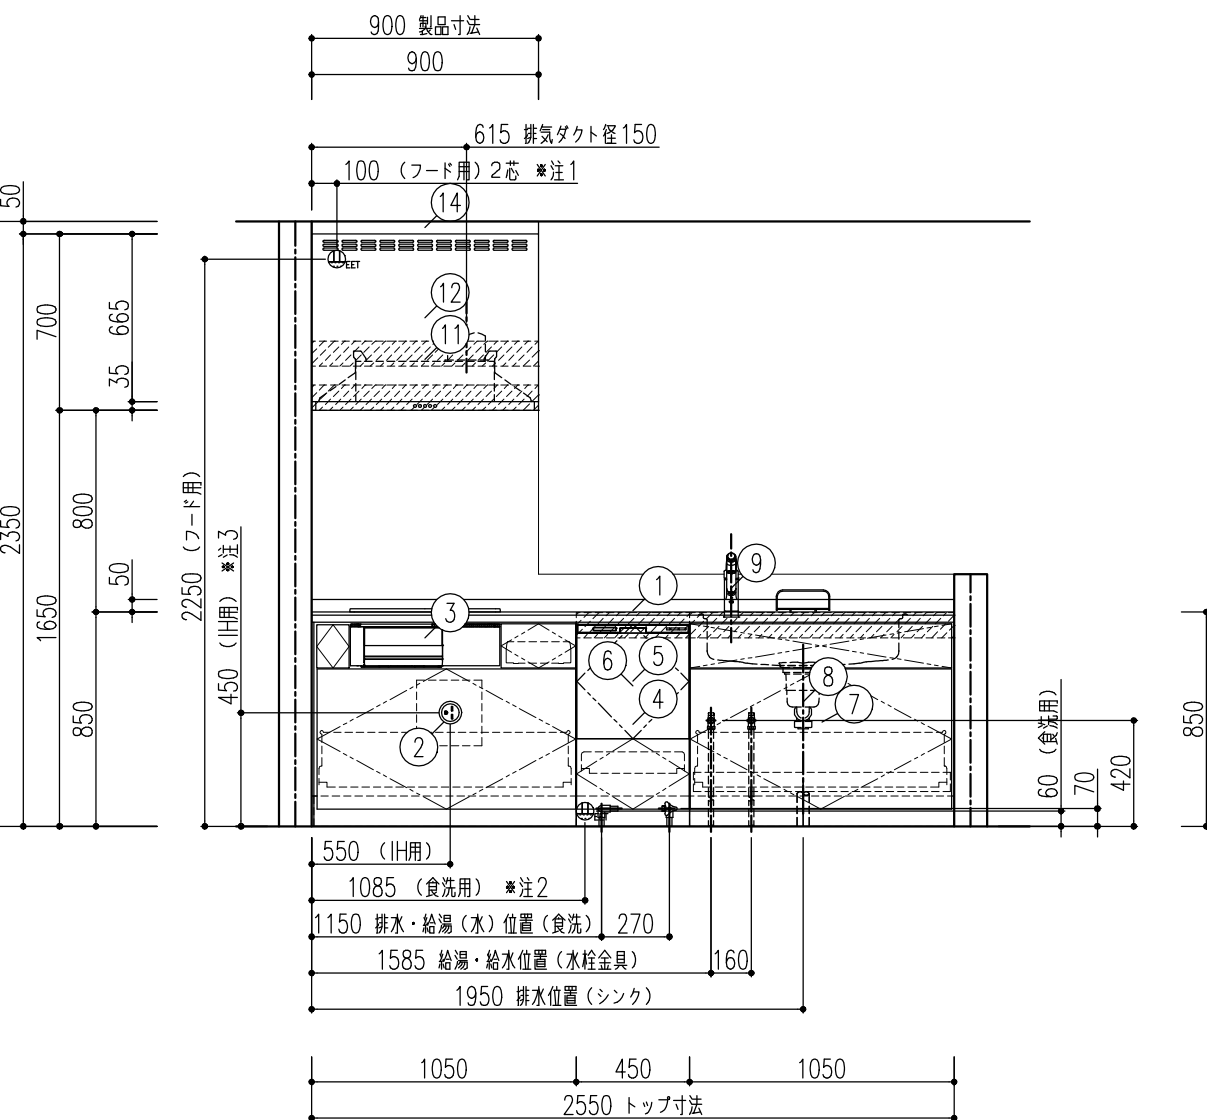

注1) 125V・15A 2極接地極付アースターミナル付コンセント 【専用】 (フード用)

注2) 125V・15A 2極接地極付アースターミナル付コンセント 側板取付【専用】


注3) 250V・30A 2極接地極付コンセント 【専用】

【 ご注意 】


- 壁面仕上材(キッチンパネル・タイルなど)の貼付下端位置が変わります。 [機能図参照]
- 記載のキャビネット寸法は扉前面での呼び寸法です。キャビネット本体の寸法・扉厚み等は商品ガイドの巻末資料をご確認ください。
- 記載のワークトップ、カウンター、エンドパネル、サイドパネルの寸法は呼び寸法です。詳細寸法は商品ガイドの巻末資料をご確認ください。
- 電気・ガス・給排水・換気等は法令・規定に従って有資格者が行ってください。
- 水道工事は排水配管工事となります。
- 取付・設置に際し、各製品の取付・設置説明書や図面の機能図を必ずお読み下さい。
- 内線規程上、各機器のプラグ仕様に関わらず建築側には接地極付コンセントを推奨しています。
- レンジフードにはアース線は同梱されておりません。別途 御用意願います。
- レンジフード電源プラグ仕様：2芯電源プラグ(アース工事が必要です。)
- 壁付けでレンジフード上に天井フィラーを設置する場合は、構壁に下地が必要となります。下地位置は、機能図を参照願います。
- 食洗機内配管の詳細については必ず別添の機能図をご確認ください。
- 食器洗い乾燥機配管は、給水接続か給湯接続かお客様に確認したうえで施工願います。

A3 20240725MGJ1-0

B面

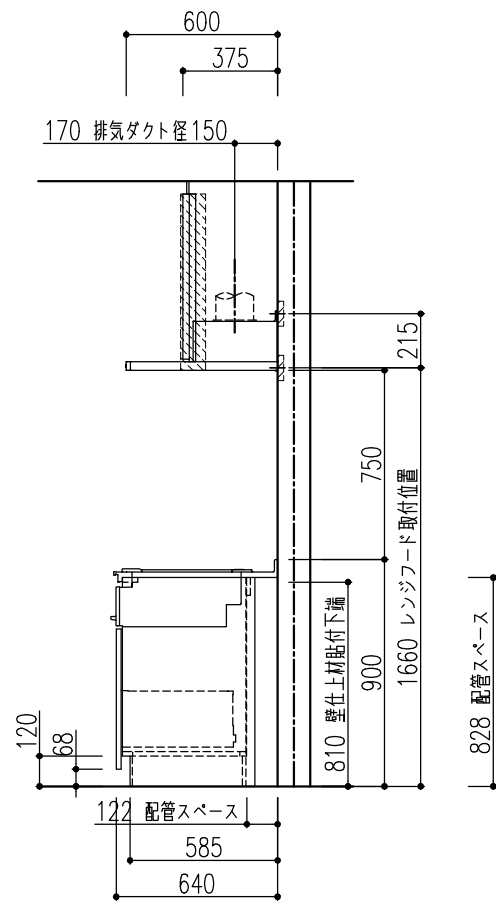

C面

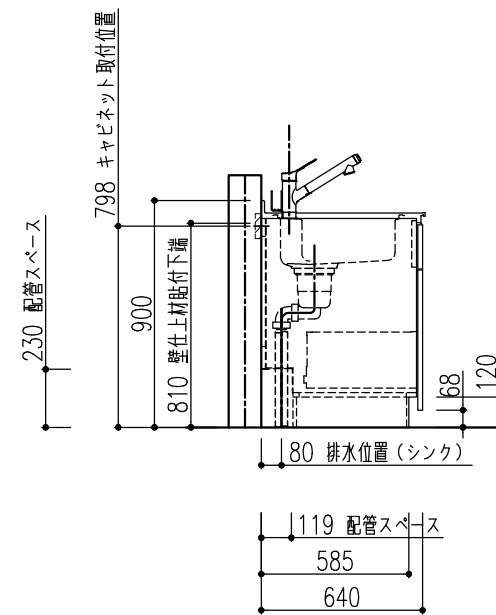


特記事項 扉色 VK5:グレージュスタック 取手 [M]スリム取手 (ブラック) ワークトップカラー 【DW】 ソルティホワイト	物件名	PG有玉西町分譲住宅 様	案件No.	図面名	担当	図面	図番
			A2407DDD0E066X	納まり図	栗野 友仁		株式会社 LIXIL
	仕様	ES21	見積No.	縮尺	日付		
			M24074457351-002	1/30	2024.07.25		

■壁面仕上材（キッチンパネル）取付注意事項〔貼付向き〕

●キッチンパネルの貼付向き


キッチンパネルの貼付向きにご注意ください。

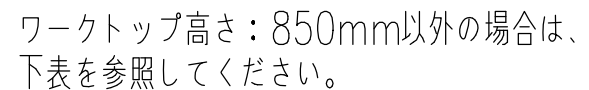

ワークトップ高さ	キッチンパネル 貼付下端位置
900	860
875	835
825	785
800	760

●上表はキッチンパネルの場合です。ステンレスパネルの場合は、キッチンパネルの「取付・設置説明書」を参照してください。

《ワークトップ高さ：850mmの場合》

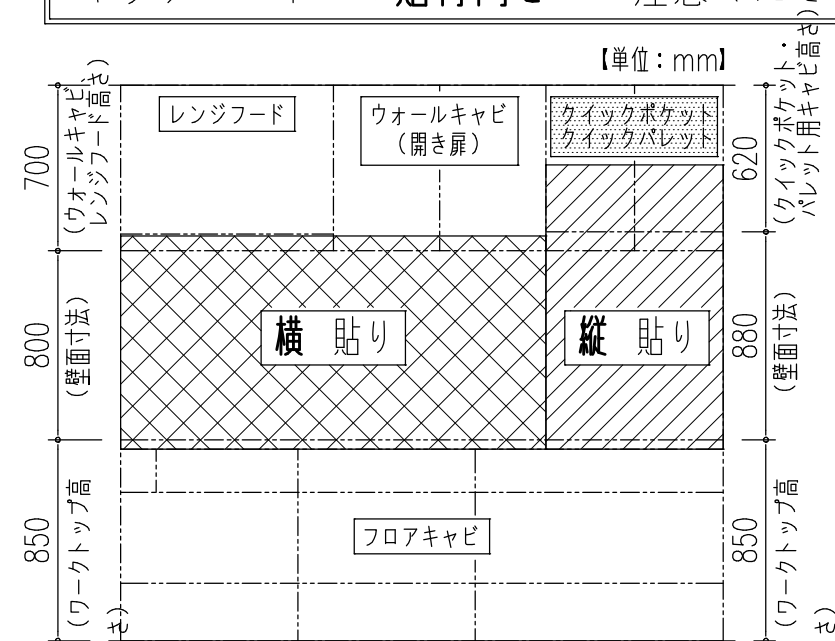

《キッチンパネル 貼付方向》
総高さ：2350mmの場合

	ウォールキャビ		
	開き扉		クイックボックet クイックバレット
	H700	H600 H500	H700 (620) H600 (520)
キッチンパネル 貼付方向	横	縦	

【ご注意】
リシエル以外のクイックパレットは、
キャビネットの背板高さがショート
(-80mm)してありませんので、
『開き扉』のキッチンパネル貼付方向
に合せてください。


《バックガード：なし、ワークトップ高さ：850mm、ウォールキャビ高さ：700mmの場合》

■レンジフード取付注意事項（壁面取付時）

レンジフードを取付ける場合は下地の桟が厚み30mm以上、幅100mm以上、ビス固定位置が桟の端部から25mm以上であることを確認してください。



また、壁強度などの詳細は「レンジフード設置説明書」を必ず事前に確認してください。

取付位置については、取付設置図を確認してください。

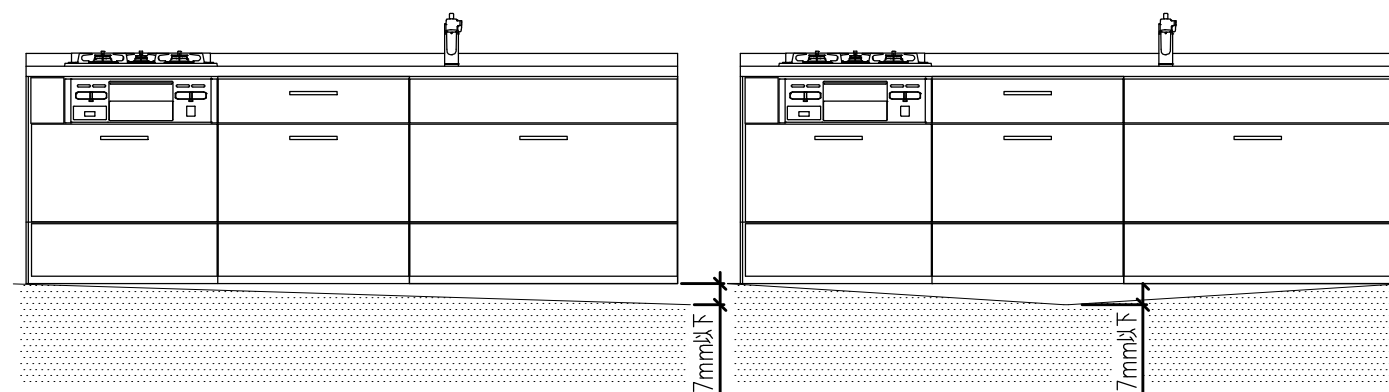


床の不陸は、7 mm 以下に抑えるようにしてください。不陸が大きい場合は、現場責任者に床の修正を依頼してください。

※キャビネット取付時には不陸調整スペーサー等で水平になるように設置してください。

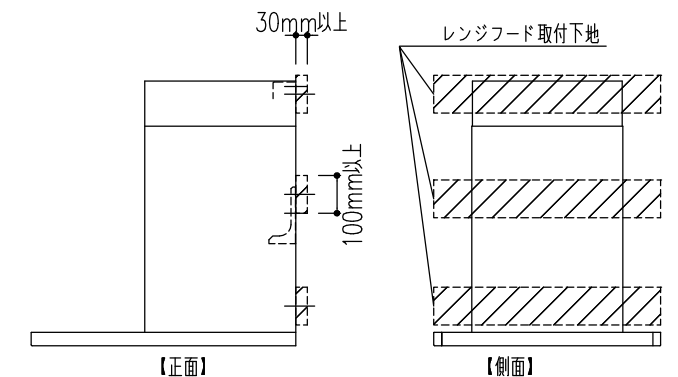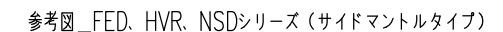

参考図 NBHシリーズ

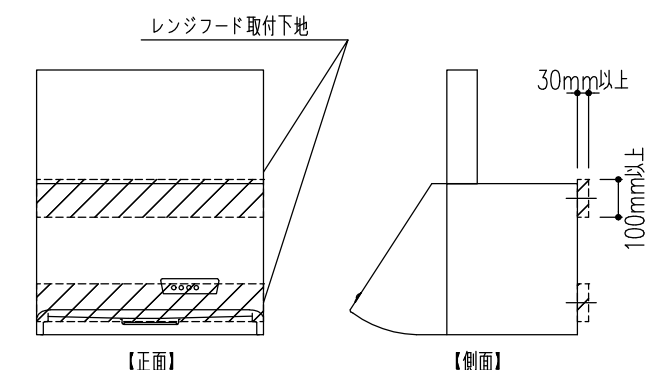


株工


株式会社 LIXIL

■天井フィラーの取付（レンジフード上部）

レンジフード横に壁がくるレイアウト時は、横壁にも取付桎が必要になります。

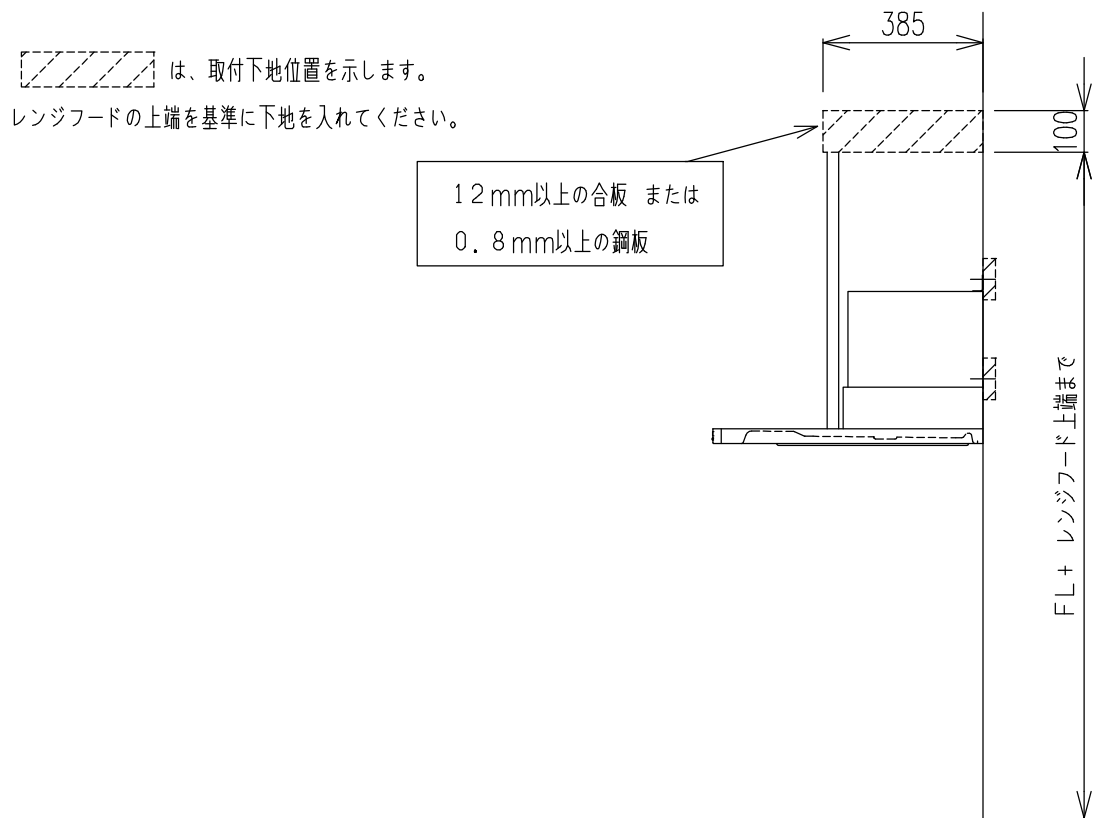

■ ASRフード

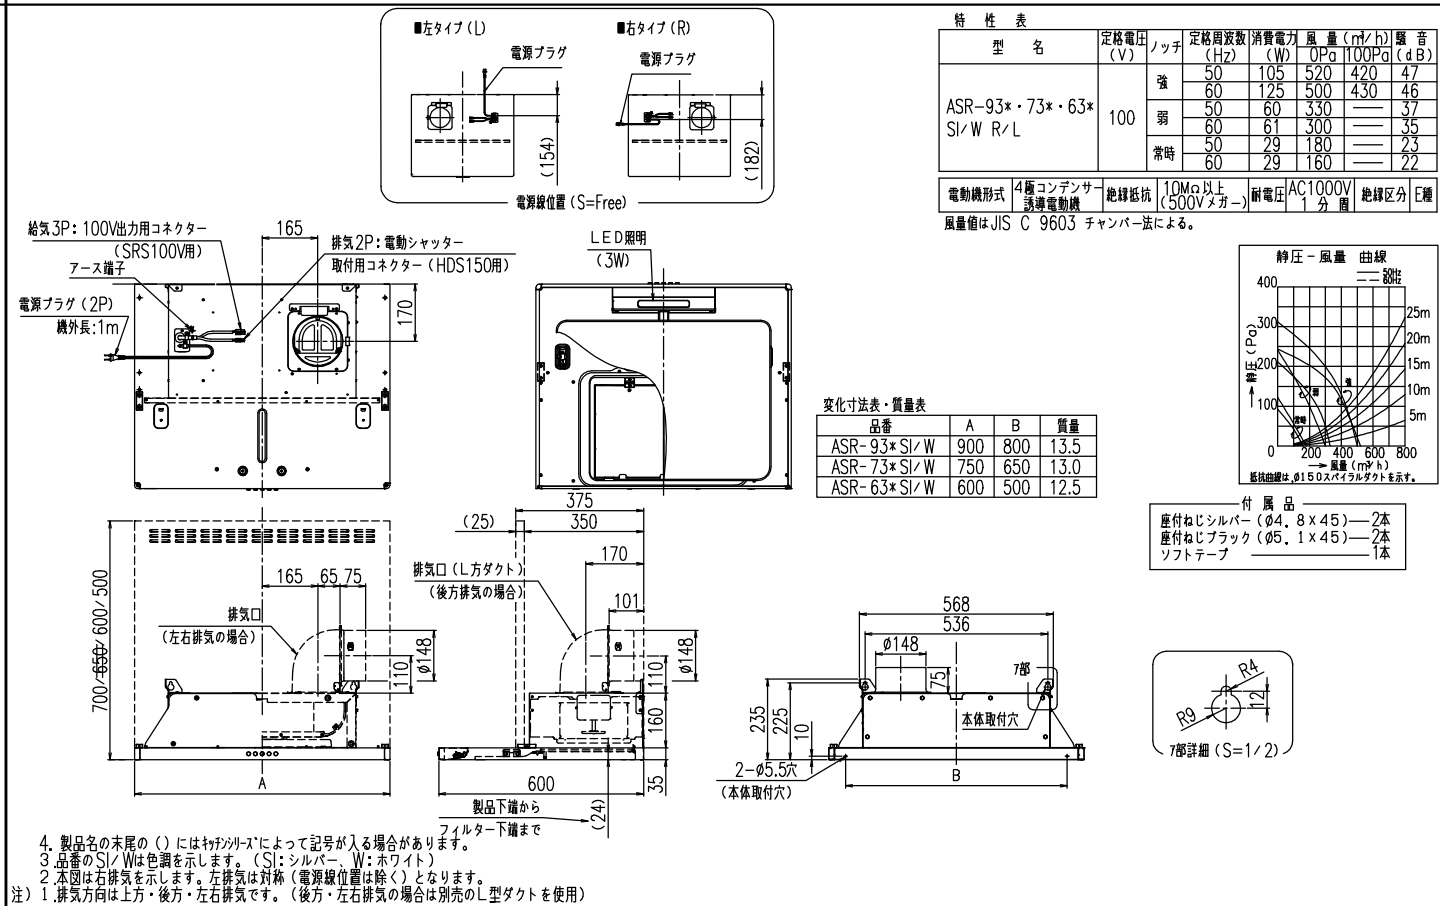


■IHヒーター用コンセント推奨位置図 / 壁付設置の場合

※コンセントや電源プラグが、引き出しおよびIHヒーター用仕切板（オプション）に接触しないように注意してください。

※木製キャビネットの配管スペース付キャビネットを使用する場合は点検口裏の配管スペース内にコンセントを設置してください。

キッチン高さ	電源線高さ
800	400
850	450
900	500

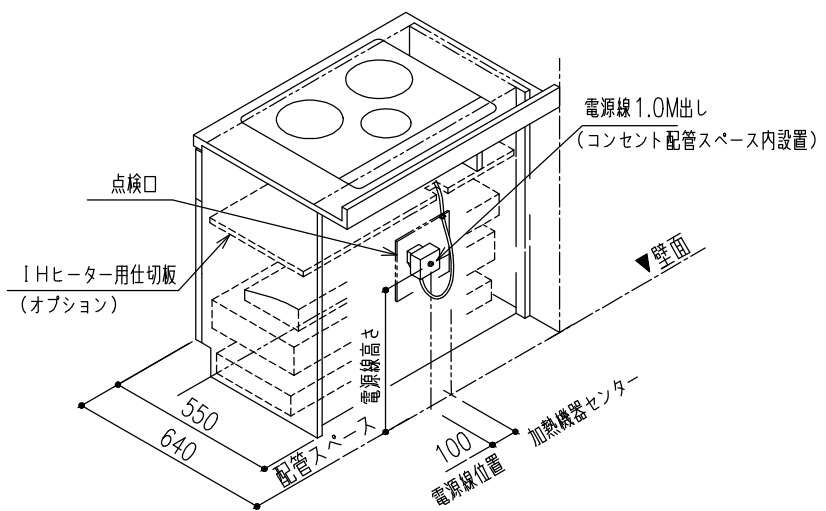

注意：引き出しおよびIHヒーター用仕切板（オプション）に接触しないように上記寸法を参照してください。

特記事項
扉色 VK5:グレイジュスタック
取手 [M]スリム取手(ブラック)
ワークトップカラー 【DW】ソルティホワイト

物件名
仕様

PG有玉西町分譲住宅 様

ES21

案件No.

A2407DDDOE066X

見積No.

M24074457351-002

[illegible]

機能図

縮尺

担当

栗野 友仁

202

面図

07.25

図番 :

株三


100

株式会社 LIXIL

■ 止水栓図（床立上げ）

床立上げ配管


配管立上げ寸法は、止水栓芯までの高さを示しています。

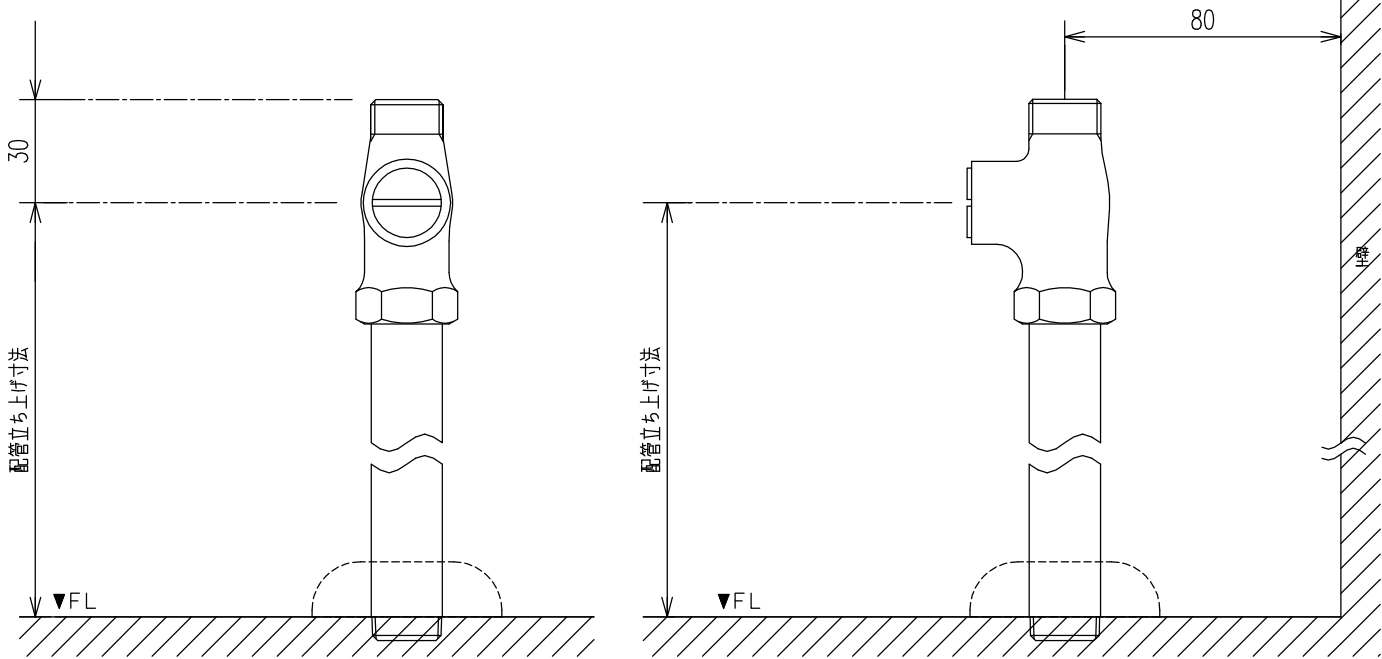

	特記事項 扉色 VK5:グレージュスタック 取手 [M]スリム取手（ブラック） ワークトップカラー 【DW】 ソルティホワイト	物件名 仕様	PG有玉西町分譲住宅 様 ES21	案件No.	図面名	担当	図面	図番
				A2407DDD0E066X	機能図	栗野 友仁		株式会社 LIXIL
				見積No.	縮尺	日付		
				M24074457351-002		2024.07.25		


■ キッチン取付者さま向け 動画コンテンツ ■
商品取付けの注意点を2次元コードでご視聴いただけます。
取付日より前に、是非ご確認ください。

不陸の確認と調整

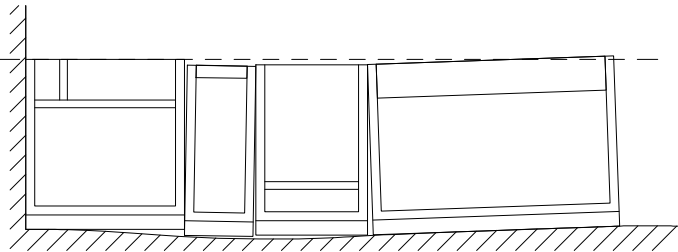


作成日：2024年02月07日

人造大理石カウンターL型キッチン

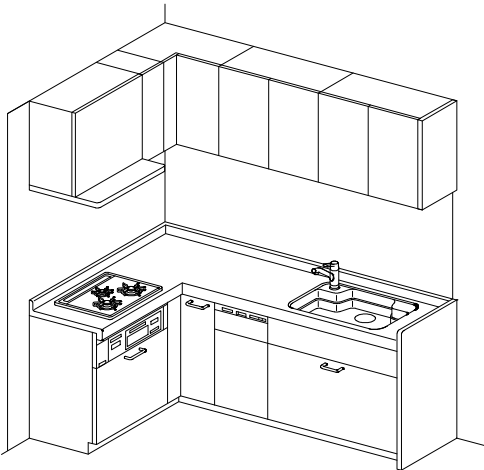

作成日：2024年02月07日

センターキッチン（ペニンシュラ型）

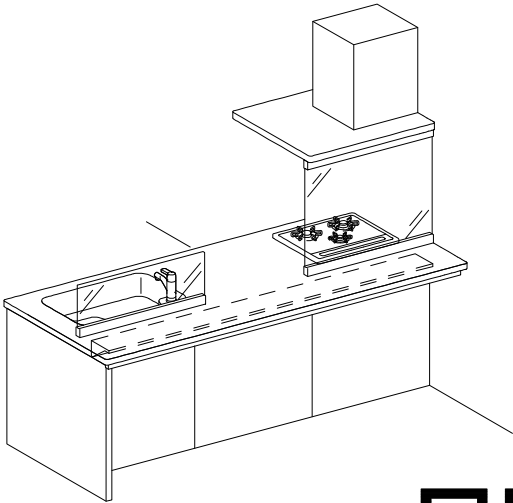

作成日：2024年02月07日

マグネットキッチンパネル





マグネット キッチンパネル
「取付・設置」ポイント



作成日：2024年03月06日

特記事項 扉色 VK5:グレージュスタック 取手 [M]スリム取手（ブラック） ワークトップカラー 【DW】ソルティホワイト	物件名	PG有玉西町分譲住宅 様	案件No.	図面名	担当	図面	図番
	仕様	ES21	A2407DDD0E066X	機能図	栗野 友仁		株式会社 LIXIL
			見積No.	縮尺	日付		
			M24074457351-002		2024.07.25		

■ キッチン取付者さま向け 動画コンテンツ ■
商品取付けの注意点を2次元コードでご視聴いただけます。
取付日より前に、是非ご確認ください。

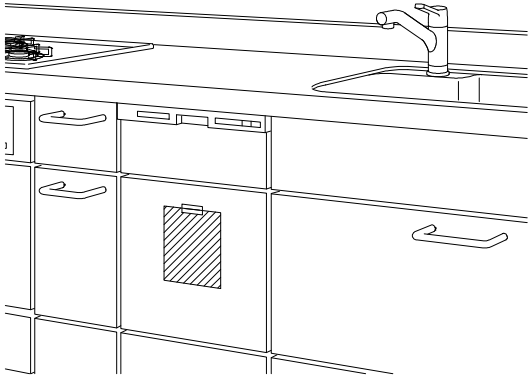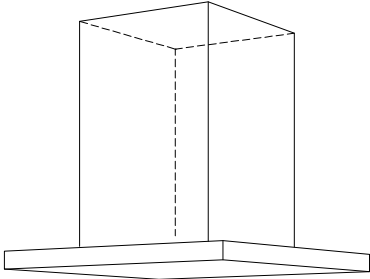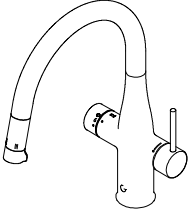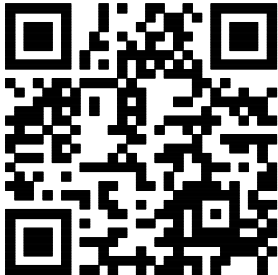I H加熱機器関連 I H加熱機器 仕切り板  作成日：2024年02月07日	食器洗い乾燥機   作成日：2024年02月07日	センターフード型レンジフード (天吊りフード)   作成日：2024年06月03日	ミネラル浄水栓 Greentap   作成日：2024年06月03日
---	--	--	--

	特記事項 扉色 VK5:グレージュスタック 取手 [M]スリム取手 (ブラック) ワークトップカラー 【DW】 ソルティホワイト	物件名 仕様	PG有玉西町分譲住宅 様		案件No.	図面名	担当	図面	図番
					A2407DDD0E066X	機能図	栗野 友仁		株式会社 LIXIL
					見積No.	縮尺	日付		
			ES21		M24074457351-002		2024.07.25		