

■ 仕 様				■ HEAT20 G1	
断熱工事		■ 床:カネライトフォーム t65 ■ 土間床等の外周:スタイロフォームAT t25 ■ 壁:アクアフォームLITE吹付 t85 ■ 天井:アクアフォームLITE吹付 t170			
床下換気		■ 基礎パッキン JOTO (玄関・UB周り:気密基礎パッキン)			
防虫防蟻		■ 土壌処理・木部 ガントナーMC			
■ 外 部 仕 上 表				■ 22条地域	
部位		仕上・仕様・メーカー		色番・品番	
屋根		■ ガルバリウム鋼板(t0.35)UK立平 ニスクカラーPro GH 軒先通気金物 日本住環境株式会社【REV-15】		GHK01 Sブラック	
パラペット笠木		■ なし			
破風・鼻隠		■ なし			
雨樋		(軒樋) ■ Panasonic サーフeskエアFS-I型		ミルクホワイト	
		(縦樋) ■ Panasonic S30角樋		ミルクホワイト	
軒天	屋根軒	■ ニチハ軒天5 木目調 910×1820×5		ライト	
	ポーチ軒	■ 神島化学 t= 6mm 軒天ボード エンボス		Wファリーホワイト	
	バルコニー軒	■ なし			
オーバーハング水切り		■ ガルバリウム鋼板 ※外壁合わせ JOTO:HF-A3550		ホワイト	
外壁	通気金物(15mm)	■メイン	ニチハ エモンekセラード16 Vシリーズ しぶきV	MG/パニラホワイトII	
	※下地面材:タイガーEXハイパー	■アクセントA	なし		
	防火認定 PC030BE-4028	■アクセントB	なし		
玄関ポーチ		■ 床 LIXILパセオ300/PSO-FIO 4		-	
基礎		■ 立上り巾木: モルタル刷毛引き		-	
基礎水切り金物		■ JOTO鋼板製 防鼠材付き水切り JOTO:WMF-N35		ホワイト	
バルコニー	床・内壁	■ 床:FRP防水仕上(グレー) 壁:外壁同仕上げ		-	
	笠木	■ アルミ笠木		ブラック	
外部建具		■ Ykkap APW330 (アルゴンガス日射遮蔽型 断熱タイプLow-E プル-) ・SD、TSで記載がないものは、オペレーターハンドルとする ・オペレーター付サッシは固定網戸とする ・グレモンハンドル式サッシの選択箇所は可動網戸とする		外観 ブラック 内観 外観色と同じ ※網戸付 樹脂スペーサ	
シャッター		■ なし			
軒天通気金物		日本住環境株式会社 SEV-15		ホワイト	
玄関扉		■ YKKapヴェナートD30(D2仕様) タグキーx3、非常用キーx2 (電池式) ※ピタットキー		ドア型: N08N ドア色: ガナッシュウォールナット ハンドル: ストレート 色 ブラック	
外部物干し金物		■ 川口技研LP型-550 バルコニー内側壁		ホワイト	
換気フード		■ 局所換気扇(トイレ 浴室 キッチンフード) 防火ダンパー無		外気フード: ホワイト	
		■ ダクトレス熱交換換気システム (日本スティーベル株式会社) VLR-70E 防火ダンパー無		外気フード: W ホワイト	

■ 構 造 概 要					
基礎	■ RCベタ基礎コンクリート				
通し柱・管柱	■ 構造用集成材 105×105		間柱	■ 集成材	
土台	■ 桧 105×105	大引き	■ 桧 90*90	筋交い	■ 構造用製材 火打梁 ■ 鋼製火打(当社基準により米松あり)
桁・梁	■ 構造用製材及び集成材			制震装置	■ Kダンパー (株)アイ・エム・エー
■ 設 備 装 着 品					
住宅設備	部位	メーカー	商品名 ※ 詳細は見積り、プレゼン参照	見積りNo.	(日付)
	キッチン	LIXIL	■ ES I型D650 食洗器 IH 壁付レンジフードASR	見積り番号 : M24074457351-003-2 (日付) 2024.7.25	
	バックカウンタ ※オプション	LIXIL	■ なし	見積り番号 : (日付)	
	浴室	LIXIL	■ AX1616 ※換気扇	見積り番号 : M24074457351-003-1 (日付) 2024.7.25	
	1Fトイレ	LIXIL	■ ベーシアシャワートイレ 白 ● タオル掛け: KF-AA70D(リング) タンク手洗 有り ● 紙巻き器: CF-AA22H /WA	見積り番号 : M24074457351-003-4 (日付) 2024.7.25	
	2Fトイレ	LIXIL	■ ベーシアシャワートイレ 白 ● タオル掛け: KF-AA70D(リング) タンク手洗 有り ● 紙巻き器: CF-AA22H /WA	見積り番号 : M24074457351-003-5 (日付) 2024.7.25	
	洗面台	LIXIL	■ EV W750(D500タイプ) 扉:グロスホワイト [引出しタイプ シングルハンドシャワー スタンダードLED三面鏡 ● タオル掛け: KF-AA71D(バー)	見積り番号 : M24074457351-003-3 (日付) 2024.7.25	
給排水設備	給湯器	■ エコキュート370L Panasonic NSシリーズ スタンダードモデル 追い焚きフルオート			
	排水	■ 下水			
	外水栓	■ 1 カ所 (平面図参照)	■ 外部立栓柱: PVC製 水栓柱12型【前澤化成工業】		
	外部ガーデンパン	■ 無し			
	その他	■ 洗濯機用単水栓: 緊急止水弁付 ■ 洗濯機用排水:トラップ金物(標準) ■ 排水さや管(長期優良住宅仕様)			
ガス配管設備	■ なし (平面図参照)				
電気設備	インターホン	■ パナソニック VL-SZ30KL			
	TVアンテナ	■ UHF + BS・110度CS／CSアンテナ [2K・4K・8K対応] ■ホワイト			
	エアコン	■ あり 設置場所: LDK 洋室②			
	ソーラー ※標準搭載	■ あり(Qセルズ) 12 枚 5.22 KW Re.RISE-G2 435 (1722×1134×30) ■ 蓄電池:無			
	その他				

	浜 岡 一 級 総 合 設 計 事 務 所 一級建築士事務所 静岡県知事登録第 (10)2441 号 一級建築士 大臣登録第 365879 号 西原利昌	LIFEFUND PG HOUSE	株式会社 LIFEFUND InDesign office 一級建築士事務所 事務所登録 (2)第7595号 一級建築士登録 第179770号 鈴木 達男 〒432-8023 静岡県浜松市中央区鴨江3丁目70番23号	年 月 日	2024.8.22	件名	PG有玉西 分譲		設計	IC	工務	図 番
				縮尺		図面	仕上表 1		倉田		青島	1-1


内 部 仕 上 表 （壁下地:石膏ボード12.5mm/天井下地:9.5mm）※脱衣室:床合板特類 下地									
階		床	巾木	壁	品番	廻 縁	天 井	品番	特記事項
1F	ポーチ	LIXILパセオ300/PSO-FIO 4							巾木立上り部はモルタル金鍍仕上
	玄関	LIXILパセオ300/PSO-FIO 4	ライン巾木(W)	ビニルクロス	SLP-250	突付	ビニルクロス	SLP-250	巾木立上り部はモルタル金鍍仕上
	ホール①	イタ銘木フロアーラステックt12 ブラックチェリー3P	ライン巾木(W)	ビニルクロス	SLP-250	突付	ビニルクロス	SLP-250	
	LDK	イタ銘木フロアーラステックt12 ブラックチェリー3P	ライン巾木(W)	ビニルクロス	SLP-250	突付	ビニルクロス	SLP-250	
	畳コーナー	1畳縁ありスタイロ畳 t55	畳寄せ	ビニルクロス	SLP-250	突付	ビニルクロス	SLP-250	畳縁:高田織物 浮No.13
	押入	イタ銘木フロアーラステックt12 ブラックチェリー3P	雑巾摺	ビニルクロス	SLP-250	突付	ビニルクロス	SLP-250	
	洗面所	フロアタイルt2.3 サンゲツIS-2070	H40ソフト巾木W97	ビニルクロス	SLP-250	突付	ビニルクロス	SLP-250	
2F	WC①	フロアタイルt2.3 サンゲツIS-2070	H40ソフト巾木W97	ビニルクロス	SLP-250	突付	ビニルクロス	SLP-250	
	ホール②	イタ銘木フロアーラステックt12 ブラックチェリー3P	ライン巾木(W)	ビニルクロス	SLP-250	突付	ビニルクロス	SLP-250	
	洋室①	イタ銘木フロアーラステックt12 ブラックチェリー3P	ライン巾木(W)	ビニルクロス	SLP-250	突付	ビニルクロス	SLP-250	
	洋室②	イタ銘木フロアーラステックt12 ブラックチェリー3P	ライン巾木(W)	ビニルクロス	SLP-250	突付	ビニルクロス	SLP-250	
	洋室③	イタ銘木フロアーラステックt12 ブラックチェリー3P	ライン巾木(W)	ビニルクロス	SLP-250	突付	ビニルクロス	SLP-250	
	WIC	イタ銘木フロアーラステックt12 ブラックチェリー3P	H40ソフト巾木W97	ビニルクロス	SLP-250	突付	ビニルクロス	SLP-250	
	WC②	フロアタイルt2.3 サンゲツIS-2070	H40ソフト巾木W97	ビニルクロス	SLP-250	突付	ビニルクロス	SLP-250	
物入・収納・CL etc		※接続する部屋と同仕様とする							

上框 & 付框	■ LIXILラシッサS 付框30×150 (全周廻し) 色: クリエペール		
階段	■ LIXIL KA 階段	ササラ:	プレシャスホワイト
	段板:	クリエペール	蹴込板: プレシャスホワイト
	ラウンド手摺:	クリエペール	手摺金物 プレシャスホワイト
	上段框:	クリエペール	長尺笠木156: LIXIL クリエペール
窓枠 ※YKKap	■ YKKap窓枠スルムタイプ	色	ピュアプレーン
	※浴室ドア枠 フクビ3方枠 []		
キッチン笠木 カウンター	■ ゴム集成カウンター(オスモカラー)	色	30627ロアーグリアmatt
	形状 L型(ジョイント加工)	t=30	
天井点検口	■ 天井アルミ点検口枠 450角	TAN45BW	フクビ化学工業 ミルキーホワイト
床下収納庫	■ 高気密型床下点検口断熱型	SPF-R6060 城東テクノ	収納付 (脱衣室) アイボリー(IV)
トイレ棚	■ 2階トイレ	D250	アートランバー棚(シェルホワイト)
室内物干し金物	■ なし		
1トイレ バックカウンター	■ アートランバー棚(シェルホワイト)	色	t=20
下足入	■ LIXILラシッサS	色	プレシャスホワイト
	サイズ: W800 D400	形状:	二の字型

支給品	■ 無し
備考	

内 部 建 具 表							
LIXIL		建具色：クリエイペール		枠色 ： 扉同色		※その他、下記特記による	
ラシッサS(標準)		把手 ： スクエアL (シャインニッケル) 丁番 固定枠(156) 外付戸当り ガイドピン床色合せ 引戸のみ上吊Wソフトモーション					
階	No	室名	形式	枠外W サイズ	デザイン	枠色	特記事項
				枠外H サイズ	建具色	把手	
1	1	LDK	片開き戸	—	LGC	—	
	WD			2000	—	—	
	2	洗面所	片引き戸	—	LAA	—	明り窓・表示錠
	WD			2000	—	—	
	3	押入	折れ戸	—	LAA	—	角型Lタテ取付
	WD			2000	—	—	
	4	パントリー	観音開	—	LAA	—	
	WD			2000	—	—	
	5	物入	観音開	—	LAA	—	
	WD			2000	—	—	
	6	WC①	片開き戸	—	LAA	—	明り窓・表示錠
	WD			2000	—	—	
2	7	WC②	片開き戸	—	LAA	—	明り窓・表示錠
	WD			2000	—	—	
	8	洋室①	片開き戸	—	LAA	—	
	WD			2000	—	—	
	9	洋室②	片開き戸	—	LAA	—	
	WD			2000	—	—	
	10	洋室③	片開き戸	—	LAA	—	
	WD			2000	—	—	

	浜 岡 一 級 総 合 設 計 事 務 所 一級建築士事務所 静岡県知事登録第 (10)2441 号 一級建築士 大臣登録第 365879 号 西原利昌	LIFEFUND 株式会社 LIFEFUND InDesign office 一級建築士事務所 事務所登録 (2) 第7595号 一級建築士登録 第179770号 鈴木 達男 〒432-8023 静岡県浜松市中央区鴨江3丁目70番23号	PG HOUSE	年 月 日	件名		設計 IC 工務 図 番
				2024.8.22	PG有玉西 分譲		
				縮尺	図面 仕上表 2		
						倉田 0 青島 1-2	

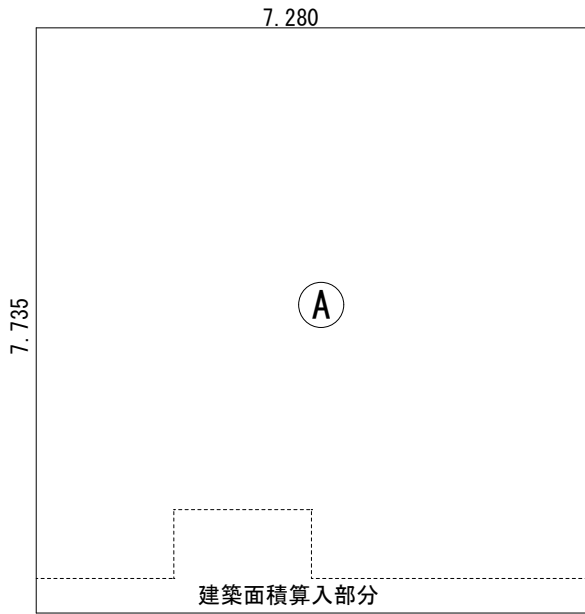


建築面積求積図 S=1/100

建築面積求積表

番号	計算式	(m)	面積 (㎡)
①	7.280 × 7.735		56.3108
合計			56.3108 56.31


(17.0坪)

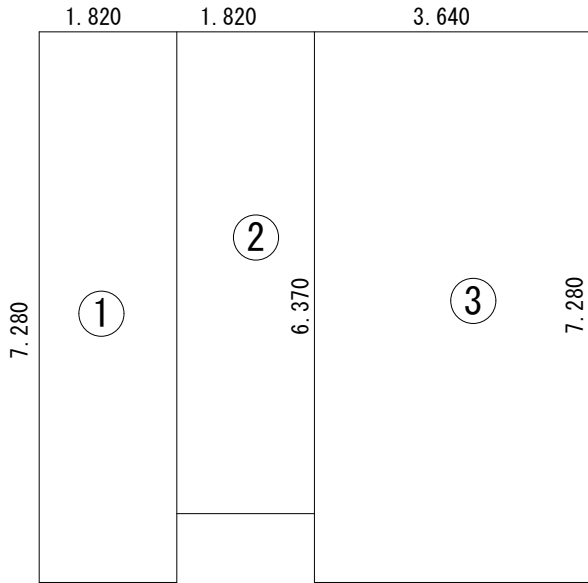

1階床面積図 S=1/100

1階床面積求積表

番号	計算式	(m)	面積 (㎡)
①	1.820 × 7.280		13.2496
②	1.820 × 6.370		11.5934
③	3.640 × 7.280		26.4992
合計			51.3422 51.34

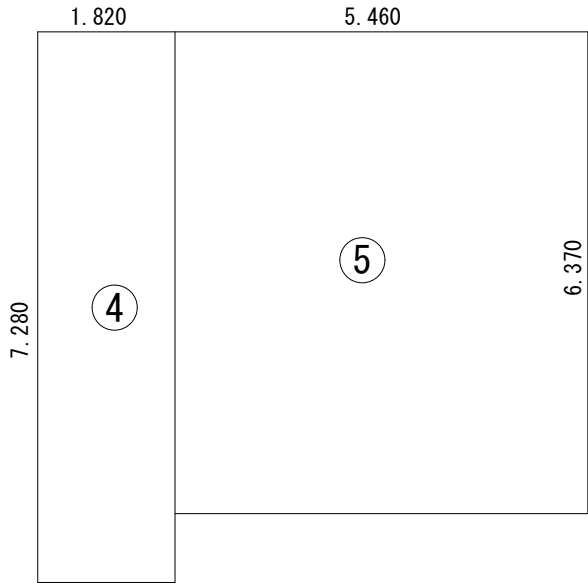

2階床面積図 S=1/100


2階床面積求積表

番号	計算式	(m)	面積 (㎡)
④	1.820 × 7.280		13.2496
⑤	5.460 × 6.370		34.7802
合計			48.0298 48.02

延べ床面積表

	番号	(m)	面積 (㎡)
1階床面積	① ② ③		51.34
2階床面積	④ ⑤		48.02
合計			99.36

(30.0坪)

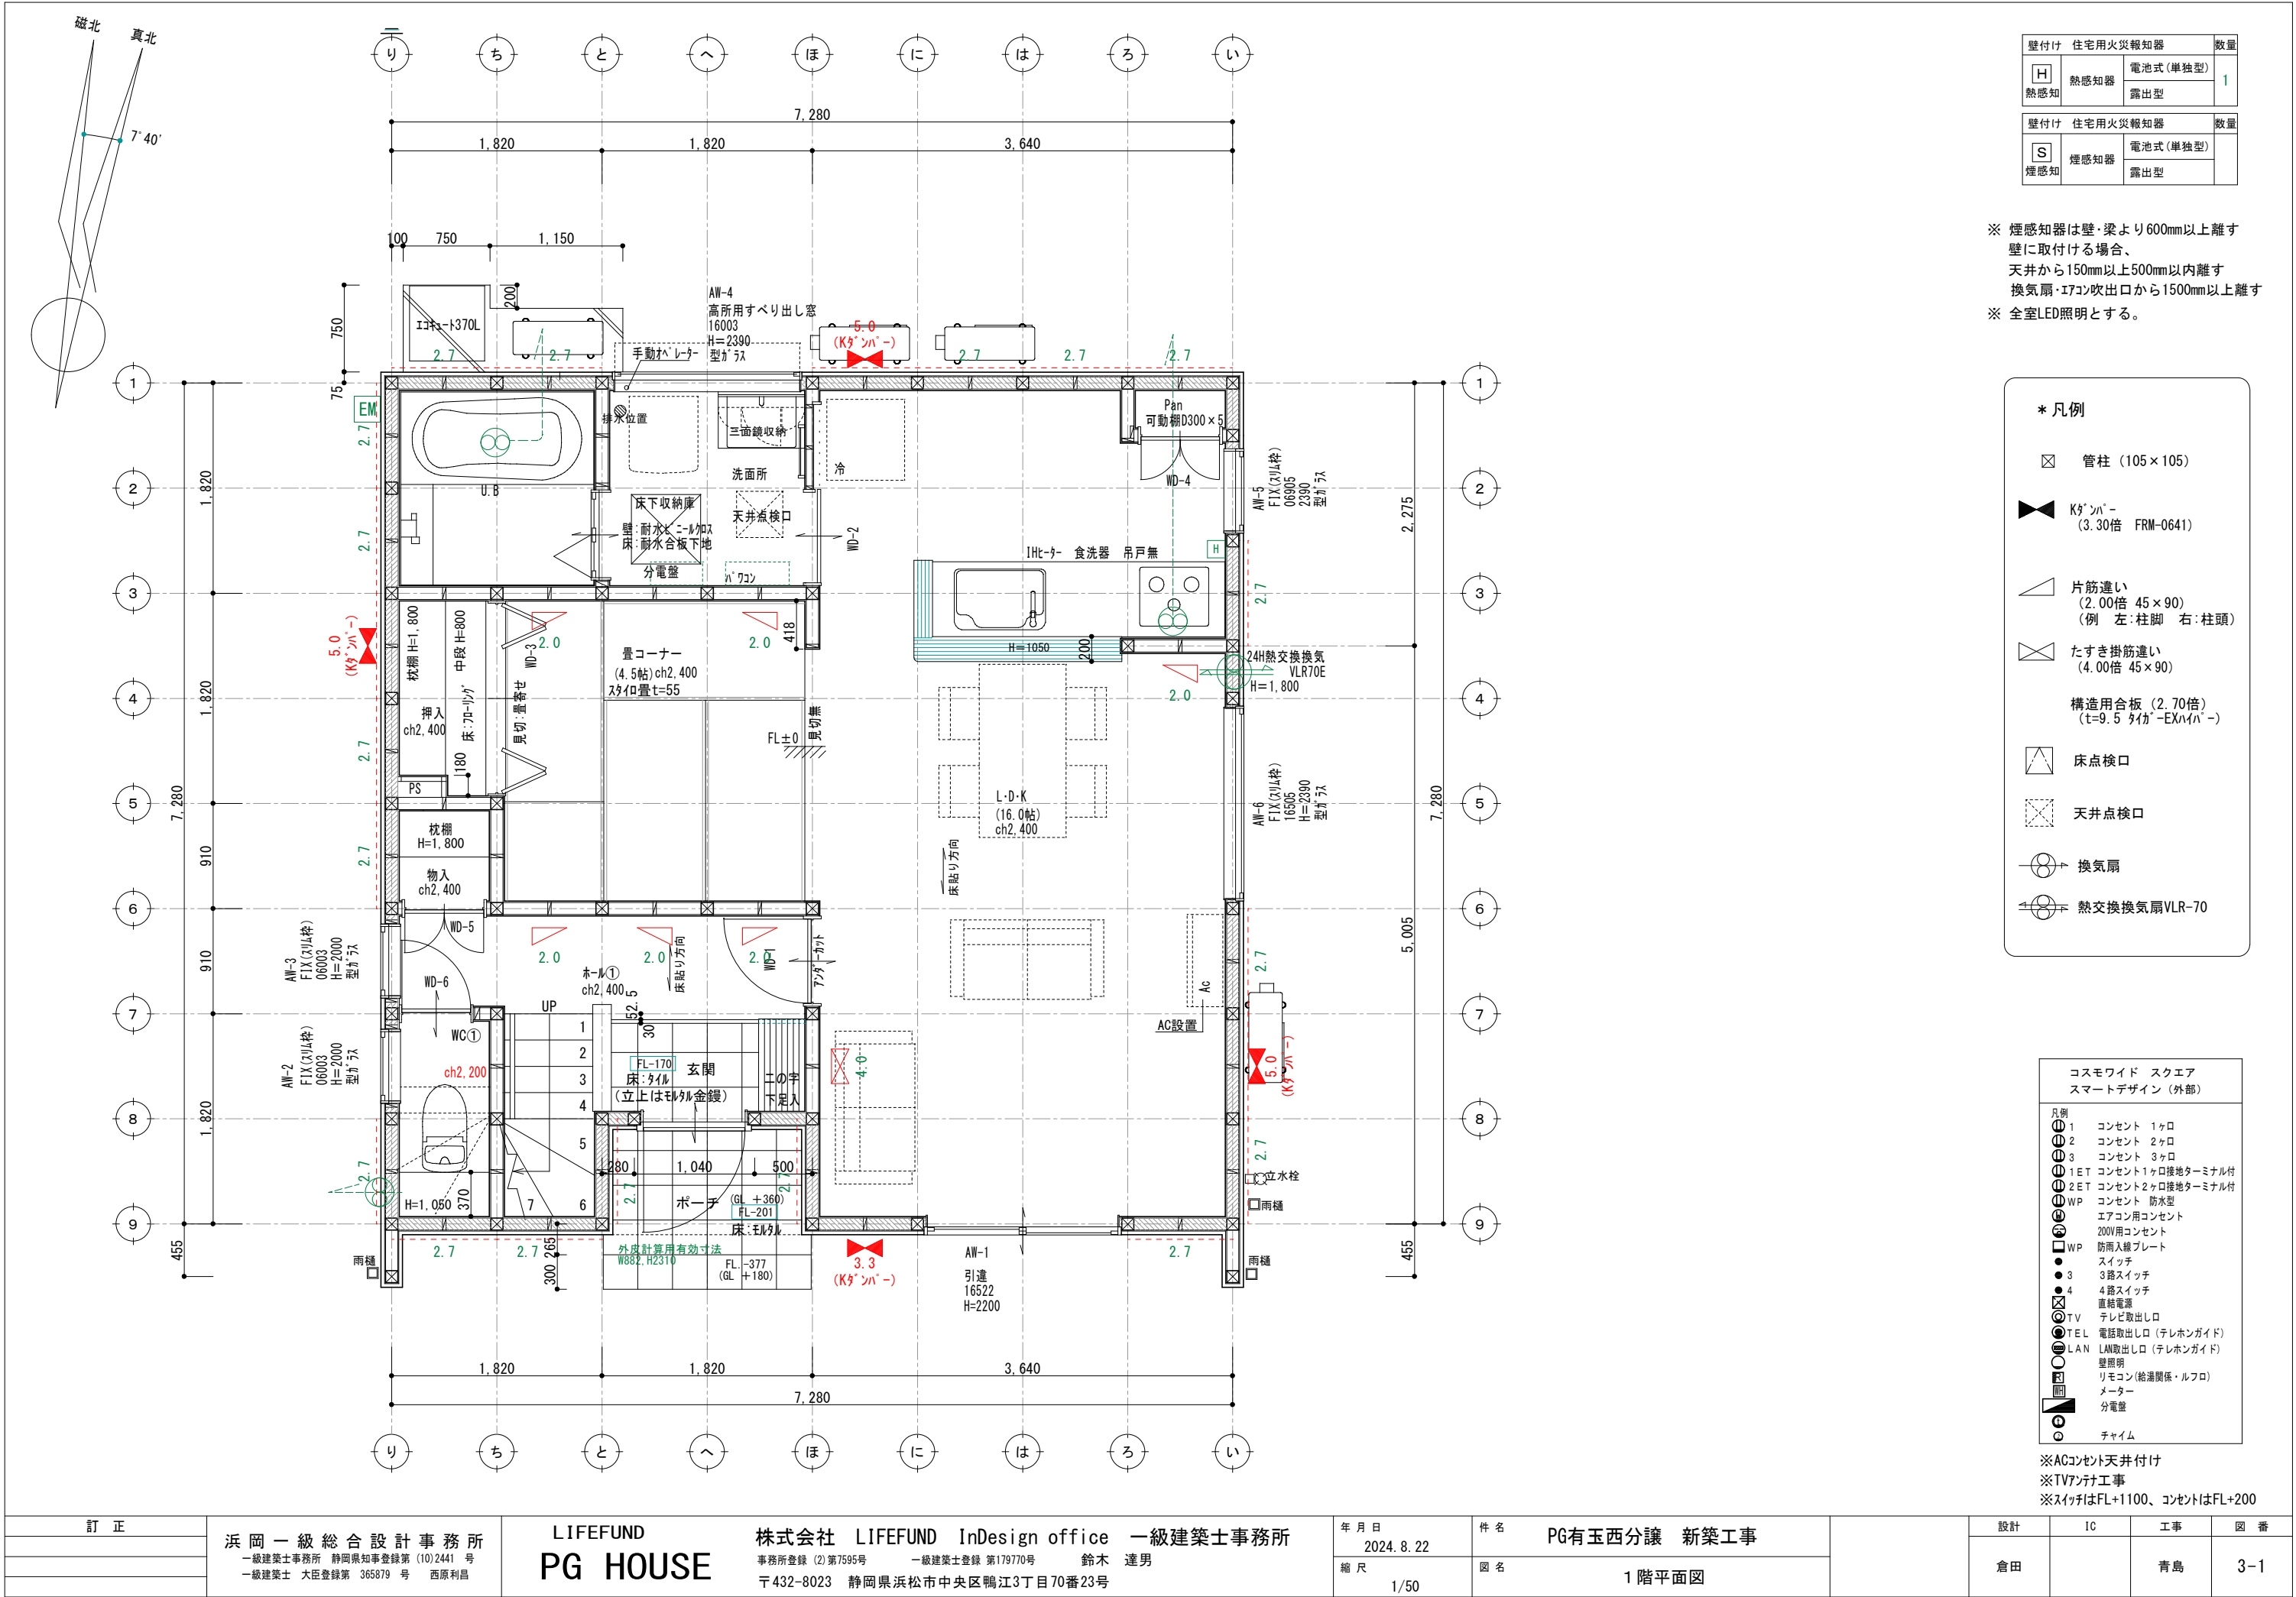



※ 煙感知器は壁・梁より600mm以上離す
壁に取付ける場合、
天井から150mm以上500mm以内離す
換気扇・エアコン吹出口から1500mm以上離す
※ 全室LED照明とする。

* 凡例


-  管柱 (105 × 105)
 K³・³ハ⁻
 (3. 30倍 FRM-0641)
 片筋違い
 (2. 00倍 45 × 90)
 (例 左: 柱脚 右: 柱頭)
 たすき掛筋違い
 (4. 00倍 45 × 90)
 構造用合板 (2. 70倍)
 (t=9. 5 タイガ⁻-EXハイハ⁻)
 床点検口
 天井点検口
 換気扇
 熱交換換気扇VLR-70

コスモワイド スクエア
スマートデザイン（外部）


- | | | |
|---|-------|------------------|
| 例 | | |
| ① | 1 | コンセント 1ヶ口 |
| ② | 2 | コンセント 2ヶ口 |
| ③ | 3 | コンセント 3ヶ口 |
| ④ | 1 E T | コンセント 1ヶ口接地ターミナル |
| ⑤ | 2 E T | コンセント 2ヶ口接地ターミナル |
| ⑥ | WP | コンセント 防水型 |
| ⑦ | | エアコン用コンセント |
| ⑧ | | 200V用コンセント |
| ⑨ | WP | 防雨入線プレート |
| ⑩ | | スイッチ |
| ⑪ | 3 | 3路スイッチ |
| ⑫ | 4 | 4路スイッチ |
| ⑬ | ⊗ | 直結電源 |
| ⑭ | TV | テレビ取出口 |
| ⑮ | TEL | 電話取出口 (テレホンガイド) |
| ⑯ | LAN | LAN取出口 (テレホンガイド) |
| ⑰ | | 鏡照明 |
| ⑱ | | 壁面照明 (給湯関係・ルーフ) |
| ⑲ | | メーター |
| ⑳ | | 分電盤 |
| ㉑ | | インターホン |
| ㉒ | | チャイム |

※ACコンセント天井付け
※TVアンテナ工事
※スイッチはFL+1100、コンセントはFL+200


訂 正	浜 岡 一 級 総 合 設 計 事 務 所 一級建築士事務所 静岡県知事登録第 (10)2441 号 一級建築士 大臣登録第 365879 号 西原利昌	LIFEFUND PG HOUSE	株式会社 LIFEFUND InDesign office 一級建築士事務所 事務所登録 (2) 第7595号 一級建築士登録 第179770号 鈴木 達男 〒432-8023 静岡県浜松市中央区鴨江3丁目70番23号	年 月 日 2024. 8. 22	件 名 PG有玉西分譲 新築工事		設計	IC	工事	図 番
				縮 尺 1/100	図 名 2 階平面図		倉田		青島	3-2

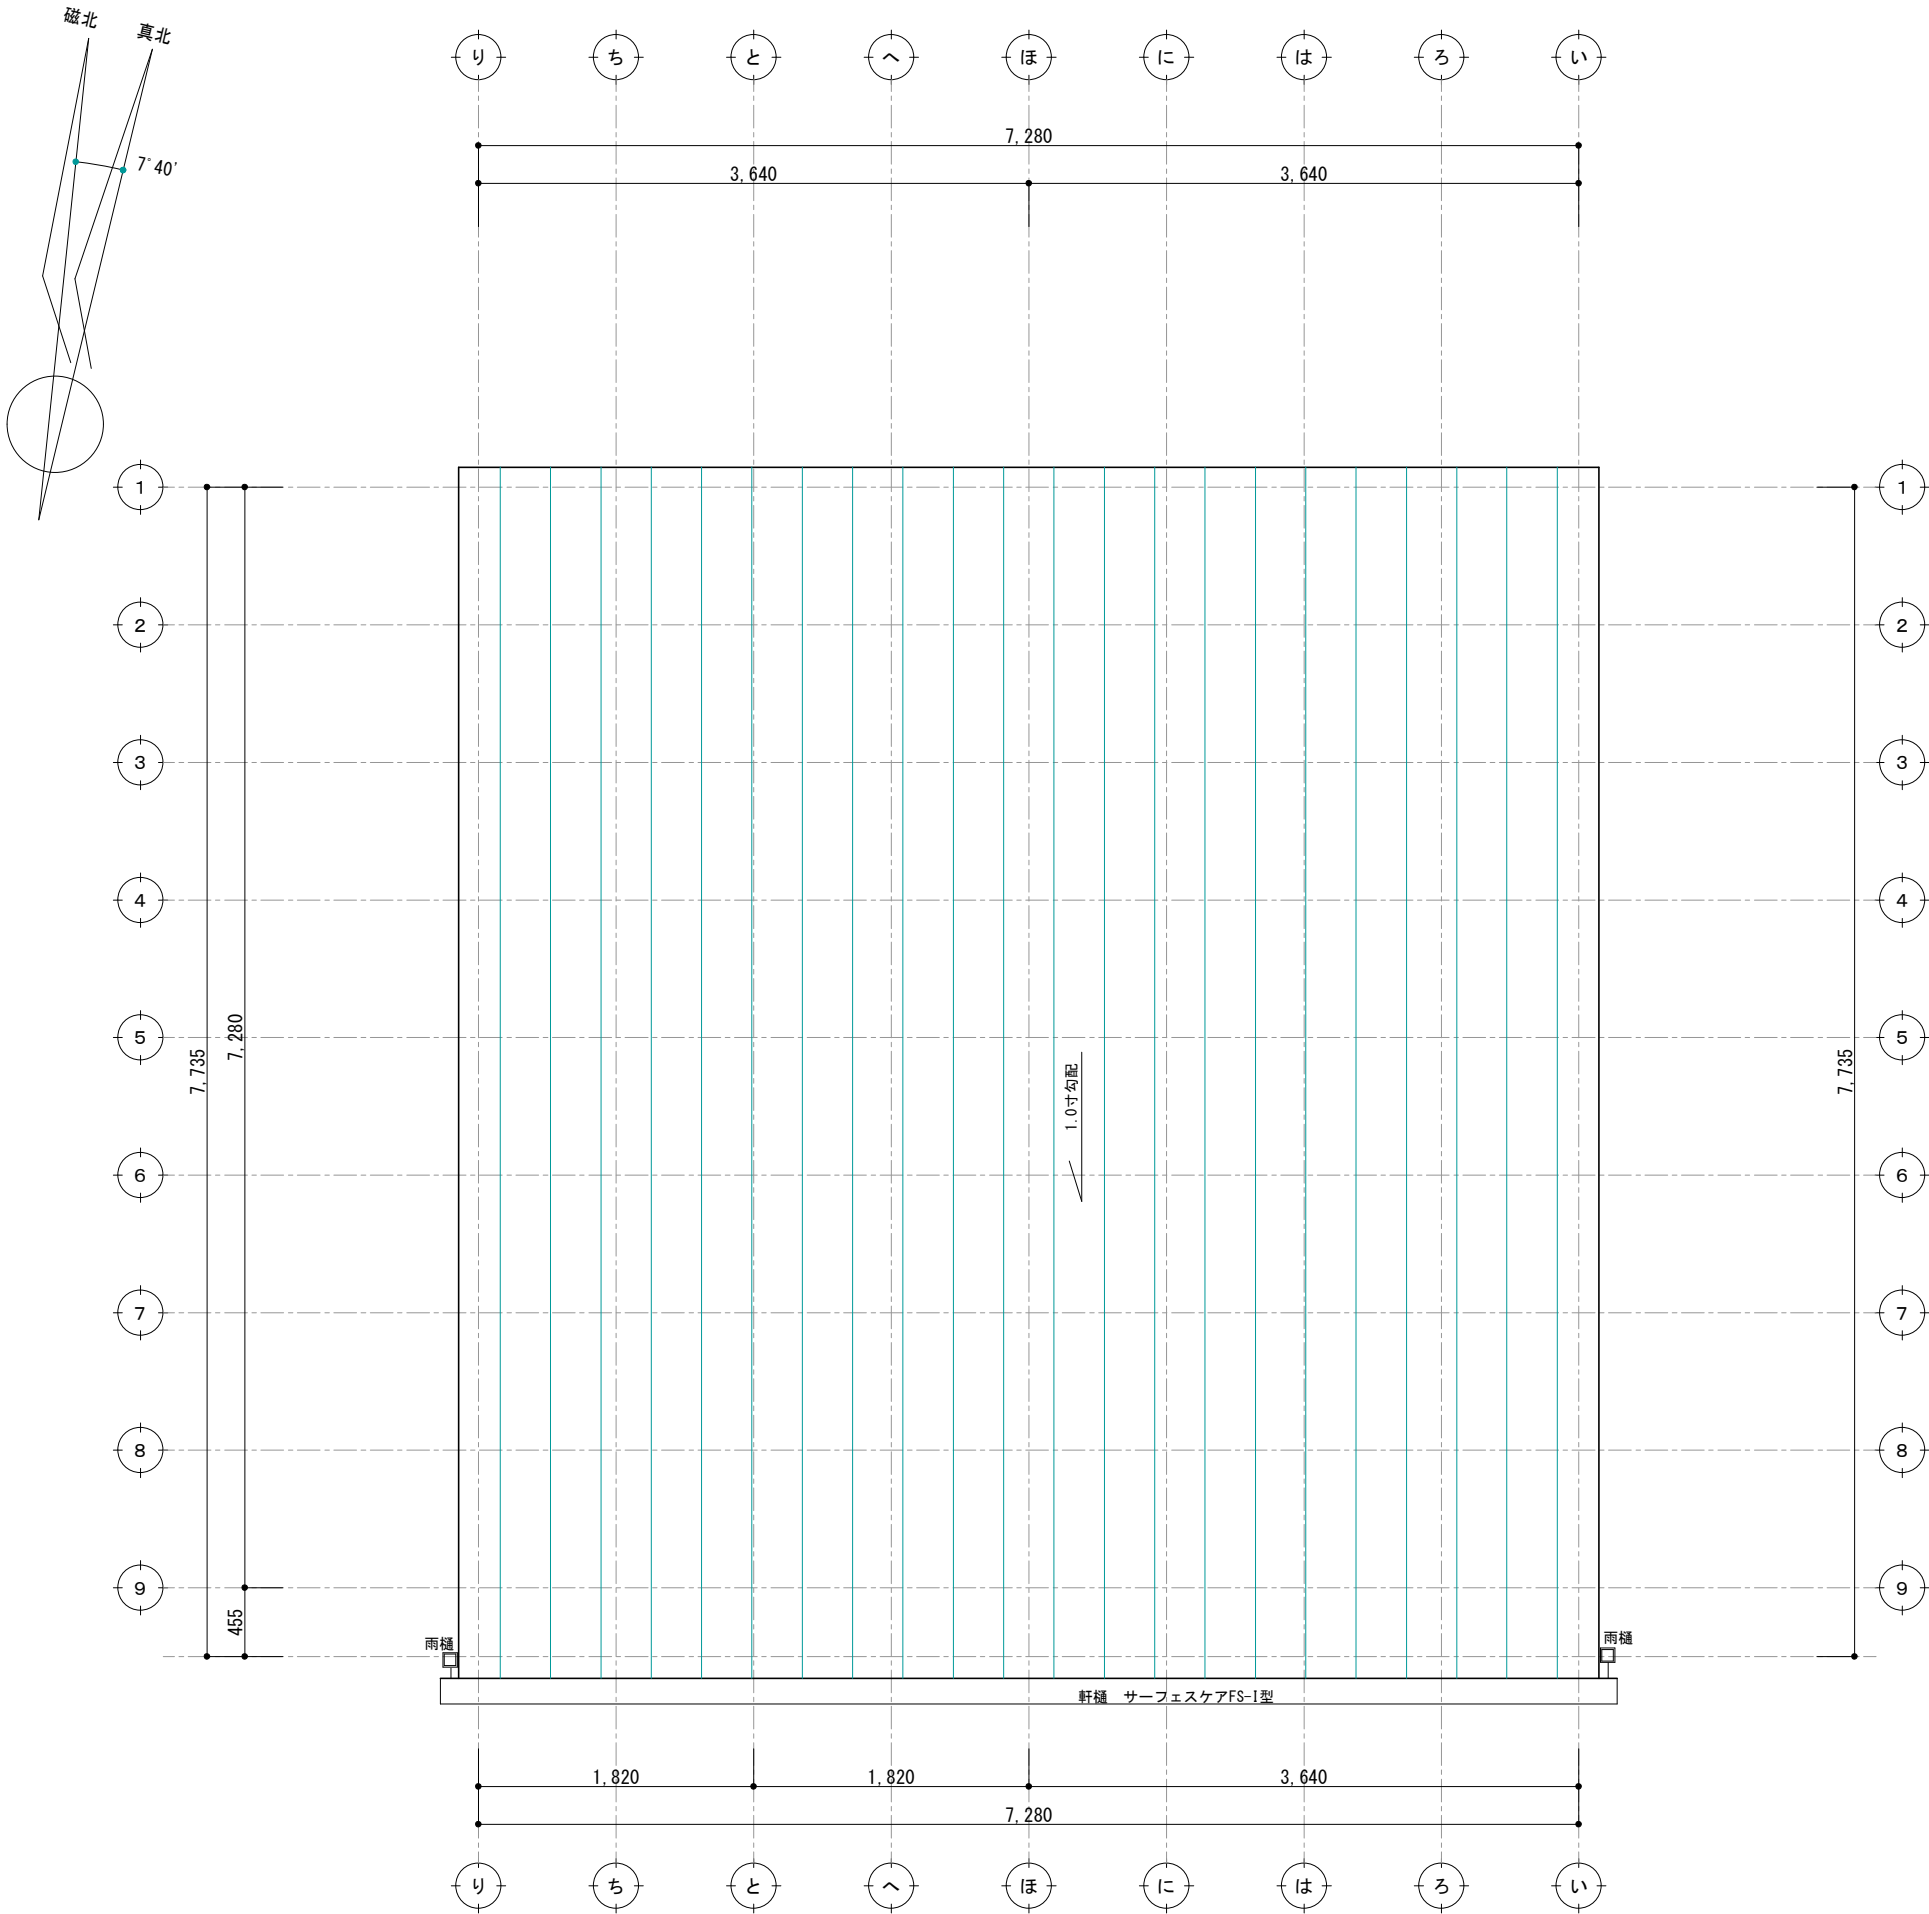


訂正	浜岡一級総合設計事務所 一級建築士事務所 静岡県知事登録第 (10)2441 号 一級建築士 大臣登録第 365879 号 西原利昌	LIFEFUND PG HOUSE	株式会社 LIFEFUND InDesign office 一級建築士事務所 事務所登録 (2) 第7595号 一級建築士登録 第179770号 鈴木 達男 〒432-8023 静岡県浜松市中央区鴨江3丁目70番23号	年月日 2024. 8. 22	件名 PG有玉西分譲 新築工事		設計	IC	工事	図番
				縮尺 1/100	図名 屋根伏図		倉田		青島	3-3

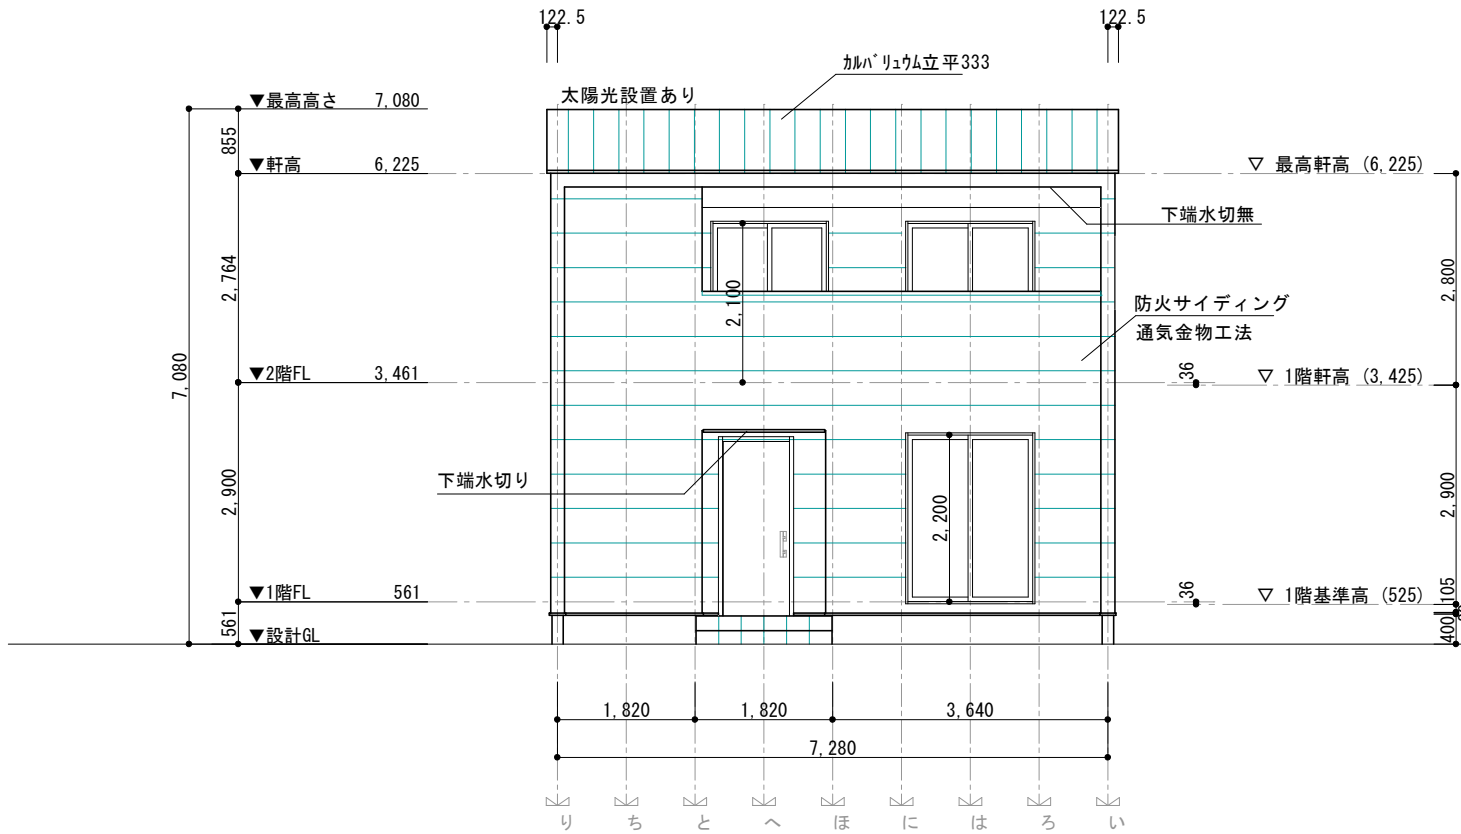


南側立面図 S=1/100

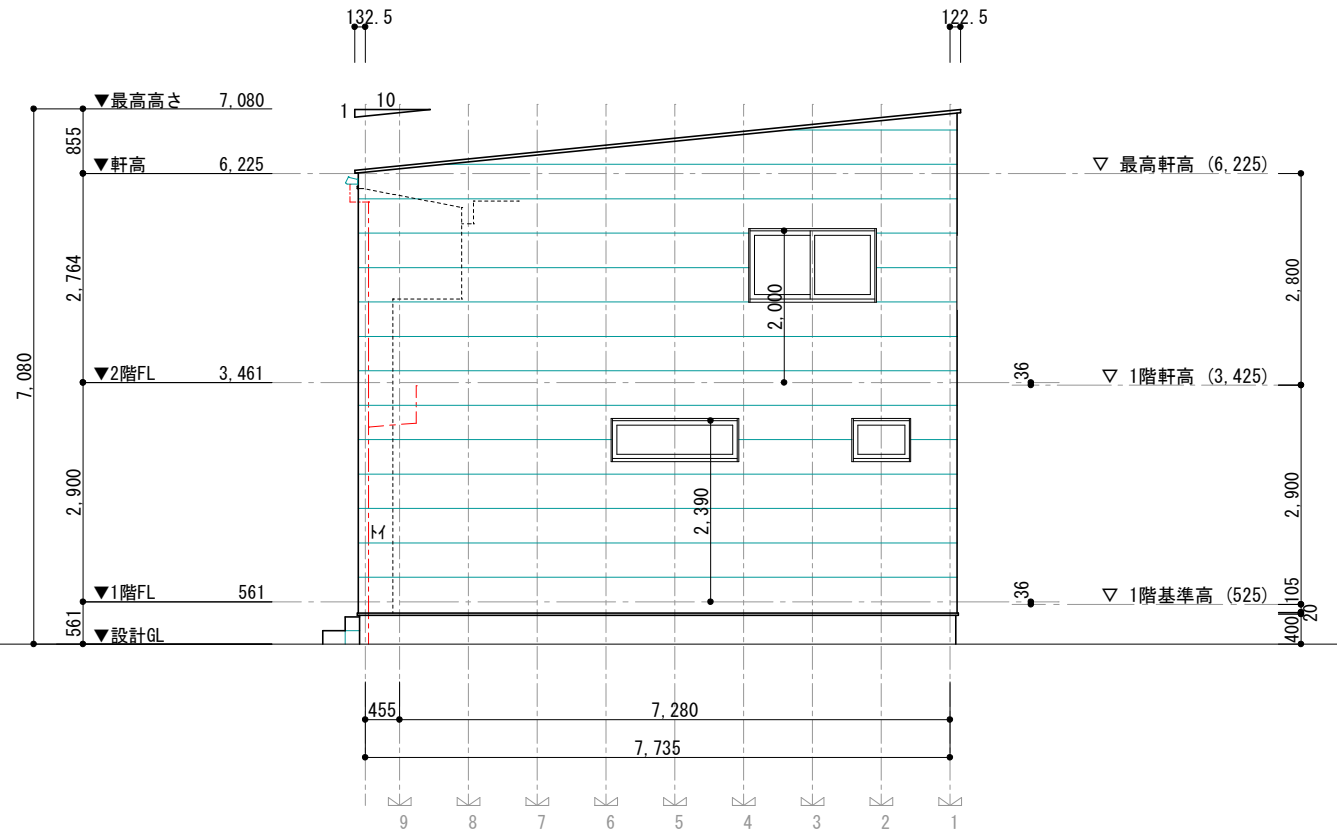

東側立面図 S=1/100

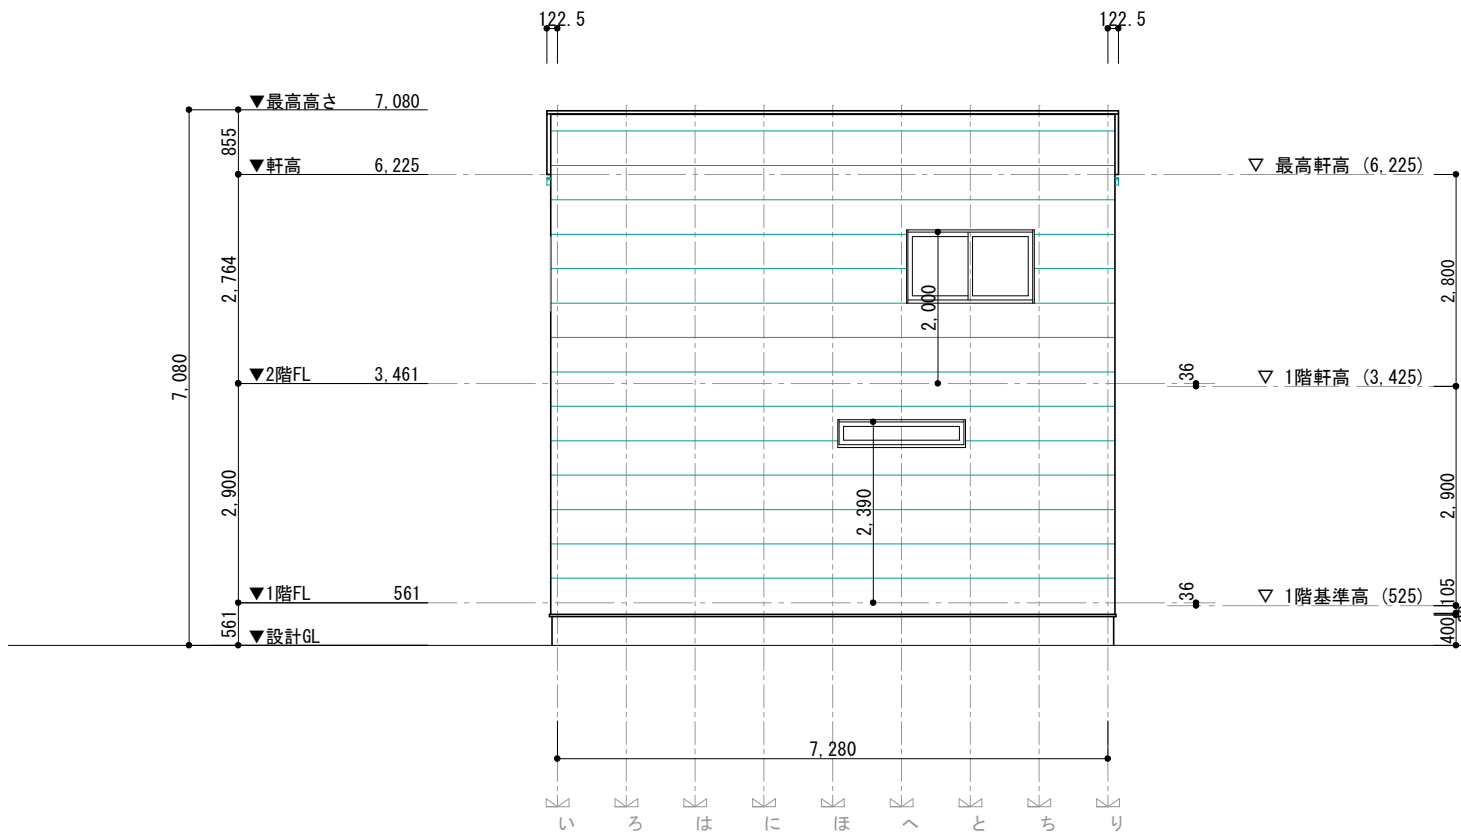


北側立面図 S=1/100












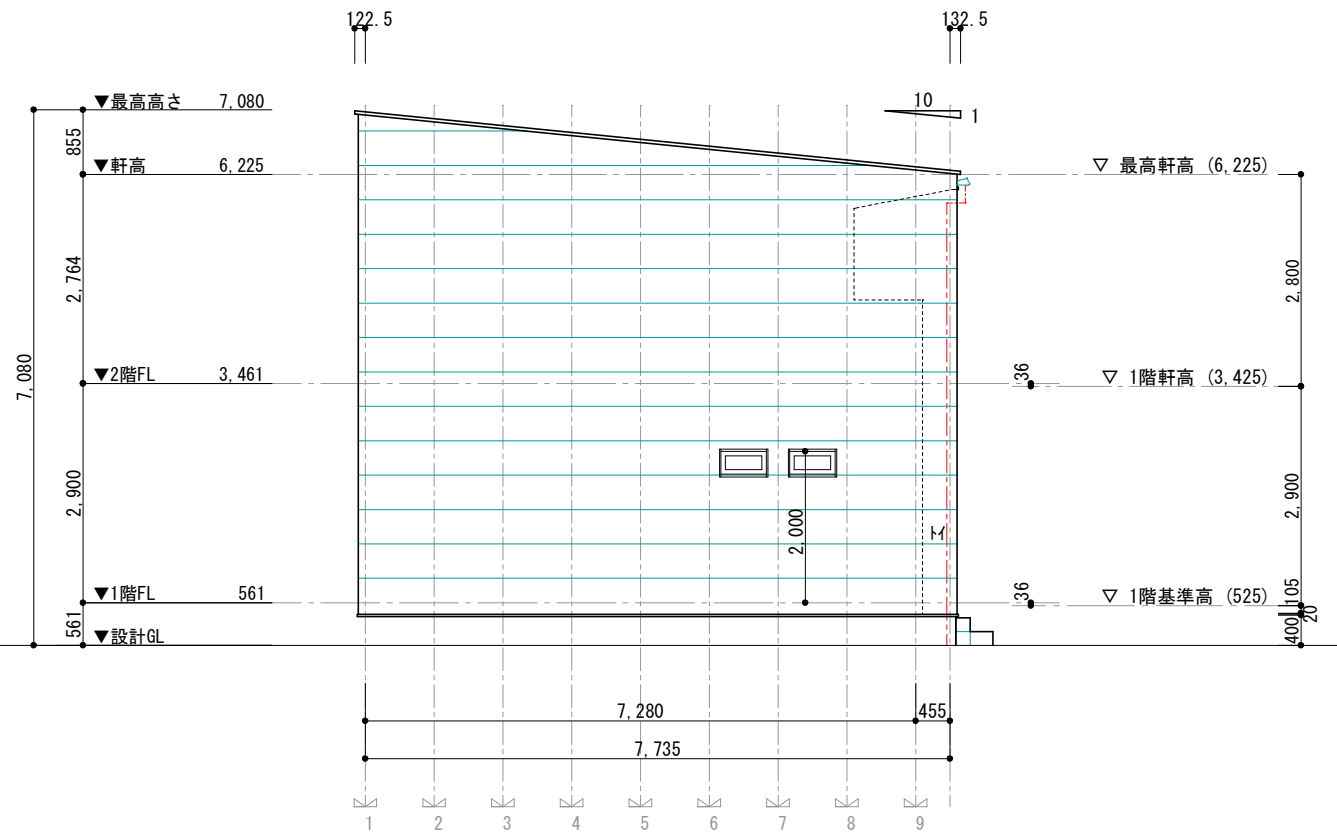


西側立面図 S=1/100


訂正	浜岡一級総合設計事務所	LIFEFUND PG HOUSE	株式会社 LIFEFUND InDesign office 一級建築士事務所 事務所登録 (2) 第7595号 一級建築士登録 第179770号 鈴木 達男 〒432-8023 静岡県浜松市中央区鴨江3丁目70番23号	年月日 2024. 8. 22	件名 PG有玉西分譲 新築工事		設計	IC	工事	図番
	一級建築士事務所 静岡県知事登録第 (10)2441 号			縮尺 1/100	図名 立面図		倉田		青島	4
	一級建築士 大臣登録第 365879 号 西原利昌									

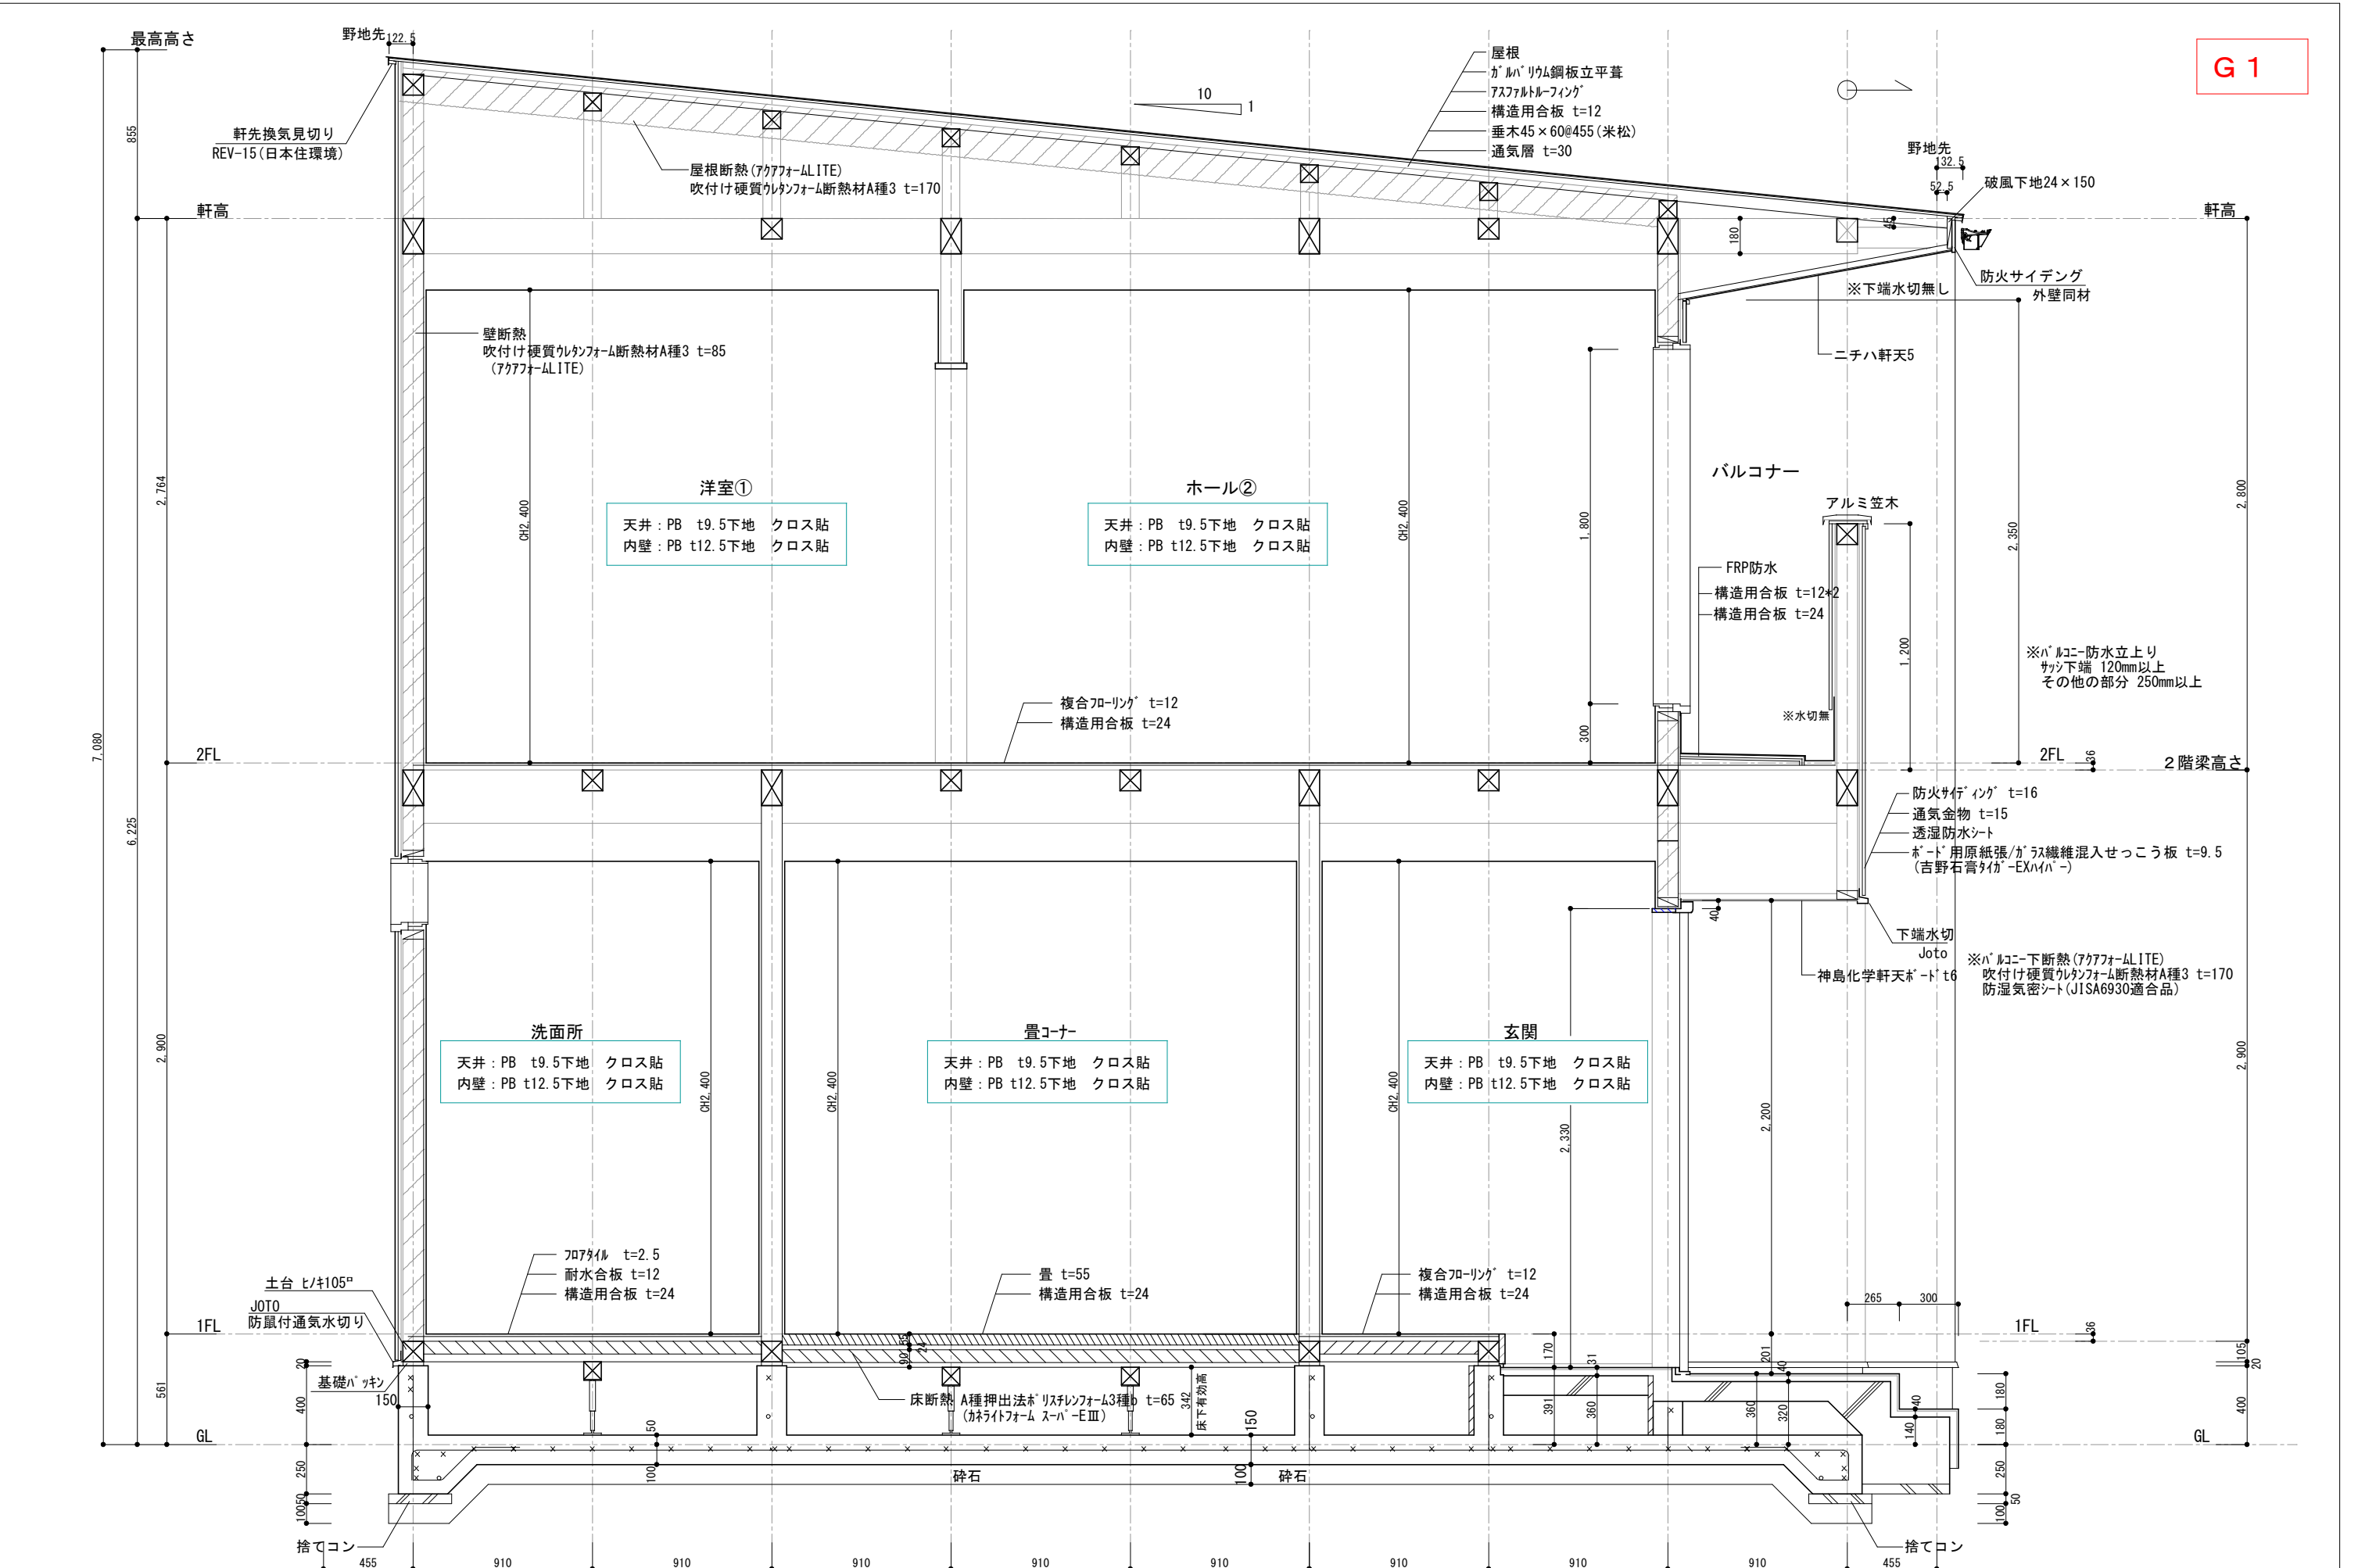


訂正	浜岡一級総合設計事務所 一級建築士事務所 静岡県知事登録第 (10)2441 号 一級建築士 大臣登録第 365879 号 西原利昌	LIFEFUND PG HOUSE	株式会社 LIFEFUND InDesign office 一級建築士事務所 事務所登録 (2)第7595号 一級建築士登録 第179770号 鈴木 達男 〒432-8023 静岡県浜松市中央区鴨江3丁目70番23号	年月日 2024. 8. 22	件名 PG有玉西 分譲 新築工事	設計 倉田	IC	工事 青島	図番 5-1
				縮尺 1/30	図名 矩計図				

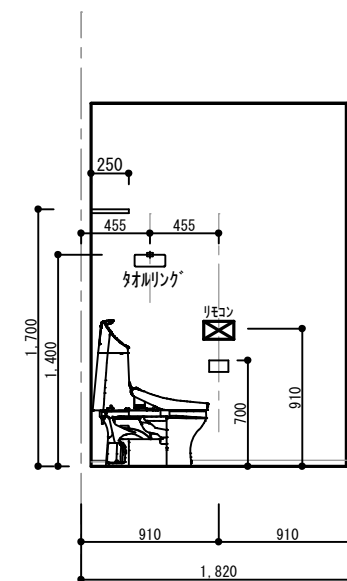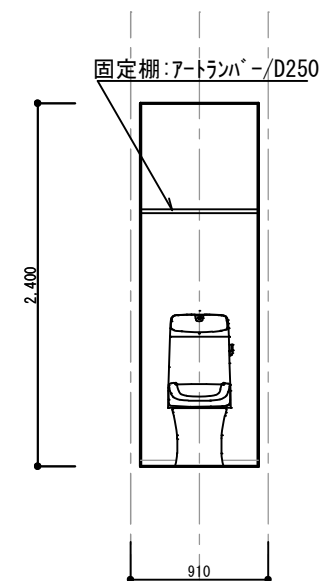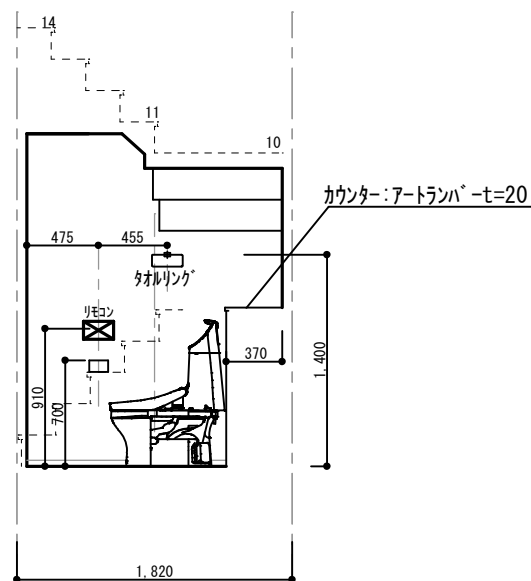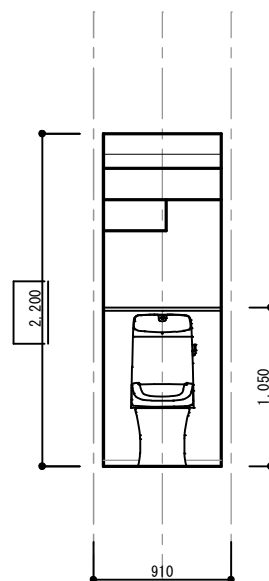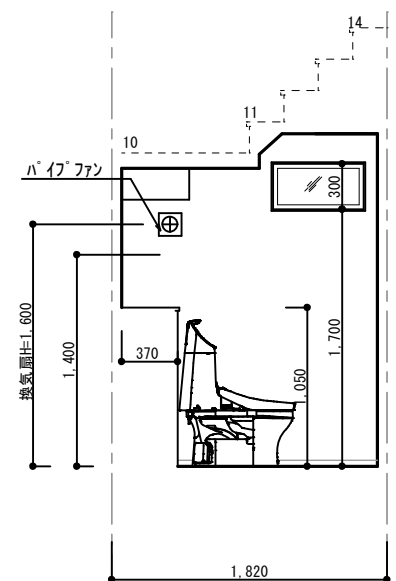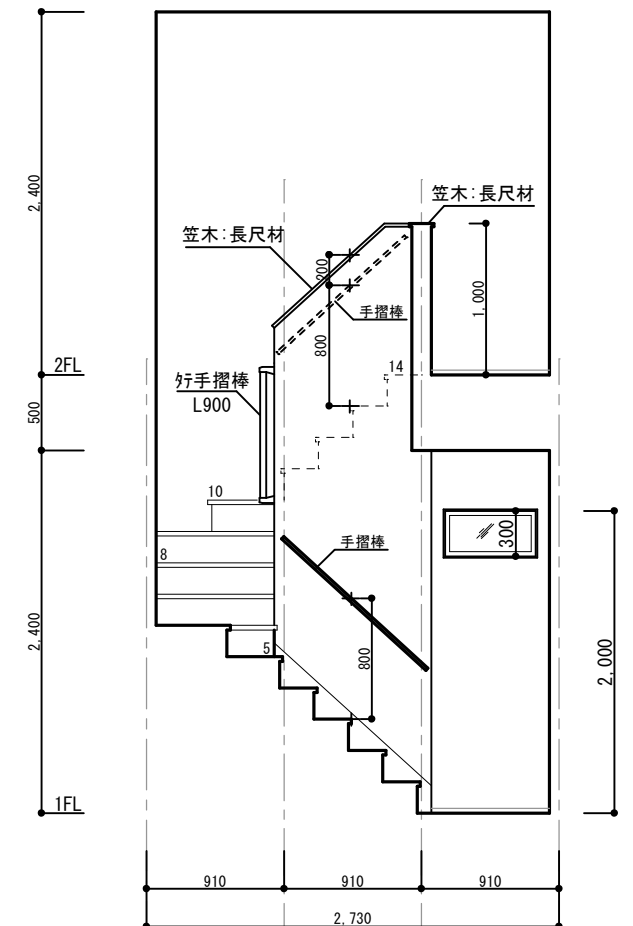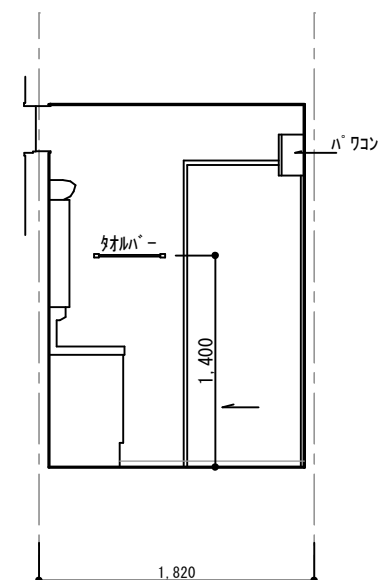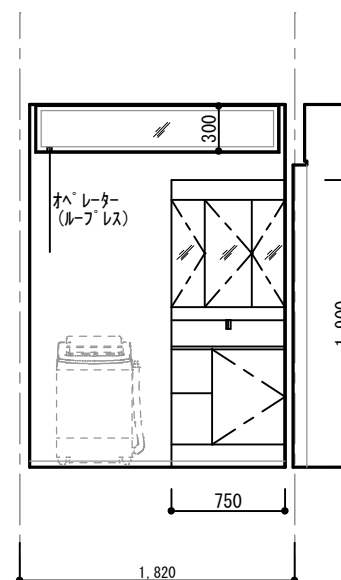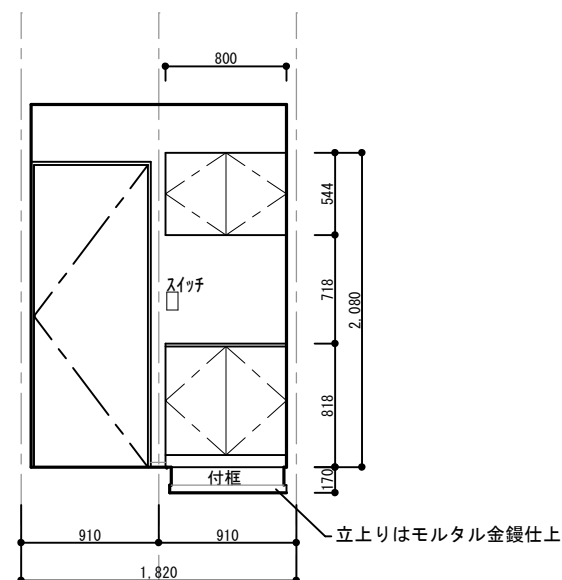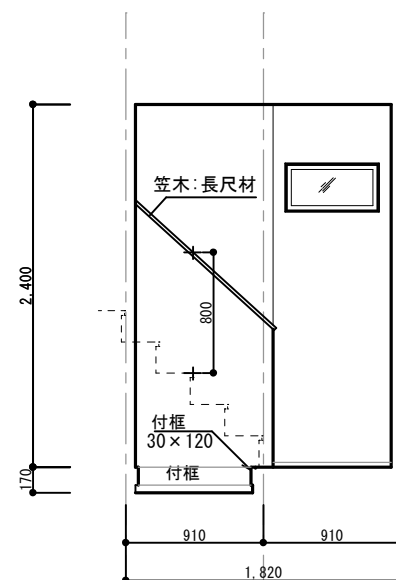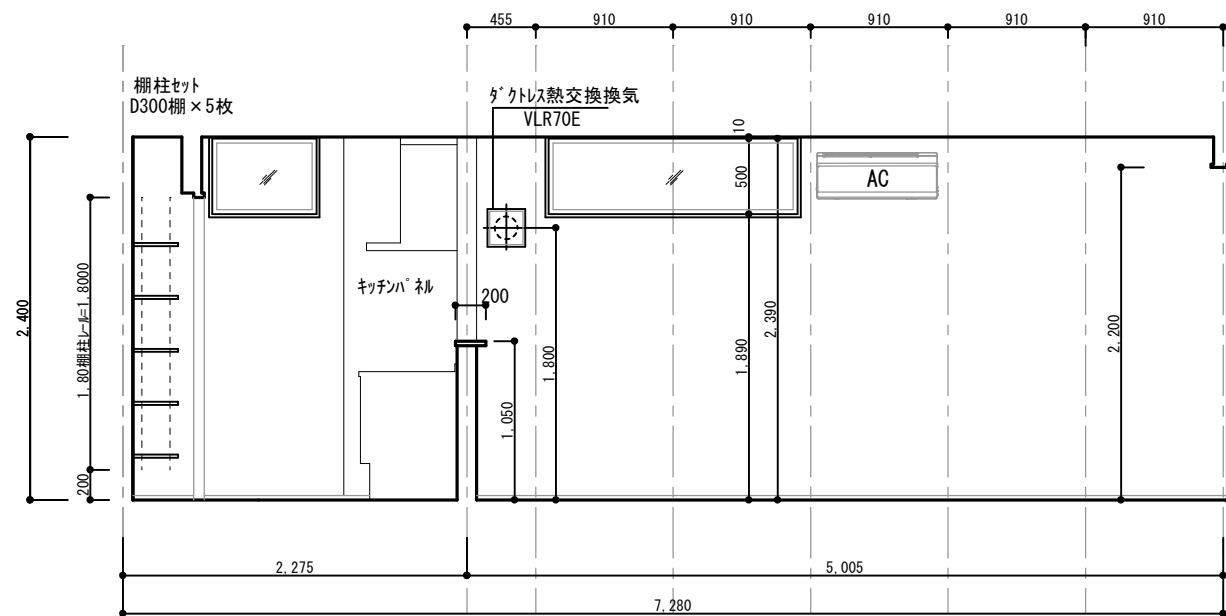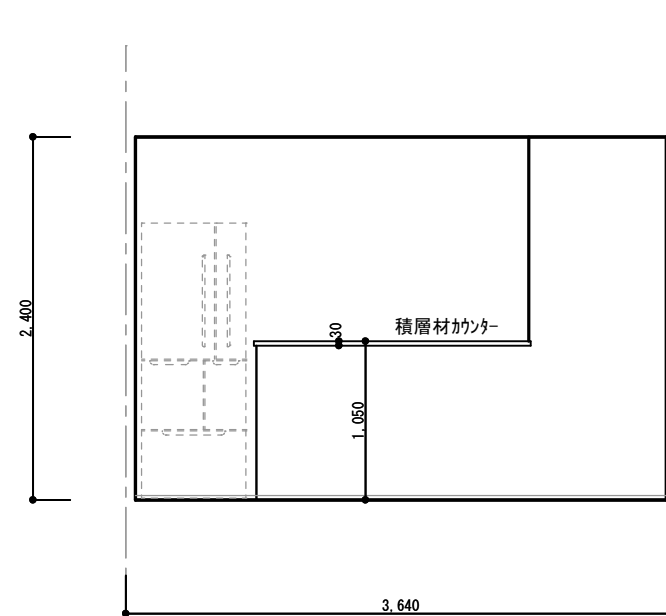

訂 正	浜 岡 一 級 総 合 設 計 事 務 所 一級建築士事務所 静岡県知事登録第 (10)2441 号 一級建築士 大臣登録第 365879 号 西原利昌	LIFEFUND PG HOUSE	株式会社 LIFEFUND InDesign office 一級建築士事務所 事務所登録 (2)第795号 一級建築士登録 第179770号 鈴木 達男 〒432-8023 静岡県浜松市中央区鴨江3丁目70番23号	年 月 日	件 名		設計	IC	工事	図 番
				2024. 8. 22	PG有玉西分譲 新築工事					
				縮 尺	図 名					
		1/30	展開図	倉田	青島	6-1				

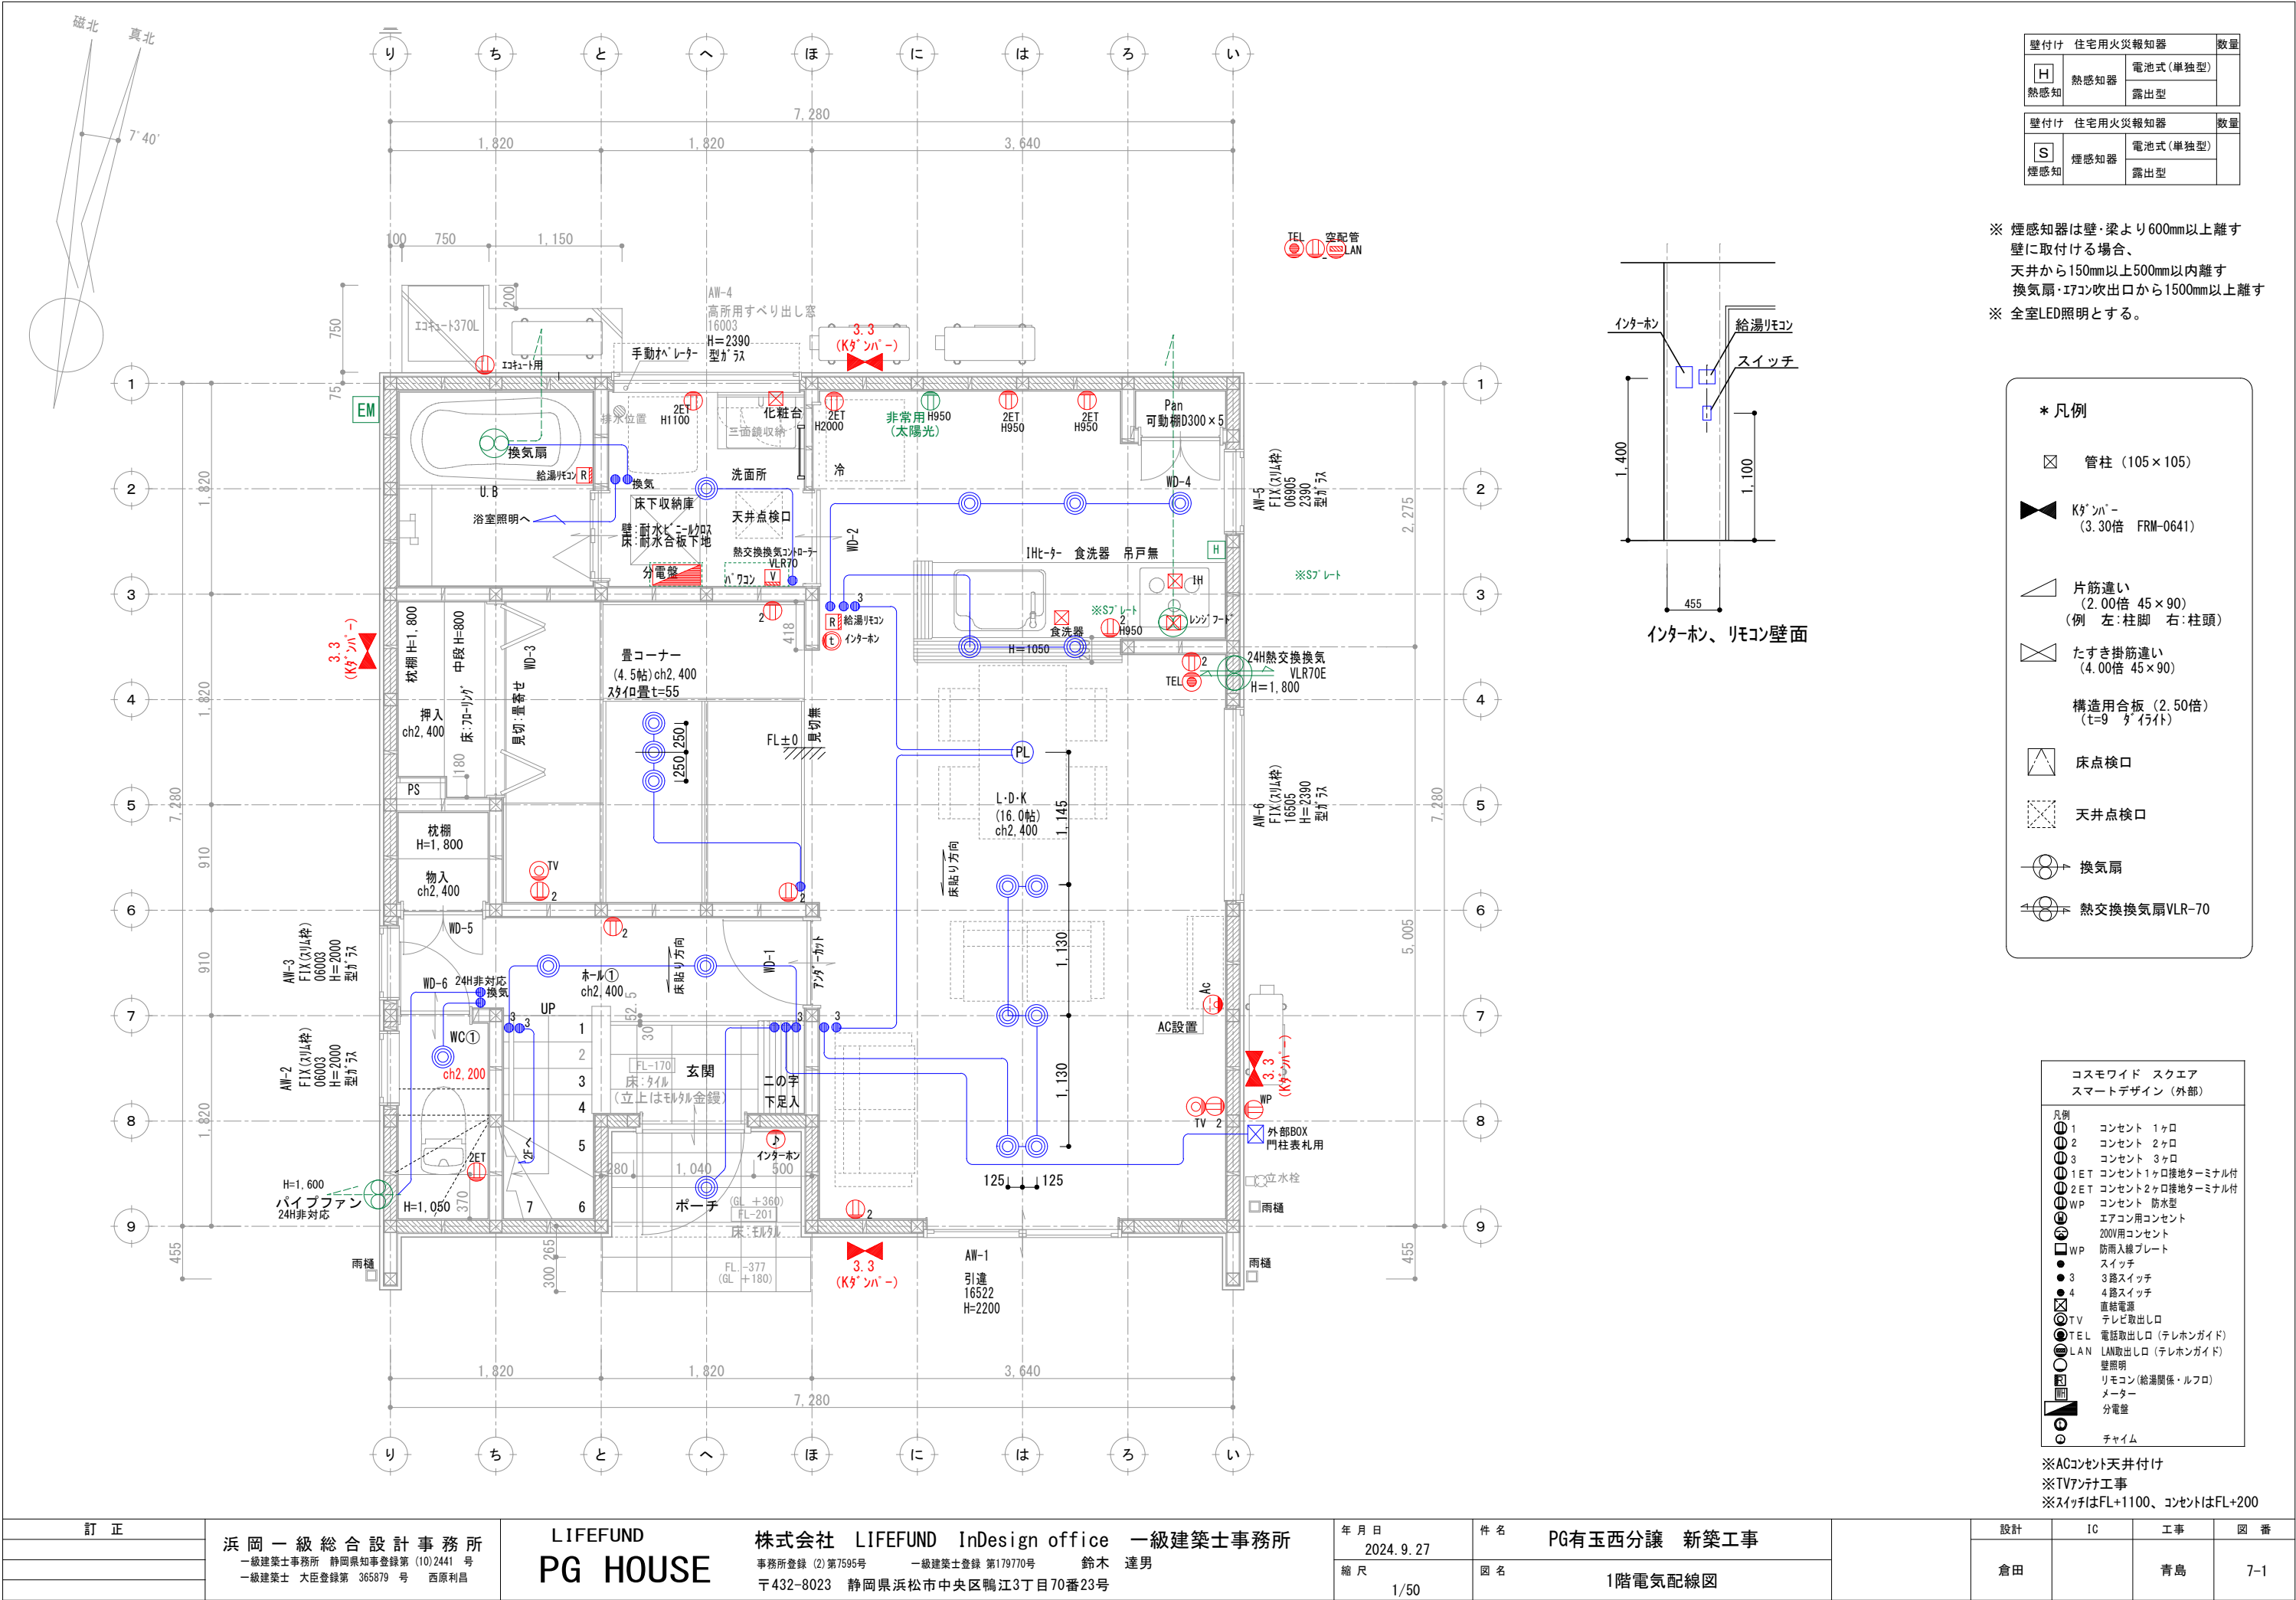

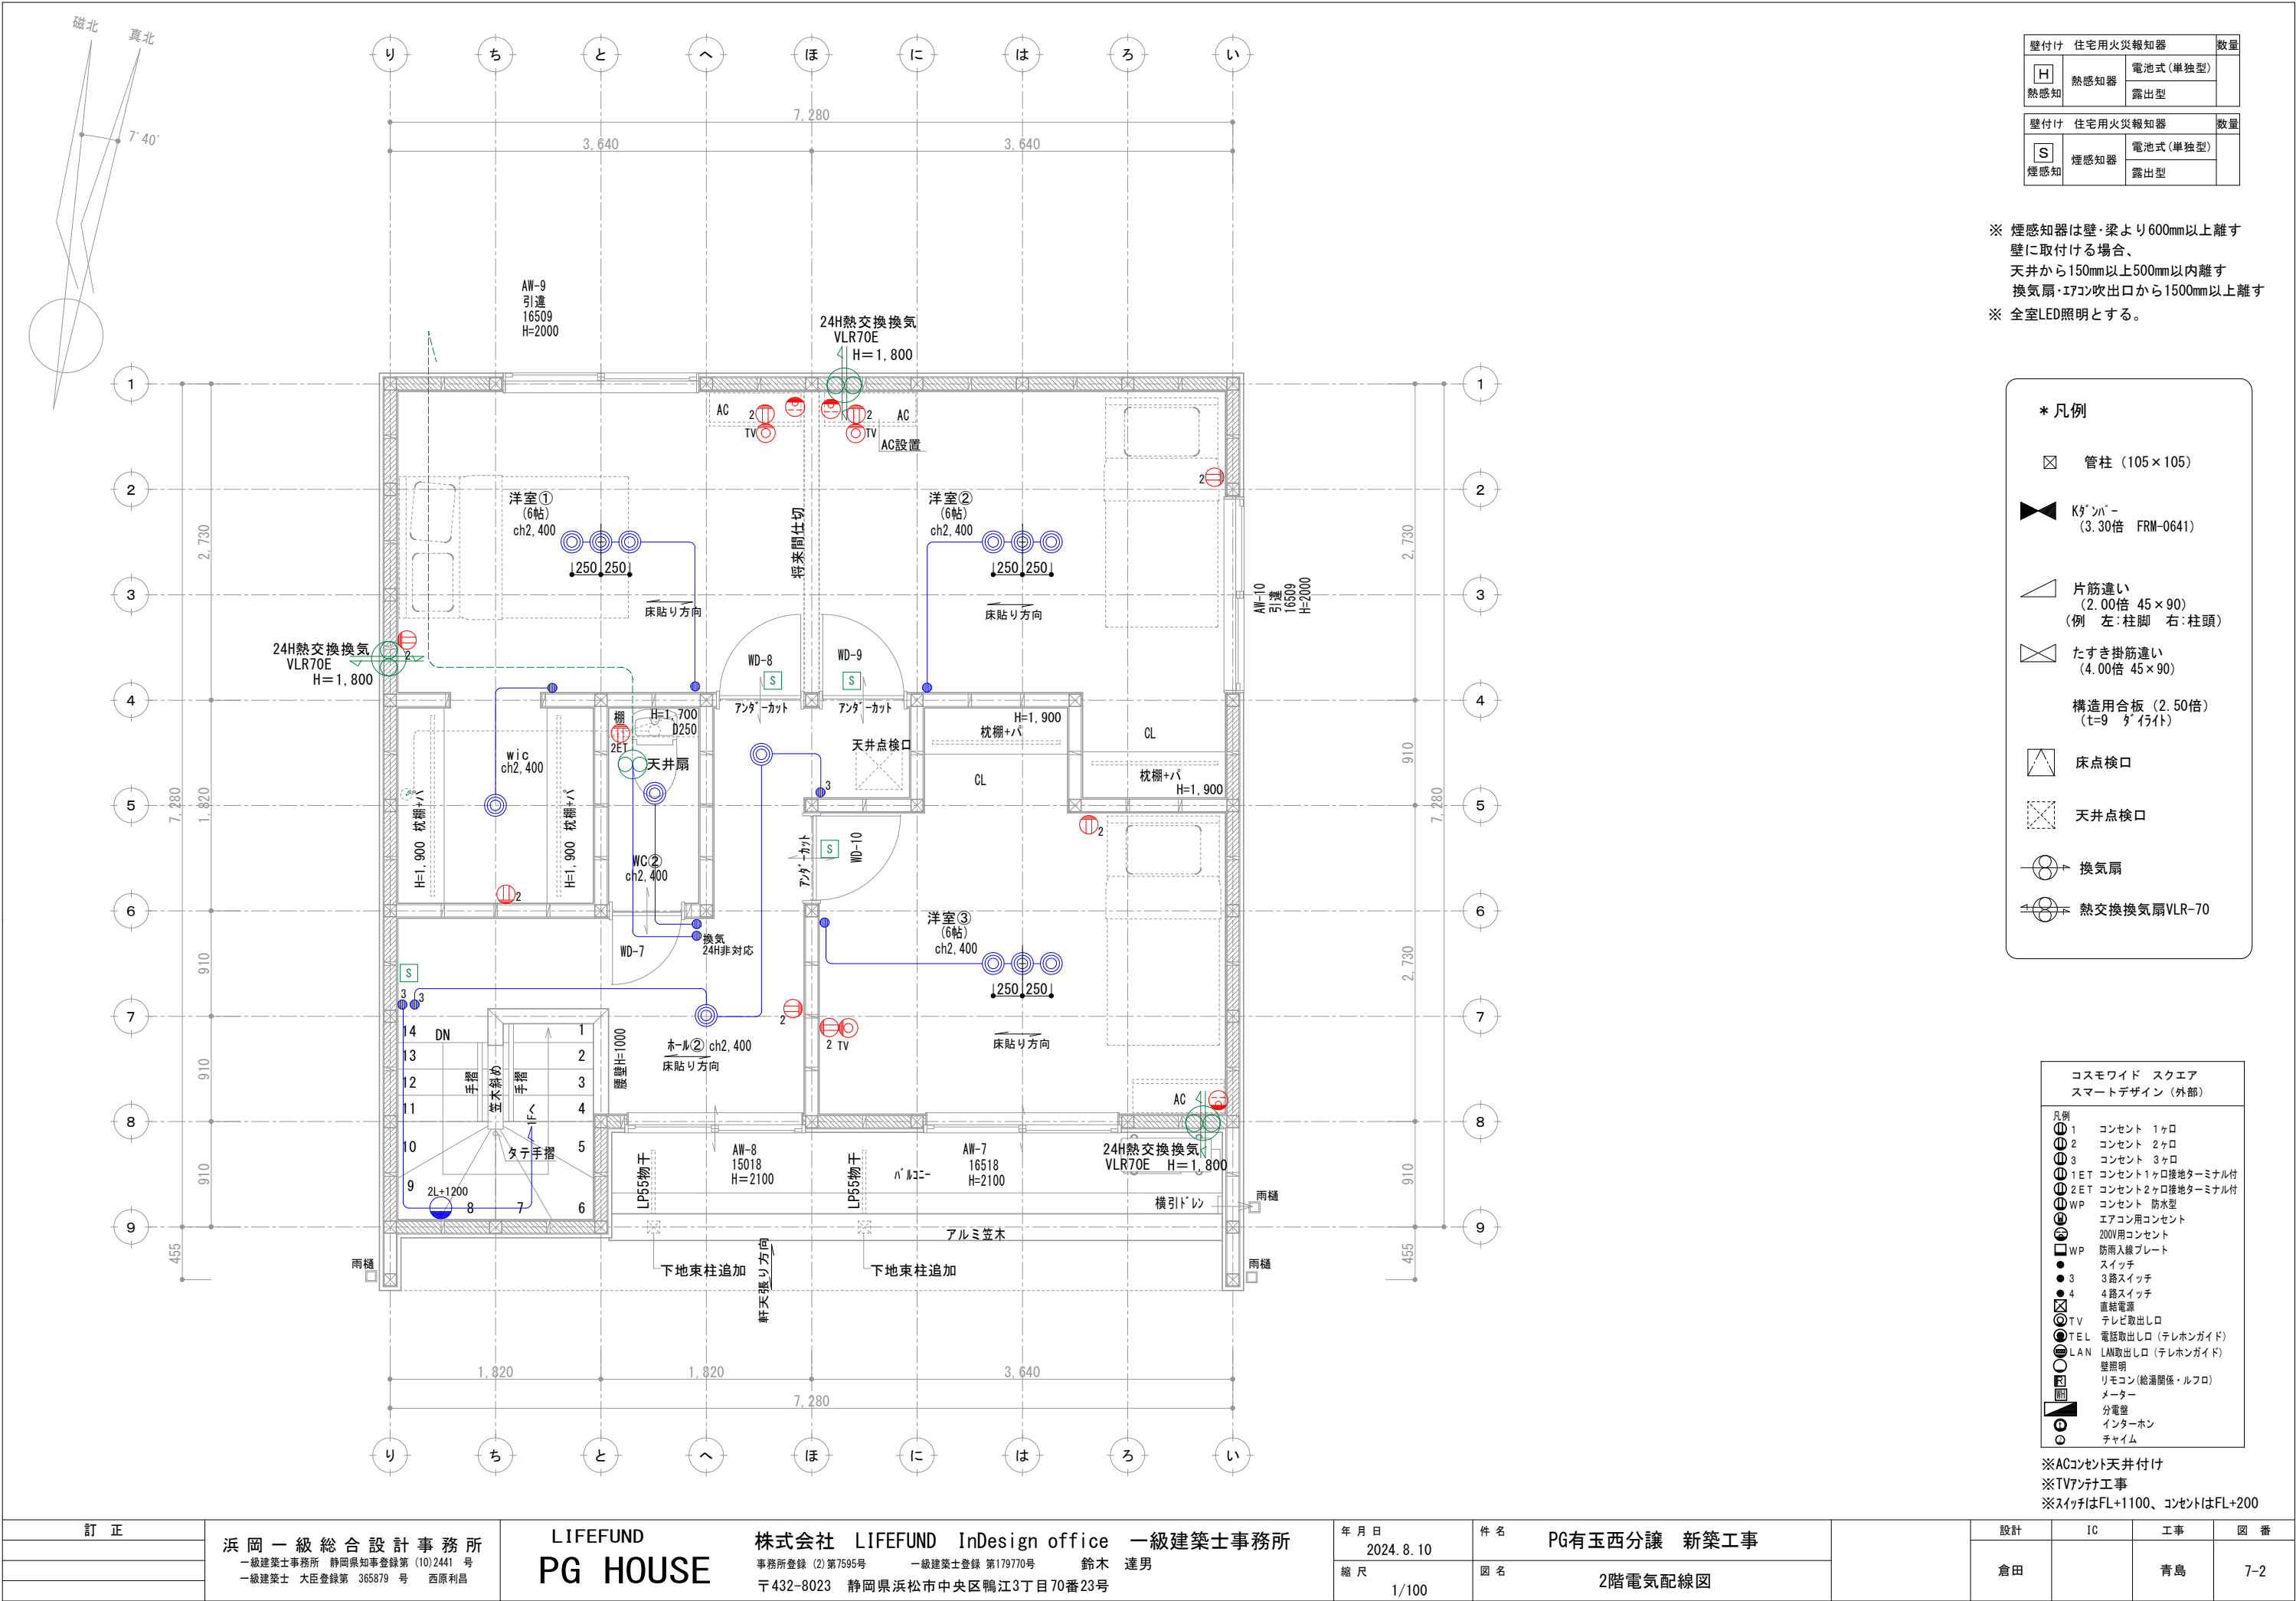

壁付け 住宅用火災報知器			数量
H 熱感知	電池式 (単独型)		
	露出型		

壁付け 住宅用火災報知器			数量
S 煙感知	電池式 (単独型)		
	露出型		


※ 煙感知器は壁・梁より600mm以上離す壁に取付ける場合、天井から150mm以上500mm以内離す換気扇・エアコン吹出口から1500mm以上離す
※ 全室LED照明とする。

*** 凡例**


- 管柱 (105×105)
- Kダクト (3.30倍 FRM-0641)
- 片筋違い (2.00倍 45×90) (例 左:柱脚 右:柱頭)
- たすき掛筋違い (4.00倍 45×90)
- 構造用合板 (2.50倍) (t=9 タイト)
- 床点検口
- 天井点検口
- 換気扇
- 熱交換換気扇VLR-70

コスモワイド スクエア スマートデザイン (外部)		
凡例	1	コンセント 1ヶロ
	2	コンセント 2ヶロ
	3	コンセント 3ヶロ
	1ET	コンセント1ヶロ接地ターミナル付
	2ET	コンセント2ヶロ接地ターミナル付
	WP	コンセント 防水型
		エアコン用コンセント
		200V用コンセント
	WP	防雨入線プレート
		スイッチ
	3	3路スイッチ
	4	4路スイッチ
		直結電源
	TV	テレビ取出口
	TEL	電話取出口 (テレホンガイド)
	LAN	LAN取出口 (テレホンガイド)
		壁照明
		リモコン (給湯関係・ルフロ)
		メーター
		分電盤
		インターホン
		チャイム

※ACコンセント天井付け
※TVアンテナ工事
※スイッチはFL+1100、コンセントはFL+200

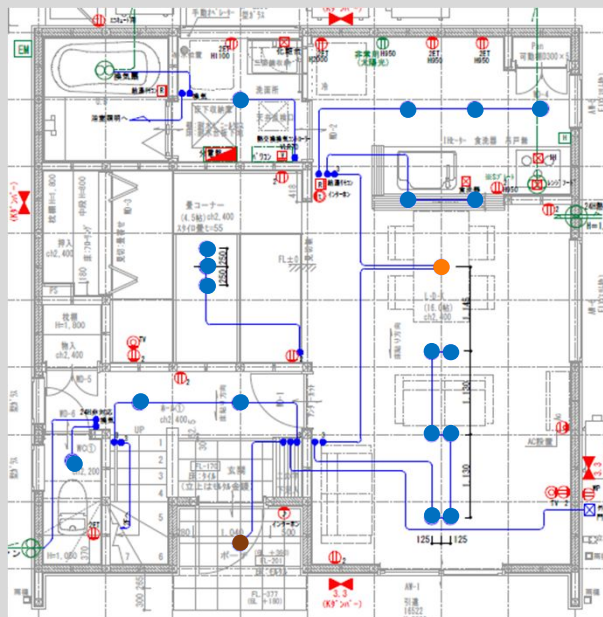


1階

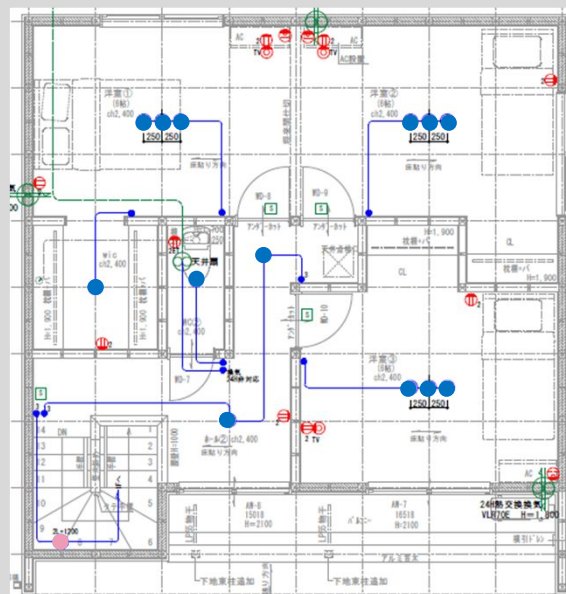

2階

内部：コスモワイド スクエア(Panasonic)

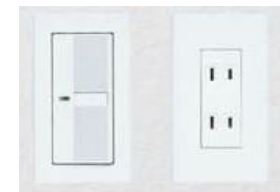

ドアホン：VL-SZ30KL
(Panasonic)



外部：スマートデザインシリーズ (Panasonic)

表情豊かな住まいをつくり出すスマートデザインシリーズ。



ポーチ灯

● × 1

DDL-4496YW



基本照明ダウナイト

● × 31

DDL6102AW



ダイニングペンダント灯

● × 1

DPN-39817 GE




階段灯












● × 1


DBK41544Y




2024.9.30.

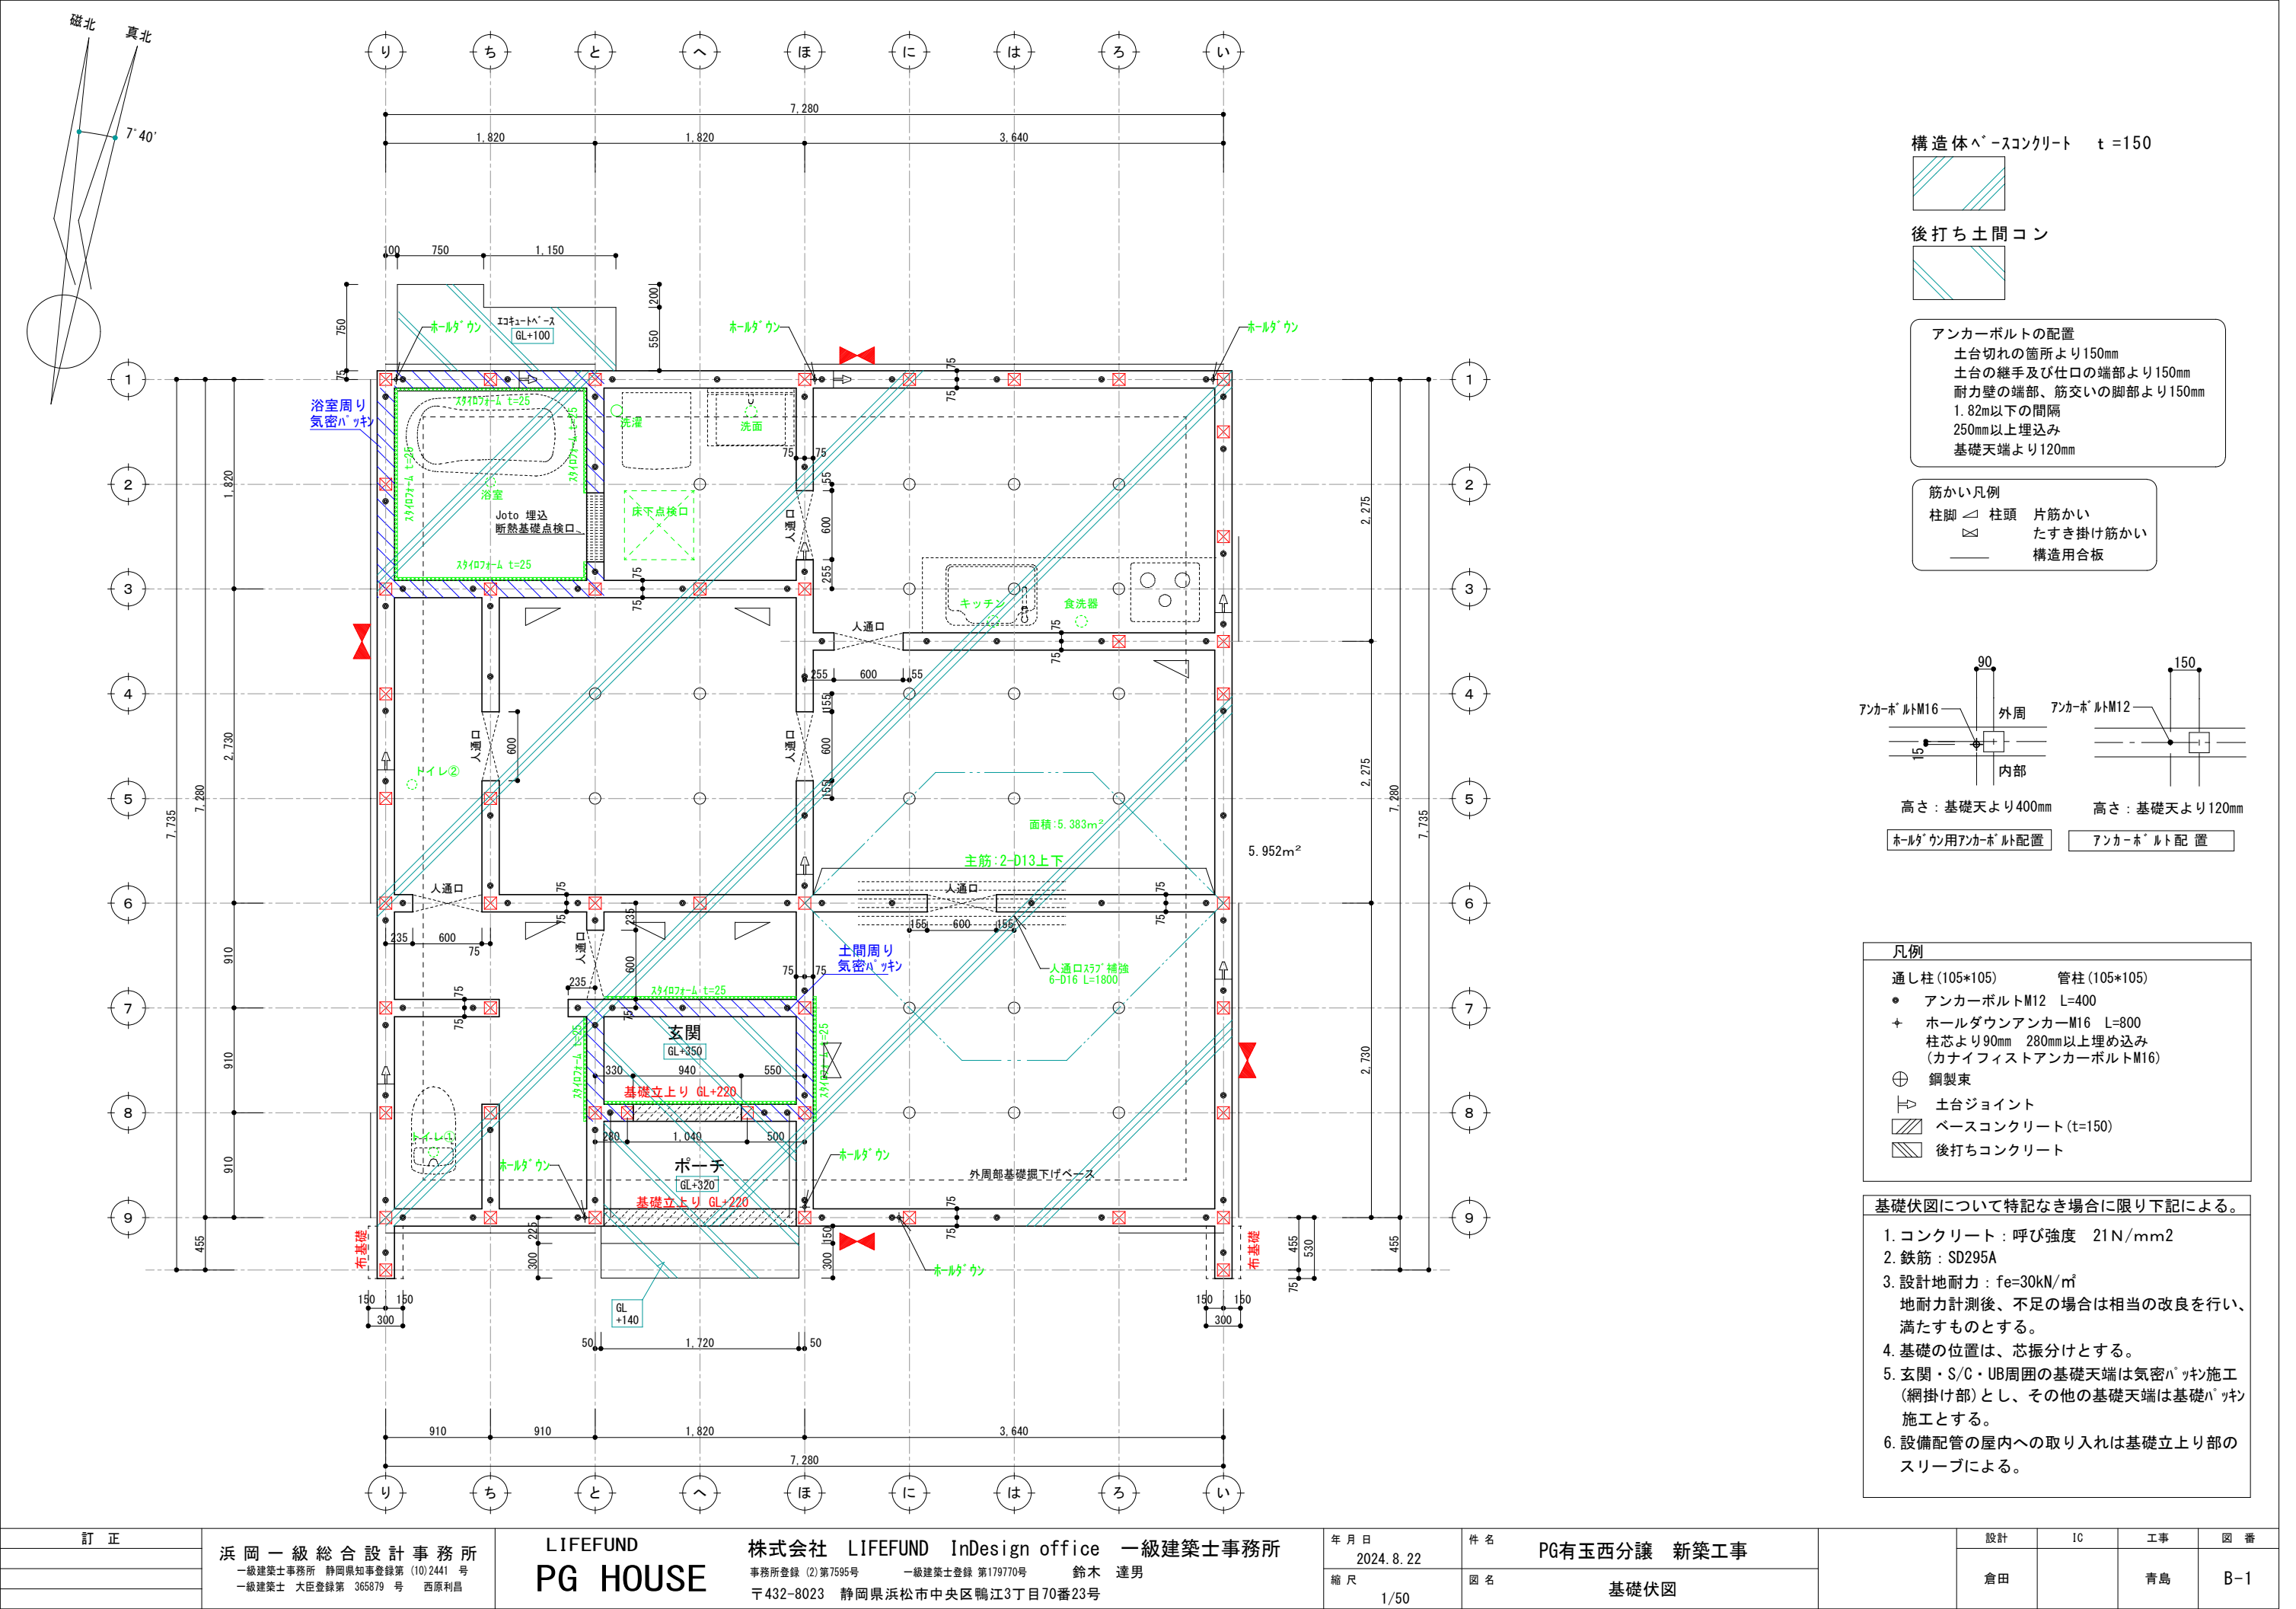

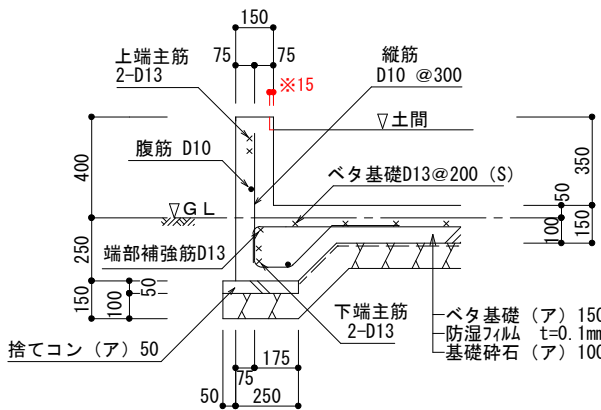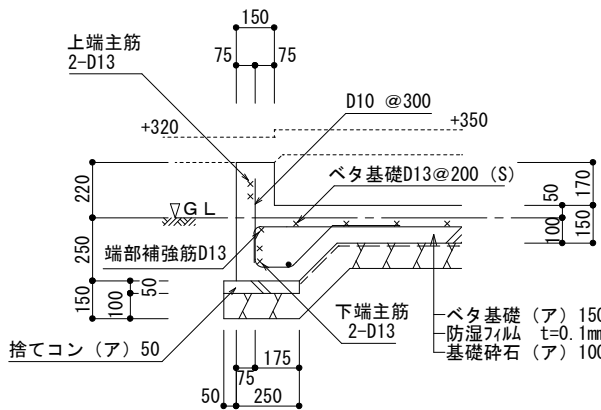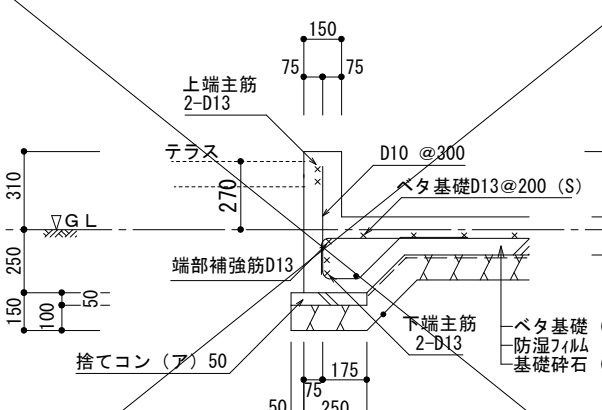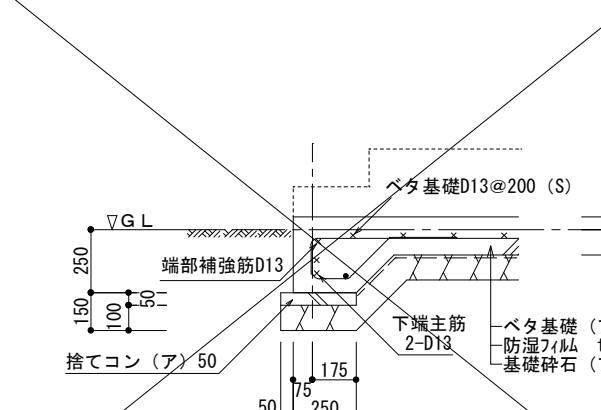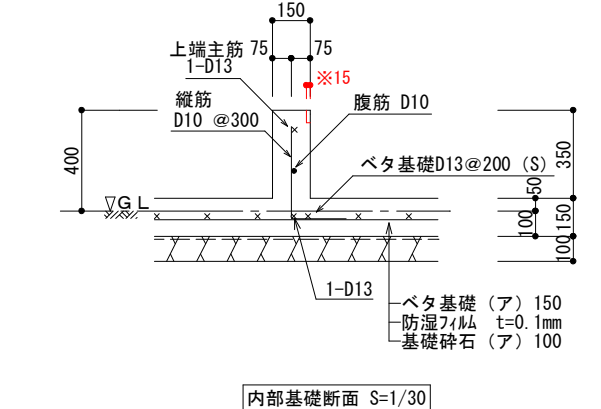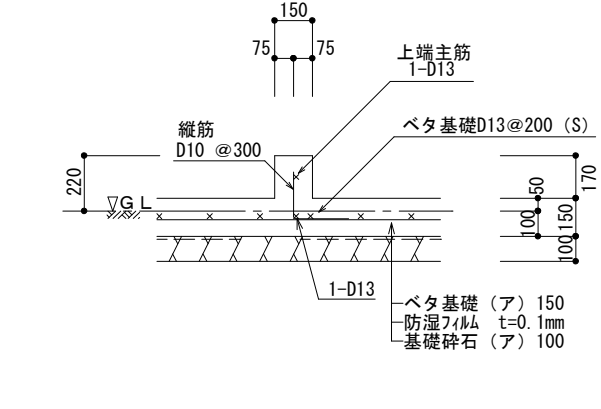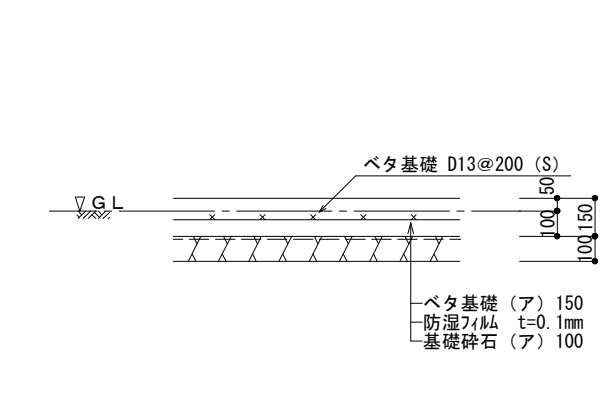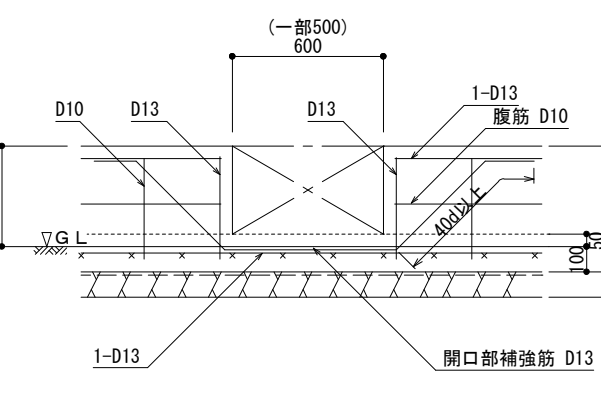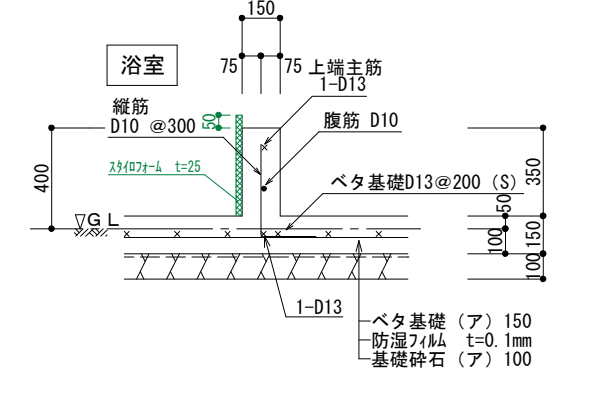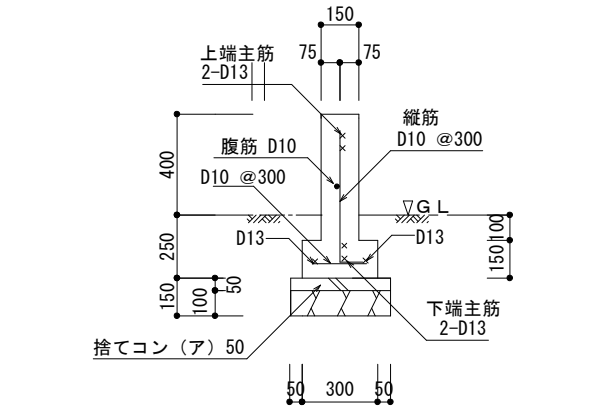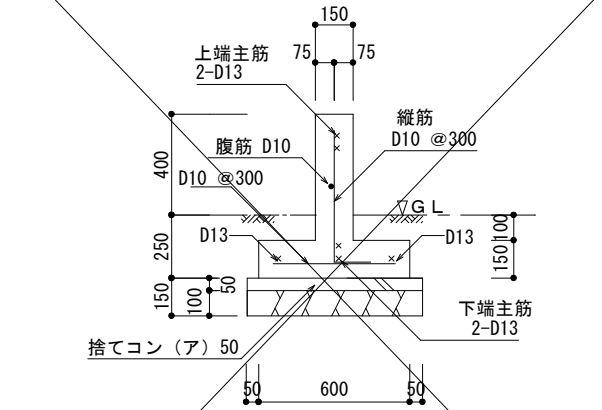 外周基礎断面 S=1/30 ※玄関内土間部分のみ15mm欠き込み	 ポーチ下 外周部基礎断面 S=1/30 倉庫ドア下 外周部基礎断面 S=1/30	 土間納め勝手口ドア下 外周部基礎断面 S=1/30	 立上り無しの基礎断面 S=1/30							
 内部基礎断面 S=1/30 ※玄関内土間部分のみ15mm欠き込み ※注意：基礎伏図に特記のない内部基礎の場合	 ポーチ下 内周部基礎断面 S=1/30 玄関ドア下 内周部基礎断面 S=1/30 玄関内横断基礎断面 S=1/30	 ベタ基礎断面 S=1/30	 人通口補強 S=1/30							
 浴室内部基礎断面 S=1/30 ※注意：基礎伏図に特記のない内部基礎の場合	 布基礎A：袖壁用 基礎断面 S=1/30	 布基礎B：底用独立 基礎断面 S=1/30	<table><tr><td>基礎の寸法 及び 配筋の検証方法</td><td>基礎立上り配筋は、 (財)日本住宅・木材技術 センター発行のスパン表 (増補版)による。 ベタ基礎スラブ配筋は、 まもりすまい保険設計施工 基準同解説のベタ基礎配筋表 による。具体的な寸法・配 筋は基礎詳細図参照。</td></tr></table> 鉄筋断面表記 ●・・・D10を示す。 ×・・・D13を示す。 ※使用しない断面は×を記入。	基礎の寸法 及び 配筋の検証方法	基礎立上り配筋は、 (財)日本住宅・木材技術 センター発行のスパン表 (増補版)による。 ベタ基礎スラブ配筋は、 まもりすまい保険設計施工 基準同解説のベタ基礎配筋表 による。具体的な寸法・配 筋は基礎詳細図参照。					
基礎の寸法 及び 配筋の検証方法	基礎立上り配筋は、 (財)日本住宅・木材技術 センター発行のスパン表 (増補版)による。 ベタ基礎スラブ配筋は、 まもりすまい保険設計施工 基準同解説のベタ基礎配筋表 による。具体的な寸法・配 筋は基礎詳細図参照。									
訂正	浜岡一級総合設計事務所 一級建築士事務所 静岡県知事登録第(10)2441号 一級建築士 大臣登録第365879号 西原利昌	LIFEFUND PG HOUSE	株式会社LIFEFUND InDesign office 一級建築士事務所 事務所登録 (2)第7595号 一級建築士登録 第179770号 鈴木 達男 〒432-8023 静岡県浜松市中央区鴨江3丁目70番23号	年月日 2024.8.22	件名 PG有玉西分譲 新築工事	図名 基礎断面リスト	設計 倉田	IC	工務 青島	図番 B-2
縮尺 1/30										

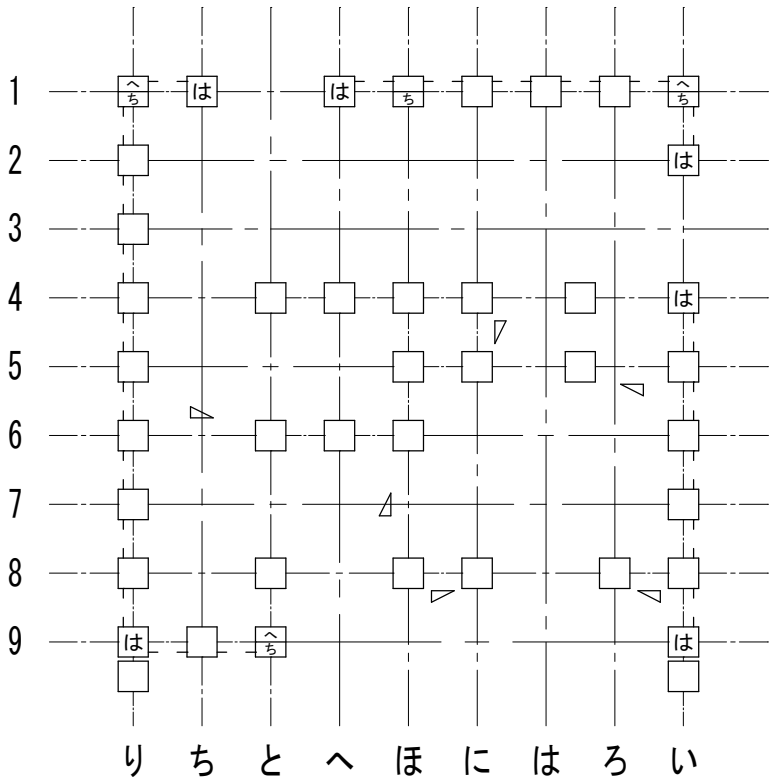

2階柱壁伏図

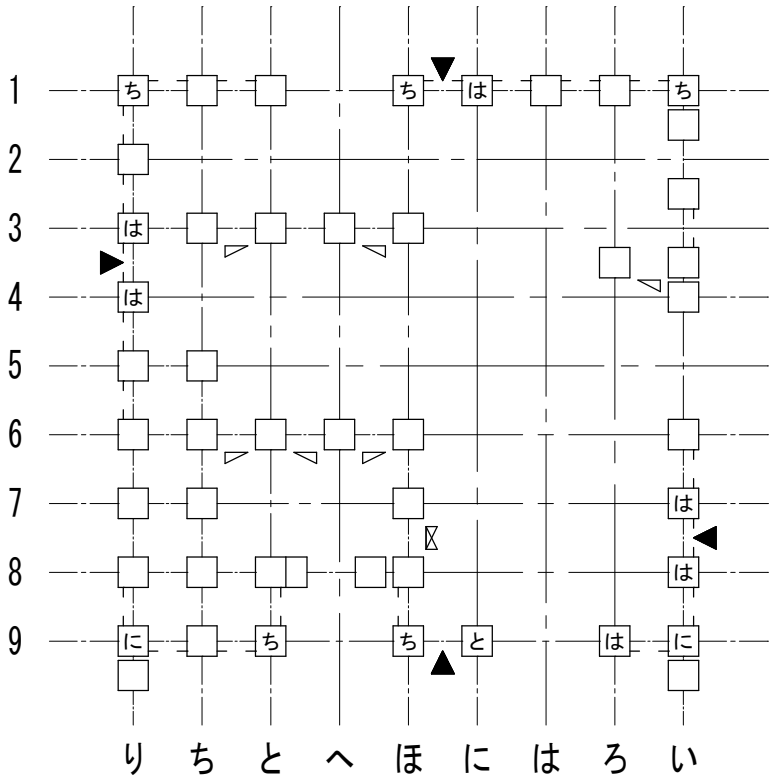

1階柱壁伏図

接合部凡例				*接合部凡例はユーザ設定されたものです。	
記号	仕様（カナイ金物）		N	倍率	
SBCP		スリムビルドコーナー75	0.00	1.00	
SBCP		スリムビルドコーナー75	0.65	1.00	
SBCP	は	スリムビルドコーナー75	1.00	1.00	
ARCG	に	アレントコーナー合板用	1.40	2.20	
ARCG	ほ	アレントコーナー合板用	1.60	2.20	
ARCG	へ	アレントコーナー合板用	1.80	2.20	
HD15	と	ブレイブホールダウン B-HD15	2.80	3.60	
HD20	ち	ブレイブホールダウン B-HD20	3.70	4.70	
HD25	り	ブレイブホールダウン B-HD25	4.70	4.80	
HD30	ぬ	ブレイブホールダウン B-HD30	5.60	7.20	
J1	る	腰掛け蟻若しくは大入れ蟻掛け+羽子板ボルト、短冊金物		1.90	
J2	を	腰掛け蟻若しくは大入れ蟻掛け+羽子板ボルト、短冊金物×2		3.00	

※表示なき金物は「は」とする。

梁継手・仕口用

梁継手・仕口用

接合部凡例				*接合部凡例はユーザ設定されたものです。	
記号	仕様（タナカ金物）		N	倍率	
FCP		フックコーナー	0.00	1.00	
FCP		フックコーナー	0.65	1.00	
FCP	は	フックコーナー	1.00	1.00	
GCP	に	シナコーナー	1.40	2.20	
GCP	ほ	シナコーナー	1.60	2.20	
GCP	へ	シナコーナー	1.80	2.20	
HD15	と	ビス止めホールダウンU HD15	2.80	3.60	
HD20	ち	ビス止めホールダウンU HD20	3.70	4.70	
HD25	り	ビス止めホールダウンU HD25	4.70	4.80	
HD30	ぬ	ビス止めホールダウンU HD15×2 (HD35)	5.60	7.20	
J1	る	腰掛け蟻若しくは大入れ蟻掛け+羽子板ボルト、短冊金物		1.90	
J2	を	腰掛け蟻若しくは大入れ蟻掛け+羽子板ボルト、短冊金物×2		3.00	

※表示なき金物は「は」とする。

梁継手・仕口用

梁継手・仕口用

筋かいの種類に応じた筋かいの端部の接合部の仕様		
	筋かいの種類	接合部の仕様（構造方法）
イ	鉄筋φ9	柱又は横架材を貫通し、三角座金を介してナット締め、又は鋼板添え板を用い鋼板を柱及び横架材にCN90, 8本平打ち
ロ	筋かい:15×90	柱・横架材を欠き込み、柱・横架材双方に対してN65, 5本平打ち
ハ	筋かい:30×90	鋼板添え板t=1.6mmを筋かいに対してボルトφ12及びCN65, 3本平打ち、柱に対してCN65, 3本平打ち、横架材に対してCN65, 4本平打ち。筋かいプレートBP同等品
ニ	筋かい:45×90	鋼板添え板t=2.3mmを筋かいに対してボルトφ12及びスクリュー釘φ4.5L50, 7本平打ち、柱及び横架材に対してスクリュー釘φ4.5L50, 5本平打ち。筋かいプレートBP-2同等品
ホ	筋かい:90×90	柱又は横架材にボルトφ12mmを用いて一面剪断接合

胴差と通し柱の接合部の仕様		
	胴差と通し柱の条件	仕口
T1	通し柱の片側に胴差が来る場合	胴差を柱にかたぎ大入れ短ほぞ差しの上、羽子板ボルト、かね折り金物又は同等以上の仕口
T2	通し柱の両側に胴差が来る場合	胴差を柱にかたぎ大入れ短ほぞ差しの上、短冊金物又は、同等以上の仕口で胴差相互を緊結
T3	通し柱と胴差の接合部の近くに90×90以上の筋かいが来る場合(通し柱が建物の出隅にあるか、筋かい壁が外壁と直交して接する場合)	胴差を通し柱に、15KN用引き寄せ金物を水平に用いて緊結