



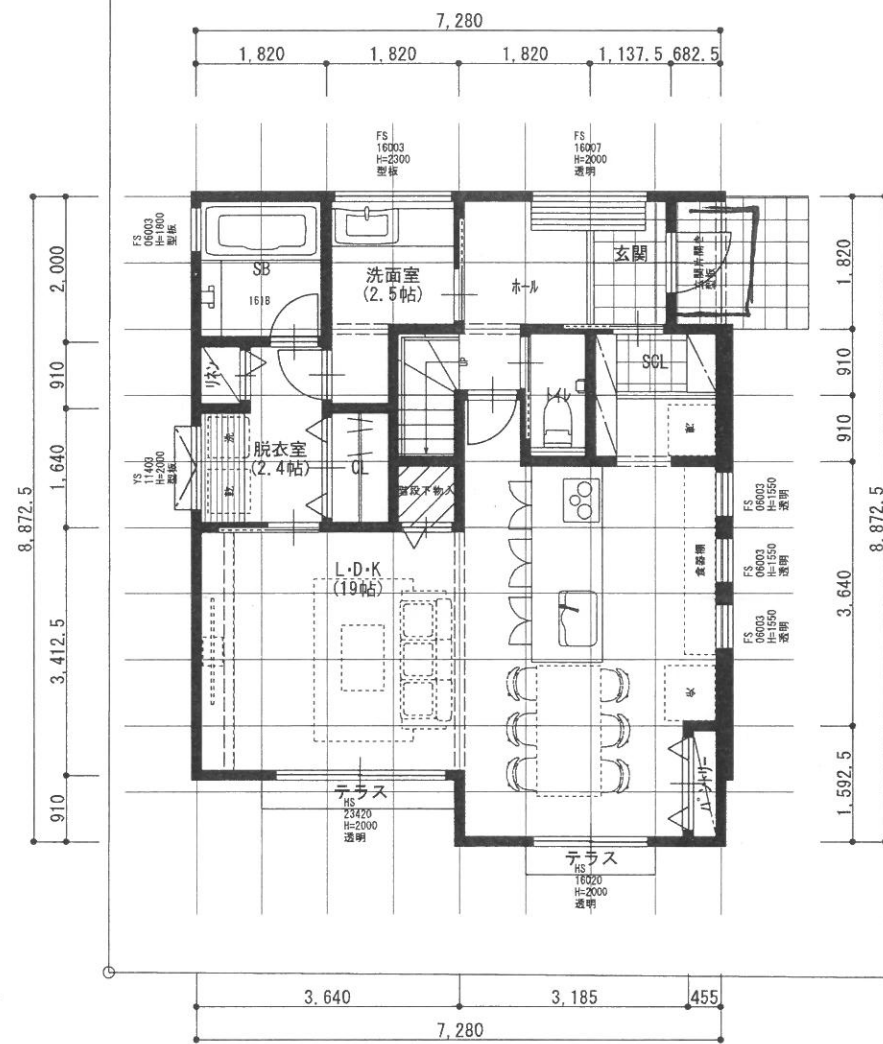

1階平面図 S=1/100

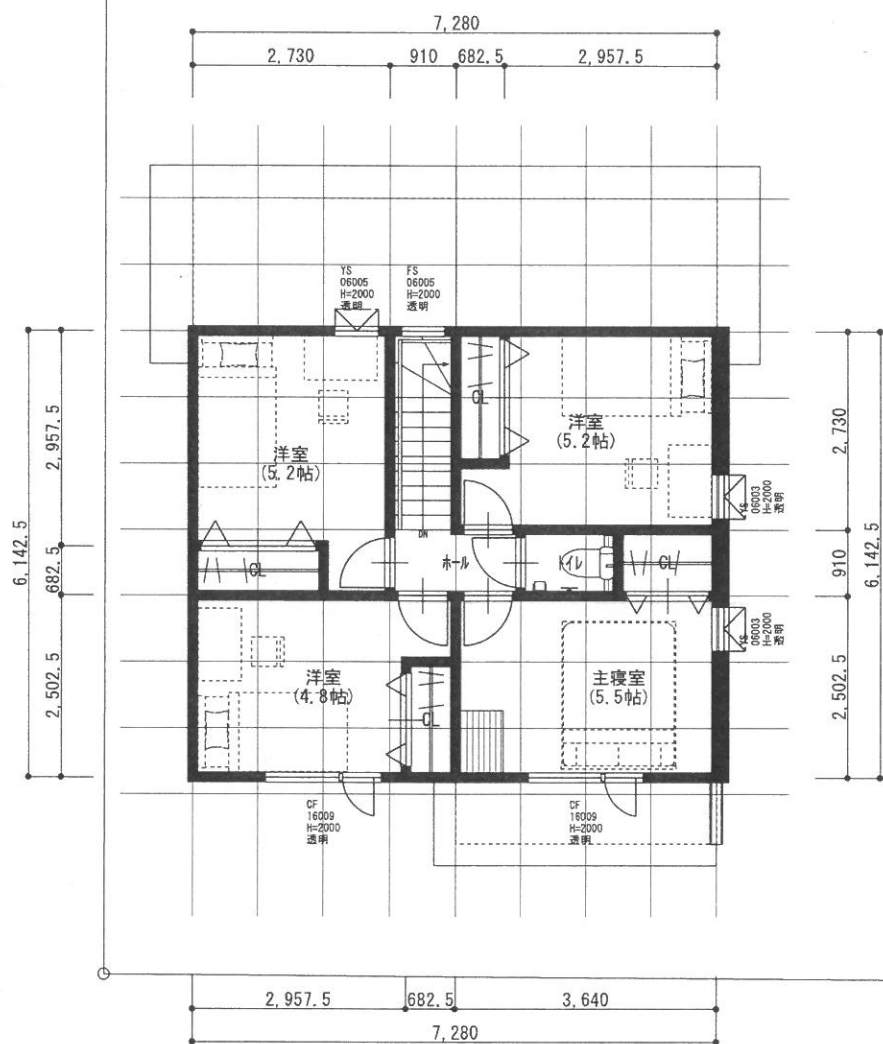


2階平面図 S=1/100

※【S・O】
※各階標準スリット仕様（壁高さ：2450mm）
※敷地形状・面積、道路・隣地との高低差は、暫定です。
※この計画は、敷地調査前につき、調査後に変更になる場合があります。


※家具の搬入経路は、詳細打ち合わせによる確認が必要になります。
※計画敷地と隣地及び道路との高低差が60cm以上の場合、別途対応が必要になる場合があります。
※民法第235条により、隣地境界線から1m未満の開口部やバルコニー・縁側等には、目隠し取り付け請求の権利が隣家に認められています。隣家の請求により追加工事やプランが一部変更になる場合があります。
※給排水・空調・換気設備の計画により、下がり天井等、プランが一部変更になる場合があります。
※構造計算により、プラン、構造用面材、壁倍率および耐震等級が変更になる場合があります。
※敷地状況及び所轄行政庁の指導によりプラン変更する場合があります。あらかじめ御承ください。

2m以上の高低差有無(道路・隣地) ☐有 ☒無
()
既存擁壁壁における検査済証の有無 ☐有 ☒無
混構造(RC工事)の有無 ☐有 ☒無
住宅以外の用途の有無 ☐有 ☒無
()


住友不動産株式会社	面積表	建築面積		1階床	2階床		延床面積	敷地面積	建ぺい率(%)	法定建ぺい率(%)	建築地 静岡県 特別用途地区 第1種低層住居専用地域	2×4工法 防火指定 法第22条区域	営業 設計 製図 岡本 川瀬 大澤	番号 日付 縮尺 1237833-15 2024年8月22日 1/100
	法	M ²	61.27	60.03	44.71		104.74	287.34	21.32	30.00				
	定	坪	18.53	18.15	13.52		31.68	86.92	容積率(%)	法定容積率(%)				
	工	M ²		61.27	44.71		105.98		36.45	50.00				
	対	坪		18.53	13.52		32.05	J A	用途地域	高度制限				

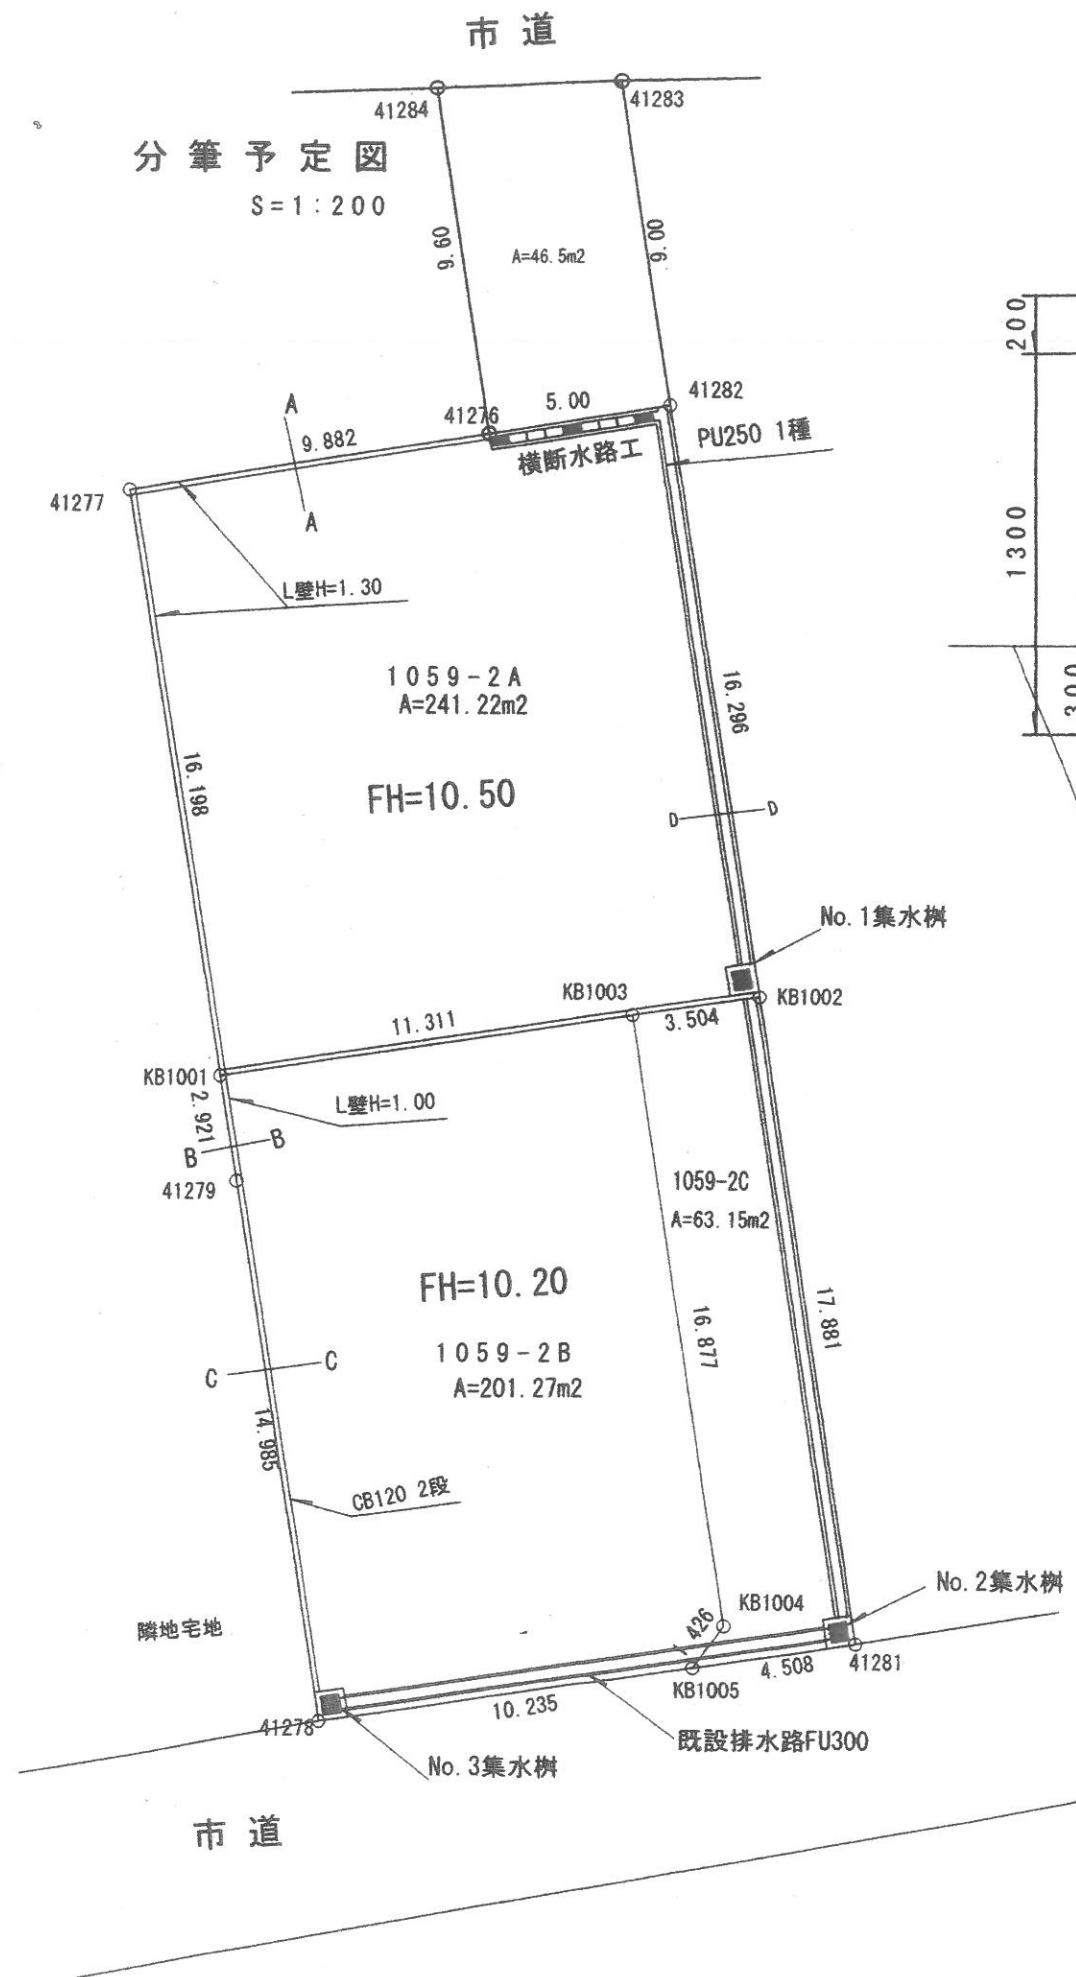


L型擁壁工 H=1300
S=1:25

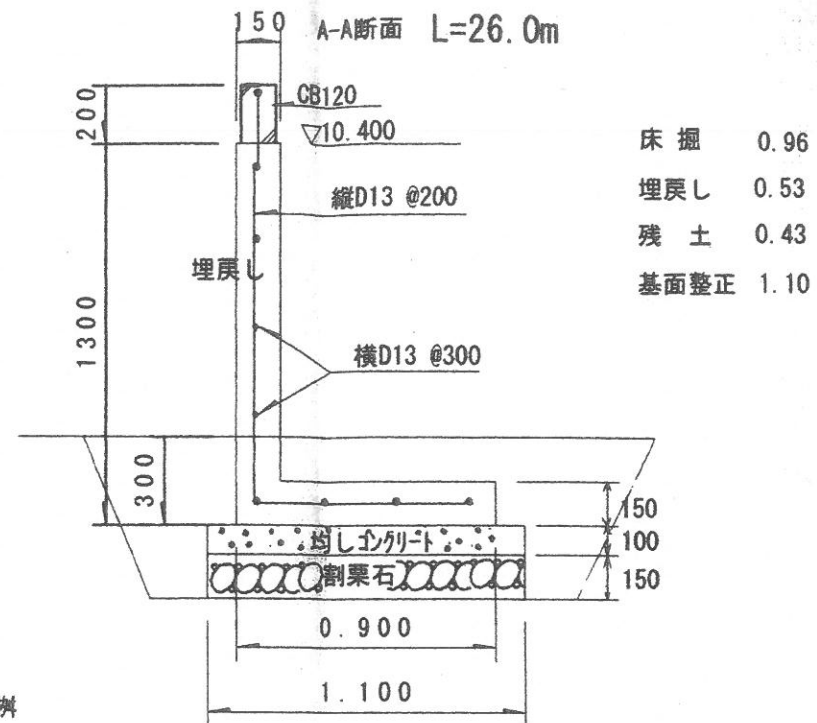

L型擁壁工 H=1000
S=1:25

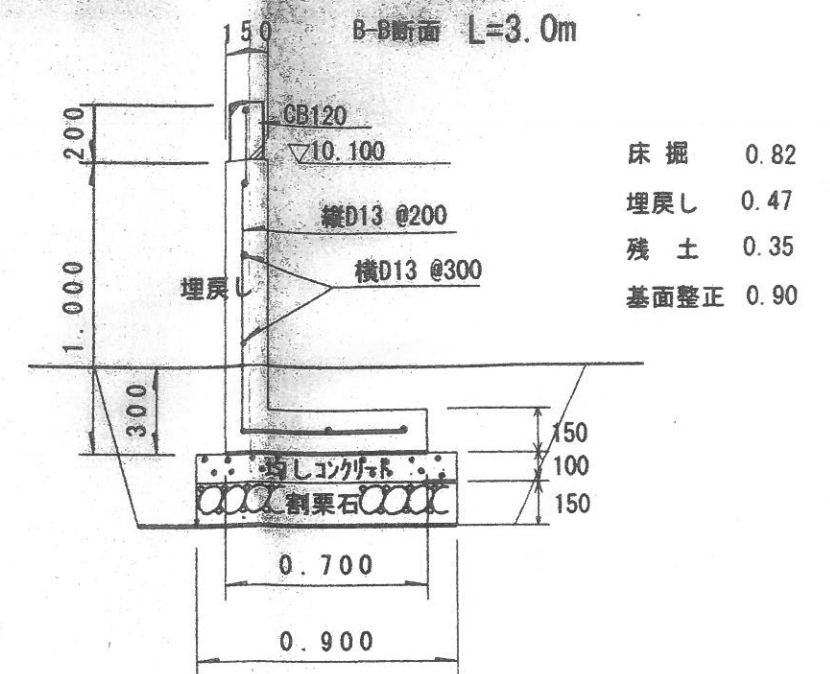

PU250 1種 D-D
L=37.6m

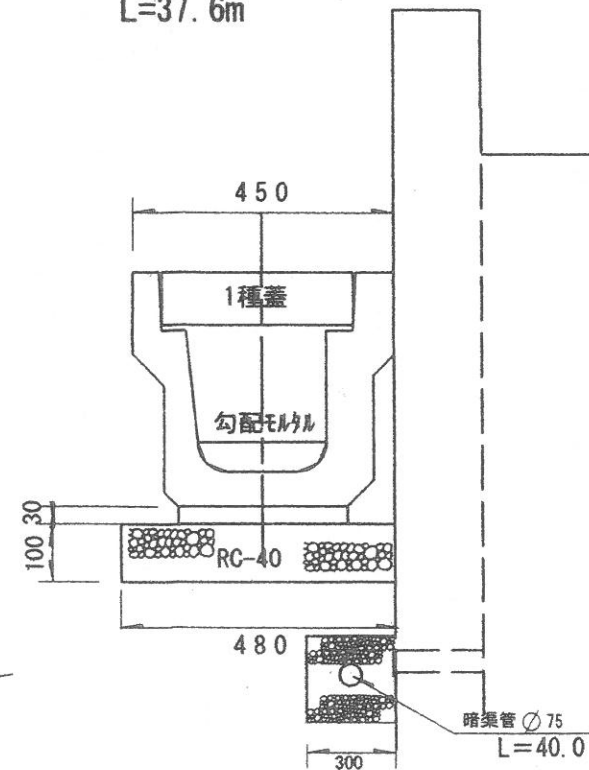

CB120積み 2段 C-C
L=14.20m

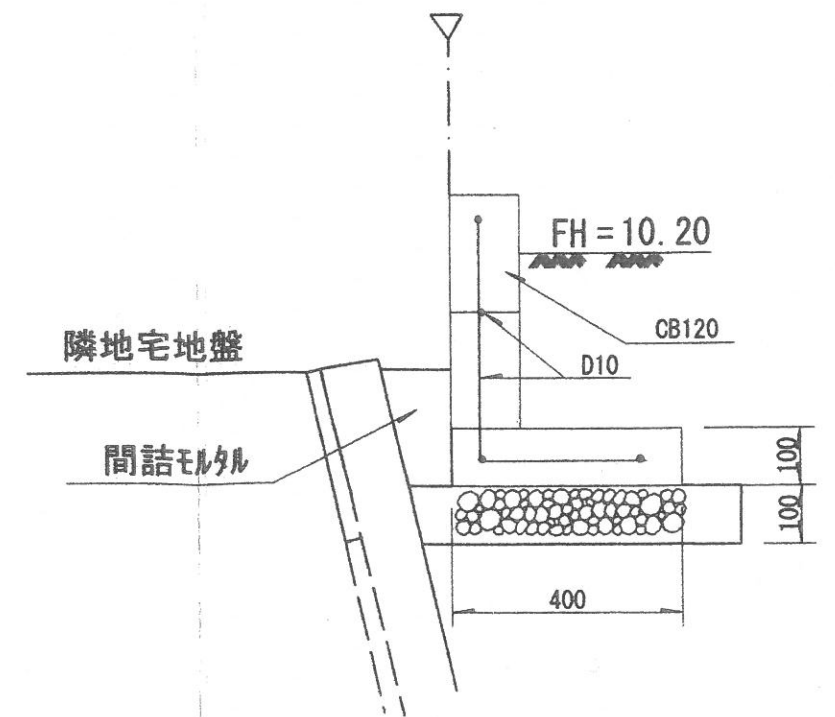




図 面 名	計画平面図
土地所在	掛川市宮脇字五輪田1059番2地先
縮 尺	S=1/300
作製年月日	令和5年3月1日
作 製 者	磐田市見付4859番地1 土地家屋調査士・行政書士 土 屋 純 TEL0538 (35) 8721 FAX0538 (35) 8722 土地家屋調査士登録番号 静岡第1591号 行政書士登録番号 第05170664号