



# 加工承認書

2024年10月29日

拝啓 貴社益々ご繁栄のこととお慶び申し上げます。平素は、格別のご配慮をいただき厚くお礼申し上げます。  
さて、この度貴社よりご依頼のありましたプレカット図面を送付致します。  
つきましては、送付図面の内容確認及び加工のご承認を本紙にて、ご回答を頂きますようお願い申し上げます。

ハイビック(株) CADセンター

発 注 (株)LIFEFUND 御 中  
担 当 者 ご担当者 様  
物 件 名 伊藤友章 様邸  
FAX

浜松CAD室 担当:鈴木淳

携帯 070-3173-7584

浜松市浜名区宮 口2461 TEL 053-582-3711


FAX 053-582-3701

プレカット販売店:浜松店 営業担当:大久保

## ■伏図確認進捗状況

|                                                    |       |       |
|----------------------------------------------------|-------|-------|
| 第1回送信日 10/29 枚送信                                   | 1 便 目 | 上 棟 日 |
| お世話になっております。<br>プレカット伏図を作成致しました。<br>御確認宜しくお願い致します。 | 1/6   |       |
| 第2回送信日 11/25 枚送信                                   | 1 便 目 | 上 棟 日 |
| 訂正図面を修正致し                                          |       |       |
| 第3回送信日 / 枚送信                                       | 1 便 目 | 上 棟 日 |
|                                                    |       |       |
| 第4回送信日 / 枚送信                                       | 1 便 目 | 上 棟 日 |
|                                                    |       |       |
| 第5回送信日 / 枚送信                                       | 1 便 目 | 上 棟 日 |
|                                                    |       |       |
| 第6回送信日 / 枚送信                                       | 1 便 目 | 上 棟 日 |
|                                                    |       |       |
| 第7回送信日 / 枚送信                                       | 1 便 目 | 上 棟 日 |
|                                                    |       |       |

## ■矩計寸法確認

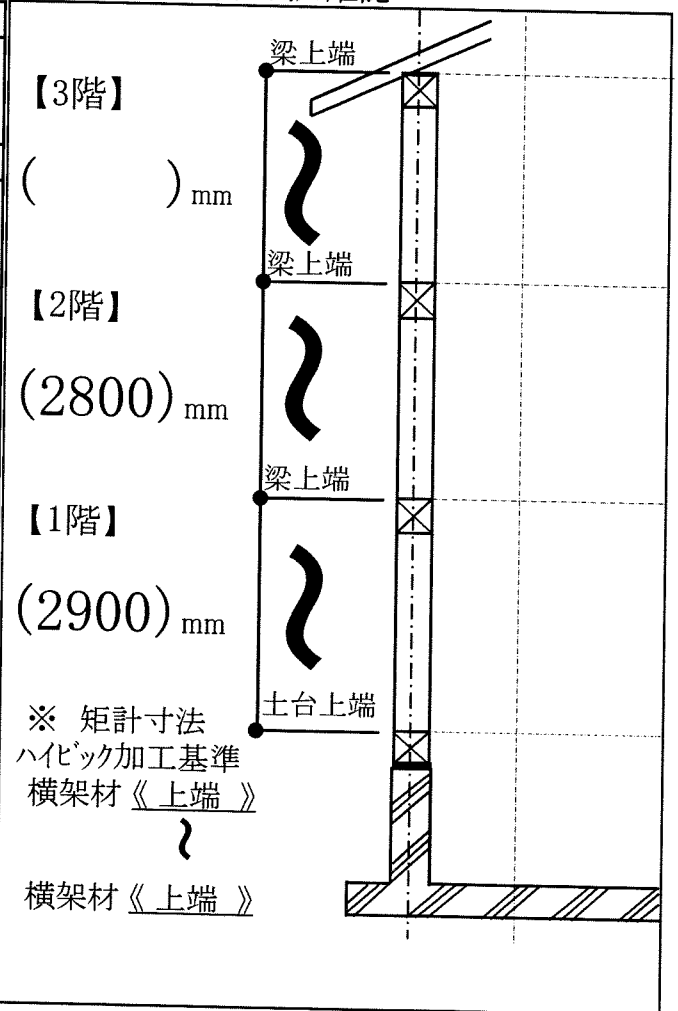

承認期限

月 日

※承認期限までにご承認お願い致します。

※ 月 日送付の図面一式にて、加工承認する。

- ・ ご承認を頂いた後は工場の生産工程に合わせ、随時加工に入らせて頂きます。
- ・ ご承認後の変更は内容によって有料となる場合がありますのでご了承願います。
- ・ 化粧材について、松系の材料にはブルーステインの混入の可能性が御座います。

加工承認日 (※承認期限までにご承認お願い致します。)



※ 年 月 日 ※承認者名

様

※

印

※部分は必ずご記入下さい(電子印はご遠慮願います様ご協力下さい)

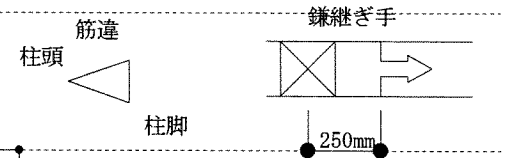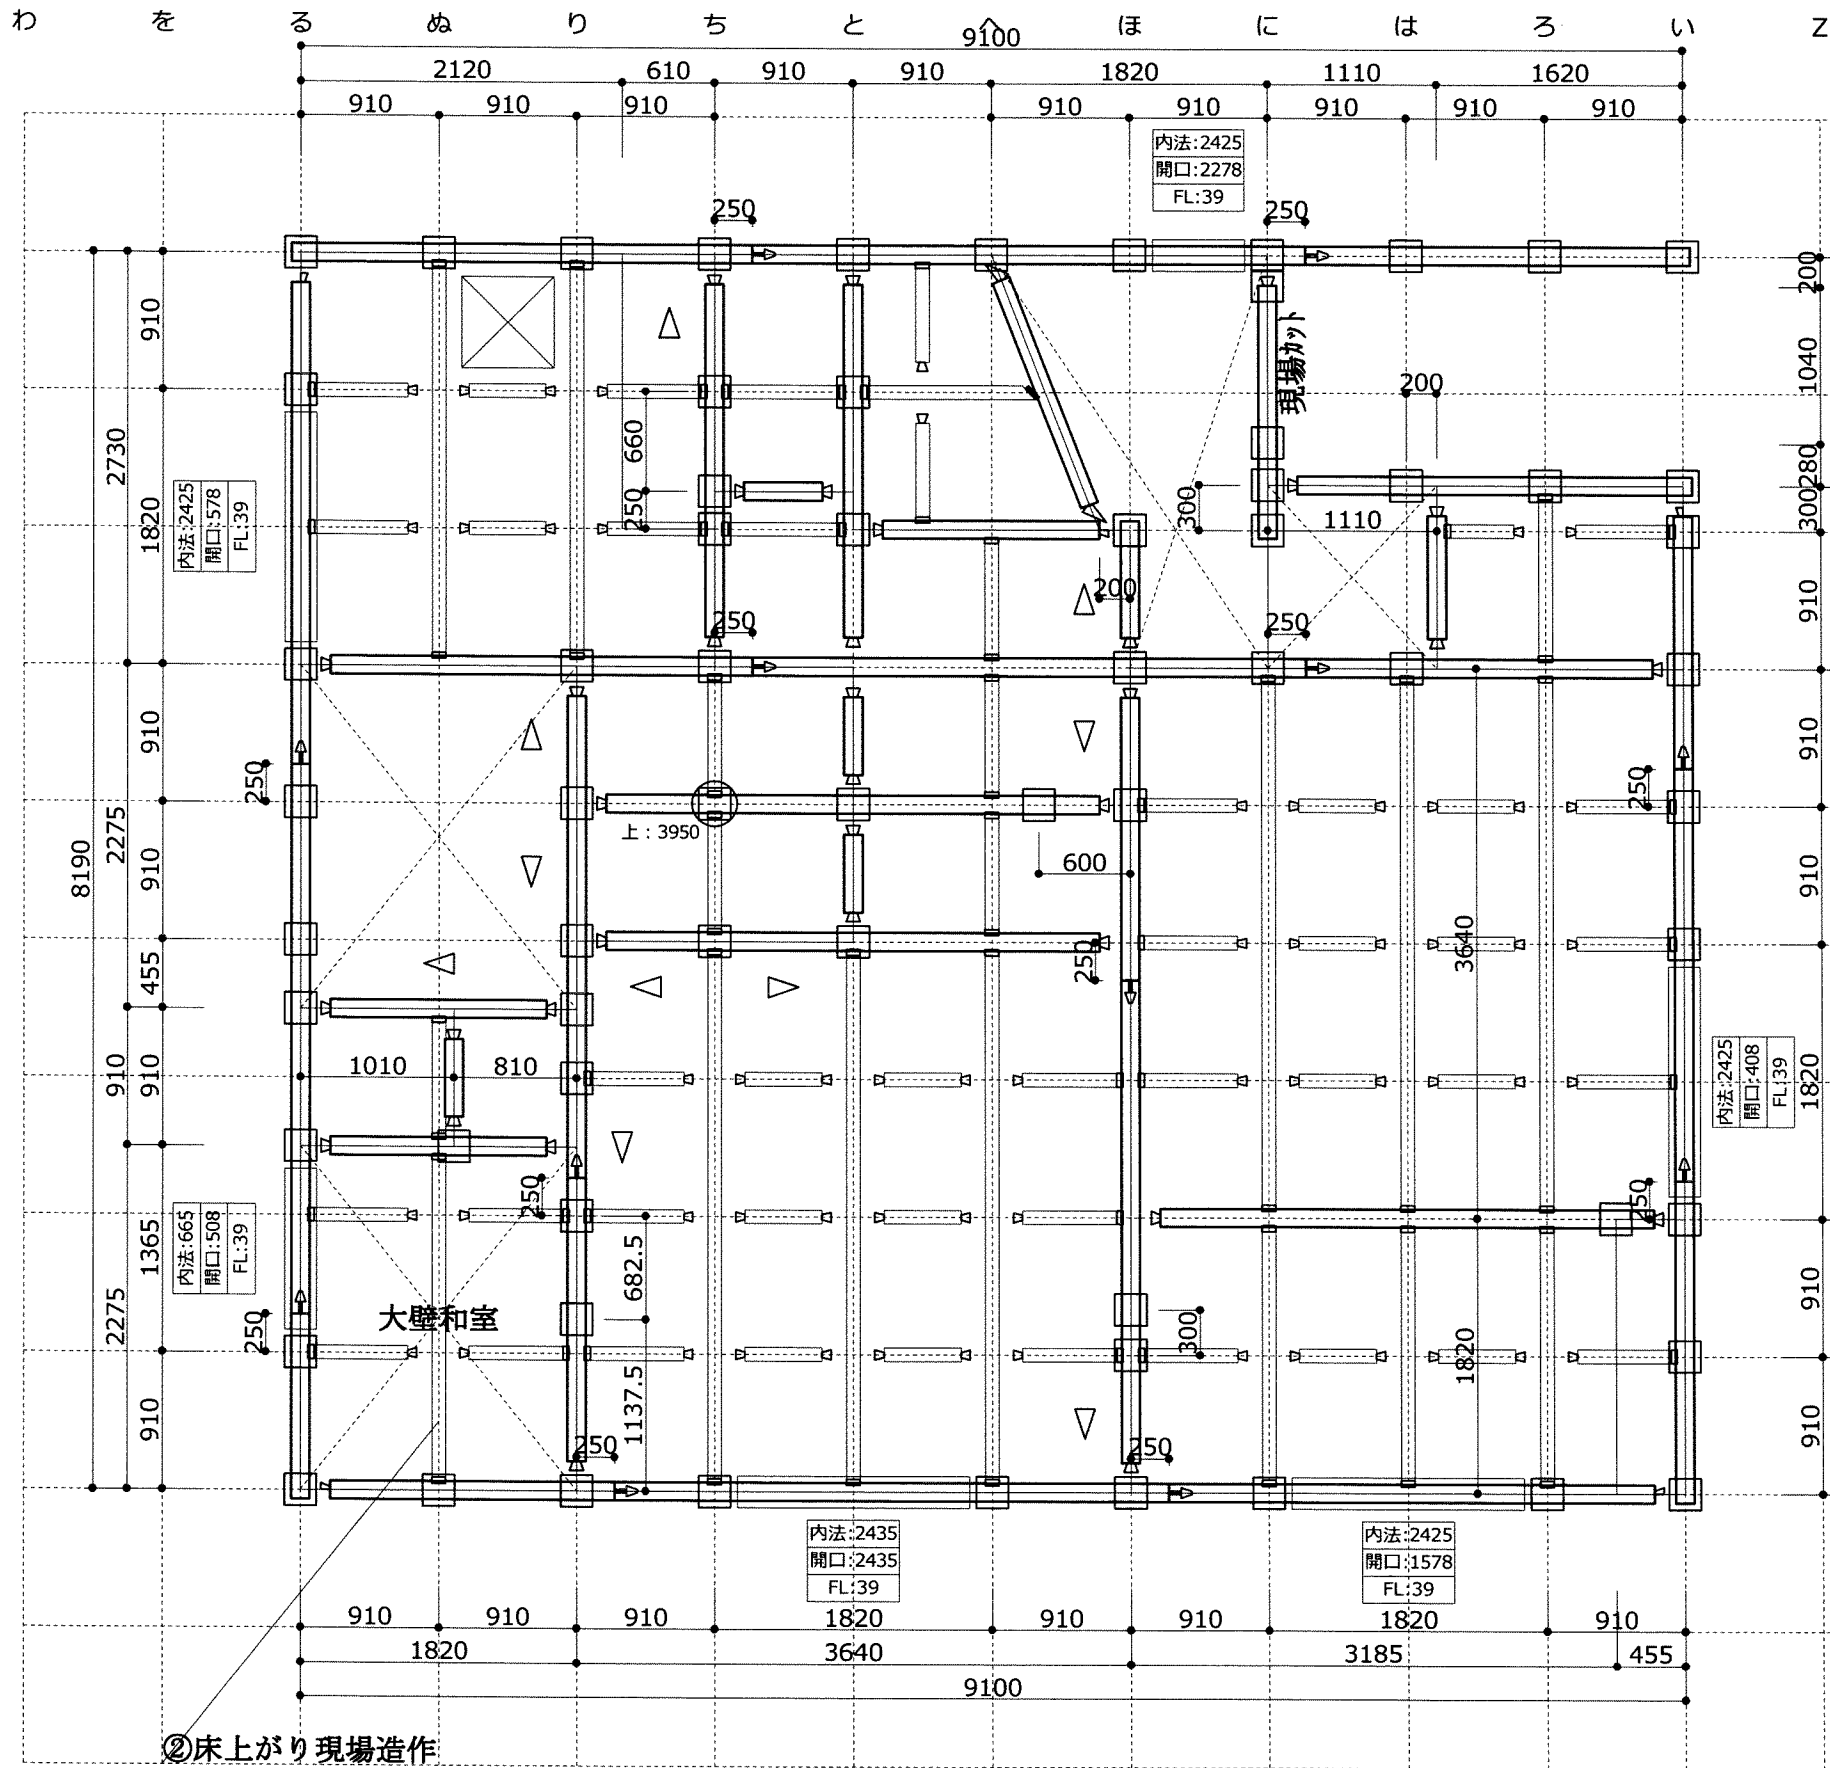

下記の内容ご確認・返答下さい

- ①土台位置、継手位置 確認お願いします。  
【OK / NG→図面に指示お願いします】
- ②大壁和室床上がり現場造作で  
宜しいですか？  
【OK / NG→図面に指示お願いします】
- ③窓台・マガサ 高さ確認お願いします。  
【OK / NG→図面に指示お願いします】

0  
1  
2  
3  
4  
5  
6  
7  
8  
9  
10  
11  
12

| 凡 例  |                 |      |  |
|------|-----------------|------|--|
| 材 種  | 樹種・等級・材寸        |      |  |
| 土 台  | 檜 支給材 105×105   |      |  |
| 大 引  | 檜 支給材 90×90     |      |  |
| 通し柱  | 杉集成 構造用 105     |      |  |
| 管 柱  | 杉集成 構造用 105     |      |  |
| 火打土台 | 防腐防蟻処理 特等 90×45 |      |  |
|      | 化粧管柱            | 床 柱  |  |
|      | 階 段 柱           | ポーチ柱 |  |
|      | 地 束             | 吊 束  |  |
|      | 間 柱             |      |  |
|      | 根 太             |      |  |
|      | 蟻               |      |  |
|      | 寄 蟻             |      |  |
|      | 逆 蟻             |      |  |
|      | 大入れ             |      |  |
|      | 大引き             |      |  |
|      | 兜               |      |  |
|      | 茶 臼             |      |  |
|      | 鎌 継             |      |  |
|      | 蟻 継             |      |  |
|      | 桁差ホゾ            |      |  |
|      | 胴差ホゾ            |      |  |

ハビック CADセンター 浜松CAD室

434-0004

静岡県浜松市浜名区宮口2461

TEL :053-582-3711

FAX :053-582-3701

■検印

|        |      |    |
|--------|------|----|
| ■モジュール | 910  | mm |
| ■桁 高   | 2900 | mm |
| ■屋根勾配  | 0.5  | 寸  |

■工事名称  
(株)LIFEFUND様 伊藤友章様邸


■印刷日時  
2024年11月25日

■縮尺  
1 / 50

■図面名称  
土台伏図

■物件番号  
HHM0192

わをるぬりちとへほにはろいZ

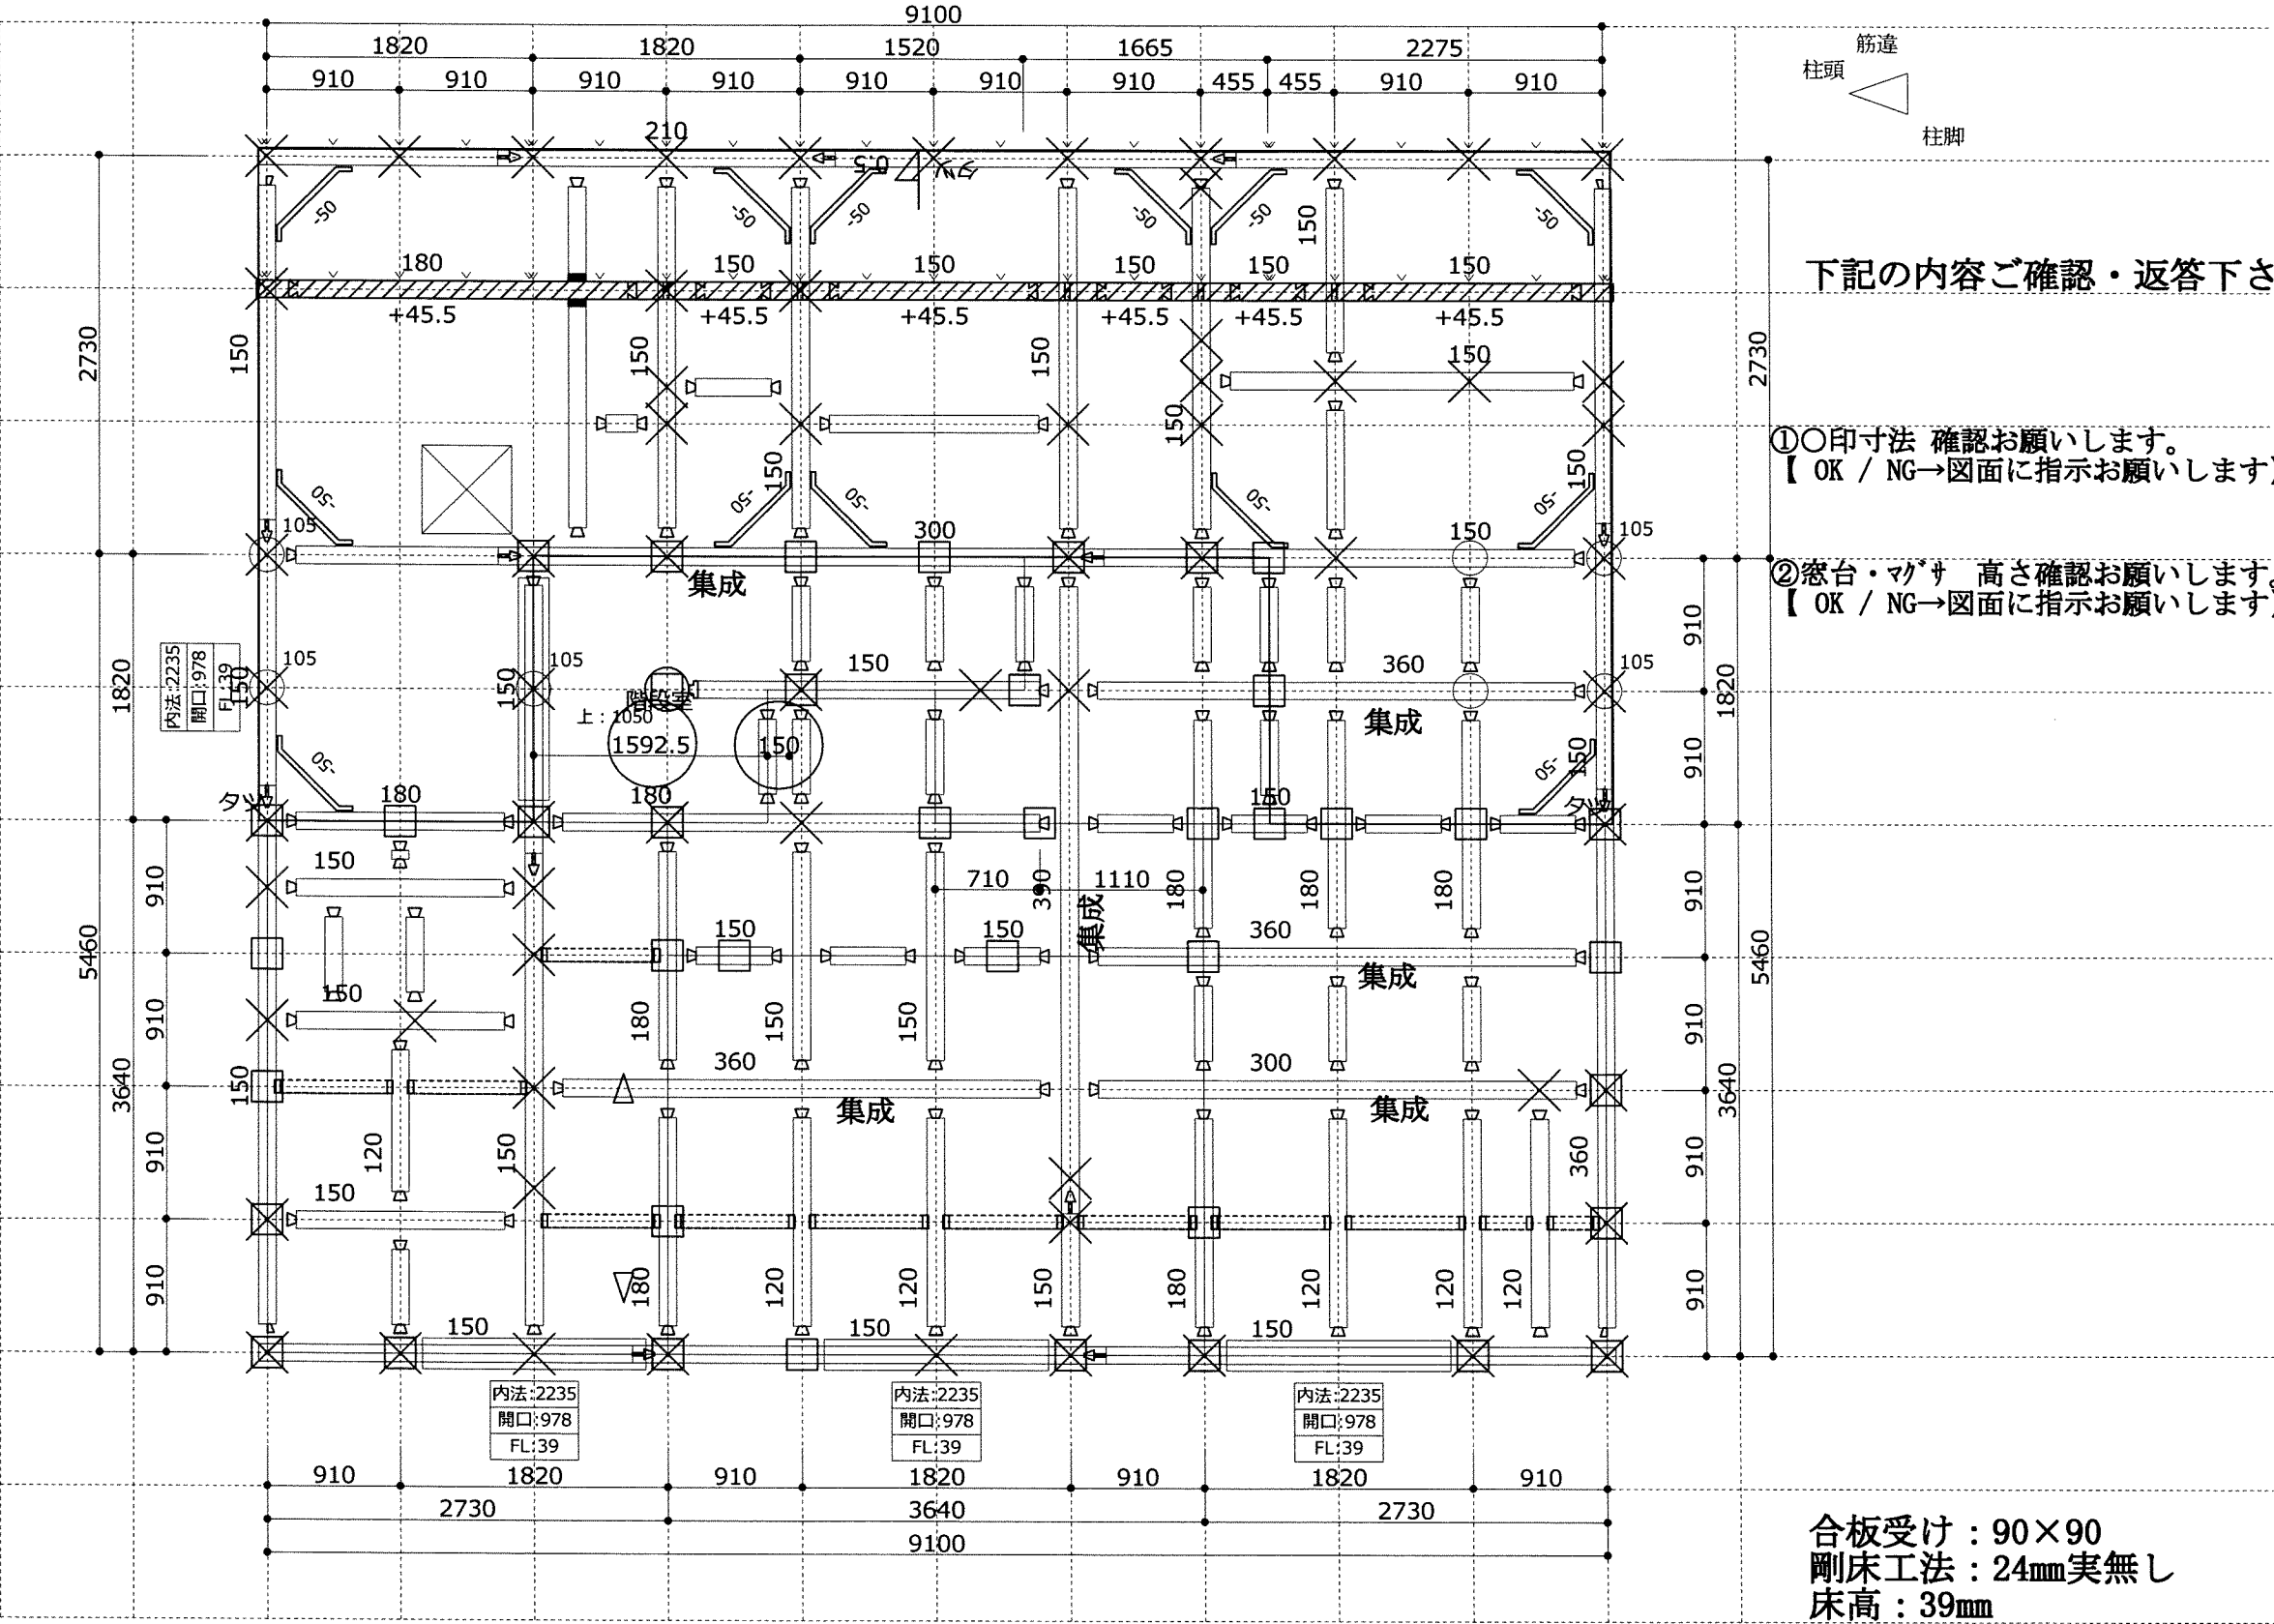

下記の内容ご確認・返答下さい

- ①〇印寸法 確認お願いします。  
【OK / NG→図面に指示お願いします】
- ②窓台・マガサ 高さ確認お願いします。  
【OK / NG→図面に指示お願いします】

| 凡 例  |                        |     |      |
|------|------------------------|-----|------|
| 材 種  | 樹種・等級・材寸               |     |      |
| 梁    | 米松<br>乾燥特等<br>105×105  |     |      |
| 通し柱  | 杉集成<br>構造用<br>105      |     |      |
| 管 柱  | 杉集成<br>構造用<br>105      |     |      |
| 小屋束  | 檜<br>支給材<br>90         |     |      |
| 火打梁  | 鉄アングル<br>乾燥特等<br>90×90 |     |      |
| 登 梁  | 米松<br>乾燥特等<br>105×105  |     |      |
| 化粧管柱 | 床 柱                    | 階段柱 | ポーチ柱 |
| 地 束  | 吊 束                    |     |      |
| 間 柱  |                        |     |      |
| 根 太  |                        |     |      |
| 蟻    |                        |     |      |
| 寄 蟻  |                        |     |      |
| 逆 蟻  |                        |     |      |
| 大入れ  |                        |     |      |
| 大引き  |                        |     |      |
| 兜    |                        |     |      |
| 茶 臼  |                        |     |      |
| 鎌 継  |                        |     |      |
| 蟻 継  |                        |     |      |
| 桁差ホゾ |                        |     |      |
| 胴差ホゾ |                        |     |      |

ハイテック CADセンター 浜松CAD室

434-0004

静岡県浜松市浜名区宮口2461

TEL :053-582-3711

FAX :053-582-3701

検印

■シールド 910

■桁 高 2800

■屋根勾配 0.5

■工事名称  
株式会社LIFEFUND様 伊藤友章様邸


■印刷日時  
2024年11月25日

■縮尺  
1 / 50

■図面名称  
2階床伏図

■物件番号  
HHM0192

わをるぬりちとへほにはろいZ

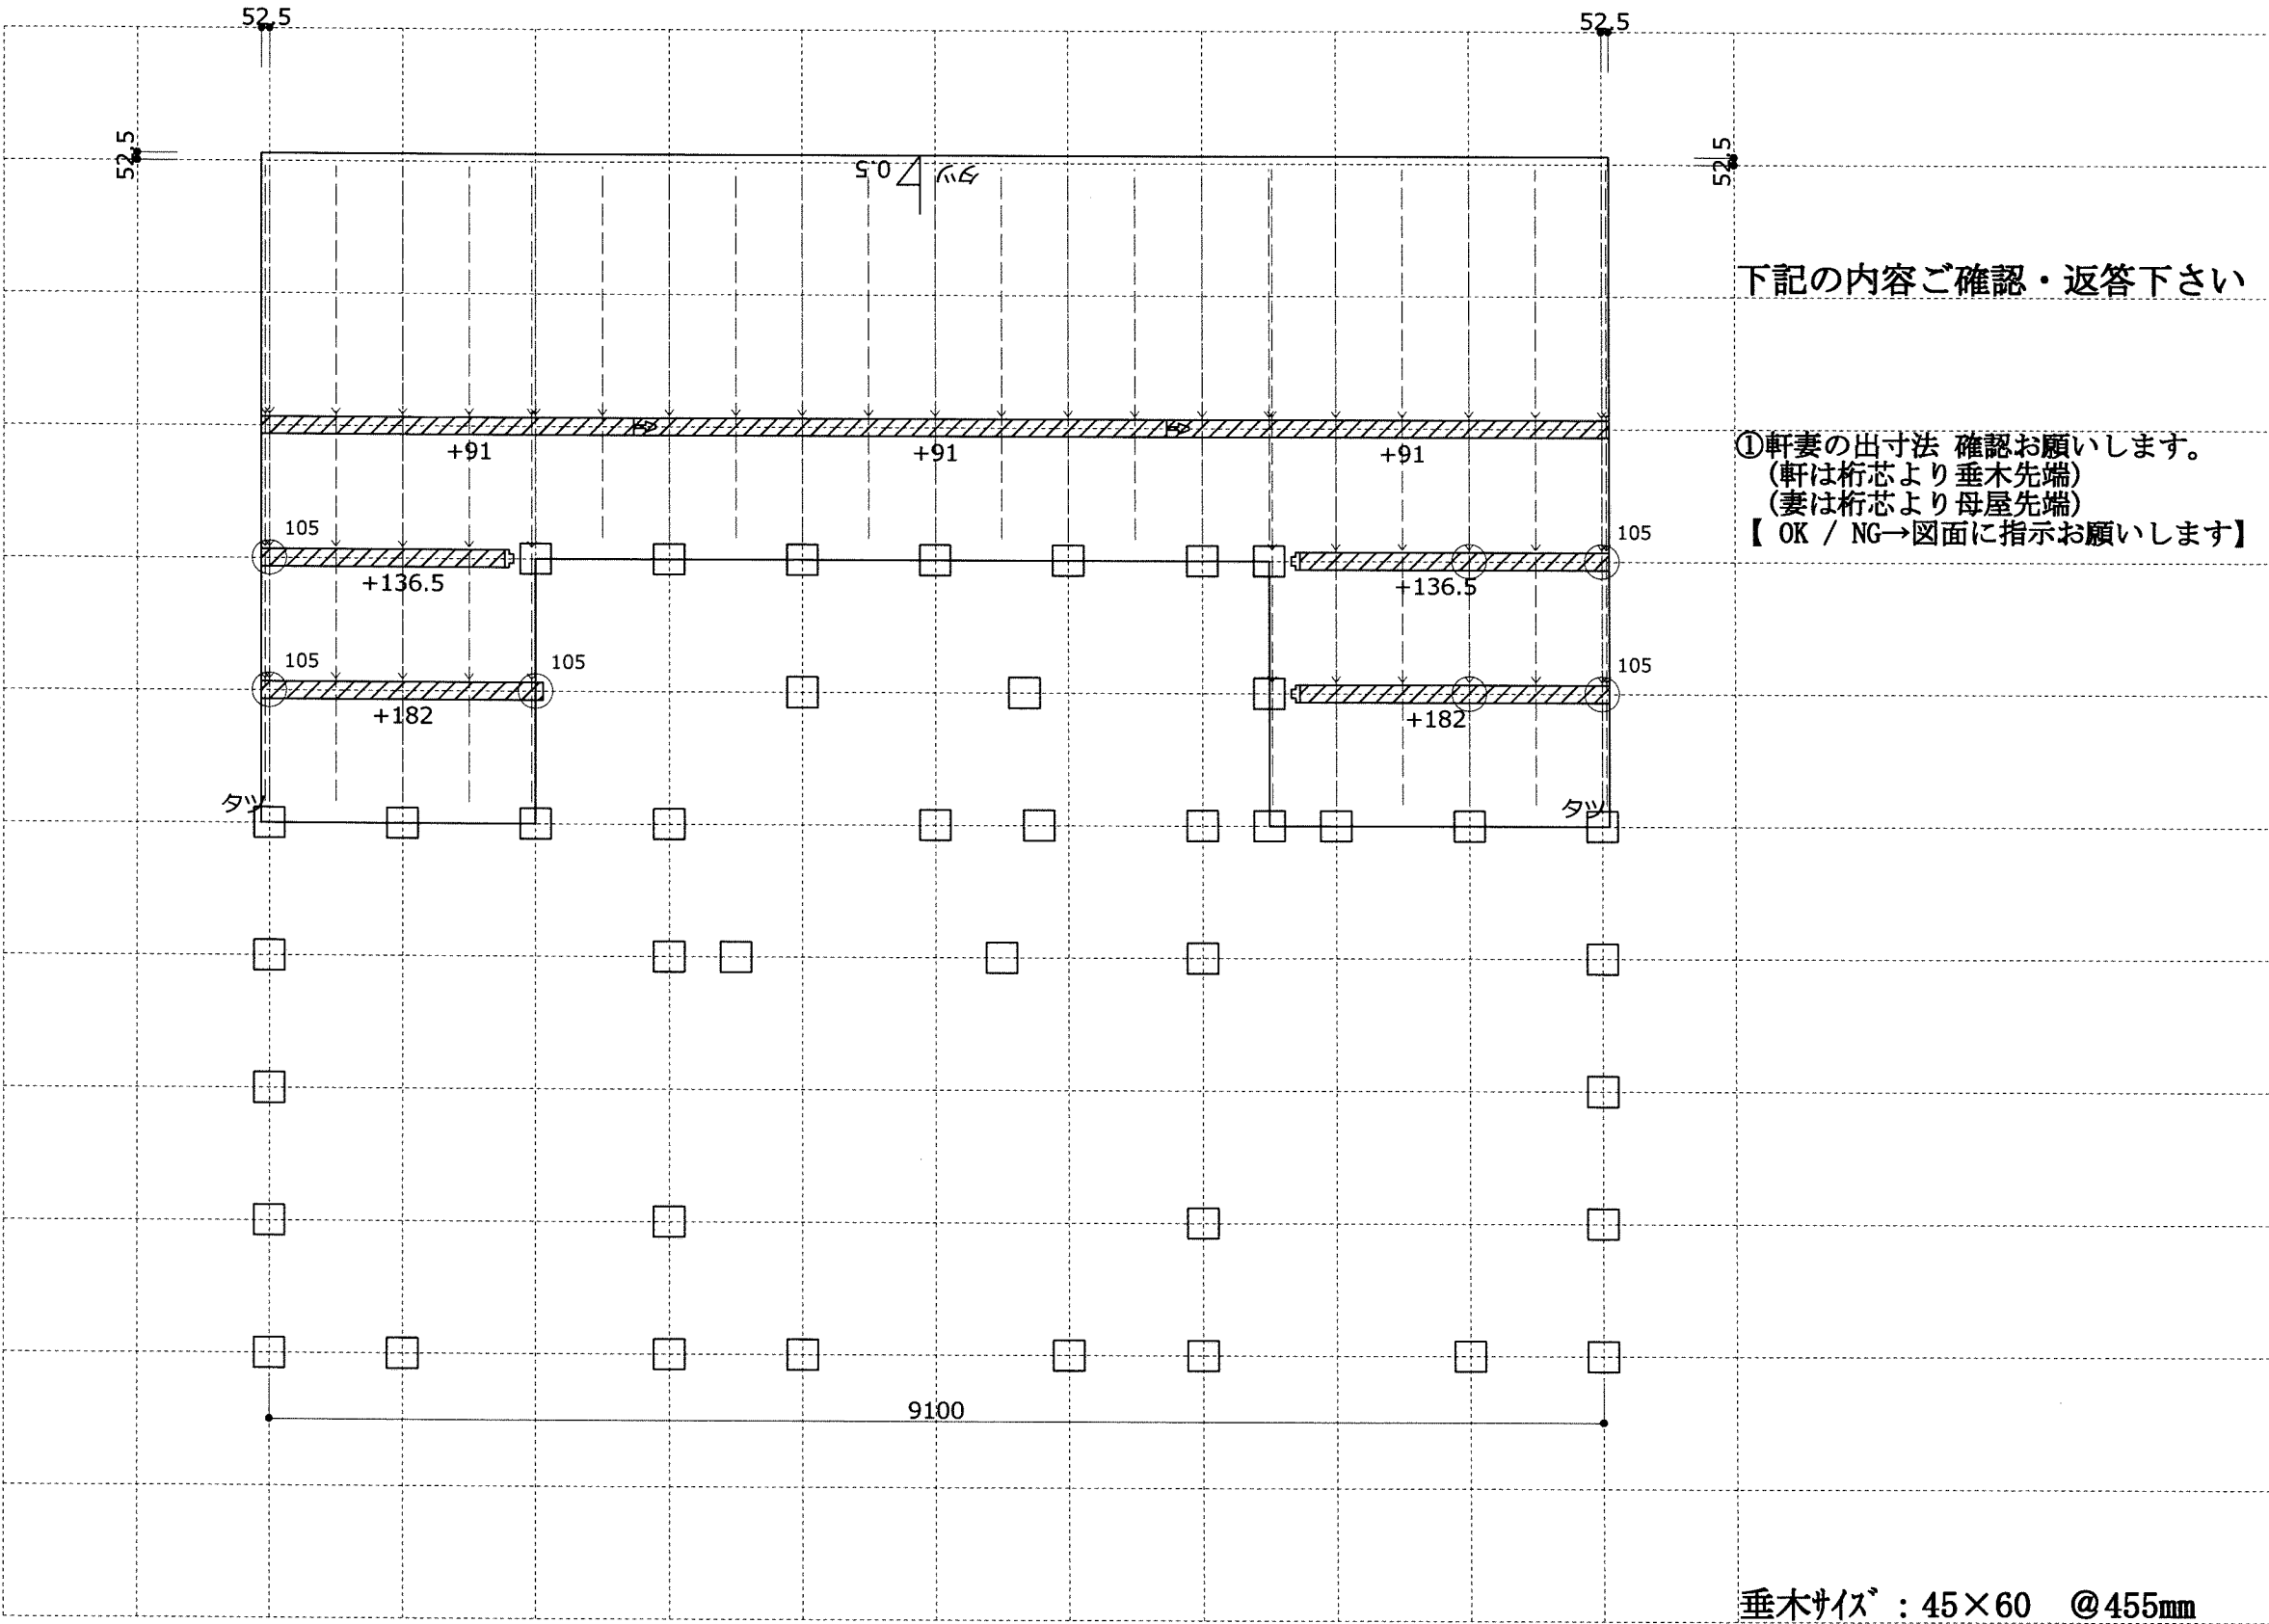

下記の内容ご確認・返答下さい

①軒妻の出寸法 確認お願いします。  
(軒は桁芯より垂木先端)  
(妻は桁芯より母屋先端)  
【 OK / NG→図面に指示お願いします】

垂木サイズ : 45×60 @455mm

凡 例

| 材 種 |       | 樹種・等級・材寸              |      |
|-----|-------|-----------------------|------|
|     | 檜     | 支給材<br>90×90          |      |
|     | 母 屋   |                       |      |
|     | 棟 木   | 支給材<br>105×105        |      |
|     |       |                       |      |
|     | 隅 木   | 米松<br>乾燥特等<br>90×90   |      |
|     | 谷 木   | 米松<br>乾燥特等<br>90×90   |      |
|     | 登 梁   | 米松<br>乾燥特等<br>105×105 |      |
|     |       |                       |      |
|     | 化粧管柱  |                       | 床 柱  |
|     | 階 段 柱 |                       | ポーチ柱 |
|     | 地 束   |                       | 吊 束  |
|     |       | 間 柱                   |      |
|     |       | 根 太                   |      |
|     |       | 蟻                     |      |
|     |       | 寄 蟻                   |      |
|     |       | 逆 蟻                   |      |
|     |       | 大入れ                   |      |
|     |       | 大引き                   |      |
|     |       | 兜                     |      |
|     |       | 茶 臼                   |      |
|     |       | 鎌 継                   |      |
|     |       | 蟻 継                   |      |
|     |       | 桁差ホゾ                  |      |
|     |       | 胴差ホゾ                  |      |

ハイテック CADセンター 浜松CAD室

434-0004

静岡県浜松市浜名区宮口2461

TEL :053-582-3711

FAX :053-582-3701

■捺印

■モジュール 910 mm

■桁 高 2900 mm

■屋根勾配 0.5 寸

■工事名称

(株)LIFEFUND様 伊藤友章様邸

■印刷日時

2024年11月25日

■縮尺

1 / 50


■図面名称











1階母屋伏図

■物件番号


HHM0192

わ を る ん り ち と へ ほ に は ろ い 2

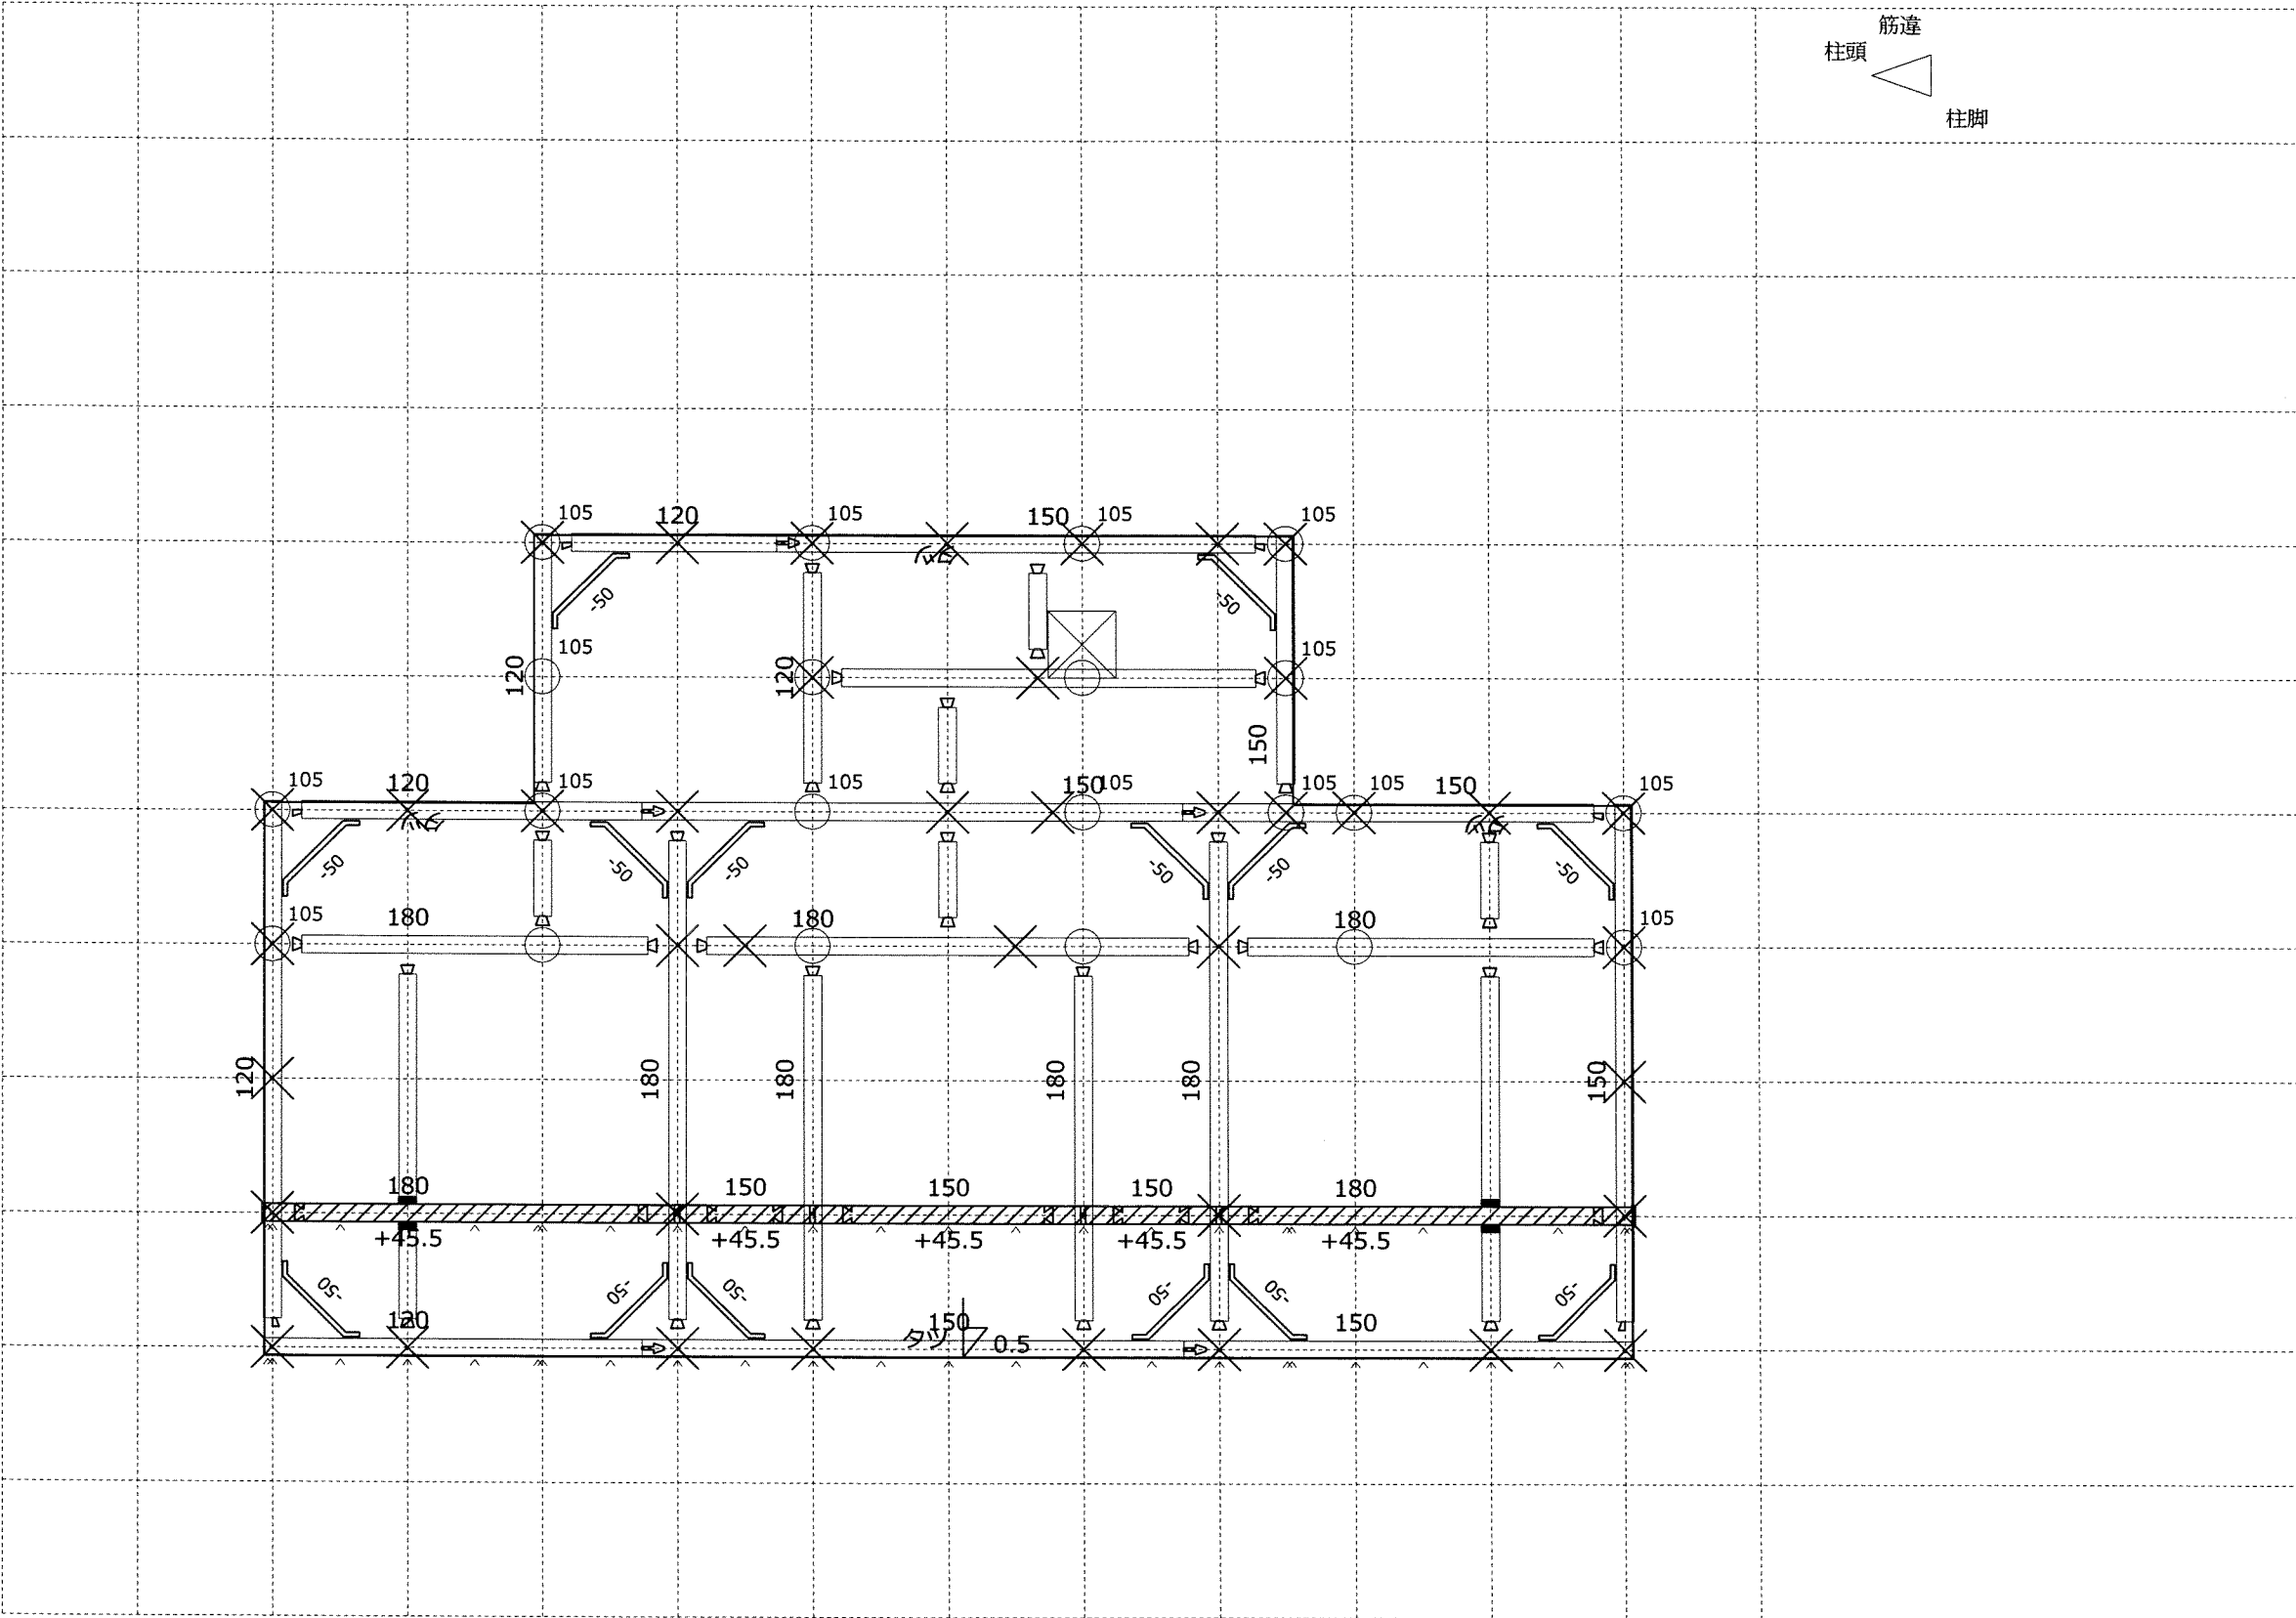
          
| 凡 例                                                                                   |       |                        |      |
|---------------------------------------------------------------------------------------|-------|------------------------|------|
| 材 種                                                                                   |       | 樹種・等級・材寸               |      |
| 梁                                                                                     |       | 米松<br>乾燥特等<br>105×105  |      |
| ○<br>小屋束                                                                              |       | 檜<br>支給材<br>90         |      |
| 火打梁                                                                                   |       | 鉄アングル<br>乾燥特等<br>90×90 |      |
| ⊠<br>登 梁                                                                              |       | 米松<br>乾燥特等<br>105×105  |      |
|                                                                                       |       |                        |      |
|                                                                                       |       |                        |      |
| ▧                                                                                     | 化粧管柱  | ▨                      | 床 柱  |
| ⊙                                                                                     | 階 段 柱 | ⊠                      | ポーチ柱 |
| □                                                                                     | 地 束   | ▣                      | 吊 束  |
|  |       | 間 柱                    |      |
|  |       | 根 太                    |      |
|  |       | 蟻                      |      |
|  |       | 寄 蟻                    |      |
|  |       | 逆 蟻                    |      |
|  |       | 大入れ                    |      |
|  |       | 大引き                    |      |
|  |       | 兜                      |      |
|  |       | 茶 臼                    |      |
|  |       | 鎌 継                    |      |
|  |       | 蟻 継                    |      |
|  |       | 桁差ホゾ                   |      |
|  |       | 胴差ホゾ                   |      |

わ を る ん り ち と へ ほ に は ろ い ズ

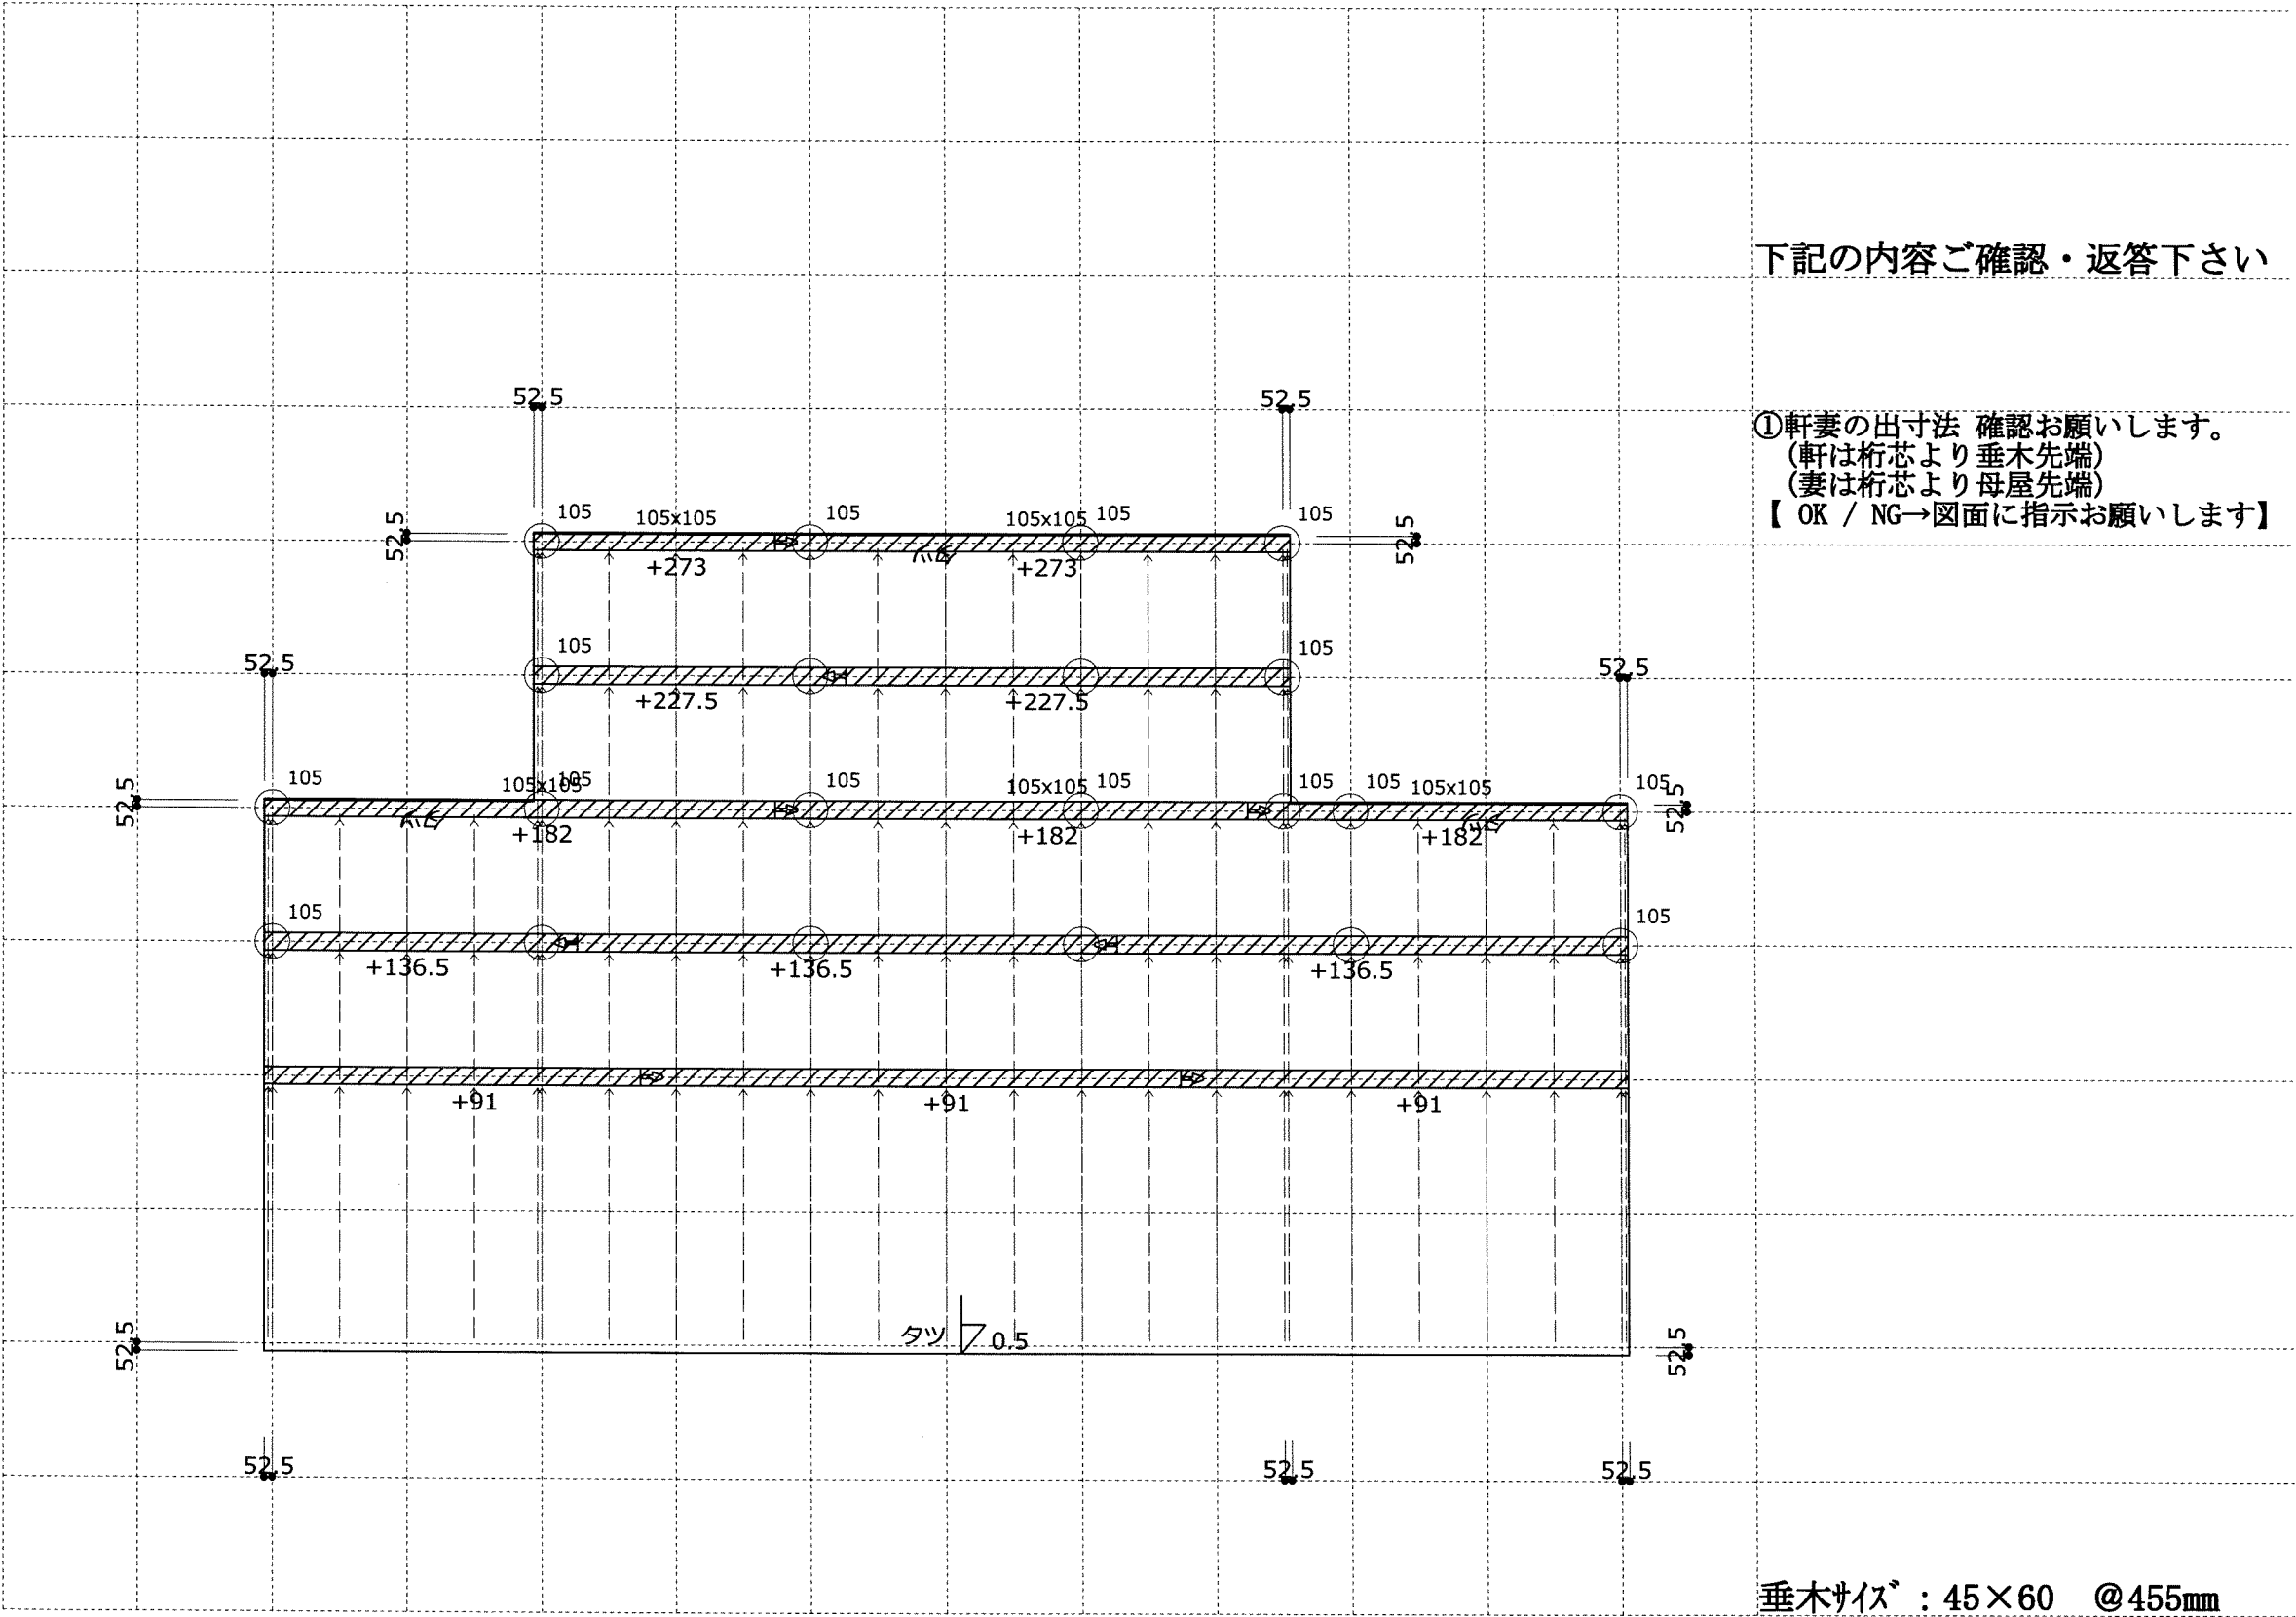

下記の内容ご確認・返答下さい

①軒妻の出寸法 確認お願いします。  
(軒は桁芯より垂木先端)  
(妻は桁芯より母屋先端)  
【 OK / NG→図面に指示お願いします】

垂木サイズ : 45×60 @455mm

凡 例

| 材 種 | 樹種・等級・材寸 |                 |  |
|-----|----------|-----------------|--|
| 母 屋 | 檜        | 支給材<br>90×90    |  |
| 棟 木 | 檜        | 支給材<br>105×105  |  |
| 隅 木 | 米松       | 乾燥特等<br>90×90   |  |
| 谷 木 | 米松       | 乾燥特等<br>90×90   |  |
| 登 梁 | 米松       | 乾燥特等<br>105×105 |  |
|     |          |                 |  |
|     | 化粧管柱     | 床 柱             |  |
|     | 階 段 柱    | ポーチ柱            |  |
|     | 地 束      | 吊 束             |  |
|     | 間 柱      |                 |  |
|     | 根 太      |                 |  |
|     | 蟻        |                 |  |
|     | 寄 蟻      |                 |  |
|     | 逆 蟻      |                 |  |
|     | 大入れ      |                 |  |
|     | 大引き      |                 |  |
|     | 兜        |                 |  |
|     | 茶 臼      |                 |  |
|     | 鎌 継      |                 |  |
|     | 蟻 継      |                 |  |
|     | 桁差ホソ     |                 |  |
|     | 胴差ホソ     |                 |  |

ハイック CADセンター 浜松CAD室

434-0004

静岡県浜松市浜名区宮口2461

TEL :053-582-3711

FAX :053-582-3701

■検印

■モジュール 910 mm

■桁 高 2800 mm

■屋根勾配 0.5 寸


■工事名称  
㈱LIFEFUND様 伊藤友章様邸

■印刷日時  
2024年11月25日

■縮尺  
1 / 50


■図面名称  
2階母屋伏図

■物件番号  
HHM0192

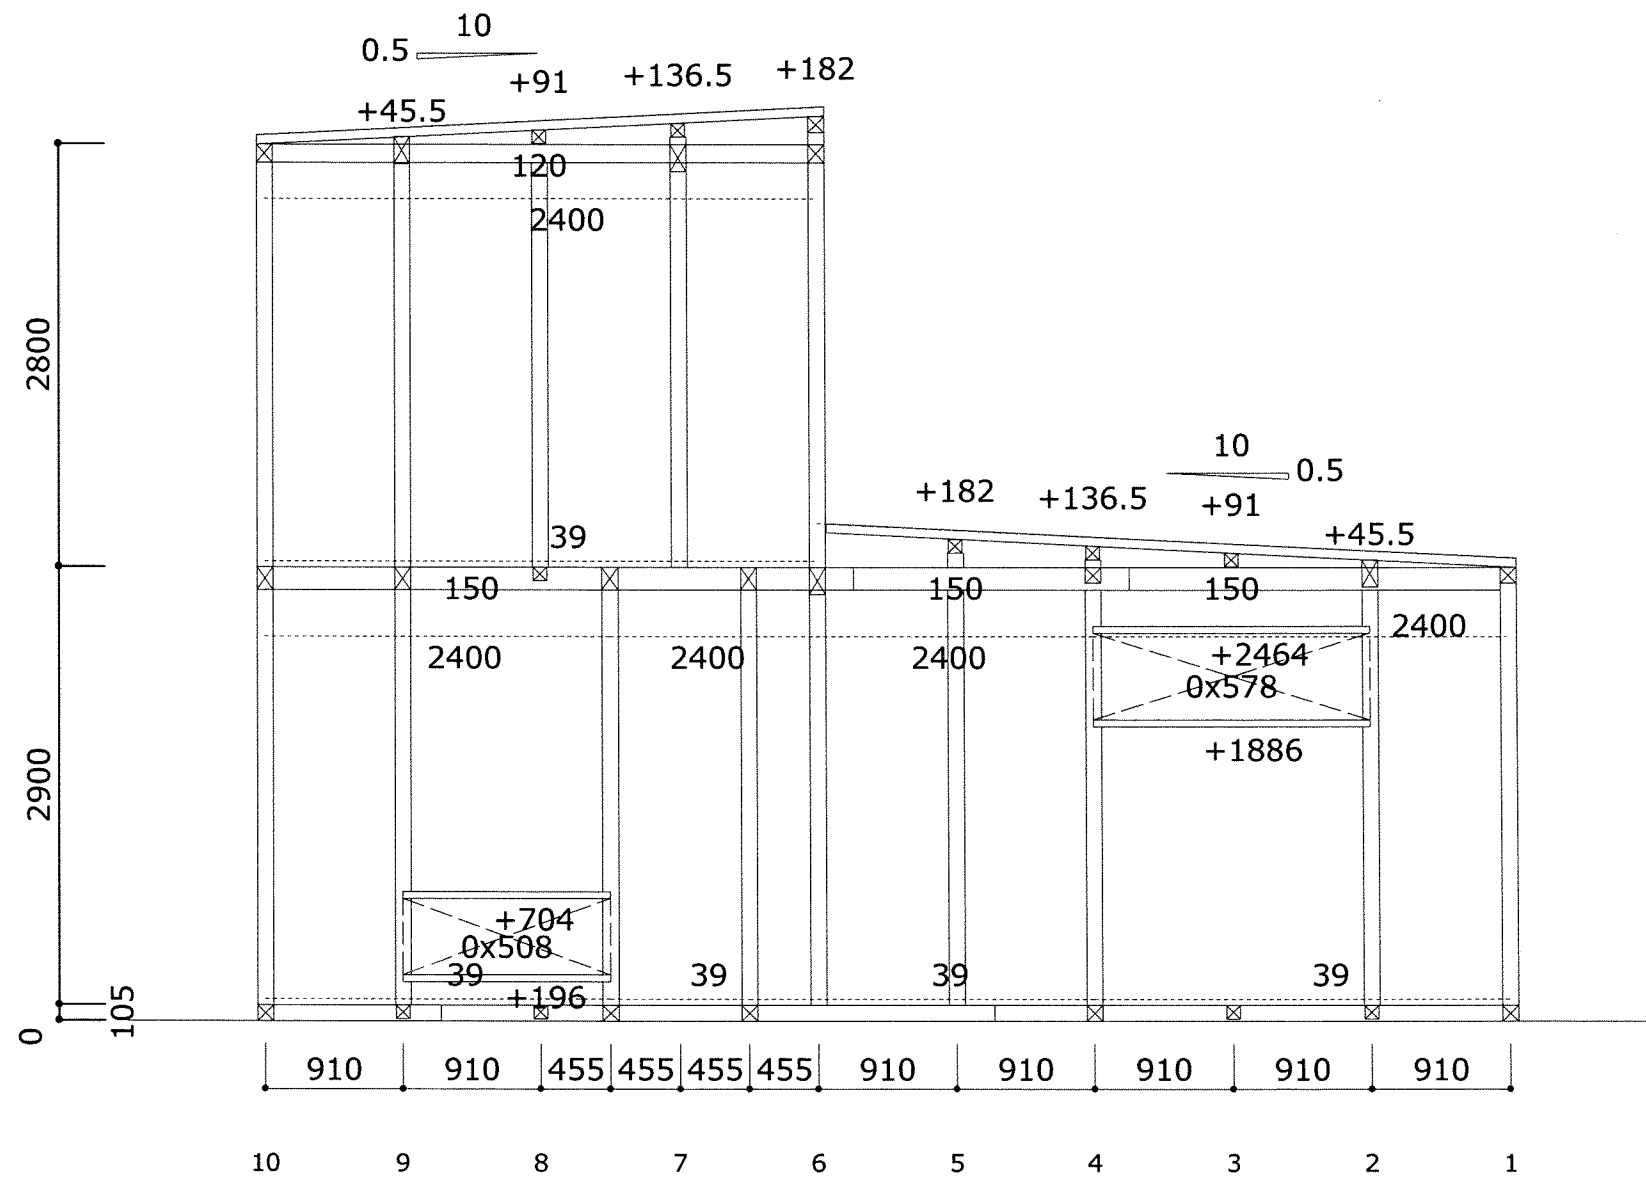

る通り 東面

|                     |  |  |                    |  |  |               |  |                         |  |             |  |               |  |
|---------------------|--|--|--------------------|--|--|---------------|--|-------------------------|--|-------------|--|---------------|--|
| ハイック CADセンター 浜松CAD室 |  |  | ■検印                |  |  | ■モジュール 910 mm |  | ■工事名称 ㈱LIFEFUND様 伊藤友章様邸 |  | ■図面名称 軸組断面図 |  |               |  |
| 434-0004            |  |  |                    |  |  | ■桁 高 mm       |  | ■印刷日時 2024年11月25日       |  | ■縮尺 1 / 50  |  | ■物件番号 HHM0192 |  |
| 静岡県浜松市浜名区宮口2461     |  |  |                    |  |  | ■屋根勾配 寸       |  |                         |  |             |  |               |  |
| TEL : 053-582-3711  |  |  | FAX : 053-582-3701 |  |  |               |  |                         |  |             |  |               |  |

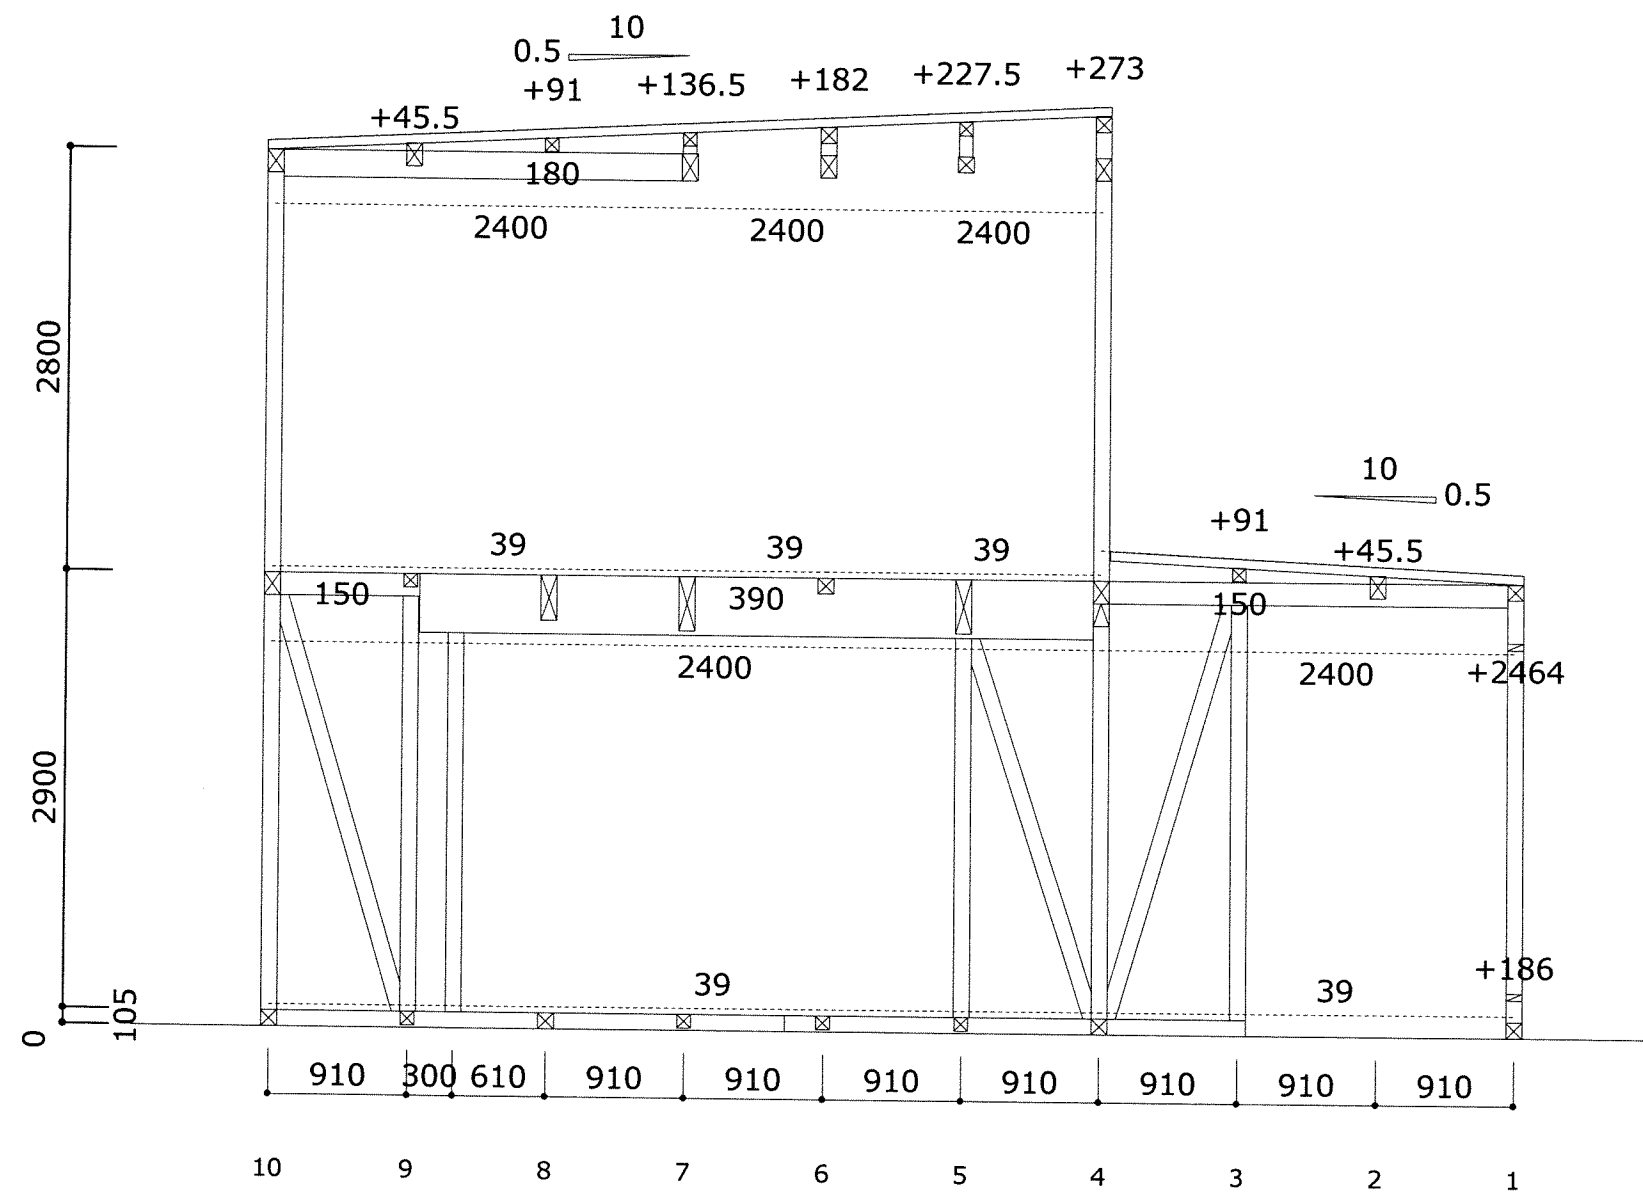

ほ通り 東面

ハイック CADセンター 浜松CAD室

434-0004

静岡県浜松市浜名区宮口2461

TEL : 053-582-3711

FAX : 053-582-3701

■検印

■モジュール 910 mm

■桁高 mm

■屋根勾配 寸

■工事名称

(株)LIFEFUND様 伊藤友章様邸

■印刷日時

2024年11月25日

■縮尺


1 / 50

■図面名称


軸組断面図

■物件番号

HHM0192

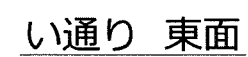


|                                                            |  |                                          |      |                                        |                                                        |                |                                      |
|------------------------------------------------------------|--|------------------------------------------|------|----------------------------------------|--------------------------------------------------------|----------------|--------------------------------------|
| <b>ハイテック CADセンター 浜松CAD室</b><br>434-0004<br>静岡県浜松市浜名区宮口2461 |  | TEL : 053-582-3711<br>FAX : 053-582-3701 | ■ 検印 | ■ モジュール 910 mm<br>■ 桁 高 mm<br>■ 屋根勾配 寸 | ■ 工事名称<br>(株)LIFEFUND様 伊藤友章様邸<br>■ 印刷日時<br>2024年11月25日 | ■ 縮尺<br>1 / 50 | ■ 図面名称<br>軸組断面図<br>■ 物件番号<br>HHM0192 |
|------------------------------------------------------------|--|------------------------------------------|------|----------------------------------------|--------------------------------------------------------|----------------|--------------------------------------|

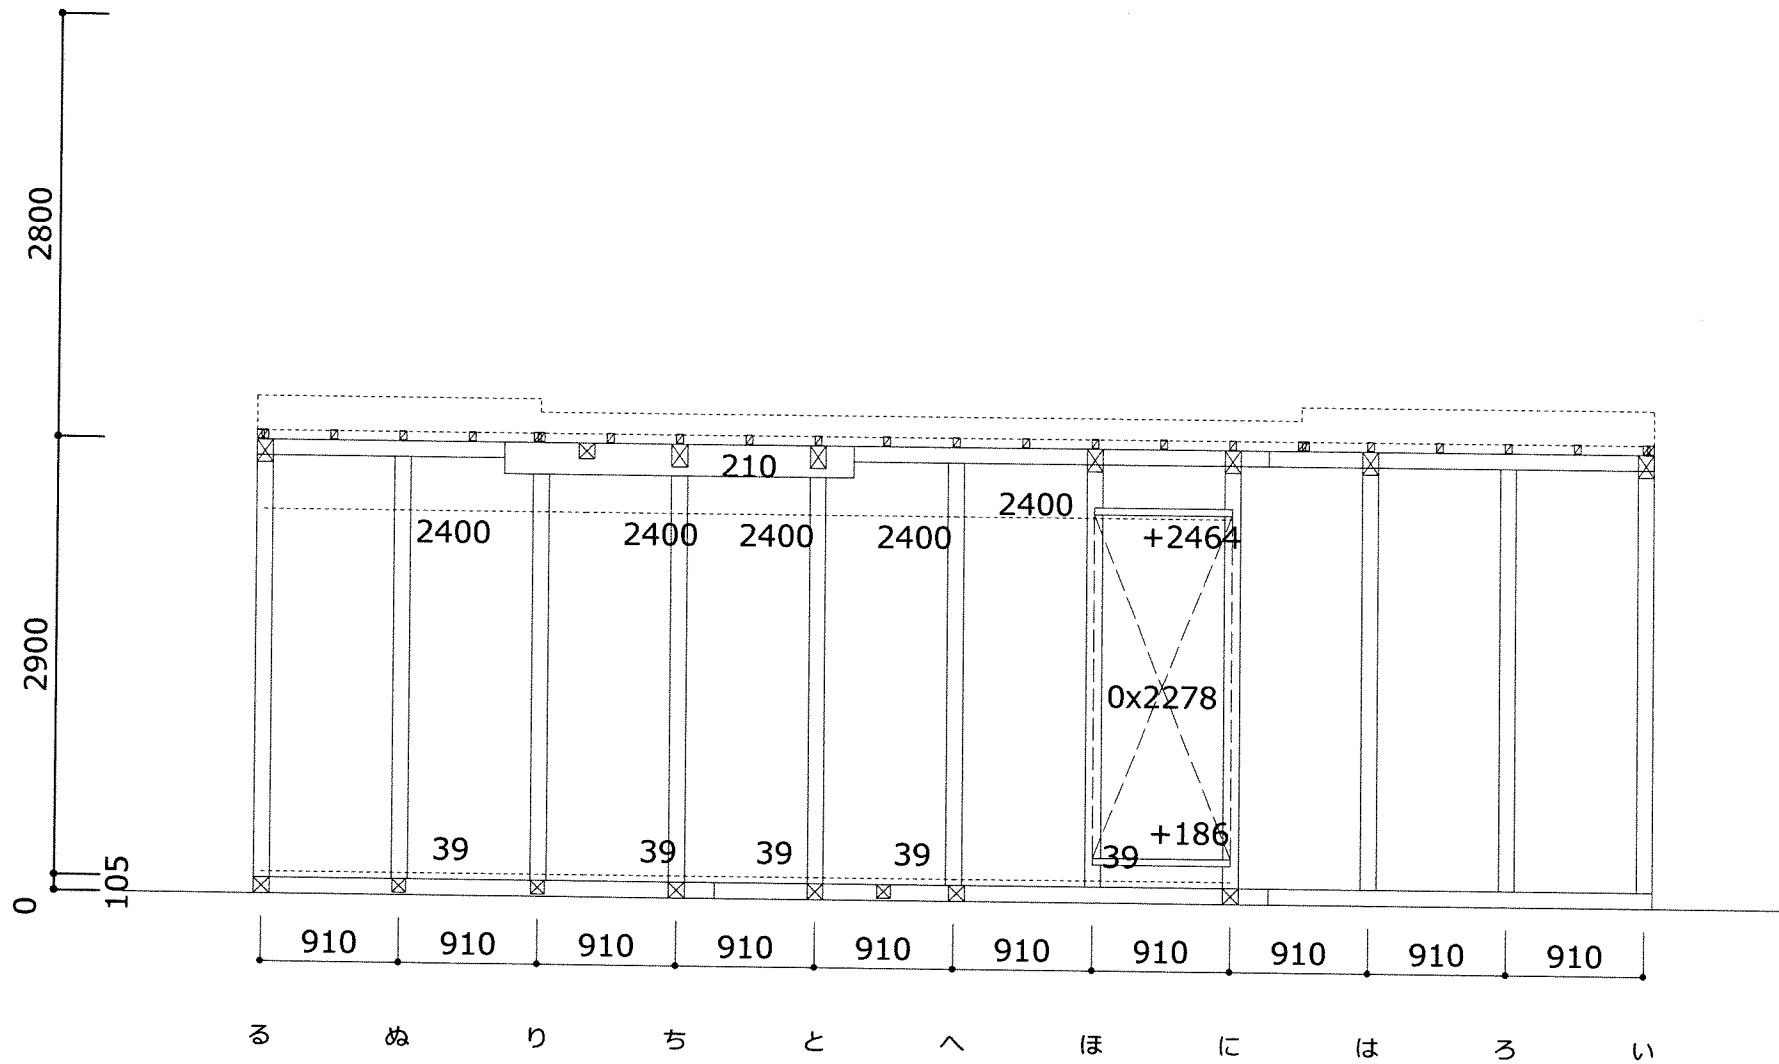


1通り 南面

|                                       |  |  |     |  |  |             |  |                              |  |                      |  |               |  |
|---------------------------------------|--|--|-----|--|--|-------------|--|------------------------------|--|----------------------|--|---------------|--|
| ハイック CADセンター 浜松CAD室                   |  |  | ■検印 |  |  | ■モデル 910 mm |  | ■工事名称<br>(株)LIFEFUND様 伊藤友章様邸 |  | ■図面名称                |  |               |  |
| 434-0004                              |  |  |     |  |  | ■桁 高 mm     |  |                              |  | ■印刷日時<br>2024年11月25日 |  | ■縮尺<br>1 / 50 |  |
| 静岡県浜松市浜名区宮口2461                       |  |  |     |  |  | ■屋根勾配 寸     |  | HHM0192                      |  |                      |  |               |  |
| TEL : 053-582-3711 FAX : 053-582-3701 |  |  |     |  |  |             |  |                              |  |                      |  |               |  |

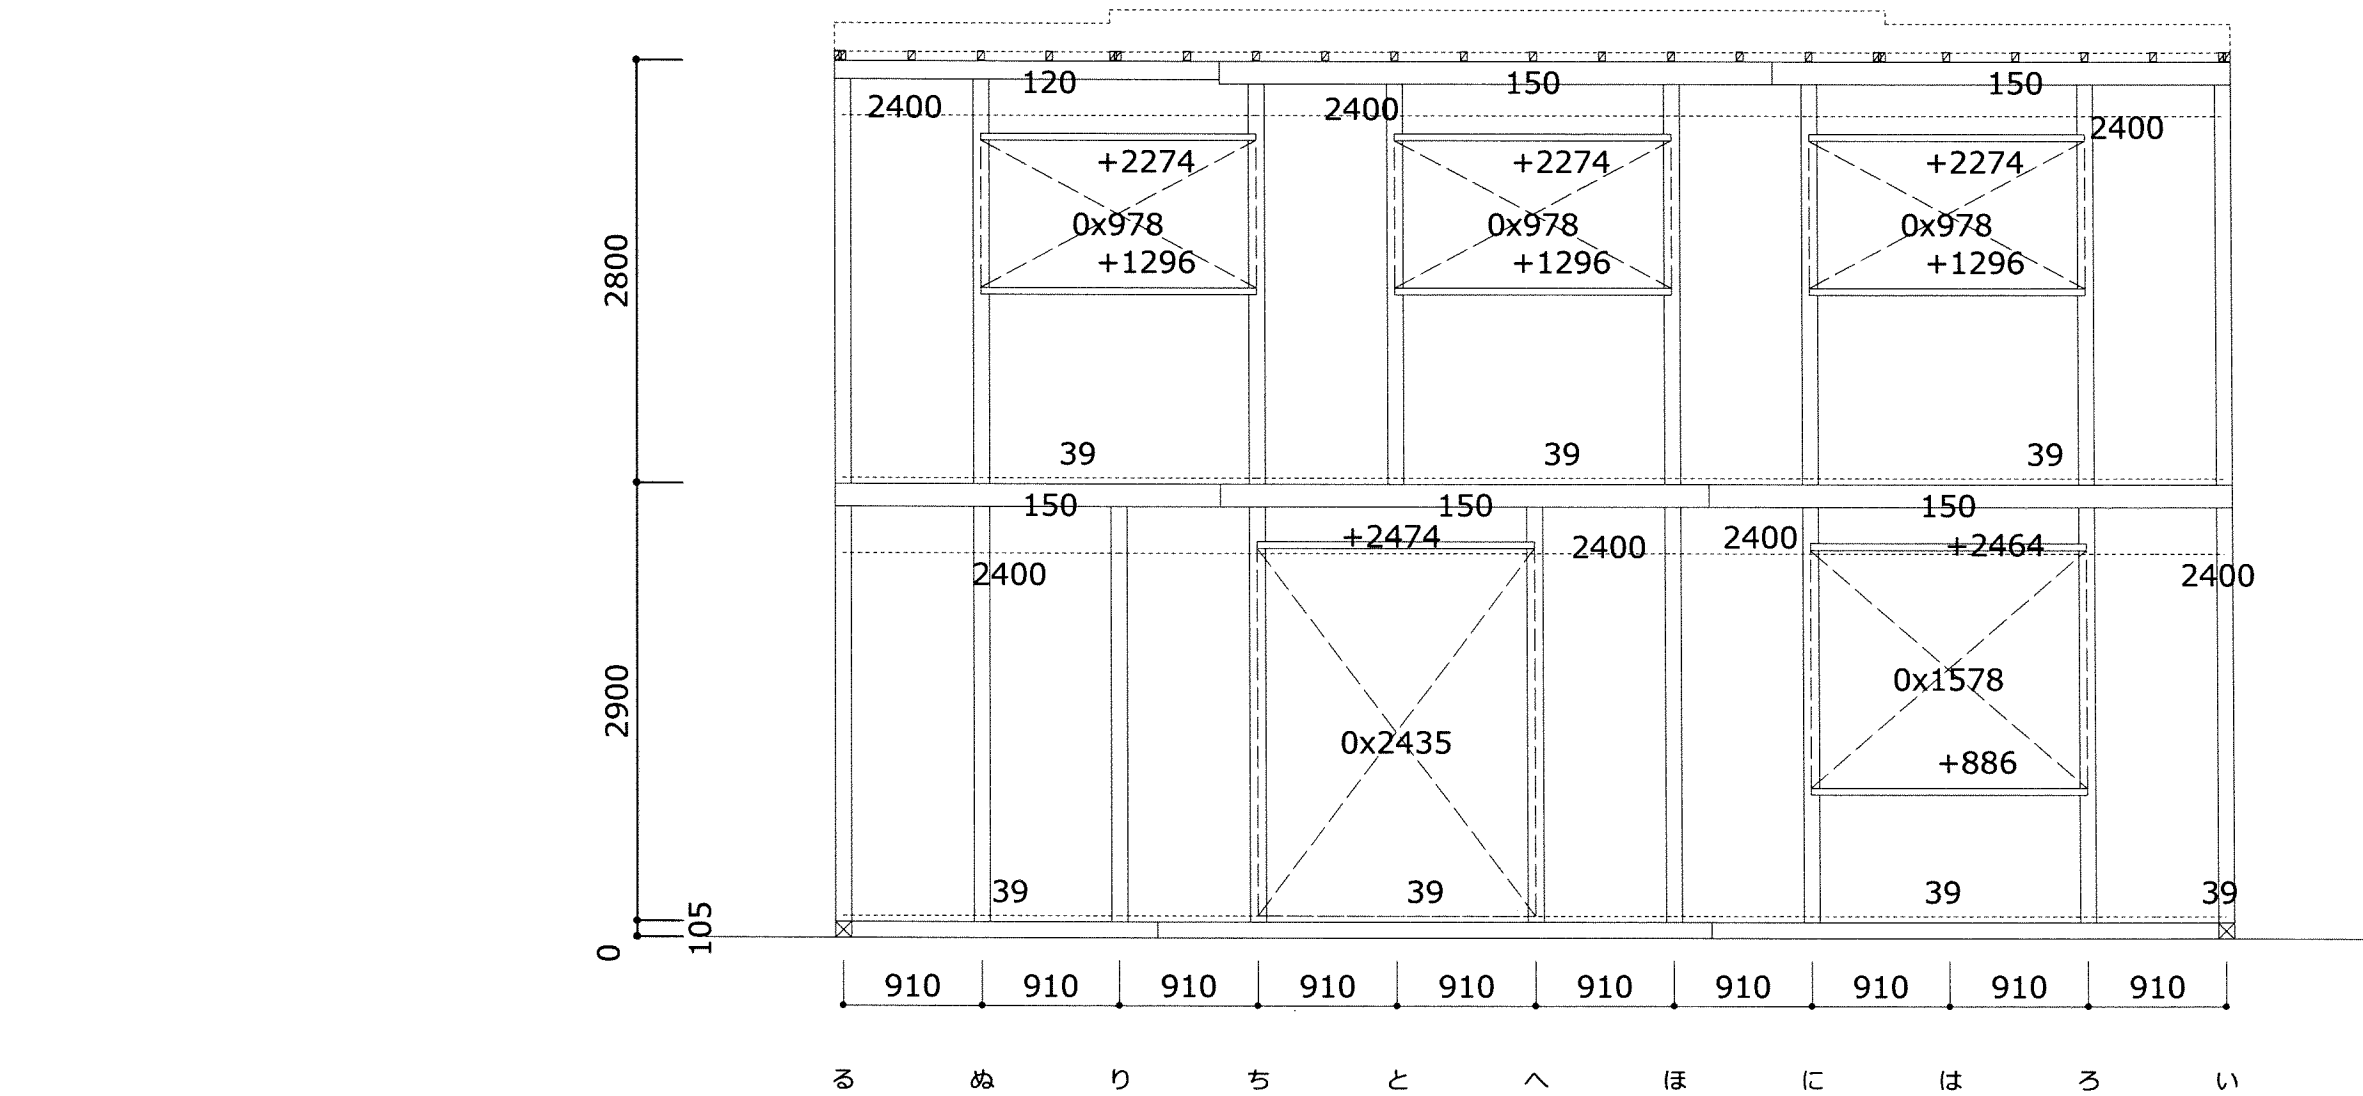

10通り 南面

|                                       |  |  |     |  |  |               |  |                           |  |             |  |            |  |
|---------------------------------------|--|--|-----|--|--|---------------|--|---------------------------|--|-------------|--|------------|--|
| ハビック CADセンター 浜松CAD室                   |  |  | ■検印 |  |  | ■モジュール 910 mm |  | ■工事名称 (株)LIFEFUND様 伊藤友章様邸 |  | ■図面名称 軸組断面図 |  |            |  |
| 434-0004                              |  |  |     |  |  | ■桁 高 mm       |  |                           |  | ■印刷日時       |  | ■縮尺 1 / 50 |  |
| 静岡県浜松市浜名区宮口2461                       |  |  |     |  |  | ■屋根勾配 寸       |  | 2024年11月25日               |  |             |  |            |  |
| TEL : 053-582-3711 FAX : 053-582-3701 |  |  |     |  |  |               |  |                           |  |             |  |            |  |

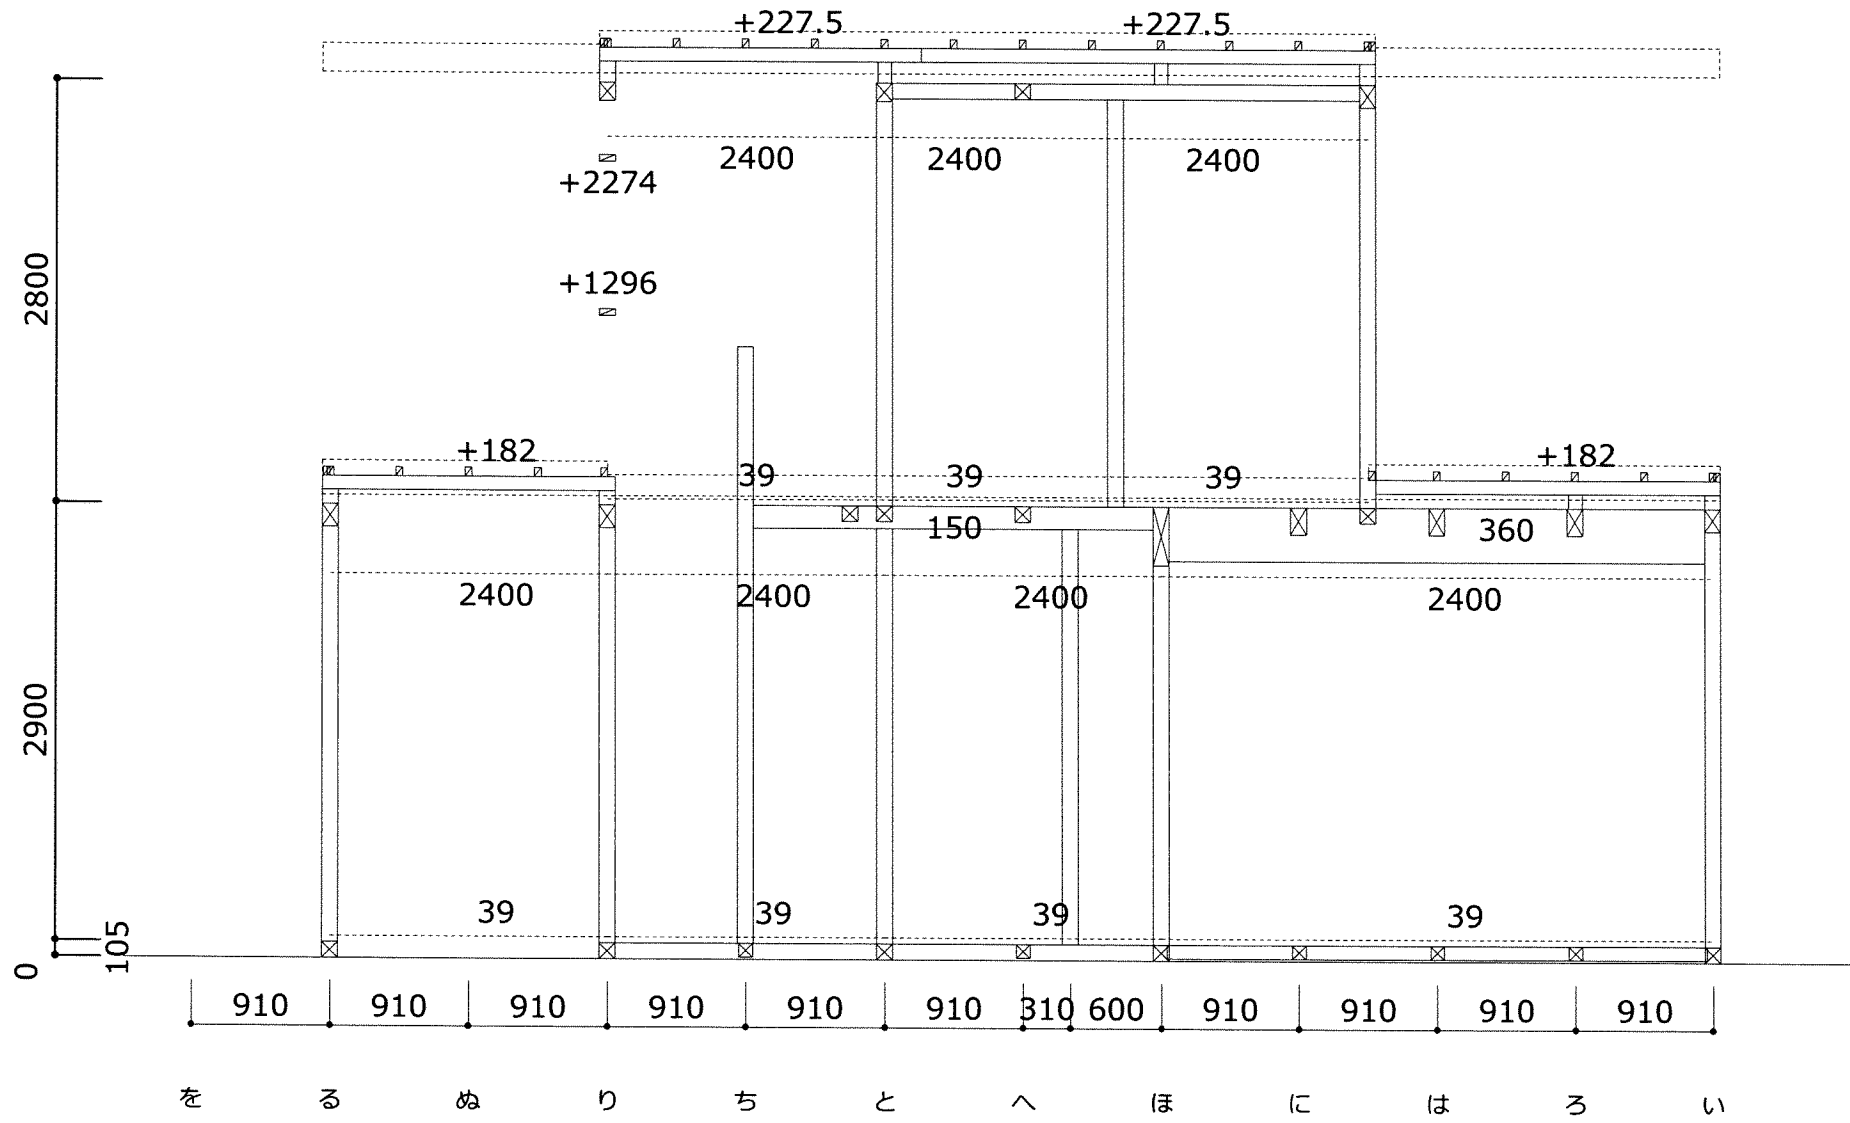

5通り 南面

|                     |  |                    |     |  |  |               |  |                     |  |         |  |       |  |
|---------------------|--|--------------------|-----|--|--|---------------|--|---------------------|--|---------|--|-------|--|
| ハイック CADセンター 浜松CAD室 |  |                    | ■検印 |  |  | ■モジュール 910 mm |  | ■工事名称               |  | ■図面名称   |  |       |  |
| 434-0004            |  |                    |     |  |  | ■桁 高 mm       |  | (株)LIFEFUND様 伊藤友章様邸 |  | 軸組断面図   |  |       |  |
| 静岡県浜松市浜名区宮口2461     |  |                    |     |  |  | ■屋根勾配 寸       |  | ■印刷日時               |  | ■縮尺     |  | ■物件番号 |  |
| TEL : 053-582-3711  |  | FAX : 053-582-3701 |     |  |  | 2024年11月25日   |  | 1 / 50              |  | HHM0192 |  |       |  |