



加工承認書

2024年10月29日

拝啓 貴社益々ご繁栄のこととお慶び申し上げます。平素は、格別のご配慮をいただき厚くお礼申し上げます。
さて、この度貴社よりご依頼のありましたプレカッ図面を送付致します。
つきましては、送付図面の内容確認及び加工のご承認を本紙にて、ご回答を頂きますようお願い申し上げます。

ハイビック(株) CADセンター

発 注 (株)LIFEFUND 御 中
担 当 者 ご担当者 様
物 件 名 伊藤友章 様邸
FAX

浜松CAD室 担当:鈴木淳
携帯 070-3173-7584

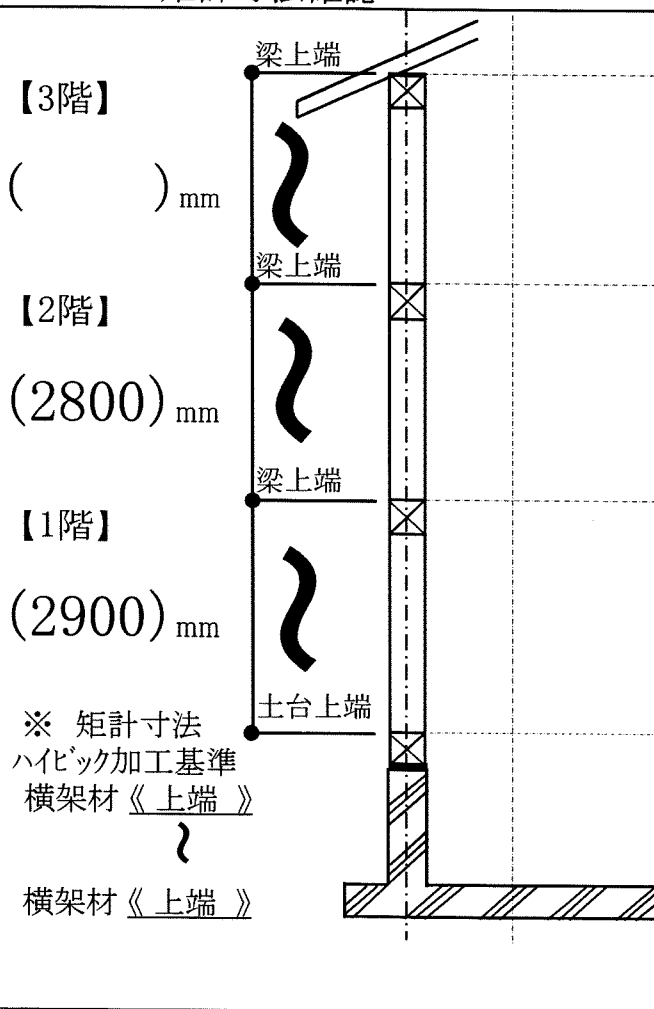
浜松市浜名区宮 口2461 TEL 053-582-3711
FAX 053-582-3701

プレカッ販売店:浜松店 営業担当:大久保

■伏図確認進捗状況

第1回送信日 10/29 枚送信	1 便 目	上 棟 日
お世話になっております。 プレカッ伏図を作成致しました。 御確認宜しくお願い致します。	1/6	
第2回送信日 / 枚送信	1 便 目	上 棟 日
第3回送信日 / 枚送信	1 便 目	上 棟 日
第4回送信日 / 枚送信	1 便 目	上 棟 日
第5回送信日 / 枚送信	1 便 目	上 棟 日
第6回送信日 / 枚送信	1 便 目	上 棟 日
第7回送信日 / 枚送信	1 便 目	上 棟 日

■矩計寸法確認



承認期限

月 日

※承認期限までにご承認お願い致します。

※ 月 日送付の図面一式にて、加工承認する。

- ・ ご承認を頂いた後は工場の生産工程に合わせ、随時加工に入らせて頂きます。
- ・ ご承認後の変更は内容によって有料となる場合がありますのでご了承願います。
- ・ 化粧材について、松系の材料にはブルーステインの混入の可能性が御座います。

加工承認日 (※承認期限までにご承認お願い致します。)

※ 年 月 日 ※承認者名

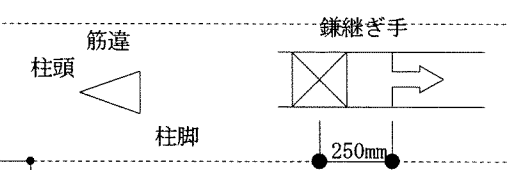
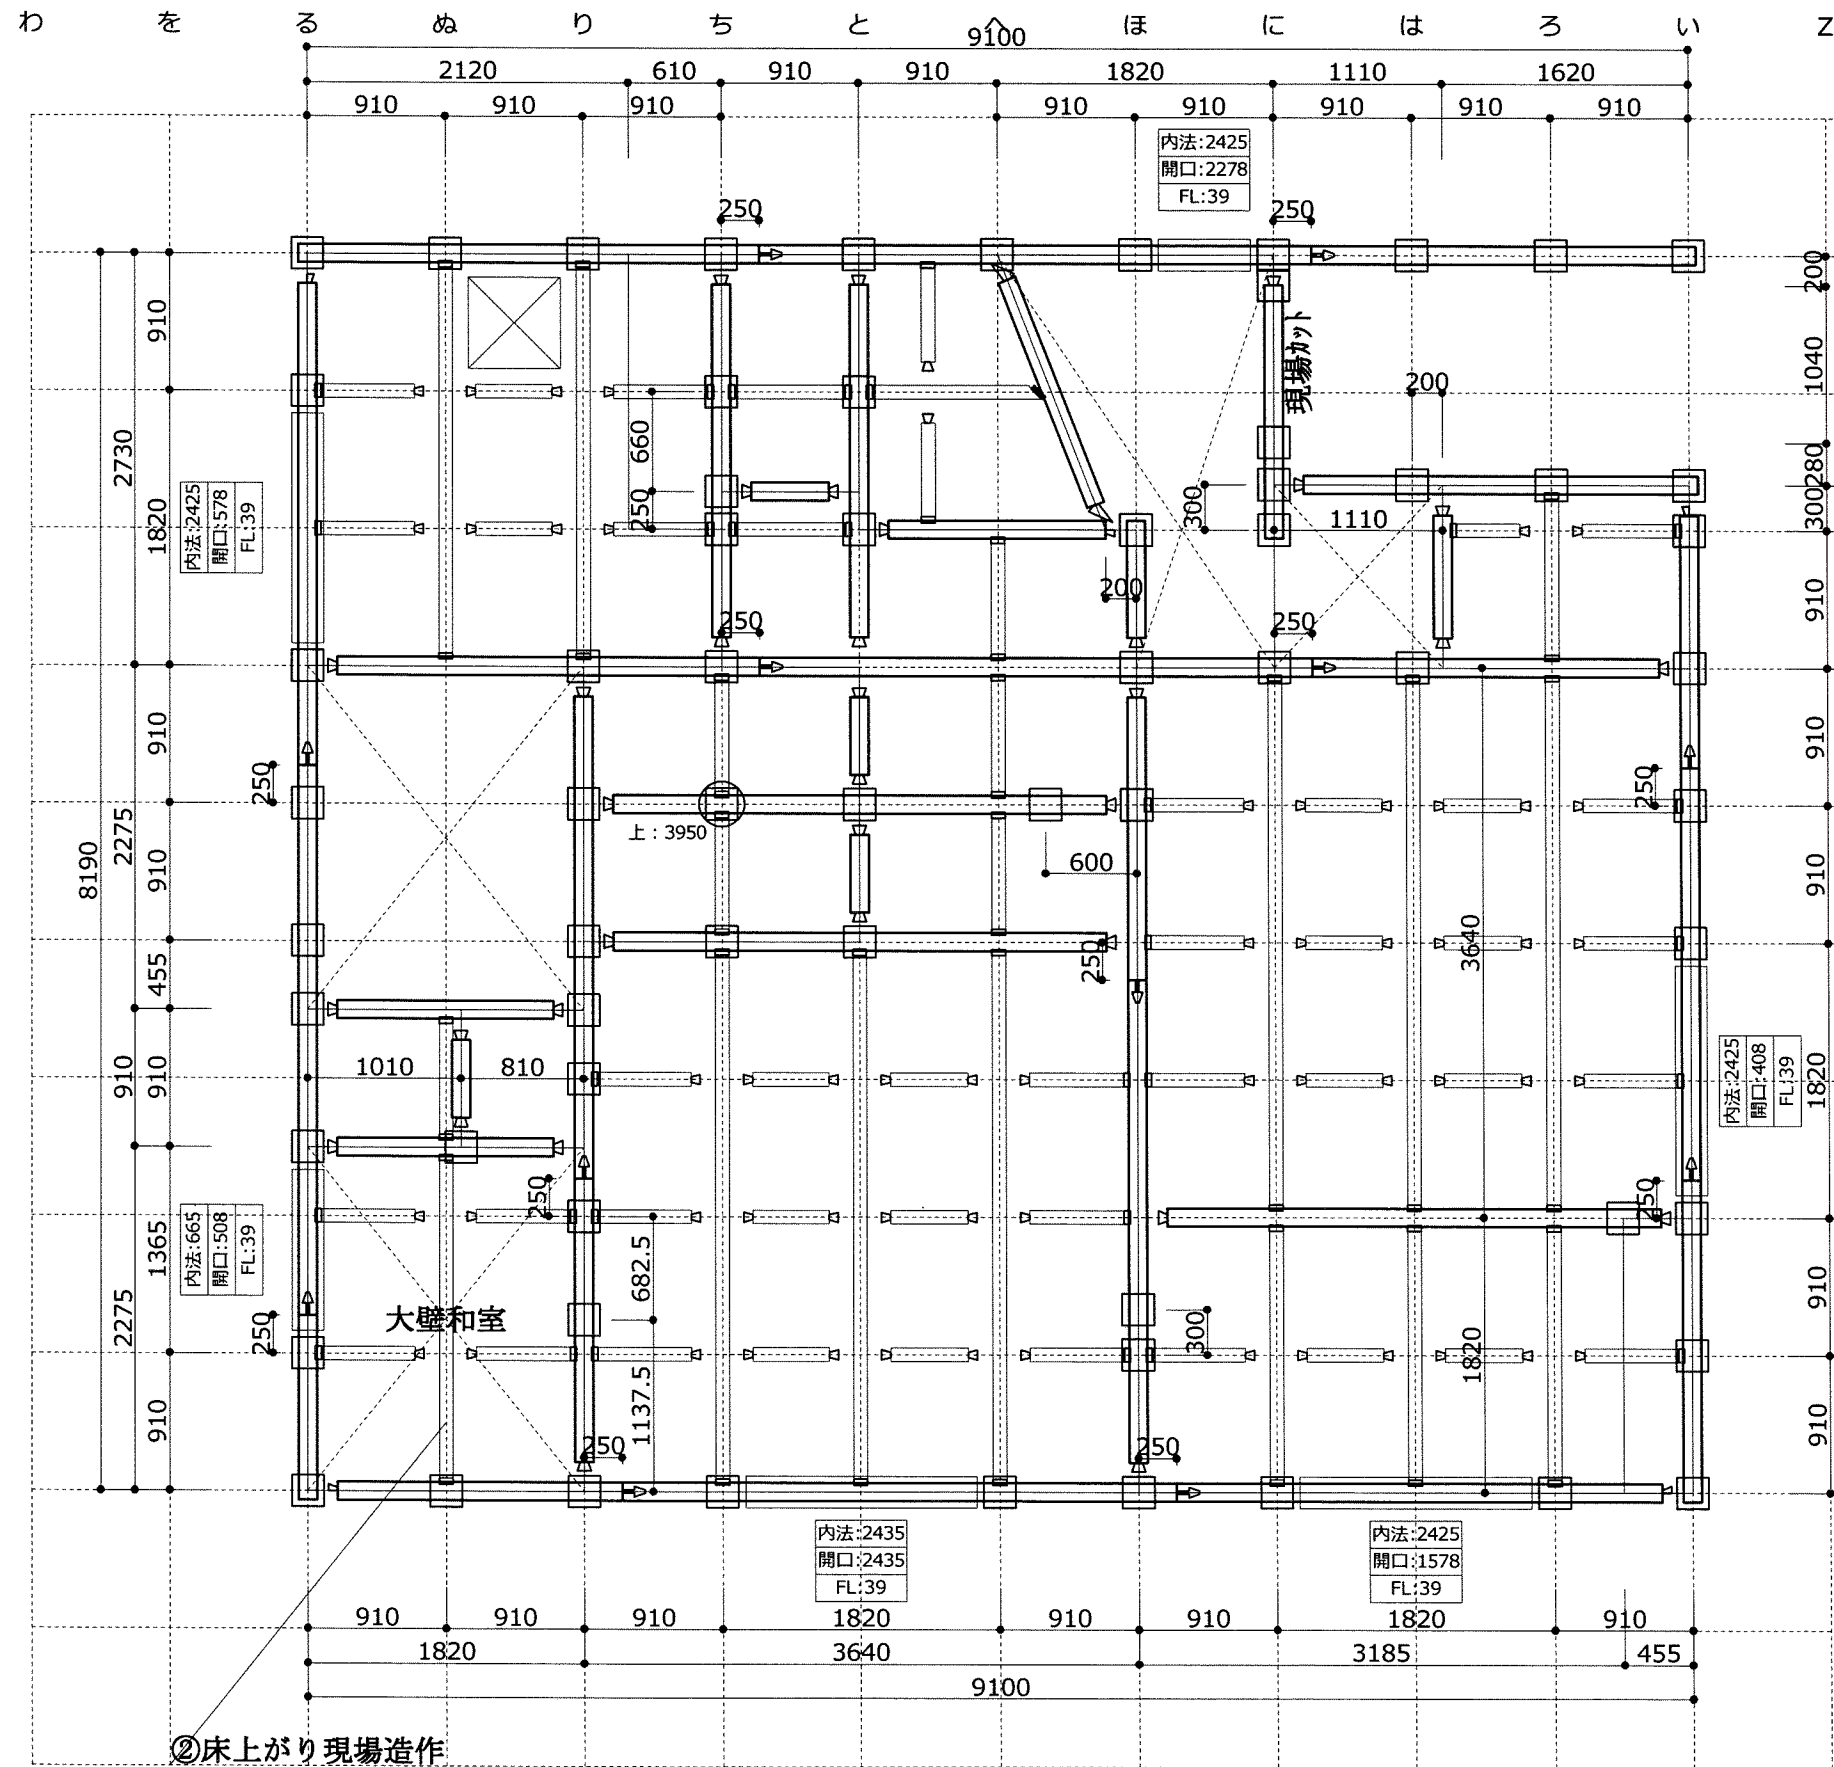
様

※

印

※部分は必ずご記入下さい(電子印はご遠慮願います様ご協力下さい)

2017.6.12改訂



下記の内容ご確認・返答下さい

- ①土台位置、継手位置 確認をお願いします。
【OK / NG→図面に指示をお願いします】
- ②大壁和室床上がり現場造作で
宜しいですか？
【OK / NG→図面に指示をお願いします】
- ③窓台・マダサ 高さ確認をお願いします。
【OK / NG→図面に指示をお願いします】

凡 例			
材 種	樹種・等級・材寸		
土 台	檜		
	支給材	105×105	
大 引	檜		
	支給材	90×90	
	杉集成		
	構造用	105	
	杉集成		
	構造用	105	
火打土台	防腐防蟻処理		
	特等	90×45	
	化粧管柱		床 柱
	階段柱		ポーチ柱
	地 束		吊 束
間 柱			
根 太			
	蟻		
	寄 蟻		
	逆 蟻		
	大入れ		
	大引き		
	兜		
	茶 臼		
	鎌 継		
	蟻 継		
	桁差ホゾ		
	胴差ホゾ		

ハビック CADセンター 浜松CAD室
434-0004
静岡県浜松市浜名区宮口2461

TEL .053-582-3711 FAX .053-582-3701

■検印


■モジュール	910	mm
■桁 高	2900	mm
■屋根勾配	0.5	寸

■工事名称
(株)LIFEFUND様 伊藤友章様邸
■印刷日時
2024年10月29日

■縮尺
1 / 50

■図面名称
土台伏図
■物件番号
HHM0192

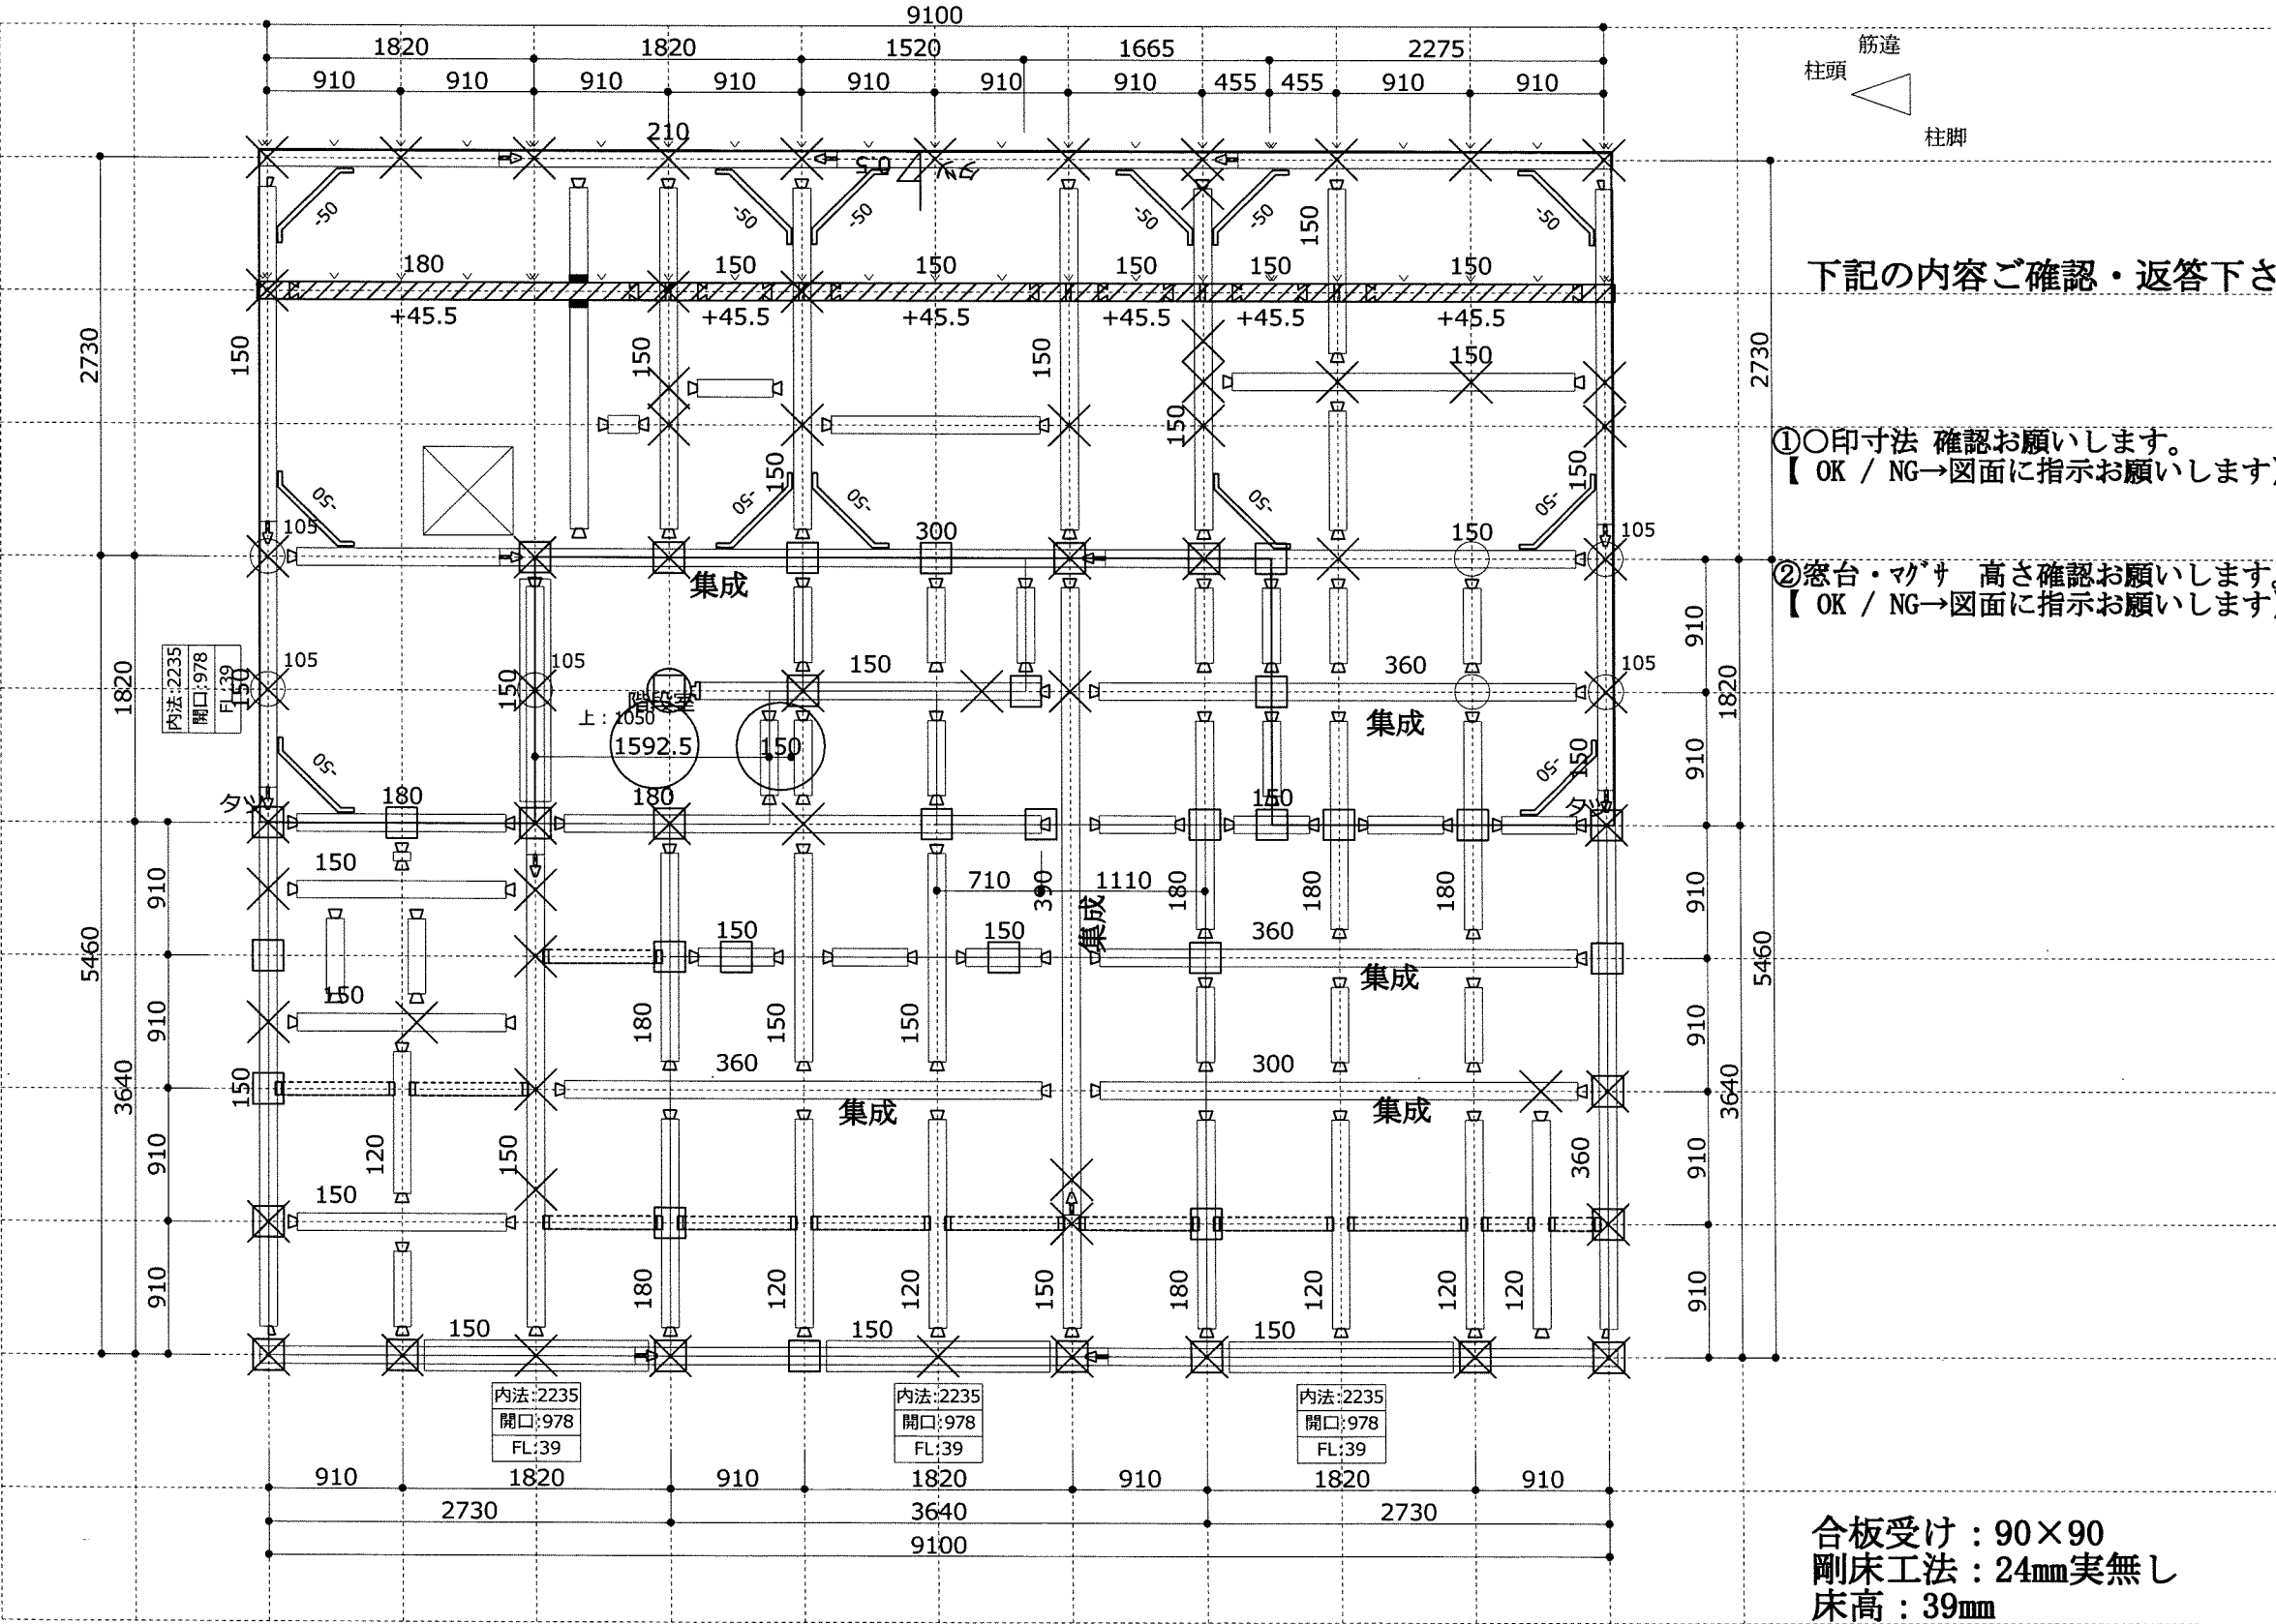わ を る ん り ち と へ ほ に は ろ い Z



下記の内容ご確認・返答下さい

①○印寸法 確認お願いします。
【OK / NG→図面に指示お願いします】

②窓台・マガサ 高さ確認お願いします。
【OK / NG→図面に指示お願いします】

凡 例	
材 種	樹種・等級・材寸
梁	米松 乾燥特等 105×105
通し柱	杉集成 構造用 105
管 柱	杉集成 構造用 105
小屋束	檜 支給材 90
火打梁	鉄アングル 乾燥特等 90×90
登 梁	米松 乾燥特等 105×105
化粧管柱	床 柱
階 段 柱	ポーチ柱
地 束	吊 束
間 柱	
根 太	
蟻	
寄 蟻	
逆 蟻	
大入れ	
大引き	
兜	
茶 臼	
鎌 継	
蟻 継	
桁差ホゾ	
胴差ホゾ	

ハビック CADセンター 浜松CAD室

434-0004

静岡県浜松市浜名区宮口2461

TEL :053-582-3711

FAX :053-582-3701

検印

■モジュール 910 mm
■桁 高 2800 mm
■屋根勾配 0.5 寸

■工事名称
(株)LIFEFUND様 伊藤友章様邸

■印刷日時
2024年10月29日

■縮尺
1 / 50

■図面名称
2階床伏図

■物件番号
HHM0192

52.5 52.5 52.5 52.5

9100

91 +136.5 +182

105 105 105 105

 
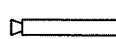
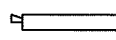
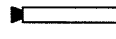
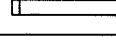
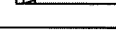
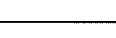
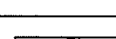
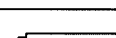
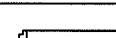
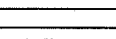
タツ

①軒妻の出寸法 確認をお願いします。
(軒は桁芯より垂木先端)
(妻は桁芯より母屋先端)
【 OK / NG→図面に指示をお願いします】


垂木サイズ : 45×60 @455mm








①軒妻の出寸法 確認をお願いします。
(軒は桁芯より垂木先端)
(妻は桁芯より母屋先端)
【 OK / NG→図面に指示をお願いします】


■ 物件番号
HHM0192

凡 例	
材 種	樹種・等級・材寸
 母 屋	檜 支給材 90×90
 棟 木	檜 支給材 105×105
 隅 木	米松 乾燥特等 90×90
 谷 木	米松 乾燥特等 90×90
 登 梁	米松 乾燥特等 105×105
	
 化粧管柱	 床 柱
 階 段 柱	 ポーチ柱
 地 束	 吊 束
	間 柱
-----	根 太
	蟻
	寄 蟻
	逆 蟻
	大入れ
	大引き
	兜
	茶 臼
	鎌 継
	蟻 継
	桁差holz
	胴差holz



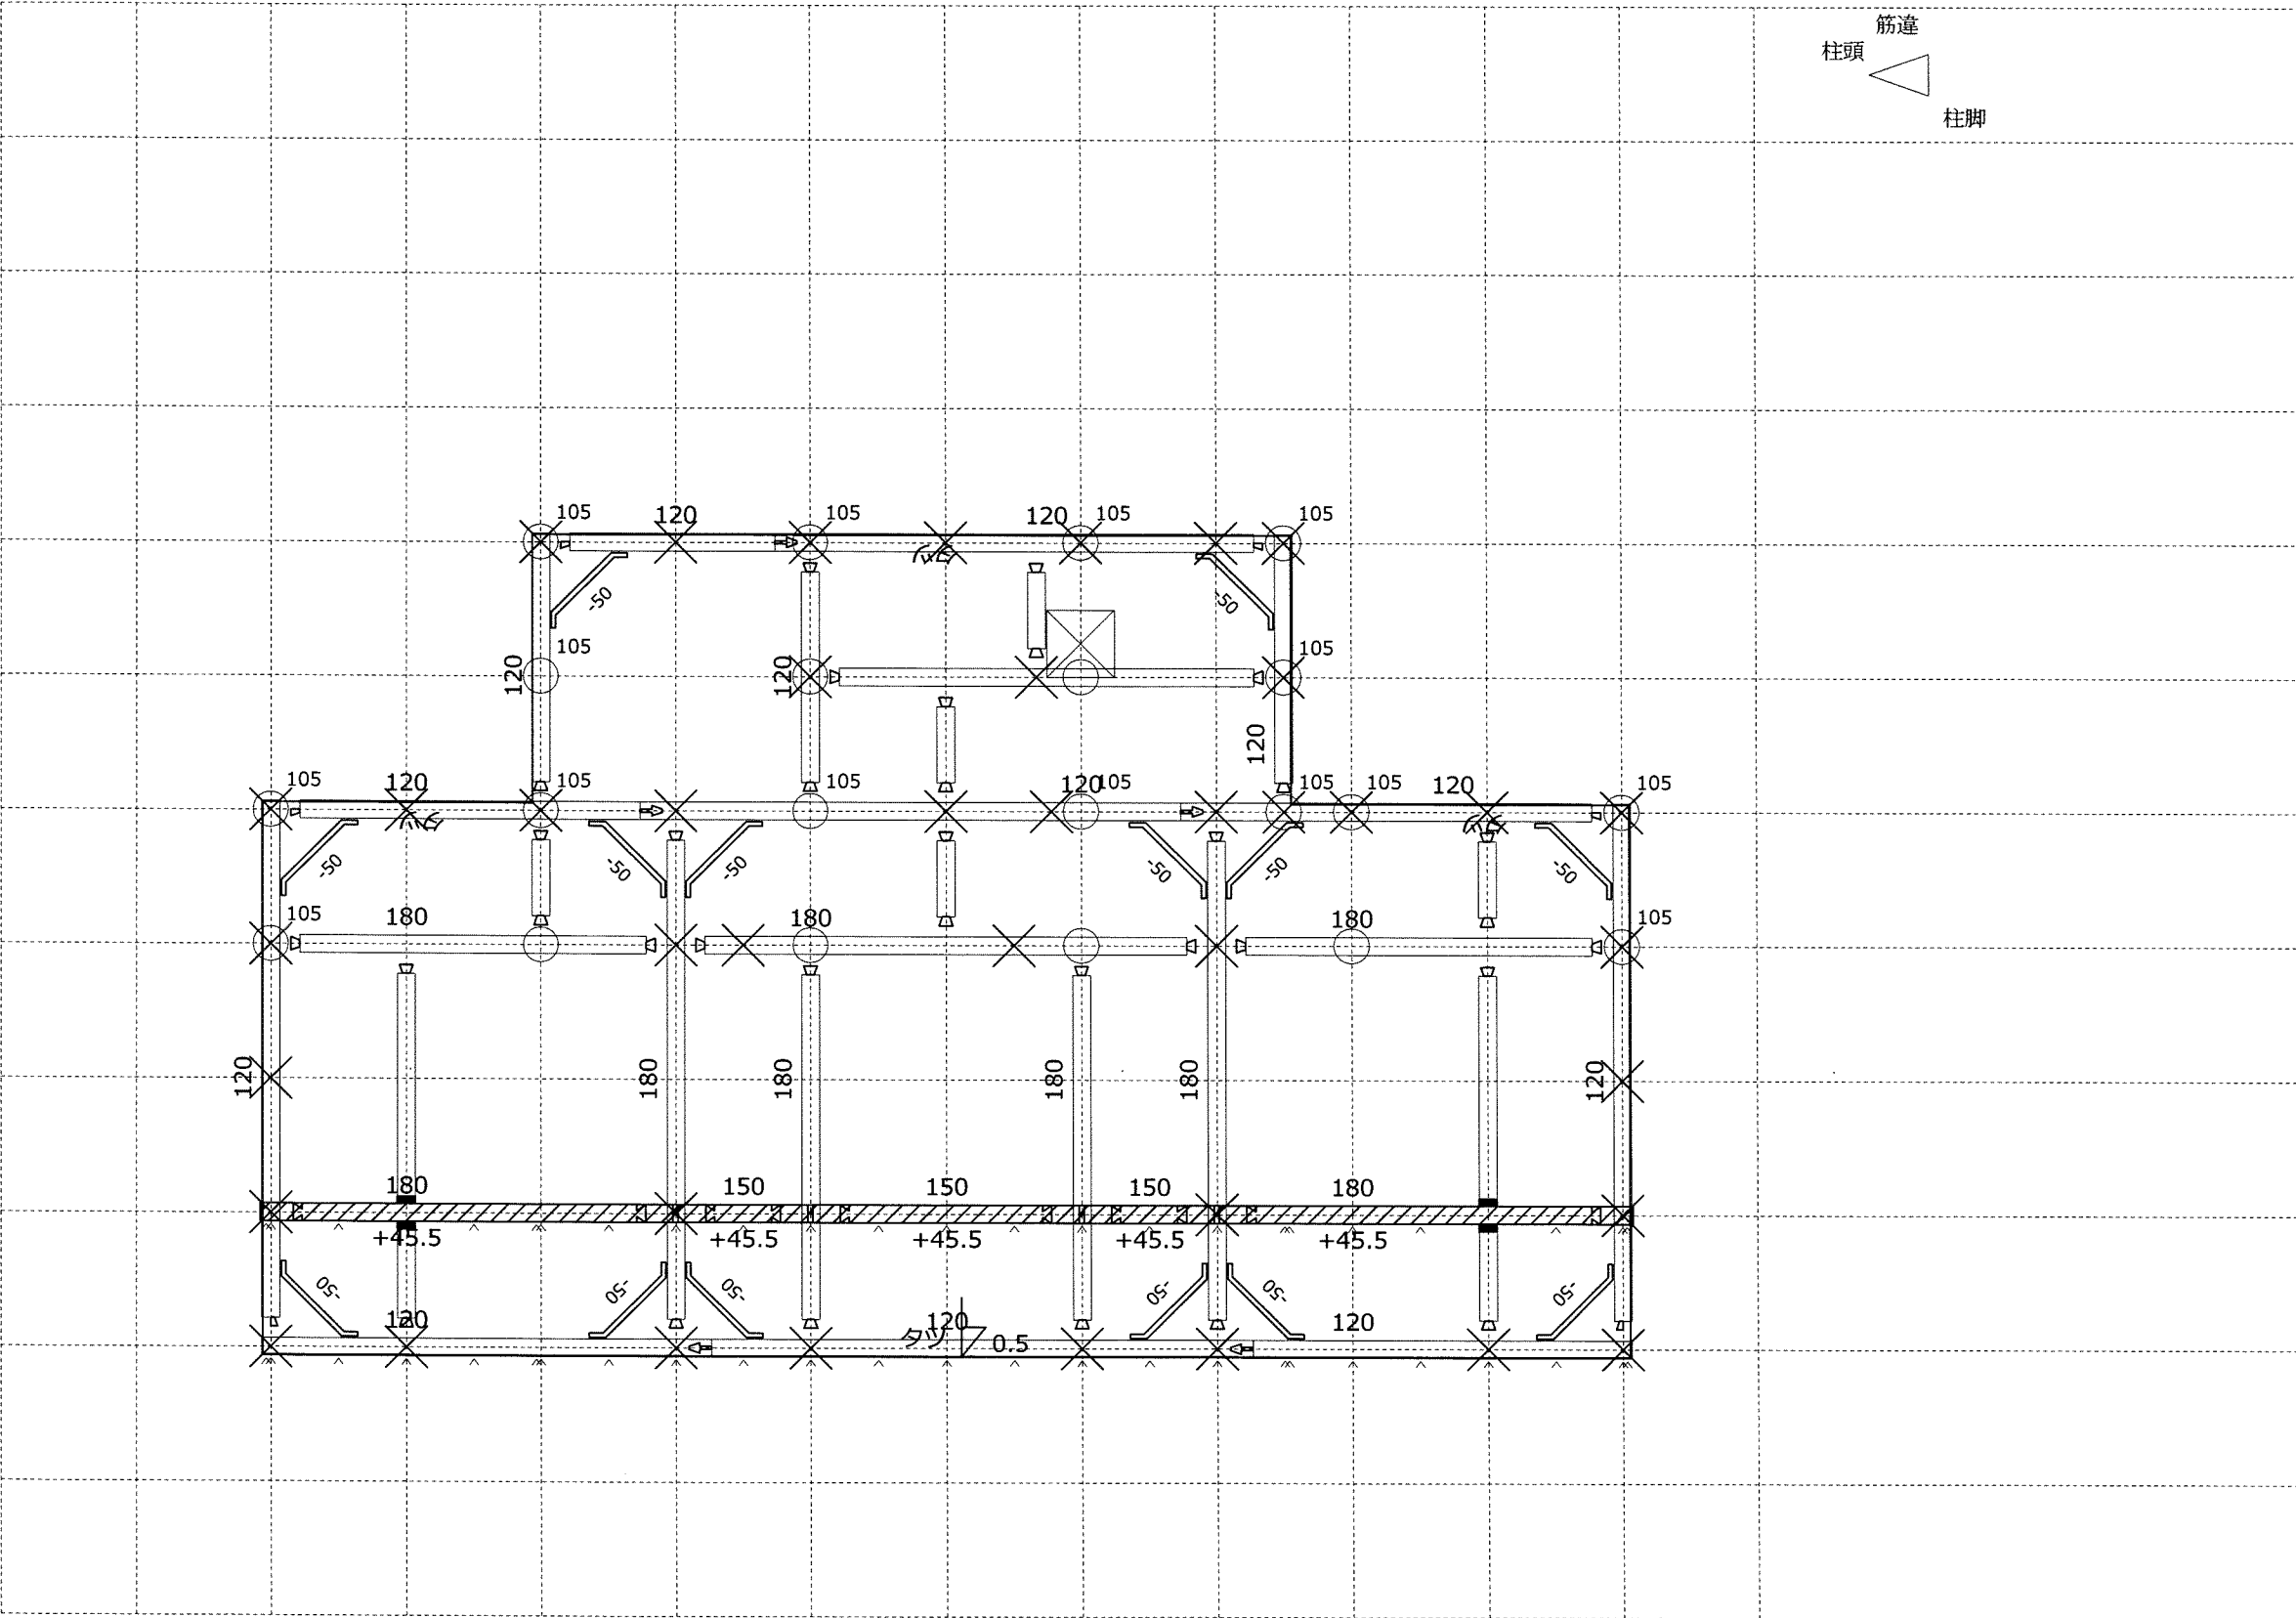
 
 
 
 
 
 
 
わ を る ん り ち と へ ほ に は る い z




凡 例			
材 種		樹種・等級・材寸	
梁		米松 乾燥特等 105×105	
○ 小屋束		檜 支給材 90	
火打梁		鉄アングル 乾燥特等 90×90	
登 梁		米松 乾燥特等 105×105	
▧	化粧管柱	▨	床 柱
◯	階 段 柱	▩	ポーチ柱
◻	地 束	◻	吊 束
		間 柱	
		根 太	
		蟻	
		寄 蟻	
		逆 蟻	
		大入れ	
		大引き	
		兜	
		茶 臼	
		鎌 継	
		蟻 継	
		桁差ホゾ	
		胴差ホゾ	

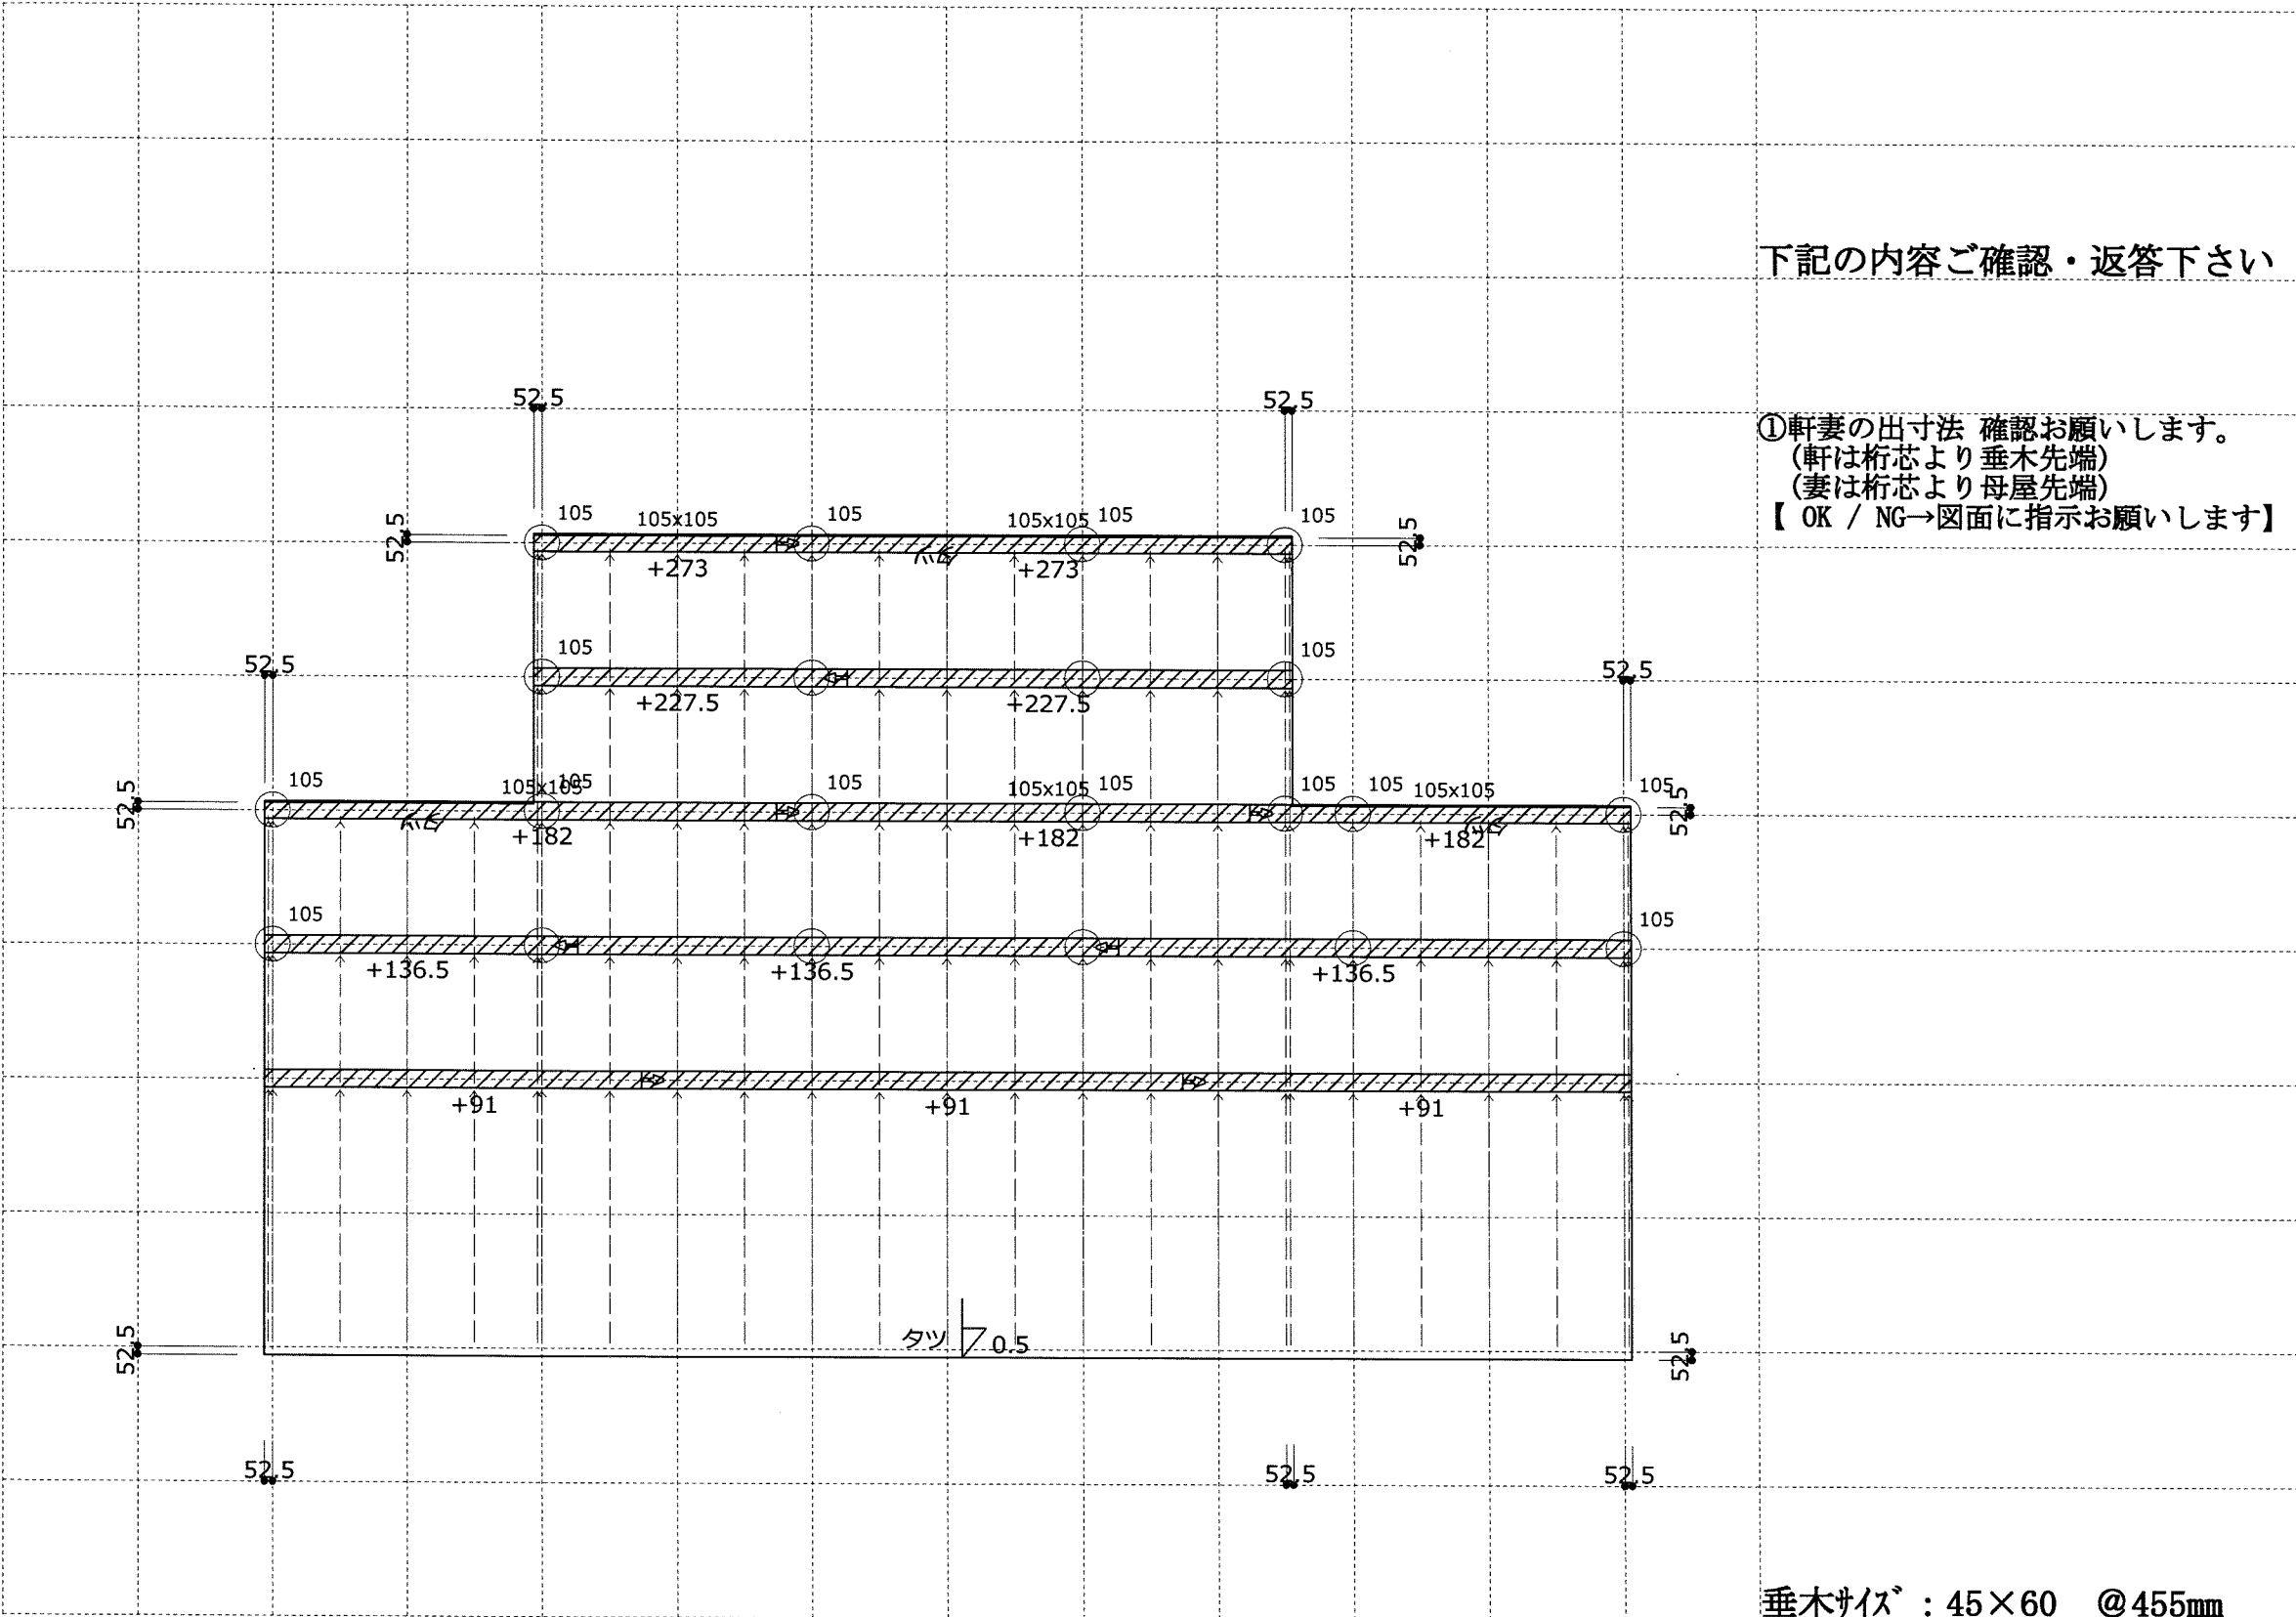


0
1
2
3
4
5
6
7
8
9
10
11
12

          凡 例			
材 種		樹種・等級・材寸	
	母 屋	檜 支給材 90×90	
	棟 木	檜 支給材 105×105	
	隅 木	米松 乾燥特等 90×90	
	谷 木	米松 乾燥特等 90×90	
	登 梁	米松 乾燥特等 105×105	
	化粧管柱		床 柱
	階 段 柱		ポーチ柱
	地 束		吊 束
		間 柱	
-----		根 太	
		蟻	
		寄 蟻	
		逆 蟻	
		大入れ	
		大引き	
		兜	
		茶 臼	
		鎌 継	
		蟻 継	
		桁差ホゾ	
		胴差ホゾ	

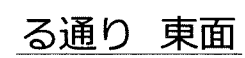


ハイテック CADセンター 浜松CAD室 434-0004 静岡県浜松市浜名区宮口2461 TEL : 053-582-3711 FAX : 053-582-3701			■検印	■モジュール 910 mm		■工事名称 (株)LIFEFUND様 伊藤友章様邸		■図面名称 軸組断面図		
		■桁 高 mm								
		■屋根勾配 寸		■印刷日時 2024年10月29日		■縮尺 1 / 50		■物件番号 HHM0192		

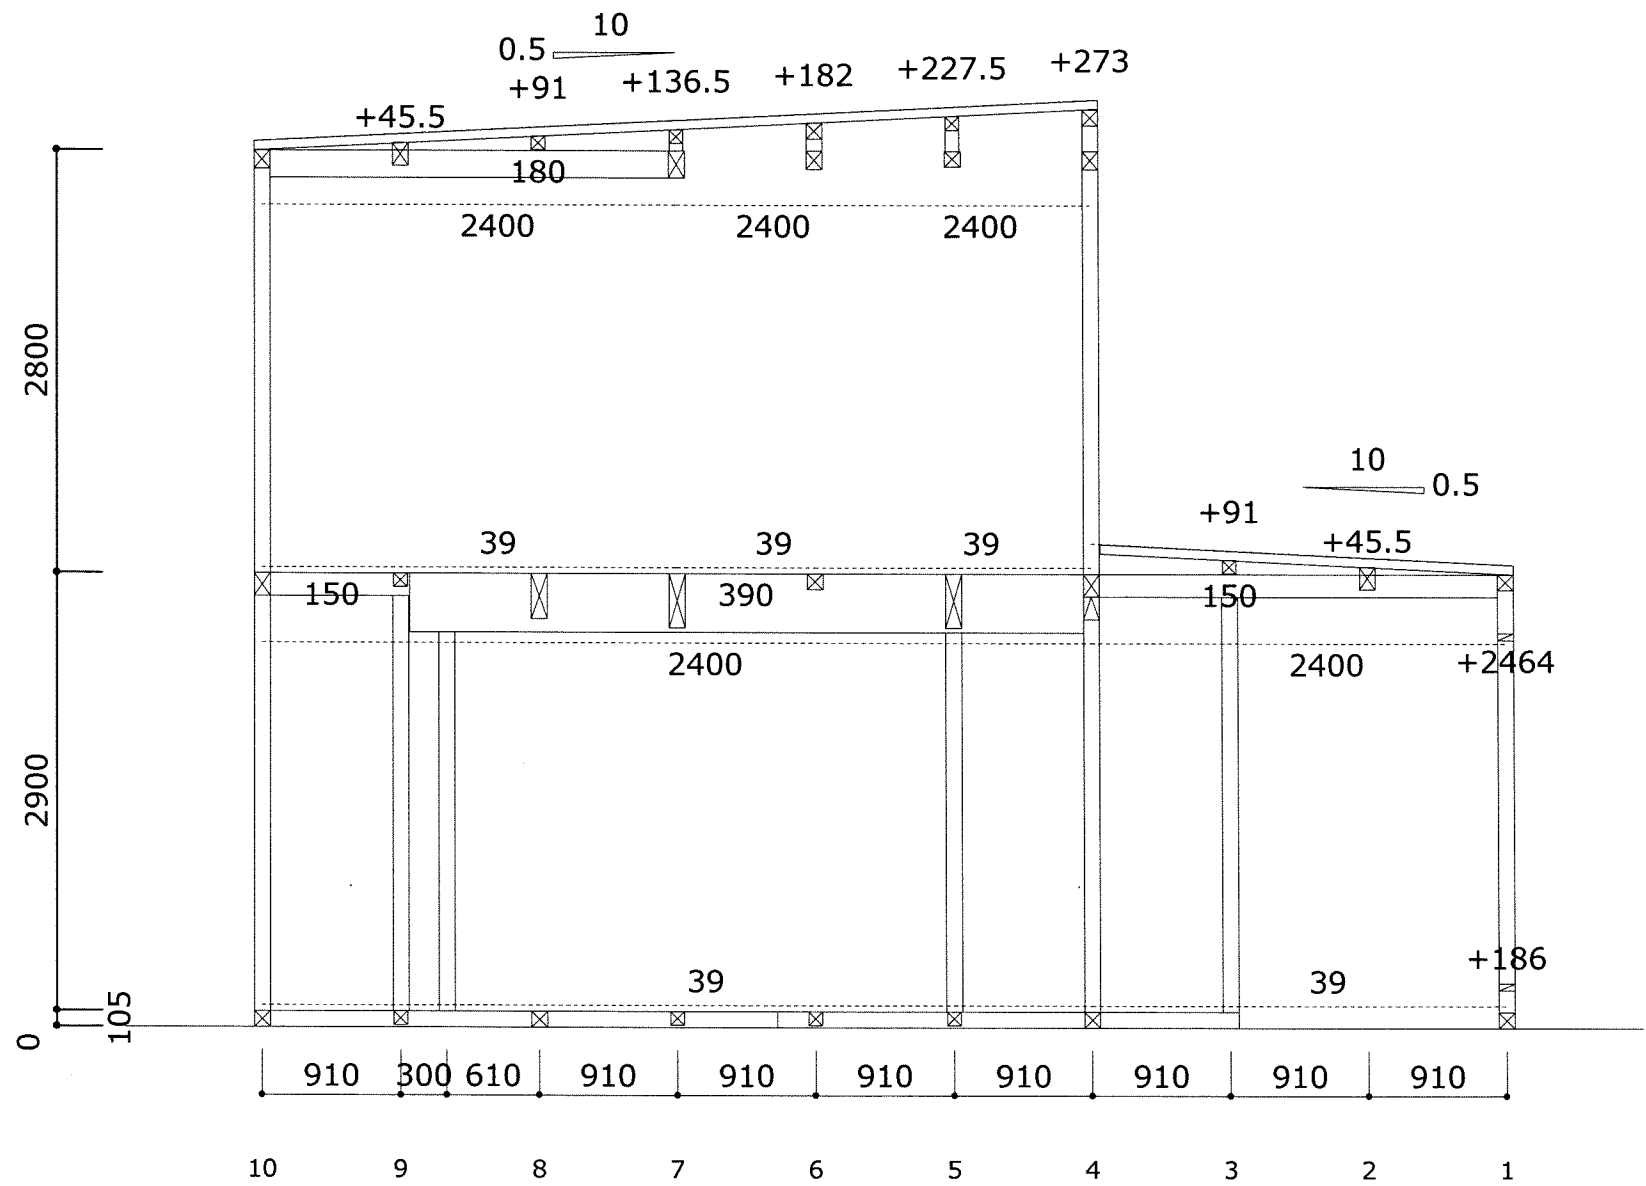


ほ通り 東面

ハピックス CADセンター 浜松 C A D 室			■検印			■モジュール 910 mm			■工事名称		■図面名称			
434-0004						■桁 高 mm			(株)LIFE FUND様 伊藤友章様邸		軸組断面図			
静岡県浜松市浜名区宮口2461						■屋根勾配 寸			■印刷日時		■縮尺		■物件番号	
TEL : 053-582-3711 FAX : 053-582-3701									2024年10月29日		1 / 50		HHM0192	

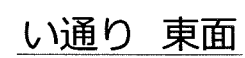


ハイテック CADセンター 浜松CAD室 434-0004 静岡県浜松市浜名区宮口2461		TEL : 053-582-3711 FAX : 053-582-3701	■検印	■モジュール 910 mm ■桁 高 mm ■屋根勾配 寸	■工事名称 (株)LIFEFUND様 伊藤友章様邸 ■印刷日時 2024年10月29日	■縮尺 1 / 50	■図面名称 軸組断面図 ■物件番号 HHM0192
---	--	--	-----	-------------------------------------	--	---------------	------------------------------------

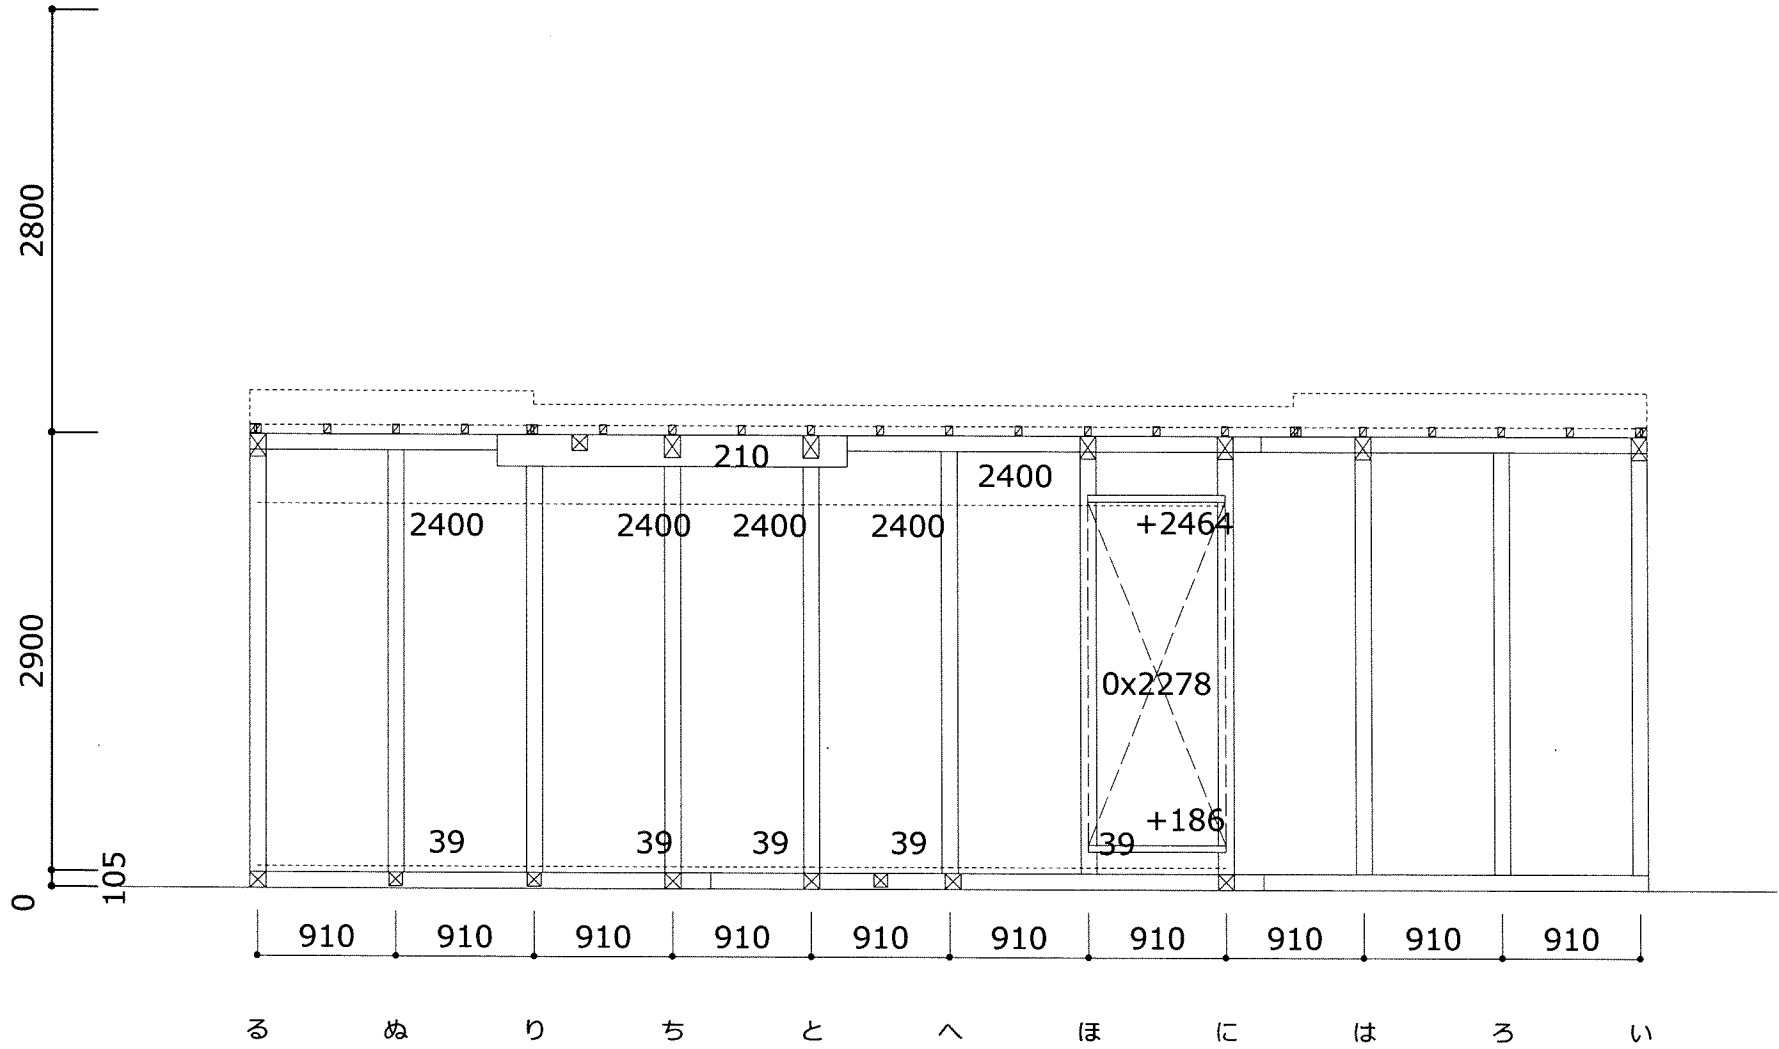


1通り 南面

ハベック CADセンター 浜松CAD室 434-0004 静岡県浜松市浜名区宮口2461 TEL : 053-582-3711 FAX : 053-582-3701	■検印			■モジュール	910	mm	■工事名称 (株)LIFEFUND様 伊藤友章様邸	■図面名称 軸組断面図
				■桁高		mm		
				■屋根勾配		寸		
							■印刷日時	2024年10月29日

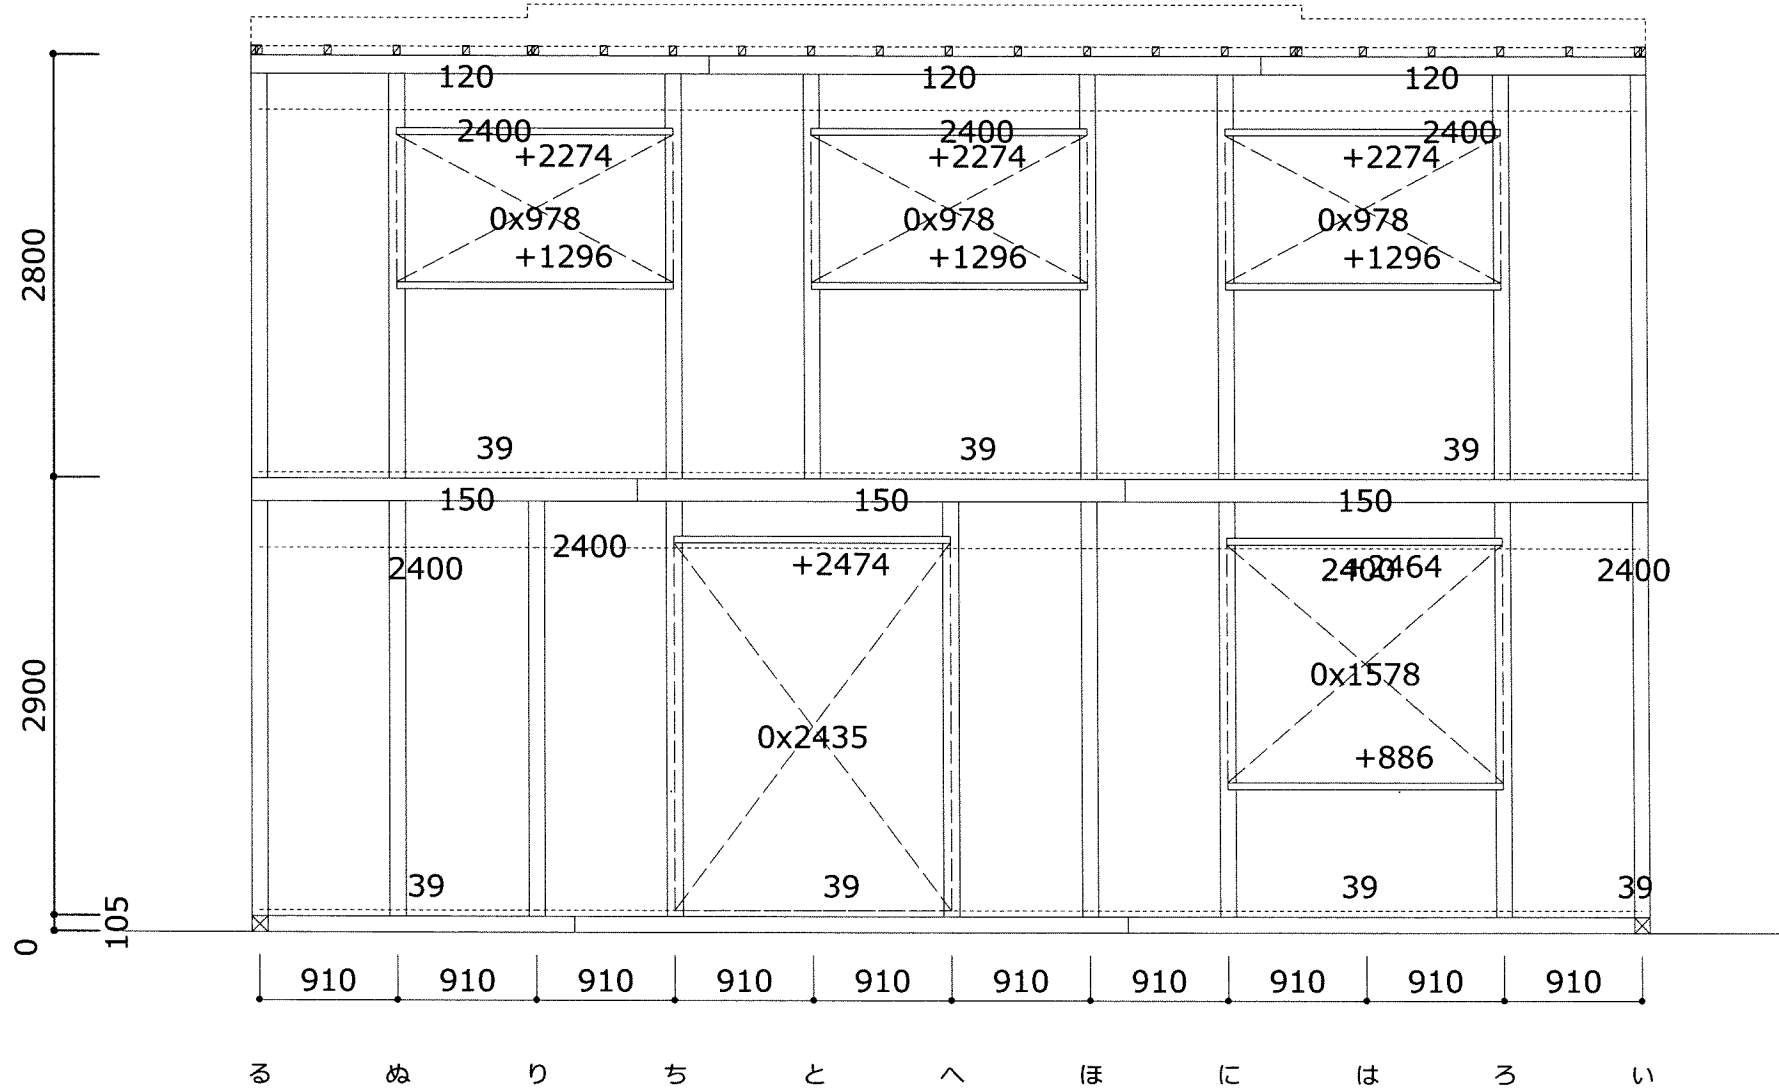

10通り 南面

ハイック CADセンター 浜松CAD室			■検印			■モジュール 910 mm		■工事名称 (株)LIFEFUND様 伊藤友章様邸		■図面名称 軸組断面図			
434-0004						■桁 高 mm							
静岡県浜松市浜名区宮口2461						■屋根勾配 寸		■印刷日時 2024年10月29日		■縮尺 1 / 50		■物件番号 HHM0192	
TEL : 053-582-3711		FAX : 053-582-3701											

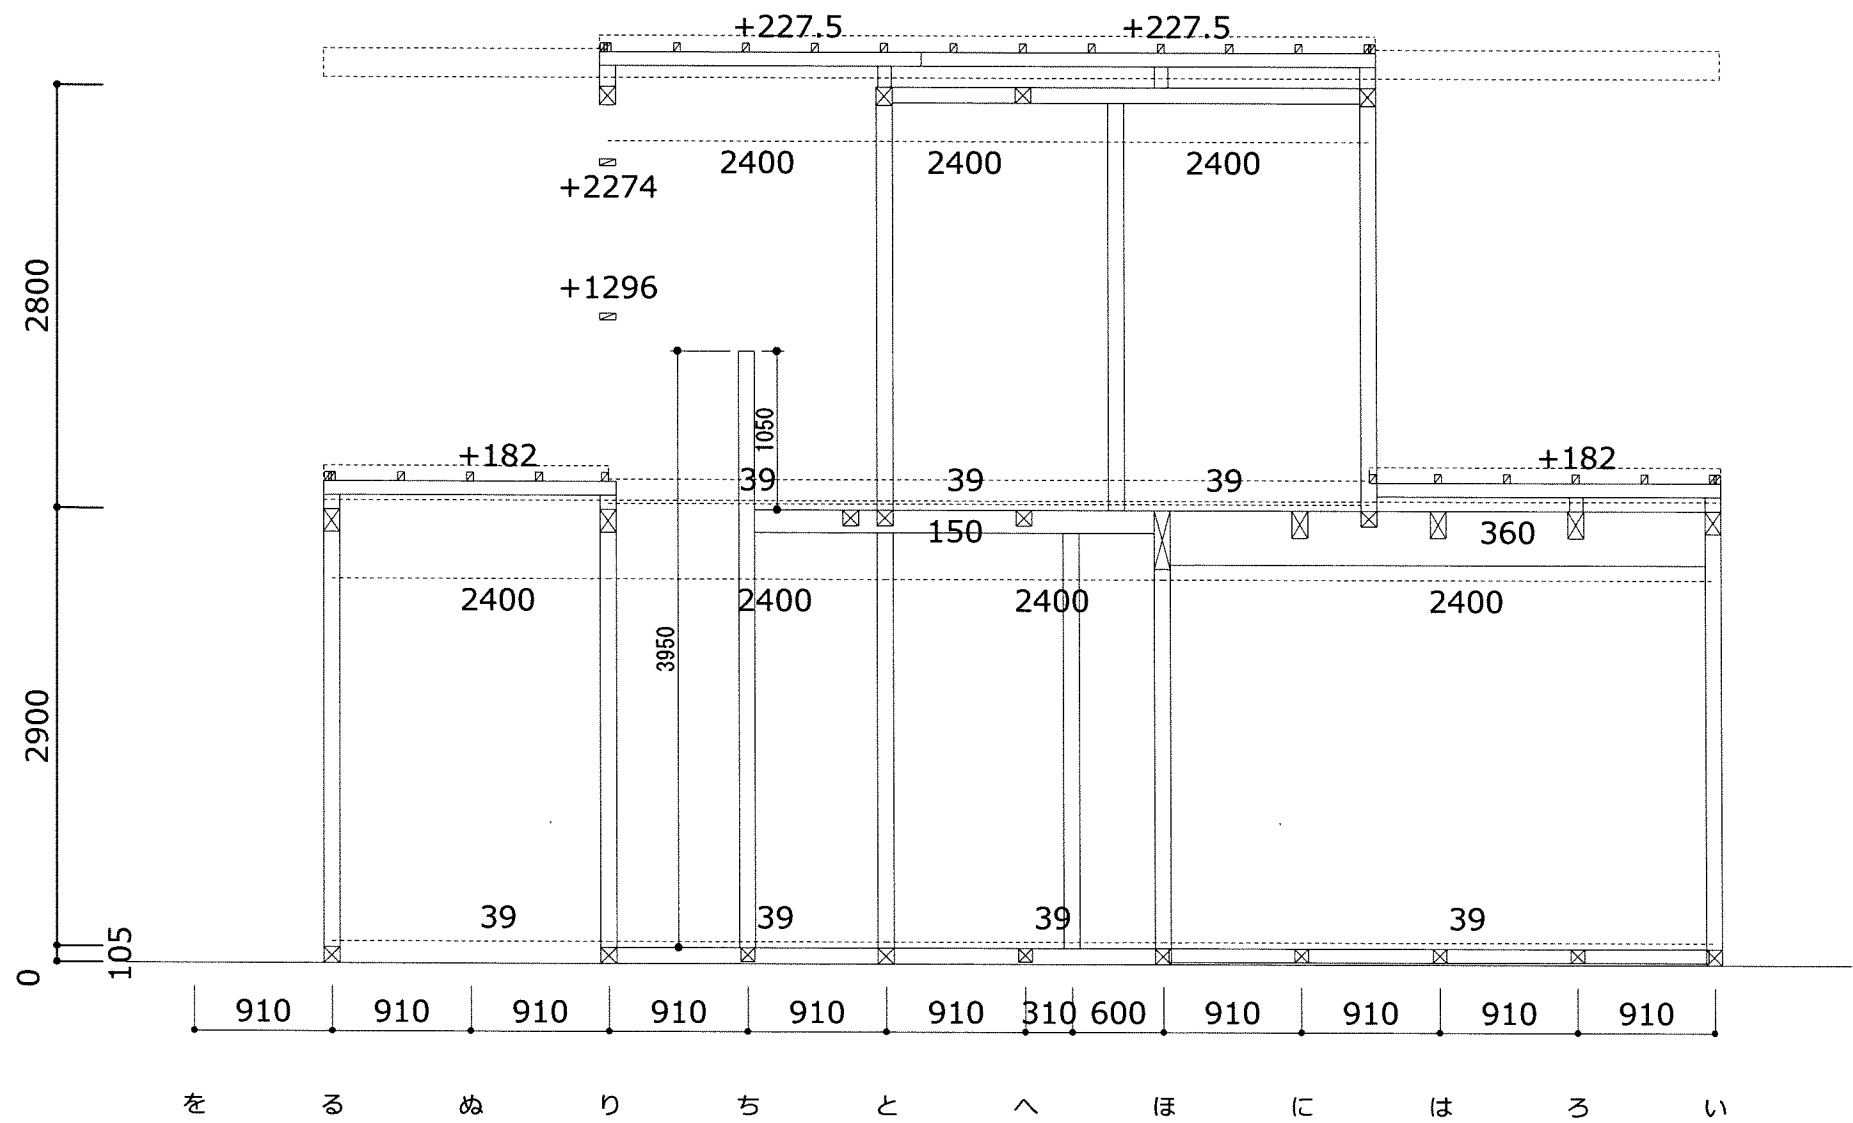

5通り 南面

ハイック CADセンター 浜松CAD室

434-0004

静岡県浜松市浜名区宮口2461

TEL : 053-582-3711

FAX : 053-582-3701

■検印

■モジュール 910

■工事名称

(株)LIFEFUND様 伊藤友章様邸

■図面名称

軸組断面図

■桁高

■印刷日時

2024年10月29日

■縮尺

1 / 50

■物件番号

HHM0192